Aguascalientes
LA CIUDAD DE TU VIDA

Dirección de Programación Presupuestal
Núm. Oficio AMPP/0578/22
Aguascalientes, Ags. 8 de Diciembre del 2022
Asunto: Validación de Expediente Técnico

C.P. SERGIO ARTURO LOZANO GONZÁLEZ
SECRETARIO DE FINANZAS MUNICIPALES
P R E S E N T E

Con fundamento en los artículos 17 fracción XV, 60 fracción XVI y 76 fracción VI del Reglamento del Sistema Integral de Desarrollo Municipal y del Instituto Municipal de Planeación y Evaluación de Aguascalientes, hago referencia al oficio SOPMA/2735/2022 recibido por este Instituto el día 8 de Diciembre del 2022 por parte de la Secretaría de Obras Públicas Municipales, mediante el cual remiten el expediente técnico original de la siguiente obra para su análisis, registro y priorización, conforme al Programa Anual de Obra Pública y Programas Sociales para el ejercicio presupuestal 2022:

DEPENDENCIA EJECUTORA:	SOPMA
NOMBRE DE LA OBRA O PROYECTO:	OBRA COMPLEMENTARIA Y SEÑALIZACIÓN
UBICACIÓN:	AV MAHATMA GANDHI (CALZADA ORIENTE), ENTRE AV. SIGLO XXI Y CENTRAL DE ABASTOS, VARIAS COLONIAS, AGUASCALIENTES, AGS.
FONDO DE INVERSIÓN:	FONDO DE INFRAESTRUCTURA SOCIAL MUNICIPAL Y DE LAS DEMARCACIONES TERRITORIALES DEL DISTRITO FEDERAL
IMPORTE:	$1,010,764.98 (ET FINAL)
No. DE OBRA:	2022-FISMDF-0096-04-1101
MODALIDAD DE EJECUCIÓN:	CONTRATO
EJE:	MUNICIPIO SOBRESALIENTE
ESTRATEGIA:	OBRA PÚBLICA INTELIGENTE
POLITICA:	5.8.1.REHABILITACIÓN Y MANTENIMIENTO VIALIDADES, CAMINOS, CALLES, ÁREAS DE TERRACERÍA Y CAUCES (C

Al respecto, hago de su conocimiento que dicho expediente ha sido analizado en su integración técnica y documental, con base en el artículo 168 fracción I del Reglamento de la Ley de Obras Públicas y Servicios Relacionados para el Estado de Aguascalientes y sus Municipios.

Asimismo, le comento que este Instituto valida dicha obra acorde a lo establecido en los artículos 14, 22 párrafo segundo y 23 de la Ley de Obras Públicas y Servicios Relacionados para el Estado de Aguascalientes y sus Municipios, la cual se encuentra alineada al Plan de Desarrollo Municipal vigente, para dar cumplimiento a las metas establecidas en el mismo, y a los Lineamientos Generales para la Operación de este Fondo de Inversión, toda vez que la misma cuente con la autorización del CODEMUN. De igual manera, se hace de su conocimiento que deberá cumplir con lo establecido en los ordenamientos aplicables en lo que respecta al ejercicio, control e información de los recursos de este Fondo. Cabe hacer mención que los recursos solicitados para este proyecto de inversión, estarán sujetos a la disponibilidad presupuestal para el presente ejercicio fiscal que determine la Secretaría a su digno cargo. Sin otro particular por el momento, le envío un cordial saludo.

A T E N T A M E N T E

ARQ. AUSTRIA GABRIELA DÁVILA DE LA LLAVE
DIRECTORA GENERAL DEL IMPLAN

SEDR/ CAAR / JDBC
C.c.p. LC. ING. MIGUEL ÁNGEL HUIZAR BOTELLO .- Secretaría de Obras Públicas Municipales .Para su conocimiento.
C.c.p. Archivo.

Instituto Municipal de Planeación y Evaluación de Aguascalientes

Antonio Acevedo Escobedo 103 A, Col. Centro
Aguascalientes, Ags. C.P. 20000
(449) 9101010 Ext. 3117
www.implanags.gob.mx

GOBIERNO MUNICIPAL DE AGUASCALIENTES

INSTITUTO MUNICIPAL DE PLANEACION

IMPLAN

ANÁLISIS INTEGRAL DE EXPEDIENTE TÉCNICO

No. DE OBRA (PAOP 2020):	2022-FISMDF-0096-04-1101	REGISTRO No.	263
OFICIO DE VALIDACIÓN:	AMPP/0578/22	FECHA RECIBIDO PARA REVISIÓN:	8 de Diciembre del 2022
PROGRAMA:	URBANIZACION MUNICIPAL	LOCALIDAD O COLONIA:	VARIAS COLONIAS
SUB-PROGRAMA:	0411- Calles y Caminos	DELEGACIÓN:	Aguascalientes
DEPENDENCIA:	Secretaría de Obras Públicas Municipales	MOD. DE EJECUCIÓN:	CONTRATO
NOMBRE DE LA OBRA:	OBRA COMPLEMENTARIA Y SEÑALIZACIÓN, AV MAHATMA GANDHI (CALZADA ORIENTE), ENTRE AV. SIGLO XXI Y CENTRAL DE ABASTOS		
FUENTE DE FINANCIAMIENTO:	FONDO DE INFRAESTRUCTURA SOCIAL MUNICIPAL Y DE LAS DEMARCACIONES TERRITORIALES DEL DISTRITO FEDERAL, FISMDF		
INVERSIÓN:	$1,010,764.98	CLASIFICACIÓN DE OBRA:	BIENES DE DOMINIO PUBLICA

TOTAL	FEDERAL	ESTATAL	MUNICIPAL	BENEFICIARIOS	OTROS	DIFERENCIA ENTRE MOD.
$1,010,764.98	$1,010,764.98	0.00	0.00	0.00	0.00	*$0,00*

TIPO DE EXPENDIENTE:	ET FINAL	AÑO: 2022	AÑO:	AÑO:		
AVANCES:	Financiero: 30 %	Físico: 100 %				
FECHA DE INICIO:	16 de Septiembre del 2022	FECHA DE TÉRMINO:	15 de Octubre del 2022	REGISTRO SIMA:	96	

CHEK LIST DE LOS ANEXOS DEL EXPEDIENTE TÉCNICO

CÉDULA DE REGISTRO DE OBRA	✓
DICTAMEN DE FACTIBILIDAD	✓
MEMORIA DESCRIPTIVA	✓
PRESUPUESTO BASE	✓
FACTIBILIDAD VERIFICADA EN CAMPO	✓
CROQUIS DE UBICACIÓN (MACRO)	✓
CROQUIS DE UBICACIÓN (MACRO)	✓
PROGRAMA DE OBRA Y MONTOS MENSUALES	✓
PLANOS O ESTUDIOS TÉCNICOS	✓
PADRÓN DE BENEFICIARIOS	N/A
ACTA DE ACEPTACIÓN DEL PROYECTO	N/A
DICTAMEN DE IMPACTO AMBIENTAL	N/A
CONVENIO DE CONCERTACIÓN	N/A
ACTA CONSTITUTIVA	N/A

METAS		BENEFICIARIOS		PERIODO DE EJECUCION		OBRA PROPUESTA		CLAVE SISCO
UNIDAD DE MEDIDA	CANT	TIPO DE BENEFICIARIOS	CANTIDAD	FECHA DE INICIO	FECHA DE TERMINO	CONCEPTO	JORNALES A GENERAR	
OBRA	1	Personas	350	2022-09-16	2022-10-15	Obra Complementaria y/o Señalización	2627	2365

INCLUIDO EN PLAN DE DESARROLLO MUNICIPAL Y EL PROGRAMA ANUAL DE OBRA PÚBLICA

OBSERVACIONES:

SIN OBSERVACIONES

RECIBIO: ING. JOSÉ DAVID BURGUETE CLAUSTRO
Analista de Programación e Inversión de Obra Pública

8 de Diciembre del 2022
Fecha de validación

8 de Diciembre del 2022
Fecha de validación Expediente

PROCEDE Si ✓ No

H. AYUNTAMIENTO CONSTITUCIONAL DEL MUNICIPIO DE AGUASCALIENTES 2021-2024

AYUNTAMIENTO DE AGUASCALIENTES

CEDULA DE REGISTRO POR OBRA

Aguascalientes

050400-001E00E05-05-2-2-1-00-1-E-0510-0-17-0096-21-2502-6144

2022-FISMDF-0096-0411109-050	Obra **OBRA COMPLEMENTARIA Y SEÑALIZACIÓN AV. MAHATMA GANDHI (CALZADA ORIENTE)**
Tipo DEFINITIVO 2 2022 Folio SISCO **2365**	Ubic. TRAMO: ENTRE BLVD. SIGLO XXI Y ACCESO A CENTRAL DE ABASTOS, AGUASCALIENTES Mpio.

Ent. Ejecutora : **050400001E00E05**

Eje: **05**	MUNICIPIO SOBRESALIENTE
Finalidad: **2**	DESARROLLO SOCIAL
Función: **2**	VIVIENDA Y SERVICIOS A LA COMUNIDAD
Subfunción: **1**	URBANIZACIÓN
Tema: **00**	SIN TEMA
Cuenta del Gasto **1**	GASTO PROGRAMABLE
Clasif. Programatica: **E**	PRESTACIÓN DE SERVICIOS PÚBLICOS
Programa: **0510**	Movilidad Urbana
SubPrograma: **0**	SUBPROGRAMA GENÉRICO
Proyecto: **17**	
Tipo de Gasto: **21**	GASTO INVERSIÓN / OBRA PÚBLICA

I N V E R S I O N 2022

Municipal	2502	FONDO PARA LA INFRAESTRUCTURA SOCIAL MUNICIPAL Y DE LAS DEMARCACIONES TERRITORIALES DEL DISTRITO FEDERAL 2022	$1,010,764.98

Folio SIMA 96 Total $1,010,764.98

M E T A S

Unidad de Medida	Cantidad	Descripción
OBRA	1	OBRA OBRA COMPLEMENTARIA Y SEÑALIZACIÓN AV. MAHATMA GANDHI (CALZADA ORIENTE)

Inversión Ejercida Total al 31 de Diciembre de 2021 $0.00

Avance Fisico Acumulado al 31 de Diciembre de 2021

Avance Fisico Acumulado Programado al 31 de Diciembre de 2022 100 %

Fecha de Inicio 16 Sep 2022 Fecha de Terminación 15 Oct 2022

Jornales a Generar en 2022 2627

Modalidad de ejecución CONTRATO

Clasificación de la Obra Bienes de Dominio Público

Registro del Patrimonio: Obras del dominio público

OBRAS PÚBLICAS

Av. Aguascalientes Sur No. 2615
Fracc. Jardines de las Fuentes,
Aguascalientes, Ags. C.P. 20278

(449) 9 78 92 01, 06, 09

www.ags.gob.mx

GENERALES

Nombre del Proyecto : OBRA COMPLEMENTARIA Y SEÑALIZACIÓN AV. MAHATMA GANDHI (CALZADA ORIENTE)

TRAMO: ENTRE BLVD. SIGLO XXI Y ACCESO A CENTRAL DE ABASTOS, AGUASCALIENTES Mpio.

Programa : 04 URBANIZACION MUNICIPAL

Subprograma : 11 Calles y caminos (428.- Rehabilitación: 0411208- Señalización)

Clave del Municipio : AGUASCALIENTES

Localidad :

Barrio, Colonia o Ejido : AGUASCALIENTES Mpio.

Tipo de Obra : NUEVA

DESCRIPCIÓN DEL PROYECTO:

OBRA COMPLEMENTARIA Y SEÑALIZACIÓN AV. MAHATMA GANDHI (CALZADA ORIENTE) 1.00 OBRA

Beneficiarios (No. y Tipo) :

350	PERSONAS

Hombres: 175 Mujeres: 175

OBRAS PÚBLICAS

Av. Aguascalientes Sur No. 2615
Fracc. Jardines de las Fuentes,
Aguascalientes, Ags. C.P. 20278

(449) 9 78 92 01, 06, 09

www.ags.gob.mx

Los abajo firmantes, hacen constar que el presente proyecto :

OBRA COMPLEMENTARIA Y SEÑALIZACIÓN AV. MAHATMA GANDHI (CALZADA ORIENTE)

TRAMO: ENTRE BLVD. SIGLO XXI Y ACCESO A CENTRAL DE ABASTOS, AGUASCALIENTES Mpio.

cumple con los Requisitos y Normas Técnicas establecidas por la Dependencia Normativa, por lo que es viable su ejecución. Comprometiéndose la misma a proporcionar la supervisión y asistencia técnica necesaria durante el proceso administrativo.

Por la Dependencia Ejecutora

Ing. Miguel Angel Huizar Botello
Secretario de Obras Públicas

Lic. Jaime Gallo Camacho
Secretario de Desarrollo Urbano

LUGAR :AGUASCALIENTES, AGS.

H. AYUNTAMIENTO CONSTITUCIONAL DEL MUNICIPIO DE AGUASCALIENTES 2021-2024

AYUNTAMIENTO DE AGUASCALIENTES

FACTIBILIDAD VERIFICADA EN CAMPO

Aguascalientes LA CIUDAD DE TU VIDA

MUNICIPIO: AGUASCALIENTES

LOCALIZACION: TRAMO: ENTRE BLVD. SIGLO XXI Y ACCESO A CENTRAL DE ABASTOS, AGUASCALIENTES Mpio.

PROGRAMA: URBANIZACION MUNICIPAL

SUBPROGRAMA: Calles y caminos (428.- Rehabilitación: 0411208- Señalización)

OBRA A REALIZAR: OBRA COMPLEMENTARIA Y SEÑALIZACIÓN AV. MAHATMA GANDHI (CALZADA ORIENTE)

DEPENDENCIA EJECUTORA: SECRETARÍA DE OBRAS PUBLICAS DEL MUNICIPIO DE AGUASCALIENTES

FORMA DE EJECUCION: CONTRATO

TIPO DE OBRA PROPUESTA: NUEVA

CONDICIONES ACTUALES DE LA OBRA:

OBRA COMPLEMENTARIA Y SEÑALIZACIÓN AV. MAHATMA GANDHI (CALZADA ORIENTE)

CARACTERISTICAS DE LA OBRA: Bueno

FACTIBILIDAD DE LA OBRA:

ESTA OBRA SE REQUIERE PARA EL BENEFICIO DE LA CIUDADANÍA

PROCEDE: SI [X] NO [ ]

REVISÓ: Jefa del Departamento de Expedientes Tecnicos y Costos

NOMBRE: Arq. Blanca Margarita Martinez Amador

FIRMA:

FECHA: 28 Nov 2022

SECRETARÍA DE OBRAS PÚBLICAS

Av. Aguascalientes Sur No. 2615
Fracc. Jardines de las Fuentes,
Aguascalientes, Ags. C.P. 20278

(449) 9 78 92 01, 06, 09

www.ags.gob.mx

No. Folio SISCO 2365

H. AYUNTAMIENTO CONSTITUCIONAL DEL MUNICIPIO DE AGUASCALIENTES 2021 2024

Aguascalientes
LA CIUDAD DE TU VIDA

MACRO LOCALIZACIÓN

APROBACIÓN	**2022-FISMDF-0096-0411109-050**
NOMBRE DE LA OBRA:	**OBRA COMPLEMENTARIA Y SEÑALIZACIÓN AV. MAHATMA GANDHI (CALZADA ORIENTE)**
UBICACIÓN:	**TRAMO: ENTRE BLVD. SIGLO XXI Y ACCESO A CENTRAL DE ABASTOS, AGUASCALIENTES Mpio.**
PROGRAMA:	**04 - URBANIZACION MUNICIPAL**




I.C. LAURA CECILIA MARTINEZ ALBA
RESIDENTE DE SUPERVISIÓN

H. AYUNTAMIENTO CONSTITUCIONAL DEL MUNICIPIO DE AGUASCALIENTES 2021 2024

Aguascalientes
LA CIUDAD DE TU VIDA

MICRO LOCALIZACIÓN

APROBACIÓN	**2022-FISMDF-0096-0411109-050**
NOMBRE DE LA OBRA:	**OBRA COMPLEMENTARIA Y SEÑALIZACIÓN AV. MAHATMA GANDHI (CALZADA ORIENTE)**
UBICACIÓN:	**TRAMO: ENTRE BLVD. SIGLO XXI Y ACCESO A CENTRAL DE ABASTOS, AGUASCALIENTES Mpio.**
PROGRAMA:	**04 - URBANIZACION MUNICIPAL**

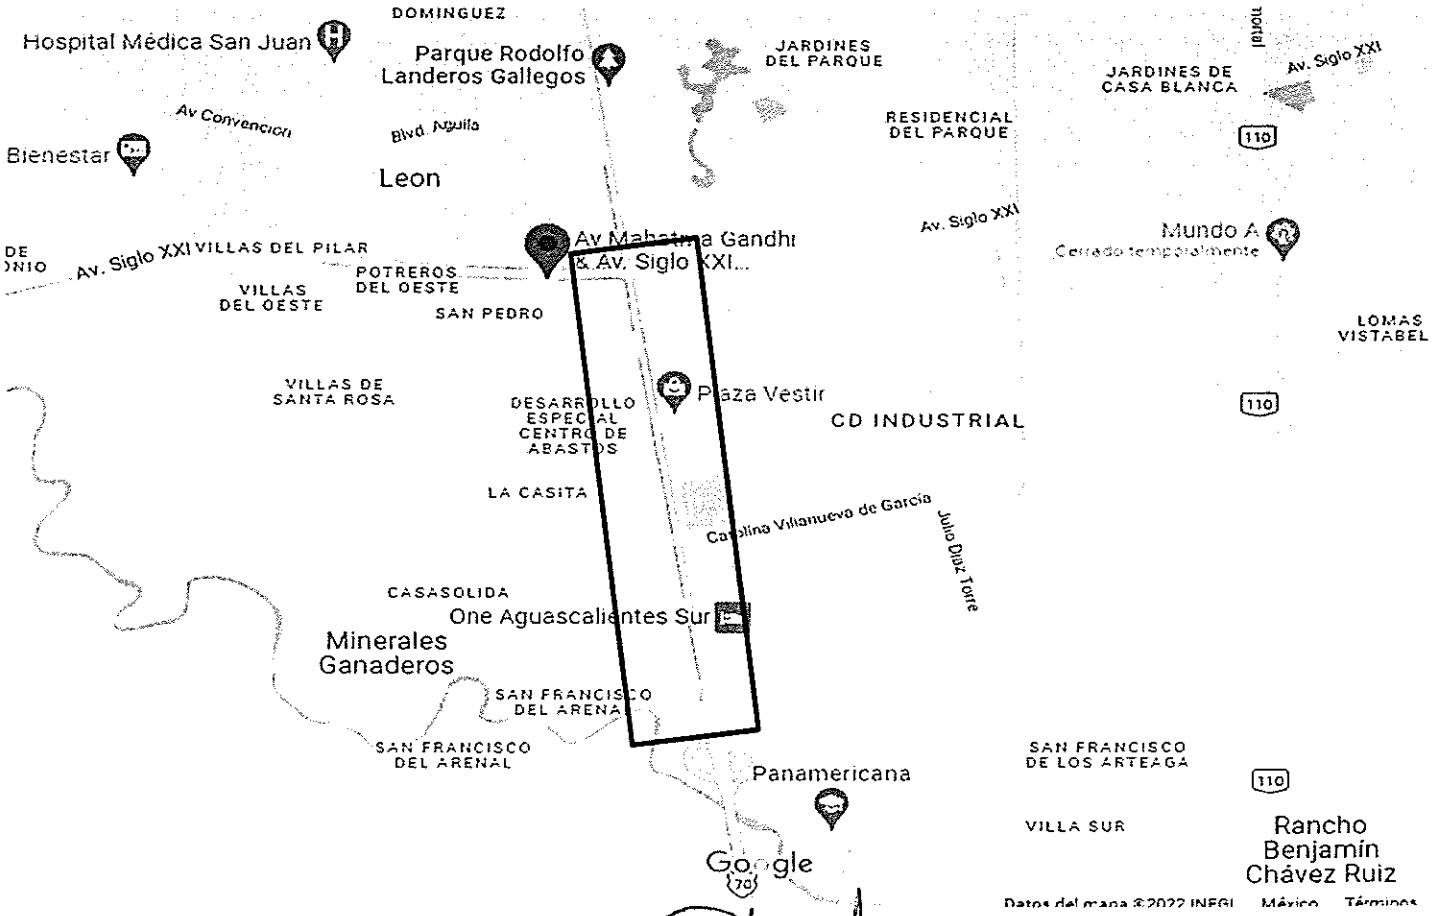

I.C. LAURA CECILIA MARTÍNEZ ALBA
RESIDENTE DE SUPERVISIÓN

PROGRAMA DE OBRA DEFINITIVO

Aguascalientes
LA CIUDAD DE TU VIDA

No. DE CONTRATO : FISMDF-0096-2022

PROGRAMA: 04 URBANIZACION MUNICIPAL

INICIO VIGENTE: 16-septiembre-22

No. OBRA Y NOMBRE DE LA OBRA: 2022-FISMDF-0096-001-0411109-050 OBRA COMPLEMENTARIA Y SEÑALIZACIÓN AV. MAHATMA GANDHI (CALZADA ORIENTE), TRAMO: ENTRE BLVD. SIGLO XXI Y ACCESO A CENTRAL DE ABASTOS, AGUASCALIENTES Mpio.

TERMINO REAL: 15-octubre-22

RECURSO 2022

CONCEPTO			1	2	3	4	5	6	7	8	9	10	11	12	13	14	15	16	PONDERACIÓN %	
			2021																	
			OCTUBRE	NOVIEMBRE	DICIEMBRE	ENERO	FEBRERO	MARZO	ABRIL	MAYO	JUNIO	JULIO	AGOSTO	SEPTIEMBRE	OCTUBRE	NOVIEMBRE	DICIEMBRE	ENERO	FINANCIERO	FÍSICO
																			%	%
DESCRIPCION	INVERSION													15	15					
OBRA COMPLEMENTARIA Y SEÑALIZACION AV. MAHATMA GANDHI (CALZADA ORIENTE)																				
TRAMO: ENTRE BLVD. SIGLO XXI Y ACCESO A CENTRAL DE ABASTOS																				
PRELIMINARES	$ 8,759.26	100												100					1.01	11.11
OBRA COMPLEMENTARIA	$ 259,594.85	100												50	50				29.79	22.22
LIMPIEZAS	$ 20,683.98	100												50	50				2.40	22.22
SEÑALIZACIÓN HORIZONTAL	$ 582,111.03	100												25	25	25	25		66.81	44.44
SUBTOTAL SIN IVA	$ 871,349.12		0	0	0	0	0	0	0	0	0	0	0	1	2	1	0	0		
AVANCE SEMANAL %			0%	0%	0%	0%	0%	0%	0%	0%	0%	0%	0%	34%	11%	27%	0%	0%		
AVANCE SEMANAL ACUMULADO %			0%	0%	0%	0%	0%	0%	0%	0%	0%	0%	0%	34%	45%	72%	72%	72%	100.00	100.00
EJERCIDO SEMANAL $			-	-	-	-	-	-	-	-	-	-	-	294,325.43	145,527.76	155,997.73	-	-	$ 871,349.12	
EJERCIDO MENSUAL $			$0.00	$0.00	$0.00	$0.00	$0.00	$0.00	$0.00	$0.00	$0.00	$0.00	$0.00	$669,851.62	$301,497.51	$0.00	$0.00	$0.00	$ 139,415.86	IVA 16%
EJERCIDO MENSUAL ACUMULADO $			0.00	0.00	0.00	0.00	0.00	0.00	0.00	0.00	0.00	0.00	0.00	669,851.62	871,349.12	871,349.12	871,349.12	871,349.12		
EJERCIDO SEMANAL %			0%	0%	0%	0%	0%	0%	0%	0%	0%	0%	0%	34%	17%	18%	0%	0%		
EJERCIDO MENSUAL %			0%	0%	0%	0%	0%	0%	0%	0%	0%	0%	0%	68%	35%	0%	0%	0%		
EJERCIDO MENSUAL ACUMULADO %			0%	0%	0%	0%	0%	0%	0%	0%	0%	0%	0%	68%	100%	100%	100%	100%	GRAN TOTAL EJERCIDO	
																			$	1,010,764.98

ING. LAURA CECILIA MARTÍNEZ ALBA
RESIDENTE DE SUPERVISIÓN

PRESIDENCIA MUNICIPAL DE AGUASCALIENTES

FACTIBILIDAD VERIFICADA EN CAMPO

GENERALES

EJERCICIO: 2022 APROBACION No: 2022-FISMDF-0096-001-0411109-050

LOCALIDAD: TRAMO: ENTRE BLVD. SIGLO XXI Y ACCESO A CENTRAL DE ABASTOS, AGUASCALIENTES Mpio.

MUNICIPIO: AGUASCALIENTES, Mpio.

TIPO DE INVERSION: FONDO PARA LA INFRAESTRUCTURA SOCIAL MUNICIPAL Y DE LAS DEMARCACIONES TERRITORIALES DEL DISTRITO FEDERAL

PROGRAMA: 04 URBANIZACION MUNICIPAL

SUB-PROGRAMA:

OBRA A REALIZARSE: OBRA COMPLEMENTARIA Y SEÑALIZACIÓN AV. MAHATMA GANDHI (CALZADA ORIENTE)

DEPENDENCIA EJECUTORA: SECRETARÍA DE OBRAS PÚBLICAS MUNICIPALES (S.O.P.M.A)

FORMACIÓN DE EJECUCION: CONTRATO NO. DE CONTRATO: FISMDF-0096-2022

NOMBRE CONTRATISTA: DIAZ SANCHEZ LUIS ROBERTO I.C.

REPRESENTANTE: DIAZ SANCHEZ LUIS ROBERTO I.C.

MONTO CONT. ORIGEN $1,010,764.98 ANTICIPO: $261,404.73 PLAZO 30 DIAS

1A AMPLIACION $: $ - 1 AMPL DIAS

2A AMPLIACION $: 2 AMPL DIAS

FIRMA CONTRATO: 12/09/2022

INICIO CONT: dd/mm/aa 13/09/2022 TERMINO CONT: 12/10/2022

INICIO REAL: dd/mm/aa 16/09/2022 TERMINO REAL: 15/10/2022

TIPO DE OBRA PROPUESTA

NUEVA CREACIÓN		CONSOLIDACIÓN	
COMPLEMENTARIA	X	AMPLIACIÓN	
REHABILITACIÓN		EQUIPAMIENTO	

CARACTERÍSTICAS DE LA OBRA:

RENIVELACION DE POZOS DE VISITA, CAJAS DE VALVULAS
PINTURA EN GUARNICION
PINTURA PASOS PEATONALES
VIALETAS SOLARES, VIALETAS ESTÁNDAR

CONDICIONES ACTUALES DE LA OBRA: (SELECCIONAR UNO OBLIGATORIO)

BUEN ESTADO X REGULAR PESIMO ESTADO

FACTIBILIDAD DE LA OBRA: (CONDICIONES ACTUALES DE LA OBRA)

ESTA OBRA SE ENCUENTRA EN CONDICIONES PARA OPERARSE

PROCEDE: SI: X NO:
MARQUE SOLO UNA

I.C. LAURA CECILIA MARTÍNEZ ALBA
SUPERVISOR

PRESIDENCIA MUNICIPAL DE AGUASCALIENTES

FACTIBILIDAD VERIFICADA EN CAMPO

GENERALES

LOCALIDAD: AV. MAHATMA GANDHI (CALZADA ORIENTE), TRAMO: ENTRE BLVD. SIGLO XXI Y ACCESO A CENTRAL DE ABASTOS, AGUASCALIENTES Mpio.

MUNICIPIO: AGUASCALIENTES

PROGRAMA: 04 - URBANIZACION MUNICIPAL

SUB-PROGRAMA:

OBRA A REALIZARSE: OBRA COMPLEMENTARIA Y SEÑALIZACIÓN AV. MAHATMA GANDHI (CALZADA ORIENTE)

DEPENDENCIA EJECUTORA: SECRETARÍA DE OBRAS PÚBLICAS MUNICIPALES (S.O.P.M.A)

FORMACIÓN DE EJECUCION: CONTRATO

TIPO DE OBRA PROPUESTA

NUEVA CREACIÓN		CONSOLIDACIÓN	
COMPLEMENTARIA	X	AMPLIACIÓN	
REHABILITACIÓN		EQUIPAMIENTO	

CARACTERÍSTICAS DE LA OBRA:

OBRA COMPLEMENTARIA Y SEÑALIZACIÓN AV. MAHATMA GANDHI (CALZADA ORIENTE)

CONDICIONES ACTUALES DE LA OBRA:

BUEN ESTADO	X	REGULAR		PESIMO ESTADO	

FACTIBILIDAD DE LA OBRA:

SE HACE ENTREGA DE LA OBRA DE ACUERDO A LAS METAS INICIALES, ATENDIENDO EL CONTRATISTA LOS DETALLES MARCADOS PREVIOS A LA ENTREGA.

PROCEDE SI X NO

Aguascalientes
LA CIUDAD DE TU VIDA

I.C. LAURA CECILIA MARTINEZ ALBA
SUPERVISOR

PRESUPUESTO MODIFICADO

Obra: **OBRA COMPLEMENTARIA Y SEÑALIZACIÓN AV. MAHATMA GANDHI (CALZADA ORIENTE)**

Ubicación: **TRAMO: ENTRE BLVD. SIGLO XXI Y ACCESO A CENTRAL DE ABASTOS, AGUASCALIENTES Mpio.**

Contratista: **DIAZ SANCHEZ LUIS ROBERTO I.C. (860)**

No.	Concepto	Unidad	Cantidad	Precio Unitario	Importe Total
	GRUPO: **OBRA COMPLEMENTARIA Y SEÑALIZACION**				
	PARTIDA: **PRELIMINARES**				
1	CORTE CON DISCO DIAMANTADO DE 14" EN PISOS DE CONCRETO ASFÁLTICO DE HASTA (HASTA 8.00 cm. DE PROFUNDIDAD). INCLUYE: TRAZO, EQUIPO Y OPERACIÓN, LIMPIEZAS.	ML	54.6	$44.67	$2,438.98
2	DEMOLICIÓN A MANO Y MECÁNICA DE PAVIMENTO HIDRÁULICO Y/O ASFÁLTICO EN CUALQUIER ESPESOR, EN PAVIMENTOS, LOSAS DIAMANTE, LOSAS DE CAJAS DE VÁLVULAS, LOSAS DE LLAVE HIDRAULICA, CAIMANES, ETC., CON O SIN ARMADO DE ACERO SIN RECUPERACIÓN., INCLUYE: CARGA Y ACARREO LOCAL DE MATERIAL AL LUGAR DE ACOPIO, HERRAMIENTA NECESARIA, CORTES CON DISCO Y TODO LO NECESARIO PARA SU CORRECTA EJECUCIÓN, LIMPIEZA, TRABAJO TERMINADO.	M3	6.57	$459.90	$3,021.54
4	CARGA MECANICA Y ACARREO DE MATERIAL PRODUCTO DE EXCAVACION Y DEMOLICION EN CAMION DE VOLTEO AL 1er. KM, VOLUMEN MEDIDO COMPACTO.	M3	6.57	$35.89	$235.80
5	ACARREO DE MATERIAL PRODUCTO DE EXCAVACION Y/O DEMOLICION EN CAMION DE VOLTEO A KILOMETROS SUBSECUENTES, AL TIRADERO OFICIAL AUTORIZADO MAS CERCANO AUTORIZADO POR LA SUPERVISION, VOLUMEN MEDIDO COMPACTO.	M3-KM	197.1	$15.54	$3,062.93
				Totales por Partida	**$8,759.26**
	PARTIDA: **OBRA COMPLEMENTARIA**				
6	RE NIVELACIÓN DE POZO DE VISITA HASTA 30 cm DE ALTURA. INCLUYE: RETIRO SIN RECUPERACIÓN DE BROCAL EXISTENTE, DEMOLICIONES, NIVELADO CON TABIQUE ROJO RECOCIDO 7X14X28, ASENTADO CON MORTERO CEMENTO-ARENA 1:3 DE 28 cm DE ESPESOR, APLANADO CON MORTERO CEMENTO-ARENA 1:3 , PLOMEADO, NIVELADO, DEMOLICIONES, CARGAS Y ACARREOS DENTRO DE LA OBRA, LIMPIEZA PREVIA Y FINAL.	PZA	8	$2,266.57	$18,132.56
7	CONSTRUCCIÓN DE LOSA DIAMANTE A BASE DE CONCRETO PREMEZCLADO MR= 45 KG/CM2, T.M.A. 3/4" (19 mm), GRAVA TRITURADA, REVENIMIENTO DE 8+-2.5 cm, RESISTENCIA RÁPIDA A 3 DÍAS, DE 25 CM DE ESPESOR, EN POZO DE VISITA, SECCIÓN DE 1.50 M X 1.50 M , INCLUYE: TRAZO, NIVELACIÓN, LIMPIEZA PREVIA Y PREPARACIÓN DE LA SUPERFICIE, COMPACTACIÓN DE TERRENO AL 95% DE SU PVSM, ESCARIFICADO, SUMINISTRO DE MATERIALES, DEMOLICIÓN Y RECONSTRUCCIÓN DE APROCHES, ESPUMA DE POLIURETANO DE ALTA DENSIDAD EN TODO EL PERÍMETRO EXTERIOR DE 1/2", ASÍ COMO EN LAS JUNTAS DIAGONALES PARA FORMAR 4 PARTES, BROCAL Y TAPA DE Fo. Fo. TIPO PESADO (165 KG), CIMBRADO, COLADO, VIBRADO, DESCIMBRADO, CURADO CON MEMBRANA QUÍMICA BASE AGUA, APLANADO FINO EN RECEPCIÓN DE BROCAL, CORTES CON CORTADORA DE DISCO DE 5 CM ENTRE JUNTAS DIAGONALES FORMANDO 8 PIEZAS Y SELLADO DE JUNTAS, CORTES RELLENOS CON MATERIAL PREFORMADO Y SELLADOR AUTONIVELANTE, MANO DE OBRA, CARGA Y ACARREOS DE MATERIAL DENTRO Y FUERA DE LA OBRA, LIMPIEZA FINAL, TRABAJO TERMINADO P.U.O.T	PZA	7	$10,137.99	$70,965.93
9	LIMPIEZA Y DESAZOLVE DE POZOS DE VISITA Y LÍNEAS DE ALCANTARILLADO EXISTENTE CON CAMIÓN TIPO VACTOR. INCLUYE: RESANE INTERIOR DEL POZO Y REMATE DE POZO CON TUBO SELLADOR FESTER Y MORTERO 1:3, MANO DE OBRA, SUMINISTRO DE AGUA EN PIPA, HERRAMIENTAS Y EQUIPO PARA SU CORRECTA EJECUCIÓN, LIMPIEZAS, RENTA DE CAMIÓN VACTOR HASTA LA CORRECTA LIMPIEZA DE LAS LÍNEAS EXISTENTES DE POZO A POZO ASÍ COMO EL TRASLADO DE LOS DESECHOS HASTA TIRADERO AUTORIZADO, LA UNIDAD DE MEDIDA SE PAGARA DE POZO A POZO.	LOTE	16	$10,627.04	$170,032.64

Obra: **OBRA COMPLEMENTARIA Y SEÑALIZACIÓN AV. MAHATMA GANDHI (CALZADA ORIENTE)**

Ubicación: **TRAMO: ENTRE BLVD. SIGLO XXI Y ACCESO A CENTRAL DE ABASTOS, AGUASCALIENTES Mpio.**

Contratista: **DIAZ SANCHEZ LUIS ROBERTO I.C. (860)**

No.	Concepto	Unidad	Cantidad	Precio Unitario	Importe Total
	GRUPO: **OBRA COMPLEMENTARIA Y SEÑALIZACION**				
	PARTIDA: **OBRA COMPLEMENTARIA**				
10	COMPACTACIÓN SOBRE MORTERO ASFALTICO TENDIDO EN APROCHES CON LOSAS DIAMANTES, CAIMANES, CAJAS DE VALVULAS, REGISTROS C.F.E. ETC. , CON EQUIPO LIGERO (PLANCHITA), INCLUYE: MANO DE OBRA Y EQUIPO, TRABAJO TERMINADO.	M2	7.32	$63.35	$463.72
			Totales por Partida		**$259,594.85**
	PARTIDA: **LIMPIEZAS**				
11	LIMPIEZA FINAL DE LA OBRA, INCLUYE: BARRIDO, CARGA, ACARREOS Y RETIRO DE ESCOMBROS FUERA DE LA OBRA, TRABAJO TERMINADO.	M2	569.3832214229	$12.51	$20,883.98
			Totales por Partida		**$20,883.98**
	PARTIDA: **SEÑALIZACION HORIZONTAL**				
14	SUMINISTRO Y APLICACIÓN DE PINTURA BASE SOLVENTE (ESMALTE) PARA MARCAS EN GUARNICIONES CLASIFICACION M-12.1, M12.2 APLICADA SOBRE GUARNICIONES Y DENTELLONES COLOR BLANCA Y/O AMARILLA, SEGÚN SE REQUIERA Y SEGÚN MANUAL DE SEÑALIZACIÓN VIAL Y DISPOSITIVOS DE SEGURIDAD SICT (S.C.T). SECADO AL TACTO EN 5 MIN Y AL DURO EN 30 MIN CON MICRO ESFERA , DESARROLLO DE 35 CM. INCLUYE: MATERIALES Y ESPECIFICACIONES QUE CUMPLAN CON LA NORMATIVA N-CMT-5-01-001/13, N-PRY-CAR-10-01-002/13 APLICADAS AL DIA DE HOY, TRAZO, MANO DE OBRA, LIMPIEZA PREVIA Y FINAL DE SUPERFICIE, EQUIPO NECESARIO PARA SU EJECUCIÓN, Y TODO LO NECESARIO PARA SU CORRECTA EJECUCIÓN, TRABAJO TERMINADO.	ML	1631.05	$39.53	$64,475.41
15	SUMINISTRO Y APLICACIÓN DE PINTURA TERMOPLASTICA ALQUIDALICA DE 120 MILESIMAS DE " (in) EN RAYA EN LA ORILLA DEL ARROYO VIAL CLASIFICACIÓN M - 3.3, CONTINUA IZQUIERDA, PARA VIALIDADES URBANAS DE FRENTE EN PISO, DE 10 CM DE ANCHO Y SEPARADA 15 CM. DE LA GUARNICION, A BASE DE PINTURA PARA TRAFICO COLOR BLANCO CON MICRO ESFERA SEGÚN MANUAL DE SEÑALIZACIÓN VIAL Y DISPOSITIVOS DE SEGURIDAD SICT (S.C.T)., INCLUYE: MATERIALES Y ESPECIFICACIONES QUE CUMPLAN CON LA NORMATIVA N-CMT-5-01-001/13, N-PRY-CAR-10-01-002/13 APLICADAS AL DIA DE HOY, MATERIAL APLICADO EN SU ESTADO DE FUSION A UNA TEMPERATURA MINIMA DE 204 C, LA SUPERFICIE DE CONCRETO O ASFALTO NO DEBE PRESENTAR UNA TEMPERATURA MENOR A LOS 10 C, ;TIEMPO DE SECADO EN RANGOS DE TEMPERATURA DE 10 C DEL SUSTRATO 2 MINUTOS, Y NO MAS DE 10 MINUTOS CUANDO EL SUSTRATO OSCILA ALREDEDOR DE 54C, TRAZO, ENMASCARILLADO, MANO DE OBRA, LIMPIEZA PREVIA Y FINAL DE SUPERFICIE, EQUIPO NECESARIO PARA SU EJECUCIÓN, Y TODO LO NECESARIO PARA SU CORRECTA EJECUCIÓN, TRABAJO TERMINADO.	ML	1578.2	$94.68	$149,423.98



Obra: **OBRA COMPLEMENTARIA Y SEÑALIZACIÓN AV. MAHATMA GANDHI (CALZADA ORIENTE)**

Ubicación: **TRAMO: ENTRE BLVD. SIGLO XXI Y ACCESO A CENTRAL DE ABASTOS, AGUASCALIENTES Mpio.**

Contratista: **DIAZ SANCHEZ LUIS ROBERTO I.C. (860)**


No.	Concepto	Unidad	Cantidad	Precio Unitario	Importe Total
	GRUPO: **OBRA COMPLEMENTARIA Y SEÑALIZACION**				
	PARTIDA: **SEÑALIZACION HORIZONTAL**				
16	SUMINISTRO Y APLICACIÓN DE PINTURA TERMOPLASTICA ALQUIDALICA DE 120 MILESIMAS DE " (in) EN RAYA GUIA EN ZONAS DE TRANSICION CLASIFICACIÓN M - 4, PARA INDICAR LÍNEA GUÍA EN ZONA DE TRANSICIÓN DE FRENTE EN PISO, DESARROLLO DE 2.00 X 0.10 MTS, CON UNA SEPARACIÓN DE 4.00 MTS ENTRE SI PROMEDIO, A BASE DE PINTURA PARA TRAFICO COLOR BLANCO CON MICRO ESFERA SEGÚN MANUAL DE SEÑALIZACIÓN VIAL Y DISPOSITIVOS DE SEGURIDAD SICT (S.C.T)., MCA. COMEX O SIMILAR, SECADO AL TACTO EN 5 MIN Y AL DURO EN 30 MIN.INCLUYE: MATERIALES Y ESPECIFICACIONES QUE CUMPLAN CON LA NORMATIVA N-CMT-5-01-001/13, N-PRY-CAR-10-01-002/13 APLICADAS AL DIA DE HOY, MATERIAL APLICADO EN SU ESTADO DE FUSION A UNA TEMPERATURA MINIMA DE 204 C, LA SUPERFICIE DE CONCRETO O ASFALTO NO DEBE PRESENTAR UNA TEMPERATURA MENOR A LOS 10 C, ;TIEMPO DE SECADO EN RANGOS DE TEMPERATURA DE 10 C DEL SUSTRATO 2 MINUTOS, Y NO MAS DE 10 MINUTOS CUANDO EL SUSTRATO OSCILA ALREDEDOR DE 54C, TRAZO, ENMASCARILLADO, MANO DE OBRA, LIMPIEZA PREVIA Y FINAL DE SUPERFICIE, EQUIPO NECESARIO PARA SU EJECUCIÓN, Y TODO LO NECESARIO PARA SU CORRECTA EJECUCIÓN, TRABAJO TERMINADO.	ML	125.35	$94.68	$11,868.14
17	SUMINISTRO Y APLICACIÓN DE PINTURA TERMOPLASTICA ALQUIDALICA DE 120 MILESIMAS DE " (in) EN RAYA DE ALTO CLASIFICACIÓN M - 6, PARA INDICAR ALTO EN CRUCEROS, COLOR BLANCO, REFLEJANTE CON MICRO ESFERA DE VIDRIO EN PROPORCIÓN SEGÚN MANUAL DE SEÑALIZACIÓN VIAL Y DISPOSITIVOS DE SEGURIDAD SICT (S.C.T). DE 0.60 MTS DE ANCHO DE LONGITUD VARIABLE, INCLUYE: MATERIALES Y ESPECIFICACIONES QUE CUMPLAN CON LA NORMATIVA N-CMT-5-01-001/13, N-PRY-CAR-10-01-002/13 APLICADAS AL DIA DE HOY, MATERIAL APLICADO EN SU ESTADO DE FUSION A UNA TEMPERATURA MINIMA DE 204 C, LA SUPERFICIE DE CONCRETO O ASFALTO NO DEBE PRESENTAR UNA TEMPERATURA MENOR A LOS 10 C, ;TIEMPO DE SECADO EN RANGOS DE TEMPERATURA DE 10 C DEL SUSTRATO 2 MINUTOS, Y NO MAS DE 10 MINUTOS CUANDO EL SUSTRATO OSCILA ALREDEDOR DE 54C, TRAZO, ENMASCARILLADO, MANO DE OBRA, LIMPIEZA PREVIA Y FINAL DE SUPERFICIE, EQUIPO NECESARIO PARA SU EJECUCIÓN, Y TODO LO NECESARIO PARA SU CORRECTA EJECUCIÓN, TRABAJO TERMINADO.	ML	49.4	$368.61	$18,209.33
18	SUMINISTRO Y APLICACIÓN DE PINTURA TERMOPLASTICA ALQUIDALICA DE 120 MILESIMAS DE " (in) EN RAYA PARA CRUCE PEATONAL CLASIFICACIÓN M - 7.1, PARA INDICAR " CRUCE PEATONAL EN VIAS PRIMARIAS", COLOR AMARILLO, REFLEJANTE CON MICRO ESFERA DE VIDRIO EN PROPORCIÓN SEGÚN MANUAL DE SEÑALIZACIÓN VIAL Y DISPOSITIVOS DE SEGURIDAD SICT (S.C.T). DE 0.40 MTS DE ANCHO Y 3.5 MTS. DE LONGITUD POR EL ANCHO DE LA VIALIDAD, CON UNA SEPARACIÓN DE 0.40 MTS. ENTRE ELLAS, INCLUYE: MATERIALES Y ESPECIFICACIONES QUE CUMPLAN CON LA NORMATIVA N-CMT-5-01-001/13, N-PRY-CAR-10-01-002/13 APLICADAS AL DIA DE HOY, MATERIAL APLICADO EN SU ESTADO DE FUSION A UNA TEMPERATURA MINIMA DE 204 C, LA SUPERFICIE DE CONCRETO O ASFALTO NO DEBE PRESENTAR UNA TEMPERATURA MENOR A LOS 10 C, ;TIEMPO DE SECADO EN RANGOS DE TEMPERATURA DE 10 C DEL SUSTRATO 2 MINUTOS, Y NO MAS DE 10 MINUTOS CUANDO EL SUSTRATO OSCILA ALREDEDOR DE 54C, TRAZO, ENMASCARILLADO, MANO DE OBRA, LIMPIEZA PREVIA Y FINAL DE SUPERFICIE, EQUIPO NECESARIO PARA SU EJECUCIÓN, Y TODO LO NECESARIO PARA SU CORRECTA EJECUCIÓN, TRABAJO TERMINADO.	M2	193.4	$651.96	$126,089.06

Obra: **OBRA COMPLEMENTARIA Y SEÑALIZACIÓN AV. MAHATMA GANDHI (CALZADA ORIENTE)**

Ubicación: **TRAMO: ENTRE BLVD. SIGLO XXI Y ACCESO A CENTRAL DE ABASTOS, AGUASCALIENTES Mpio.**

Contratista: **DIAZ SANCHEZ LUIS ROBERTO I.C. (860)**

No.	Concepto	Unidad	Cantidad	Precio Unitario	Importe Total
	GRUPO: **OBRA COMPLEMENTARIA Y SEÑALIZACION**				
	PARTIDA: **SEÑALIZACION HORIZONTAL**				
19	SUMINISTRO Y APLICACIÓN DE PINTURA TERMOPLASTICA ALQUIDALICA DE 120 MILESIMAS DE " (in) EN FLECHAS CLASIFICACIÓN M - 11.1, "FLECHA SENCILLA" PARA INDICAR SENTIDO DE CIRCULACIÓN , EN VIALIDADES PARA VELOCIDAD MENOR A 60KM POR HORA DIMENSION NORMATIVA SEGUN MANUAL DE SEÑALIZACIÓN VIAL Y DISPOSITIVOS DE SEGURIDAD SICT (SCT) Y/O (VER PLANO DE SEÑALAMIENTOS), COLOR BLANCO, REFLEJANTE CON MICRO ESFERA DE VIDRIO EN PROPORCIÓN SEGÚN NORMA SCT, INCLUYE: MATERIALES Y ESPECIFICACIONES QUE CUMPLAN CON LA NORMATIVA N-CMT-5-01-001/13, N-PRY-CAR-10-01-002/13 APLICADAS AL DIA DE HOY, MATERIAL APLICADO EN SU ESTADO DE FUSION A UNA TEMPERATURA MINIMA DE 204 C, LA SUPERFICIE DE CONCRETO O ASFALTO NO DEBE PRESENTAR UNA TEMPERATURA MENOR A LOS 10 C, ;TIEMPO DE SECADO EN RANGOS DE TEMPERATURA DE 10 C DEL SUSTRATO 2 MINUTOS, Y NO MAS DE 10 MINUTOS CUANDO EL SUSTRATO OSCILA ALREDEDOR DE 54C, TRAZO, ENMASCARILLADO, MANO DE OBRA, LIMPIEZA PREVIA Y FINAL DE SUPERFICIE, EQUIPO NECESARIO PARA SU EJECUCIÓN, Y TODO LO NECESARIO PARA SU CORRECTA EJECUCIÓN, TRABAJO TERMINADO.	PZA	23	$2,442.51	$56,177.73
20	SUMINISTRO Y APLICACIÓN DE PINTURA TERMOPLASTICA ALQUIDALICA DE 120 MILESIMAS DE " (in) EN FLECHAS CLASIFICACIÓN M - 11.1, " FLECHA CABEZA DOBLE" PARA INDICAR SENTIDO DE CIRCULACIÓN (VUELTA IZQUIERDA O DERECHA), EN VIALIDADES PARA VELOCIDAD MENOR A 60KM POR HORA SEGUN MANUAL DE SEÑALIZACIÓN VIAL Y DISPOSITIVOS DE SEGURIDAD SICT (SCT), (VER PLANO DE SEÑALAMIENTOS), EN COLOR BLANCO, REFLEJANTE CON MICRO ESFERA DE VIDRIO EN PROPORCIÓN SEGÚN NORMA SCT, INCLUYE: MATERIALES Y ESPECIFICACIONES QUE CUMPLAN CON LA NORMATIVA N-CMT-5-01-001/13, N-PRY-CAR-10-01-002/13 APLICADAS AL DIA DE HOY, MATERIAL APLICADO EN SU ESTADO DE FUSION A UNA TEMPERATURA MINIMA DE 204 C, LA SUPERFICIE DE CONCRETO O ASFALTO NO DEBE PRESENTAR UNA TEMPERATURA MENOR A LOS 10 C, ;TIEMPO DE SECADO EN RANGOS DE TEMPERATURA DE 10 C DEL SUSTRATO 2 MINUTOS, Y NO MAS DE 10 MINUTOS CUANDO EL SUSTRATO OSCILA ALREDEDOR DE 54C, TRAZO, ENMASCARILLADO, MANO DE OBRA, LIMPIEZA PREVIA Y FINAL DE SUPERFICIE, EQUIPO NECESARIO PARA SU EJECUCIÓN, Y TODO LO NECESARIO PARA SU CORRECTA EJECUCIÓN, TRABAJO TERMINADO.	PZA	1	$4,884.01	$4,884.01
21	SUMINISTRO Y APLICACIÓN DE PINTURA TERMOPLASTICA ALQUIDALICA DE 120 MILESIMAS DE " (in) EN LETRAS Y NUMEROS CLASIFICACIÓN M - 11.1 "LETRAS Y NUMEROS" EN VIALIDADES PARA VELOCIDAD MENOR A 60KM POR HORA SEGUN MANUAL DE SEÑALIZACIÓN VIAL Y DISPOSITIVOS DE SEGURIDAD SICT (SCT), (VER PLANO DE SEÑALAMIENTOS) EN COLOR BLANCO, REFLEJANTE CON MICRO ESFERA DE VIDRIO EN PROPORCIÓN SEGÚN NORMA SCT DE (VER DETALLES EN PLANOS) INCLUYE: MATERIALES Y ESPECIFICACIONES QUE CUMPLAN CON LA NORMATIVA N-CMT-5-01-001/13, N-PRY-CAR-10-01-002/13 APLICADAS AL DIA DE HOY, MATERIAL APLICADO EN SU ESTADO DE FUSION A UNA TEMPERATURA MINIMA DE 204 C, LA SUPERFICIE DE CONCRETO O ASFALTO NO DEBE PRESENTAR UNA TEMPERATURA MENOR A LOS 10 C, ;TIEMPO DE SECADO EN RANGOS DE TEMPERATURA DE 10 C DEL SUSTRATO 2 MINUTOS, Y NO MAS DE 10 MINUTOS CUANDO EL SUSTRATO OSCILA ALREDEDOR DE 54C, TRAZO, ENMASCARILLADO, MANO DE OBRA, LIMPIEZA PREVIA Y FINAL DE SUPERFICIE, EQUIPO NECESARIO PARA SU EJECUCIÓN, Y TODO LO NECESARIO PARA SU CORRECTA EJECUCIÓN, TRABAJO TERMINADO.	PZA	204	$347.08	$70,804.32

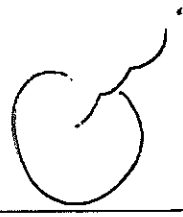

Obra: **OBRA COMPLEMENTARIA Y SEÑALIZACIÓN AV. MAHATMA GANDHI (CALZADA ORIENTE)**

Ubicación: **TRAMO: ENTRE BLVD. SIGLO XXI Y ACCESO A CENTRAL DE ABASTOS, AGUASCALIENTES Mpio.**

Contratista: **DIAZ SANCHEZ LUIS ROBERTO I.C. (860)**

No.	Concepto	Unidad	Cantidad	Precio Unitario	Importe Total
	GRUPO: **OBRA COMPLEMENTARIA Y SEÑALIZACION**				
	PARTIDA: **SEÑALIZACION HORIZONTAL**				
23	SUMINISTRO Y COLOCACIÓN DE VIALETA STANDARD (S-200) DE 10X10CM. COLOR: CUERPO AMARILLO Y/O BLANCO Y REFLEJANTE AMARILLO 1 CARA MARCA SEA O SIMILAR EN CALIDAD Y ESPECIFICACIONES DE FICHA TÉCNICA, FIJADO EN PAVIMENTO CON SISTEMA DE SUJECIÓN DE ALTO AGARRE PEGAMENTO EPOXICO 100 A/B (RESINA EPÓXICA/RESINA POLIAMIDA MODIFICADA), RESISTENTE A ALTA TEMPERATURA (VER PLANO DE DETALLES DE SEÑALAMIENTOS HORIZONTAL), INCLUYE: LIMPIEZA PREVIA Y FINAL DE LA SUPERFICIE, PREPARACIÓN DE LA SUPERFICIE, TRAZO, ALINEACIÓN, Y TODO LO NECESARIO PARA SU CORRECTA EJECUCIÓN, TRABAJO TERMINADO.	PZA	210	$83.50	$17,535.00
24	SUMINISTRO Y COLOCACION DE VIALETA SOLAR DE 10X10CM. COLOR: CUERPO ALUMINIO 3 LED DOS CARAS REFLEJANTES MARCA CREATIVAL VT-29 O SIMILAR EN CALIDAD Y ESPECIFICACIONES DE FICHA TÉCNICA, FIJADO EN PAVIMENTO CON SISTEMA DE SUJECIÓN DE ALTO AGARRE PEGAMENTO EPOXICO 100 A/B (RESINA EPÓXICA/RESINA POLIAMIDA MODIFICADA), RESISTENTE A ALTA TEMPERATURA (VER PLANO DE DETALLES DE SEÑALAMIENTOS HORIZONTAL), INCLUYE: LIMPIEZA PREVIA Y FINAL DE LA SUPERFICIE+C92, PREPARACIÓN DE LA SUPERFICIE, TRAZO, ALINEACIÓN, Y TODO LO NECESARIO PARA SU CORRECTA EJECUCIÓN, TRABAJO TERMINADO.	PZA	105	$596.61	$62,644.05

Totales por Partida		**$582,111.03**
Totales por Grupo		**$871,349.12**
Totales Presup.		**$871,349.12**
Anticipo	**+**	**$261,404.73**
Amortizac. Ant.	**-**	**$261,404.73**
SubTotal. Ant.	**=**	**$871,349.12**
IVA	**+**	**$139,415.86**
Total	**=**	**$1,010,764.98**

H. AYUNTAMIENTO CONSTITUCIONAL DEL MUNICIPIO DE AGUASCALIENTES 2021-2024

PRESUPUESTO MODIFICADO

Aguascalientes

Obra: OBRA COMPLEMENTARIA Y SEÑALIZACIÓN AV. MAHATMA GANDHI (CALZADA ORIENTE)

Ubicación: TRAMO: ENTRE BLVD. SIGLO XXI Y ACCESO A CENTRAL DE ABASTOS, AGUASCALIENTES Mpio.

Contratista: DIAZ SANCHEZ LUIS ROBERTO I.C. (860)

Grupo	Partida	Importe
OBRA COMPLEMENTARIA Y SEÑALIZACION		
	PRELIMINARES	$8,759.26
	OBRA COMPLEMENTARIA	$259,594.85
	LIMPIEZAS	$20,883.98
	SEÑALIZACION HORIZONTAL	$582,111.03
	Subtotal por Grupo	**$871,349.12**

Totales Presup.		**$871,349.12**
Anticipo	+	**$261,404.73**
Amortizac. Ant.	-	**$261,404.73**
SubTotal. Ant.	=	**$871,349.12**
IVA	+	**$139,415.86**
Total	=	**$1,010,764.98**



H. AYUNTAMIENTO DE AGUASCALIENTES
SECRETARÍA DE OBRAS PÚBLICAS
DIRECCIÓN DE SUPERVISIÓN DE OBRA

Aguascalientes
LA CIUDAD DE TU VIDA


MEMORIA FOTOGRÁFICA


OBRA:	**OBRA COMPLEMENTARIA Y SEÑALIZACIÓN AV. MAHATMA GANDHI (CALZADA ORIENTE), TRAMO: ENTRE BLVD. SIGLO XXI Y ACCESO A CENTRAL DE ABASTOS, AGUASCALIENTES Mpio.**		
NO. DE CONTRATO:	**FISMDF-0096-2022**	CONTRATISTA:	**DIAZ SANCHEZ LUIS ROBERTO I.C.**

INICIO





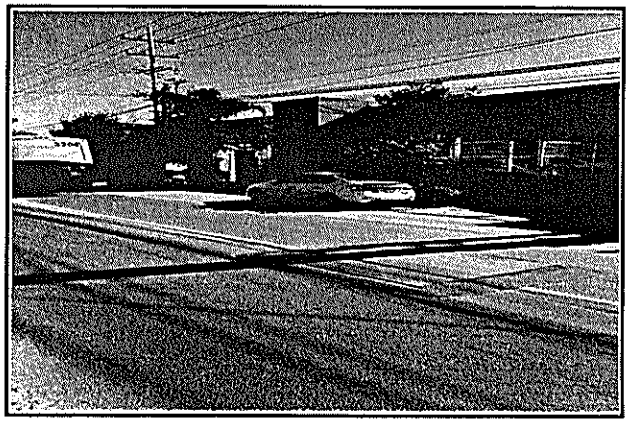

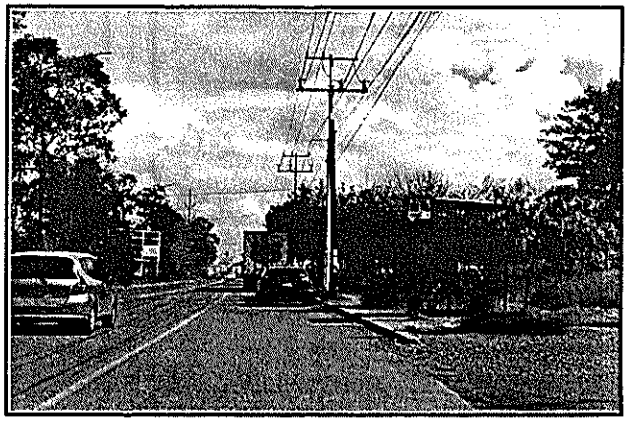

I.C. LAURA CECILIA MARTINEZ ALBA
RESIDENTE DE SUPERVISIÓN

H. AYUNTAMIENTO DE AGUASCALIENTES

SECRETARÍA DE OBRAS PÚBLICAS

DIRECCIÓN DE SUPERVISIÓN DE OBRA

Aguascalientes
LA CIUDAD DE TU VIDA


MEMORIA FOTOGRÁFICA


OBRA:	OBRA COMPLEMENTARIA Y SEÑALIZACIÓN AV. MAHATMA GANDHI (CALZADA ORIENTE), TRAMO: ENTRE BLVD. SIGLO XXI Y ACCESO A CENTRAL DE ABASTOS, AGUASCALIENTES Mpio.		
NO. DE CONTRATO:	FISMDF-0096-2022	CONTRATISTA:	DIAZ SANCHEZ LUIS ROBERTO I.C.

PROCESO





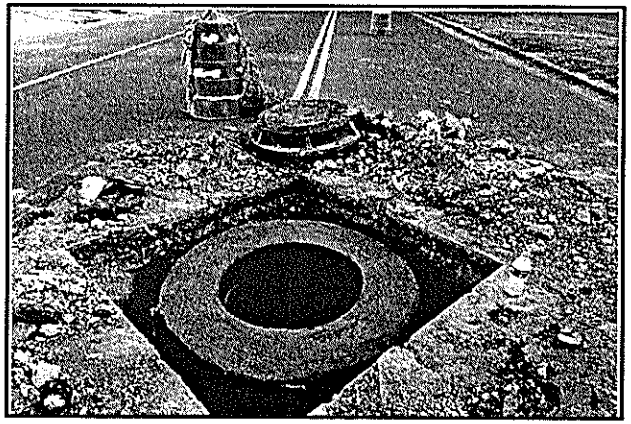

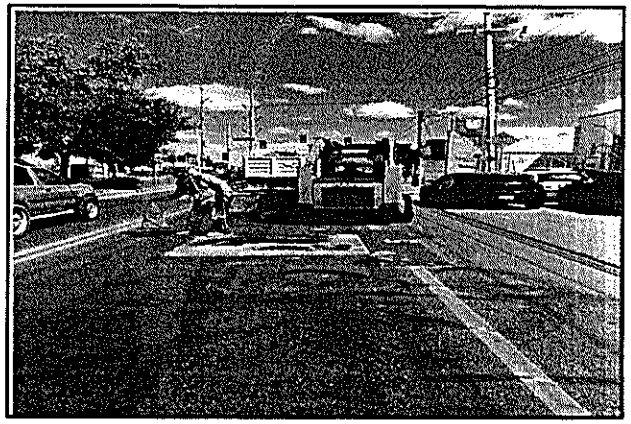

I.C. LAURA CECILIA MARTINEZ ALBA
RESIDENTE DE SUPERVISIÓN

H. AYUNTAMIENTO DE AGUASCALIENTES

SECRETARÍA DE OBRAS PÚBLICAS


DIRECCIÓN DE SUPERVISIÓN DE OBRA

Aguascalientes
LA CIUDAD DE TU VIDA


MEMORIA FOTOGRÁFICA

OBRA:	**OBRA COMPLEMENTARIA Y SEÑALIZACIÓN AV. MAHATMA GANDHI (CALZADA ORIENTE), TRAMO: ENTRE BLVD. SIGLO XXI Y ACCESO A CENTRAL DE ABASTOS, AGUASCALIENTES Mpio.**		
NO. DE CONTRATO:	**FISMDF-0096-2022**	CONTRATISTA:	**DIAZ SANCHEZ LUIS ROBERTO I.C.**

FINAL

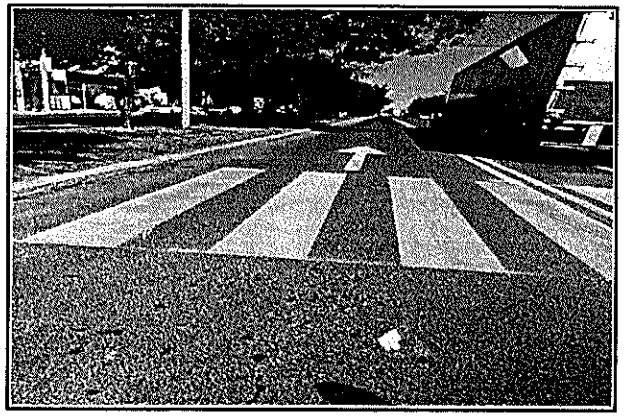



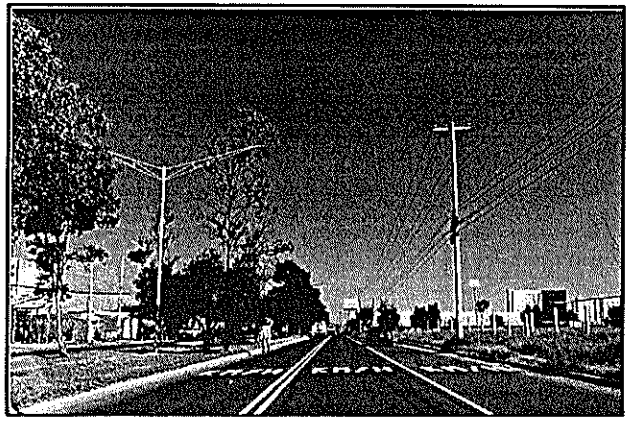



I.C. LAURA CECILIA MARTINEZ ALBA
RESIDENTE DE SUPERVISIÓN

EXPEDIENTE MODIFICADO

SECRETARÍA DE OBRAS PÚBLICAS

DIRECCIÓN DE SUPERVISIÓN DE OBRA

EJERCICIO: 2022

N° DE CONTRATO: FISMDF-0096-2022

NOMBRE DE LA OBRA: OBRA COMPLEMENTARIA Y SEÑALIZACIÓN AV. MAHATMA GANDHI (CALZADA ORIENTE), TRAMO: ENTRE BLVD. SIGLO XXI Y ACCESO A CENTRAL DE ABASTOS, AGUASCALIENTES Mpio.

MONTO MODIFICADO FINAL: $1,010,764.98


VOLUMEN	UNIDAD	COMPONENTE DE LA OBRA	MONTO
6.57	M³	DEMOLICIÓN A MANO Y MECÁNICA DE PAVIMENTO HIDRÁULICO Y/O	$ 8,759.26
7.00	PZA	CONSTRUCCIÓN DE LOSA DIAMANTE A BASE DE CONCRETO	$ 259,594.85
1669.38	M2	LIMPIEZA FINAL DE LA OBRA, INCLUYE: BARRIDO, CARGA, ACARREOS Y	$ 20,883.98
1578.20	ML	SUMINISTRO Y APLICACIÓN DE PINTURA TERMOPLASTICA ALQUIDALICA	$ 582,111.03

MONTO BASE: $ 871,349.12

IVA: $ 139,415.86

TOTAL: $ 1,010,764.98

I.C. Laura Cecilia Martínez Alba
RESIDENTE DE SUPERVISIÓN

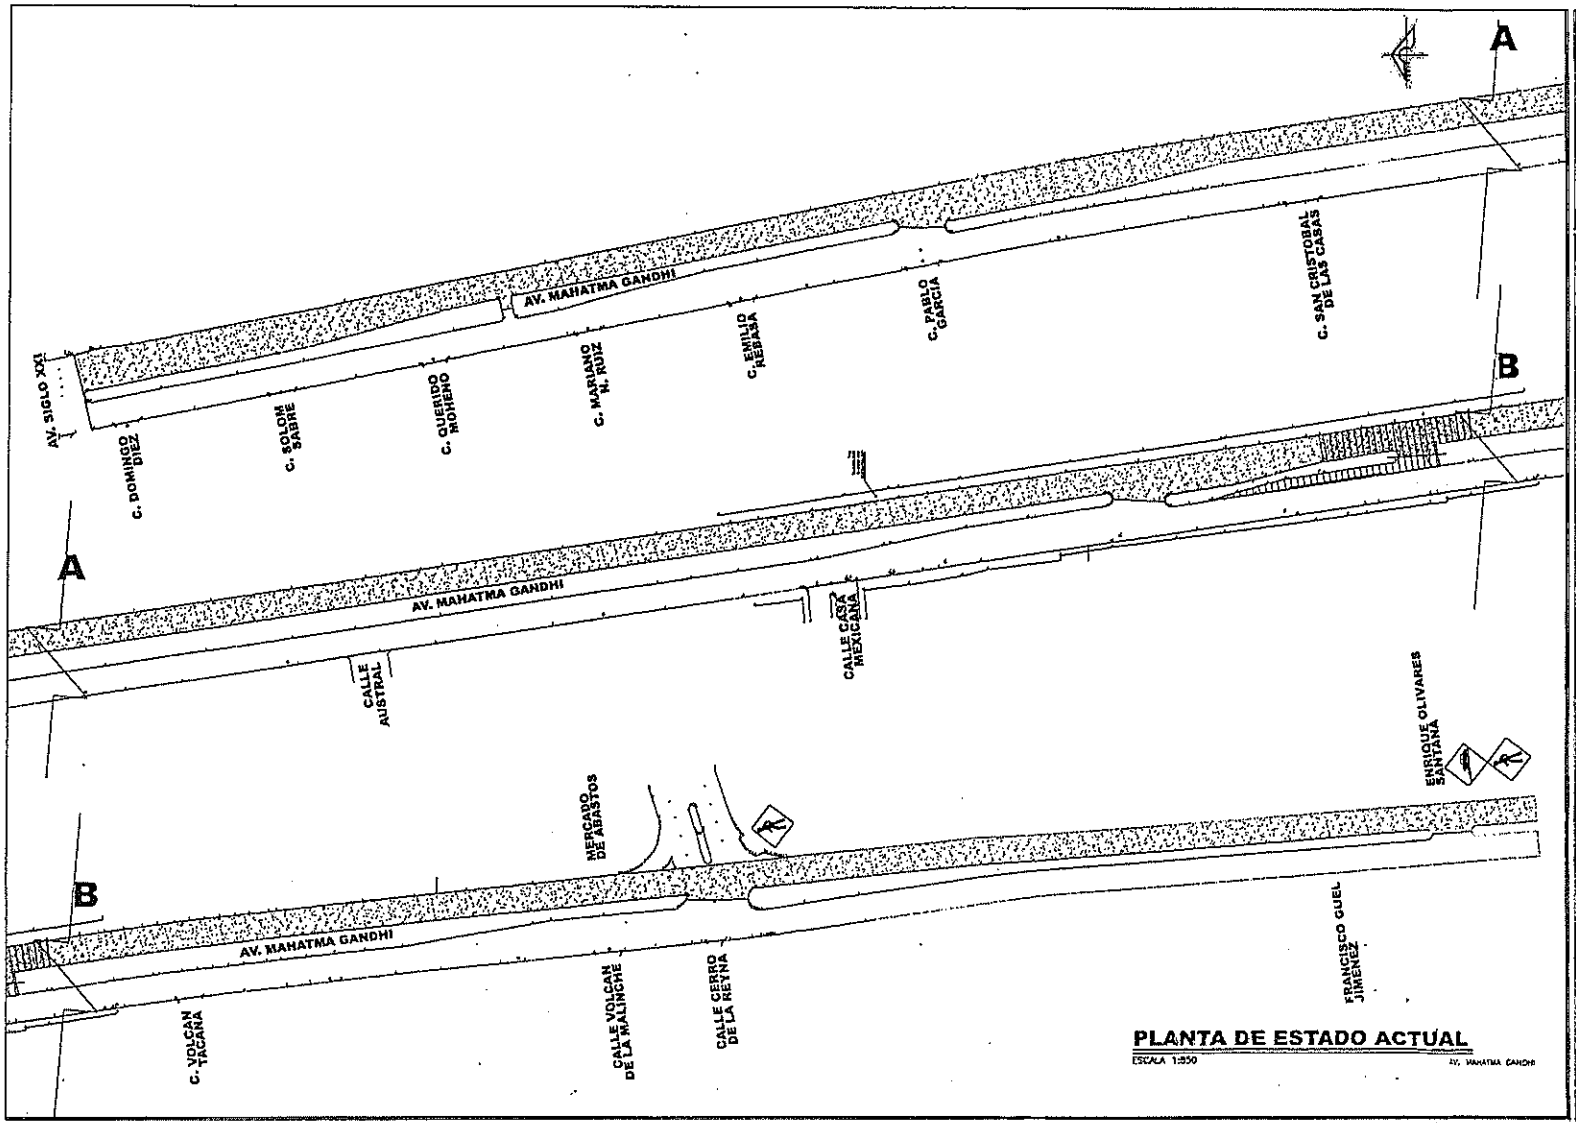


PLANTA DE ESTADO ACTUAL

ESCALA 1:850

AV. MAHATMA GANDHI

LOCALIZACION:

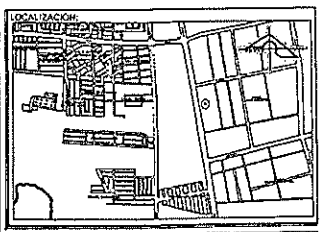

SIMBOLOGIA

SIMBOLOGIA

- LIMITE DE PROYECTO
- BANQUETAS EXISTENTES
- PARAMENTO EXISTENTE
- CARPETA ASFALTICA EXISTENTE
- POZO DE VISITA EXISTENTE
- LIMITE DE PROYECTO
- BANQUETAS EXISTENTES
- PARAMENTO EXISTENTE
- REGISTRO CFE (RE-CFE)
- ALUMBRADO
- POSTES CFE
- POSTES TELMEX
- POZO DE VISITA EXISTENTE
- ASPERSOR

La Dirección de Planeación y Proyectos solo autoriza el proyecto ejecutivo, no es responsable de la correcta ejecución de la obra. Este documento no tiene validez si no presenta los firmas de los responsables para su autorización, así como los sellos respectivos.

PRESIDENTE MUNICIPAL
M.P.P. Leonardo Montañez Castro
ENCARGADA DE DESPACHO DE LA SOPMA
Arq. Gloria Guadalupe Castillo González

REV	FECHA	OBSERVACIONES

Vo. Bo. DE LA DEPENDENCIA

RESP. DE PROY. EXTERNO		LOGO EXTERNO
CED. PROFESIONAL		
PROYECTO	REVISO	AUTORIZO

Dirección de Planeación y Proyectos de Obra y Secretaría de Obras Públicas

PROYECTISTA	COORDINADOR
ARQ. ALVARO DE HEZ CONTRERAS	ARQ. ALEJANDRO JAIME LEAL
FECHA OCT	DIRECTOR
ARQ. J. JESUS SALAZAR GONZALEZ	M. en ARQ. JOSE LUIS JIMENEZ GARCIA


PROYECTO
OBRA COMPLEMENTARIA Y SEÑALETICA AV. MAHATMA GANDHI

UBICACION
CALZADA ORIENTE DE ENTRE AV. SIGLO XXI Y ACCESO A CENTRAL DE ABASTOS

CONTENIDO
ESTADO ACTUAL Y LEVANTAMIENTO TOPOGRAFICO


CLAVE	No. PLANO
EA 01	02
FECHA MAR 2022	ESCALA INDICADA
ACOTACION METROS	No. EXP. E-000-22

Aguascalientes
LA CIUDAD DE TU VIDA

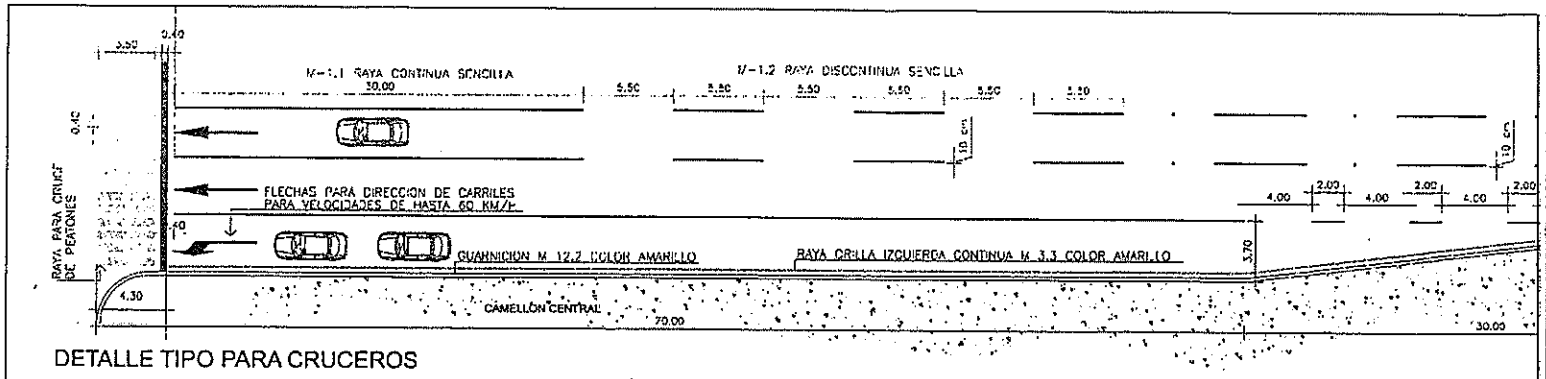

DETALLE TIPO PARA CRUCEROS CON CARGA VEHICULAR BAJA/MEDIA

COTAS: cm.

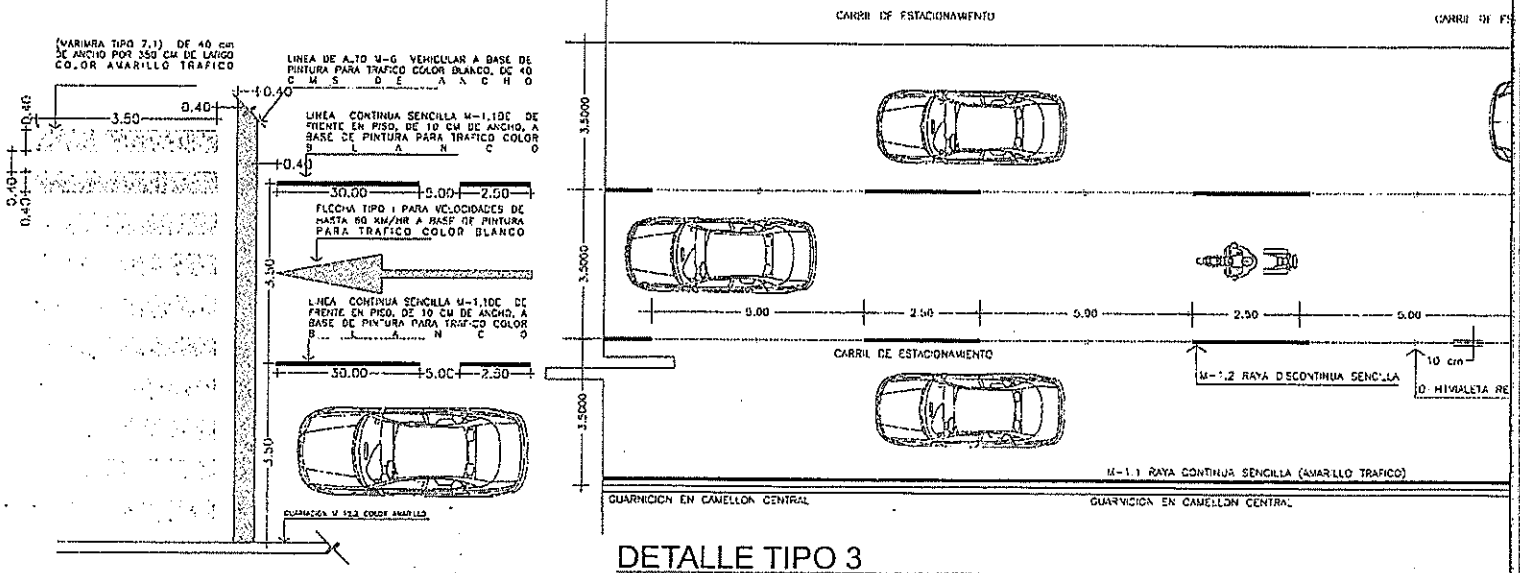


DETALLE TIPO 2

TRAZO PINTURA EN CRUCEROS SIN ESCALA

DETALLE TIPO 3

PARA VELOCIDADES MENOR A 60 KM/HR S/E
LINEA DISCONTINUA DE 2.50 MTS ESPACIO 5 MTS
ESPESOR 10CM

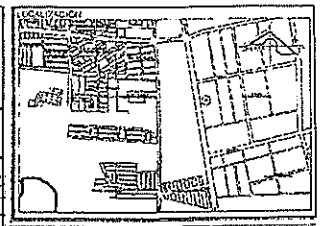

SIMBOLOGIA

NOTA:

Nota1:

Se aplicará en todos los señalamientos horizontales pintura para trafico termoplastica base alquidralica de secado rápido, que cumpla con las especificaciones n-cmt-5-01-001/05, n-pry-car-10-01-002/13 de la SCT aplicadas al día de hoy.

Nota2:
Dosificación de micro esfera

La cantidad de esferas de vidrio en la película de pintura en húmedo, según su tipo, será la que se indica en la Tabla.

Nota 3:

Se aplicará solo en señalamiento de guarnicion conpintura para trafico base solvente tipo alquidal de secado rápido, que cumpla con las especificaciones n-cmt-5-01-001/05, n-pry-car-10-01-002/13 de la SCT aplicadas al día de hoy.

TABLA 8: Cantidad de esferas de vidrio en la pelicula de pintura en humedo.

CANTIDAD DE ESFERAS DE VIDRIO EN LA PELICULA DE PINTURA EN HUMEDO				
TIPO DE PINTURA	ESPESOR DE LA PELICULA DE PINTURA EN HÚMEDO (mm)	CANTIDAD DE ESFERAS KG/LT		TIPO DE GRANULOMETRÍA
		MEZCLADAS	SOBRE CAPEADAS, MIN/MAX	
BASE SOLVENTE	0.20 A 0.30	-	0.230	1
BASE AGUA	0.20 A 0.30	-	0.230	1 Y 2
TERMOPLASTICA	1.70 A 3.00	-	0.130	4

La Dirección de Planeación y Proyectos solo autoriza el proyecto ejecutivo, no es responsable de la correcta ejecución de la obra. Este documento no tiene validez si no presenta las firmas de los responsables para su autorización, así como los sellos respectivos.

PRESIDENTE MUNICIPAL
M.P.P. Leonardo Montañez Castro
ENCARGADA DE DESPACHO DE LA SOPSA
Arq. Gloria Guadalupe Castillo González

REV	FECHA	OBSERVACIONES

RESP DE PROY. EXTERNO		LOGO EXTERNO
CED PROFESIONAL		
PROYECTO	REVISO	AUTORIZO


Dirección de Planeación y Proyectos de Obra — Secretaría de Obras Públicas


PROYECTO	COORDINADOR
ARQ. ALFREDO [illegible]	ARQ. M. RICARDO JAIME LEAL
JEFE DE DEPTO.	DIRECTOR
ARQ. [illegible]	M. en ARQ. [illegible]


PROYECTO
OBRA COMPLEMENTARIA Y SEÑALETICA AV. MAHATMA GANDHI
UBICACIÓN
CALZADA ORIENTE DE ENTRE AV. SIGLO XXI Y ACCESO A CENTRAL DE ABASTOS
CONTENIDO
DETALLES SEÑALETICA HORIZONTAL

CLAVE	No. PLANO
DSH 01	04
FECHA: MAR 2022	ESCALA: INDICADA
ACOTACION: METROS	No. EXP.: E-000-22

Aguascalientes
LA CIUDAD DE TU VIDA

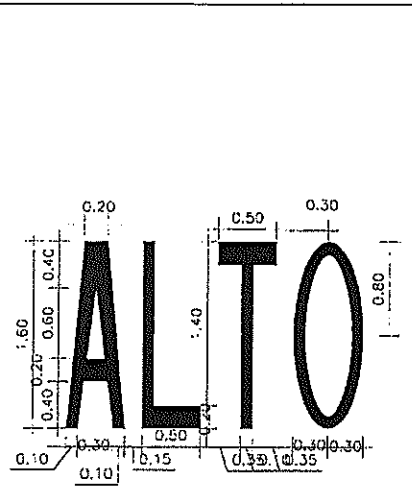


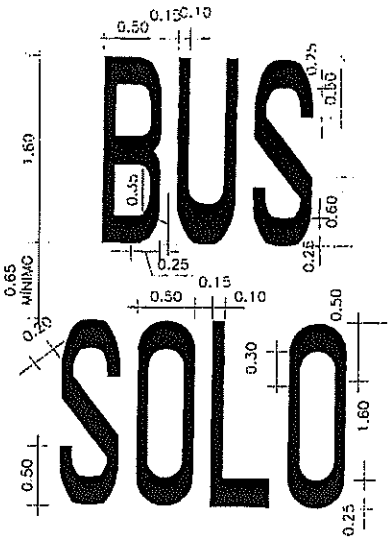

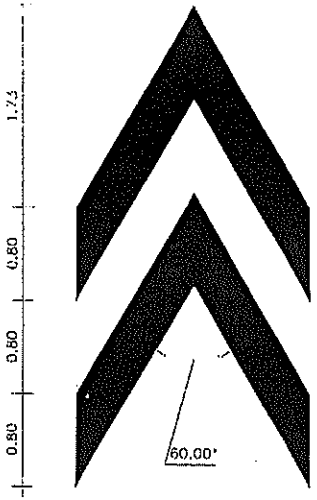

PARADA DE AUTOBUS

V – 11.2 "FLECHA SIN CUERPO" PARA ESTABLECER LUGARES DE PARADA COLOR BLANCO, REFLEJANTE

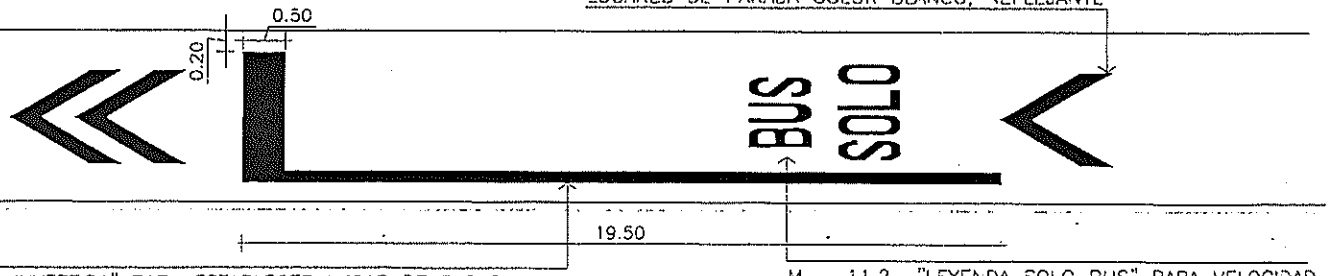


M – 11.4 "L INVERTIDA" PARA ESTABLECER LUGAR DE PARADA SOBRE PAVIMENTO EN VIALIDADES PARA VELOCIDAD MENOR A 60KM POR HORA

M – 11.2 "LEYENDA SOLO BUS" PARA VELOCIDAD MENOR A 60KM POR HORA DIFERENTES DIMENSIONES, COLOR BLANCO REFLEJANTE

SEÑALIZACION HORIZONTAL SOLO BUS

SIN ESCALA

COTAS: M.

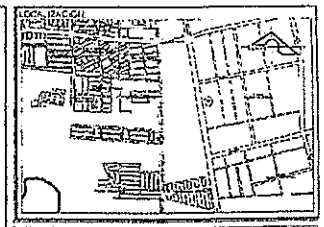

SIMBOLOGIA

NOTA:

Nota1:

Se aplicará en todos los señalamientos horizontales pintura para trafico termoplastica base alquidalica de secado rápido, que cumpla con las especificaciones n-cmt-5-01-001/05, n-pry-car-10-01-002/13 de la SCT aplicadas al dia de hoy.

Nota2:
Dosificación de micro esfera

La cantidad de esferas de vidrio en la pelicula de pintura en húmedo, según su tipo, será la que se indica en la Tabla.

Nota 3:

Se aplicará solo en señalamiento de guarnicion con pintura para trafico base solvente tipo alquidal de secado rápido, que cumpla con las especificaciones n-cmt-5-01-001/05, n-pry-car-10-01-002/13 de la SCT aplicadas al dia de hoy.


TABLA 8: Cantidad de esferas de vidrio en la pelicula de pintura en humedo.

CANTIDAD DE ESFERAS DE VIDRIO EN LA PELICULA DE PINTURA EN HUMEDO				
TIPO DE PINTURA	ESPESOR DE LA PELICULA DE PINTURA EN HUMEDO mm	CANTIDAD DE ESFERAS M2/KG		TIPO DE GRANULOMETRIA
		RIEGO SIMPLE	RIEGO DOBLE	
BASE SOLVENTE	0.203 a 0.50	-	0.315	I
BASE AGUA	0.254 a 0.50	-	0.330	I o II
TERMOPLASTICO	1.524 a 2.00	-	0.220	II


La Dirección de Planeación y Proyectos solo autoriza el proyecto ejecutivo, no es responsable de la correcta ejecución de la obra. Este documento no tiene validez si no presenta las firmas de los responsables para su autorización, así como los sellos respectivos.

PRESIDENTE MUNICIPAL: M.P.P. Leonardo Montañez Castro. ENCARGADA DE DESPACHO DE LA SOPMA: Arq. Gloria Guadalupe Castillo González			PESP DE PROY. EXTERNO	LOGO EXTERNO	Dirección de Planeación y Proyectos de Obra / Secretaría de Obras Públicas	PROYECTO: OBRA COMPLEMENTARIA Y SEÑALETICA AV. MAHATMA GANDHI	CLAVE: DSH 02	NO. PLANO: 05
	SEC. FECHA	OBSERVACIONES	CED. PROFESIONAL		COORDINADOR: ARQ. ALEJANDRO JAIME LEAL	UBICACION: CALZADA ORIENTE DE ENTRE AV. SIGLO XXI Y ACCESO A CENTRAL DE ABASTOS	FECHA: MAR 2022	ESCALA: INDICADA
			PROYECTO / REVISO / AUTORIZO		DIRECTOR: M. en ARQ. JOSE LUIS JIMENEZ GARCIA	CONTENIDO: DETALLES SEÑALETICA HORIZONTAL	ACOTACION: METROS	No. SXF: E-000-22


Aguascalientes
LA CIUDAD DE TU VIDA

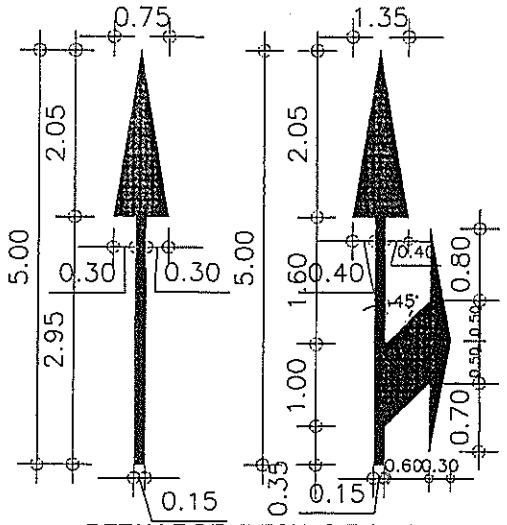


DETALLE DE FLECHAS EN PAVIMENTO
PARA VELOCIDADES HASTA DE 60KM/H
COTAS EN M

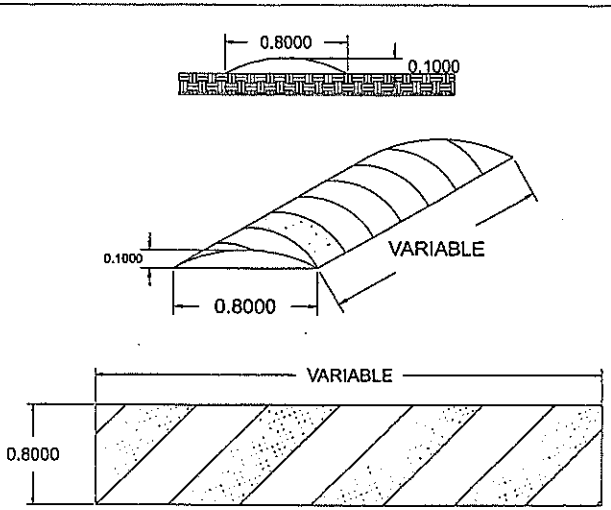

DETALLE DE TOPE VEHICULAR

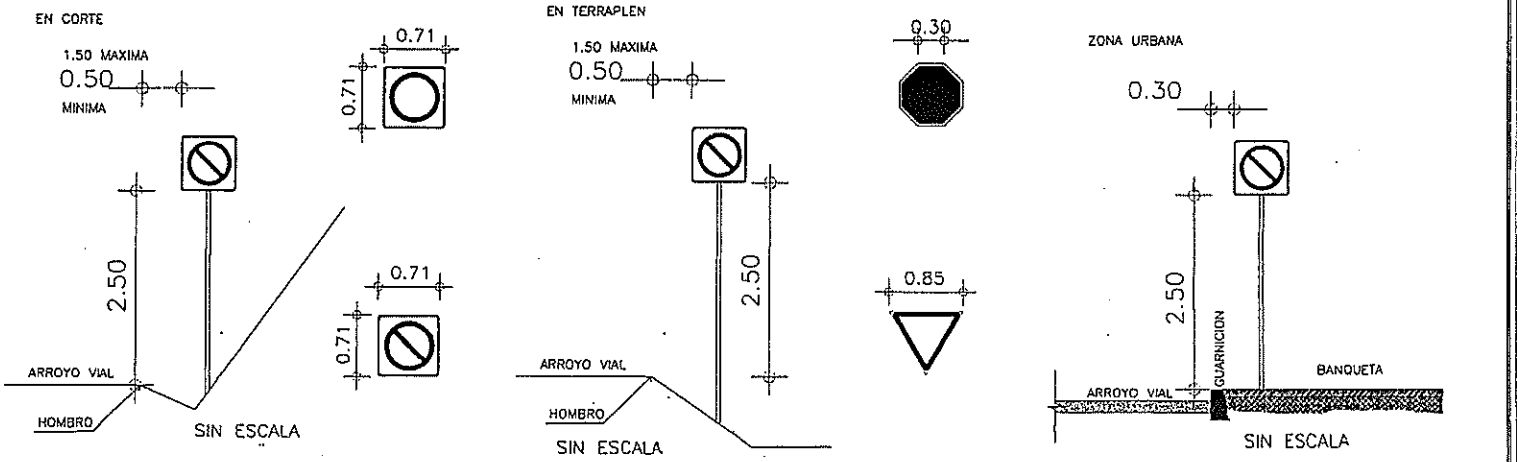

NOTA: LAS SECCIONES ESTRUCTURALES SE ENCUENTRAN EL APARTADO II.7.3. ESTRUCTURA DE SOPORTE DE SEÑALES BAJAS. DEL MANUAL DE SEÑALAMIENTO VIAL DE LA SCT

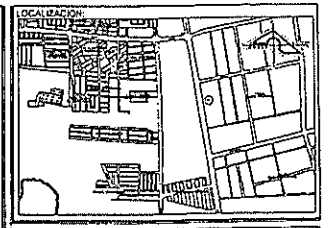

SIMBOLOGIA

NOTA:

Nota1:

Se aplicará en todos los señalamientos horizontales pintura para trafico termoplastica base alquidalica de secado rápido, que cumpla con las especificaciones n-cmt-5-01-001/05, n-pry-car-10-01-002/13 de la SCT aplicadas al dia de hoy.

Nota2:
Dosificación de micro esfera

La cantidad de esferas de vidrio en la pelicula de pintura en húmedo, según su tipo, será la que se indica en la Tabla.

Nota 3:

Se aplicará solo en señalamiento de guarnicion con pintura para trafico base solvente tipo alquidal de secado rápido, que cumpla con las especificaciones n-cmt-5-01-001/05, n-pry-car-10-01-002/13 de la SCT aplicadas al dia de hoy.

TABLA 8: Cantidad de esferas de vidrio en la pelicula de pintura en humedo.

CANTIDAD DE ESFERAS DE VIDRIO EN LA PELICULA DE PINTURA EN HÚMEDO				
TIPO DE PINTURA	ESPESOR DE LA PELICULA DE PINTURA EN HÚMEDO mm	CANTIDAD DE ESFERAS MINIMA		TIPO DE GRADUACIÓN
		INTEGRADAS	SUPERFICIALES, MINIMO	
BASE SOLVENTE	0,30 A 0,50	-	0,030	I
BASE AGUA	0,30 A 0,50	-	0,250	I A II
TERMOPLÁSTICA	1,50 A 3,00	-	0,030	II

La Dirección de Planeación y Proyectos solo autoriza el proyecto ejecutivo, no es responsable de la correcta ejecución de la obra, este documento no tiene validez si no presenta las firmas de los corresponsables para su autorización, así como los sellos respectivos.

PRESIDENTE MUNICIPAL M.P.P. Leonardo Montañez Castro ENCARGADA DE DESPACHO DE LA SOPMA Arq. Gloria Guadalupe Castillo González	REV. FECHA OBSERVACIONES	No. Ref. DE LA DEPENDENCIA	RESP. DE PROY. EXTERNO CED. PROFESIONAL PROYECTO / REVISO / AUTORIZO	LOGO EXTERNO	Dirección de Planeación y Proyectos de Obra / Secretaría de Obras Públicas PROYECTO: ARQ. ALVARO DE JESUS HERAS COORDINADOR: ARQ. ALEJANDRO JAIME LEAL JEFE DE DEPTO.: ARQ. CARLOS PALAFOX GONZALEZ DIRECTOR: ARQ. JOSE LUIS SANCHEZ GARCIA	PROYECTO OBRA COMPLEMENTARIA Y SEÑALETICA AV. MAHATMA GANDHI UBICACIÓN CALZADA ORIENTE DE ENTRE AV. SIGLO XXI Y ACCESO A CENTRAL DE ABASTOS CONTENIDO DETALLES SEÑALETICA VERTICAL	CLAVE DSV 01 FECHA MAR 2022 ACOTACIÓN METROS	No. PLANO 07 ESCALA INDICADA No. EXP. E-000-22	Aguascalientes LA CIUDAD DE TU VIDA

SEÑALES RESTRICTIVAS

SIMBOLO	CLAVE	DESCRIPCIÓN	DIMENSIÓN (cm)	UNIDAD	COLOR	CANTIDAD
	SR-6	ALTO	30 X LADO	PZA	ROJO REFLEJANTE	0
	SR-7	CEDA EL PASO	85 X LADO	PZA	BLANCO REFLEJANTE	0
	SR-9	VELOCIDAD 50 KM/H	71 X 71	PZA	BLANCO REFLEJANTE CON ANILLO ROJO REFLEJANTE	0
	SR-9	VELOCIDAD 60 KM/H	71 X 71	PZA	BLANCO REFLEJANTE CON ANILLO ROJO REFLEJANTE	0
	SR-21	ESTACIONAMIENTO PERMITIDO	71 X 71	PZA	BLANCO REFLEJANTE CON ANILLO ROJO REFLEJANTE	0

SEÑALES PREVENTIVAS


SIMBOLO	CLAVE	DESCRIPCIÓN	DIMENSIÓN (cm)	UNIDAD	COLOR	CANTIDAD
	SP-32	PEATONES	71 X 71	PZA	AMARILLO REFLEJANTE	3
	SP-33	ESCOLARES	71 X 71	PZA	VERDE LIMON FLUORESCENTE REFLEJANTE	0
	SP-41	REDUCTOR DE VELOCIDAD	71 X 71	PZA	AMARILLO REFLEJANTE	2
	SP-19I	SALIDA A LA IZQUIERDA	71 X 71	PZA	AMARILLO REFLEJANTE	0
	SP-19	SALIDA A LA DERECHA	71 X 71	PZA	AMARILLO REFLEJANTE	0

SEÑALES TURÍSTICAS Y DE SERVICIOS

SIMBOLO	CLAVE	DESCRIPCIÓN	DIMENSIÓN (cm)	UNIDAD	COLOR	CANTIDAD
	SIS-19	PARADERO DE AUTOBUS	71 X 71	PZA	AZÚL REFLEJANTE	3
	SIS-11	GASOLINERA	71 X 71	PZA	AZÚL REFLEJANTE	1
	SIS-51	ZONA O INSTALACIONES PARA DISCAPACITADOS	71 X 71	PZA	AZÚL REFLEJANTE	0
	SIS-64	ZONA PEATONAL	71 X 71	PZA	AZÚL REFLEJANTE	0

OBRAS Y DISPOSITIVOS DIVERSOS

SIMBOLO	CLAVE	DESCRIPCIÓN	DIMENSIÓN (cm)	UNIDAD	COLOR	CANTIDAD
	OD-5I	ZONA PEATONAL	71 X 71	PZA	AMARILLO REFLEJANTE	0
	OD-5D	ZONA PEATONAL	71 X 71	PZA	AMARILLO REFLEJANTE	0
	OD-5	ZONA PEATONAL	71 X 71	PZA	AMARILLO REFLEJANTE	0

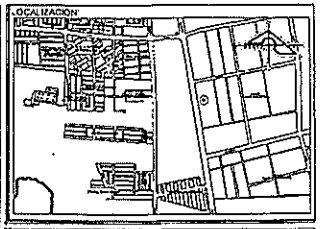

SIMBOLOGÍA

La Dirección de Planeación y Proyectos solo autoriza el proyecto ejecutivo, no es responsable de la correcta ejecución de la obra. Este documento no tiene validez si no presenta las firmas de los responsables para su autorización, así como los sellos respectivos.

PRESIDENTE MUNICIPAL
M.P.P. Leonardo Montañez Castro
ENCARGADA DE DESPACHO DE LA SOPMA
Arq. Gloria Guadalupe Castillo González

REV	FECHA	OBSERVACIONES

Vo. Bo. DE LA DEPENDENCIA


RESP. DE PROY. EXTERNO		LOGO EXTERNO
CED. PROFESIONAL		
PROYECTO	REVISO	AUTORIZO

Dirección de Planeación y Proyectos de Obra — Secretaría de Obras Públicas
DIRECTOR — COORDINADOR
ARQ. ALEJANDRO JAIME LEAL
JEFE DE DEPTO. — PROYECTOR
ARQ. J. JESÚS MARCOS GONZÁLEZ — M. en ARQ. JOSÉ LUIS MÁNEZ GARCÍA

PROYECTO
OBRA COMPLEMENTARIA Y SEÑALETICA AV. MAHATMA GANDHI
UBICACIÓN
CALZADA ORIENTE DE ENTRE AV. SIGLO XXI Y ACCESO A CENTRAL DE ABASTOS
CONTENIDO
DETALLES SEÑALETICA VERTICAL

CLAVE	No. PLANO
DSV 02	08
FECHA MAR 2022	ESCALA INDICADA
ACOTACIÓN METROS	No. EXP. E-000-22

Aguascalientes
LA CIUDAD DE TU VIDA

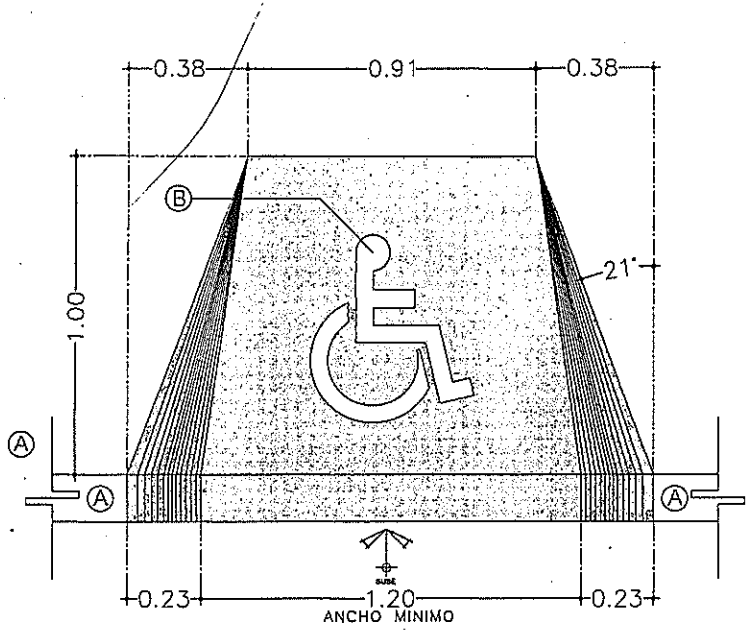


DETALLE DE LOGOTIPO "A" EN RAMPA

VISTA EN PLANTA S/E

Ⓐ SUMINISTRO Y APLICACIÓN DE PINTURA BASE SOLVENTE COLOR AZUL (PANTONE 294) EN RAMPAS PARA DISCAPACITADOS

Ⓑ SUMINISTRO Y APLICACIÓN DE LOGOTIPO "A" (SILLA DE RUEDAS) EN PINTURA BASE SOLVENTE COLOR BLANCO EN RAMPAS PARA DISCAPACITADOS TAMAÑO Y DISEÑO SEGÚN PLANOS.

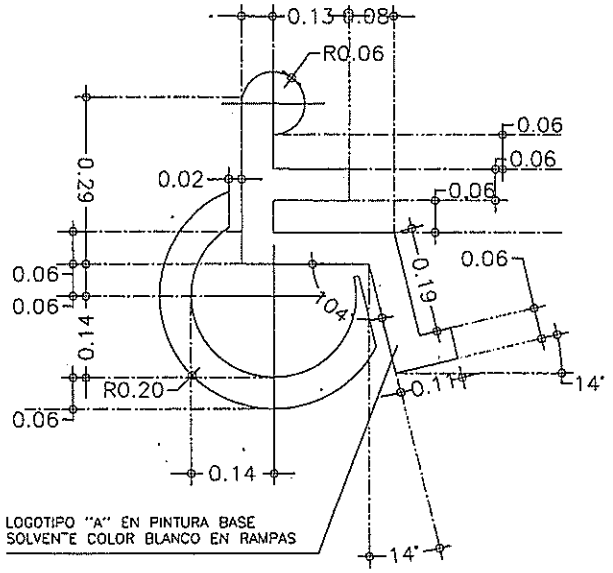


DETALLE DE LOGOTIPO "A" EN RAMPA

VISTA EN PLANTA S/E

CANTIDAD DE ESFERAS DE VIDRIO EN LA PELÍCULA DE PINTURA EN HÚMEDO

TIPO DE PINTURA	ESPESOR DE LA PELÍCULA DE PINTURA EN HÚMEDO mm	CANTIDAD DE ESFERAS KG/M2		TIPO DE GRANULOMETRÍA
		INTEGRADAS	SEMBRADAS, MÍNIMO	
BASE SOLVENTE	0,30 A 0,50	-	0,330	I
BASE AGUA	0,38 A 0,50	-	0,330	I ó II
TERMOPLÁSTICA	1,50 A 3,00	-	0,330	II

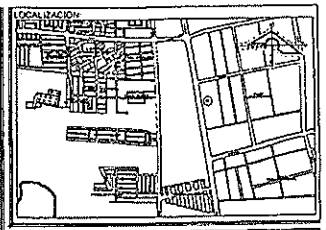

SIMBOLOGIA

NOTA:

Nota1:

Se aplicará en todos los señalamientos horizontales pintura para trafico termoplastica base solvente tipo alquidal de secado rápido, que cumpla con las especificaciones n-crrt-5-01-001/05, n-pry-car-10-01-002/13 de la SCT aplicadas al dia de hoy.

Nota2: Dosificación de micro esfera
La cantidad de esferas de vidrio en la pelicula de pintura en húmedo, según su tipo, será la que se indica en la Tabla.

TABLA 8: Cantidad de esferas de vidrio en la pelicula de pintura en humedo.

La Dirección de Planeación y Proyectos sólo autoriza el proyecto ejecutivo, no es responsable de la correcta ejecución de la obra, este documento no tiene validez si no presenta las firmas de los responsables para su autorización, así como los sellos respectivos.

PRESIDENTE MUNICIPAL
M.P.P. Leonardo Montañez Castro
ENCARGADA DE DESPACHO DE LA SOPMA
Arq. Gloria Guadalupe Castillo González

REV	FECHA	OBSERVACIONES

V°B° DE LA DEPENDENCIA

RESP. DE PROY. EXTERNO		LOGO EXTERNO
CED. PROFESIONAL		
PROYECTO	REVISO	AUTORIZO

Dirección de Planeación y Proyectos de Obra — Secretaría de Obras Públicas

PROYECTISTA	COORDINADOR
ARQ. ALVARO ALEJANDRO MONTAÑEZ RIVERA	ARQ. ALEJANDRO JUAREZ LEAL
JEFE DE DEP.	DIRECTOR
ARQ. JESÚS PALACIOS GONZÁLEZ	M. EN ARQ. JOSÉ LUIS MÁRQUEZ GARCÍA

PROYECTO
OBRA COMPLEMENTARIA Y SEÑALETICA AV. MAHATMA GANDHI
UBICACION
CALZADA ORIENTE DE ENTRE AV. SIGLO XXI Y ACCESO A CENTRAL DE ABASTOS
CONTENIDO
DETALLES SEÑALETICA DISCAPACITADOS

CLAVE	No. PLANO
DSD 01	12
FECHA	ESCALA
MAR 2022	INDICADA
ACOTACION	No. EXP.
METROS	E-000-22

Aguascalientes
LA CIUDAD DE TU VIDA