Aguascalientes
LA CIUDAD DE TU VIDA

Dirección de Programación Presupuestal
Núm. Oficio AMPP/0645/22
Aguascalientes, Ags. 7 de Diciembre del 2022
Asunto: Validación de Expediente Técnico

C.P. SERGIO ARTURO LOZANO GONZÁLEZ
SECRETARIO DE FINANZAS MUNICIPALES
P R E S E N T E

Con fundamento en los artículos 17 fracción XV, 60 fracción XVI y 76 fracción VI del Reglamento del Sistema Integral de Desarrollo Municipal y del Instituto Municipal de Planeación y Evaluación de Aguascalientes, hago referencia al oficio SOPMA/2968/2022 recibido por este Instituto el día 7 de Diciembre del 2022 por parte de la Secretaría de Obras Públicas Municipales, mediante el cual remiten el expediente técnico original de la siguiente obra para su análisis, registro y priorización, conforme al Programa Anual de Obra Pública y Programas Sociales para el ejercicio presupuestal 2022:

| | |
|---|---|
| DEPENDENCIA EJECUTORA: | SOPMA |
| NOMBRE DE LA OBRA O PROYECTO: | SOBRECARPETA ASFÁLTICA Y PAVIMENTO HIDRÁULICO |
| UBICACIÓN: | AV. DE LOS MAESTROS (CALZADA ORIENTE), TRAMO: ENTRE CALLE PROF. JOSÉ GUADALUPE PERALTA Y AV. SIGLO XXI, VARIAS COLONIAS, AGUASCALIENTES, AGS. |
| FONDO DE INVERSIÓN: | FONDO DE INFRAESTRUCTURA SOCIAL MUNICIPAL Y DE LAS DEMARCACIONES TERRITORIALES DEL DISTRITO FEDERAL |
| IMPORTE: | $6,652,667.32 (ET FINAL) |
| No. DE OBRA: | 2022-FISMDF-0085-04-1101 |
| MODALIDAD DE EJECUCIÓN: | CONTRATO |
| EJE: | MUNICIPIO SOBRESALIENTE |
| ESTRATEGIA: | OBRA PÚBLICA INTELIGENTE |
| POLITICA: | 5.8.1.REHABILITACIÓN Y MANTENIMIENTO VIALIDADES, CAMINOS, CALLES, ÁREAS DE TERRACERÍA Y CAUCES (C |

Al respecto, hago de su conocimiento que dicho expediente ha sido analizado en su integración técnica y documental, con base en el artículo 168 fracción I del Reglamento de la Ley de Obras Públicas y Servicios Relacionados para el Estado de Aguascalientes y sus Municipios.

Asimismo, le comento que este Instituto valida dicha obra acorde a lo establecido en los artículos 14, 22 párrafo segundo y 23 de la Ley de Obras Públicas y Servicios Relacionados para el Estado de Aguascalientes y sus Municipios, la cual se encuentra alineada al Plan de Desarrollo Municipal vigente, para dar cumplimiento a las metas establecidas en el mismo, y a los Lineamientos Generales para la Operación de este Fondo de Inversión, toda vez que la misma cuente con la autorización del CODEMUN. De igual manera, se hace de su conocimiento que deberá cumplir con lo establecido en los ordenamientos aplicables en lo que respecta al ejercicio, control e información de los recursos de este Fondo. Cabe hacer mención que los recursos solicitados para este proyecto de inversión, estarán sujetos a la disponibilidad presupuestal para el presente ejercicio fiscal que determine la Secretaría a su digno cargo. Sin otro particular por el momento, le envío un cordial saludo.

A T E N T A M E N T E

ARQ. AUSTRIA GABRIELA DÁVILA DE LA LLAVE
DIRECTORA GENERAL DEL IMPLAN

SEDR/ CAAR / JDBC
C.c.p. I.C. ING. MIGUEL ANGEL HUIZAR BOTELLO .- Secretaría de Obras Públicas Municipales .Para su conocimiento.
C.c.p. Archivo.

Instituto Municipal de Planeación y Evaluación de Aguascalientes

Antonio Acevedo Escobedo 103 A, Col. Centro
Aguascalientes, Ags. C.P. 20000

(449) 9101010 Ext. 3117

www.implanags.gob.mx

GOBIERNO MUNICIPAL DE AGUASCALIENTES

INSTITUTO MUNICIPAL DE PLANEACION

IMPLAN

## ANÁLISIS INTEGRAL DE EXPEDIENTE TÉCNICO

| | | | |
|---|---|---|---|
| No. DE OBRA (PAOP 2020): | 2022-FISMDF-0085-04-1101 | REGISTRO No. | 249 |
| OFICIO DE VALIDACIÓN: | AMPP/0645/22 | FECHA RECIBIDO PARA REVISIÓN: | 7 de Diciembre del 2022 |
| PROGRAMA: | URBANIZACION MUNICIPAL | LOCALIDAD O COLONIA: | VARIAS COLONIAS |
| SUB-PROGRAMA: | 0411- Calles y Caminos | DELEGACIÓN: | Aguascalientes |
| DEPENDENCIA: | Secretaría de Obras Públicas Municipales | MOD. DE EJECUCIÓN: | CONTRATO |
| NOMBRE DE LA OBRA: | SOBRECARPETA ASFÁLTICA Y PAVIMENTO HIDRÁULICO, AV. DE LOS MAESTROS (CALZADA ORIENTE), TRAMO: ENTRE CALLE PROF. JOSÉ GUADALUPE PERALTA Y AV. SIGLO XXI | | |
| FUENTE DE FINANCIAMIENTO: | FONDO DE INFRAESTRUCTURA SOCIAL MUNICIPAL Y DE LAS DEMARCACIONES TERRITORIALES DEL DISTRITO FEDERAL, FISMDF | | |
| INVERSIÓN: | $6,652,667.32 | CLASIFICACIÓN DE OBRA: | BIENES DE DOMINIO PUBLICA |

| TOTAL | FEDERAL | ESTATAL | MUNICIPAL | BENEFICIARIOS | OTROS | DIFERENCIA ENTRE MOD. |
|---|---|---|---|---|---|---|
| $6,652,667.32 | $6,652,667.32 | 0.00 | 0.00 | 0.00 | 0.00 | *$272.647,29* |

| | | | | | | |
|---|---|---|---|---|---|---|
| TIPO DE EXPENDIENTE: | ET FINAL | AÑO: 2022 | AÑO: | AÑO: | | |
| AVANCES: | Financiero: 100 % | Físico: 100 % | | | | |
| FECHA DE INICIO: | 8 de Septiembre del 2022 | FECHA DE TÉRMINO: | 6 de Diciembre del 2022 | REGISTRO SIMA: | 85 | |

## CHEK LIST DE LOS ANEXOS DEL EXPEDIENTE TÉCNICO

| | |
|---|---|
| CÉDULA DE REGISTRO DE OBRA | ✓ |
| DICTAMEN DE FACTIBILIDAD | ✓ |
| MEMORIA DESCRIPTIVA | ✓ |
| PRESUPUESTO BASE | ✓ |
| FACTIBILIDAD VERIFICADA EN CAMPO | ✓ |
| CROQUIS DE UBICACIÓN (MACRO) | ✓ |
| CROQUIS DE UBICACIÓN (MACRO) | ✓ |
| PROGRAMA DE OBRA Y MONTOS MENSUALES | ✓ |
| PLANOS O ESTUDIOS TÉCNICOS | ✓ |
| PADRÓN DE BENEFICIARIOS | N/A |
| ACTA DE ACEPTACIÓN DEL PROYECTO | N/A |
| DICTAMEN DE IMPACTO AMBIENTAL | N/A |
| CONVENIO DE CONCERTACIÓN | N/A |
| ACTA CONSTITUTIVA | N/A |

| METAS | | BENEFICIARIOS | | PERIODO DE EJECUCION | | OBRA PROPUESTA | | CLAVE SISCO |
|---|---|---|---|---|---|---|---|---|
| UNIDAD DE MEDIDA | CANT | TIPO DE BENEFICIARIOS | CANTIDAD | FECHA DE INICIO | FECHA DE TERMINO | CONCEPTO | JORNALES A GENERAR | |
| M2 | 17296 | Personas | 550 | 2022-09-08 | 2022-12-06 | Sobrecarpeta Asfáltica | 17296 | 2355 |

## INCLUIDO EN PLAN DE DESARROLLO MUNICIPAL Y EL PROGRAMA ANUAL DE OBRA PÚBLICA

OBSERVACIONES:

SIN OBSERVACIONES

RECIBIO: ING. JOSÉ DAVID BURGUETE CLAUSTRO
Analista de Programación e Inversión de Obra Pública

7 de Diciembre del 2022
Fecha de validación

7 de Diciembre del 2022
Fecha de validación Expediente

PROCEDE Si ✓ No

H. AYUNTAMIENTO CONSTITUCIONAL DEL MUNICIPIO DE AGUASCALIENTES 2021-2024

# AYUNTAMIENTO DE AGUASCALIENTES

## CEDULA DE REGISTRO POR OBRA

Aguascalientes
LA CIUDAD DE TU VIDA

**050400-001E00E05-05-2-2-1-00-1-E-0510-0-17-0085-21-2502-6144**

| | |
|---|---|
| **2022-FISMDF-0085-0411101-039** | Obra **SOBRECARPETA ASFÁLTICA Y PAVIMENTO HIDRÁULICO AV. DE LOS MAESTROS (CALZADA ORIENTE)** |
| Tipo DEFINITIVO 1 2022<br>Folio SISCO **2355** | Ubic. TRAMO: ENTRE CALLE PROF. JOSÉ GUADALUPE PERALTA GÁMEZ Y BLVD. SIGLO XXI, AGUASCALIENTES Mpio. |

Ent. Ejecutora : **050400001E00E05**

| | |
|---|---|
| Eje: **05** | MUNICIPIO SOBRESALIENTE |
| Finalidad: **2** | DESARROLLO SOCIAL |
| Función: **2** | VIVIENDA Y SERVICIOS A LA COMUNIDAD |
| Subfunción: **1** | URBANIZACIÓN |
| Tema: **00** | SIN TEMA |
| Cuenta del Gasto **1** | GASTO PROGRAMABLE |
| Clasif. Programatica: **E** | PRESTACIÓN DE SERVICIOS PÚBLICOS |
| Programa: **0510** | Movilidad Urbana |
| SubPrograma: **0** | SUBPROGRAMA GENÉRICO |
| Proyecto: **17** | |
| Tipo de Gasto: **21** | GASTO INVERSIÓN / OBRA PÚBLICA |

### I N V E R S I O N 2022

| | | | |
|---|---|---|---|
| Municipal | 2502 | FONDO PARA LA INFRAESTRUCTURA SOCIAL MUNICIPAL Y DE LAS DEMARCACIONES TERRITORIALES DEL DISTRITO FEDERAL 2022 | $6,652,667.32 |

Folio SIMA 85 Total $6,652,667.32

### M E T A S

| Unidad de Medida | Cantidad | Descripción |
|---|---|---|
| M2 | 2071.61 | SOBRECARPETA ASFÁLTICA SOBRECARPETA ASFÁLTICA Y PAVIMENTO HIDRÁULICO AV. DE LOS MAESTROS (CALZADA ORIENTE) |

| | | |
|---|---|---|
| Inversión Ejercida Total al | 31 de Diciembre de 2021 | $0.00 |
| Avance Fisico Acumulado al | 31 de Diciembre de 2021 | |
| Avance Fisico Acumulado Programado al | 31 de Diciembre de 2022 | 100 % |

Fecha de Inicio 08 Sep 2022 Fecha de Terminación 06 Dic 2022

Jornales a Generar en 2022 17296

Modalidad de ejecución CONTRATO

Clasificación de la Obra Bienes de Dominio Público

Registro del Patrimonio: Obras del dominio público

OBRAS PÚBLICAS

Av. Aguascalientes Sur No. 2615
Fracc. Jardines de las Fuentes,
Aguascalientes, Ags. C.P. 20278

(449) 9 78 92 01, 06, 09

www.ags.gob.mx

GENERALES

Nombre del Proyecto : SOBRECARPETA ASFÁLTICA Y PAVIMENTO HIDRÁULICO AV. DE LOS MAESTROS (CALZADA ORIENTE)

TRAMO: ENTRE CALLE PROF. JOSÉ GUADALUPE PERALTA GÁMEZ Y BLVD. SIGLO XXI, AGUASCALIENTES Mpio.

Programa : 04 URBANIZACION MUNICIPAL

Subprograma : 11 Calles y caminos (421.- Rehabilitación: 0411201- Concreto Hidraúlico)

Clave del Municipio : AGUASCALIENTES

Localidad :

Barrio, Colonia o Ejido : AGUASCALIENTES Mpio.

Tipo de Obra : NUEVA

DESCRIPCIÓN DEL PROYECTO:

SOBRECARPETA ASFÁLTICA Y PAVIMENTO HIDRÁULICO AV. DE LOS MAESTROS (CALZADA ORIENTE)

PRELIMINARES 3873.08 M2
SOBRECARPETA ASFÁLTICA 2071.61 M2
CONCRETO HIDRÁULICO 2146.23 M2
OBRA COMPLEMENTARIA 1.00 OBRA
HIDRÁULICO SANITARIO 87.5 ML
EXTRAORDINARIO

Beneficiarios ( No. y Tipo ) :

| 550 | PERSONAS |
|---|---|

Hombres: 247 Mujeres: 303

OBRAS PÚBLICAS

Av. Aguascalientes Sur No. 2615
Fracc. Jardines de las Fuentes,
Aguascalientes, Ags. C.P. 20278

(449) 9 78 92 01, 06, 09

www.ags.gob.mx

Los abajo firmantes, hacen constar que el presente proyecto :

SOBRECARPETA ASFÁLTICA Y PAVIMENTO HIDRÁULICO AV. DE LOS MAESTROS (CALZADA ORIENTE)

TRAMO: ENTRE CALLE PROF. JOSÉ GUADALUPE PERALTA GÁMEZ Y BLVD. SIGLO XXI, AGUASCALIENTES Mpio.

cumple con los Requisitos y Normas Técnicas establecidas por la Dependencia Normativa, por lo que es viable su ejecución. Comprometiéndose la misma a proporcionar la supervisión y asistencia técnica necesaria durante el proceso administrativo.

Por la Dependencia Ejecutora

Ing. Miguel Angel Huizar Botello
Secretario de Obras Públicas

Lic. Jaime Gallo Camacho
Secretario de Desarrollo Urbano

LUGAR :AGUASCALIENTES, AGS.



Av. Aguascalientes Sur No. 2615
Fracc. Jardines de las Fuentes,
Aguascalientes, Ags. C.P. 20278

(449) 9 78 92 01, 06, 09

www.ags.gob.mx

H. AYUNTAMIENTO CONSTITUCIONAL DEL MUNICIPIO DE AGUASCALIENTES 2021-2024

# AYUNTAMIENTO DE AGUASCALIENTES

## FACTIBILIDAD VERIFICADA EN CAMPO

Aguascalientes
LA CIUDAD DE TU VIDA

MUNICIPIO: AGUASCALIENTES

LOCALIZACION: TRAMO: ENTRE CALLE PROF. JOSÉ GUADALUPE PERALTA GÁMEZ Y BLVD. SIGLO XXI, AGUASCALIENTES Mpio.

PROGRAMA: URBANIZACION MUNICIPAL

SUBPROGRAMA: Calles y caminos (421.- Rehabilitación: 0411201- Concreto Hidraúlico)

OBRA A REALIZAR: SOBRECARPETA ASFÁLTICA Y PAVIMENTO HIDRÁULICO AV. DE LOS MAESTROS (CALZADA ORIENTE)

DEPENDENCIA EJECUTORA: SECRETARÍA DE OBRAS PUBLICAS DEL MUNICIPIO DE AGUASCALIENTES

FORMA DE EJECUCION: CONTRATO

TIPO DE OBRA PROPUESTA: NUEVA

CONDICIONES ACTUALES DE LA OBRA:

SOBRECARPETA ASFÁLTICA Y PAVIMENTO HIDRÁULICO AV. DE LOS MAESTROS (CALZADA ORIENTE)

CARACTERISTICAS DE LA OBRA: Bueno

FACTIBILIDAD DE LA OBRA:

ESTA OBRA SE REQUIERE PARA EL BENEFICIO DE LA CIUDADANÍA

PROCEDE: SI [X] NO [ ]

REVISÓ: Jefa del Departamento de Expedientes Tecnicos y Costos

NOMBRE: Arq. Blanca Margarita Martinez Amador

FIRMA:

FECHA: 09 Dic 2022

SECRETARÍA DE OBRAS PÚBLICAS

Av. Aguascalientes Sur No. 2615
Fracc. Jardines de las Fuentes,
Aguascalientes, Ags. C.P. 20278

(449) 9 78 92 01, 06, 09

www.ags.gob.mx

No. Folio SISCO 2355

# PRESIDENCIA MUNICIPAL DE AGUASCALIENTES

## FACTIBILIDAD VERIFICADA EN CAMPO

**GENERALES**

EJERCICIO: 2022 APROBACION No: 2022-FISMDF-0085-0411101-039
LOCALIDAD: TRAMO: ENTRE CALLE PROF. JOSÉ GUADALUPE PERALTA GÁMEZ Y BLVD. SIGLO XXI, AGUASCA
MUNICIPIO: AGUASCALIENTES, AGS
TIPO DE INVERCION: FONDO PARA LA INFRAESTRUCTURA SOCIAL MUNICIPAL Y DE LAS DEMARCACIONES TERRITORIALES DEL DISTRITO FEDERAL

PROGRAMA: 04 URBANIZACIÓN MUNICIPAL

SUB-PROGRAMA:

OBRA A REALIZARSE: FISMDF-0085-2022 SOBRECARPETA ASFÁLTICA Y PAVIMENTO HIDÁULICO AV. DE LOS MAESTROS (CALZADA ORIENTE)

DEPENDENCIA EJECUTORA: SECRETARÍA DE OBRAS PÚBLICAS MUNICIPALES (S.O.P.M.A)
FORMACIÓN DE EJECUCION: CONTRATO NO. DE CONTRATO: FISMDF-0085-2022
NOMBRE CONTRATISTA: CONSORCIO INDUSTRIAL INTERNACIONAL AIRE, S.A DE C.V
REPRESENTANTE: ARRIAGA RAMOS ERNESTO ING. RESIDENTE:
MONTO CONT. ORIGEN $6,652,667.33 ANTICIPO: PLAZO 90 DIAS
1A AMPLIACION $: 1 AMPL DIAS
2A AMPLIACION $: 2 AMPL DIAS
FIRMA CONTRATO: 31/08/2022
INICIO CONT: dd/mm/aa 1 de septiembre de 2022 TERMINO CONT: 29 de noviembre de 2022
INICIO REAL: dd/mm/aa 8 de septiembre de 2022 TERMINO REAL: 6 de diciembre de 2022

**TIPO DE OBRA PROPUESTA**

| | | | |
|---|---|---|---|
| NUEVA CREACIÓN | | CONSOLIDACIÓN | |
| COMPLEMENTARIA | X | AMPLIACIÓN | |
| REHABILITACIÓN | | EQUIPAMIENTO | |

**CARACTERÍSTICAS DE LA OBRA:**

FISMDF-0085-2022 SOBRECARPETA ASFÁLTICA Y PAVIMENTO HIDÁULICO AV. DE LOS MAESTROS (CALZADA ORIENTE)

**CONDICIONES ACTUALES DE LA OBRA: (SELECCIONAR UNO OBLIGATORIO)**

BUEN ESTADO X REGULAR PESIMO ESTADO

**FACTIBILIDAD DE LA OBRA: (CONDICIONES ACTUALES DE LA OBRA)**

ESTA OBRA SE ENCUENTRA EN CONDICIONES PARA OPERARSE

**PROCEDE:** SI: X NO:
MARQUE SOLO UNA

HÉCTOR ERNESTO URIBE PEDROZA.
**SUPERVISOR**

# PRESIDENCIA MUNICIPAL DE AGUASCALIENTES

## FACTIBILIDAD VERIFICADA EN CAMPO

**GENERALES**

LOCALIDAD: TRAMO: ENTRE CALLE PROF. JOSÉ GUADALUPE PERALTA GÁMEZ Y BLVD. SIGLO XXI, AGUASCALIENTES Mpio
MUNICIPIO: AGUASCALIENTES, AGS
PROGRAMA: 04 URBANIZACIÓN MUNICIPAL
SUB-PROGRAMA: 0
OBRA A REALIZARSE: FISMDF-0085-2022 SOBRECARPETA ASFÁLTICA Y PAVIMENTO HIDÁULICO AV. DE LOS MAESTROS (CALZADA ORIENTE)

DEPENDENCIA EJECUTORA: SECRETARÍA DE OBRAS PÚBLICAS MUNICIPALES (S.O.P.M.A)
FORMACIÓN DE EJECUCION: CONTRATO

**TIPO DE OBRA PROPUESTA**

| | | | |
|---|---|---|---|
| NUEVA CREACIÓN | | CONSOLIDACIÓN | |
| COMPLEMENTARIA | X | AMPLIACIÓN | |
| REHABILITACIÓN | | EQUIPAMIENTO | |

**CARACTERÍSTICAS DE LA OBRA:**

FISMDF-0085-2022 SOBRECARPETA ASFÁLTICA Y PAVIMENTO HIDÁULICO AV. DE LOS MAESTROS (CALZADA ORIENTE)

**CONDICIONES ACTUALES DE LA OBRA:**

| | | | | | |
|---|---|---|---|---|---|
| BUEN ESTADO: | X | REGULAR: | | PESIMO ESTADO: | |

**FACTIBILIDAD DE LA OBRA:**

ESTA OBRA SE ENCUENTRA EN CONDICIONES PARA OPERARSE

| | | | | | |
|---|---|---|---|---|---|
| **PROCEDE** | **SI:** | X | **NO:** | | |

HÉCTOR ERNESTO URIBE PEDROZA.
**SUPERVISOR**

| RO3-POS-SOS-7.5.1-04 | |
|---|---|
| REVISION: | 00 |
| FECHA DE REVISION: | |
| RESPONSABLE: | SUPERVISOR DE OBRA |
| TIEMPO DE RET: | 02 AÑOS |

Aguascalientes
LA CIUDAD DE TU VIDA

# PROGRAMA DE OBRA

No. DE CONTRATO : FISMDF-0085-2022

PROGRAMA: 04 URBANIZACIÓN MUNICIPAL — INICIO VIGENTE: 08-septiembre-22

No. OBRA Y NOMBRE DE LA OBRA: FISMDF-0085-2022 SOBRECARPETA ASFÁLTICA Y PAVIMENTO HIDÁULICO AV. DE LOS MAESTROS (CALZADA ORIENTE) — TERMINO REAL: 06-diciembre-22

RECURSO

| CONCEPTO | | | | 1 | 2 | 3 | 4 | 5 | 6 | 7 | 8 | 9 | 10 | 11 | 12 | 13 | 14 | 15 | 16 | PONDERACIÓN % | |
|---|---|---|---|---|---|---|---|---|---|---|---|---|---|---|---|---|---|---|---|---|---|
| | | | | 2022 | | | | | | | | | | | | | | | | | |
| | | | | ENERO | FEBRERO | MARZO | ABRIL | MAYO | JUNIO | JULIO | AGOSTO | SEPTIEMBRE | OCTUBRE | NOVIEMBRE | DICIEMBRE | ENERO | FEBRERO | MARZO | ABRIL | FINANCIERO | FÍSICO |
| | | | | | | | | | | | | | | | | | | | | % | % |
| DESCRIPCION | INVERSION | | | | | | | | | | | | | | | | | | | | |
| FISMDF-0085-2022 SOBRECARPETA ASFALTICA Y PAVIMENTO HIDÁULICO AV. DE LOS MAESTROS (CALZADA ORIENTE) | | | | | | | | | | | | 8 | | | 6 | | | | | | |
| TRAMO: ENTRE CALLE PROF. JOSE GUADALUPE PERALTA GAMEZ Y BLVD. SIGLO XXI, AGUASCALIENTES Mpio | | | | | | | | | | | | | | | | | | | | | |
| PRELIMINARES | $ 212,679.75 | 100 | | | | | | | | | | 30 20 30 20 | | | | | | | | 3.71 | 22.22 |
| SOBRE CARPETA ASFALTICA | $ 1,354,156.14 | 100 | | | | | | | | | 20 30 30 20 | | | | | | | | | 23.61 | 22.22 |
| CONCRETO HIDRAULICO | $ 1,642,379.46 | 100 | | | | | | | | | 20 20 40 20 | | | | | | | | | 28.64 | 22.22 |
| OBRA COMPLEMENTARIA | $ 487,694.39 | 100 | | | | | | | | | | | 90 10 | | | | | | | 8.50 | 11.11 |
| HIDRAULICO SANITARIO | $ 199,916.01 | 100 | | | | | | | | | 30 30 30 10 | | | | | | | | | 3.49 | 22.22 |
| EXTRAORDINARIO | $ 1,838,030.28 | 100 | | | | | | | | | 25 25 25 25 | | | | | | | | | 32.05 | 22.22 |
| | | - | | | | | | | | | | | | | | | | | | | |
| | | - | | | | | | | | | | | | | | | | | | | |
| | | - | | | | | | | | | | | | | | | | | | | |
| SUBTOTAL SIN IVA | $ 5,735,058.03 | $ 18.00 | | 0 0 0 0 | 0 0 0 0 | 0 0 0 0 | 0 0 0 0 | 0 0 0 0 | 0 0 0 0 | 0 0 0 0 | 1 3 0 4 | 4 2 1 2 | 1 0 0 0 | 0 0 0 0 | 0 0 0 0 | 0 0 0 0 | 0 0 0 0 | 0 0 0 0 | 0 0 0 0 | | |
| | AVACE SEMANAL % | | | 0% 0% 0% 0% | 0% 0% 0% 0% | 0% 0% 0% 0% | 0% 0% 0% 0% | 0% 0% 0% 0% | 0% 0% 0% 0% | 0% 0% 0% 0% | 5% 17% 22% 22% | 22% 11% 0% 11% | 0% 0% 0% 0% | 0% 0% 0% 0% | 0% 0% 0% 0% | 0% 0% 0% 0% | 0% 0% 0% 0% | 0% 0% 0% 0% | 0% 0% 0% 0% | | |
| | AVANCE SEMANAL ACUMULADO % | | | 0% 0% 0% 0% | 0% 0% 0% 0% | 0% 0% 0% 0% | 0% 0% 0% 0% | 0% 0% 0% 0% | 0% 0% 0% 0% | 0% 0% 0% 0% | 5% 22% 44% 67% | 78% 89% 89% 100% | 100% 100% 100% 100% | 100% 100% 100% 100% | 100% 100% 100% 100% | 100% 100% 100% 100% | 100% 100% 100% 100% | 100% 100% 100% 100% | 100% 100% 100% 100% | 100.00 | 122.2 |
| | EJERCIDO SEMANAL $ | | | | | | | | | | 270,631.23 794,698.14 1,254,205.71 1,447,255.99 | 871,888.19 502,863.52 63,863.33 481,500.59 | 48,769.44 | | | | | | | | $ 5,735,058.03 | |
| | EJERCIDO MENSUAL $ | | | $0.00 | $0.00 | $0.00 | $0.00 | $0.00 | $0.00 | $0.00 | $3,767,001.06 | $1,919,287.53 | $48,769.44 | $0.00 | $0.00 | $0.00 | $0.00 | $0.00 | $0.00 | $ 917,609.29 | IVA 16 |
| | EJERCIDO MENSUAL ACUMULADO $ | | | 0.00 | 0.00 | 0.00 | 0.00 | 0.00 | 0.00 | 0.00 | 3,767,001.06 | 5,686,288.59 | 5,735,058.03 | 5,735,058.03 | 5,735,058.03 | 5,735,058.03 | 5,735,058.03 | 5,735,058.03 | 5,735,058.03 | | |
| | EJERCIDO SEMANAL % | | | 0% 0% 0% 0% | 0% 0% 0% 0% | 0% 0% 0% 0% | 0% 0% 0% 0% | 0% 0% 0% 0% | 0% 0% 0% 0% | 0% 0% 0% 0% | 5% 14% 22% 25% | 15% 9% 1% 8% | 1% 0% 0% 0% | 0% 0% 0% 0% | 0% 0% 0% 0% | 0% 0% 0% 0% | 0% 0% 0% 0% | 0% 0% 0% 0% | 0% 0% 0% 0% | | |
| | EJERCIDO MENSUAL % | | | 0% | 0% | 0% | 0% | 0% | 0% | 0% | 66% | 33% | 1% | 0% | 0% | 0% | 0% | 0% | 0% | GRAN TOTAL EJERCIDO | |
| | EJERCIDO MENSUAL ACUMULADO % | | | 0% | 0% | 0% | 0% | 0% | 0% | 0% | 66% | 99% | 100% | 100% | 100% | 100% | 100% | 100% | 100% | $ | 6,652,667.3 |
| | | $ 18.00 | | | | | | | | | | | | | | | | | | | |

HÉCTOR ERNESTO URIBE PEDROZA.
SUPERVISOR


H. AYUNTAMIENTO DE AGUASCALIENTES
**SECRETARÍA DE OBRAS PÚBLICAS**
**DIRECCIÓN DE SUPERVISIÓN DE OBRA**

Aguascalientes
LA CIUDAD DE TU VIDA

# MEMORIA FOTOGRAFICA


| | | | | | | |
|---|---|---|---|---|---|---|
| OBRA: | FISMDF-0085-2022 SOBRECARPETA ASFÁLTICA Y PAVIMENTO HIDÁULICO AV. DE LOS MAESTROS (CALZADA ORIENTE) | | | | | |
| NO. DE CONTRATO: | FISMDF-0085-2022 | | CONTRATISTA: | CONSORCIO INDUSTRIAL INTERNACIONAL AIRE, S.A DE C.V | | |

## INICIO.

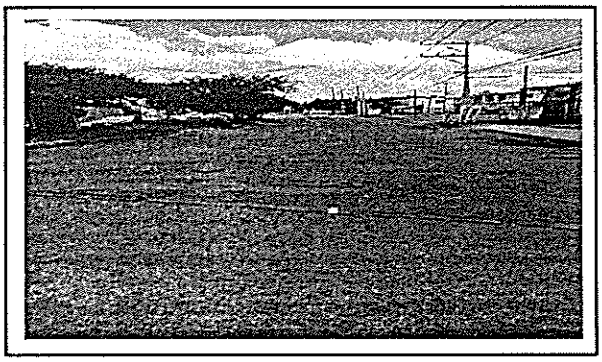





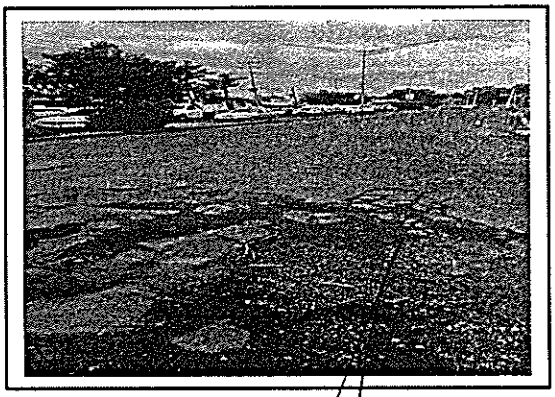

HÉCTOR ERNESTO URIDE PEDROZA.
SUPERVISOR DE OBRA.


H. AYUNTAMIENTO DE AGUASCALIENTES
SECRETARÍA DE OBRAS PÚBLICAS
DIRECCIÓN DE SUPERVISIÓN DE OBRA

Aguascalientes
LA CIUDAD DE TU VIDA


# MEMORIA FOTOGRAFICA

| | | | | | | |
|---|---|---|---|---|---|---|
| OBRA: | FISMDF-0085-2022 SOBRECARPETA ASFÁLTICA Y PAVIMENTO HIDÁULICO AV. DE LOS MAESTROS (CALZADA ORIENTE) | | | | | |
| NO. DE CONTRATO: | FISMDF-0085-2022 | | CONTRATISTA: | CONSORCIO INDUSTRIAL INTERNACIONAL AIRE, S.A DE C.V | | |

## PROCESO

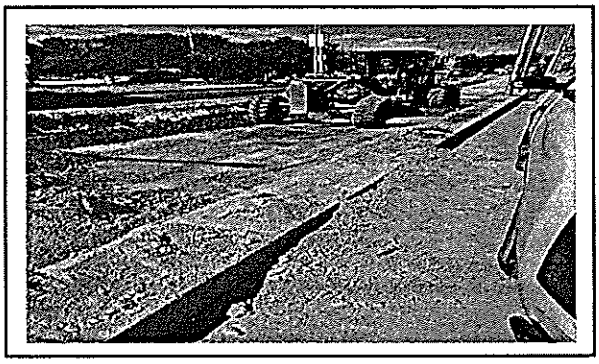



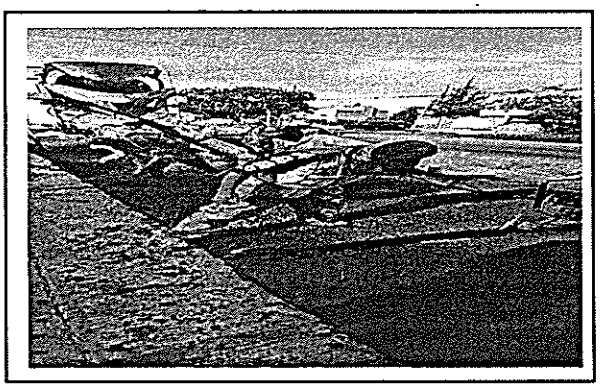



HÉCTOR ERNESTO URIBE PEDROZA.
SUPERVISOR DE OBRA.

H. AYUNTAMIENTO DE AGUASCALIENTES

**SECRETARÍA DE OBRAS PÚBLICAS**


**DIRECCIÓN DE SUPERVISIÓN DE OBRA**


Aguascalientes
LA CIUDAD DE TU VIDA


# MEMORIA FOTOGRAFICA


| | | | | | | |
|---|---|---|---|---|---|---|
| OBRA: | FISMDF-0085-2022 SOBRECARPETA ASFÁLTICA Y PAVIMENTO HIDÁULICO AV. DE LOS MAESTROS (CALZADA ORIENTE) | | | | | |
| NO. DE CONTRATO: | FISMDF-0085-2022 | | CONTRATISTA: | CONSORCIO INDUSTRIAL INTERNACIONAL AIRE, S.A DE C.V | | |

## TERMINO

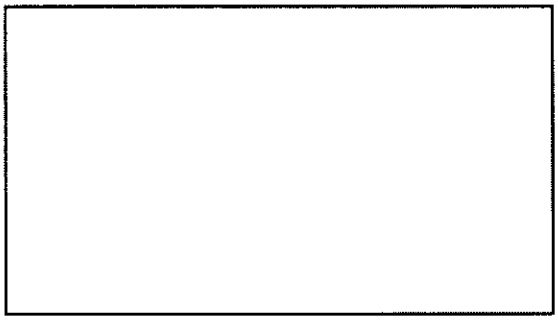

 

 


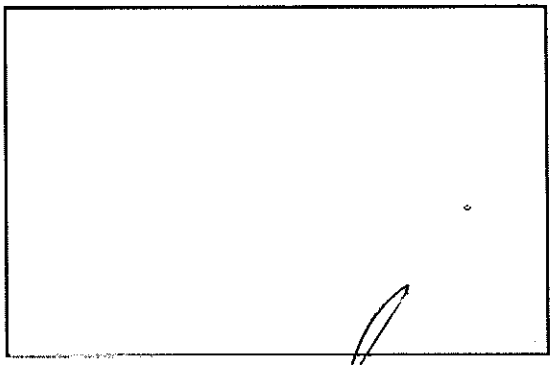

HÉCTOR ERNESTO URIBE PEDROZA.
SUPERVISOR DE OBRA.

# H. AYUNTAMIENTO DE AGUASCALIENTES
## SECRETARÍA DE OBRAS PÚBLICAS
## DIRECCIÓN DE SUPERVISIÓN DE OBRA
# UBICACIÓN

| | | | | | | |
|---|---|---|---|---|---|---|
| OBRA: | FISMDF-0085-2022 SOBRECARPETA ASFÁLTICA Y PAVIMENTO HIDÁULICO AV. DE LOS MAESTROS (CALZADA ORIENTE) | | | | | |
| NO. DE CONT | FISMDF-0085-2022 | | CONTRATISTA: | CONSORCIO INDUSTRIAL INTERNACIONAL AIRE, S.A DE C.V | | |

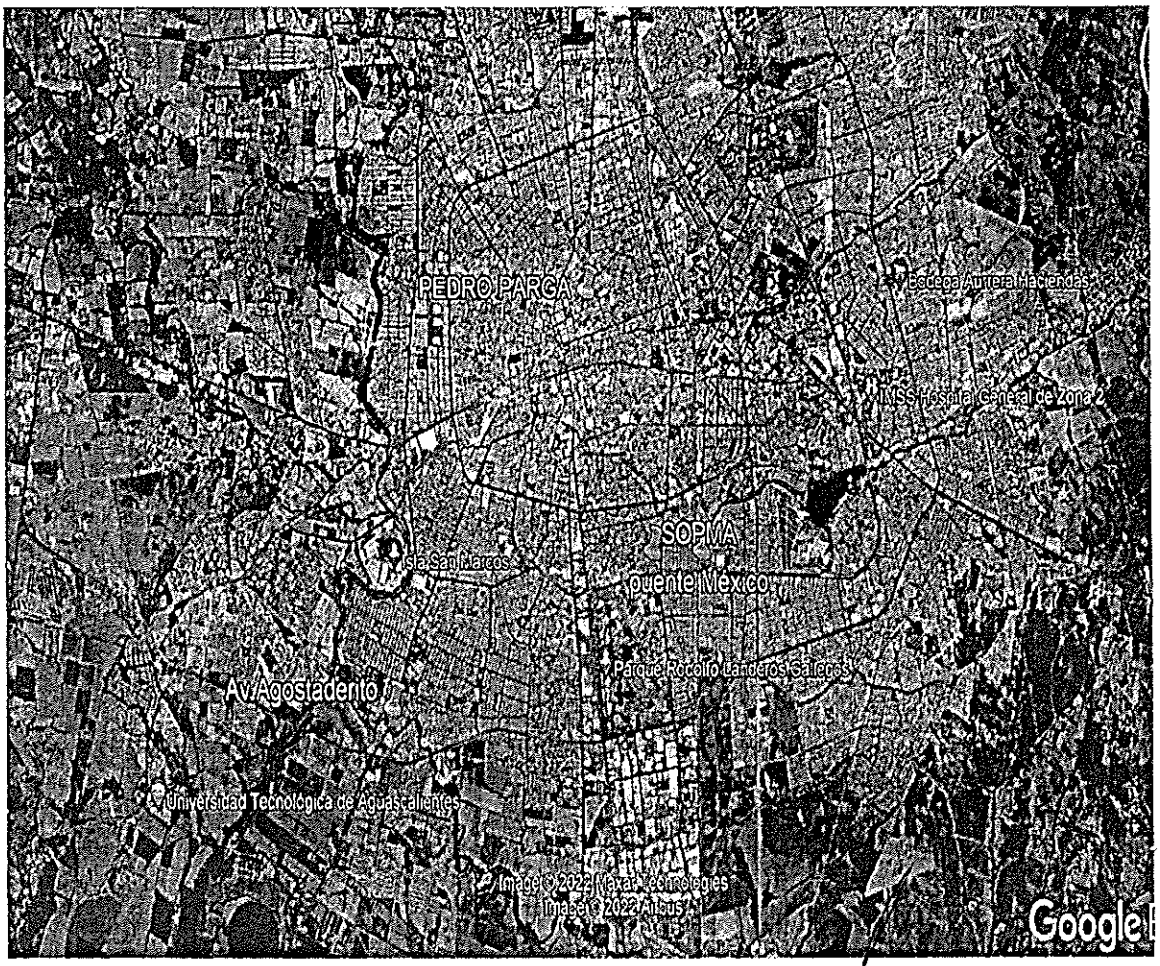


HÉCTOR ERNESTO URIBE PEDROZA.
SUPERVISOR DE OBRA.

# H. AYUNTAMIENTO DE AGUASCALIENTES
## SECRETARÍA DE OBRAS PÚBLICAS
## DIRECCIÓN DE SUPERVISIÓN DE OBRA
# UBICACIÓN

| | | | | | | |
|---|---|---|---|---|---|---|
| OBRA: | FISMDF-0085-2022 SOBRECARPETA ASFÁLTICA Y PAVIMENTO HIDÁULICO AV. DE LOS MAESTROS (CALZADA ORIENTE) | | | | | |
| NO. DE CONT | FISMDF-0085-2022 | | CONTRATISTA: | CONSORCIO INDUSTRIAL INTERNACIONAL AIRE, S.A DE C.V | | |




HÉCTOR ERNESTO URIBE PEDROZA.
SUPERVISOR DE OBRA.

# MODIFICADO.

## SECRETARÍA DE OBRAS PÚBLICAS

### DIRECCIÓN DE SUPERVISIÓN DE OBRAS

# FISMDF-0085-2022

**N° DE CONTRATO:** FISMDF-0085-2022

**NOMBRE DE LA OBRA:** FISMDF-0085-2022 SOBRECARPETA ASFÁLTICA Y PAVIMENTO HIDÁULICO AV. DE LOS MAESTROS (CALZADA ORIENTE)

**MONTO MODIFICADO FINAL:** $ 6,652,667.32

| VOLUMEN | UNIDAD | COMPONENTE DE LA OBRA | MONTO |
|---|---|---|---|
| 12.00 | SONDE | PRELIMINARES | $ 212,879.75 |
| 12,671.44 | M2 | SOBRE CARPETA ASFÁLTICA | $ 1,354,156.14 |
| 349.17 | M3 | CONCRETO HIDRAULICO | $ 1,642,379.46 |
| 5.00 | PZA | OBRA COMPLEMENTARIA | $ 487,694.39 |
| 87.50 | ML | HIDRÁULICO SANITARIO | $ 199,918.01 |
| 646.26 | M2 | EXTRAORDINARIO | $ 1,838,030.28 |
| | | | |

| | | |
|---|---|---|
| TOTAL PRESUP. | $ | 5,735,058.03 |
| IVA | $ | 917,609.29 |
| TOTAL | $ | 6,652,667.32 |

**NOMBRE DEL SUPERVISOR:** HÉCTOR ERNESTO URIBE PEDROZA

H. AYUNTAMIENTO CONSTITUCIONAL DEL MUNICIPIO DE AGUASCALIENTES 2021-2024

# PRESUPUESTO MODIFICADO

Aguascalientes

Obra: SOBRECARPETA ASFÁLTICA Y PAVIMENTO HIDRÁULICO AV. DE LOS MAESTROS (CALZADA ORIENTE)

Ubicación: TRAMO: ENTRE CALLE PROF. JOSÉ GUADALUPE PERALTA GÁMEZ Y BLVD. SIGLO XXI, AGUASCALIENTES Mpio.

Contratista: CONSORCIO INDUSTRIAL INTERNACIONAL AIRE, S.A. DE C.V. (713)

| Grupo | Partida | Importe |
|---|---|---|
| **PRELIMINARES** | | |
| | PRELIMINARES Y DEMOLICIONES | $212,879.75 |
| | **Subtotal por Grupo** | **$212,879.75** |
| **SOBRECARPETA ASFALTICA** | | |
| | BACHEO PROFUNDO | $60,179.10 |
| | SOBRE CARPETA ASFALTICA | $1,293,977.04 |
| | **Subtotal por Grupo** | **$1,354,156.14** |
| **CONCRETO HIDRAULICO** | | |
| | EXCAVACIONES, ACARREOS Y TERRACERIAS | $1,007,960.93 |
| | PAVIMENTO | $621,311.34 |
| | DENTELLONES DE CONCRETO | $5,851.47 |
| | GUARNICIONES | $7,255.71 |
| | **Subtotal por Grupo** | **$1,642,379.46** |
| **OBRA COMPLEMENTARIA** | | |
| | OBRA COMPLEMENTARIA | $292,205.24 |
| | LIMPIEZAS | $58,966.20 |
| | SEÑALIZACION HORIZONTAL | $127,486.43 |
| | SEÑALAMIENTO VERTICAL | $9,036.52 |
| | **Subtotal por Grupo** | **$487,694.39** |
| **HIDRAULICO SANITARIO** | | |
| | LINEA DE ALCANTARILLADO | $186,496.40 |
| | DESCARGAS DOMICILIARIAS | $13,421.61 |
| | **Subtotal por Grupo** | **$199,918.01** |
| **EXTRAORDINARIO** | | |
| | EXTRAORDINARIOS | $1,838,030.28 |
| | **Subtotal por Grupo** | **$1,838,030.28** |

| | | |
|---|---|---|
| **Totales Presup.** | | **$5,735,058.03** |
| **Anticipo** | + | **$1,720,517.41** |
| **Amortizac. Ant.** | - | **$1,720,517.41** |
| **SubTotal. Ant.** | = | **$5,735,058.03** |
| **IVA** | + | **$917,609.29** |
| **Total** | = | **$6,652,667.32** |

# PRESUPUESTO MODIFICADO

Obra: **SOBRECARPETA ASFÁLTICA Y PAVIMENTO HIDRÁULICO AV. DE LOS MAESTROS (CALZADA ORIENTE)**

Ubicación: **TRAMO: ENTRE CALLE PROF. JOSÉ GUADALUPE PERALTA GÁMEZ Y BLVD. SIGLO XXI, AGUASCALIENTES Mpio.**

Contratista: **CONSORCIO INDUSTRIAL INTERNACIONAL AIRE, S.A. DE C.V. (713)**

| No. | Concepto | Unidad | Cantidad | Precio Unitario | Importe Total |
|---|---|---|---|---|---|
| | GRUPO: **PRELIMINARES** | | | | |
| | PARTIDA: **PRELIMINARES Y DEMOLICIONES** | | | | |
| 1 | LIMPIA, TRAZO Y NIVELACION EN PAVIMENTOS, CALLES Y VIALIDADES CON EQUIPO TOPOGRAFICO, INCLUYE: EJES, BANCO DE NIVEL, RENIVELACIONES LAS VECES NECESARIAS, CORRECCION DE RASANTE A PUNTOS OBLIGADOS (AUTORIZADOS POR LA SUPERVISION), ESTACAS, VARILLAS, MANO DE OBRA CALIFICADA, HERRAMIENTA NECESARIA, EQUIPO DE PRECISION CALIBRADO, TRABAJO TERMINADO.P.U.O.T. | M2 | 3873.08 | $8.01 | $31,023.37 |
| 2 | SONDEO A MANO O A MAQUINA PARA LOCALIZACION DE TUBERIAS CUALQUIER PROFUNDIDAD Y MATERIAL PARA VERIFICAR LA CALIDAD DE LAS INSTALACIONES HIDRAULICO SANITARIAS CUIDANDO NO DAÑARLAS PARA NO INTERFERIR EN LOS SERVICIOS, INCLUYE: EXCAVACION, EQUIPO, MANO DE OBRA, REPORTE A LA SUPERVISION, RELLENOS, COMPACTACIONES, TRABAJO TERMINADO. | SONDE | 12 | $2,650.70 | $31,808.40 |
| 3 | CORTE CON DISCO DIAMANTADO DE 14" EN PISOS DE CONCRETO ASFALTICO DE HASTA 8.00 cm. DE PROFUNDIDAD. INCLUYE: TRAZO, EQUIPO Y OPERACION, LIMPIEZAS. | ML | 34 | $33.65 | $1,144.10 |
| 4 | DEMOLICION PARCIAL DE PAVIMENTO HIDRAULICO Y/O ASFALTICO DE HASTA 15 CM. DE ESPESOR PROMEDIO EN PAVIMENTOS Y ( BANQUETAS, LOSAS DIAMANTE Y CAJAS DE VALVULAS, TOPES ) CON O SIN ARMADO DE ACERO, SIN RECUPERACION, MUROS, MOJONERAS, ANCLAJES, ETC, DE FORMA MANUAL Y MECANICA, INCLUYE ACARREO DE MATERIAL AL LUGAR DE ACOPIO, HERRAMIENTA NECESARIA Y TODO LO NECESARIO PARA SU CORRECTA EJECUCION, LIMPIEZA, TRABAJO TERMINADO | M3 | 2.48 | $411.74 | $1,021.12 |
| 5 | FRESADO UNIFORME DE LA SUPERFICIE DE RODADURA EN PAVIMENTO DE CONCRETO ASFALTICO 3-7 CM ( 5 cm de espesor promedio) MEDIANTE FRESADORA EN FRIO COMPACTA, EQUIPADA CON BANDA TRANSPORTADORA PARA CARGA DIRECTA SOBRE CAMION DE VOLTEO, INCLUYE: TRAMO DE PRUEBA AL INICIO DEL FRESADO PARA AUTORIZACION DE SUPERVISION (SUPERFICIE FRESADA UNIFORME Y SIN PROTUBERANCIAS NI ONDEOS), ACARREOS LOCALES, CARGA Y ACARREO A KM SUBSECUENTES (11 A 15 KM APROX) DE MATERIAL PRODUCTO DEL FRESADO DE CARPETA ASFALTICA EL TRASLADO SERA A PARQUE DE MAQUINARIA DE LA SOPMA, PIEZAS DE DESGASTE, COMBUSTIBLES, CONSUMIBLES, MANO DE OBRA, CUALQUIER VOLUMEN Y AREA,EQUIPO NECESARIO, LIMPIEZA FINA Y GRUESA, TRABAJO TERMINADO. | M3 | 102.18 | $976.93 | $99,822.71 |
| 6 | REMOCIÓN DE CARPETA ASFÁLTICA SOBRE CONCRETO HIDRÁULICO EXISTENTE POR MEDIOS MECÁNICOS (MOTO CONFORMADORA), DE HASTA 5 CM DE ESPESOR, INCLUYE: ACAMELLONAMIENTO, EQUIPO, ACARREO DE MATERIAL PRODUCTO DE REMOCIÓN DE CARPETA ASFÁLTICA A LUGAR DE ACOPIO, PIEZAS DE DESGASTE, COMBUSTIBLES, MANO DE OBRA, EQUIPO, DESPERDICIOS, LIMPIEZAS, TRABAJO TERMINADO, ACARREOS LOCALES, CARGA Y ACARREO A KM SUBSECUENTES (11 A 15 KM APROX) DE MATERIAL PRODUCTO DE REMOCIÓN DE CARPETA ASFÁLTICA, EL TRASLADO SERA A PARQUE DE MAQUINARIA DE LA SOPMA | M3 | 114.8 | $162.92 | $18,703.22 |
| 8 | CARGA MECANICA Y ACARREO DE MATERIAL PRODUCTO DE EXCAVACION Y DEMOLICION EN CAMION DE VOLTEO AL 1er. KM, VOLUMEN MEDIDO COMPACTO. | M3 | 217.7 | $28.12 | $6,121.72 |
| 9 | ACARREO DE MATERIAL PRODUCTO DE EXCAVACION Y/O DEMOLICION EN CAMION DE VOLTEO A KILOMETROS SUBSECUENTES, AL TIRADERO OFICIAL AUTORIZADO MAS CERCANO AUTORIZADO POR LA SUPERVISION, VOLUMEN MEDIDO COMPACTO. | M3-KM | 2830.1 | $8.21 | $23,235.12 |
| | | | | **Totales por Partida** | **$212,879.75** |
| | | | | **Totales por Grupo** | **$212,879.75** |

Obra: **SOBRECARPETA ASFÁLTICA Y PAVIMENTO HIDRÁULICO AV. DE LOS MAESTROS (CALZADA ORIENTE)**

Ubicación: **TRAMO: ENTRE CALLE PROF. JOSÉ GUADALUPE PERALTA GÁMEZ Y BLVD. SIGLO XXI, AGUASCALIENTES Mpio.**

Contratista: **CONSORCIO INDUSTRIAL INTERNACIONAL AIRE, S.A. DE C.V. (713)**

| No. | Concepto | Unidad | Cantidad | Precio Unitario | Importe Total |
|---|---|---|---|---|---|
| | GRUPO: **SOBRECARPETA ASFALTICA** | | | | |
| | PARTIDA: **BACHEO PROFUNDO** | | | | |
| 11 | BACHEO PROFUNDO AISLADO UTILIZANDO MATERIAL CALIDAD BASE HIDRAULICA PARA MAS DE UN MILLON DE EJES EQUIVALENTES DEL BANCO QUE ELIJA EL CONTRATISTA, INCISO N.CSV.CAR-1.02.004/03 DE LAS NORMAS DE CONSTRUCCION DE CARR. DE LA SCT, BASE HIDRAULICA MEJORADA CON CEMENTO EN PROPORCION DE 40 KILOS DE CEMENTO POR CADA M3, INCLUYE: PREPARACION, PERFILADO, MATERIALES, MANO DE OBRA, HERRAMIENTA MENOR Y EQUIPO NECESARIO QUE SE REQUIERA PARA LOGRAR LA COMPACTACION DE 100 %, PVSM, ACARREOS DENTRO Y FUERA DE LA OBRA, PREPARACION DE MATERIAL, HUMEDECIDO, NIVELADO, TRASLADO DE UN PUNTO A OTRO DENTRO DE LA OBRA EN CUALQUIER VOLUMEN, MOVIMIENTO DE MAQUINARIA P.U.O.T | M3 | 61.324647 | $981.32 | $60,179.10 |
| | | | **Totales por Partida** | | **$60,179.10** |
| | PARTIDA: **SOBRE CARPETA ASFALTICA** | | | | |
| 14 | RENIVELACIONES CON CONCRETO ASFALTICO MEZCLA EN PLANTA EN CALIENTE ASFALTO MODIFICADO CON POLIMERO TIPO I, CUMPLIENDO LAS NORMAS SCT REFERENTES DE CONSTRUCCCION Y CONSERVACION, GRANULOMETRIA DENSA 3/4" A FINOS, MEDIDO COMPACTO AL NOVENTA Y CINCO PORCIENTO (95%), INCLUYE CARGA Y ACARREO EN TRAMOS AISLADOS, MATERIALES, MANO DE OBRA, ACARREO DE MATERIALES, Y MAQUINARIA Y EQUIPO AL SIGUIENTE PUNTO EN CUALQUIER VOLUEN, PERFILADO, LIMPIEZA DE HUESO Y GRAVA SUELTA, TRABAJO TERMINADO P.U.O.T | M3 | 44.96 | $4,891.83 | $219,936.68 |
| 16 | SUMINISTRO Y COLOCACION DE EMULSIONASFALTICA DE ROMPIMIENTO RAPIDO (RIEGO DE SELLADO NEGRO) EN CALIENTE A RAZON DE 1.5 LT/M2 (60% EMULSUON - 40% AGUA) EN TRAMOS AISLADOS O CONTINUO, (DOS CAPAS) Y O SELLADO DE CARPETA ASFALTICA EN REMATES CON GUARNICION EN EL ANCHO QUE LA SUPERVICION INDIQUE, CON USO DE BACHADOR O DE ESPREAS, INCLUYE: PREPARACION DE LA SUPERFICIE (CALAFATEO DE JUNTAS CON EMULSION Y ARENA Y GRIETAS EXISTENTES ) NO SE ACEPTA LEVENTAMIENTO DEL RIEGO, TRABAJO TERMINADO, P.U.O.T. | M2 | 233.1 | $21.31 | $4,967.36 |
| 18 | RIEGO DE LIGA CON EMULSION DE ROMPIMIENTO RAPIDO (ECR-65 %), INCLUYE, SUMINISTRO, ALMACENAMIENTO, CALENTAMIENTO, Y APLICACION DE LA EMULSION CON EQUIPO ESPECIAL PARA ESA ACTIVIDAD, ESPREAS O BACHADOR LIMPIAS Y ALINEADAS, CONTROL DE CALIDAD A CADA DOS REMESAS EN OBRA (INDEPENDIENTEMENTE DE LA CANTIDAD A UTILIZAR) EN LA PETROLIZADORA, A RAZON DE 0.8 LT DE EMULSION POR M2, O LO QUE INDIQUE EL LABORATORIO DE CALIDAD DEL CONTRATISTA, NO SE ACEPTAN "IMPREGNALICA", TRABAJO TERMINADO, P.U.O.T. | M2 | 2071.61 | $14.64 | $30,328.37 |
| 19 | SUMINISTRO Y COLOCACION DE CONCRETO ASFALTICO EN CALIENTE DE GRANULOMETRIA DENSA ELABORADA CON ASFALTO MODIFICADO TIPO I, AGREGADO 3/4" A FINOS, DE 5 CM DE ESPESOR, FORMADA Y COMPACTADO AL 95%, INCLUYE MATERIALES, QUE CUMPLAN LA NORMATIVA SCT-N-CMT-04-04, SCT-CMT-4-05-002, SCT-CMT-4-05-003, SCT-CMT-4-05-004, SCT-CTR-CAR-1-04-006-14 APLICADAS AL DIA DE HOY, DISEÑO MARSHALL (DEVERÁ SER AUTORIZADO POR EL LABORATORIO DE CALIDAD DE SOPMA AL MENOS 3 DIAS ANTES DE INICIO DE TENDIDO DE LA MEZCLA ASFALTICA), INCUYE: TRAMO DE PRUEBA AL INICIO PARA REVISION Y AUTORIZACION DEL ESPESOR POR PARTE DEL SUPERVISOR, EL CONTRATISTA DEBERÁ PREVEER EL SUMINISTRO Y TIEMPOS MUERTOS POR MOVIMIENTOS DEL TREN DE MAQUINAS DE TRABAJO EN TRAMOS AISLADOS. TRABAJO TERMINADO P.U.O.T. Y LIMPIEZAS DE GRANZON Y HUESO LATERAL. | M2 | 2071.61 | $264.13 | $547,174.35 |

Obra: **SOBRECARPETA ASFÁLTICA Y PAVIMENTO HIDRÁULICO AV. DE LOS MAESTROS (CALZADA ORIENTE)**

Ubicación: **TRAMO: ENTRE CALLE PROF. JOSÉ GUADALUPE PERALTA GÁMEZ Y BLVD. SIGLO XXI, AGUASCALIENTES Mpio.**

Contratista: **CONSORCIO INDUSTRIAL INTERNACIONAL AIRE, S.A. DE C.V. (713)**

| No. | Concepto | Unidad | Cantidad | Precio Unitario | Importe Total |
|---|---|---|---|---|---|
| | GRUPO: **SOBRECARPETA ASFALTICA** | | | | |
| | PARTIDA: **SOBRE CARPETA ASFALTICA** | | | | |
| 20 | COMPACTACION SOBRE MORTERO ASFALTICO TENDIDO EN APROCHES CON GUARNICIONES CON EQUIPO LIGERO (PLANCHITA), INCLUYE: MANO DE OBRA Y EQUIPO, TRABAJO TERMINADO. | M2 | 277.61 | $309.61 | $85,950.83 |
| 21 | SUMINISTRO Y COLOCACION DE JUNTA WABO ESL 400 ELASTOFLEX BRIDGE DUREZA SHORE TIPO A, JUNTA DE EXPANSION PARA PUENTES CONDICIONES DE LOSA A LOSA, INCLUYE: PREPARACION Y TERMINADO DE LOSA, SEGUN ESPECIFICACION DEL FABRICANTE, ELEMENTOS DE FIJACION QUIMICOS Y MECANICOS, CARGAS Y ACARREOS, DEMOLICIONES, CONCRETO MR=42 KG/CM2, ARMADO DE LOSAS DE RODAMIENTO, CURADO Y COLADO DE LOSAS ( LOSAS DE 50 CM DE ANCHO ARMADAS CON 8 VRS No. 4 y estribos No. 3 @ 15 cm,), PREPARACION DE LOSA A BASE DE APUNTALAMIENTO INFERIOR SUFICIENTE SEGUN LA SUPERVISION, DEMOLICION DEL AREA NECESARIA PARA LA NUEVA LOSA (3 CM ABAJO DEL ACERO POR TEMPERATURA) PARA AMARRAR EL NUEVO ARMADO, ELEMENTOS QUIMICOS PARA UNIR CONCRETO NUEVO CON CONCRETO VIEJO, LIMPIEZA CON AIRE DEL ELEMENTO ANTES DE COLAR, COLADO, CURADO CON MEMBRANA QUIMICA Y RAYADO SEGUN LAS LOSAS EXISTENTES, COLOCACION DE JUNTA Y HERRAJES, CORTE CON DISCO, TRAZO, CORTES Y DESPERDICIOS, TRABAJO TERMINADO, LIMPIEZAS DE LOS ELEMENTOS Y LIMPIEZA FINA DEL AREA, P.U.O.T | ML | 19.86 | $20,423.94 | $405,619.45 |
| | | | | **Totales por Partida** | **$1,293,977.04** |
| | | | | **Totales por Grupo** | **$1,354,156.14** |

Obra: **SOBRECARPETA ASFÁLTICA Y PAVIMENTO HIDRÁULICO AV. DE LOS MAESTROS (CALZADA ORIENTE)**

Ubicación: **TRAMO: ENTRE CALLE PROF. JOSÉ GUADALUPE PERALTA GÁMEZ Y BLVD. SIGLO XXI, AGUASCALIENTES Mpio.**

Contratista: **CONSORCIO INDUSTRIAL INTERNACIONAL AIRE, S.A. DE C.V. (713)**

| No. | Concepto | Unidad | Cantidad | Precio Unitario | Importe Total |
|---|---|---|---|---|---|
| | GRUPO: **CONCRETO HIDRAULICO** | | | | |
| | PARTIDA: **EXCAVACIONES, ACARREOS Y TERRACERIAS** | | | | |
| 22 | EXCAVACION EN CORTE CON MAQUINA HASTA UNA PROFUNDIDAD DE 80 CM, EN MATERIAL TIPO II, INCLUYE: AFLOJE Y EXTRACCION DE MATERIAL, ACARREOS AL LUGAR DE ACOPIO PARA SU CARGA Y ACARREO FUERA DE LA OBRA, VOLUMEN MEDIDO COMPACTO. | M3 | 1718.6 | $72.38 | $124,392.27 |
| 23 | COMPACTACION DE TERRENO NATURAL AL 90% DE SU P.V.S.M EN SU COMPACTACION., INCLUYE ESCARIFICADO, TENDIDO, HOMOGENIZADO, HUMEDECIDO OPTIMO NIVELADO Y COMPACTADO EN CAPAS DE 20 CM, CALIDAD Limite liquido máximo 50%, Valor de Soporte California (CBR) mínimo 15%, Expansión máxima 5%, Grado de Compactación minimo 90% ± 2, Y TODO LO NECESARIO PARA SU CORRECTA EJECUCION, | M2 | 2149.16 | $16.47 | $35,396.67 |
| 24 | MEJORAMIENTO DE TERRENO NATURAL ADICIONANDO CAL AL MATERIAL DEL LUGAR, EXCARIFICADO, ADICIONADO DEL CAL AL 3% PVSS, MEZCLADO, HUMEDECIDO, TENDIDO Y COMPACTADO AL 90 %, EN CAPAS DE 20 CM DE ESPESOR MAXIMO, TRABAJO TERMINADO | M2 | 1095.05 | $49.48 | $54,183.07 |
| 25 | FORMACION Y COMPACTACION DE SUB-RRASANTE, CON EL USO DE EQUIPO MAYOR, HASTA ALCANZAR EL 100% AASHTO MODIFICADA. EN CAPAS DE 20 CM MAXIMO, INCLUYE: SUMINISTRO DE MATERIAL DE BANCO QUE CUMPLA CON LA NORMA, HUMEDAD OPTIMA Y TODO LO NECESARIO PARA SU CORRECTA COLOCACION, EL MATERIAL DEBERA CUMPLIR CON UN C.B.R. DEL 60% PARA LO CUAL EL CONTRATISTA DEBERA PROPONER UN BANCO DE MATERIAL Y UN FRENTE, DEBERA PRESENTAR EL ESTUDIO DE CALIDAD QUE AVALE EL CUMPLIMIENTO AL 100 % DE LA NORMA Y DEMAS CARACTERISTICAS SOLICITADAS, P.U.O.T. | M3 | 425.67 | $262.84 | $111,883.10 |
| 26 | FORMACION Y COMPACTACION DE SUB-BASE PARA MENOS DE UN MILLON DE EJES EQUIVALENTES, CON EL USO DE EQUIPO MAYOR, HASTA ALCANZAR EL 100% AASHTO MODIFICADA. EN CAPAS DE 20 CM MAXIMO, INCLUYE: SUMINISTRO DE MATERIAL DE BANCO QUE CUMPLA CON LA NORMA, HUMEDAD OPTIMA Y TODO LO NECESARIO PARA SU CORRECTA COLOCACION, EL MATERIAL DEBERA CUMPLIR CON UN C.B.R. DEL 50% PARA LO CUAL EL CONTRATISTA DEBERA PROPONER UN BANCO DE MATERIAL Y UN FRENTE, DEBERA PRESENTAR EL ESTUDIO DE CALIDAD QUE AVALE EL CUMPLIMIENTO AL 100 % . Y DEMAS CARACTERISTICAS SOLICITADAS, P.U.O.T. | M3 | 426.65 | $262.84 | $112,140.69 |
| 27 | FORMACION Y COMPACTACION DE BASE HIDRAULICA PARA MENOS DE UN MILLON DE EJES EQUIVALENTES DE 20 CMS. DE ESPESOR, PARA SUPERFICIE DE RODAMIENTO DE CONCRETO HIDRAULICO, CON MATERIAL 100% TRITURADO O MEZCLA DE 1 1/2" A FINOS QUE CUMPLA CON LA NORMA, COMPACTADA AL 100 % DE PRUEBA AASHTO. COMBINANDO COMPACTADOR DE RODILLO EN BAJA Y MUERTO Y LLANTEO CON EQUIPO PESADO (CAMION DE VOLTEO CARGADO AL MAXIMO), INCLUYE HOMOGENEIZADO, TENDIDO, COMPACTADO, E INCORPORACION DE AGUA HASTA ALCANZAR LA HUMEDAD OPTIMA Y NIVELACIONES. | M3 | 426.65 | $658.88 | $281,111.15 |
| 28 | CARGA MECANICA Y ACARREO DE MATERIAL PRODUCTO DE EXCAVACION Y DEMOLICION EN CAMION DE VOLTEO AL 1er. KM, VOLUMEN MEDIDO COMPACTO. | M3 | 1718.24 | $28.12 | $48,316.91 |
| 29 | ACARREO DE MATERIAL PRODUCTO DE EXCAVACION Y/O DEMOLICION EN CAMION DE VOLTEO A KILOMETROS SUBSECUENTES, AL TIRADERO OFICIAL AUTORIZADO MAS CERCANO AUTORIZADO POR LA SUPERVISION, VOLUMEN MEDIDO COMPACTO. | M3-KM | 29298.06 | $8.21 | $240,537.07 |
| | | | | **Totales por Partida** | **$1,007,960.93** |

Obra: **SOBRECARPETA ASFÁLTICA Y PAVIMENTO HIDRÁULICO AV. DE LOS MAESTROS (CALZADA ORIENTE)**

Ubicación: **TRAMO: ENTRE CALLE PROF. JOSÉ GUADALUPE PERALTA GÁMEZ Y BLVD. SIGLO XXI, AGUASCALIENTES Mpio.**

Contratista: **CONSORCIO INDUSTRIAL INTERNACIONAL AIRE, S.A. DE C.V. (713)**

| No. | Concepto | Unidad | Cantidad | Precio Unitario | Importe Total |
|---|---|---|---|---|---|
| | GRUPO: **CONCRETO HIDRAULICO** | | | | |
| | PARTIDA: **PAVIMENTO** | | | | |
| 31 | SUMINISTRO Y COLOCACION DE CANASTILLAS O PASAJUNTAS TIPO PESADO DE SECCION NOMINAL DE BARRA PRINCIPAL DE 46 CMS, CON REDONDO LISO DE 1 1/4" SOLDADO EN EXTREMOS ALTERNOS @ 30 CMS. SEPARADORES, ATIESADORES, BASES Y SOPORTES DE ACERO F´y= 4,200 DE DIAMETRO 5/16", DE ACUERDO A DISEÑO ANEXO EN PLANOS, INCLUYE: MATERIAL, MANO DE OBRA, CORTES, PULIDO EN CORTES, ANCLAJES, FUNDAS DE PLASTICO EN LOS EXTREMOS NO SOLDADOS, AJUSTES, DESPERDICIOS, ACARREOS, FLETES DENTRO Y FUERA DE LA OBRA. | ML | 731.3 | $800.94 | $585,727.42 |
| 32 | SUMINISTRO Y COLOCACION DE RELLENO PARA JUNTAS DE EXPANSION A BASE DE ESPUMA DE POLIETILENO DE CELDAS CERRADAS (FOAMTECH) DE 1/2" DE ESPESOR Y 20 CM DE ALTURA DE ACUERDO AL DISEÑO ANEXO EN PLANOS, INCLUYE: MATERIAL, SELLADOR AUTONIVELANTE,MANO DE OBRA, CORTES, AJUSTES, DESPERDICIOS, ACARREO, FLETES DENTRO Y FUERA DE LA OBRA DE ACUERDO A ESPECIFICACIONES DE CONTROL DE CALIDAD (LA FICHA TECNICA DEL FABRICANTE DEBERA CUMPLIR CON LAS ESPECIFICACIONES DE LA NORMA) | ML | 527.56 | $67.45 | $35,583.92 |
| | | | | **Totales por Partida** | **$621,311.34** |
| | PARTIDA: **DENTELLONES DE CONCRETO** | | | | |
| 33 | EXCAVACION A MANO EN MATERIAL TIPO B DE 0.00 A 2.00 M DE PROFUNDIDAD, INCLUYE: TRASPALEO VERTICAL, AFINE DE TALUDES CONSERVACION DE LA EXCAVACION Y ACARREO DE MATERIAL AL LUGAR DE ACOPIO PARA SU POSTERIOR CARGA Y ACARREO FUERA DE LA OBRA. | M3 | 2.26 | $261.33 | $590.61 |
| 34 | COMPACTACION DE TERRENO NATURAL AL 90% DE SU P.V.S.M EN SU COMPACTACION., INCLUYE ESCARIFICADO, TENDIDO, HOMOGENIZADO, HUMEDECIDO OPTIMO NIVELADO Y COMPACTADO EN CAPAS DE 20 CM, CALIDAD Limite liquido máximo 50%, Valor de Soporte California (CBR) mínimo 15%, Expansión máxima 5%, Grado de Compactación minimo 90% ± 2, Y TODO LO NECESARIO PARA SU CORRECTA EJECUCION. | M2 | 2.82 | $20.75 | $58.52 |
| 35 | RELLENO COMPACTADO AL 90% CON MATERIAL DE BANCO EN CAPAS DE 20 CM UTILIZANDO BAILARINA. INCLUYE: SUMINISTRO DE TEPETATE (MATERIAL DE BANCO) EN LA OBRA, ABUNDAMIENTO, ACARREOS DENTRO DE LA OBRA, CRIBADO, RETIRO DE MATERIAL, MANO DE OBRA Y EQUIPO, LIMPIEZAS, TRABAJO TERMINADO. | M3 | 0.56 | $312.59 | $175.05 |
| 36 | CARGA MECANICA Y ACARREO DE MATERIAL PRODUCTO DE EXCAVACION Y DEMOLICION EN CAMION DE VOLTEO AL 1er. KM, VOLUMEN MEDIDO COMPACTO. | M3 | 1.13 | $28.12 | $31.78 |
| 37 | ACARREO DE MATERIAL PRODUCTO DE EXCAVACION Y/O DEMOLICION EN CAMION DE VOLTEO A KILOMETROS SUBSECUENTES, AL TIRADERO OFICIAL AUTORIZADO MAS CERCANO AUTORIZADO POR LA SUPERVISION, VOLUMEN MEDIDO COMPACTO. | M3-KM | 21.97 | $8.21 | $180.37 |
| 38 | CONSTRUCCION DE DENTELLON RECTO Y/O CURVO 20-20X40 CM DE SECCION, CON CONCRETO PREMEZCLADO MR=42 KGF/CM2, TMA 1 1/2", R.R 3 DIAS. REVENIMIENTO NORMAL DE 10+-2 CM, GRAVA TRITURADA, ACABADO CON DOBLADOR Y PULIDO. INCLUYE: TRAZO, NIVELACION, CIMBRADO, COLADO, VIBRADO, DESCIMBRADO, , Y CURADO CON MEMBRANA QUIMICA APLICADA CON ASPERSOR Y LIMPIEZA, REMATE CON PAVIMENTO EXISTENTE DEL MISMO MATERIAL Y TIPO, TRABAJO TERMINADO P.U.O.T. | ML | 14.1 | $341.50 | $4,815.15 |
| | | | | **Totales por Partida** | **$5,851.47** |

Obra: **SOBRECARPETA ASFÁLTICA Y PAVIMENTO HIDRÁULICO AV. DE LOS MAESTROS (CALZADA ORIENTE)**

Ubicación: **TRAMO: ENTRE CALLE PROF. JOSÉ GUADALUPE PERALTA GÁMEZ Y BLVD. SIGLO XXI, AGUASCALIENTES Mpio.**

Contratista: **CONSORCIO INDUSTRIAL INTERNACIONAL AIRE, S.A. DE C.V. (713)**

| No. | Concepto | Unidad | Cantidad | Precio Unitario | Importe Total |
|---|---|---|---|---|---|
| | GRUPO: **CONCRETO HIDRAULICO** | | | | |
| | PARTIDA: **GUARNICIONES** | | | | |
| 39 | EXCAVACION A MAQUINA Y/O A MANO EN MATERIAL TIPO II, EN SECO O PRESENCIA DE AGUA, INCLUYE. CORTE DE RAIZ DE CUALQUIER TAMAÑO Y GROSOR, HASTA UNA PROFUNDIDAD DE 40 CM DESPUES DE DESMONTE, DESPALME Y/O DEMOLICION DE SUPERFICIE O ELEMENTO ESTRUCTURAL O DE ACABADO, PROTECCION DE AREAS ADYACENTES, SIN DAÑAR AREAS ALEDAÑAS, CARGA Y ACARREO A TIRADERO OFICIAL, CONSERVACION DE LA MISMA, TRABAJO TERMINADO, LIMPIEZAS. | M3 | 2.4 | $144.25 | $346.20 |
| 40 | COMPACTACION DE TERRENO NATURAL AL 90% DE SU P.V.S.M EN SU COMPACTACION., INCLUYE ESCARIFICADO, TENDIDO, HOMOGENIZADO, HUMEDECIDO OPTIMO NIVELADO Y COMPACTADO EN CAPAS DE 20 CM, CALIDAD Limite liquido máximo 50%, Valor de Soporte California (CBR) mínimo 15%, Expansión máxima 5%, Grado de Compactación minimo 90% ± 2, Y TODO LO NECESARIO PARA SU CORRECTA EJECUCION, | M2 | 4 | $20.75 | $83.00 |
| 41 | CONSTRUCCION DE GUARNICION RECTA Y/O CURVA TRAPEZOIDAL 15-20X40 CM DE SECCION CON CONCRETO PREMEZCLADO MR=38 KGF/CM2, R.N.REVENIMIENTO DE 8 A 10 CM, T.M.A. 3/4", GRAVA TRITURADA, ACABADO PULIDO EN PARTE DE SUPERIOR Y DOBLADOR EN ARISTAS, INCLUYE: COMPACTADO DE PLANTILLA, CIMBRADO, COLADO, VIBRADO, ACABADO, DESCIMBRADO, ALINEADO, NIVELADO, Y CURADO EN SU PARTE SUPERIOR CON MEMBRANA BASE AGUA A RAZON DE 1 LTO/M2, JUNTA DE AISLAMIENTO LONGITUDINAL AL COMBINAR CON OTRO ELEMENTO Y TRANSVERSAL @ 30 MT MAXIMO, SELLADO CON SELLADOR AUTONIVELANTE LONGITUDINAL, TRABAJO TERMINADO, .P.U.O.T. | ML | 20 | $312.64 | $6,252.80 |
| 42 | RELLENO COMPACTADO AL 90% CON MATERIAL DE BANCO EN CAPAS DE 20 CM UTILIZANDO BAILARINA. INCLUYE: SUMINISTRO DE TEPETATE (MATERIAL DE BANCO) EN LA OBRA, ABUNDAMIENTO, ACARREOS DENTRO DE LA OBRA, CRIBADO, RETIRO DE MATERIAL, MANO DE OBRA Y EQUIPO, LIMPIEZAS, TRABAJO TERMINADO. | M3 | 0.8 | $312.59 | $250.07 |
| 43 | CARGA MECANICA Y ACARREO DE MATERIAL PRODUCTO DE EXCAVACION Y DEMOLICION EN CAMION DE VOLTEO AL 1er. KM, VOLUMEN MEDIDO COMPACTO. | M3 | 2.4 | $28.12 | $67.49 |
| 44 | ACARREO DE MATERIAL PRODUCTO DE EXCAVACION Y/O DEMOLICION EN CAMION DE VOLTEO A KILOMETROS SUBSECUENTES, AL TIRADERO OFICIAL AUTORIZADO MAS CERCANO AUTORIZADO POR LA SUPERVISION, VOLUMEN MEDIDO COMPACTO. | M3-KM | 31.2 | $8.21 | $256.15 |
| | | | | **Totales por Partida** | **$7,255.71** |
| | | | | **Totales por Grupo** | **$1,642,379.46** |

Obra: **SOBRECARPETA ASFÁLTICA Y PAVIMENTO HIDRÁULICO AV. DE LOS MAESTROS (CALZADA ORIENTE)**

Ubicación: **TRAMO: ENTRE CALLE PROF. JOSÉ GUADALUPE PERALTA GÁMEZ Y BLVD. SIGLO XXI, AGUASCALIENTES Mpio.**

Contratista: **CONSORCIO INDUSTRIAL INTERNACIONAL AIRE, S.A. DE C.V. (713)**

| No. | Concepto | Unidad | Cantidad | Precio Unitario | Importe Total |
|---|---|---|---|---|---|
| | GRUPO: **OBRA COMPLEMENTARIA** | | | | |
| | PARTIDA: **OBRA COMPLEMENTARIA** | | | | |
| 53 | RE NIVELACIÓN DE POZO DE VISITA HASTA 30 cm DE ALTURA. INCLUYE: RETIRO SIN RECUPERACIÓN DE BROCAL EXISTENTE, DEMOLICIONES, NIVELADO CON TABIQUE ROJO RECOCIDO 7X14X28, ASENTADO CON MORTERO CEMENTO-ARENA 1:3 DE 28 cm DE ESPESOR, APLANADO CON MORTERO CEMENTO-ARENA 1:3 , PLOMEADO, NIVELADO, DEMOLICIONES, CARGAS Y ACARREOS DENTRO DE LA OBRA, LIMPIEZAS Y TODO LO NECESARIO PARA SU CORRECTA EJECUCIÓN DEL CONCEPTO. | PZA | 19 | $1,305.53 | $24,805.07 |
| 54 | CONSTRUCCION DE LOSA DE DIAMANTE DE CONCRETO MR= 45 , T.M.A. DE 3/4" (19MM), GRAVA TRITURADA, REVENIMIENTO DE 8+-2.5CM CM, FRAGUADO RAPIDOA A 3 DIAS, DE 25 CM DE ESPESOR, EN POZO DE VISITA, Y 1.50 M POR LADO, INCLUYE: SUMINISTRO DE MATERIALES, ESPUMA DE POLIURETANO DE ALTA DENSIDAD EN TODO EL PERIMETRO EXTERIOR DE 1/2" ASI COMO DE LAS JUNTAS DIAGONALES PARA FORMAR 4 PARTES, BROCAL Y TAPA DE Fo. Fo. TIPO PESADO, (165 KG), CIMBRADO, COLADO, VIBRADO, DESCIMBRADO, CURADO CON MEMBRANA QUIMICA BASE AGUA, APLANADO FINO EN RECEPCION DE BROCAL, CORTES CON CORTADORA DE DISCO DE 5 CM ENTRE JUNTAS DIAGONALES FORMADO 8 PIEZAS Y SELLADO DE JUNTAS Y CORTES CON MATERIAL PREFORMADO Y SELLADOR AUTONIVELANTE, MANO DE OBRA, ACARREOS DE MATERIAL DENTRO Y FUERA DE LA OBRA, TRABAJO TERMINADO. P.U.O.T. | PZA | 22 | $10,813.10 | $237,888.20 |
| 55 | RENIVELACION DE RASANTE (PARTE SUPERIOR DE CAIMAN) DE 5.0 M2 A MAXIMO 6.5 M2 Y HASTA 0.3 MTS DE ALTURA. INCLUYE: DESMONTAJE, DEMOLICION Y RETIRO CON RECUPERACION DE REJILLA EXISTENTE, NIVELADO CON TABIQUE ASENTADO CON MORTERO CEMENTO-ARENA 1:3 DE 28 cm DE ESPESOR, APLANADO CON MORTERO CEMENTO-ARENA 1:3, ACABADO PULIDO, COLOCACION DE REJILLA RECUPERADA Y REHABILITADA SEGUN PROYECTO O SIMILAR A LA EXISTENTE, CONSIDERAR LA CONSTRUCCION DE UNA CADENA DE CERRAMIENTO SECCION 28*20, CON 4 VRS No 4 y ESTRIBOS DEL No. 2 @ 20, CONCRETO F'c= 250 KG/CM2 TMA 19 MM RN. EN EL PEIMETRO DEL CAIMAN, PLOMEADO, CORTES, ANCLAS DE ACERO, REPOSICIONES, SOLDADURA EN TALLER Y CAMPO, DESPERDICIOS, NIVELADO, DEMOLICIONES, CARGAS Y ACARREOS DENTRO Y FUERA DE LA OBRA MAQUINARIA, MANO DE OBRA MATERIALES, LIMPIEZAS TRABAJO TERMINADO. PUOT. | PZA | 1 | $16,482.60 | $16,482.60 |
| 56 | LIMPIEZA Y DESASOLVE DE POZOS DE VISITA Y LINEAS DE ALCANTARILLADO EXISTENTE CON CAMION TIPO VACTOR. INCLUYE: RESANE INTERIOR DEL POZO Y REMTE DE POZO CO TUBO CON SELLADOR, FESTER Y MORTERO 1:3, MANO DE OBRA, SUMINISTRO DE AGUA EN PIPA, HERRAMIENTAS Y EQUIPO PARA SU CORRECTA EJECUCION, LIMPIEZAS, RENTA DE CAMION VACTOR HASTA LA CORRECTA LIMPIEZA DE LAS LINEAS EXISTENTES DE POZO A POZO, ASI COMO EL TRASLADO DE LOS DESECHOS HASTA TIRADERO AUTORIZADO MEDIDO POZO A POZO. | LOTE | 2 | $5,988.36 | $11,976.72 |
| 57 | LIMPIEZA Y DESASOLVE DE CAIMANES DESDE 5.0 M2 Y HASTA 6.50 M2 X HASTA 1.50 M DE PROFUNDIDAD, INCLUYE: MANO DE OBRA, SUMINISTRO DE AGUA EN PIPA, HERRAMIENTAS Y EQUIPO PARA SU CORRECTA EJECUCION, LIMPIEZAS MANUALES, CARGAS Y ACARREOS LOCALES ASI COMO RETIRO DE MATERIAL PRODUCTO DEL DESASOLVE A TIRADERO AUTORIZADO. | PZA | 1 | $1,052.65 | $1,052.65 |
| | | | **Totales por Partida** | | **$292,205.24** |
| | PARTIDA: **LIMPIEZAS** | | | | |
| 58 | LIMPIEZA GENERAL DE LA OBRA, INCLUYE: BARRIDO, CARGA, ACARREOS Y RETIRO DE ESCOMBROS FUERA DE LA OBRA, TRABAJO TERMINADO. | M2 | 4230 | $13.94 | $58,966.20 |
| | | | **Totales por Partida** | | **$58,966.20** |

Obra: **SOBRECARPETA ASFÁLTICA Y PAVIMENTO HIDRÁULICO AV. DE LOS MAESTROS (CALZADA ORIENTE)**

Ubicación: **TRAMO: ENTRE CALLE PROF. JOSÉ GUADALUPE PERALTA GÁMEZ Y BLVD. SIGLO XXI, AGUASCALIENTES Mpio.**

Contratista: **CONSORCIO INDUSTRIAL INTERNACIONAL AIRE, S.A. DE C.V. (713)**

| No. | Concepto | Unidad | Cantidad | Precio Unitario | Importe Total |
|---|---|---|---|---|---|
| | GRUPO: **OBRA COMPLEMENTARIA** | | | | |
| | PARTIDA: **SEÑALIZACION HORIZONTAL** | | | | |
| 59 | SUMINISTRO Y APLICACIÓN DE PINTURA EPOXICA BASE SOLVENTE COLOR AZUL (PANTONE 294) EN RAMPAS PARA PERSONAS CON DISCAPACIDAD CUALQUIER SECCIÓN SEGÚN PLANOS. INCLUYE: TRAZO, MANO DE OBRA, LIMPIEZA PREVIA DE SUPERFICIE, EQUIPO NECESARIO PARA SU EJECUCIÓN, Y TODO LO NECESARIO PARA SU CORRECTA EJECUCIÓN, TRABAJO TERMINADO. | M2 | 1.62 | $549.52 | $890.22 |
| 60 | SUMINISTRO Y APLICACIÓN DE LOGOTIPO A (SILLA DE RUEDAS) EN PINTURA EPOXICA BASE SOLVENTE COLOR BLANCO EN RAMPAS PARA PERSONAS CON DISCAPACIDAD TAMAÑO Y DISEÑO SEGÚN PLANOS. INCLUYE: TRAZO, ENMASCARILLADO, PLANTILLA, MANO DE OBRA, LIMPIEZA PREVIA DE SUPERFICIE, EQUIPO NECESARIO PARA SU EJECUCIÓN, Y TODO LO NECESARIO PARA SU CORRECTA EJECUCIÓN, TRABAJO TERMINADO. | PZA | 2 | $146.55 | $293.10 |
| 61 | SUMINISTRO Y APLICACIÓN DE PINTURA BASE SOLVENTE PARA MARCAS EN GUARNICIONES CLASIFICACION M-12.1, M12.2 APLICADA SOBRE GUARNICIONES Y DENTELLONES DE CUALQUIER COLOR, SEGÚN SE REQUIERA Y SEGÚN NORMA S.C.T. SECADO AL TACTO EN 5 MIN Y AL DURO EN 30 MIN CON MICRO ESFERA , DESARROLLO DE 35 CM. INCLUYE: MATERIALES Y ESPECIFICACIONES QUE CUMPLAN CON LA NORMATIVA N-CMT-5-01-001/05, N-PRY-CAR-10-01-002/13 APLICADAS AL DIA DE HOY, TRAZO, MANO DE OBRA, LIMPIEZA PREVIA DE SUPERFICIE, EQUIPO NECESARIO PARA SU EJECUCIÓN, Y TODO LO NECESARIO PARA SU CORRECTA EJECUCIÓN, TRABAJO TERMINADO. | ML | 834.5 | $23.21 | $19,368.75 |
| 62 | SUMINISTRO Y APLICACIÓN DE PINTURA TERMOPLASTICA ALQUIDALICA DE 120 MILESIMAS DE " (in) EN RAYA SEPARADORA DE SENTIDOS DE CIRCULACION CLASIFICACIÓN M - 1.1, LÍNEA CONTINUA SENCILLA DE DIVISIÓN DE CARRILES DE FRENTE EN PISO, DE 10 CM DE ANCHO, COLOR BLANCO Y/O AMARILLO CON MICRO ESFERA SEGUN MANUAL DE SEÑALIZACIÓN VIAL Y DISPOSITIVOS DE SEGURIDAD SICT, SECADO AL TACTO EN 5 MIN Y AL DURO EN 30 MIN. INCLUYE: MATERIALES Y ESPECIFICACIONES QUE CUMPLAN CON LA NORMATIVA N-CMT-5-01-001/13, N-PRY-CAR-10-01-002/13 APLICADAS AL DIA DE HOY, MATERIAL APLICADO EN SU ESTADO DE FUSION A UNA TEMPERATURA MINIMA DE 204 C, LA SUPERFICIE DE CONCRETO O ASFALTO NO DEBE PRESENTAR UNA TEMPERATURA MENOR A LOS 10 C, ;TIEMPO DE SECADO EN RANGOS DE TEMPERATURA DE 10 C DEL SUSTRATO 2 MINUTOS, Y NO MAS DE 10 MINUTOS CUANDO EL SUSTRATO OSCILA ALREDEDOR DE 54C, TRAZO, ENMASCARILLADO, MANO DE OBRA, LIMPIEZA PREVIA Y FINAL DE SUPERFICIE, EQUIPO NECESARIO PARA SU EJECUCIÓN, Y TODO LO NECESARIO PARA SU CORRECTA EJECUCIÓN, TRABAJO TERMINADO. | ML | 28 | $39.07 | $1,093.96 |

Obra: **SOBRECARPETA ASFÁLTICA Y PAVIMENTO HIDRÁULICO AV. DE LOS MAESTROS (CALZADA ORIENTE)**

Ubicación: **TRAMO: ENTRE CALLE PROF. JOSÉ GUADALUPE PERALTA GÁMEZ Y BLVD. SIGLO XXI, AGUASCALIENTES Mpio.**

Contratista: **CONSORCIO INDUSTRIAL INTERNACIONAL AIRE, S.A. DE C.V. (713)**

| No. | Concepto | Unidad | Cantidad | Precio Unitario | Importe Total |
|---|---|---|---|---|---|
| | GRUPO: **OBRA COMPLEMENTARIA** | | | | |
| | PARTIDA: **SEÑALIZACION HORIZONTAL** | | | | |
| 63 | SUMINISTRO Y APLICACIÓN DE PINTURA TERMOPLASTICA ALQUIDALICA DE 120 MILESIMAS DE " (in) EN RAYA SEPARADORA DE SENTIDOS DE CIRCULACION CLASIFICACIÓN M - 1.2, RAYA DISCONTINUA SENCILLA, DE DIVISIÓN DE CARRILES PARA VELOCIDADES MENORES A 60 KM/HR DE FRENTE EN PISO, DESARROLLO DE 2.50 ML X 0.10 MTS DE ANCHO, CON UNA SEPARACIÓN DE 5.00 MTS ENTRE SI PROMEDIO, A BASE DE PINTURA PARA TRAFICO COLOR BLANCO CON MICRO ESFERA SEGÚN MANUAL DE SEÑALIZACIÓN VIAL Y DISPOSITIVOS DE SEGURIDAD SICT (S.C.T). INCLUYE: MATERIALES Y ESPECIFICACIONES QUE CUMPLAN CON LA NORMATIVA N-CMT-5-01-001/13, N-PRY-CAR-10-01-002/13 APLICADAS AL DIA DE HOY, MATERIAL APLICADO EN SU ESTADO DE FUSION A UNA TEMPERATURA MINIMA DE 204 C, LA SUPERFICIE DE CONCRETO O ASFALTO NO DEBE PRESENTAR UNA TEMPERATURA MENOR A LOS 10 C, ;TIEMPO DE SECADO EN RANGOS DE TEMPERATURA DE 10 C DEL SUSTRATO 2 MINUTOS, Y NO MAS DE 10 MINUTOS CUANDO EL SUSTRATO OSCILA ALREDEDOR DE 54C, TRAZO, ENMASCARILLADO, MANO DE OBRA, LIMPIEZA PREVIA Y FINAL DE SUPERFICIE, EQUIPO NECESARIO PARA SU EJECUCIÓN, Y TODO LO NECESARIO PARA SU CORRECTA EJECUCIÓN, TRABAJO TERMINADO. | ML | 300 | $39.07 | $11,721.00 |
| 64 | SUMINISTRO Y APLICACIÓN DE PINTURA TERMOPLASTICA ALQUIDALICA DE 120 MILESIMAS DE " (in) EN RAYA EN LA ORILLA DEL ARROYO VIAL CLASIFICACIÓN M - 3.3, CONTINUA IZQUIERDA, PARA VIALIDADES URBANAS DE FRENTE EN PISO, DE 10 CM DE ANCHO Y SEPARADA 15 CM. DE LA GUARNICION, A BASE DE PINTURA PARA TRAFICO COLOR BLANCO CON MICRO ESFERA SEGÚN MANUAL DE SEÑALIZACIÓN VIAL Y DISPOSITIVOS DE SEGURIDAD SICT (S.C.T)., INCLUYE: MATERIALES Y ESPECIFICACIONES QUE CUMPLAN CON LA NORMATIVA N-CMT-5-01-001/13, N-PRY-CAR-10-01-002/13 APLICADAS AL DIA DE HOY, MATERIAL APLICADO EN SU ESTADO DE FUSION A UNA TEMPERATURA MINIMA DE 204 C, LA SUPERFICIE DE CONCRETO O ASFALTO NO DEBE PRESENTAR UNA TEMPERATURA MENOR A LOS 10 C, ;TIEMPO DE SECADO EN RANGOS DE TEMPERATURA DE 10 C DEL SUSTRATO 2 MINUTOS, Y NO MAS DE 10 MINUTOS CUANDO EL SUSTRATO OSCILA ALREDEDOR DE 54C, TRAZO, ENMASCARILLADO, MANO DE OBRA, LIMPIEZA PREVIA Y FINAL DE SUPERFICIE, EQUIPO NECESARIO PARA SU EJECUCIÓN, Y TODO LO NECESARIO PARA SU CORRECTA EJECUCIÓN, TRABAJO TERMINADO. | ML | 834.5 | $39.07 | $32,603.92 |
| 65 | SUMINISTRO Y APLICACIÓN DE PINTURA TERMOPLASTICA ALQUIDALICA DE 120 MILESIMAS DE " (in) EN RAYA GUIA EN ZONAS DE TRANSICION CLASIFICACIÓN M - 4, PARA INDICAR LÍNEA GUÍA EN ZONA DE TRANSICIÓN DE FRENTE EN PISO, DESARROLLO DE 2.00 X 0.10 MTS, CON UNA SEPARACIÓN DE 4.00 MTS ENTRE SI PROMEDIO, A BASE DE PINTURA PARA TRAFICO COLOR BLANCO CON MICRO ESFERA SEGÚN MANUAL DE SEÑALIZACIÓN VIAL Y DISPOSITIVOS DE SEGURIDAD SICT (S.C.T)., MCA. COMEX O SIMILAR, SECADO AL TACTO EN 5 MIN Y AL DURO EN 30 MIN.INCLUYE: MATERIALES Y ESPECIFICACIONES QUE CUMPLAN CON LA NORMATIVA N-CMT-5-01-001/13, N-PRY-CAR-10-01-002/13 APLICADAS AL DIA DE HOY, MATERIAL APLICADO EN SU ESTADO DE FUSION A UNA TEMPERATURA MINIMA DE 204 C, LA SUPERFICIE DE CONCRETO O ASFALTO NO DEBE PRESENTAR UNA TEMPERATURA MENOR A LOS 10 C, ;TIEMPO DE SECADO EN RANGOS DE TEMPERATURA DE 10 C DEL SUSTRATO 2 MINUTOS, Y NO MAS DE 10 MINUTOS CUANDO EL SUSTRATO OSCILA ALREDEDOR DE 54C, TRAZO, ENMASCARILLADO, MANO DE OBRA, LIMPIEZA PREVIA Y FINAL DE SUPERFICIE, EQUIPO NECESARIO PARA SU EJECUCIÓN, Y TODO LO NECESARIO PARA SU CORRECTA EJECUCIÓN, TRABAJO TERMINADO. | ML | 1.4 | $39.07 | $54.70 |

Obra: **SOBRECARPETA ASFÁLTICA Y PAVIMENTO HIDRÁULICO AV. DE LOS MAESTROS (CALZADA ORIENTE)**

Ubicación: **TRAMO: ENTRE CALLE PROF. JOSÉ GUADALUPE PERALTA GÁMEZ Y BLVD. SIGLO XXI, AGUASCALIENTES Mpio.**

Contratista: **CONSORCIO INDUSTRIAL INTERNACIONAL AIRE, S.A. DE C.V. (713)**

| No. | Concepto | Unidad | Cantidad | Precio Unitario | Importe Total |
|---|---|---|---|---|---|
| | GRUPO: **OBRA COMPLEMENTARIA** | | | | |
| | PARTIDA: **SEÑALIZACION HORIZONTAL** | | | | |
| 66 | SUMINISTRO Y APLICACIÓN DE PINTURA TERMOPLASTICA ALQUIDALICA DE 120 MILESIMAS DE " (in) EN RAYA CANALIZADORA CLASIFICACIÓN M - 5, PARA INDICAR ENTRADA Y SALIDA EN BIFURCACIONES, COLOR BLANCO O AMARILLO, REFLEJANTE CON MICRO ESFERA DE VIDRIO EN PROPORCIÓN SEGÚN MANUAL DE SEÑALIZACIÓN VIAL Y DISPOSITIVOS DE SEGURIDAD SICT (S.C.T). DE 0.20 MTS DE ANCHO DE LONGITUD Y TRAZO VARIABLE (SEGUN PROYECTO), INCLUYE: MATERIALES Y ESPECIFICACIONES QUE CUMPLAN CON LA NORMATIVA N-CMT-5-01-001/13, N-PRY-CAR-10-01-002/13 APLICADAS AL DIA DE HOY, MATERIAL APLICADO EN SU ESTADO DE FUSION A UNA TEMPERATURA MINIMA DE 204 C, LA SUPERFICIE DE CONCRETO O ASFALTO NO DEBE PRESENTAR UNA TEMPERATURA MENOR A LOS 10 C, ;TIEMPO DE SECADO EN RANGOS DE TEMPERATURA DE 10 C DEL SUSTRATO 2 MINUTOS, Y NO MAS DE 10 MINUTOS CUANDO EL SUSTRATO OSCILA ALREDEDOR DE 54C, TRAZO, ENMASCARILLADO, MANO DE OBRA, LIMPIEZA PREVIA Y FINAL DE SUPERFICIE, EQUIPO NECESARIO PARA SU EJECUCIÓN, Y TODO LO NECESARIO PARA SU CORRECTA EJECUCIÓN, TRABAJO TERMINADO. | ML | 25 | $78.16 | $1,954.00 |
| 68 | SUMINISTRO Y APLICACIÓN DE PINTURA TERMOPLASTICA ALQUIDALICA DE 120 MILESIMAS DE " (in) EN RAYA PARA CRUCE PEATONAL CLASIFICACIÓN M - 7.1, PARA INDICAR " CRUCE PEATONAL EN VIAS PRIMARIAS", COLOR AMARILLO, REFLEJANTE CON MICRO ESFERA DE VIDRIO EN PROPORCIÓN SEGÚN MANUAL DE SEÑALIZACIÓN VIAL Y DISPOSITIVOS DE SEGURIDAD SICT (S.C.T). DE 0.40 MTS DE ANCHO Y 3.5 MTS. DE LONGITUD POR EL ANCHO DE LA VIALIDAD, CON UNA SEPARACIÓN DE 0.40 MTS. ENTRE ELLAS, INCLUYE: MATERIALES Y ESPECIFICACIONES QUE CUMPLAN CON LA NORMATIVA N-CMT-5-01-001/13, N-PRY-CAR-10-01-002/13 APLICADAS AL DIA DE HOY, MATERIAL APLICADO EN SU ESTADO DE FUSION A UNA TEMPERATURA MINIMA DE 204 C, LA SUPERFICIE DE CONCRETO O ASFALTO NO DEBE PRESENTAR UNA TEMPERATURA MENOR A LOS 10 C, ;TIEMPO DE SECADO EN RANGOS DE TEMPERATURA DE 10 C DEL SUSTRATO 2 MINUTOS, Y NO MAS DE 10 MINUTOS CUANDO EL SUSTRATO OSCILA ALREDEDOR DE 54C, TRAZO, ENMASCARILLADO, MANO DE OBRA, LIMPIEZA PREVIA Y FINAL DE SUPERFICIE, EQUIPO NECESARIO PARA SU EJECUCIÓN, Y TODO LO NECESARIO PARA SU CORRECTA EJECUCIÓN, TRABAJO TERMINADO. | M2 | 19.6 | $439.60 | $8,616.16 |
| 69 | SUMINISTRO Y APLICACIÓN DE PINTURA TERMOPLASTICA ALQUIDALICA DE 120 MILESIMAS DE " (in) EN FLECHAS CLASIFICACIÓN M - 11.1, "FLECHA SENCILLA" PARA INDICAR SENTIDO DE CIRCULACIÓN , EN VIALIDADES PARA VELOCIDAD MENOR A 60KM POR HORA DIMENSION NORMATIVA SEGUN MANUAL DE SEÑALIZACIÓN VIAL Y DISPOSITIVOS DE SEGURIDAD SICT (SCT) Y/O (VER PLANO DE SEÑALAMIENTOS), COLOR BLANCO, REFLEJANTE CON MICRO ESFERA DE VIDRIO EN PROPORCIÓN SEGUN NORMA SCT, INCLUYE: MATERIALES Y ESPECIFICACIONES QUE CUMPLAN CON LA NORMATIVA N-CMT-5-01-001/13, N-PRY-CAR-10-01-002/13 APLICADAS AL DIA DE HOY, MATERIAL APLICADO EN SU ESTADO DE FUSION A UNA TEMPERATURA MINIMA DE 204 C, LA SUPERFICIE DE CONCRETO O ASFALTO NO DEBE PRESENTAR UNA TEMPERATURA MENOR A LOS 10 C, ;TIEMPO DE SECADO EN RANGOS DE TEMPERATURA DE 10 C DEL SUSTRATO 2 MINUTOS, Y NO MAS DE 10 MINUTOS CUANDO EL SUSTRATO OSCILA ALREDEDOR DE 54C, TRAZO, ENMASCARILLADO, MANO DE OBRA, LIMPIEZA PREVIA Y FINAL DE SUPERFICIE, EQUIPO NECESARIO PARA SU EJECUCIÓN, Y TODO LO NECESARIO PARA SU CORRECTA EJECUCIÓN, TRABAJO TERMINADO. | PZA | 6 | $793.75 | $4,762.50 |

Obra: **SOBRECARPETA ASFÁLTICA Y PAVIMENTO HIDRÁULICO AV. DE LOS MAESTROS (CALZADA ORIENTE)**

Ubicación: **TRAMO: ENTRE CALLE PROF. JOSÉ GUADALUPE PERALTA GÁMEZ Y BLVD. SIGLO XXI, AGUASCALIENTES Mpio.**

Contratista: **CONSORCIO INDUSTRIAL INTERNACIONAL AIRE, S.A. DE C.V. (713)**

| No. | Concepto | Unidad | Cantidad | Precio Unitario | Importe Total |
|---|---|---|---|---|---|
| | GRUPO: **OBRA COMPLEMENTARIA** | | | | |
| | PARTIDA: **SEÑALIZACION HORIZONTAL** | | | | |
| 70 | SUMINISTRO Y APLICACIÓN DE PINTURA TERMOPLASTICA ALQUIDALICA DE 120 MILESIMAS DE " (in) EN FLECHAS CLASIFICACIÓN M - 11.1, " FLECHA CABEZA DOBLE" PARA INDICAR SENTIDO DE CIRCULACIÓN (VUELTA IZQUIERDA O DERECHA), EN VIALIDADES PARA VELOCIDAD MENOR A 60KM POR HORA SEGUN MANUAL DE SEÑALIZACIÓN VIAL Y DISPOSITIVOS DE SEGURIDAD SICT (SCT), (VER PLANO DE SEÑALAMIENTOS), EN COLOR BLANCO, REFLEJANTE CON MICRO ESFERA DE VIDRIO EN PROPORCIÓN SEGÚN NORMA SCT, INCLUYE: MATERIALES Y ESPECIFICACIONES QUE CUMPLAN CON LA NORMATIVA N-CMT-5-01-001/13, N-PRY-CAR-10-01-002/13 APLICADAS AL DIA DE HOY, MATERIAL APLICADO EN SU ESTADO DE FUSION A UNA TEMPERATURA MINIMA DE 204 C, LA SUPERFICIE DE CONCRETO O ASFALTO NO DEBE PRESENTAR UNA TEMPERATURA MENOR A LOS 10 C, ;TIEMPO DE SECADO EN RANGOS DE TEMPERATURA DE 10 C DEL SUSTRATO 2 MINUTOS, Y NO MAS DE 10 MINUTOS CUANDO EL SUSTRATO OSCILA ALREDEDOR DE 54C, TRAZO, ENMASCARILLADO, MANO DE OBRA, LIMPIEZA PREVIA Y FINAL DE SUPERFICIE, EQUIPO NECESARIO PARA SU EJECUCIÓN, Y TODO LO NECESARIO PARA SU CORRECTA EJECUCIÓN, TRABAJO TERMINADO. | PZA | 3 | $903.65 | $2,710.95 |
| 71 | SUMINISTRO Y COLOCACION DE VIALETA STANDARD (S-200) DE 10X10CM. COLOR: CUERPO AMARILLO Y REFLEJANTE AMARILLO 1 CARA MARCA SEA O SIMILAR EN CALIDAD Y ESPECIFICACIONES DE FICHA TECNICA, ANCLADO EN PAVIMENTO SISTEMA DE SUJECION DE ALTO AGARRE BASE CUÑAS CON AB PEGAMENTO EPOXICO 50/50 RESISTENTE A ALTA TEMPERATURA (VER PLANO DE DETALLES DE SEÑALAMIENTOS HORIZONTAL Y VERTICAL). INCLUYE: TRAZO, ALINEACION, ELEVACION CUALQUIER ALTURA, TRABAJO TERMINADO, LIMPIEZAS. | PZA | 141 | $52.49 | $7,401.09 |
| 72 | SUMINISTRO Y COLOCACION DE VIALETA SOLAR DE 10X10CM. COLOR: CUERPO ALUMINIO 3 LED DOS CARAS REFLEJANTES MARCA CREATIVAL VT-29 O SIMILAR EN CALIDAD Y ESPECIFICACIONES DE FICHA TÉCNICA, FIJADO EN PAVIMENTO CON SISTEMA DE SUJECIÓN DE ALTO AGARRE PEGAMENTO EPOXICO 100 A/B (RESINA EPÓXICA/RESINA POLIAMIDA MODIFICADA), RESISTENTE A ALTA TEMPERATURA (VER PLANO DE DETALLES DE SEÑALAMIENTOS HORIZONTAL), INCLUYE: LIMPIEZA PREVIA DE LA SUPERFICIE+C92, PREPARACIÓN DE LA SUPERFICIE, TRAZO, ALINEACIÓN, Y TODO LO NECESARIO PARA SU CORRECTA EJECUCIÓN, TRABAJO TERMINADO. | PZA | 50 | $561.72 | $28,086.00 |
| 74 | SUMINISTRO Y APLICACION DE PINTURA VINILICA APLICADA CON BROCHA Y RODILLO EN PARAPETO DE CONCRETO INCLUYE: PREPARACION DE LA SUPERFICIES, RETIRO DE CAPAS DE PINTURA SUELTA, GRASAS, SUCIEDAD, ETC, DEJANDO SUPERFICIE LIMPIA Y TRATADA PARA RECIBIR, UNA MANO DE SELLADOR Y PINTURA VINILICA PARA EXTERIORES CALIDAD COMEX COLOR BLANCO O SIMILAR EN PRECIO Y CALIDAD, MANOS DE PINTURA SUFICIENTES PARA CUBRIR TOTAL Y SATISFACTORIAMENTE LA SUPERFICIE, MATERIALES, MANO DE OBRA, ACARREOS, FLETES, DESPERDICIOS, LIMPIEZAS, TRABAJO TERMINADO. | M2 | 118.06 | $67.17 | $7,930.09 |
| | | | | **Totales por Partida** | **$127,486.43** |

Obra: **SOBRECARPETA ASFÁLTICA Y PAVIMENTO HIDRÁULICO AV. DE LOS MAESTROS (CALZADA ORIENTE)**

Ubicación: **TRAMO: ENTRE CALLE PROF. JOSÉ GUADALUPE PERALTA GÁMEZ Y BLVD. SIGLO XXI, AGUASCALIENTES Mpio.**

Contratista: **CONSORCIO INDUSTRIAL INTERNACIONAL AIRE, S.A. DE C.V. (713)**

| No. | Concepto | Unidad | Cantidad | Precio Unitario | Importe Total |
|---|---|---|---|---|---|
| | GRUPO: **OBRA COMPLEMENTARIA** | | | | |
| | PARTIDA: **SEÑALAMIENTO VERTICAL** | | | | |
| 75 | SUMINISTRO Y COLOCACION DE SEÑALAMIENTO VERTICAL DE PREVENCION SP-19 ( SALIDA ), DISEÑO NORMATIVO SCT, HECHO A ABASE DE LAMINA GALVANIZADA CON CEJA DE 72 X 72 CM CALIBRE 16, CON TERMINADO GRADO INGENIERIA EN SU TOTALIDAD, EL COLOR SERA REFLEJANTE GRADO INGENIERIA Y SIMBOLOS EN COLOR REFLEJANTE, TODOS LOS COLORES RESISTENTES A LA INTEMPERIE, FIJADA MEDIANTE BARRENADO Y TORNILLOS DE 2 1/2" X 5/16" A UN POSTE DE PTR DE 2 X 2" CALIBRE 14 EN ACABADO GALVANIZADO Y CON UNA ALTURA DE 2.5 MTS AL NIVEL DE BANQUETA A LA PARTE INFERIOR DE LA LAMINA MAS EL EXCEDENTE REQUERIDO PARA FIJAR LAS LAMINAS Y ANCLADO DE 50 CM DE PROFUNDIDAD CON ANGULO TRANSVERSAL DE 1 X 1" DE 25 CM, EN DADO DE CONCRETO F´c=150 KG/CM2 DE 30 CM DE LADO (VER PLANO DE DETALLES CRITERIOS DE ANCLAJE DE SEÑALAMIENTO VERTICAL, DETALLE SEÑ-02 Y SEÑ 03), MCA ASEA O SIMILAR EN CALIDAD Y ESPECIFICACIONES, INCLUYE: MANO DE OBRA, FLETES, MANIOBRAS LIMPIEZAS Y RETIRO DEL SOBRANTE FUERA DE LA OBRA HASTA TIRADERO OFICIAL, TRABAJO TERMINADO. | PZA | 2 | $2,259.13 | $4,518.26 |
| 76 | SUMINISTRO Y COLOCACION DE SEÑALAMIENTO VERTICAL DE RESTRICCION SR-9 ( VELOCIDAD MAXIMA ), DISEÑO NORMATIVO SCT, HECHO A ABASE DE LAMINA GALVANIZADA CON CEJA DE 72 X 72 CM CALIBRE 16, CON TERMINADO GRADO INGENIERIA EN SU TOTALIDAD, EL COLOR SERA REFLEJANTE GRADO INGENIERIA Y SIMBOLOS EN COLOR REFLEJANTE, TODOS LOS COLORES RESISTENTES A LA INTEMPERIE, FIJADA MEDIANTE BARRENADO Y TORNILLOS DE 2 1/2" X 5/16" A UN POSTE DE PTR DE 2 X 2" CALIBRE 14 EN ACABADO GALVANIZADO Y CON UNA ALTURA DE 2.5 MTS AL NIVEL DE BANQUETA A LA PARTE INFERIOR DE LA LAMINA MAS EL EXCEDENTE REQUERIDO PARA FIJAR LAS LAMINAS Y ANCLADO DE 50 CM DE PROFUNDIDAD CON ANGULO TRANSVERSAL DE 1 X 1" DE 25 CM, EN DADO DE CONCRETO F´c=150 KG/CM2 DE 30 CM DE LADO (VER PLANO DE DETALLES CRITERIOS DE ANCLAJE DE SEÑALAMIENTO VERTICAL, DETALLE SEÑ-02 Y SEÑ 03), MCA ASEA O SIMILAR EN CALIDAD Y ESPECIFICACIONES, INCLUYE: MANO DE OBRA, FLETES, MANIOBRAS LIMPIEZAS Y RETIRO DEL SOBRANTE FUERA DE LA OBRA HASTA TIRADERO OFICIAL, TRABAJO TERMINADO. | PZA | 2 | $2,259.13 | $4,518.26 |
| | | | | **Totales por Partida** | **$9,036.52** |
| | | | | **Totales por Grupo** | **$487,694.39** |

Obra: **SOBRECARPETA ASFÁLTICA Y PAVIMENTO HIDRÁULICO AV. DE LOS MAESTROS (CALZADA ORIENTE)**

Ubicación: **TRAMO: ENTRE CALLE PROF. JOSÉ GUADALUPE PERALTA GÁMEZ Y BLVD. SIGLO XXI, AGUASCALIENTES Mpio.**

Contratista: **CONSORCIO INDUSTRIAL INTERNACIONAL AIRE, S.A. DE C.V. (713)**

| No. | Concepto | Unidad | Cantidad | Precio Unitario | Importe Total |
|---|---|---|---|---|---|
| | GRUPO: **HIDRAULICO SANITARIO** | | | | |
| | PARTIDA: **LINEA DE ALCANTARILLADO** | | | | |
| 77 | TRAZO Y NIVELACION DE TERRENO CON APARATO TOPOGRAFICO, PARA LINEAS DE AGUA POTABLE Y ALCANTARILLADO, INCLUYE: EJES, BANCOS DE NIVEL, RENIVELACIONES, CORRECCION DE ARRASTRES Y NIVELES A PUNTOS OBLIGADOS (AUTORIZADOS POR LA SUPERVISION), ESTACAS, VARILLAS, MANO DE OBRA CALIFICADA, HERRAMIENTA NECESARIA, EQUIPO DE PRECISION CALIBRADO, (SE ENTREGARA A LA DEPENDENCIA PLANO DE PERFIL Y SECCIONES ORIGINAL Y FINAL CON PUNTOS X,Y,Z) TRABAJO TERMINADO.P.U.O.T. | ML | 93.1 | $8.01 | $745.73 |
| 78 | EXCAVACION A MAQUINA EN ZANJAS EN MATERIAL TIPO II DE 0.00 A 2.00 M DE PROFUNDIDAD, INCLUYE: AFLOJE Y EXTRACCION DEL MATERIAL, AFINE, TRASPALEO VERTICAL PARA SU EXTRACCION, CONSERVACION DE LA EXCAVACION, ACARREO HASTA EL LUGAR DE ACOPIO PARA SU CARGA Y ACARREO FUERA DE LA OBRA, SEÑALAMIENTOS, COLOCACION DE PASOS PEATONALES Y PROTECCION PERIMETRAL DE LA ZANJA. | M3 | 118.17 | $72.38 | $8,553.15 |
| 79 | PLANTILLA Y ACOSTILLADO CON GRAVA CANTO RODADO MEZCLADO DE 3/4 A 1" Y ARENA (50-50) Y PISON DE MANO, INCLUYE: SUMINISTRO DE MATERIAL EN LA OBRA, ACARREO EN CARRETILLA, DESCARGA EN LA ZANJA, EXTENDIDO, NIVELADO Y APISONADO, APOYO SEMICIRCULAR PARA LA TUBERIA SE CONSTRUIRA INMEDIATAMENTE ANTES DE TENDER LA TUBERIA, DEBIENDO COLOCAR HILOS LONGITUDINALMENTE PARA VERIFICAR LA UNIFORMIDAD DE LA PLANTILLA. | M3 | 26.98 | $609.58 | $16,446.47 |
| 80 | ACOSTILLADO CON MATERIAL DE PROD. DE EXCAVACION EN CAPAS DE 20 CMS. AL 85% DE SU P.V.M.S. CON EL USO DE BAILARINA, HOMOGENIZACION DEL MATERIAL, AGUA LA NECESARIA, EXTENDIDO Y COMPACTADO. | M3 | 14.47 | $121.09 | $1,752.17 |
| 83 | CARGA MECANICA Y ACARREO DE MATERIAL PRODUCTO DE EXCAVACION Y DEMOLICION EN CAMION DE VOLTEO AL 1er. KM, VOLUMEN MEDIDO COMPACTO. | M3 | 118.18 | $28.12 | $3,323.22 |
| 84 | ACARREO DE MATERIAL PRODUCTO DE EXCAVACION Y/O DEMOLICION EN CAMION DE VOLTEO A KILOMETROS SUBSECUENTES, AL TIRADERO OFICIAL AUTORIZADO MAS CERCANO AUTORIZADO POR LA SUPERVISION, VOLUMEN MEDIDO COMPACTO. | M3-KM | 1536.21 | $8.21 | $12,612.28 |
| 88 | SUMINISTRO DE TUBERIA DE PVC PARA ALCANTARILLADO SERIE 20 DE 18", CON JUNTA HERMETICA, INCLUYE: FLETES Y ACARREO HASTA EL SITIO DE SU COLOCACION, ALINEADO, MATERIAL, MANO DE OBRA. | ML | 87.5 | $1,529.03 | $133,790.13 |
| 89 | INSTALACION DE TUBERIA DE PVC PARA ALCANTARILLADO SERIE 20 DE 18", CON JUNTA HERMETICA. INCLUYE: FLETES Y ACARREO HASTA EL SITIO DE SU COLOCACION, MATERIALES DE LIMPIEZA, LUBRICACION, NIVELADO, MATERIAL Y MANO DE OBRA. | ML | 87.5 | $105.98 | $9,273.25 |
| | | | **Totales por Partida** | | **$186,496.40** |
| | PARTIDA: **DESCARGAS DOMICILIARIAS** | | | | |
| 90 | EXCAVACION A MAQUINA EN ZANJAS EN MATERIAL TIPO II DE 0.00 A 2.00 M DE PROFUNDIDAD, INCLUYE: AFLOJE Y EXTRACCION DEL MATERIAL, AFINE, TRASPALEO VERTICAL PARA SU EXTRACCION, CONSERVACION DE LA EXCAVACION, ACARREO HASTA EL LUGAR DE ACOPIO PARA SU CARGA Y ACARREO FUERA DE LA OBRA, SEÑALAMIENTOS, COLOCACION DE PASOS PEATONALES Y PROTECCION PERIMETRAL DE LA ZANJA. | M3 | 2.98 | $72.38 | $215.69 |

Obra: **SOBRECARPETA ASFÁLTICA Y PAVIMENTO HIDRÁULICO AV. DE LOS MAESTROS (CALZADA ORIENTE)**

Ubicación: **TRAMO: ENTRE CALLE PROF. JOSÉ GUADALUPE PERALTA GÁMEZ Y BLVD. SIGLO XXI, AGUASCALIENTES Mpio.**

Contratista: **CONSORCIO INDUSTRIAL INTERNACIONAL AIRE, S.A. DE C.V. (713)**

GRUPO: **HIDRAULICO SANITARIO**

PARTIDA: **DESCARGAS DOMICILIARIAS**

| No. | Concepto | Unidad | Cantidad | Precio Unitario | Importe Total |
|---|---|---|---|---|---|
| 91 | PLANTILLA Y ACOSTILLADO CON GRAVA CANTO RODADO MEZCLADO DE 3/4 A 1" Y ARENA (50-50) Y PISON DE MANO, INCLUYE: SUMINISTRO DE MATERIAL EN LA OBRA, ACARREO EN CARRETILLA, DESCARGA EN LA ZANJA, EXTENDIDO, NIVELADO Y APISONADO, APOYO SEMICIRCULAR PARA LA TUBERIA SE CONSTRUIRA INMEDIATAMENTE ANTES DE TENDER LA TUBERIA, DEBIENDO COLOCAR HILOS LONGITUDINALMENTE PARA VERIFICAR LA UNIFORMIDAD DE LA PLANTILLA. | M3 | 0.36 | $609.58 | $219.45 |
| 92 | ACOSTILLADO CON MATERIAL DE PROD. DE EXCAVACION EN CAPAS DE 20 CMS. AL 85% DE SU P.V.M.S. CON EL USO DE BAILARINA, HOMOGENIZACION DEL MATERIAL, AGUA LA NECESARIA, EXTENDIDO Y COMPACTADO. | M3 | 0.26 | $121.09 | $31.48 |
| 93 | RELLENO COMPACTADO AL 90% CON MATERIAL DE BANCO EN CAPAS DE 20 CM UTILIZANDO BAILARINA. INCLUYE: SUMINISTRO DE TEPETATE (MATERIAL DE BANCO) EN LA OBRA, ABUNDAMIENTO, ACARREOS DENTRO DE LA OBRA, CRIBADO, RETIRO DE MATERIAL, MANO DE OBRA Y EQUIPO, LIMPIEZAS, TRABAJO TERMINADO. | M3 | 0.26 | $312.59 | $81.27 |
| 94 | RELLENO COMPACTADO AL 95% CON MATERIAL DE BANCO EN CAPAS DE 20 CM UTILIZANDO BAILARINA, INCLUYE: SELECCION DEL MATERIAL, ABUNDAMIENTO, ACARREOS DENTRO DE LA OBRA, CRIBADO, MANO DE OBRA Y EQUIPO, PRUEBA DE CONTROL DE CALIDAD. | M3 | 0.26 | $323.31 | $84.06 |
| 95 | CARGA MECANICA Y ACARREO DE MATERIAL PRODUCTO DE EXCAVACION Y DEMOLICION EN CAMION DE VOLTEO AL 1er. KM, VOLUMEN MEDIDO COMPACTO. | M3 | 2.98 | $28.12 | $83.80 |
| 96 | ACARREO DE MATERIAL PRODUCTO DE EXCAVACION Y/O DEMOLICION EN CAMION DE VOLTEO A KILOMETROS SUBSECUENTES, AL TIRADERO OFICIAL AUTORIZADO MAS CERCANO AUTORIZADO POR LA SUPERVISION, VOLUMEN MEDIDO COMPACTO. | M3-KM | 38.74 | $8.21 | $318.06 |
| 97 | DESCARGA DOMICILIARIA PARA USO FUTURO DE 9.00 M DE LONGITUD (NOMINAL), A BASE DE TUBO DE PVC ALCANTARILLADO SERIE 20 DE 6" DE DIAMETRO, INCLUYE: SILLETA DE 10 A 12" X 6", CODO DE 6" X 45°, TAPON HEMBRA, ALINEACION, INDICACION DE UBICACION CON VARILLA EN PREDIO, PRUEBAS DE ESCURRIMIENTO, SUMINISTROS, ACARREOS, TRABAJO TERMINADO. | PZA | 2 | $2,671.44 | $5,342.88 |
| 98 | REGISTRO SANTARIO DE 0.40X0.60X0.80 M (MEDIDAS INTERIORES) DE TABIQUE ROJO RECOCIDO (14 CM DE ESPESOR) JUNTEADO CON MORTERO CEMENTO-ARENA 1:4 Y APLANADO DE 2.00 CM CON EL MISMO MORTERO, ACABADO PULIDO INTERIOR, PLANTILLA DE 7.00 CM DE ESPESOR DE CONCRETO F'C=150 KG/CM2, HECHO EN OBRA, TMA 19 MM. INCLUYE: MARCO Y CONTRAMARCO DE ANGULO DE 2" X 3/16" COLADA CON EL MISMO CONCRETO, PLOMEADO, ALINEADO, NIVELADO, ACARREOS DENTRO DE LA OBRA Y CONEXION A RED EXISTENTE, LIMPIEZAS. | PZA | 2 | $3,522.46 | $7,044.92 |

**Totales por Partida** **$13,421.61**

**Totales por Grupo** **$199,918.01**

Obra: **SOBRECARPETA ASFÁLTICA Y PAVIMENTO HIDRÁULICO AV. DE LOS MAESTROS (CALZADA ORIENTE)**

Ubicación: **TRAMO: ENTRE CALLE PROF. JOSÉ GUADALUPE PERALTA GÁMEZ Y BLVD. SIGLO XXI, AGUASCALIENTES Mpio.**

Contratista: **CONSORCIO INDUSTRIAL INTERNACIONAL AIRE, S.A. DE C.V. (713)**

| No. | Concepto | Unidad | Cantidad | Precio Unitario | Importe Total |
|---|---|---|---|---|---|
| | GRUPO: **EXTRAORDINARIO** | | | | |
| | PARTIDA: **EXTRAORDINARIOS** | | | | |
| 122 | CONSTRUCCION DE PAVIMENTO HIDRAULICO A BASE DE CONCRETO PREMEZCLADO MR=42 KG/CM2 TMA 1 1/2" GRAVA TRITURADA, REVENIMIENTO DE 6 A 8 CM RESISTENCIA RAPIDA 14 DIAS DE 20 CM DE ESPESOR MODULADO EN LOSAS DE 3.5 MTS. (ANCHO) X 3.5 MTS (LARGO) COMO MAXIMO, CON CORTES EN LAS LOSAS DE 1/3 DEL ESPESOR DE LA LOSA (7 CM) Y SELLADO CON MATERIAL ELASTOMERICO Y TIRA PREFORMADA EN JUNTAS Y CORTES LONGITUDINALES Y TRANSVERSALES COLA DE RATA DE 1/8", ASI COMO EL APROCHE CON GUARNICION Y DENTELLON. INCLUYE: CIMBRADO, COLADO, VIBRADO CON INMERSION Y REGLA VIBRATORIA, DESCIMBRADO, REGLEADO FINAL, ACABADO CEPILLO DE ALUMINIO Y CON DOBLADOR, CALAFATEO, CURADO CON MEMBRANA BASE AGUA Y TODO LO NECESARIO PARA SU CORRECTA COLOCACION, P.U.O.T. | M2 | 509.29 | $803.93 | $409,433.51 |
| 123 | CONSTRUCCION DE PAVIMENTO HIDRAULICO A BASE DE CONCRETO PREMEZCLADO MR=42 KG/CM2 TMA 1 1/2" GRAVA TRITURADA, REVENIMIENTO DE 6 A 8 CM RESISTENCIA RAPIDA 7 DIAS DE 20 CM DE ESPESOR MODULADO EN LOSAS DE 3.5 MTS. (ANCHO) X 3.5 MTS (LARGO) COMO MAXIMO, CON CORTES EN LAS LOSAS DE 1/3 DEL ESPESOR DE LA LOSA (7 CM) Y SELLADO CON MATERIAL ELASTOMERICO Y TIRA PREFORMADA EN JUNTAS Y CORTES LONGITUDINALES Y TRANSVERSALES COLA DE RATA DE 1/8", ASI COMO EL APROCHE CON GUARNICION Y DENTELLON. INCLUYE: CIMBRADO, COLADO, VIBRADO CON INMERSION Y REGLA VIBRATORIA, DESCIMBRADO, REGLEADO FINAL, ACABADO CEPILLO DE ALUMINIO Y CON DOBLADOR, CALAFATEO, CURADO CON MEMBRANA BASE AGUA Y TODO LO NECESARIO PARA SU CORRECTA COLOCACION, P.U.O.T. | M2 | 1636.94 | $820.61 | $1,343,289.33 |
| 124 | CONSTRUCCION DE POZO DE VISITA DE HASTA 2.0 A 2.5 M DE PROFUNDIDAD, CON PLANTILLA DE MAMPOSTERIA DE PIEDRA, ASENTADA CON MORTERO CEM ARENA 1:3, CON MURO DE TABIQUE ROJO RECOCIDO DE 28 CM DE ESPESOR JUNTADO CON MORTERO CEMENTO-ARENA 1:3 NO MAYOR DE 1.5 CM DE ESPESOR EN FORMA CUATRAPEADA, APLANADO INTERIOR DE MORTERO CEM-ARENA 1:3 DE UN ESPESOR MINIMO DE 1 CM, ACABADO PULIDO FINO DE CEMENTO, LAS INTERSECCIONES DE LAS TUBERIAS SE EMBOQUILLARAN, ESCALONES, LA HECHURA DE LA MEDIA CAÑA DE CONCRETO HECHO EN OBRA F'C=150 KG/CM, DONDE SE AHOGARA TUBERIA CORTADA A MEDIA CAÑA Y SE PULIRA CUIDADOSAMENTE, INCLUYE: EXCAVACION, RELLENO, MATERIALES, ACARREOS, FLETES, MANO DE OBRA, MANIOBRAS LOCALES INSTALACION Y EQUIPO NECESARIO PARA SU CORRECTA CONSTRUCCION, PRUEBA DE HERMETICIDAD Y FUNCIONAMIENTO. | PZA | 4 | $14,807.80 | $59,231.20 |
| 125 | INTERCONEXION DE LINEA DE RED DE AGUA POTABLE DE 3" DE DIAM. (BAYPAS), A BASE DE 1.5 MTS DE TUBERIA DE PVC RD-26 DE 3" DE DIAM, 4 CODOS DE PVC 3X45o, 4 COPLES DE PVC DE 3", INCLUYE: LIMPIEZA, LUBRICANTE, FRANELA, PEGAMENTO, PRUEBAS DE FUNCIONAMIENTO, ACARREOS DENTRO DE LA OBRA, LIMPIEZAS. | PZA | 2 | $1,775.37 | $3,550.74 |
| 126 | CONCRETO ARMADO PARA RAMPA DE LAVADERO DE 10 CM DE ESPESOR, MALLA ELECTROSOLDADA 6-6/10-10 DE CONCRETO F´c= 200 KG/CM2. TMA 3/4", INCLUYE: CIMBRADO, DESCIMBRADO, CURADO, COLADO, TERMINADO CERRADO A PLANA, ACARREOS DENTRO DE LA OBRA, LIMPIEZAS. | M2 | 22.8799664876 | $352.11 | $8,056.27 |

2'146.23


Obra: **SOBRECARPETA ASFÁLTICA Y PAVIMENTO HIDRÁULICO AV. DE LOS MAESTROS (CALZADA ORIENTE)**


Ubicación: **TRAMO: ENTRE CALLE PROF. JOSÉ GUADALUPE PERALTA GÁMEZ Y BLVD. SIGLO XXI, AGUASCALIENTES Mpio.**

Contratista: **CONSORCIO INDUSTRIAL INTERNACIONAL AIRE, S.A. DE C.V. (713)**

| No. | Concepto | Unidad | Cantidad | Precio Unitario | Importe Total |
|---|---|---|---|---|---|
| | GRUPO: **EXTRAORDINARIO** | | | | |
| | PARTIDA: **EXTRAORDINARIOS** | | | | |
| 127 | CONSTRUCCION DE BANQUETA DE 10 CM DE ESPESOR A BASE DE CONCRETO H.O. F´c= 200 KG/CM2, TMA 3/4, ACABADO RAYADO FINO CON BROCHA DE PELO, JUNTAS FRIAS CON DOBLADOR DE 2", SECCION DE LOSAS COMO INDIQUE EL PROYECTO, REFORZADA CON VR #3@15 CM EN AMBOS SENTIDOS, INCLUYE: CIMBRADO, COLADO, DESCIMBRADO,, CORTES CON CORTADORA DE DISCO, SELLADO, SELLADO DE CORTES CON SELLADOR AUTONIVELANTE Y TIRA DE RELLENO PREFORMADANO ADHERENTE DE 1/8" (EN TODAS LAS JUNTAS DE CONTRACCION Y CONSTRUCCION TRANSVERSALES, CURADO CON MEMBRANA QUIMICA APLICADA CON ASPERSOR, TRABAJO TERMINADO. | M2 | 16 | $627.30 | $10,036.80 |
| 128 | REPARACION DE RED HIDRAULICA DE PVC RD-26 DE 6" DE DIAMETRO, A BASE DE 1.5 MTS DE TUBO DE PVC RD-26 DE 6" DE DIAMETRO Y 2 COPLES DE REPARACION DE PVC DE 6", INCLUYE:TRABAJOS EN VIVO, MATERIALES, MANO DE OBRA, CORTES, AJUSTES, PRUEBAS DE FUNCIONAMIENTO, ACARREOS DENTRO DE LA OBRA, LIMPIEZAS | M2 | 1 | $1,883.08 | $1,883.08 |
| 129 | MURO DE CONTENCION DE CONCRETO ARMADO ´c= 200 KG/CM2 DE 1.00 X 0.50M X X0.15 M DE SECCION REFORZADA CON 2 ARMEX 15-20-4 EN SENTIDO TRANSVERSAL A LA BANQUETA Y 2 ANCLAJES A LA BANQUETA DE ARMEX 15-20-4 DE 1.00 M EN LOS EXTREMOS, INCLUYE: CIMBRADO, DESCIMBRADO, HABILITADO DE ACERO, ALINEADO, COLADO, VIBRADO, EXCAVACION A MANO EN SECCION DE 0.40 X 0.3.0 X 1.0 MTS, ACARREOS DENTRO DE LA OBRA, LIMPIEZAS | PZA | 5 | $509.87 | $2,549.35 |

| | | |
|---|---|---|
| **Totales por Partida** | | **$1,838,030.28** |
| **Totales por Grupo** | | **$1,838,030.28** |
| **Totales Presup.** | | **$5,735,058.03** |
| **Anticipo** | **+** | **$1,720,517.41** |
| **Amortizac. Ant.** | **-** | **$1,720,517.41** |
| **SubTotal. Ant.** | **=** | **$5,735,058.03** |
| **IVA** | **+** | **$917,609.29** |
| **Total** | **=** | **$6,652,667.32** |

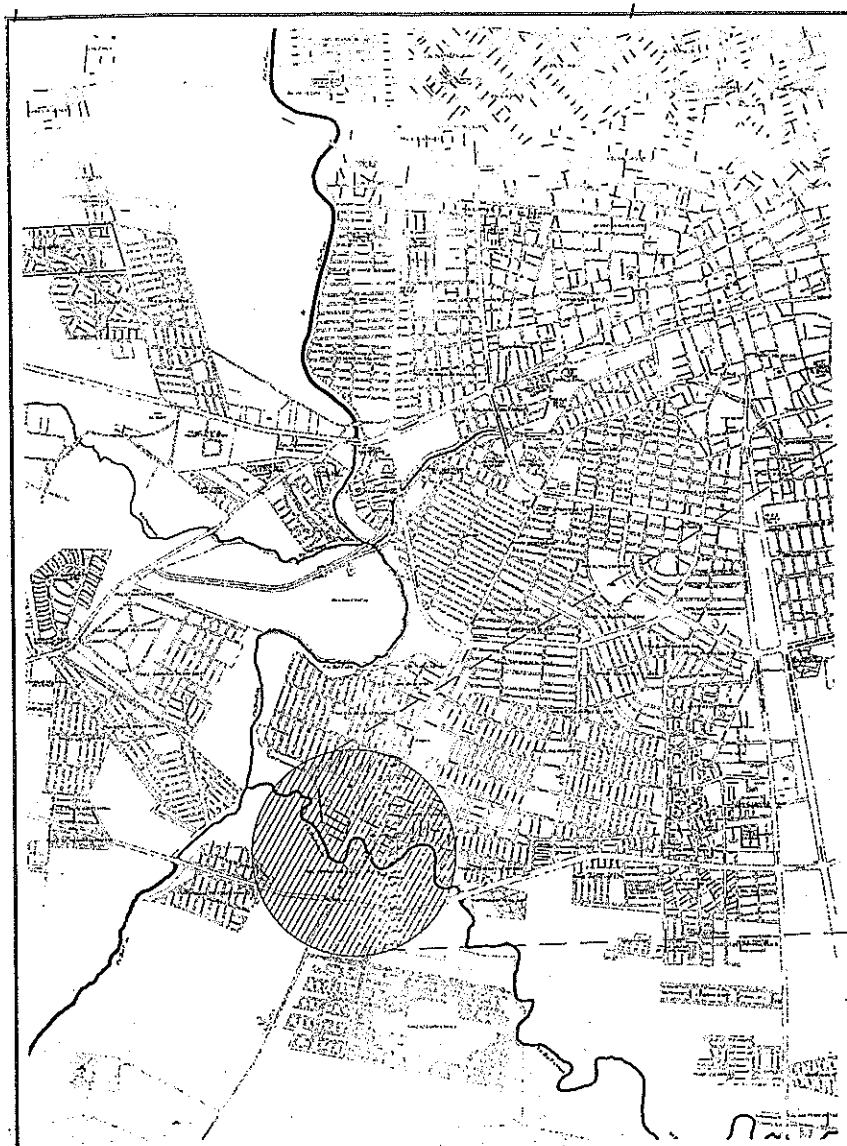

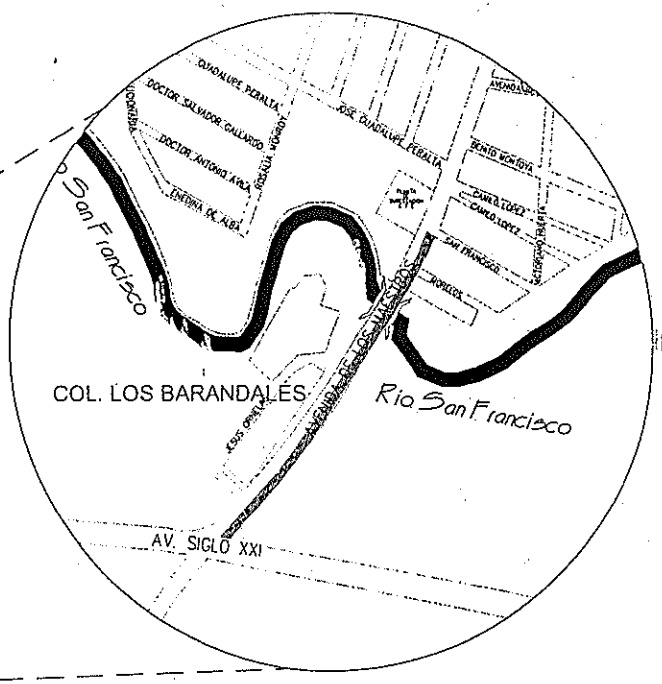



## CROQUIS DE LOCALIZACIÓN

SIN ESCALA

AV. LOS MAESTROS

LOCALIZACIÓN

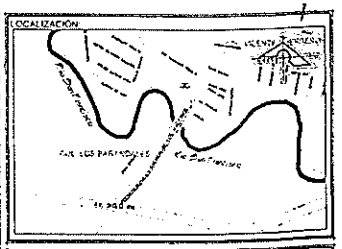


SIMBOLOGÍA

La Dirección de Planeación y Proyectos solo autoriza el proyecto ejecutivo, no es responsable de la correcta ejecución de la obra. Este documento no tiene validez si no presenta las firmas de los responsables para su autorización, así como los sellos respectivos.

PRESIDENTE MUNICIPAL
M.P.P. Leonardo Montañez Castro
ENCARGADA DE DESPACHO DE LA SOPMA
Arq. Gloria Guadalupe Castillo González

| REV | FECHA | OBSERVACIONES |
|---|---|---|
| | | |

V°B° DE LA DEPENDENCIA

| RESP DE PROY EXTERNO | | LOGO EXTERNO |
|---|---|---|
| CED. PROFESIONAL | | |
| PROYECTO | REVISO | AUTORIZO |

Dirección de Planeación y Proyectos de Obra — Secretaría de Obras Públicas

| PROYECTISTA | COORDINADOR |
|---|---|
| ARQ. ALEJANDRO CONTRERAS | ARQ. ALEJANDRO JAIME LEAL |
| JEFE DE DEP. | DIRECTOR |
| ARQ. J. JESUS PALACIOS GONZALEZ | M.en.ARQ. JOSÉ LUIS JIMÉNEZ GARCÍA |


PROYECTO
CONSTRUCCION DE SOBRECARPETA ASFALTICA Y PAVIMENTO HIDRAULICO, AV. DE LOS MAESTROS CALZADA ORIENTE

UBICACIÓN
TRAMO ENTRE C. PROF. JOSE GUADALUPE PERALTA Y AV. SIGLO XXI


CONTENIDO
CROQUIS DE LOCALIZACIÓN

| CLAVE | No. PLANO |
|---|---|
| LOC 01 | 01 |
| FECHA JULIO 2022 | ESCALA INDICADA |
| ACOTACIÓN METROS | No. EXP. E-000-22 |


Aguascalientes
LA CIUDAD DE TU VIDA

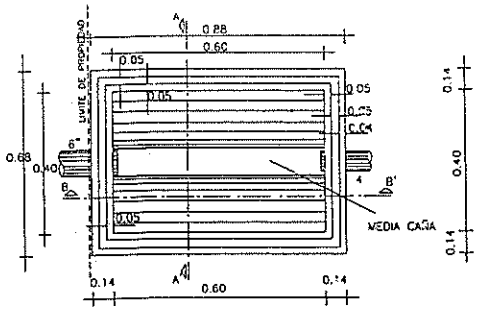



PLANTA

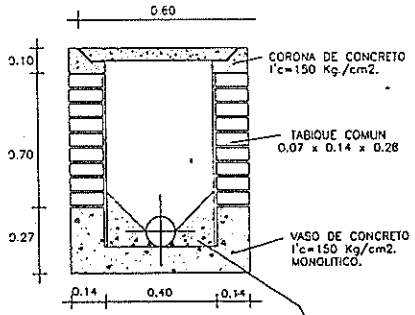



CORTE A–A'

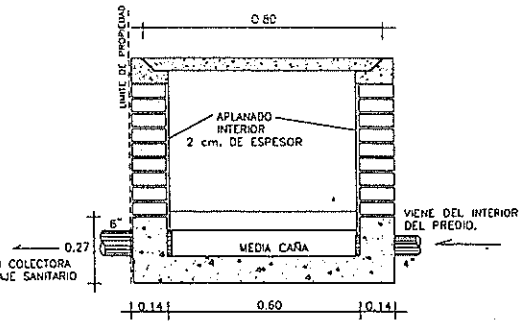



CORTE B–B'

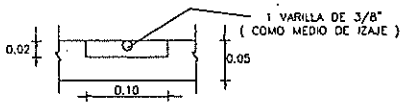



DETALLE DE NICHO

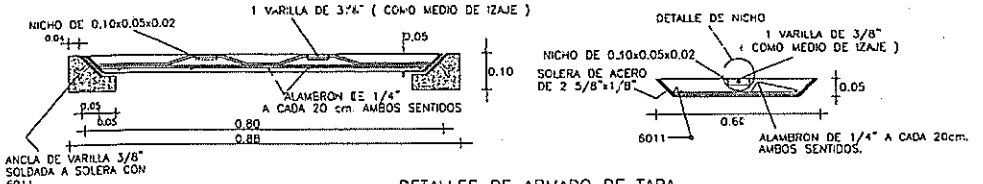



DETALLES DE ARMADO DE TAPA

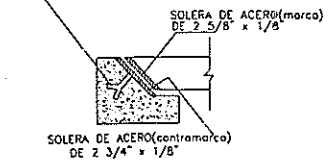


DETALLE DE MARCO

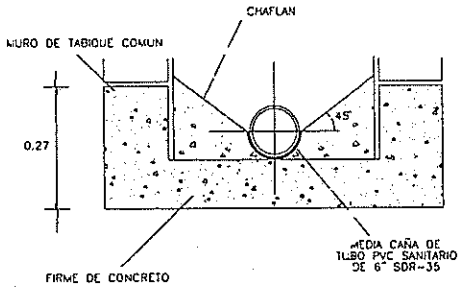



DETALLE DE FONDO DE REGISTRO

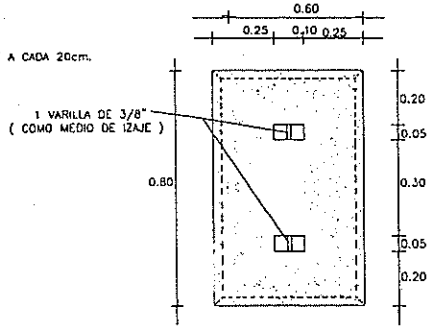


DETALLE DE TAPA EN PLANTA

TODAS LAS ACOTACIONES SON EN METROS, EXCEPTO DE LAS INDICADAS EN OTRA UNIDAD.

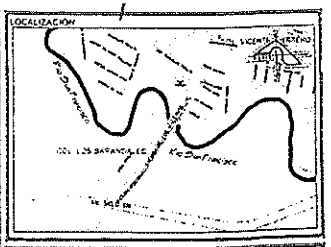


SIMBOLOGIA

## NOTAS

1. PULIDO INTERIOR CON APLANADO A BASE DE MORTERO CEMENTO–ARENA EN PROP. 1:2 .
2. TABIQUE JUNTEADO CON MORTERO CEMENTO–ARENA PROP. 1:3
3. EXCAVACION DE 1.00 x 0.80 x 1.10 m.
4. TAPA DE REGISTRO DE 0.60 x 0.80 DE 0.05m. (2") DE ESPESOR.
5. ARMADO A BASE DE ALAMBRON DE 1/4" EN TAPA.
6. CONCRETO f'c= 150 kg/cm2. EN TAPA, CORONA Y VASO
7. MARCO Y CONTRAMARCO DE SOLERA DE ACERO DE 2 3/4"x1/8". Y DE 2 5/8"x1/8", CONTRAMARCO CON ANCLAJE A BASE DE VARILLA CON GANCHO DE 3/8" SOLDADA A SOLERA CON 6011
8. FIRME DE CONCRETO f'c= 130 kg/cm2. CON CHAFLAN A 45 grados Y MEDIA CAÑA DE TUBO PVC DE 6" SDR-35 CORTADO POR LA MITAD.
9. EL EMPOTRAMIENTO DE LA TUBERIA CON EL MURO DEBERA IMPERMEABILIZARSE CON SELLADOR.
10. LA LOCALIZACION DEL REGISTRO DEBERA SER DONDE NO EXISTA ENTRADA O TRANSITO DE VEHICULOS.
11. UBICAR EL MURO DEL LADO DE LA DESCARGA EN EL LIMITE DE PROPIEDAD.
12. PENDIENTE LONGITUDINAL DE 2.5% (1 cm. DE DESNIVEL)
13. LOS TUBOS DEBERAN AHOGARSE EN EL VASO DE CONCRETO.
14. EL REGISTRO TENDRA COMO MINIMO 1.00 m. DE PROFUNDIDAD.

La Dirección de Planeación y Proyectos solo autoriza el proyecto ejecutivo, no es responsable de la correcta ejecución de la obra. Este documento no tiene validez si no presenta las firmas de los responsables para su autorización, así como los sellos respectivos.

PRESIDENTE MUNICIPAL
M.P.P. Leonardo Montañez Castro
ENCARGADA DE DESPACHO DE LA SOPMA
Arq. Gloria Guadalupe Castillo González

| REV | FECHA | OBSERVACIONES |
|---|---|---|
| | | |

VO. BO. DE LA DEPENDENCIA

| RESP. DE PROY. EXTERNO | | LOGO EXTERNO |
|---|---|---|
| CED. PROFESIONAL | | |
| PROYECTO | REVISO | AUTORIZO |


Dirección de Planeación y Proyectos de Obra — Secretaría de Obras Públicas

| PROYECTO | COORDINADOR |
|---|---|
| ARQ. ALVARO CASTAÑEDA CENTENO | ARQ. ALEJANDRO JAIME LEAL |
| JEFE DE DEPTO. | DIRECTOR |
| ARQ. J. JESUS PRADO GONZALEZ | M. en ARQ. JOSE LUIS JIMENEZ GARCIA |


PROYECTO
CONSTRUCCION DE SOBRECARPETA ASFALTICA Y PAVIMENTO HIDRAULICO, AV. DE LOS MAESTROS CALZADA ORIENTE
UBICACION
TRAMO ENTRE C. PROF. JOSE GUADALUPE PERALTA Y AV. SIGLO XXI
CONTENIDO
PLANO DE DETALLES SANITARIOS

| CLAVE | No. PLANO |
|---|---|
| DETS 01 | 11 |
| FECHA: JULIO 2022 | ESCALA: INDICADA |
| ACOTACION: METROS | No. EXP.: E-000-22 |


Aguascalientes
LA CIUDAD DE TU VIDA

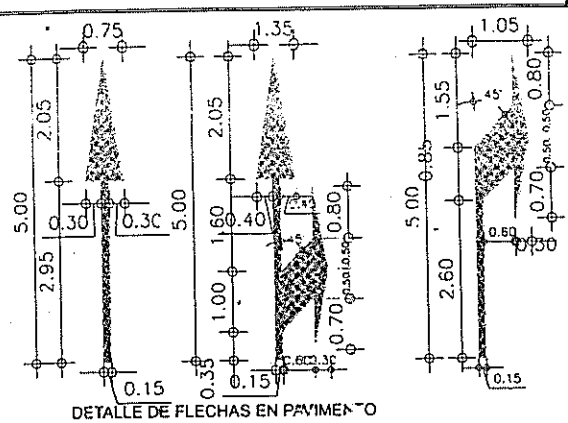


DETALLE DE FLECHAS EN PAVIMENTO
PARA VELOCIDADES HASTA DE 60 KM/H
COTAS EN M

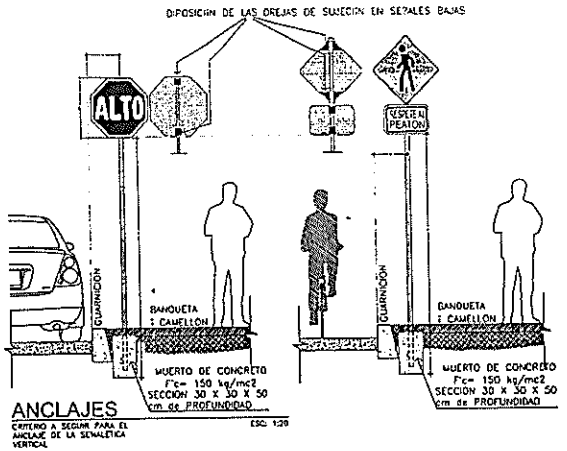


ANCLAJES
CRITERIO A SEGUIR PARA EL ANCLAJE DE LA SEÑALETICA VERTICAL

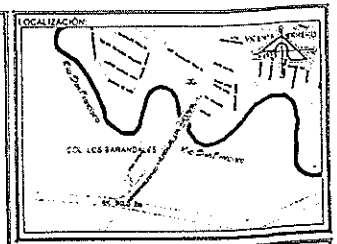


SIMBOLOGÍA

NOTA:
Se aplicará en todas las señalamientos horizontales pintura para trafico base solvente tipo alquidal de secado rápido, que cumpla con las especificaciones n-cmt-5-01-001/05, n-pry-car-10-01-002/13 de la SCT aplicadas al día de hoy.

M-12.1, M12.2 APLICADA SOBRE GUARNICIONES Y DENTELLONES DE CUALQUIER COLOR

Se aplicara en todas las señalamientos horizontales pintura para trafico Termoplastico tipo alquidal de secado rápido, que cumpla con las especificaciones n-cmt-5-01-001/05, n-pry-car-10-01-002/13 de la SCT aplicadas al día de hoy.

M - 1.2, LÍNEA DISCONTINUA SENCILLA DE DIVISIÓN DE CARRILES DE FRENTE EN PISO, DE 10 CM DE ANCHO
M - 3.3, CONTINUA AZOQUERGA, PARA VIALIDADES URBANAS DE FRENTE EN PISO, SEPARADA 15 CM. DE LA GUARNICION, COLOR AMARILLO
M - 4, PARA INDICAR LÍNEA GUÍA EN ZONA DE TRANSICIÓN DE FRENTE EN PISO, DESARROLLO DE 2.00 X 0.10 MTS, CON UNA SEPARACIÓN DE 4.00 MTS ENTRE SI PROMEDIO
M - 5, PARA INDICAR ENTRADA Y SALIDA EN BIFURCACIONES
M - 6, PARA INDICAR ALTO EN CRUCEROS. COLOR BLANCO
M - 7.1, PARA INDICAR " CRUCE PEATONAL EN VIAS PRIMARIAS" COLOR AMARILLO
M - 11.1, "FLECHA SENCILLA" PARA INDICAR SENTIDO DE CIRCULACIÓN
M - 11.1, "FLECHA CABEZA DOBLE" PARA INDICAR SENTIDO DE CIRCULACIÓN (VUELTA IZQUIERDA O DERECHA)

NOTA:
Nota1: Se aplicará en todas las señalamientos horizontales pintura para trafico base solvente y/o termoplastico tipo alquidal de secado rápido, que cumpla con las especificaciones n-cmt-5-01-001/05, n-pry-car-10-01-002/13 de la SCT aplicadas al día de hoy.

Nota2: Dosificación de micro esfera
La cantidad de esferas de vidrio en la película de pintura en húmedo, según su tipo, será la que se indica en la Tabla.

TABLA B: Cantidad de esferas de vidrio en la película de pintura en humedo.

| TIPO DE PINTURA | ESPESOR DE LA PELÍCULA DE PINTURA EN HÚMEDO mm | CANTIDAD ESFERAS (g/m²) INTEGRADAS | SEMBRADAS MÍNIMO | TIPO DE GRADACIÓN/TIPO |
|---|---|---|---|---|
| BASE SOLVENTE | 0.38 a 0.50 | — | 0.250 | I |
| BASE AGUA | 0.38 a 0.50 | — | 0.350 | I II |
| TERMOPLÁSTICA | 3.5 a 6.00 | 0.17 a 0.66 | 0.350 | II |

La Dirección de Planeación y Proyectos solo autoriza el aspecto ejecutivo, no es responsable de la correcta ejecución de la obra. El documento no tiene validez si no presenta las firmas de los responsables para su autorización, así como los sellos respectivos.


## SEÑALES PREVENTIVAS

| SIMBOLO | CLAVE | DESCRIPCIÓN | DIMENSIÓN (cm) | UNIDAD | COLOR | CANTIDAD |
|---|---|---|---|---|---|---|
| | SP-19 | SALIDA A LA DERECHA | 71 X 71 | PZA | AMARILLO REFLEJANTE | 1 |

## SEÑALES RESTRICTIVAS


| SIMBOLO | CLAVE | DESCRIPCIÓN | DIMENSIÓN (cm) | UNIDAD | COLOR | CANTIDAD |
|---|---|---|---|---|---|---|
| | SR-9 | VELOCIDAD 50 KM/H | 71 X 71 | PZA | BLANCO REFLEJANTE CON ANILLO ROJO REFLEJANTE | 2 |

EN CORTE

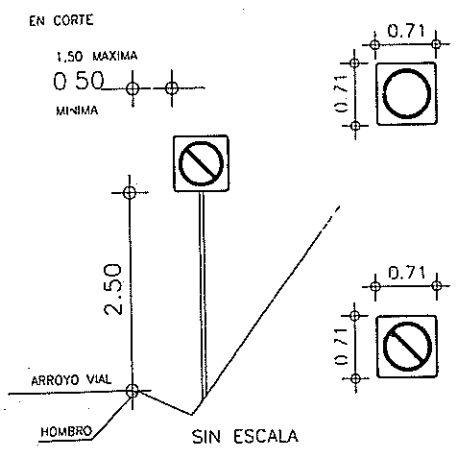



SIN ESCALA


EN TERRAPLEN

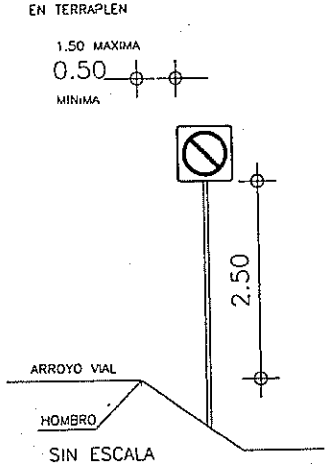


SIN ESCALA

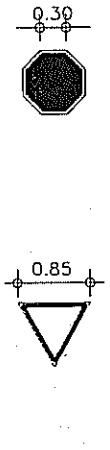


ZONA URBANA

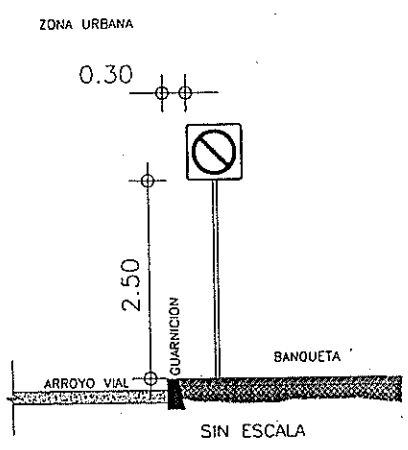


SIN ESCALA

NOTA: LAS SECCIONES ESTRUCTURALES SE ENCUENTRAN EL APARTADO II.7.3. ESTRUCTURA DE SOPORTE DE SEÑALES BAJAS. DEL MANUAL DE SEÑALAMIENTO VIAL DE LA SCT

PRESIDENTE MUNICIPAL
M.P.P. Leonardo Montañez Castro
ENCARGADA DE DESPACHO DE LA SOPIMA
Arq. Gloria Guadalupe Castillo González

| REV | FECHA | OBSERVACIONES |
|---|---|---|

V°B° DE LA DEPENDENCIA

| RESP. DE PROY. EXTERNO | | LOGO EXTERNO |
|---|---|---|
| CED. PROFESIONAL | | |
| PROYECTO | REVISO | AUTORIZÓ |

Dirección de Planeación y Proyectos de Obra — Secretaría de Obras Públicas

| PROYECTO | COORDINADOR |
|---|---|
| ARQ. RAFAEL MEDINA CONTRERAS | ARQ. ALEJANDRO JAIME LEAL |
| JEFE DE DEPTO. | DIRECTOR |
| ARQ. J. JESÚS PRADO GONZÁLEZ | ARQ. JOSÉ LUIS JUÁREZ GARCÍA |


PROYECTO
CONSTRUCCIÓN DE SOBRECARPETA ASFÁLTICA Y PAVIMENTO HIDRÁULICO, AV. DE LOS MAESTROS CALZADA ORIENTE

UBICACIÓN
TRAMO ENTRE C. PROF. JOSE GUADALUPE PERALTA Y AV. SIGLO XXI

CONTENIDO
DETALLES SEÑALETICA VERTICAL


| CLAVE | No. PLANO |
|---|---|
| DSV 01 | 09 |
| FECHA JULIO 2022 | ESCALA INDICADA |
| ACOTACIÓN METROS | No. EXP. E-000-22 |

Aguascalientes
LA CIUDAD DE TU VIDA

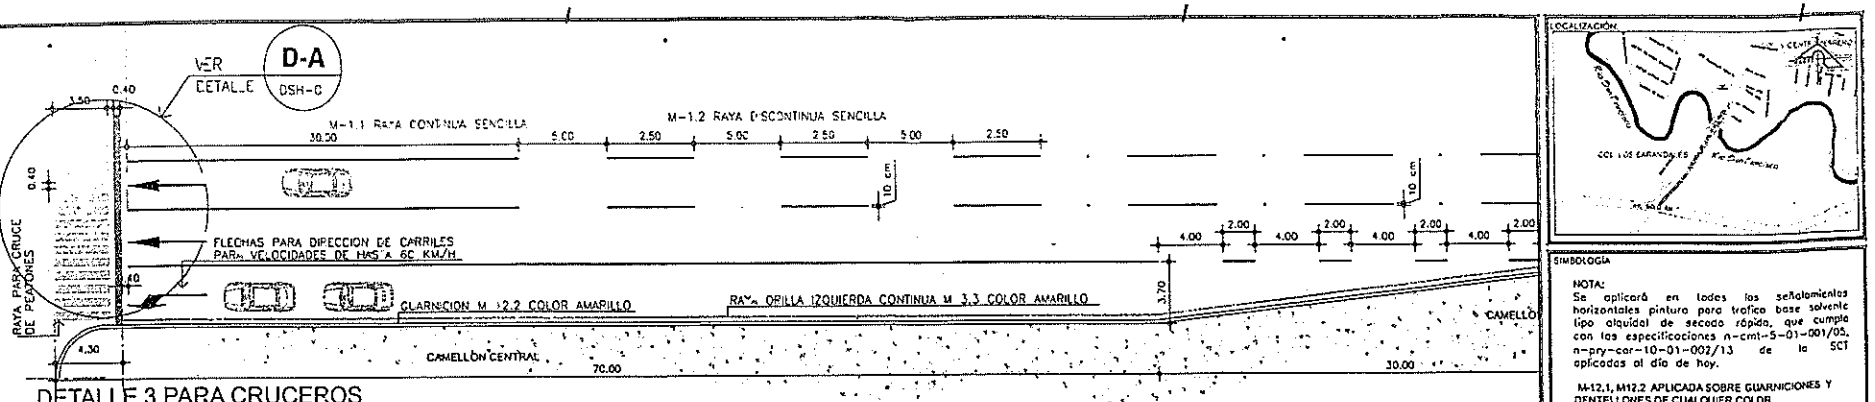


## DETALLE 3 PARA CRUCEROS CON CARGA VEHICULAR BAJA/MEDIA

COTAS: cm.

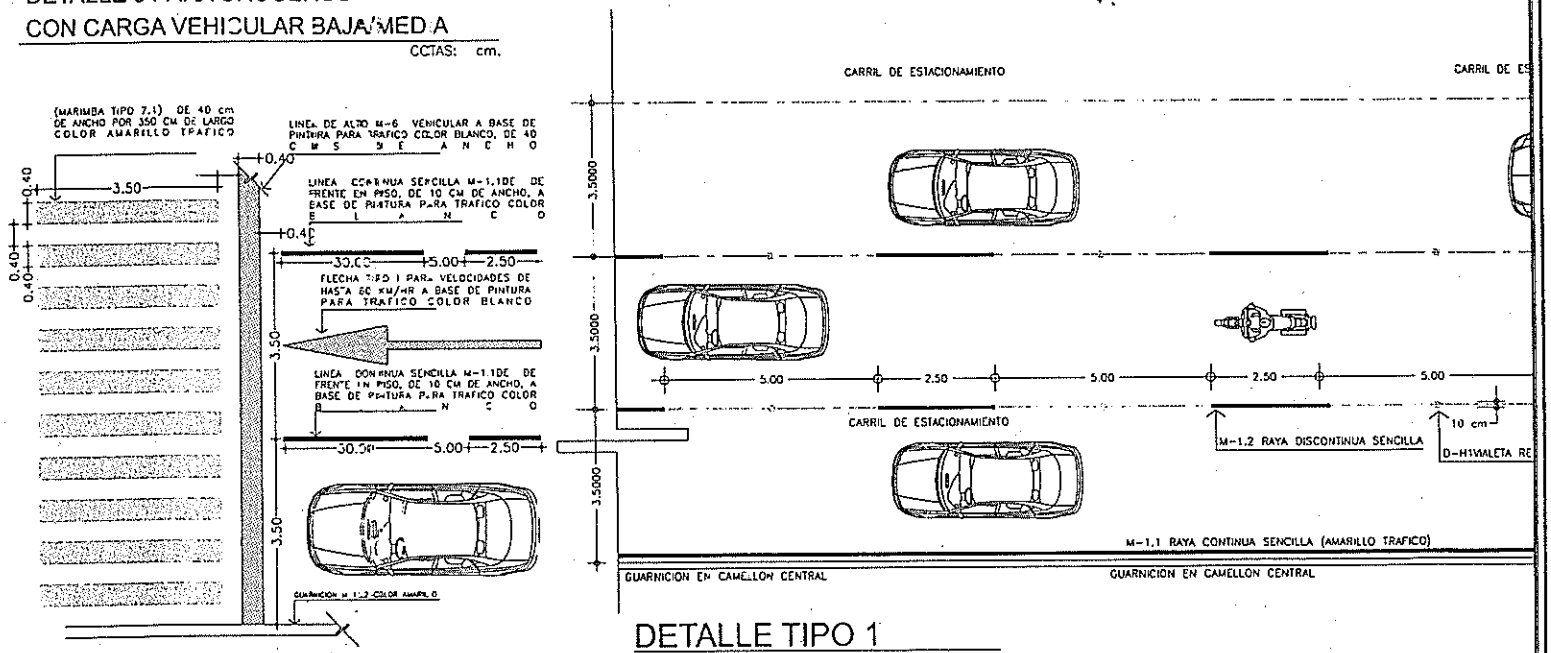


## DETALLE A

TRAZO PINTURA EN CRUCEROS SIN ESCALA

## DETALLE TIPO 1

PARA VELOCIDADES MENOR A 60 KM/HR S/E
LINEA DISCONTINUA DE 2.50 MTS ESPACIO 5 MTS
ESPESOR 10CM

LOCALIZACIÓN




SIMBOLOGÍA

NOTA:
Se aplicará en todas las señalamientos horizontales pintura para trafico base solvente tipo alquidal de secado rápido, que cumple con las especificaciones n-cmt-5-01-001/05, n-pry-car-10-01-002/13 de la SCT aplicadas al día de hoy.

M-12.1, M12.2 APLICADA SOBRE GUARNICIONES Y DENTELLONES DE CUALQUIER COLOR

Se aplicará en todas las señalamientos horizontales pintura para trafico Termoplastica tipo alquidal de secado rápido, que cumple con las especificaciones n-cmt-5-01-001/05, n-pry-car-10-01-002/13 de la SCT aplicadas al día de hoy.

M - 1.2, LÍNEA DISCONTINUA SENCILLA DE DIVISIÓN DE CARRILES DE FRENTE EN PISO, DE 10 CM DE ANCHO
M - 3.3, CONTINUA IZQUIERDA, PARA VIALIDADES URBANAS DE FRENTE EN PISO, SEPARADA 15 CM. DE LA GUARNICION, COLOR AMARILLO
M - 4, PARA INDICAR LÍNEA GUÍA EN ZONA DE TRANSICIÓN DE FRENTE EN PISO, DESARROLLO DE 2.00 X 0.10 MTS, CON UNA SEPARACIÓN DE 4.00 MTS ENTRE SI PROMEDIO
M - 5, PARA INDICAR ENTRADA Y SALIDA EN BIFURCACIONES
M - 6, PARA INDICAR ALTO EN CRUCEROS, COLOR BLANCO
M - 7.1, PARA INDICAR " CRUCE PEATONAL EN VIAS PRIMARIAS" COLOR AMARILLO
M - 11.1, "FLECHA SENCILLA" PARA INDICAR SENTIDO DE CIRCULACIÓN
M - 11.1, "FLECHA CABEZA DOBLE" PARA INDICAR SENTIDO DE CIRCULACIÓN (VUELTA IZQUIERDA O DERECHA)

NOTA:
Nota1: Se aplicará en todas las señalamientos horizontales pintura para trafico base solvente y/o termoplastica tipo alquidal de secado rápido, que cumple con las especificaciones n-cmt-5-01-001/05, n-pry-car-10-01-002/13 de la SCT aplicadas al día de hoy.

Nota2: Dosificación de micro esfera
La cantidad de esferas de vidrio en la película de pintura en humedo, según su tipo, será la que se indica en la Tabla.

TABLA 8: Cantidad de esferas de vidrio en la película de pintura en humedo.

| TIPO DE PINTURA | ESPESOR DE LA PELÍCULA DE PINTURA EN HÚMEDO (mm) | CANTIDAD DE ESFERAS (g/m2) | | TIPO DE GRADUACIÓN ESFERAS |
|---|---|---|---|---|
| | | INTEGRADAS | SEMBRADAS, MÍNIMO | |
| BASE SOLVENTE | 0.38 ± 0.50 | — | 0.350 | I |
| BASE AGUA | 0.38 ± 0.50 | — | 0.350 | II & III |
| TERMOPLÁSTICA | 1.5 ± 0.99 | 0.52 ± 0.65 | 0.350 | II |

La Dirección de Planeación y Proyectos solo autoriza el proyecto ejecutivo, no es responsable de la correcta ejecución de la obra. Este documento no tiene validez si no presenta las firmas de los responsables para su autorización, así como los sellos respectivos.

PRESIDENTE MUNICIPAL
M.P.P. Leonardo Montañez Castro
ENCARGADA DE DESPACHO DE LA DOPMA
Arq. Gloria Guadalupe Castillo González

| REV | FECHA | OBSERVACIONES |
|---|---|---|

VO. BO. DE LA DEPENDENCIA

| RESP. DE PROY EXTERNO | LOGO EXTERNO |
|---|---|
| CED. PROFESIONAL | |
| PROYECTO | REVISÓ / AUTORIZÓ |

Dirección de Planeación y Proyectos de Obra — Secretaría de Obras Públicas 2021-2024

| PROYECTISTA | COORDINADOR |
|---|---|
| ARQUITECTO [illegible] CONTRERAS | ARQ. ALEJANDRO JAIME LEAL |
| JEFE DE DEPTO. | DIRECTOR |
| ARQ. JESÚS PALACIOS GONZÁLEZ | M. en ARQ. JOSÉ LUIS JIMÉNEZ GARCÍA |


PROYECTO
CONSTRUCCION DE SOBRECARPETA ASFALTICA Y PAVIMENTO HIDRAULICO, AV. DE LOS MAESTROS CALZADA ORIENTE

UBICACIÓN
TRAMO ENTRE C. PROF. JOSE GUADALUPE PERALTA Y AV. SIGLO XXI


CONTENIDO
DETALLES SEÑALETICA HORIZONTAL

| CLAVE | No. PLANO |
|---|---|
| DSH 01 | 08 |
| FECHA: JULIO 2022 | ESCALA: INDICADA |
| ACOTACIÓN: METROS | No. EXP.: E.000-23 |

Aguascalientes
LA CIUDAD DE TU VIDA

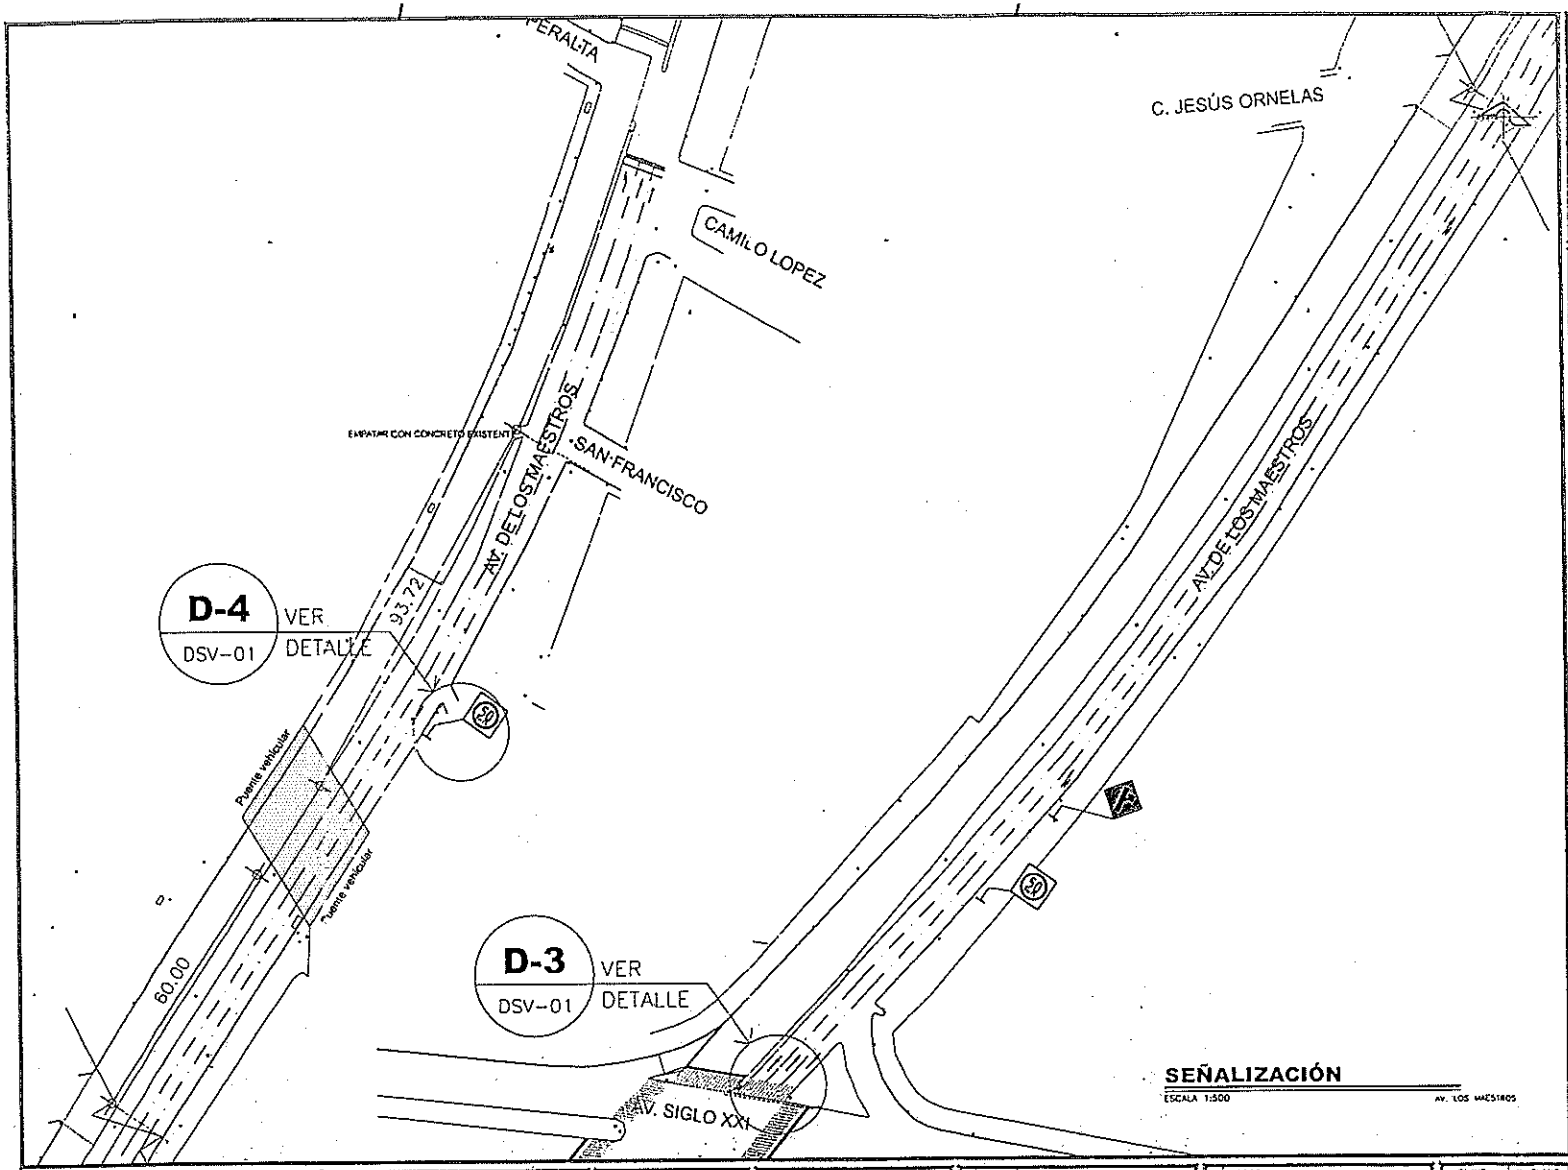


LOCALIZACIÓN

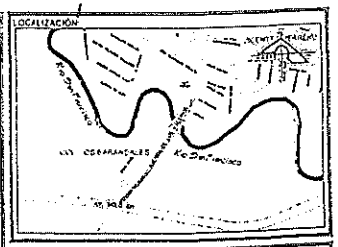

SIMBOLOGÍA

NOTA:
Se aplicará en todos los señalamientos horizontales pintura para trafico base solvente tipo alquidal de secado rápido, que cumpla con las especificaciones n-cmt-5-01-001/05, n-pry-car-10-01-002/13 de la SCT aplicadas al día de hoy.

M-12.1, M12.2 APLICADA SOBRE GUARNICIONES Y DENTELLONES DE CUALQUIER COLOR

Se aplicará en todos los señalamientos horizontales pintura para trafico Termoplastica tipo alquidal de secado rápido, que cumpla con las especificaciones n-cmt-5-01-001/05, n-pry-car-10-01-002/13 de la SCT aplicadas al día de hoy.

M - 1.2, LÍNEA DISCONTINUA SENCILLA DE DIVISIÓN DE CARRILES DE FRENTE EN PISO, DE 10 CM DE ANCHO
M - 3.3, CONTINUA IZQUIERDA, PARA VIALIDADES URBANAS DE FRENTE EN PISO, SEPARADA 15 CM, DE LA GUARNICIÓN, COLOR AMARILLO
M - 4, PARA INDICAR LÍNEA GUÍA EN ZONA DE TRANSICIÓN DE FRENTE EN PISO, DESARROLLO DE 2.00 X 0.10 MTS, CON UNA SEPARACIÓN DE 4.00 MTS ENTRE SI PROMEDIO
M - 5, PARA INDICAR ENTRADA Y SALIDA EN BIFURCACIONES
M - 6, PARA INDICAR ALTO EN CRUCEROS, COLOR BLANCO
M - 7.1, PARA INDICAR " CRUCE PEATONAL EN VIAS PRIMARIAS" COLOR AMARILLO
M - 1 .1, "FLECHA SENCILLA" PARA INDICAR SENTIDO DE CIRCULACIÓN
M - 1 .1, "FLECHA CABEZA DOBLE" PARA INDICAR SENTIDO DE CIRCULACIÓN (VUELTA IZQUIERDA O DERECHA)

NOTA:
Nota1: Se aplicará en todos los señalamientos horizontales pintura para trafico base solvente y/o termoplastica tipo alquidal de secado rápido, que cumpla con las especificaciones n-cmt-5-03-001/05, n-pry-car-10-01-002/13 de la SCT aplicadas al día de hoy.

Nota2: Dosificación de micro esfera
La cantidad de esferas de vidrio en la película de pintura en húmedo, según su tipo, será la que se indica en la Tabla.

TABLA 8: Cantidad de esferas de vidrio en la película de pintura en humedo.

| TIPO DE PINTURA | ESPESOR DE LA PELICULA DE PINTURA EN HÚMEDO mm | CANTIDAD DE ESFERAS kg/m² INTEGRADAS | SOBREADAS, MÍNIMO | TIPO DE GRANULOMETRÍA |
|---|---|---|---|---|
| BASE SOLVENTE | 0.38 - 0.50 | --- | 0.330 | 1 |
| BASE AGUA | 0.38 - 0.50 | --- | 0.330 | 1 ó 12 |
| TERMOPLASTICA | 3.5 a 0.65 | 0.17 a 0.65 | 0.330 | 21 |

La Dirección de Planeación y Proyectos solo autoriza el proyecto ejecutivo, no es responsable de la correcta ejecución de la obra. Este documento no tiene validez si no presenta las firmas de los responsables para su autorización, así como los sellos respectivos.

PRESIDENTE MUNICIPAL
M.P.P. Leonardo Montañez Castro
ENCARGADA DE DESPACHO DE LA SOPMA
Arq. Gloria Guadalupe Castillo González

REV. FECHA OBSERVACIONES

V°B° DE LA DEPENDENCIA

RESP. DE PROY. EXTERNO
CED. PROFESIONAL
PROYECTÓ REVISÓ AUTORIZÓ
LOGO EXTERNO

Dirección de Planeación y Proyectos de Obra
Secretaría de Obras Públicas
PROYECTÓ: ARQ. ALVARO DE LA FUENTE
COORDINADOR: ARQ. ALEJANDRO JAIME LEAL
JEFE DE DEPTO.: ARQ. J. SEBASTIAN LAVIN GONZALEZ
DIRECTOR: M. en ARQ. JOSÉ LUIS JIMÉNEZ GARCÍA

PROYECTO
CONSTRUCCION DE SOBRECARPETA ASFALTICA Y PAVIMENTO HIDRAULICO, AV. DE LOS MAESTROS CALZADA ORIENTE
UBICACIÓN
TRAMO ENTRE C. PROF. JOSE GUADALUPE PERALTA Y AV. SIGLO XXI
CONTENIDO
PROYECTO SEÑALIZACIÓN HORIZONTAL

| CLAVE | No. PLANO |
|---|---|
| SEÑ 01 | 07 |
| FECHA JULIO 2022 | ESCALA INDICADA |
| ACOTACIÓN METROS | No. EXP. E-000-22 |

Aguascalientes
LA CIUDAD DE TU VIDA

## SIMBOLOGIA


a) BACHEO PROFUNDO AISLADO UTILIZANDO MATERIAL CALIDAD BASE HIDRAULICO, PARA MAS DE UN MILLON DE EJES EQUIVALENTES DEL BANCO QUE E.N.L. E. CONTRATISTA, INCISO N.CSV.CAR.1.02.004/03 DE LAS NORMAS DE CONSTRUCCION DE CARR. DE LA SCT.

c) RENIVELACIONES CON CONCRETO ASFALTICO MEZCLA EN PLANTA EN CALIENTE ASFALTO MODIFICADO CON POLIMERO TIPO I, CUMPLIENDO CON LAS NORMAS SC REFERENTES DE CONSTRUCCION Y CONSERVACION, GRANULOMETRIA DENSA 3/4" A FINOS, MEDIDO COMPACTO AL NOVENTA Y CINCO PORCIENTO (95%)

c) RIEGO DE IMPREGNACION CON EMULSION DE ROMPIMIENTO LENTO (ECL-60 %), INCLUYE BARRIDO DE LA SUPERFICIE, LIMPIEZA A DETALLE, SUMINISTRO, ALMACENAMIEN O, CALENTAMIENTO, Y APLICACION DE LA EMULSION CON EQUIPO ESPECIAL PARA ESA ACTIVIDAD, ESPREAS LIMPIAS Y ALINEADAS, EN CASO DE RECOMENDARLO EL LABORATORIO DE CALIDAD DEL CONTRATISTA SE DEBERA DAR UN RIEGO MATAPOLVO ANTES DE COLOCAR LA CAPA DE IMPREGNACION, A RAZON DE 1.5 LT DE EMULSION POR M2, O LO QUE INDIQUE EL LABORATORIO DE CALIDAD DEL CONTRATISTA


d) RIEGO DE LIGA CON EMULSION DE ROMPIMIENTO RAPIDO (ECR-65 %), INCLUYE, SUMINISTRO, ALMACENAMIENTO, CALENTAMIENTO, Y APLICACION DE LA EMULSION CON EQUIPO ESPECIAL PARA ESA ACTIVIDAD, ESPREAS O BACHADOR LIMPIAS Y ALINEADAS, EN LA PETROLIZADORA, A RAZON DE 0.8 LT DE EMULSION POR M2, O LO QUE INDIQUE EL LABORATORIO DE CALID-D DEL CONTRATISTA, NO SE ACEPTAN "IMPREGNALICA"

e) CONCRETO ASFALTICO EN CALIENTE DE GRANULOMETRIA DENSA ELABORADA CON ASFALTO MODIFICADO TIPO I, AGREGADO 3/4" A FINOS, DE 5 CM DE ESPESOR TOTAL, FORMADA Y COMPACTADO AL 95%, INCLUYE MATERIALES, QUE CUMPLAN LA NORMATIVA SCT-N-CMT-04-04, SCT-CMT-4-05-002, SCT-CMT-4-05-003, SCT-CMT-4-05-004, SCT-CTR-CAR-1-04-006-14 APLICADAS AL DIA DE HOY, DISEÑO MARSHALL (DEBERA SER AUTORIZADO POR EL LABORATORIO DE CALIDAD DE SOPMA AL MENOS 3 DIAS ANTES DE INICIO DE TENDIDO DE LA MEZCLA ASFALTICA)

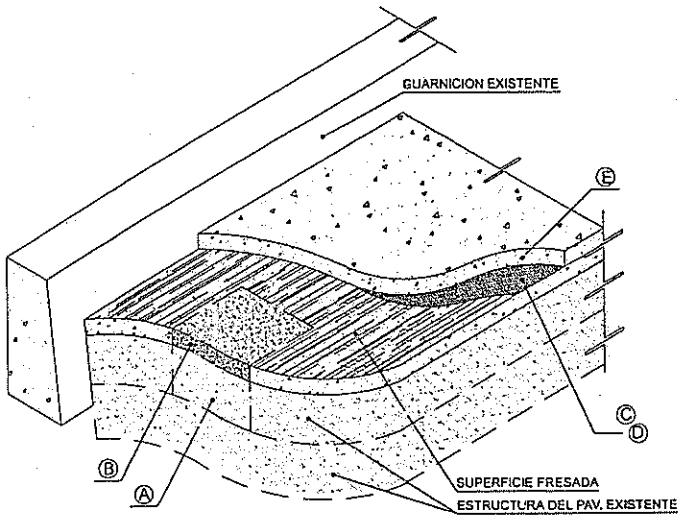



**ESTRUCTURA DE PAVIMENTO**
ESCALA S/E

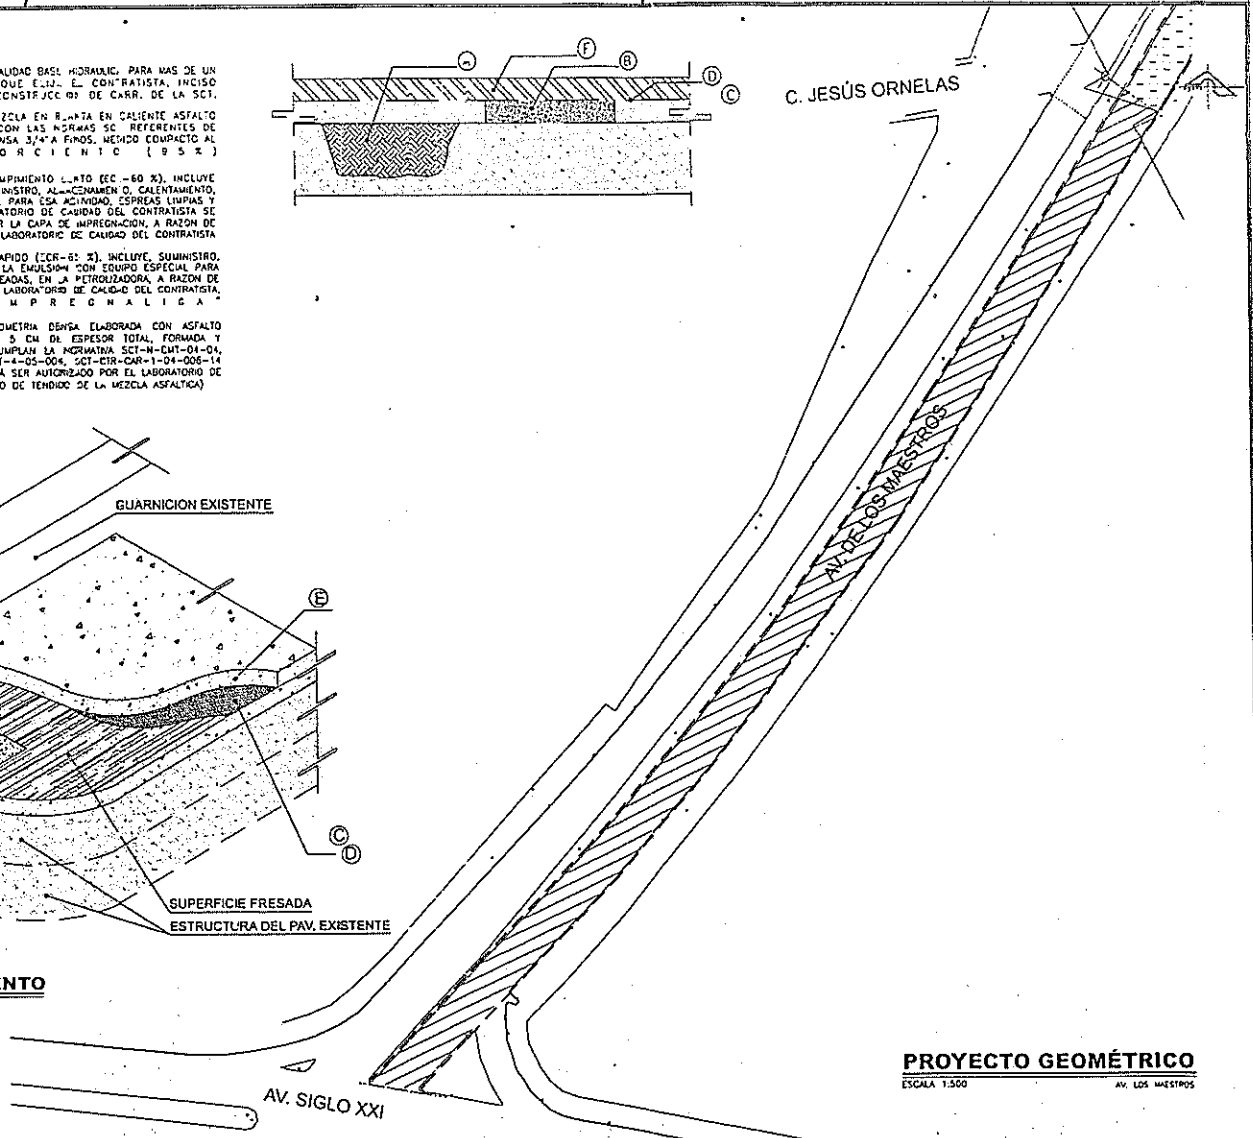


**PROYECTO GEOMÉTRICO**
ESCALA 1:500 AV. LOS MAESTROS

LOCALIZACIÓN

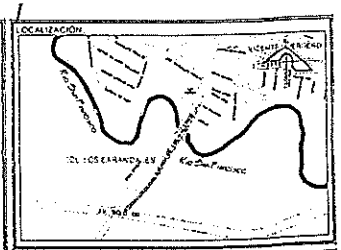



SIMBOLOGIA

- LIMITE DE PROYECTO
- BANQUETAS
- PAVIMENTO
- CAMAN
- CAJA VALVULAS
- BOTA HIDRÁULICA
- POZO DE VISITA EXISTENTE
- CONSTRUCCIÓN DE DENTELLON RECTO Y/O CURVO 20-20X40 CM DE SECCIÓN, CON CONCRETO PREMEZCLADO MR=42 KG/CM2 T.M.A. 1 ½" GRAVA TRITURADA, R.R. 3 DIAS, REVENIMIENTO NORMAL DE 10±2 CM, GRAVA TRITURADA, ACABADO CON DOBLADOR Y PULIDO.
- CONSTRUCCIÓN DE PAVIMENTO HIDRAULICO A BASE DE CONCRETO PREMEZCLADO MR=42 KG/CM2 T.M.A. 1 ½" GRAVA TRITURADA, REVENIMIENTO DE 6 A 8 CM FRAGUADO NORMAL DE 20 CM DE ESPESOR MODULADO EN LOSAS DE 3.5 MTS. (ANCHO) X 3.5 MTS. (LARGO) COMO MAXIMO, CON CORTES EN LAS LOSAS DE ⅓ DEL ESPESOR DE LA LOSA (7 CM) Y SELLADO CON MATERIAL ELASTOMERICO Y TIRA PREFORMADA EN JUNTAS Y CORTES LONGITUDINALES Y TRASVERSALES CON COLA DE RATA DE ½", ASI COMO EL APROCHE CON GUARNICION Y DENTELLON.
- SUMINISTRO Y COLOCACION DE CONCRETO ASFALTICO EN CALIENTE DE GRANULOMETRIA DENSA ELABORADA CON ASFALTO MODIFICADO TIPO I, AGREGADO 3/4" A FINOS, DE 5 CM DE ESPESOR, FORMADA Y COMPACTADO AL 95% QUE CUMPLAN LA NORMATIVA SCT-N-CMT-04-04, SCT-CMT-4-05-002, SCT-CMT-4-05-003, SCT-CMT-4-05-004, SCT-CTR-CAR-1-04-006-14 APLICADAS AL DIA DE HOY, DISEÑO MARSHALL (DEVERA SER AUTORIZADO POR EL LABORATORIO DE CALIDAD DE SOPMA AL MENOS 3 DIAS ANTES DE INICIO DE TENDIDO DE LA MEZCLA ASFALTICA).
- BACHEO SUPERFICIAL AISLADO CON CARPETA DE CONCRETO ASFALTICO ELABORADO EN PLANTA EN CALIENTE, A BASE DE CEMENTO ASFALTICO AC-20 T.M.A. 3/4" A FINOS EN UN ESPESOR PROMEDIO DE 5.0 CM COMPACTOS.
- BACHEO PROFUNDO AISLADO CON CARPETA DE CONCRETO ASFALTICO ELABORADO EN PLANTA EN CALIENTE, A BASE DE CEMENTO ASFALTICO AC-20 T.M.A. 3/4" A FINOS, EN UN ESPESOR DE 5.0 CM COMPACTOS Y MATERIAL DE BASE HIDRAULICA DE 20 CM. DE ESPESOR COMPACTOS.
- LIMPIEZA GENERAL DE LA OBRA, INCLUYE: BARRIDO, CARGA, ACARREOS Y RETIRO DE ESCOMBROS FUERA DE LA OBRA, TRABAJO TERMINADO, EN TODA LA SUPERFICIE A INTERVENIR.


La Dirección de Planeación y Proyectos solo autoriza el proyecto ejecutivo, no es responsable de la correcta ejecución de la obra. Este documento no tiene validez si no presenta las firmas de los responsables para su autorización, así como los sellos respectivos.

| | | | | | | | | | |
|---|---|---|---|---|---|---|---|---|---|
| PRESIDENTE MUNICIPAL<br>M.P.P. Leonardo Montañez Castro<br>ENCARGADA DE DESPACHO DE LA SOPMA<br>Arq. Gloria Guadalupe Castillo González | REV. FECHA OBSERVACIONES | No. DE LA DEPENDENCIA | RESP. DE PROY. EXTERNO<br>CED. PROFESIONAL<br>PROYECTO / REVISO | LOGO EXTERNO<br>AUTORIZO | Dirección de Planeación y Proyectos de Obra<br>PROYECTO<br>ARQ. ALVARO ALEJANDRO CONTRERAS<br>JEFE DE DEPTO.<br>ARQ. J. JESUS PALACIOS GONZALEZ | Secretaría de Obras Públicas<br>COORDINADOR<br>ARQ. ALEJANDRO JOSUE LEAL<br>DIRECTOR<br>M. en ARQ. JOSE LUIS JIMENEZ GARCIA | PROYECTO<br>CONSTRUCCION DE SOBRECARPETA ASFALTICA Y PAVIMENTO HIDRAULICO, AV. DE LOS MAESTROS CALZADA ORIENTE<br>UBICACIÓN<br>TRAMO ENTRE C. PROF. JOSE GUADALUPE PERALTA Y AV. SIGLO XXI<br>CONTENIDO<br>PROYECTO GEOMETRICO | CLAVE<br>GEO 01<br>FECHA<br>JULIO 2022<br>ACOTACIÓN<br>METROS | No. PLANO<br>04<br>ESCALA<br>INDICADA<br>No. EXP.<br>E-000-22 | Aguascalientes<br>LA CIUDAD DE TU VIDA |

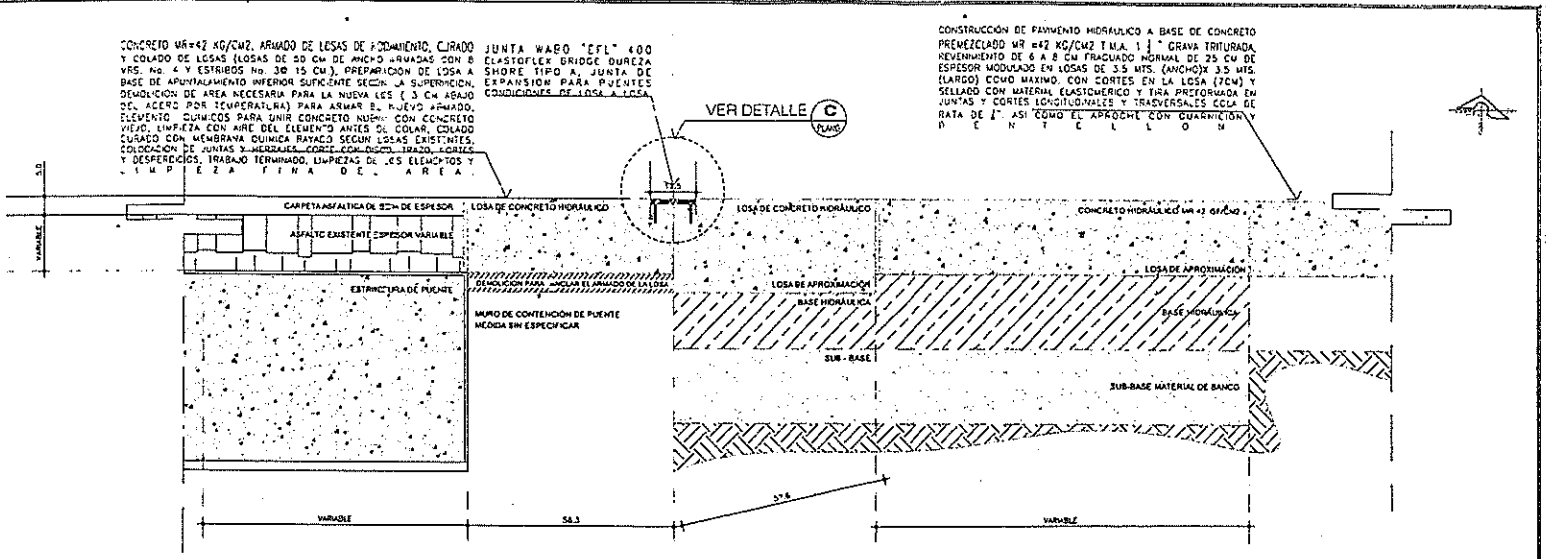



## DETALLE JUNTA DE PAVIMENTO EN PUENTE VEHICULAR

ESCALA S/E

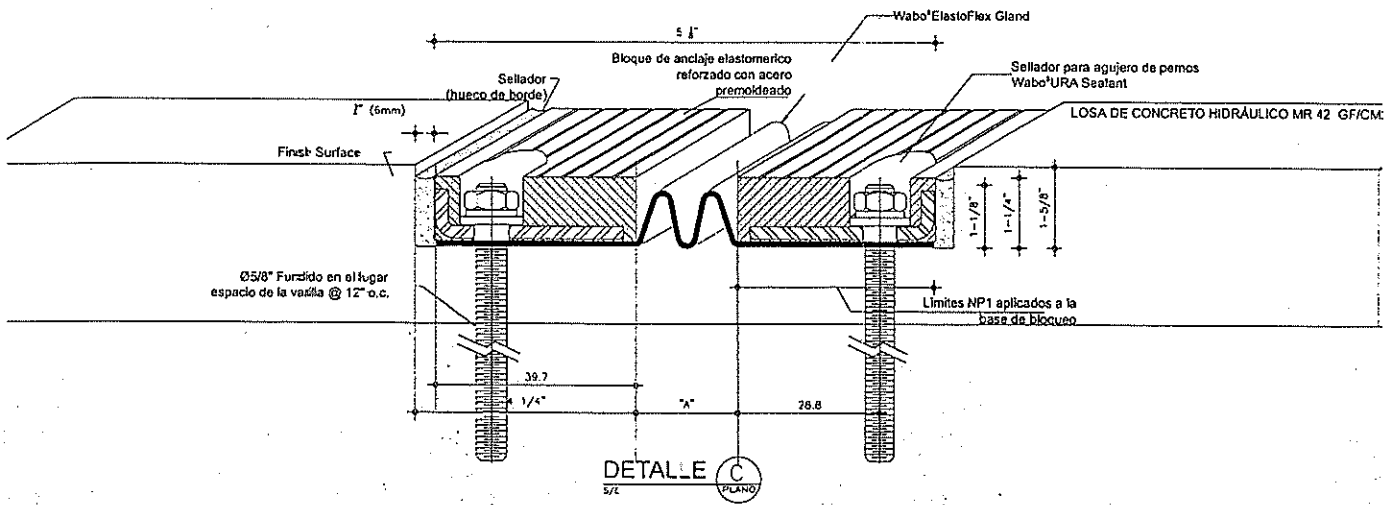


DETALLE C (PLANO) S/E

LOCALIZACIÓN

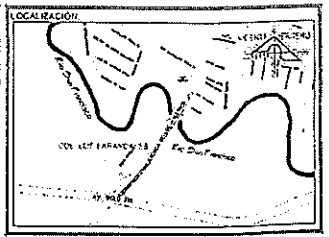

SIMBOLOGÍA

La Dirección de Planeación y Proyectos solo autoriza el proyecto ejecutivo, no es responsable de la correcta ejecución de la obra. Este documento no tiene validez si no presenta las firmas de los responsables para su autorización, así como los sellos respectivos.

PRESIDENTE MUNICIPAL
M.P.P. Leonardo Montañez Castro
ENCARGADA DE DESPACHO DE LA SOPMA
Arq. Gloria Guadalupe Castillo González

| REV | FECHA | OBSERVACIONES |
|---|---|---|
| | | |

V°B° DE LA DEPENDENCIA

| RESP. DE PROY. EXTERNO | | LOGO EXTERNO |
|---|---|---|
| CED. PROFESIONAL | | |
| PROYECTO | REVISO | AUTORIZO |

Dirección de Planeación y Proyectos de Obra — Secretaría de Obras Públicas

| PROYECTO | COORDINADOR |
|---|---|
| ARQ. ALVARO ALEJANDRO CONTRERAS | ARQ. ALEJANDRO JAIME LEAL |
| JEFE DE DEP. | DIRECTOR |
| ARQ. I. JESÚS PAULINO GONZÁLEZ | M. en ARQ. JOSÉ LUIS IBÁÑEZ GARCÍA |


PROYECTO
CONSTRUCCION DE SOBRECARPETA ASFALTICA Y PAVIMENTO HIDRAULICO, AV. DE LOS MAESTROS CALZADA ORIENTE

UBICACIÓN
TRAMO ENTRE C. PROF. JOSE GUADALUPE PERALTA Y AV. SIGLO XXI

CONTENIDO
DETALLE JUNTA DE EXPANSION

| CLAVE | No. PLANO |
|---|---|
| GEO 03 | 06 |
| FECHA: JULIO 2022 | ESCALA: INDICADA |
| ACOTACIÓN: METROS | No. EXP.: E-000-22 |

Aguascalientes
LA CIUDAD DE TU VIDA

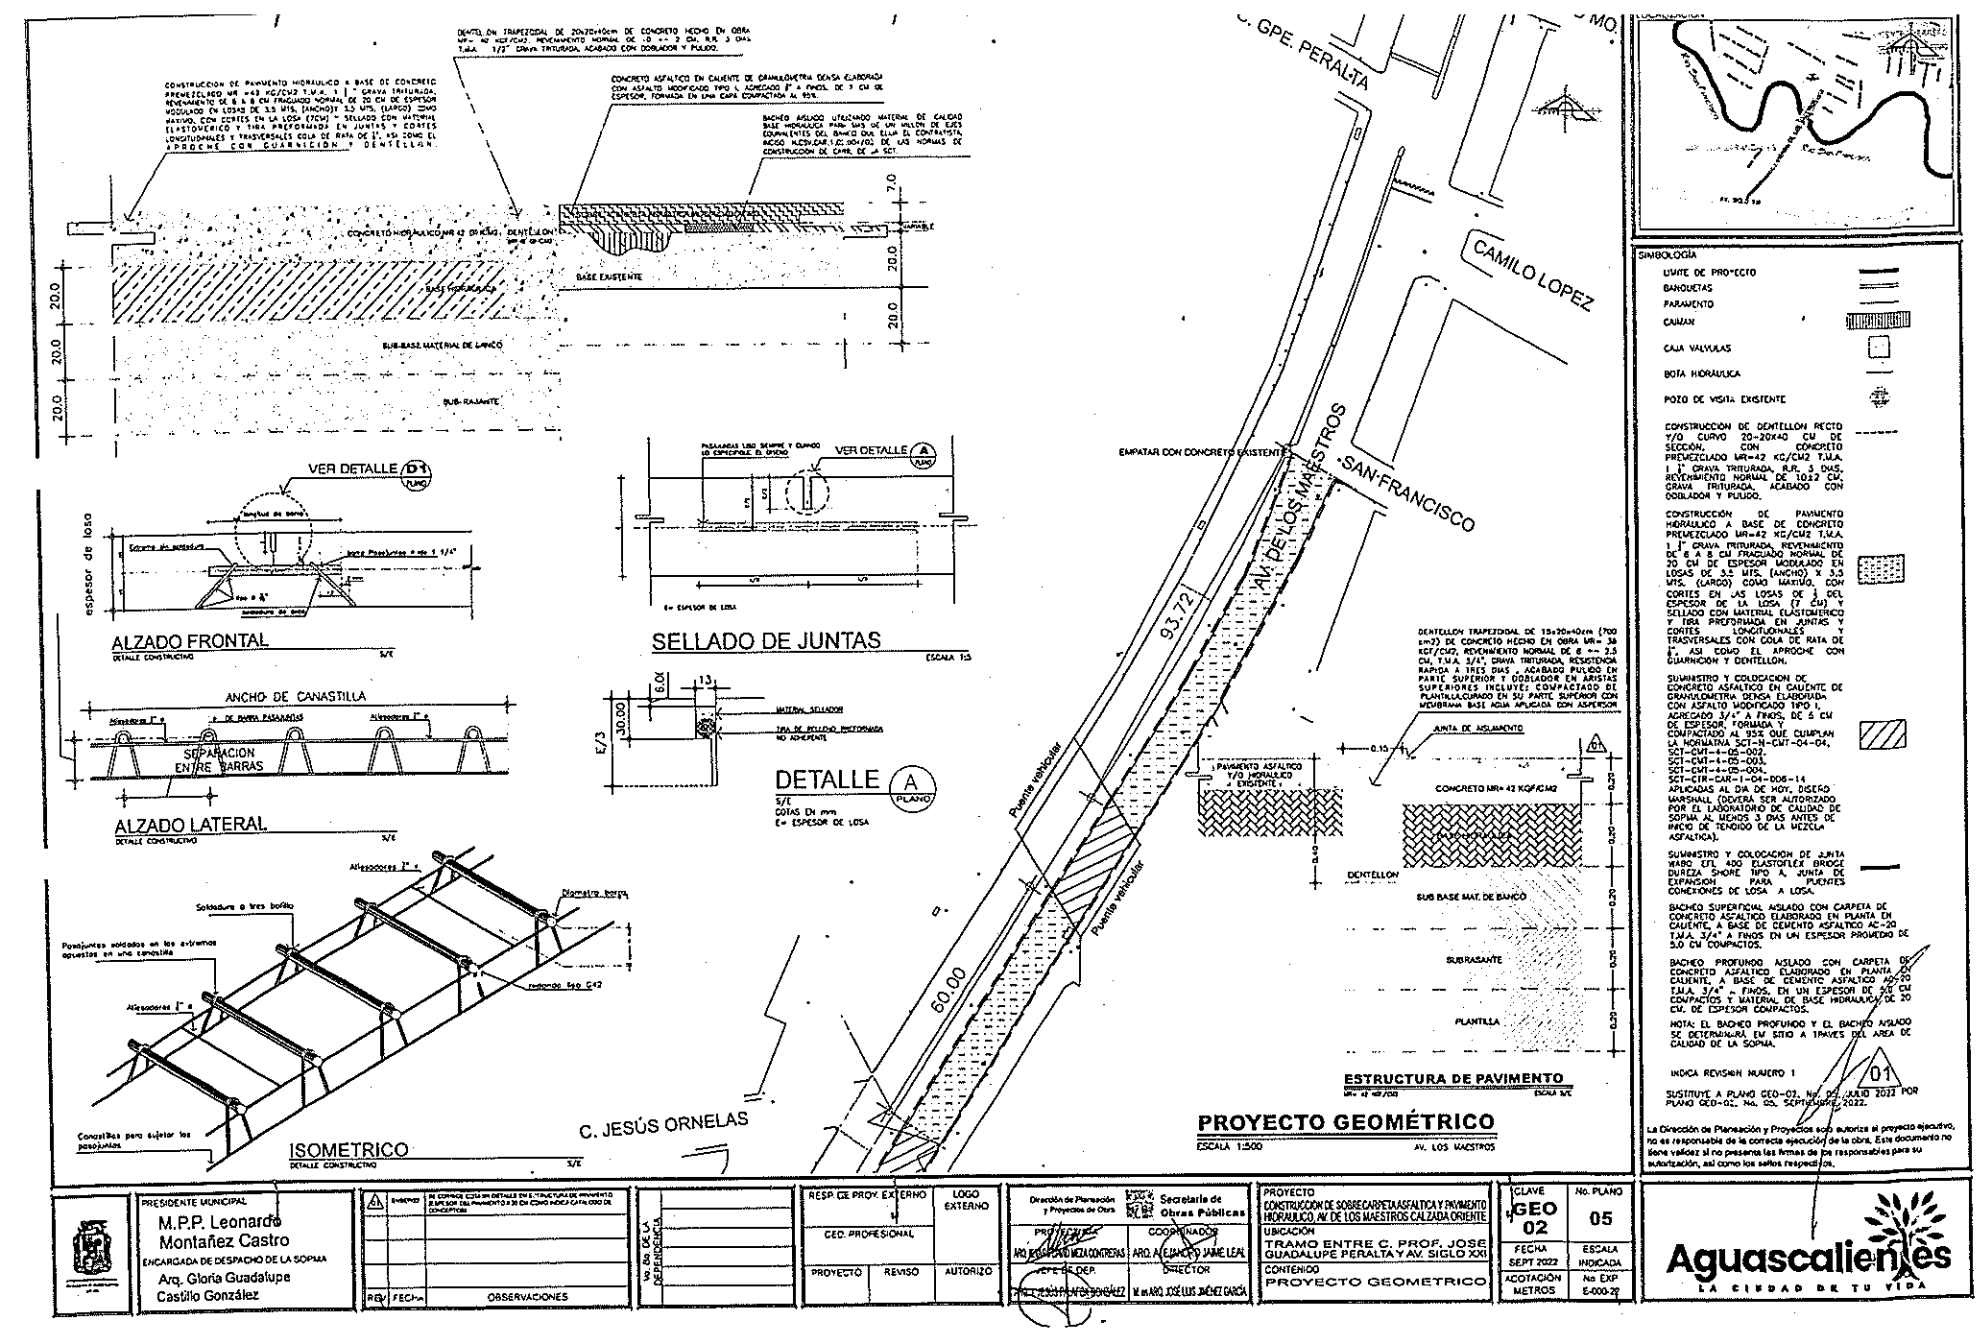


PRESIDENTE MUNICIPAL
M.P.P. Leonardo Montañez Castro
ENCARGADA DE DESPACHO DE LA SOPMA
Arq. Gloria Guadalupe Castillo González

| REV. | FECHA | OBSERVACIONES |
|---|---|---|
| 1 | | RE CONFORME CLOSA SIN DETALLE EN E. ESTRUCTURA DE PAVIMENTO Y SE SOP DEL PAVIMENTO 2.5 DE CON NUEVO CATALOGO DE CONCEPTOS |

No. DE LA DEPENDENCIA

| RESP. DE PROY. EXTERNO | | LOGO EXTERNO |
|---|---|---|
| CED. PROFESIONAL | | |
| PROYECTO | REVISO | AUTORIZO |


Dirección de Planeación y Proyectos de Obra — Secretaría de Obras Públicas

| PROYECTO | COORDINADOR |
|---|---|
| ARQ. ESTEFANIA MEZA CONTRERAS | ARQ. ALEJANDRO JAIME LEAL |
| JEFE DE DEP. | DIRECTOR |
| ARQ. ESTEFANIA MEZA GONZÁLEZ | M. en ARQ. JOSÉ LUIS JIMÉNEZ GARCÍA |

PROYECTO
CONSTRUCCION DE SOBRECARPETA ASFALTICA Y PAVIMENTO HIDRAULICO AV. DE LOS MAESTROS CALZADA ORIENTE
UBICACIÓN
TRAMO ENTRE C. PROF. JOSE GUADALUPE PERALTA Y AV. SIGLO XXI
CONTENIDO
PROYECTO GEOMETRICO

| CLAVE | No. PLANO |
|---|---|
| GEO 02 | 05 |
| FECHA | ESCALA |
| SEPT 2022 | INDICADA |
| ACOTACIÓN | No EXP |
| METROS | E-000-22 |

Aguascalientes
LA CIUDAD DE TU VIDA

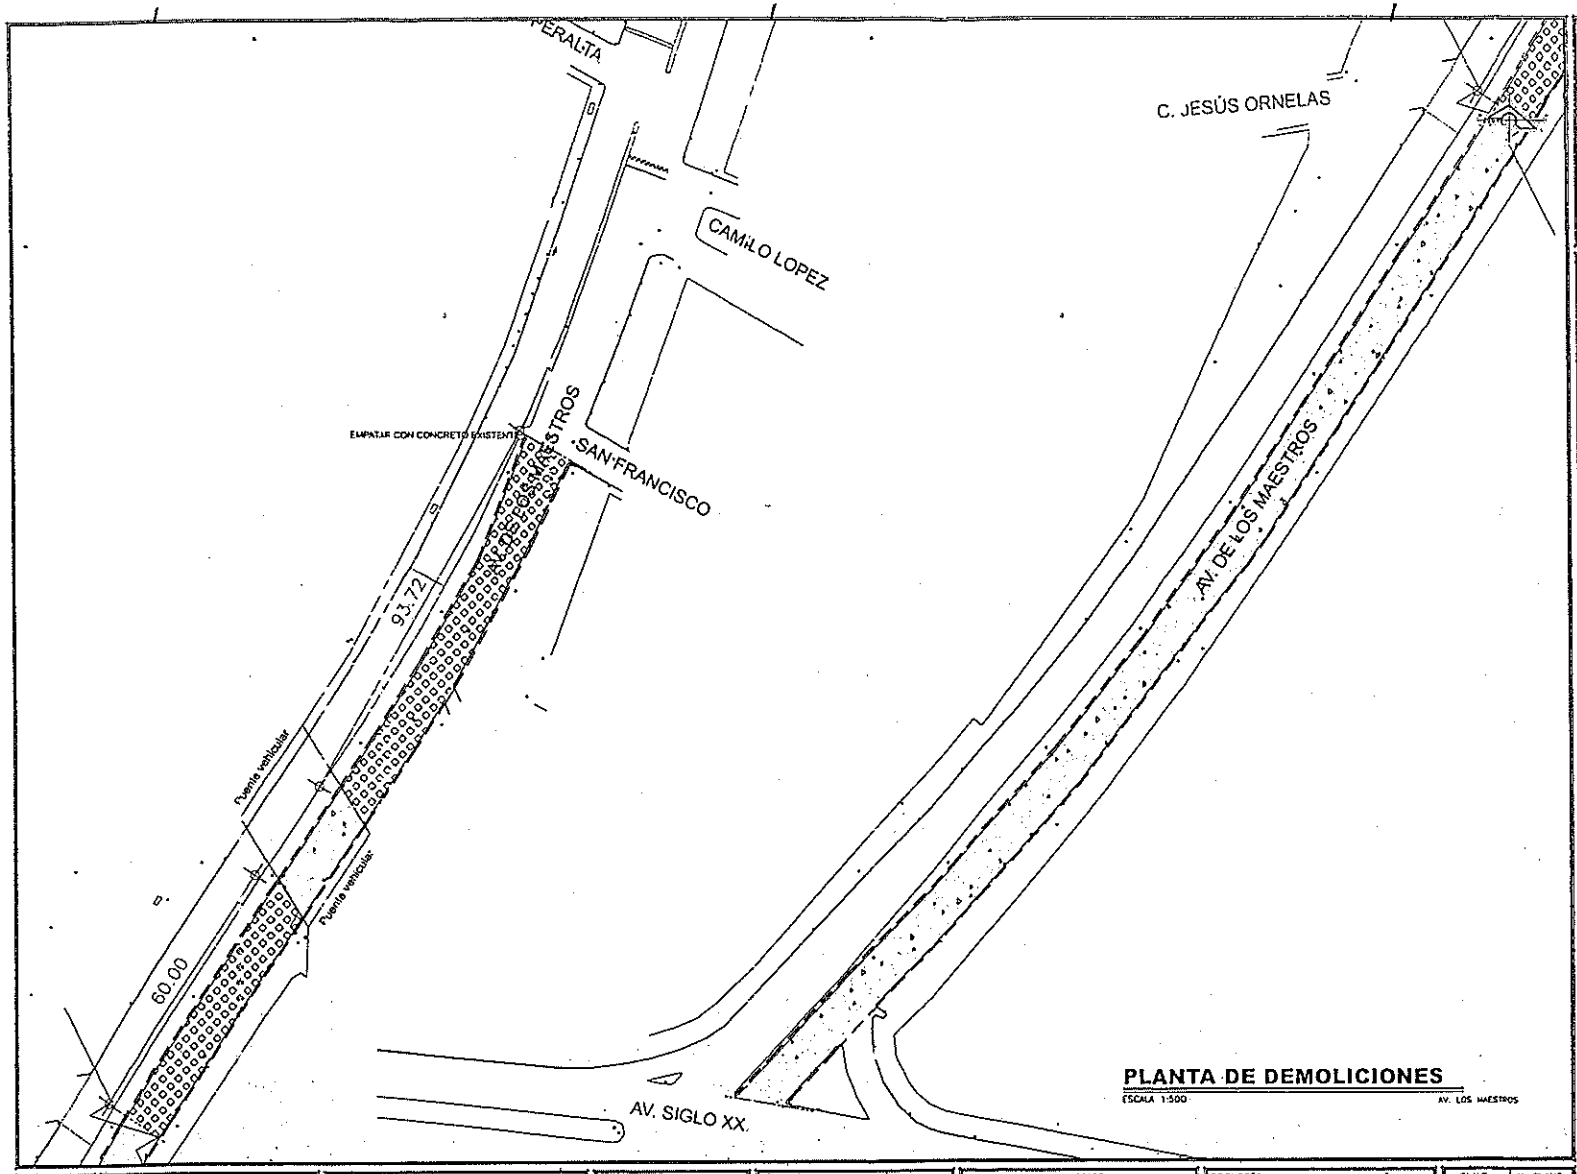



## PLANTA DE DEMOLICIONES

ESCALA 1:500

AV. LOS MAESTROS

LOCALIZACIÓN:

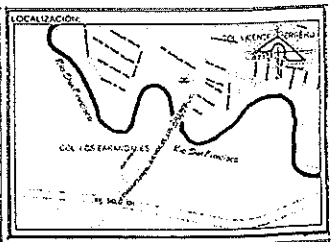

SIMBOLOGÍA

- LIMITE DE PROYECTO
- LIMITE DE PROYECTO
- BANQUETAS
- PARAMENTO
- CORTE CON DISCO
- FRESADO UNIFORME DE LA SUPERFICIE DE RODADURA EN PAVIMENTOS DE CONCRETO ASFÁLTICO (5 CM DE ESPESOR PROMEDIO), MEDIANTE FRESADORA EN FRIO COMPACTA, EQUIPADA CON BANDA TRANSPORTADORA PARA CARGA DIRECTA SOBRE CAMIÓN DE VOLTEO.
- DEMOLICION PARCIAL DE PAVIMENTO ASFALTICO Y/O HIDRAULICO EN PAVIMENTOS Y ( BANQUETAS, LOSAS DIAMANTE Y CAJAS DE VALVULAS, TOPES ) CON O SIN ARMADO DE ACERO, SIN RECUPERACION, MUROS, MOJONERAS, ANCLAJES, ETC, DE FORMA MANUAL Y MECANICA.
- DESMONTAJE DE BROCAL

NOTA:
LAS DEMOLICIONES DE GUARNICIONES Y/O DENTELLONES SE DETERMINAN EN SITIO, UBICANDO O DANDO PRIORIDAD A LAS ÁREAS MAS DAÑADA, DANDO LA AUTORIZACIÓN AL EJECUTOR POR PARTE DEL SUPERVISOR DE OBRA DE SOPMA.

La Dirección de Planeación y Proyectos solo aunotza el proyecto ejecutivo, no es responsable de la correcta ejecución de la obra. Este documento no tiene validez sino presenta las firmas de los responsables para su autorización, así como los sellos respectivos.

PRESIDENTE MUNICIPAL
M.P.P. Leonardo Montañez Castro
ENCARGADA DE DESPACHO DE LA SOPMA
Arq. Gloria Guadalupe Castillo González

| REV | FECHA | OBSERVACIONES |
|---|---|---|
| | | |

No. DE LA DEPENDENCIA

| RESP. DE PROY. EXTERNO | | LOGO EXTERNO |
|---|---|---|
| CED. PROFESIONAL | | |
| PROYECTO | REVISÓ | AUTORIZÓ |

Dirección de Planeación y Proyectos de Obra — Secretaría de Obras Públicas

| PROYECTISTA | COORDINADOR |
|---|---|
| ARQ. ALEJANDRO JAIME LEAL | |
| JEFE DE DEPTO. | DIRECTOR |
| ING. J. JESÚS PULIDO GONZÁLEZ | M. en ARQ. JOSÉ LUIS MÁRQUEZ GARCÍA |


| | |
|---|---|
| PROYECTO | CONSTRUCCION DE SOBRECARPETA ASFALTICA Y PAVIMENTO HIDRAULICO, AV. DE LOS MAESTROS CALZADA ORIENTE |
| UBICACIÓN | TRAMO ENTRE C. PROF. JOSE GUADALUPE PERALTA Y AV. SIGLO XXI |
| CONTENIDO | PLANTA DE DEMOLICIONES |

| CLAVE | No. PLANO |
|---|---|
| DEM 01 | 03 |
| FECHA: JULIO 2022 | ESCALA: INDICADA |
| ACOTACIÓN: METROS | No. EXP.: E-000-22 |

Aguascalientes
LA CIUDAD DE TU VIDA


## ESTADO ACTUAL

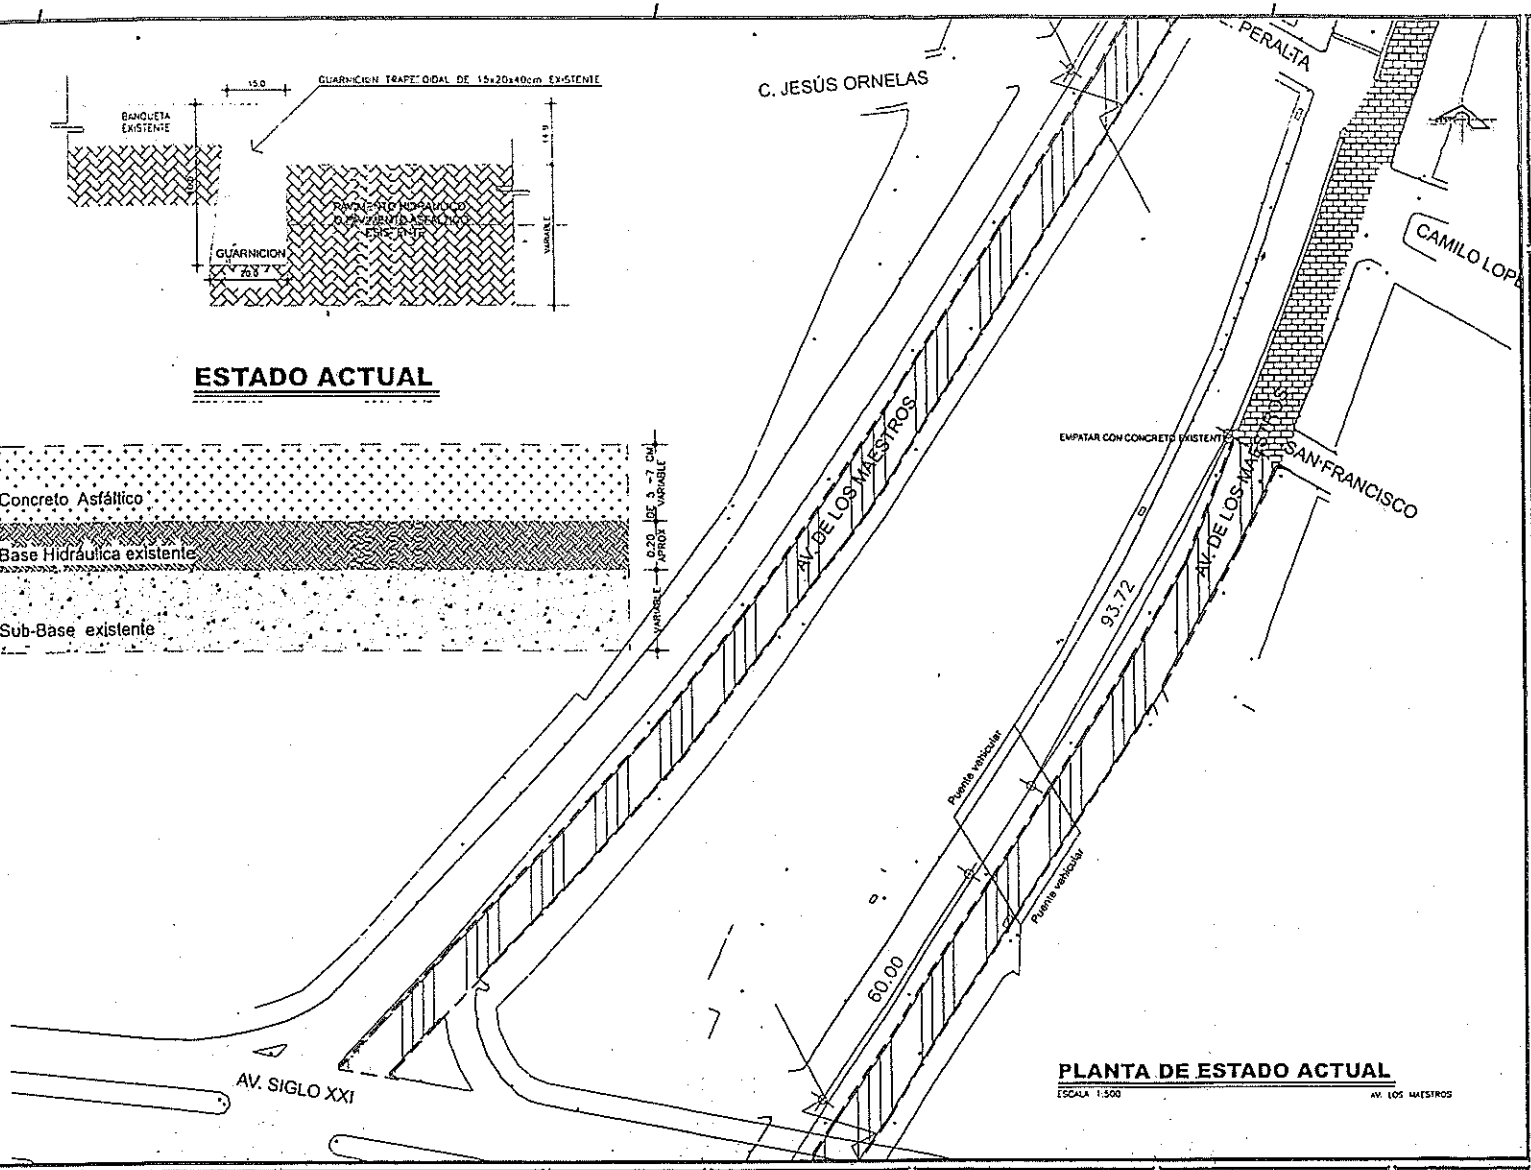


## PLANTA DE ESTADO ACTUAL

ESCALA 1:500 AV. LOS MAESTROS

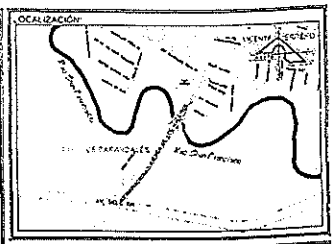


SIMBOLOGÍA

- LIMITE DE PROYECTO
- BANQUETAS EXISTENTES
- PARAMENTO EXISTENTE
- PAVIMENTO HIDRAULICO EXISTENTE
- CARPETA ASFALTICA EXISTENTE
- PUENTE VEHICULAR EXISTENTE CON CARPETA ASFALTICA
- REGISTRO CFE (REG-CFE)
- ALUMBRADO
- POSTES CFE
- POSTES TELMEX
- POZO DE VISITA EXISTENTE

La Dirección de Planeación y Proyectos solo autoriza el proyecto ejecutivo, no es responsable de la correcta ejecución de la obra. Este documento no tiene validez si no presenta las firmas de los responsables para su autorización, así como los sellos respectivos.

PRESIDENTE MUNICIPAL
M.P.P. Leonardo Montañez Castro
ENCARGADA DE DESPACHO DE LA SOPMA
Arq. Gloria Guadalupe Castillo González

| REV. | FECHA | OBSERVACIONES |
|---|---|---|

V° B° DE LA DEPENDENCIA

| RESP. DE PROY. EXTERNO | | LOGO EXTERNO |
|---|---|---|
| CED. PROFESIONAL | | |
| PROYECTO | REVISO | AUTORIZO |

Dirección de Planeación y Proyectos de Obra — Secretaría de Obras Públicas

| PROYECTO | COORDINADOR |
|---|---|
| ING. ALEJANDRO JAIME LEAL | ARQ. ALEJANDRO JAIME LEAL |
| JEFE DE DEP. | DIRECTOR |
| LIC. J. JESÚS PALAFOX GONZÁLEZ | M. en ARQ. JOSÉ LUIS JIMÉNEZ GARCÍA |


PROYECTO
CONSTRUCCION DE SOBRECARPETA ASFALTICA Y PAVIMENTO HIDRAULICO, AV. DE LOS MAESTROS CALZADA ORIENTE

UBICACIÓN
TRAMO ENTRE C. PROF. JOSE GUADALUPE PERALTA Y AV. SIGLO XXI

CONTENIDO
ESTADO ACTUAL Y LEVANTAMIENTO TOPOGRAFICO

| CLAVE | No. PLANO |
|---|---|
| EA 01 | 02 |
| FECHA: JULIO 2022 | ESCALA: INDICADA |
| ACOTACIÓN: METROS | No. EXP.: E-000-22 |

Aguascalientes
LA CIUDAD DE TU VIDA

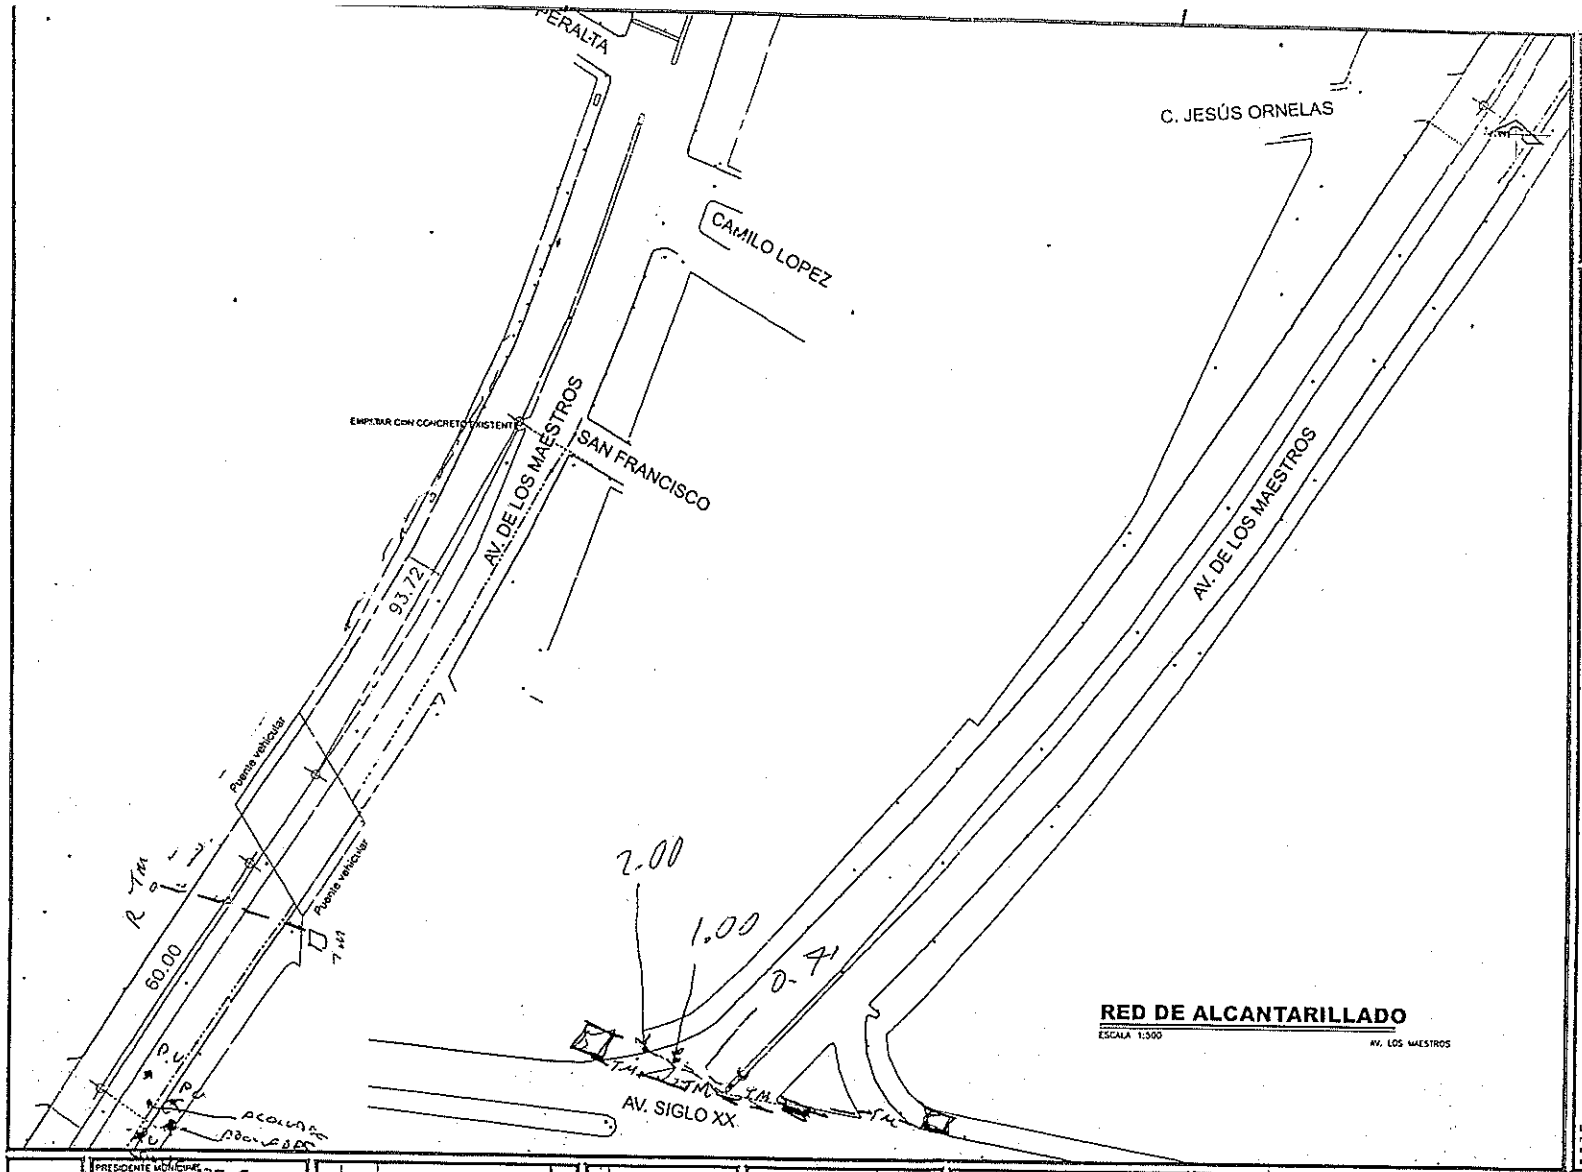



## RED DE ALCANTARILLADO

ESCALA 1:500

AV. LOS MAESTROS

LOCALIZACIÓN

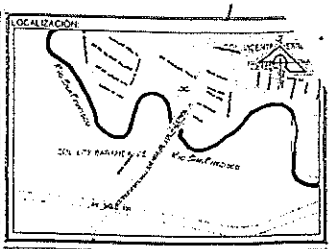

SIMBOLOGÍA

- LIMITE DE PROYECTO
- 100.00 / 98.00 — 2.00 — PROFUNDIDAD DE POZO
- 100.00 — 6 - 20" — RED ALCANTARILLADO

La Dirección de Planeación y Proyectos solo autoriza el proyecto ejecutivo, no es responsable de la correcta ejecución de la obra. Este documento no tiene validez si no presenta las firmas de los responsables para su autorización, así como los sellos respectivos.

PRESIDENTE MUNICIPAL
M.P.P. Leonardo Montañez Castro
ENCARGADA DE DESPACHO DE LA SOPMA
Arq. Gloria Guadalupe Castillo González

| REV. | FECHA | OBSERVACIONES |
|---|---|---|
| | | |

V°. Bo. DE LA DEPENDENCIA

| RESP. DE PROY. EXTERNO | | LOGO EXTERNO |
|---|---|---|
| CED. PROFESIONAL | | |
| PROYECTÓ | REVISÓ | AUTORIZÓ |

Dirección de Planeación y Proyectos de Obra — Secretaría de Obras Públicas

| PROYECTISTA | COORDINADOR TÉCNICO |
|---|---|
| ARQ. ALEJANDRO SOLÍS CONTRERAS | ARQ. ALEJANDRO JAIME LEAL |
| JEFE DE DEPARTAMENTO | DIRECCIÓN |
| PROJ. J. JESÚS PALACIOS GONZÁLEZ | M.en ARQ. JOSÉ LUIS MÉNDEZ GARCÍA |

| | |
|---|---|
| PROYECTO | CONSTRUCCIÓN DE SOBRECARPETA ASFÁLTICA Y PAVIMENTO HIDRÁULICO, AV. DE LOS MAESTROS CALZADA ORIENTE |
| UBICACIÓN | TRAMO ENTRE C. PROF. JOSE GUADALUPE PERALTA Y AV. SIGLO XXI |
| CONTENIDO | RED DE ALCANTARILLADO |

| CLAVE | No. PLANO |
|---|---|
| SAN 01 | 10 |
| FECHA: JULIO 2022 | ESCALA: INDICADA |
| ACOTACIÓN: METROS | No. EXP.: E-000-22 |

Aguascalientes
LA CIUDAD DE TU VIDA