Aguascalientes
LA CIUDAD DE TU VIDA

Dirección de Programación Presupuestal
Núm. Oficio AMPP/0669/22
Aguascalientes, Ags. 29 de Diciembre del 2022
Asunto: Validación de Expediente Técnico

C.P. SERGIO ARTURO LOZANO GONZÁLEZ
SECRETARIO DE FINANZAS MUNICIPALES
P R E S E N T E

Con fundamento en los artículos 17 fracción XV, 60 fracción XVI y 76 fracción VI del Reglamento del Sistema Integral de Desarrollo Municipal y del Instituto Municipal de Planeación y Evaluación de Aguascalientes, hago referencia al oficio SOPMA/3077/2022 recibido por este Instituto el día 29 de Diciembre del 2022 por parte de la Secretaría de Obras Públicas Municipales, mediante el cual remiten el expediente técnico original de la siguiente obra para su análisis, registro y priorización, conforme al Programa Anual de Obra Pública y Programas Sociales para el ejercicio presupuestal 2022:

DEPENDENCIA EJECUTORA:	SOPMA
NOMBRE DE LA OBRA O PROYECTO:	SOBRECARPETA ASFÁLTICA
UBICACIÓN:	CALLE VALLADOLID, TRAMO: DE CALLE PETRÓLEOS MEXICANOS A CALLE BENJAMÍN DE LA MORA, DEL CARMEN, AGUASCALIENTES, AGS.
FONDO DE INVERSIÓN:	FONDO DE INFRAESTRUCTURA SOCIAL MUNICIPAL Y DE LAS DEMARCACIONES TERRITORIALES DEL DISTRITO FEDERAL
IMPORTE:	$2,788,800.44 (ET FINAL)
No. DE OBRA:	2022-FISMDF-0135-04-1101
MODALIDAD DE EJECUCIÓN:	CONTRATO
EJE:	MUNICIPIO SOBRESALIENTE
ESTRATEGIA:	OBRA PÚBLICA INTELIGENTE
POLITICA:	5.8.1.REHABILITACIÓN Y MANTENIMIENTO VIALIDADES, CAMINOS, CALLES, ÁREAS DE TERRACERÍA Y CAUCES (C

Al respecto, hago de su conocimiento que dicho expediente ha sido analizado en su integración técnica y documental, con base en el artículo 168 fracción I del Reglamento de la Ley de Obras Públicas y Servicios Relacionados para el Estado de Aguascalientes y sus Municipios.

Asimismo, le comento que este Instituto valida dicha obra acorde a lo establecido en los artículos 14, 22 párrafo segundo y 23 de la Ley de Obras Públicas y Servicios Relacionados para el Estado de Aguascalientes y sus Municipios, la cual se encuentra alineada al Plan de Desarrollo Municipal vigente, para dar cumplimiento a las metas establecidas en el mismo, y a los Lineamientos Generales para la Operación de este Fondo de Inversión, toda vez que la misma cuente con la autorización del CODEMUN. De igual manera, se hace de su conocimiento que deberá cumplir con lo establecido en los ordenamientos aplicables en lo que respecta al ejercicio, control e información de los recursos de este Fondo. Cabe hacer mención que los recursos solicitados para este proyecto de inversión, estarán sujetos a la disponibilidad presupuestal para el presente ejercicio fiscal que determine la Secretaría a su digno cargo. Sin otro particular por el momento, le envío un cordial saludo.

A T E N T A M E N T E

ARQ. AUSTRIA GABRIELA DÁVILA DE LA LLAVE
DIRECTORA GENERAL DEL IMPLAN

SEDR/ CAAR / JDBC
C.c.p. I.C. ING. MIGUEL ÁNGEL HUIZAR BOTELLO .- Secretaría de Obras Públicas Municipales .Para su conocimiento.
C.c.p. Archivo.

Instituto Municipal de Planeación y Evaluación de Aguascalientes

Antonio Acevedo Escobedo 103 A. Col. Centro
Aguascalientes. Ags C.P. 20000

(449) 9101010 Ext. 3117

www.implanags.gob.mx

GOBIERNO MUNICIPAL DE AGUASCALIENTES

INSTITUTO MUNICIPAL DE PLANEACION

IMPLAN

ANÁLISIS INTEGRAL DE EXPEDIENTE TÉCNICO

No. DE OBRA (PAOP 2020):	2022-FISMDF-0135-04-1101	REGISTRO No.	300
OFICIO DE VALIDACIÓN:	AMPP/0669/22	FECHA RECIBIDO PARA REVISIÓN:	29 de Diciembre del 2022
PROGRAMA:	URBANIZACION MUNICIPAL	LOCALIDAD O COLONIA:	DEL CARMEN
SUB-PROGRAMA:		DELEGACIÓN:	Centro Oriente
DEPENDENCIA:	Secretaría de Obras Públicas Municipales	MOD. DE EJECUCIÓN:	CONTRATO
NOMBRE DE LA OBRA:	SOBRECARPETA ASFÁLTICA, CALLE VALLADOLID, TRAMO: DE CALLE PETRÓLEOS MEXICANOS A CALLE BENJAMÍN DE LA MORA		
FUENTE DE FINANCIAMIENTO:	FONDO DE INFRAESTRUCTURA SOCIAL MUNICIPAL Y DE LAS DEMARCACIONES TERRITORIALES DEL DISTRITO FEDERAL, FISMDF		
INVERSIÓN:	$2,788,800.44	CLASIFICACIÓN DE OBRA:	BIENES DE DOMINIO PUBLICA

TOTAL	FEDERAL	ESTATAL	MUNICIPAL	BENEFICIARIOS	OTROS	DIFERENCIA ENTRE MOD.
$2,788,800.44	$2,788,800.44	0.00	0.00	0.00	0.00	*$0,00*

TIPO DE EXPENDIENTE:	ET FINAL	AÑO: 2022	AÑO:	AÑO:
AVANCES:	Financiero: 100 %	Físico: 100 %		
FECHA DE INICIO:	14 de Diciembre del 2022	FECHA DE TÉRMINO:	28 de Diciembre del 2022	REGISTRO SIMA: 135

CHEK LIST DE LOS ANEXOS DEL EXPEDIENTE TÉCNICO

CÉDULA DE REGISTRO DE OBRA	✓
DICTAMEN DE FACTIBILIDAD	✓
MEMORIA DESCRIPTIVA	✓
PRESUPUESTO BASE	✓
FACTIBILIDAD VERIFICADA EN CAMPO	✓
CROQUIS DE UBICACIÓN (MACRO)	✓
CROQUIS DE UBICACIÓN (MACRO)	✓
PROGRAMA DE OBRA Y MONTOS MENSUALES	✓
PLANOS O ESTUDIOS TÉCNICOS	✓
PADRÓN DE BENEFICIARIOS	N/A
ACTA DE ACEPTACIÓN DEL PROYECTO	N/A
DICTAMEN DE IMPACTO AMBIENTAL	N/A
CONVENIO DE CONCERTACIÓN	N/A
ACTA CONSTITUTIVA	N/A

METAS		BENEFICIARIOS		PERIODO DE EJECUCION		OBRA PROPUESTA		CLAVE SISCO
UNIDAD DE MEDIDA	CANT	TIPO DE BENEFICIARIOS	CANTIDAD	FECHA DE INICIO	FECHA DE TERMINO	CONCEPTO	JORNALES A GENERAR	
M2	4473.16	Personas	120	2022-12-14	2022-12-28	Sobrecarpeta Asfáltica	7250	2394

INCLUIDO EN PLAN DE DESARROLLO MUNICIPAL Y EL PROGRAMA ANUAL DE OBRA PÚBLICA

OBSERVACIONES:

SIN OBSERVACIONES

RECIBIO: ING. JOSÉ DAVID BURGUETE CLAUSTRO
Analista de Programación e Inversión de Obra Pública

29 de Diciembre del 2022
Fecha de validación

29 de Diciembre del 2022
Fecha de validación Expediente

PROCEDE Si ✓ No

H. AYUNTAMIENTO CONSTITUCIONAL DEL MUNICIPIO DE AGUASCALIENTES 2021-2024

AYUNTAMIENTO DE AGUASCALIENTES

CEDULA DE REGISTRO POR OBRA

Aguascalientes
TU CIUDAD DE TU VIDA

050400-001E00E05-05-2-2-1-00-1-E-0510-0-17-0135-21-2502-6144

2022-FISMDF-0135-0411102-072	Obra **CONSTRUCCIÓN DE SOBRECARPETA ASFÁLTICA CALLE VALLADOLID**
Tipo DEFINITIVO 1 2022 Folio SISCO **2394**	Ubic. TRAMO: DE CALLE PETRÓLEOS MEXICANOS A CALLE BENJAMÍN DE LA MORA, COLONIA DEL CARMEN Y BARRIO DE GUADALUPE, AGUASCALIENTES Mpio.

Ent. Ejecutora : **050400001E00E05**

Eje: **05**	MUNICIPIO SOBRESALIENTE
Finalidad: **2**	DESARROLLO SOCIAL
Función: **2**	VIVIENDA Y SERVICIOS A LA COMUNIDAD
Subfunción: **1**	URBANIZACIÓN
Tema: **00**	SIN TEMA
Cuenta del Gasto **1**	GASTO PROGRAMABLE
Clasif. Programatica: **E**	PRESTACIÓN DE SERVICIOS PÚBLICOS
Programa: **0510**	Movilidad Urbana
SubPrograma: **0**	SUBPROGRAMA GENÉRICO
Proyecto: **17**	
Tipo de Gasto: **21**	GASTO INVERSIÓN / OBRA PÚBLICA

I N V E R S I O N 2022

Municipal	2502	FONDO PARA LA INFRAESTRUCTURA SOCIAL MUNICIPAL Y DE LAS DEMARCACIONES TERRITORIALES DEL DISTRITO FEDERAL 2022	$2,788,800.44

Folio SIMA 135 Total $2,788,800.44

M E T A S

Unidad de Medida	Cantidad	Descripción
M2	4473.16	SOBRECARPETA ASFÁLTICA CONSTRUCCIÓN DE SOBRECARPETA ASFÁLTICA CALLE VALLADOLID

Inversión Ejercida Total al	31 de Diciembre de 2021	$0.00
Avance Fisico Acumulado al	31 de Diciembre de 2021	
Avance Fisico Acumulado Programado al	31 de Diciembre de 2022	

Fecha de Inicio 14 Dic 2022 Fecha de Terminación 28 Dic 2022

Jornales a Generar en 2022 7250

Modalidad de ejecución CONTRATO
Clasificación de la Obra Bienes de Dominio Público
Registro del Patrimonio: Obras del dominio público

OBRAS PÚBLICAS

Av. Aguascalientes Sur No. 2615
Fracc. Jardines de las Fuentes,
Aguascalientes, Ags. C.P. 20278

(449) 9 78 92 01, 06, 09

www.ags.gob.mx

H. AYUNTAMIENTO CONSTITUCIONAL DEL MUNICIPIO DE AGUASCALIENTES 2021-2024

GENERALES

Nombre del Proyecto : CONSTRUCCIÓN DE SOBRECARPETA ASFÁLTICA CALLE VALLADOLID

TRAMO: DE CALLE PETRÓLEOS MEXICANOS A CALLE BENJAMÍN DE LA MORA, COLONIA DEL CARMEN Y BARRIO DE GUADALUPE, AGUASCALIENTES Mpio.

Programa : 04 URBANIZACION MUNICIPAL

Subprograma : 11 Calles y caminos (2.- Construcción; 02- Concreto Asfáltico)

Clave del Municipio : AGUASCALIENTES

Localidad :

Barrio, Colonia o Ejido : AGUASCALIENTES Mpio.

Tipo de Obra :

DESCRIPCIÓN DEL PROYECTO:

CONSTRUCCIÓN DE SOBRECARPETA ASFÁLTICA CALLE VALLADOLID

PRELIMINARES Y DEMOLICIONES 2,772.15 M2
BACHEO PROFUNDO 56.40 M3
SOBRECARPETA ASFÁLTICA 4,473.16 M2
OBRA COMPLEMENTARIA 1.00 OBRA
LIMPIEZAS 2,772.15 M2
GUARNICIONES 25.00 ML
SEÑALIZACIÓN HORIZONTAL Y VERTICAL 1.00 OBRA

Beneficiarios (No. y Tipo) :

120	PERSONAS

Hombres: 60 Mujeres: 60

OBRAS PÚBLICAS

Av. Aguascalientes Sur No. 2615
Fracc. Jardines de las Fuentes,
Aguascalientes, Ags. C.P. 20278

(449) 9 78 92 01, 06, 09

www.ags.gob.mx

Los abajo firmantes, hacen constar que el presente proyecto :

CONSTRUCCIÓN DE SOBRECARPETA ASFÁLTICA CALLE VALLADOLID

TRAMO: DE CALLE PETRÓLEOS MEXICANOS A CALLE BENJAMÍN DE LA MORA, COLONIA DEL CARMEN Y BARRIO DE GUADALUPE, AGUASCALIENTES Mpio.

cumple con los Requisitos y Normas Técnicas establecidas por la Dependencia Normativa, por lo que es viable su ejecución. Comprometiéndose la misma a proporcionar la supervisión y asistencia técnica necesaria durante el proceso administrativo.

Por la Dependencia Ejecutora

Ing. Miguel Angel Huizar Botello
Secretario de Obras Públicas

Lic. Jaime Gallo Camacho
Secretario de Desarrollo Urbano

LUGAR :AGUASCALIENTES, AGS.

Av. Aguascalientes Sur No. 2615
Fracc. Jardines de las Fuentes,
Aguascalientes, Ags. C.P. 20278

(449) 9 78 92 01, 06, 09

www.ags.gob.mx

MUNICIPIO: AGUASCALIENTES

LOCALIZACION: TRAMO: DE CALLE PETRÓLEOS MEXICANOS A CALLE BENJAMÍN DE LA MORA, COLONIA DEL CARMEN Y BARRIO DE GUADALUPE, AGUASCALIENTES Mpio.

PROGRAMA: URBANIZACION MUNICIPAL

SUBPROGRAMA: Calles y caminos (2.- Construcción; 02- Concreto Asfáltico)

OBRA A REALIZAR: CONSTRUCCIÓN DE SOBRECARPETA ASFÁLTICA CALLE VALLADOLID

DEPENDENCIA EJECUTORA: SECRETARÍA DE OBRAS PUBLICAS DEL MUNICIPIO DE AGUASCALIENTES

FORMA DE EJECUCION: CONTRATO

TIPO DE OBRA PROPUESTA:

CONDICIONES ACTUALES DE LA OBRA:

CONSTRUCCIÓN DE SOBRECARPETA ASFÁLTICA CALLE VALLADOLID

CARACTERISTICAS DE LA OBRA: Pesimo

FACTIBILIDAD DE LA OBRA:

ESTA OBRA SE REQUIERE PARA EL BENEFICIO DE LA CIUDADANÍA

PROCEDE: SI [X] NO [ ]

REVISÓ: Jefa del Departamento de Expedientes Tecnicos y Costos

NOMBRE: Arq. Blanca Margarita Martinez Amador

FIRMA:

FECHA:

SECRETARÍA DE OBRAS PÚBLICAS

No. Folio SISCO 2394

H. AYUNTAMIENTO CONSTITUCIONAL DEL MUNICIPIO DE AGUASCALIENTES 2021-2024

Aguascalientes
LA CIUDAD DE TU VIDA

MACRO LOCALIZACIÓN

APROBACIÓN	**2022-FISMDF-0135-0411102-072**
NOMBRE DE LA OBRA:	**CONSTRUCCIÓN DE SOBRECARPETA ASFÁLTICA CALLE VALLADOLID**
UBICACIÓN:	**TRAMO: DE CALLE PETRÓLEOS MEXICANOS A CALLE BENJAMÍN DE LA MORA, COLONIA DEL CARMEN Y BARRIO DE GUADALUPE, AGUASCALIENTES Mpio.**
PROGRAMA:	**04 URBANIZACIÓN MUNICIPAL**



I.C. LAURA CECILIA MARTÍNEZ ALBA
RESIDENTE DE SUPERVISIÓN

H. AYUNTAMIENTO CONSTITUCIONAL DEL MUNICIPIO DE AGUASCALIENTES 2021 2024

Aguascalientes
LA CIUDAD DE TU VIDA

MICRO LOCALIZACIÓN

APROBACIÓN	**2022-FISMDF-0135-0411102-072**
NOMBRE DE LA OBRA:	**CONSTRUCCIÓN DE SOBRECARPETA ASFÁLTICA CALLE VALLADOLID**
UBICACIÓN:	**TRAMO: DE CALLE PETRÓLEOS MEXICANOS A CALLE BENJAMÍN DE LA MORA, COLONIA DEL CARMEN Y BARRIO DE GUADALUPE, AGUASCALIENTES Mpio.**
PROGRAMA:	**04 URBANIZACIÓN MUNICIPAL**



I.C. LAURA CECILIA MARTÍNEZ ALBA
RESIDENTE DE SUPERVISIÓN

PROGRAMA DE OBRA DEFINITIVO

No. DE CONTRATO : FISMDF-0135-2022

PROGRAMA: 04 URBANIZACIÓN MUNICIPAL

No. OBRA Y NOMBRE DE LA OBRA: 2022-FISMDF-0135-0411102-072 CONSTRUCCIÓN DE SOBRECARPETA ASFÁLTICA CALLE VALLADOLID, TRAMO: DE CALLE PETRÓLEOS MEXICANOS A CALLE BENJAMÍN DE LA MORA, COLONIA DEL CARMEN Y BARRIO DE GUADALUPE, AGUASCALIENTES Mpio.

INICIO VIGENTE: 14-diciembre-22

TERMINO REAL: 28-diciembre-22

RECURSO 2022

CONCEPTO			2022																PONDERACIÓN %	
			OCTUBRE	NOVIEMBRE	DICIEMBRE	ENERO	FEBRERO	MARZO	ABRIL	MAYO	JUNIO	JULIO	AGOSTO	SEPTIEMBRE	OCTUBRE	NOVIEMBRE	DICIEMBRE	ENERO	FINANCIERO	FÍSICO
DESCRIPCION	INVERSION																		%	%
CONSTRUCCIÓN DE SOBRECARPETA ASFÁLTICA CALLE VALLADOLID																	14	28		
TRAMO: DE CALLE PETRÓLEOS MEXICANOS A CALLE BENJAMIN DE LA MORA, COLONIA DEL CARMEN Y BARRIO DE GUADALUPE																				
PRELIMINARES Y DEMOLICIONES	$ 202,339.29	100															100		8.42	10.00
BACHEO PROFUNDO	$ 65,639.45	100															50	50	2.73	20.00
SOBRE CARPETA ASFÁLTICA	$ 1,687,846.84	100															100		70.23	10.00
OBRA COMPLEMENTARIA	$ 78,907.74	100															50	50	3.28	20.00
LIMPIEZAS	$ 12,058.85	100															100		0.50	10.00
GUARNICIONES	$ 6,25 .71	100															50	50	0.26	20.00
SEÑALIZACIÓN HORIZONTAL	$ 351,094.43	100															100		14.60	10.00
SUBTOTAL, SIN IVA	$ 2,404,138.31		0 0 0 0	0 0 0 0	0 0 0 0	0 0 0 0	0 0 0 0	0 0 0 0	0 0 0 0	0 0 0 0	0 0 0 0	0 0 0 0	0 0 0 0	0 0 0 0	0 0 0 0	0 0 0 0	2 4	0 0 0 0		
AVANCE SEMANAL %			0% 0% 0% 0%	0% 0% 0% 0%	0% 0% 0% 0%	0% 0% 0% 0%	0% 0% 0% 0%	0% 0% 0% 0%	0% 0% 0% 0%	0% 0% 0% 0%	0% 0% 0% 0%	0% 0% 0% 0%	0% 0% 0% 0%	0% 0% 0% 0%	0% 0% 0% 0%	0% 0% 0% 0%	20% 40%	100% 100% 100% 100%		
AVANCE SEMANAL ACUMULADO %			0% 0% 0% 0%	0% 0% 0% 0%	0% 0% 0% 0%	0% 0% 0% 0%	0% 0% 0% 0%	0% 0% 0% 0%	0% 0% 0% 0%	0% 0% 0% 0%	0% 0% 0% 0%	0% 0% 0% 0%	0% 0% 0% 0%	0% 0% 0% 0%	0% 0% 0% 0%	0% 0% 0% 0%	20% 40%	100% 100% 100% 100%	100.00	100.0
EJERCIDO SEMANAL $																	226,159.02 1,782,146.29	395,733.01	$ 2,404,138.31	
EJERCIDO MENSUAL $			$0.00	$0.00	$0.00	$0.00	$0.00	$0.00	$0.00	$0.00	$0.00	$0.00	$0.00	$0.00	$0.00	$0.00	$2,404,138.31	$0.00	$ 384,662.13	IVA 1
EJERCIDO MENSUAL ACUMULADO $			0.00	0.00	0.00	0.00	0.00	0.00	0.00	0.00	0.00	0.00	0.00	0.00	0.00	0.00	2,404,138.31	2,404,138.31		
EJERCIDO SEMANAL %			0% 0% 0% 0%	0% 0% 0% 0%	0% 0% 0% 0%	0% 0% 0% 0%	0% 0% 0% 0%	0% 0% 0% 0%	0% 0% 0% 0%	0% 0% 0% 0%	0% 0% 0% 0%	0% 0% 0% 0%	0% 0% 0% 0%	0% 0% 0% 0%	0% 0% 0% 0%	0% 0% 0% 0%	0% 0%	0% 0% 0% 0%		
EJERCIDO MENSUAL %			0%	0%	0%	0%	0%	0%	0%	0%	0%	0%	0%	0%	0%	0%	100%	0%	GRAN TOTAL EJERCIDO	
EJERCIDO MENSUAL ACUMULADO %			0%	0%	0%	0%	0%	0%	0%	0%	0%	0%	0%	0%	0%	0%	100%	100%	$	2,788,800.4

ING. LAURA CECILIA MARTÍNEZ ALBA
RESIDENTE DE SUPERVISIÓN

PRESIDENCIA MUNICIPAL DE AGUASCALIENTES

FACTIBILIDAD VERIFICADA EN CAMPO

GENERALES

LOCALIDAD: TRAMO: DE CALLE PETRÓLEOS MEXICANOS A CALLE BENJAMÍN DE LA MORA, COLONIA DEL CARMEN Y BARRIO DE GUADALUPE

MUNICIPIO: AGUASCALIENTES

PROGRAMA: 04 URBANIZACIÓN MUNICIPAL

SUB-PROGRAMA: 11 Calles y caminos

OBRA A REALIZARSE: CONSTRUCCIÓN DE SOBRECARPETA ASFÁLTICA CALLE VALLADOLID

DEPENDENCIA EJECUTORA: SECRETARÍA DE OBRAS PÚBLICAS MUNICIPALES (S.O.P.M.A)

FORMACIÓN DE EJECUCION: CONTRATO

TIPO DE OBRA PROPUESTA

NUEVA CREACIÓN	X	CONSOLIDACIÓN	
COMPLEMENTARIA		AMPLIACIÓN	
REHABILITACIÓN		EQUIPAMIENTO	

CARACTERÍSTICAS DE LA OBRA:

CONSTRUCCIÓN DE SOBRECARPETA ASFÁLTICA CALLE VALLADOLID

CONDICIONES ACTUALES DE LA OBRA:

BUEN ESTADO	X	REGULAR		PESIMO ESTADO	

FACTIBILIDAD DE LA OBRA:

SE HACE ENTREGA DE LA OBRA DE ACUERDO A LAS METAS INICIALES, ATENDIENDO EL CONTRATISTA LOS DETALLES MARCADOS PREVIOS A LA ENTREGA.

PROCEDE SI X NO

Aguascalientes
LA CIUDAD DE TU VIDA

I.C. LAURA CECILIA MARTINEZ ALBA
SUPERVISOR

PRESIDENCIA MUNICIPAL DE AGUASCALIENTES

FACTIBILIDAD VERIFICADA EN CAMPO

GENERALES

EJERCICIO: 2022 APROBACION No: 2022-FISMDF-0135-0411102-072

LOCALIDAD: TRAMO: DE CALLE PETRÓLEOS MEXICANOS A CALLE BENJAMÍN DE LA MORA, COLONIA DEL CARMEN Y BARRIO DE GUADALUPE, AGUASCALIENTES Mpio.

MUNICIPIO: AGUASCALIENTES, Mpio.

TIPO DE INVERSION: FONDO PARA LA INFRAESTRUCTURA SOCIAL MUNICIPAL Y DE LAS DEMARCACIONES TERRITORIALES DEL DISTRITO FEDERAL

PROGRAMA: 04 URBANIZACIÓN MUNICIPAL

SUB-PROGRAMA: 11 Calles y caminos

OBRA A REALIZARSE: CONSTRUCCIÓN DE SOBRECARPETA ASFÁLTICA CALLE VALLADOLID

DEPENDENCIA EJECUTORA: SECRETARÍA DE OBRAS PÚBLICAS MUNICIPALES (S.O.P.M.A)

FORMACIÓN DE EJECUCION: CONTRATO NO. DE CONTRATO: FISMDF-0135-2022

NOMBRE CONTRATISTA: ODZ ARQUITECTURA Y CONSTRUCCION S.A. DE C.V.

REPRESENTANTE: ARQ. OSCAR MIGUEL ORDAZ CARRILLO

MONTO CONT. ORIGEN $2,694,076.22 ANTICIPO: $1,347,038.11 PLAZO 15 DÍAS

1A AMPLIACION $: $ 94,724.22 1 AMPL DIAS

2A AMPLIACION $: 2 AMPL DIAS

FIRMA CONTRATO: 02/12/2022

INICIO CONT: dd/mm/aa 03/12/2022 TERMINO CONT: 17/12/2022

INICIO REAL: dd/mm/aa 14/12/2022 TERMINO REAL: 28/12/2022

TIPO DE OBRA PROPUESTA

NUEVA CREACIÓN	X	CONSOLIDACIÓN	
COMPLEMENTARIA		AMPLIACIÓN	
REHABILITACIÓN		EQUIPAMIENTO	

CARACTERÍSTICAS DE LA OBRA:

FRESADO DE CARPETA EXISTENTE

BACHEO PROFUNDO Y RENIVELACIONES

COLOCACIÓN DE SOBRE CARPETA ASFÁLTICA

SUMINISTRO Y COLOCACIÓN DE PINTURA Y VIALETAS

CONDICIONES ACTUALES DE LA OBRA: (SELECCIONAR UNO OBLIGATORIO)

BUEN ESTADO X REGULAR PESIMO ESTADO

FACTIBILIDAD DE LA OBRA: (CONDICIONES ACTUALES DE LA OBRA)

ESTA OBRA SE ENCUENTRA EN CONDICIONES PARA OPERARSE

PROCEDE: SI: X NO:
MARQUE SOLO UNA

I.C. LAURA CECILIA MARTÍNEZ ALBA
SUPERVISOR

H. AYUNTAMIENTO CONSTITUCIONAL DEL MUNICIPIO DE AGUASCALIENTES 2021-2024

PRESUPUESTO MODIFICADO

Aguascalientes

Obra: **CONSTRUCCIÓN DE SOBRECARPETA ASFÁLTICA CALLE VALLADOLID**

Ubicación: **TRAMO: DE CALLE PETRÓLEOS MEXICANOS A CALLE BENJAMÍN DE LA MORA, COLONIA DEL CARMEN Y BARRIO DE GUADALUPE, AGUASCALIENTES Mpio.**

Contratista: **ODZ ARQUITECTURA Y CONSTRUCCION S.A. DE C.V. (349)**

No.	Concepto	Unidad	Cantidad	Precio Unitario	Importe Total
GRUPO: **PRELIMINARES**					
PARTIDA: **PRELIMINARES Y DEMOLICIONES**					
1	LIMPIA, TRAZO Y NIVELACION EN PAVIMENTOS, CALLES Y VIALIDADES CON EQUIPO TOPOGRAFICO, INCLUYE: EJES, BANCO DE NIVEL, RENIVELACIONES LAS VECES NECESARIAS, CORRECCION DE RASANTE A PUNTOS OBLIGADOS (AUTORIZADOS POR LA SUPERVISION), ESTACAS, VARILLAS, MANO DE OBRA CALIFICADA, HERRAMIENTA NECESARIA, EQUIPO DE PRECISION CALIBRADO, TRABAJO TERMINADO.P.U.O.T.	M2	2772.15	$5.69	$15,773.53
2	SONDEO A MANO O A MAQUINA PARA LOCALIZACION DE TUBERIAS CUALQUIER PROFUNDIDAD Y MATERIAL PARA VERIFICAR LA CALIDAD DE LAS INSTALACIONES HIDRAULICO SANITARIAS CUIDANDO NO DAÑARLAS PARA NO INTERFERIR EN LOS SERVICIOS, INCLUYE: EXCAVACION, EQUIPO, MANO DE OBRA, REPORTE A LA SUPERVISION, RELLENOS, COMPACTACIONES, TRABAJO TERMINADO.	SONDE	6	$1,678.06	$10,068.36
3	CORTE CON DISCO DIAMANTADO DE 14" EN PISOS DE CONCRETO ASFALTICO DE HASTA 8.00 cm. DE PROFUNDIDAD. INCLUYE: TRAZO, EQUIPO Y OPERACION, LIMPIEZAS.	ML	13.5	$19.33	$260.95
4	DEMOLICION PARCIAL DE PAVIMENTO HIDRAULICO Y/O ASFALTICO DE HASTA 15 CM. DE ESPESOR PROMEDIO EN PAVIMENTOS Y (BANQUETAS, LOSAS DIAMANTE Y CAJAS DE VALVULAS, TOPES) CON O SIN ARMADO DE ACERO, SIN RECUPERACION, MUROS, MOJONERAS, ANCLAJES, ETC, DE FORMA MANUAL Y MECANICA, INCLUYE ACARREO DE MATERIAL AL LUGAR DE ACOPIO, HERRAMIENTA NECESARIA Y TODO LO NECESARIO PARA SU CORRECTA EJECUCION, LIMPIEZA, TRABAJO TERMINADO	M3	3.37	$261.99	$882.91
5	FRESADO UNIFORME DE LA SUPERFICIE DE RODADURA EN PAVIMENTO DE CONCRETO ASFALTICO 3-7 CM (5 cm de espesor promedio) MEDIANTE FRESADORA EN FRIO COMPACTA, EQUIPADA CON BANDA TRANSPORTADORA PARA CARGA DIRECTA SOBRE CAMION DE VOLTEO, INCLUYE: TRAMO DE PRUEBA AL INICIO DEL FRESADO PARA AUTORIZACION DE SUPERVISION (SUPERFICIE FRESADA UNIFORME Y SIN PROTUBERANCIAS NI ONDEOS), ACARREOS LOCALES, CARGA Y ACARREO A KM SUBSECUENTES (11 A 15 KM APROX) DE MATERIAL PRODUCTO DEL FRESADO DE CARPETA ASFALTICA EL TRASLADO SERA A PARQUE DE MAQUINARIA DE LA SOPMA, PIEZAS DE DESGASTE, COMBUSTIBLES, CONSUMIBLES, MANO DE OBRA, CUALQUIER VOLUMEN Y AREA,EQUIPO NECESARIO, LIMPIEZA FINA Y GRUESA, TRABAJO TERMINADO.	M3	138.6	$1,211.19	$167,870.93
7	DEMOLICION CONTROLADA DE CONCRETO HIDRAULICO EN DENTELLONES Y GUARNICIONES DE 15 x 20 x 40 CM. DE FORMA MANUAL Y MECÁNICA, INCLUYE: CORTES CON DISCO, ACARREO DEL MATERIAL AL LUGAR DE ACOPIO PARA SU CARGA Y ACARREO FUERA DE LA OBRA.	ML	25	$290.67	$7,266.75
8	CARGA MECANICA Y ACARREO DE MATERIAL PRODUCTO DE EXCAVACION Y DEMOLICION EN CAMION DE VOLTEO AL 1er. KM, VOLUMEN MEDIDO COMPACTO.	M3	4.12	$52.39	$215.85
				Totales por Partida	**$202,339.29**
				Totales por Grupo	**$202,339.29**

Obra: **CONSTRUCCIÓN DE SOBRECARPETA ASFÁLTICA CALLE VALLADOLID**

Ubicación: **TRAMO: DE CALLE PETRÓLEOS MEXICANOS A CALLE BENJAMÍN DE LA MORA, COLONIA DEL CARMEN Y BARRIO DE GUADALUPE, AGUASCALIENTES Mpio.**

Contratista: **ODZ ARQUITECTURA Y CONSTRUCCION S.A. DE C.V. (349)**

No.	Concepto	Unidad	Cantidad	Precio Unitario	Importe Total
	GRUPO: **SOBRECARPETA ASFALTICA**				
	PARTIDA: **BACHEO PROFUNDO**				
10	BACHEO PROFUNDO AISLADO UTILIZANDO MATERIAL CALIDAD BASE HIDRAULICA PARA MAS DE UN MILLON DE EJES EQUIVALENTES DEL BANCO QUE ELIJA EL CONTRATISTA, INCISO N.CSV.CAR.1.02.004/03 DE LAS NORMAS DE CONSTRUCCION DE CARR. DE LA SCT, INCLUYE: PREPARACION, PERFILADO, MATERIALES, MANO DE OBRA, HERRAMIENTA MENOR Y EQUIPO NECESARIO QUE SE REQUIERA PARA LOGRAR LA COMPACTACION DE 100% PVSM, ACARREOS DENTRO Y FUERA DE LA OBRA, PREPARACION DE MATERIAL, HUMEDECIDO, NIVELADO, TRASLADO DE UN PUNTO A OTRO DENTRO DE LA OBRA, EN CUALQUIER VOLUMEN, MOVIMIENTO DE MAQUINARIA P.U.O.T	M3	56.4	$1,163.82	$65,639.45
				Totales por Partida	**$65,639.45**
	PARTIDA: **SOBRE CARPETA ASFALTICA**				
13	PREPARACIÓN DE LA SUPERFICIE DE CONTACTO EN LOS EXTREMOS DONDE LA PERFILADORA NO ALCANCE POR LÍMITES CON LA GUARNICIÓN, CON UN RASPADO SUPERFICIAL CON RETROEXCAVADORA, ELIMINANDO TECATAS QUE HAYAN QUEDADO PARA RENIVELADO, BARRIDOS ENTRE PASADA DE MOTOCONFORMADORA Y EN REMATES DE EMPATES A DETALLE A MANO, INCLUYE: RETIRO DE MATERIAL FUERA DE LA OBRA A TIRADERO OFICIAL INDICADO.	M2	132	$193.78	$25,578.96
14	RENIVELACIONES CON CONCRETO ASFALTICO MEZCLA EN PLANTA EN CALIENTE ASFALTO MODIFICADO CON POLIMERO TIPO I, CUMPLIENDO LAS NORMAS SCT REFERENTES DE CONSTRUCCCION Y CONSERVACION, GRANULOMETRIA DENSA 3/4" A FINOS, MEDIDO COMPACTO AL NOVENTA Y CINCO PORCIENTO (95%), INCLUYE CARGA Y ACARREO EN TRAMOS AISLADOS, MATERIALES, MANO DE OBRA, ACARREO DE MATERIALES, Y MAQUINARIA Y EQUIPO AL SIGUIENTE PUNTO EN CUALQUIER VOLUEN, PERFILADO, LIMPIEZA DE HUESO Y GRAVA SUELTA, TRABAJO TERMINADO P.U.O.T	M3	67.5	$5,776.57	$389,918.47
17	RIEGO DE LIGA CON EMULSION DE ROMPIMIENTO RAPIDO (ECR-65 %), INCLUYE, SUMINISTRO, ALMACENAMIENTO, CALENTAMIENTO, Y APLICACION DE LA EMULSION CON EQUIPO ESPECIAL PARA ESA ACTIVIDAD, ESPREAS O BACHADOR LIMPIAS Y ALINEADAS, CONTROL DE CALIDAD A CADA DOS REMESAS EN OBRA (INDEPENDIENTEMENTE DE LA CANTIDAD A UTILIZAR) EN LA PETROLIZADORA, A RAZON DE 0.8 LT DE EMULSION POR M2, O LO QUE INDIQUE EL LABORATORIO DE CALIDAD DEL CONTRATISTA, NO SE ACEPTAN "IMPREGNALIGA", TRABAJO TERMINADO, P.U.O.T.	M2	2772.15	$17.87	$49,538.32
18	SUMINISTRO Y COLOCACION DE CONCRETO ASFALTICO EN CALIENTE DE GRANULOMETRIA DENSA ELABORADA CON ASFALTO MODIFICADO TIPO I, AGREGADO 3/4" A FINOS, DE 5 CM DE ESPESOR, FORMADA Y COMPACTADO AL 95%, INCLUYE MATERIALES, QUE CUMPLAN LA NORMATIVA SCT-N-CMT-04-04, SCT-CMT-4-05-002, SCT-CMT-4-05-003, SCT-CMT-4-05-004, SCT-CTR-CAR-1-04-006-14 APLICADAS AL DIA DE HOY, DISEÑO MARSHALL (DEVERÁ SER AUTORIZADO POR EL LABORATORIO DE CALIDAD DE SOPMA AL MENOS 3 DIAS ANTES DE INICIO DE TENDIDO DE LA MEZCLA ASFALTICA), INCUYE: TRAMO DE PRUEBA AL INICIO PARA REVISION Y AUTORIZACION DEL ESPESOR POR PARTE DEL SUPERVISOR, EL CONTRATISTA DEBERÁ PREVEER EL SUMINISTRO Y TIEMPOS MUERTOS POR MOVIMIENTOS DEL TREN DE MAQUINAS DE TRABAJO EN TRAMOS AISLADOS. TRABAJO TERMINADO P.U.O.T. Y LIMPIEZAS DE GRANZON Y HUESO LATERAL.	M2	173.1565271839	$272.60	$1,219,382.47

PRESUPUESTO MODIFICADO

Obra: **CONSTRUCCIÓN DE SOBRECARPETA ASFÁLTICA CALLE VALLADOLID**

Ubicación: **TRAMO: DE CALLE PETRÓLEOS MEXICANOS A CALLE BENJAMÍN DE LA MORA, COLONIA DEL CARMEN Y BARRIO DE GUADALUPE, AGUASCALIENTES Mpio.**

Contratista: **ODZ ARQUITECTURA Y CONSTRUCCION S.A. DE C.V. (349)**

No.	Concepto	Unidad	Cantidad	Precio Unitario	Importe Total
	GRUPO: **SOBRECARPETA ASFALTICA**				
	PARTIDA: **SOBRE CARPETA ASFALTICA**				
19	COMPACTACION SOBRE MORTERO ASFALTICO TENDIDO EN APROCHES CON GUARNICIONES CON EQUIPO LIGERO (PLANCHITA), INCLUYE: MANO DE OBRA Y EQUIPO, TRABAJO TERMINADO.	M2	298.4	$11.49	$3,428.62
			Totales por Partida		**$1,687,846.84**
	PARTIDA: **OBRA COMPLEMENTARIA**				
20	RE NIVELACIÓN DE POZO DE VISITA HASTA 30 cm DE ALTURA. INCLUYE: RETIRO SIN RECUPERACIÓN DE BROCAL EXISTENTE, DEMOLICIONES, NIVELADO CON TABIQUE ROJO RECOCIDO 7X14X28, ASENTADO CON MORTERO CEMENTO-ARENA 1:3 DE 28 cm DE ESPESOR, APLANADO CON MORTERO CEMENTO-ARENA 1:3 , PLOMEADO, NIVELADO, DEMOLICIONES, CARGAS Y ACARREOS DENTRO DE LA OBRA, LIMPIEZAS Y TODO LO NECESARIO PARA SU CORRECTA EJECUCIÓN DEL CONCEPTO.	PZA	6	$2,854.62	$17,127.72
21	CONSTRUCCION DE LOSA DE DIAMANTE DE CONCRETO MR= 45 , T.M.A. DE 3/4" (19MM), GRAVA TRITURADA, REVENIMIENTO DE 8+-2.5CM CM, FRAGUADO RAPIDOA A 3 DIAS, DE 25 CM DE ESPESOR, EN POZO DE VISITA, Y 1.50 M POR LADO, INCLUYE: SUMINISTRO DE MATERIALES, ESPUMA DE POLIURETANO DE ALTA DENSIDAD EN TODO EL PERIMETRO EXTERIOR DE 1/2" ASI COMO DE LAS JUNTAS DIAGONALES PARA FORMAR 4 PARTES, BROCAL Y TAPA DE Fo. Fo. TIPO PESADO, (165 KG), CIMBRADO, COLADO, VIBRADO, DESCIMBRADO, CURADO CON MEMBRANA QUIMICA BASE AGUA, APLANADO FINO EN RECEPCION DE BROCAL, CORTES CON CORTADORA DE DISCO DE 5 CM ENTRE JUNTAS DIAGONALES FORMADO 8 PIEZAS Y SELLADO DE JUNTAS Y CORTES CON MATERIAL PREFORMADO Y SELLADOR AUTONIVELANTE, MANO DE OBRA, ACARREOS DE MATERIAL DENTRO Y FUERA DE LA OBRA, TRABAJO TERMINADO. P.U.O.T.	PZA	6	$7,531.42	$45,188.52
24	LIMPIEZA Y DESASOLVE DE POZOS DE VISITA Y LINEAS DE ALCANTARILLADO EXISTENTE CON CAMION TIPO VACTOR. INCLUYE: RESANE INTERIOR DEL POZO Y REMTE DE POZO CO TUBO CON SELLADOR, FESTER Y MORTERO 1:3, MANO DE OBRA, SUMINISTRO DE AGUA EN PIPA, HERRAMIENTAS Y EQUIPO PARA SU CORRECTA EJECUCION, LIMPIEZAS, RENTA DE CAMION VACTOR HASTA LA CORRECTA LIMPIEZA DE LAS LINEAS EXISTENTES DE POZO A POZO, ASI COMO EL TRASLADO DE LOS DESECHOS HASTA TIRADERO AUTORIZADO MEDIDO POZO A POZO.	LOTE	6	$2,765.25	$16,591.50
			Totales por Partida		**$78,907.74**
	PARTIDA: **LIMPIEZAS**				
25	LIMPIEZA GENERAL DE LA OBRA, INCLUYE: BARRIDO, CARGA, ACARREOS Y RETIRO DE ESCOMBROS FUERA DE LA OBRA, TRABAJO TERMINADO.	M2	2772.15	$4.35	$12,058.85
			Totales por Partida		**$12,058.85**
			Totales por Grupo		**$1,844,452.88**

Obra: **CONSTRUCCIÓN DE SOBRECARPETA ASFÁLTICA CALLE VALLADOLID**

Ubicación: **TRAMO: DE CALLE PETRÓLEOS MEXICANOS A CALLE BENJAMÍN DE LA MORA, COLONIA DEL CARMEN Y BARRIO DE GUADALUPE, AGUASCALIENTES Mpio.**

Contratista: **ODZ ARQUITECTURA Y CONSTRUCCION S.A. DE C.V. (349)**

No.	Concepto	Unidad	Cantidad	Precio Unitario	Importe Total
	GRUPO: **GUARNICIONES Y BANQUETAS**				
	PARTIDA: **GUARNICIONES**				
26	EXCAVACION A MAQUINA Y/O A MANO EN MATERIAL TIPO II, EN SECO O PRESENCIA DE AGUA, INCLUYE. CORTE DE RAIZ DE CUALQUIER TAMAÑO Y GROSOR, HASTA UNA PROFUNDIDAD DE 40 CM DESPUES DE DESMONTE, DESPALME Y/O DEMOLICION DE SUPERFICIE O ELEMENTO ESTRUCTURAL O DE ACABADO, PROTECCION DE AREAS ADYACENTES, SIN DAÑAR AREAS ALEDAÑAS, CARGA Y ACARREO A TIRADERO OFICIAL, CONSERVACION DE LA MISMA, TRABAJO TERMINADO, LIMPIEZAS.	M3	3.13	$394.55	$1,234.94
27	COMPACTACION DE TERRENO NATURAL AL 90% DE SU P.V.S.M EN SU COMPACTACION., INCLUYE ESCARIFICADO, TENDIDO, HOMOGENIZADO, HUMEDECIDO OPTIMO NIVELADO Y COMPACTADO EN CAPAS DE 20 CM, CALIDAD Limite liquido máximo 50%, Valor de Soporte California (CBR) mínimo 15%, Expansión máxima 5%, Grado de Compactación minimo 90% ± 2, Y TODO LO NECESARIO PARA SU CORRECTA EJECUCION,	M2	12.5	$26.40	$330.00
28	CONSTRUCCION DE GUARNICION RECTA Y/O CURVA TRAPEZOIDAL 15-20X40 CM DE SECCION CON CONCRETO PREMEZCLADO MR=38 KGF/CM2, R.N.REVENIMIENTO DE 8 A 10 CM, T.M.A. 3/4", GRAVA TRITURADA, ACABADO PULIDO EN PARTE DE SUPERIOR Y DOBLADOR EN ARISTAS, INCLUYE: COMPACTADO DE PLANTILLA, CIMBRADO, COLADO, VIBRADO, ACABADO, DESCIMBRADO, ALINEADO, NIVELADO, Y CURADO EN SU PARTE SUPERIOR CON MEMBRANA BASE AGUA A RAZON DE 1 LTO/M2, JUNTA DE AISLAMIENTO LONGITUDINAL AL COMBINAR CON OTRO ELEMENTO Y TRANSVERSAL @ 30 MT MAXIMO, SELLADO CON SELLADOR AUTONIVELANTE LONGITUDINAL, TRABAJO TERMINADO, .P.U.O.T.	ML	25	$164.71	$4,117.75
29	RELLENO COMPACTADO AL 95% CON MATERIAL DE BANCO EN CAPAS DE 20 CM UTILIZANDO BAILARINA. INCLUYE: SUMINISTRO DE TEPETATE (MATERIAL DE BANCO) EN LA OBRA, ABUNDAMIENTO, ACARREOS DENTRO DE LA OBRA, CRIBADO, RETIRO DE MATERIAL, MANO DE OBRA Y EQUIPO, LIMPIEZAS, TRABAJO TERMINADO.	M3	1.13	$428.23	$483.90
30	CARGA MECANICA Y ACARREO DE MATERIAL PRODUCTO DE EXCAVACION Y DEMOLICION EN CAMION DE VOLTEO AL 1er. KM, VOLUMEN MEDIDO COMPACTO.	M3	2	$42.56	$85.12
				Totales por Partida	**$6,251.71**
				Totales por Grupo	**$6,251.71**

Obra: **CONSTRUCCIÓN DE SOBRECARPETA ASFÁLTICA CALLE VALLADOLID**

Ubicación: **TRAMO: DE CALLE PETRÓLEOS MEXICANOS A CALLE BENJAMÍN DE LA MORA, COLONIA DEL CARMEN Y BARRIO DE GUADALUPE, AGUASCALIENTES Mpio.**

Contratista: **ODZ ARQUITECTURA Y CONSTRUCCION S.A. DE C.V. (349)**

No.	Concepto	Unidad	Cantidad	Precio Unitario	Importe Total
	GRUPO: **SEÑALIZACION**				
	PARTIDA: **SEÑALIZACION HORIZONTAL**				
41	SUMINISTRO Y APLICACIÓN DE PINTURA EPOXICA BASE SOLVENTE COLOR AZUL (PANTONE 294) EN RAMPAS PARA PERSONAS CON DISCAPACIDAD CUALQUIER SECCIÓN SEGÚN PLANOS. INCLUYE: TRAZO, MANO DE OBRA, LIMPIEZA PREVIA DE SUPERFICIE, EQUIPO NECESARIO PARA SU EJECUCIÓN, Y TODO LO NECESARIO PARA SU CORRECTA EJECUCIÓN, TRABAJO TERMINADO.	M2	34.56	$441.62	$15,262.39
42	SUMINISTRO Y APLICACIÓN DE LOGOTIPO A (SILLA DE RUEDAS) EN PINTURA EPOXICA BASE SOLVENTE COLOR BLANCO EN RAMPAS PARA PERSONAS CON DISCAPACIDAD TAMAÑO Y DISEÑO SEGÚN PLANOS. INCLUYE: TRAZO, ENMASCARILLADO, PLANTILLA, MANO DE OBRA, LIMPIEZA PREVIA DE SUPERFICIE, EQUIPO NECESARIO PARA SU EJECUCIÓN, Y TODO LO NECESARIO PARA SU CORRECTA EJECUCIÓN, TRABAJO TERMINADO.	PZA	24	$245.32	$5,887.68
43	SUMINISTRO Y APLICACIÓN DE PINTURA BASE SOLVENTE PARA MARCAS EN GUARNICIONES CLASIFICACION M-12.1, M12.2 APLICADA SOBRE GUARNICIONES Y DENTELLONES DE CUALQUIER COLOR, SEGÚN SE REQUIERA Y SEGÚN NORMA S.C.T. SECADO AL TACTO EN 5 MIN Y AL DURO EN 30 MIN CON MICRO ESFERA , DESARROLLO DE 35 CM. INCLUYE: MATERIALES Y ESPECIFICACIONES QUE CUMPLAN CON LA NORMATIVA N-CMT-5-01-001/05, N-PRY-CAR-10-01-002/13 APLICADAS AL DIA DE HOY, TRAZO, MANO DE OBRA, LIMPIEZA PREVIA DE SUPERFICIE, EQUIPO NECESARIO PARA SU EJECUCIÓN, Y TODO LO NECESARIO PARA SU CORRECTA EJECUCIÓN, TRABAJO TERMINADO.	ML	746	$50.37	$37,576.02
44	SUMINISTRO Y APLICACIÓN DE PINTURA TERMOPLASTICA ALQUIDALICA DE 120 MILESIMAS DE " (in) EN RAYA SEPARADORA DE SENTIDOS DE CIRCULACION CLASIFICACIÓN M - 1.1, LÍNEA CONTINUA SENCILLA DE DIVISIÓN DE CARRILES DE FRENTE EN PISO, DE 10 CM DE ANCHO, COLOR BLANCO Y/O AMARILLO CON MICRO ESFERA SEGÚN MANUAL DE SEÑALIZACIÓN VIAL Y DISPOSITIVOS DE SEGURIDAD SICT, SECADO AL TACTO EN 5 MIN Y AL DURO EN 30 MIN. INCLUYE: MATERIALES Y ESPECIFICACIONES QUE CUMPLAN CON LA NORMATIVA N-CMT-5-01-001/13, N-PRY-CAR-10-01-002/13 APLICADAS AL DIA DE HOY, MATERIAL APLICADO EN SU ESTADO DE FUSION A UNA TEMPERATURA MINIMA DE 204 C, LA SUPERFICIE DE CONCRETO O ASFALTO NO DEBE PRESENTAR UNA TEMPERATURA MENOR A LOS 10 C, ;TIEMPO DE SECADO EN RANGOS DE TEMPERATURA DE 10 C DEL SUSTRATO 2 MINUTOS, Y NO MAS DE 10 MINUTOS CUANDO EL SUSTRATO OSCILA ALREDEDOR DE 54C, TRAZO, ENMASCARILLADO, MANO DE OBRA, LIMPIEZA PREVIA Y FINAL DE SUPERFICIE, EQUIPO NECESARIO PARA SU EJECUCIÓN, Y TODO LO NECESARIO PARA SU CORRECTA EJECUCIÓN, TRABAJO TERMINADO.	ML	127	$55.35	$7,029.45



Obra: **CONSTRUCCIÓN DE SOBRECARPETA ASFÁLTICA CALLE VALLADOLID**

Ubicación: **TRAMO: DE CALLE PETRÓLEOS MEXICANOS A CALLE BENJAMÍN DE LA MORA, COLONIA DEL CARMEN Y BARRIO DE GUADALUPE, AGUASCALIENTES Mpio.**

Contratista: **ODZ ARQUITECTURA Y CONSTRUCCION S.A. DE C.V. (349)**

No.	Concepto	Unidad	Cantidad	Precio Unitario	Importe Total
	GRUPO: **SEÑALIZACION**				
	PARTIDA: **SEÑALIZACION HORIZONTAL**				
45	SUMINISTRO Y APLICACIÓN DE PINTURA TERMOPLASTICA ALQUIDALICA DE 120 MILESIMAS DE " (in) EN RAYA SEPARADORA DE SENTIDOS DE CIRCULACION CLASIFICACIÓN M - 1.2, RAYA DISCONTINUA SENCILLA, DE DIVISIÓN DE CARRILES PARA VELOCIDADES MENORES A 60 KM/HR DE FRENTE EN PISO, DESARROLLO DE 2.50 ML X 0.10 MTS DE ANCHO, CON UNA SEPARACIÓN DE 5.00 MTS ENTRE SI PROMEDIO, A BASE DE PINTURA PARA TRAFICO COLOR BLANCO CON MICRO ESFERA SEGÚN MANUAL DE SEÑALIZACIÓN VIAL Y DISPOSITIVOS DE SEGURIDAD SICT (S.C.T). INCLUYE: MATERIALES Y ESPECIFICACIONES QUE CUMPLAN CON LA NORMATIVA N-CMT-5-01-001/13, N-PRY-CAR-10-01-002/13 APLICADAS AL DIA DE HOY, MATERIAL APLICADO EN SU ESTADO DE FUSION A UNA TEMPERATURA MINIMA DE 204 C, LA SUPERFICIE DE CONCRETO O ASFALTO NO DEBE PRESENTAR UNA TEMPERATURA MENOR A LOS 10 C, ;TIEMPO DE SECADO EN RANGOS DE TEMPERATURA DE 10 C DEL SUSTRATO 2 MINUTOS, Y NO MAS DE 10 MINUTOS CUANDO EL SUSTRATO OSCILA ALREDEDOR DE 54C, TRAZO, ENMASCARILLADO, MANO DE OBRA, LIMPIEZA PREVIA Y FINAL DE SUPERFICIE, EQUIPO NECESARIO PARA SU EJECUCIÓN, Y TODO LO NECESARIO PARA SU CORRECTA EJECUCIÓN, TRABAJO TERMINADO.	ML	430	$55.35	$23,800.50
46	SUMINISTRO Y APLICACIÓN DE PINTURA TERMOPLASTICA ALQUIDALICA DE 120 MILESIMAS DE " (in) EN RAYA EN LA ORILLA DEL ARROYO VIAL CLASIFICACIÓN M - 3.3, CONTINUA IZQUIERDA, PARA VIALIDADES URBANAS DE FRENTE EN PISO, DE 10 CM DE ANCHO Y SEPARADA 15 CM. DE LA GUARNICION, A BASE DE PINTURA PARA TRAFICO COLOR BLANCO CON MICRO ESFERA SEGÚN MANUAL DE SEÑALIZACIÓN VIAL Y DISPOSITIVOS DE SEGURIDAD SICT (S.C.T)., INCLUYE: MATERIALES Y ESPECIFICACIONES QUE CUMPLAN CON LA NORMATIVA N-CMT-5-01-001/13, N-PRY-CAR-10-01-002/13 APLICADAS AL DIA DE HOY, MATERIAL APLICADO EN SU ESTADO DE FUSION A UNA TEMPERATURA MINIMA DE 204 C, LA SUPERFICIE DE CONCRETO O ASFALTO NO DEBE PRESENTAR UNA TEMPERATURA MENOR A LOS 10 C, ;TIEMPO DE SECADO EN RANGOS DE TEMPERATURA DE 10 C DEL SUSTRATO 2 MINUTOS, Y NO MAS DE 10 MINUTOS CUANDO EL SUSTRATO OSCILA ALREDEDOR DE 54C, TRAZO, ENMASCARILLADO, MANO DE OBRA, LIMPIEZA PREVIA Y FINAL DE SUPERFICIE, EQUIPO NECESARIO PARA SU EJECUCIÓN, Y TODO LO NECESARIO PARA SU CORRECTA EJECUCIÓN, TRABAJO TERMINADO.	ML	296	$55.35	$16,383.60
47	SUMINISTRO Y APLICACIÓN DE PINTURA TERMOPLASTICA ALQUIDALICA DE 120 MILESIMAS DE " (in) EN RAYA PARA CRUCE PEATONAL CLASIFICACIÓN M - 7.1, PARA INDICAR " CRUCE PEATONAL EN VIAS PRIMARIAS", COLOR AMARILLO, REFLEJANTE CON MICRO ESFERA DE VIDRIO EN PROPORCIÓN SEGÚN MANUAL DE SEÑALIZACIÓN VIAL Y DISPOSITIVOS DE SEGURIDAD SICT (S.C.T). DE 0.40 MTS DE ANCHO Y 3.5 MTS. DE LONGITUD POR EL ANCHO DE LA VIALIDAD, CON UNA SEPARACIÓN DE 0.40 MTS. ENTRE ELLAS, INCLUYE: MATERIALES Y ESPECIFICACIONES QUE CUMPLAN CON LA NORMATIVA N-CMT-5-01-001/13, N-PRY-CAR-10-01-002/13 APLICADAS AL DIA DE HOY, MATERIAL APLICADO EN SU ESTADO DE FUSION A UNA TEMPERATURA MINIMA DE 204 C, LA SUPERFICIE DE CONCRETO O ASFALTO NO DEBE PRESENTAR UNA TEMPERATURA MENOR A LOS 10 C, ;TIEMPO DE SECADO EN RANGOS DE TEMPERATURA DE 10 C DEL SUSTRATO 2 MINUTOS, Y NO MAS DE 10 MINUTOS CUANDO EL SUSTRATO OSCILA ALREDEDOR DE 54C, TRAZO, ENMASCARILLADO, MANO DE OBRA, LIMPIEZA PREVIA Y FINAL DE SUPERFICIE, EQUIPO NECESARIO PARA SU EJECUCIÓN, Y TODO LO NECESARIO PARA SU CORRECTA EJECUCIÓN, TRABAJO TERMINADO.	M2	381.5	$461.21	$175,951.61

Obra: **CONSTRUCCIÓN DE SOBRECARPETA ASFÁLTICA CALLE VALLADOLID**

Ubicación: **TRAMO: DE CALLE PETRÓLEOS MEXICANOS A CALLE BENJAMÍN DE LA MORA, COLONIA DEL CARMEN Y BARRIO DE GUADALUPE, AGUASCALIENTES Mpio.**

Contratista: **ODZ ARQUITECTURA Y CONSTRUCCION S.A. DE C.V. (349)**

No.	Concepto	Unidad	Cantidad	Precio Unitario	Importe Total
	GRUPO: **SEÑALIZACION**				
	PARTIDA: **SEÑALIZACION HORIZONTAL**				
48	SUMINISTRO Y APLICACIÓN DE PINTURA TERMOPLASTICA ALQUIDALICA DE 120 MILESIMAS DE " (in) EN FLECHAS CLASIFICACIÓN M - 11.1, "FLECHA SENCILLA" PARA INDICAR SENTIDO DE CIRCULACIÓN , EN VIALIDADES PARA VELOCIDAD MENOR A 60KM POR HORA DIMENSION NORMATIVA SEGUN MANUAL DE SEÑALIZACIÓN VIAL Y DISPOSITIVOS DE SEGURIDAD SICT (SCT) Y/O (VER PLANO DE SEÑALAMIENTOS), COLOR BLANCO, REFLEJANTE CON MICRO ESFERA DE VIDRIO EN PROPORCIÓN SEGÚN NORMA SCT, INCLUYE: MATERIALES Y ESPECIFICACIONES QUE CUMPLAN CON LA NORMATIVA N-CMT-5-01-001/13, N-PRY-CAR-10-01-002/13 APLICADAS AL DIA DE HOY, MATERIAL APLICADO EN SU ESTADO DE FUSION A UNA TEMPERATURA MINIMA DE 204 C, LA SUPERFICIE DE CONCRETO O ASFALTO NO DEBE PRESENTAR UNA TEMPERATURA MENOR A LOS 10 C, ;TIEMPO DE SECADO EN RANGOS DE TEMPERATURA DE 10 C DEL SUSTRATO 2 MINUTOS, Y NO MAS DE 10 MINUTOS CUANDO EL SUSTRATO OSCILA ALREDEDOR DE 54C, TRAZO, ENMASCARILLADO, MANO DE OBRA, LIMPIEZA PREVIA Y FINAL DE SUPERFICIE, EQUIPO NECESARIO PARA SU EJECUCIÓN, Y TODO LO NECESARIO PARA SU CORRECTA EJECUCIÓN, TRABAJO TERMINADO.	PZA	19	$2,030.83	$38,585.77
49	SUMINISTRO Y APLICACIÓN DE PINTURA TERMOPLASTICA ALQUIDALICA DE 120 MILESIMAS DE " (in) EN FLECHAS CLASIFICACIÓN M - 11.1, " FLECHA CABEZA DOBLE" PARA INDICAR SENTIDO DE CIRCULACIÓN (VUELTA IZQUIERDA O DERECHA), EN VIALIDADES PARA VELOCIDAD MENOR A 60KM POR HORA SEGUN MANUAL DE SEÑALIZACIÓN VIAL Y DISPOSITIVOS DE SEGURIDAD SICT (SCT), (VER PLANO DE SEÑALAMIENTOS), EN COLOR BLANCO, REFLEJANTE CON MICRO ESFERA DE VIDRIO EN PROPORCIÓN SEGÚN NORMA SCT, INCLUYE: MATERIALES Y ESPECIFICACIONES QUE CUMPLAN CON LA NORMATIVA N CMT 5 01 001/13, N PRY CAR 10 01 002/13 APLICADAS AL DIA DE HOY, MATERIAL APLICADO EN SU ESTADO DE FUSION A UNA TEMPERATURA MINIMA DE 204 C, LA SUPERFICIE DE CONCRETO O ASFALTO NO DEBE PRESENTAR UNA TEMPERATURA MENOR A LOS 10 C, ;TIEMPO DE SECADO EN RANGOS DE TEMPERATURA DE 10 C DEL SUSTRATO 2 MINUTOS, Y NO MAS DE 10 MINUTOS CUANDO EL SUSTRATO OSCILA ALREDEDOR DE 54C, TRAZO, ENMASCARILLADO, MANO DE OBRA, LIMPIEZA PREVIA Y FINAL DE SUPERFICIE, EQUIPO NECESARIO PARA SU EJECUCIÓN, Y TODO LO NECESARIO PARA SU CORRECTA EJECUCIÓN, TRABAJO TERMINADO.	PZA	9	$1,153.01	$10,377.09
50	SUMINISTRO Y APLICACIÓN DE PINTURA TERMOPLASTICA ALQUIDALICA DE 120 MILESIMAS DE " (in) EN RAYA DE ALTO CLASIFICACIÓN M - 6, PARA INDICAR ALTO EN CRUCEROS, COLOR BLANCO, REFLEJANTE CON MICRO ESFERA DE VIDRIO EN PROPORCIÓN SEGÚN MANUAL DE SEÑALIZACIÓN VIAL Y DISPOSITIVOS DE SEGURIDAD SICT (S.C.T). DE 0.60 MTS DE ANCHO DE LONGITUD VARIABLE, INCLUYE: MATERIALES Y ESPECIFICACIONES QUE CUMPLAN CON LA NORMATIVA N-CMT-5-01-001/13, N-PRY-CAR-10-01-002/13 APLICADAS AL DIA DE HOY, MATERIAL APLICADO EN SU ESTADO DE FUSION A UNA TEMPERATURA MINIMA DE 204 C, LA SUPERFICIE DE CONCRETO O ASFALTO NO DEBE PRESENTAR UNA TEMPERATURA MENOR A LOS 10 C, ;TIEMPO DE SECADO EN RANGOS DE TEMPERATURA DE 10 C DEL SUSTRATO 2 MINUTOS, Y NO MAS DE 10 MINUTOS CUANDO EL SUSTRATO OSCILA ALREDEDOR DE 54C, TRAZO, ENMASCARILLADO, MANO DE OBRA, LIMPIEZA PREVIA Y FINAL DE SUPERFICIE, EQUIPO NECESARIO PARA SU EJECUCIÓN, Y TODO LO NECESARIO PARA SU CORRECTA EJECUCIÓN, TRABAJO TERMINADO.	ML	43	$279.24	$12,007.32

Obra: **CONSTRUCCIÓN DE SOBRECARPETA ASFÁLTICA CALLE VALLADOLID**

Ubicación: **TRAMO: DE CALLE PETRÓLEOS MEXICANOS A CALLE BENJAMÍN DE LA MORA, COLONIA DEL CARMEN Y BARRIO DE GUADALUPE, AGUASCALIENTES Mpio.**

Contratista: **ODZ ARQUITECTURA Y CONSTRUCCION S.A. DE C.V. (349)**

No.	Concepto	Unidad	Cantidad	Precio Unitario	Importe Total
	GRUPO: SEÑALIZACION				
	PARTIDA: SEÑALIZACION HORIZONTAL				
51	SUMINISTRO Y COLOCACION DE VIALETA STANDARD (S-200) DE 10X10CM. COLOR: CUERPO AMARILLO Y REFLEJANTE AMARILLO 1 CARA MARCA SEA O SIMILAR EN CALIDAD Y ESPECIFICACIONES DE FICHA TECNICA, ANCLADO EN PAVIMENTO SISTEMA DE SUJECION DE ALTO AGARRE BASE CUÑAS CON AB PEGAMENTO EPOXICO 50/50 RESISTENTE A ALTA TEMPERATURA (VER PLANO DE DETALLES DE SEÑALAMIENTOS HORIZONTAL Y VERTICAL). INCLUYE: TRAZO, ALINEACION, ELEVACION CUALQUIER ALTURA, TRABAJO TERMINADO, LIMPIEZAS.	PZA	60	$74.41	$4,464.60
52	SUMINISTRO Y COLOCACION DE VIALETA SOLAR DE 10X10CM. COLOR: CUERPO ALUMINIO 3 LED DOS CARAS REFLEJANTES MARCA CREATIVAL VT-29 O SIMILAR EN CALIDAD Y ESPECIFICACIONES DE FICHA TÉCNICA, FIJADO EN PAVIMENTO CON SISTEMA DE SUJECIÓN DE ALTO AGARRE PEGAMENTO EPOXICO 100 A/B (RESINA EPÓXICA/RESINA POLIAMIDA MODIFICADA), RESISTENTE A ALTA TEMPERATURA (VER PLANO DE DETALLES DE SEÑALAMIENTOS HORIZONTAL), INCLUYE: LIMPIEZA PREVIA DE LA SUPERFICIE+C92, PREPARACIÓN DE LA SUPERFICIE, TRAZO, ALINEACIÓN, Y TODO LO NECESARIO PARA SU CORRECTA EJECUCIÓN, TRABAJO TERMINADO.	PZA	20	$188.42	$3,768.40

Totales por Partida		**$351,094.43**
Totales por Grupo		**$351,094.43**
Totales Presup.		**$2,404,138.31**
Anticipo	+	**$1,161,239.75**
Amortizac. Ant.	-	**$1,161,239.75**
SubTotal. Ant.	=	**$2,404,138.31**
IVA	+	**$384,662.13**
Total	=	**$2,788,800.44**



H. AYUNTAMIENTO CONSTITUCIONAL DEL MUNICIPIO DE AGUASCALIENTES 2021-2024

PRESUPUESTO MODIFICADO

Aguascalientes

Obra: CONSTRUCCIÓN DE SOBRECARPETA ASFÁLTICA CALLE VALLADOLID

Ubicación: TRAMO: DE CALLE PETRÓLEOS MEXICANOS A CALLE BENJAMÍN DE LA MORA, COLONIA DEL CARMEN Y BARRIO DE GUADALUPE, AGUASCALIENTES Mpio.

Contratista: ODZ ARQUITECTURA Y CONSTRUCCION S.A. DE C.V. (349)

Grupo	Partida	Importe
PRELIMINARES		
	PRELIMINARES Y DEMOLICIONES	$202,339.29
	Subtotal por Grupo	$202,339.29
SOBRECARPETA ASFALTICA		
	BACHEO PROFUNDO	$65,639.45
	SOBRE CARPETA ASFALTICA	$1,687,846.84
	OBRA COMPLEMENTARIA	$78,907.74
	LIMPIEZAS	$12,058.85
	Subtotal por Grupo	$1,844,452.88
GUARNICIONES Y BANQUETAS		
	GUARNICIONES	$6,251.71
	Subtotal por Grupo	$6,251.71
SEÑALIZACION		
	SEÑALIZACION HORIZONTAL	$351,094.43
	Subtotal por Grupo	$351,094.43

Totales Presup.		$2,404,138.31
Anticipo	+	$1,161,239.75
Amortizac. Ant.	-	$1,161,239.75
SubTotal. Ant.	=	$2,404,138.31
IVA	+	$384,662.13
Total	=	$2,788,800.44



H. AYUNTAMIENTO CONSTITUCIONAL DEL MUNICIPIO DE AGUASCALIENTES 2021-2024

ANALISIS DEL PRESUPUESTO DE OBRA POR CONTRATO

Aguascalientes

Obra 2022-FISMDF-0135-0411102-072 CONSTRUCCIÓN DE SOBRECARPETA ASFÁLTICA CALLE VALLADOLID, TRAMO: DE CALLE PETRÓLEOS MEXICANOS A CALLE BENJAMÍN DE LA MORA, COLONIA DEL CARMEN Y BARRIO DE GUADALUPE

Programa 04 URBANIZACION MUNICIPAL Subprograma 11 Calles y caminos

Contratista ODZ ARQUITECTURA Y CONSTRUCCION S.A. DE C.V. (349)

Contrato FISMDF-0135-2022 CONSTRUCCIÓN DE SOBRECARPETA ASFÁLTICA CALLE VALLADOLID, TRAMO: DE CALLE PETRÓLEOS MEXICANOS A CALLE BENJAMÍN DE LA MORA, COLONIA DEL CARMEN Y BARRIO DE GUADALUPE, AGUASCALIENTES Mpio.

Ultima Estim. 2 de 22 Dic 2022 al 28 Dic 2022

Total Contrato	$2,694 076.22
Total Ampliaciones	$94 724.22
Total Contratado	$2,788 800.44
Anticipo (50 %)	$1,161 239.75
Total Estimado	$2,788 800.44
Total por Estimar	$0.00

No.	Concepto	Unid. Med.	Volumen			% Avanc. Estimado	Precio Contratado	Importe		
			Contratado	Acumulado	Excedente			Contratado	Acumulado	Excedente
GRUPO: PRELIMINARES										
PARTIDA: PRELIMINARES Y DEMOLICIONES										
1	LIMPIA, TRAZO Y NIVELACION EN PAVIMENTOS, CALLES Y VIALIDADES CON EQUIPO TOPOGRAFICO, INCLUYE: EJES, BANCO DE NIVEL, RENIVELACIONES LAS VECES NECESARIAS, CORRECCION DE RASANTE A PUNTOS OBLIGADOS (AUTORIZADOS POR LA SUPERVISION), ESTACAS, VARILLAS, MANO DE OBRA CALIFICADA, HERRAMIENTA NECESARIA, EQUIPO DE PRECISION CALIBRADO, TRABAJO TERMINADO.P.U.O.T.	M2	2,864.40	2,772.15		96.78	$5.69	$16,298.44	$15,773.53	
2	SONDEO A MANO O A MAQUINA PARA LOCALIZACION DE TUBERIAS CUALQUIER PROFUNDIDAD Y MATERIAL PARA VERIFICAR LA CALIDAD DE LAS INSTALACIONES HIDRAULICO SANITARIAS CUIDANDO NO DAÑARLAS PARA NO INTERFERIR EN LOS SERVICIOS, INCLUYE: EXCAVACION, EQUIPO, MANO DE OBRA, REPORTE A LA SUPERVISION, RELLENOS, COMPACTACIONES, TRABAJO TERMINADO.	SONDE	8.00	6.00		75.00	$1,678.06	$13,424.48	$10,068.36	
3	CORTE CON DISCO DIAMANTADO DE 14" EN PISOS DE CONCRETO ASFALTICO DE HASTA 8.00 cm. DE PROFUNOIDAD. INCLUYE: TRAZO, EQUIPO Y OPERACION, LIMPIEZAS.	ML	197.15	13.50		6.85	$19.33	$3,810.91	$260.95	
4	DEMOLICION PARCIAL DE PAVIMENTO HIDRAULICO Y/O ASFALTICO DE HASTA 15 CM. DE ESPESOR PROMEDIO EN PAVIMENTOS Y (BANQUETAS, LOSAS DIAMANTE Y CAJAS DE VALVULAS, TOPES) CON O SIN ARMADO DE ACERO, SIN RECUPERACION, MUROS, MOJONERAS, ANCLAJES, ETC, DE FORMA MANUAL Y MECANICA, INCLUYE ACARREO DE MATERIAL AL LUGAR DE ACOPIO, HERRAMIENTA NECESARIA Y TODO LO NECESARIO PARA SU CORRECTA EJECUCION, LIMPIEZA, TRABAJO TERMINADO	M3	8.40	3.37		40.12	$261.99	$2,200.72	$882.91	
5	FRESADO UNIFORME DE LA SUPERFICIE DE RODADURA EN PAVIMENTO DE CONCRETO ASFALTICO 3-7 CM (5 cm de espesor promedio) MEDIANTE FRESADORA EN FRIO COMPACTA, EQUIPADA CON BANDA TRANSPORTADORA PARA CARGA DIRECTA SOBRE CAMION DE VOLTEO, INCLUYE: TRAMO DE PRUEBA AL INICIO DEL FRESADO PARA AUTORIZACION DE SUPERVISION (SUPERFICIE FRESADA UNIFORME Y SIN PROTUBERANCIAS NI ONDEOS), ACARREOS LOCALES, CARGA Y ACARREO A KM SUBSECUENTES (11 A 15 KM APROX) DE MATERIAL PRODUCTO DEL FRESADO DE CARPETA ASFALTICA EL TRASLADO SERA A PARQUE DE MAQUINARIA DE LA SOPMA, PIEZAS DE DESGASTE, COMBUSTIBLES, CONSUMIBLES, MANO DE OBRA, CUALQUIER VOLUMEN Y AREA,EQUIPO NECESARIO, LIMPIEZA FINA Y GRUESA, TRABAJO TERMINADO.	M3	98.58	138.60	40.02	140.60	$1,211.19	$119,399.11	$167,870.93	$48,471.82
7	DEMOLICION CONTROLADA DE CONCRETO HIDRAULICO EN DENTELLONES Y GUARNICIONES DE 15 x 20 x 40 CM. DE FORMA MANUAL Y MECÁNICA, INCLUYE: CORTES CON DISCO, ACARREO DEL MATERIAL AL LUGAR DE ACOPIO PARA SU CARGA Y ACARREO FUERA DE LA OBRA.	ML	25.00	25.00		100.00	$290.67	$7,266.75	$7,266.75	
8	CARGA MECANICA Y ACARREO DE MATERIAL PRODUCTO DE EXCAVACION Y DEMOLICION EN CAMION DE VOLTEO AL 1er. KM, VOLUMEN MEDIDO COMPACTO.	M3	10.40	4.12		39.62	$52.39	$544.86	$215.85	
							Totales por Partida:	$162,945.26	$202,339.29	$48,471.82
							Totales por Grupo:	$162,945.26	$202,339.29	$48,471.82

GRUPO: SOBRECARPETA ASFALTICA

ANALISIS DEL PRESUPUESTO DE OBRA POR CONTRATO

No.	Concepto	Unid. Med.	Volumen			% Avanc. Estimado	Precio Contratado	Importe		
			Contratado	Acumulado	Excedente			Contratado	Acumulado	Excedente
GRUPO: SOBRECARPETA ASFALTICA										
PARTIDA: BACHEO PROFUNDO										
10	BACHEO PROFUNDO AISLADO UTILIZANDO MATERIAL CALIDAD BASE HIDRAULICA PARA MAS DE UN MILLON DE EJES EQUIVALENTES DEL BANCO QUE ELIJA EL CONTRATISTA, INCISO N.CSV.CAR.1.02.004/03 DE LAS NORMAS DE CONSTRUCCION DE CARR. DE LA SCT, INCLUYE: PREPARACION, PERFILADO, MATERIALES, MANO DE OBRA, HERRAMIENTA MENOR Y EQUIPO NECESARIO QUE SE REQUIERA FARA LOGRAR LA COMPACTACION DE 100% PVSM, ACARREOS DENTRO Y FUERA DE LA OERA, PREPARACION DE MATERIAL, HUMEDECIDO, NIVELADO, TRASLADO DE UN PUNTO A OTRO DENTRO DE LA OBRA, EN CUALQUIER VOLUMEN, MOVIMIENTO DE MAQUINARIA P.U.O.T	M3	4.20	56.40	52.20	1,342.86	$1,163.82	$4,888.04	$65,639.45	$60,751.40
							Totales por Partida:	$4,888.04	$65,639.45	$60,751.40
PARTIDA: SOBRE CARPETA ASFALTICA										
13	PREPARACIÓN DE LA SUPERFICIE DE CONTACTO EN LOS EXTREMOS DONDE LA PERFILADORA NO ALCANCE POR LÍMITES CON LA GUARNICIÓN, CON UN RASPADO SUPERFICIAL CON RETROEXCAVADORA, ELIMINANDO TECATAS QUE HAYAN QUEDADO PARA RENIVELADO, BARRIDOS ENTRE PASADA DE MOTOCONFORMADORA Y EN REMATES DE EMPATES A DETALLE A MANO, INCLUYE: RETIRO DE MATERIAL FUERA DE LA OBRA A TIRADERO OFICIAL INDICADO.	M2	1,701.20	132.00		7.76	$193.78	$329,658.54	$25,578.96	
14	RENIVELACIONES CON CONCRETO ASFALTICO MEZCLA EN PLANTA EN CALIENTE ASFALTO MODIFICADO CON POLIMERO TIPO I, CUMPLIENDO LAS NORMAS SCT REFERENTES DE CONSTRUCCCION Y CONSERVACION, GRANULOMETRIA DENSA 3/4" A FINOS, MEDIDO COMPACTO AL NOVENTA Y CINCO PORCIENTO (95%), INCLUYE CARGA Y ACARREO EN TRAMOS AISLADOS, MATERIALES MANO DE OBRA, ACARREO DE MATERIALES, Y MAQUINARIA Y EQUIPO AL SIGUIENTE PUNTO EN CUALQUIER VOLUEN, PERFILADO, LIMPIEZA DE HUESO Y GRAVA SUELTA, TRABAJO TERMINADO P.U.O.T	M3	42.25	67.50	25.25	159.76	$5,776.57	$244,060.08	$389,918.47	$145,858.39
17	RIEGO DE LIGA CON EMULSION DE ROMPIMIENTO RAPIDO (ECR-65 %), INCLUYE, SUMINISTRO, ALMACENAMIENTO, CALENTAMIENTO, Y APLICACION DE LA EMULSION CON EQUIPO ESPECIAL PARA ESA ACTIVIDAD, ESPREAS O BACHADOR LIMPIAS Y ALINEADAS, CONTROL DE CALIDAD A CADA DOS REMESAS EN OBRA (INDEPENDIENTEMENTE DE LA CANTIDAD A UTILIZAR) EN LA PETROLIZADORA, A RAZON DE 0.8 LT DE EMULSION POR M2, O LO QUE INDIQUE EL LABORATORIO DE CALIDAD DEL CONTRATISTA, NO SE ACEPTAN "IMPREGNALIGA", TRABAJO TERMINADO, P.U.O.T.	M2	2,816.40	2,772.15		98.43	$17.87	$50,329.07	$49,538.32	
18	SUMINISTRO Y COLOCACION DE CONCRETO ASFALTICO EN CALIENTE DE GRANULOMETRIA DENSA ELABORADA CON ASFALTO MODIFICADO TIPO I, AGREGADO 3/4" A FINOS, DE 5 CM DE ESPESOR, FORMADA Y COMPACTADO AL 95%, INCLUYE MATERIALES, QUE CUMPLAN LA NORMATIVA SCT-N-CMT-04-04, SCT-CMT-4-05-002, SCT-CMT-4-05-003, SCT-CMT-4-05-004, SCT-CTR-CAR-1-04-006-14 APLICADAS AL DIA DE HOY, DISEÑO MARSHALL (DEVERÁ SER AUTORIZADO POR EL LABORATORIO DE CALIDAD DE SOPMA AL MENOS 3 DIAS ANTES DE INICIO DE TENDIDO DE LA MEZCLA ASFALTICA), INCUYE: TRAMO DE PRUEBA AL INICIO PARA REVISION Y AUTORIZACION DEL ESPESOR POR PARTE DEL SUPERVISOR, EL CONTRATISTA DEBERÁ PREVEER EL SUMINISTRO Y TIEMPOS MUERTOS POR MOVIMIENTOS DEL TREN DE MAQUINAS DE TRABAJO EN TRAMOS AISLADOS. TRABAJO TERMINADO P.U.O.T. Y LIMPIEZAS DE GRANZON Y HUESO LATERAL.	M2	2,816.40	4,473.16	1,656.76	158.83	$272.60	$767,750.64	$1,219,382.47	$451,632.78
19	COMPACTACION SOBRE MORTERO ASFALTICC TENDIDO EN APROCHES CON GUARNICIONES CON EQUIPO LIGERO (PLANCHITA), INCLUYE: MANO DE OBRA Y EQUIPO, TRABAJO TERMINADO.	M2	298.40	298.40		100.00	$11.49	$3,428.62	$3,428.62	
							Totales por Partida:	$1,395,226.94	$1,687,846.84	$597,491.17
PARTIDA: OBRA COMPLEMENTARIA										
20	RE NIVELACIÓN DE POZO DE VISITA HASTA 30 cm DE ALTURA. INCLUYE: RETIRO SIN RECUPERACIÓN DE BROCAL EXISTENTE, DEMOLICIONES, NIVELADO CON TABIQUE ROJO RECOCIDO 7X14X28, ASENTADO CON MORTERO CEMENTO-ARENA 1:3 DE 28 cm DE ESPESOR, APLANADO CON MORTERO CEMENTO-ARENA 1:3 , PLOMEADO, NIVELADO, DEMOLICIONES, CARGAS Y ACARREOS DENTRO DE LA OBRA, LIMPIEZAS Y TODO LO NECESARIO PARA SU CORRECTA EJECUCIÓN DEL CONCEPTO.	PZA	6.00	6.00		100.00	$2,854.62	$17,127.72	$17,127.72	

ANALISIS DEL PRESUPUESTO DE OBRA POR CONTRATO

No.	Concepto	Unid. Med.	Volumen			% Avanc. Estimado	Precio Contratado	Importe		
			Contratado	Acumulado	Excedente			Contratado	Acumulado	Excedente
GRUPO: SOBRECARPETA ASFALTICA										
PARTIDA: OBRA COMPLEMENTARIA										
21	CONSTRUCCION DE LOSA DE DIAMANTE DE CONCRETO MR= 45 , T.M.A. DE 3/4" (19MM), GRAVA TRITURADA, REVENIMIENTO DE 8+-2.5CM CM, FRAGUADO RAPIDOA A 3 DIAS, DE 25 CM DE ESPESOR, EN POZO DE VISITA, Y 1.50 M POR LADO, INCLUYE: SUMINISTRO DE MATERIALES, ESPUMA DE POLIURETANO DE ALTA DENSIDAD EN TODO EL PERIMETRO EXTERIOR DE 1/2" ASI COMO DE LAS JUNTAS DIAGONALES PARA FORMAR 4 PARTES, BROCAL Y TAPA DE Fo. Fo. TIPO PESADO, (165 KG), CIMBRADO, COLADO, VIBRADO, DESCIMBRADO, CURADO CON MEMBRANA QUIMICA BASE AGUA, APLANADO FINO EN RECEPCION DE BROCAL, CORTES CON CORTADORA DE DISCO DE 5 CM ENTRE JUNTAS DIAGONALES FORMADO 8 PIEZAS Y SELLADO DE JUNTAS Y CORTES CON MATERIAL PREFORMADO Y SELLADOR AUTONIVELANTE, MANO DE OBRA, ACARREOS DE MATERIAL DENTRO Y FUERA DE LA OBRA, TRABAJO TERMINADO. P.U.O.T.	PZA	6.00	6.00		100.00	$7,531.42	$45,188.52	$45,188.52	
24	LIMPIEZA Y DESASOLVE DE POZOS DE VISITA Y LINEAS DE ALCANTARILLADO EXISTENTE CON CAMION TIPO VACTOR. INCLUYE: RESANE INTERIOR DEL POZO Y REMTE DE POZO CO TUBO CON SELLADOR, FESTER Y MORTERO 1:3, MANO DE OBRA, SUMINISTRO DE AGUA EN PIPA, HERRAMIENTAS Y EQUIPO PARA SU CORRECTA EJECUCION, LIMPIEZAS, RENTA DE CAMION VACTOR HASTA LA CORRECTA LIMPIEZA DE LAS LINEAS EXISTENTES DE POZO A POZO, ASI COMO EL TRASLADO DE LOS DESECHOS HASTA TIRADERO AUTORIZADO MEDIDO POZO A POZO.	LOTE	4.00	6.00	2.00	150.00	$2,765.25	$11,061.00	$16,591.50	$5,530.50
							Totales por Partida:	$73,377.24	$78,907.74	$5,530.50
PARTIDA: LIMPIEZAS										
25	LIMPIEZA GENERAL DE LA OBRA, INCLUYE: BARRIDO, CARGA, ACARREOS Y RETIRO DE ESCOMBROS FUERA DE LA OBRA, TRABAJO TERMINADO.	M2	2,864.40	2,772.15		96.78	$4.35	$12,460.14	$12,058.85	
							Totales por Partida:	$12,460.14	$12,058.85	$0.00
							Totales por Grupo:	$1,485,952.37	$1,844,452.88	$663,773.07
GRUPO: GUARNICIONES Y BANQUETAS										
PARTIDA: GUARNICIONES										
26	EXCAVACION A MAQUINA Y/O A MANO EN MATERIAL TIPO II, EN SECO O PRESENCIA DE AGUA, INCLUYE. CORTE DE RAIZ DE CUALQUIER TAMAÑO Y GROSOR, HASTA UNA PROFUNDIDAD DE 40 CM DESPUES DE DESMONTE, DESPALME Y/O DEMOLICION DE SUPERFICIE O ELEMENTO ESTRUCTURAL O DE ACABADO, PROTECCION DE AREAS ADYACENTES, SIN DAÑAR AREAS ALEDAÑAS, CARGA Y ACARREO A TIRADERO OFICIAL, CONSERVACION DE LA MISMA, TRABAJO TERMINADO, LIMPIEZAS.	M3	3.13	3.13		100.00	$394.55	$1,234.94	$1,234.94	
27	COMPACTACION DE TERRENO NATURAL AL 90% DE SJ P.V.S.M EN SU COMPACTACION., INCLUYE ESCARIFICADO, TENDIDO, HOMOGENIZADO, HUMEDECIDO OPTIMO NIVELADO Y COMPACTADO EN CAPAS DE 20 CM, CALIDAD Límite líquido máximo 50%, Valor de Soporte California (CBR) mínimo 15%, Expansión máxima 5%, Grado de Compactación mínimo 90% ± 2, Y TODO LO NECESARIO PARA SU CORRECTA EJECUCION	M2	12.50	12.50		100.00	$26.40	$330.00	$330.00	
28	CONSTRUCCION DE GUARNICION RECTA Y/O CURVA TRAPEZOIDAL 15-20X40 CM DE SECCION CON CONCRETO PREMEZCLADO MR=38 KGF/CM2, R.N.REVENIMIENTO DE 8 A 10 CM, T.M.A. 3/4", GRAVA TRITURADA, ACABADO PULIDO EN PARTE DE SUPERIOR Y DOBLADOR EN ARISTAS, INCLUYE: COMPACTADO DE PLANTILLA, CIMBRADO, COLADO, VIBRADO, ACABADO, DESCIMBRADO, ALINEADO, NIVELADO, Y CURADO EN SU PARTE SUPERIOR CON MEMBRANA BASE AGUA A RAZON DE 1 LTO/M2, JUNTA DE AISLAMIENTO LONGITUDINAL AL COMBINAR CON OTRO ELEMENTO Y TRANSVERSAL @ 30 MT MAXIMO, SELLADO CON SELLADOR AUTONIVELANTE LONGITUDINAL, TRABAJO TERMINADO, .P.U.O.T.	ML	25.00	25.00		100.00	$164.71	$4,117.75	$4,117.75	
29	RELLENO COMPACTADO AL 95% CON MATERIAL DE BANCO EN CAPAS DE 20 CM UTILIZANDO BAILARINA. INCLUYE: SUMINISTRO DE TEPETATE (MATERIAL DE BANCO) EN LA OBRA, ABUNDAMIENTO, ACARREOS DENTRO DE LA OBRA, CRIBADO, RETIRO DE MATERIAL, MANO DE OBRA Y EQUIPO, LIMPIEZAS, TRABAJO TERMINADO.	M3	1.13	1.13		100.00	$428.23	$483.90	$483.90	

No.	Concepto	Unid. Med.	Volumen			% Avanc. Estimado	Precio Contratado	Importe		
			Contratado	Acumulado	Excedente			Contratado	Acumulado	Excecente
GRUPO: GUARNICIONES Y BANQUETAS										
PARTIDA: GUARNICIONES										
30	CARGA MECANICA Y ACARREO DE MATERIAL PRODUCTO DE EXCAVACION Y DEMOLICION EN CAMION DE VOLTEO AL 1er. KM, VOLUMEN MEDIDO COMPACTO.	M3	2.00	2.00		100.00	$42.56	$85.12	$85.12	
						Totales por Partida:		$6,251.71	$6,251.71	$0.00
						Totales por Grupo:		$6,251.71	$6,251.71	$0.00
GRUPO: SEÑALIZACION										
PARTIDA: SEÑALIZACION HORIZONTAL										
41	SUMINISTRO Y APLICACIÓN DE PINTURA EPOXICA BASE SOLVENTE COLOR AZUL (PANTONE 294) EN RAMPAS PARA PERSONAS CON DISCAPACIDAD CUALQUIER SECCIÓN SEGÚN PLANOS. INCLUYE: TRAZO, MANO DE OBRA, LIMPIEZA PREVIA DE SUPERFICIE, EQUIPO NECESARIO PARA SU EJECUCIÓN, Y TODO LO NECESARIO PARA SU CORRECTA EJECUCIÓN, TRABAJO TERMINADO.	M2	34.56	34.56		100.00	$441.62	$15 262.39	$15,262.39	
42	SUMINISTRO Y APLICACIÓN DE LOGOTIPO A (SILLA DE RUEDAS) EN PINTURA EPOXICA BASE SOLVENTE COLOR BLANCO EN RAMPAS PARA PERSONAS CON DISCAPACIDAD TAMAÑO Y DISEÑO SEGÚN PLANOS. INCLUYE: TRAZO, ENMASCARILLADO, PLANTILLA, MANO DE OBRA, LIMPIEZA PREVIA DE SUPERFICIE, EQUIPO NECESARIO PARA SU EJECUCIÓN, Y TODO LO NECESARIO PARA SU CORRECTA EJECUCIÓN, TRABAJO TERMINADO.	PZA	24.00	24.00		100.00	$245.32	$5 887.68	$5,887.68	
43	SUMINISTRO Y APLICACIÓN DE PINTURA BASE SOLVENTE PARA MARCAS EN GUARNICIONES CLASIFICACION M-12.1, M12.2 APLICADA SOBRE GUARNICIONES Y DENTELLONES DE CUALQUIER COLOR, SEGÚN SE REQUIERA Y SEGÚN NORMA S.C.T. SECADO AL TACTO EN 5 MIN Y AL DURO EN 30 MIN CON MICRO ESFERA , DESARROLLO DE 35 CM. INCLUYE: MATERIALES Y ESPECIFICACIONES QUE CUMPLAN CON LA NORMATIVA N-CMT-5-01-001/05, N-PRY-CAR-10-01-002/13 APLICADAS AL DIA DE HOY, TRAZO, MANO DE OBRA, LIMPIEZA PREVIA DE SUPERFICIE, EQUIPO NECESARIO PARA SU EJECUCIÓN, Y TODO LO NECESARIO PARA SU CORRECTA EJECUCIÓN TRABAJO TERMINADO.	ML	746.00	746.00		100.00	$50.37	$37 576.02	$37,576.02	
44	SUMINISTRO Y APLICACIÓN DE PINTURA TERMOPLASTICA ALQUIDALICA DE 120 MILESIMAS DE " (in) EN RAYA SEPARADORA DE SENTIDOS DE CIRCULACION CLASIFICACIÓN M - 1.1, LÍNEA CONTINUA SENCILLA DE DIVISIÓN DE CARRILES DE FRENTE EN PISO, DE 10 CM DE ANCHO, COLOR BLANCO Y/O AMARILLO CON MICRO ESFERA SEGÚN MANUAL DE SEÑALIZACIÓN VIAL Y DISPOSITIVOS DE SEGURIDAD SICT, SECADO AL TACTO EN 5 MIN Y AL CURO EN 30 MIN. INCLUYE: MATERIALES Y ESPECIFICACIONES QUE CUMPLAN CON LA NORMATIVA N-CMT-5-01-001/13, N-PRY-CAR-10-01-002/13 APLICADAS AL DIA DE HOY, MATERIAL APLICADO EN SU ESTADO DE FUSION A UNA TEMPERATURA MINIMA DE 204 C, LA SUPERFICIE DE CONCRETO O ASFALTO NO DEBE PRESENTAR UNA TEMPERATURA MENOR A LOS 10 C, ;TIEMPO DE SECADO EN RANGOS DE TEMPERATURA DE 10 C DEL SUSTRATO 2 MINUTOS, Y NO MAS DE 10 MINUTOS CUANDO EL SUSTRATO OSCILA ALREDEDOR DE 54C, TRAZO, ENMASCARILLADO, MANO DE OBRA, LIMPIEZA PREVIA Y FINAL DE SUPERFICIE, EQUIPO NECESARIO PARA SU EJECUCIÓN, Y TODO LO NECESARIO PARA SU CORRECTA EJECUCIÓN, TRABAJO TERMINADO.	ML	127.00	127.00		100.00	$55.35	$7 029.45	$7,029.45	
45	SUMINISTRO Y APLICACIÓN DE PINTURA TERMOPLASTICA ALQUIDALICA DE 120 MILESIMAS DE " (in) EN RAYA SEPARADORA DE SENTIDOS DE CIRCULACION CLASIFICACIÓN M - 1.2, RAYA DISCONTINUA SENCILLA, DE DIVISIÓN DE CARRILES PARA VELOCIDADES MENORES A 60 KM/HR DE FRENTE EN PISO, DESARROLLO DE 2.50 ML X 0.10 MTS DE ANCHO, CON UNA SEPARACIÓN DE 5.00 MTS ENTRE SI PROMEDIO, A BASE DE PINTURA PARA TRAFICO COLOR BLANCO CON MICRO ESFERA SEGÚN MANUAL DE SEÑALIZACIÓN VIAL Y DISPOSITIVOS DE SEGURIDAD SICT (S.C.T). INCLUYE: MATERIALES Y ESPECIFICACIONES QUE CUMPLAN CON LA NORMATIVA N-CMT-5-01-001/13, N-PRY-CAR-10-01-002/13 APLICADAS AL DIA DE HOY, MATERIAL APLICADO EN SU ESTADO DE FUSION A UNA TEMPERATURA MINIMA DE 204 C, LA SUPERFICIE DE CONCRETO O ASFALTO NO DEBE PRESENTAR UNA TEMPERATURA MENOR A LOS 10 C, ;TIEMPO DE SECADO EN RANGOS DE TEMPERATURA DE 10 C DEL SUSTRATO 2 MINUTOS, Y NO MAS DE 10 MINUTOS CUANDO EL SUSTRATO OSCILA ALREDEDOR DE 54C, TRAZO, ENMASCARILLADO, MANO DE OBRA, LIMPIEZA PREVIA Y FINAL DE SUPERFICIE, EQUIPO NECESARIO PARA SU EJECUCIÓN, Y TODO LO NECESARIO PARA SU CORRECTA EJECUCIÓN, TRABAJO TERMINADO.	ML	430.00	430.00		100.00	$55.35	$23 800.50	$23,800.50	

No.	Concepto	Unid. Med.	Volumen			% Avanc. Estimado	Precio Contratado	Importe		
			Contratado	Acumulado	Excedente			Contratado	Acumulado	Excedente
GRUPO: SEÑALIZACION										
PARTIDA: SEÑALIZACION HORIZONTAL										
46	SUMINISTRO Y APLICACIÓN DE PINTURA TERMOPLASTICA ALQUIDALICA DE 120 MILESIMAS DE " (in) EN RAYA EN LA ORILLA DEL ARROYO VIAL CLASIFICACIÓN M - 3.3, CONTINUA IZQUIERDA, PARA VIALIDADES URBANAS DE FRENTE EN PISO, DE 10 CM DE ANCHO Y SEPARADA 15 CM. DE LA GUARNICION, A BASE DE PINTURA PARA TRAFICO COLOR BLANCO CON MICRO ESFERA SEGÚN MANUAL DE SEÑALIZACIÓN VIAL Y DISPOSITIVOS DE SEGURIDAD SICT (S.C.T)., INCLUYE: MATERIALES Y ESPECIFICACIONES QUE CUMPLAN CON LA NORMATIVA N-CMT-5-01-001/13, N-PRY-CAR-10-01-002/13 APLICADAS AL DIA DE HOY, MATERIAL APLICADO EN SU ESTADO DE FUSION A UNA TEMPERATURA MINIMA DE 204 C, LA SUPERFICIE DE CONCRETO O ASFALTO NO DEBE PRESENTAR UNA TEMPERATURA MENOR A LOS 10 C, ;TIEMPO DE SECADO EN RANGOS DE TEMPERATURA DE 10 C DEL SUSTRATO 2 MINUTOS, Y NO MAS DE 10 MINUTOS CUANDO EL SUSTRATO OSCILA ALREDEDOR DE 54C, TRAZO, ENMASCARILLADO, MANO DE OBRA, LIMPIEZA PREVIA Y FINAL DE SUPERFICIE, EQUIPO NECESARIO PARA SU EJECUCIÓN, Y TODO LO NECESARIO PARA SU CORRECTA EJECUCIÓN, TRABAJO TERMINADO.	ML	296.00	296.00		100.00	$55.35	$16,383.60	$16,383.60	
47	SUMINISTRO Y APLICACIÓN DE PINTURA TERMOPLASTICA ALQUIDALICA DE 120 MILESIMAS DE " (in) EN RAYA PARA CRUCE PEATONAL CLASIFICACIÓN M - 7.1, PARA INDICAR " CRUCE PEATONAL EN VIAS PRIMARIAS", COLOR AMARILLO, REFLEJANTE CON MICRO ESFERA DE VIDRIO EN PROPORCION SEGÚN MANUAL DE SEÑALIZACIÓN VIAL Y DISPOSITIVOS DE SEGURIDAD SICT (S.C.T). DE 0.40 MTS DE ANCHO Y 3.5 MTS. DE LONGITUD POR EL ANCHO DE LA VIALIDAD, CON UNA SEPARACIÓN DE 0.40 MTS. ENTRE ELLAS, INCLUYE: MATERIALES Y ESPECIFICACIONES QUE CUMPLAN CON LA NORMATIVA N-CMT-5-01-001/13, N-PRY-CAR-10-01-002/13 APLICADAS AL DIA DE HOY, MATERIAL APLICADO EN SU ESTADO DE FUSION A UNA TEMPERATURA MINIMA DE 204 C, LA SUPERFICIE DE CONCRETO O ASFALTO NO DEBE PRESENTAR UNA TEMPERATURA MENOR A LOS 10 C, ;TIEMPO DE SECADO EN RANGOS DE TEMPERATURA DE 10 C DEL SUSTRATO 2 MINUTOS, Y NO MAS DE 10 MINUTOS CUANDO EL SUSTRATO OSCILA ALREDEDOR DE 54C, TRAZO, ENMASCAR_LADO, MANO DE OBRA, LIMPIEZA PREVIA Y FINAL DE SUPERFICIE, EQUIPO NECESARIO PARA SU EJECUCIÓN, Y TODO LO NECESARIO PARA SU CORRECTA EJECUCIÓN, TRABAJO TERMINADO.	M2	381.50	381.50		100.00	$461.21	$175,951.61	$175,951.61	
48	SUMINISTRO Y APLICACIÓN DE PINTURA TERMOPLASTICA ALQUIDALICA DE 120 MILESIMAS DE " (in) EN FLECHAS CLASIFICACIÓN M - 11.1, "FLECHA SENCILLA" PARA INDICAR SENTIDO DE CIRCULACIÓN , EN VIALIDADES PARA VELOCIDAD MENOR A 60KM POR HORA DIMENSION NORMATIVA SEGUN MANUAL DE SEÑALIZACIÓN VIAL Y DISPOSITIVOS DE SEGURIDAD SICT (SCT) Y/O (VER PLANO DE SEÑALAMIENTOS), COLOR BLANCO, REFLEJANTE CON MICRO ESFERA DE VIDRIO EN PROPORCIÓN SEGÚN NORMA SCT, INCLUYE: MATERIALES Y ESPECIFICACIONES QUE CUMPLAN CON LA NORMATIVA N-CMT-5-01-001/13, N-PRY-CAR-10-01-002/13 APLICADAS AL DIA DE HOY, MATERIAL APLICADO EN SU ESTADO DE FUSION A UNA TEMPERATURA MINIMA DE 204 C, LA SUPERFICIE DE CONCRETO O ASFALTO NO DEBE PRESENTAR UNA TEMPERATURA MENOR A LOS 10 C, ;TIEMPO DE SECADO EN RANGOS DE TEMPERATURA DE 10 C DEL SUSTRATO 2 MINUTOS, Y NO MAS DE 10 MINUTOS CUANDO EL SUSTRATO OSCILA ALREDEDOR DE 54C, TRAZO, ENMASCARILLADO, MANO DE OBRA, LIMPIEZA PREVIA Y FINAL DE SUPERFICIE, EQUIPO NECESARIO PARA SU EJECUCIÓN, Y TODO LO NECESARIO PARA SU CORRECTA EJECUCIÓN, TRABAJO TERMINADO.	PZA	19.00	19.00		100.00	$2,030.83	$38,585.77	$38,585.77	
49	SUMINISTRO Y APLICACIÓN DE PINTURA TERMOPLASTICA ALQUIDALICA DE 120 MILESIMAS DE " (in) EN FLECHAS CLASIFICACIÓN M - 11.1, " FLECHA CABEZA DOBLE" PARA INDICAR SENTIDO DE CIRCULACIÓN (VUELTA IZQUIERDA O DERECHA), EN VIALIDADES PARA VELOCIDAD MENOR A 60KM POR HORA SEGUN MANUAL DE SEÑALIZACIÓN VIAL Y DISPOSITIVOS DE SEGURIDAD SICT (SCT); (VER PLANO DE SEÑALAMIENTOS), EN COLOR BLANCO, REFLEJANTE CON MICRO ESFERA DE VIDRIO EN PROPORCIÓN SEGÚN NORMA SCT, INCLUYE: MATERIALES Y ESPECIFICACIONES QUE CUMPLAN CON LA NORMATIVA N-CMT-5-01-001/13, N-PRY-CAR-10-01-002/13 APLICADAS AL DIA DE HOY, MATERIAL APLICADO EN SU ESTADO DE FUSION A UNA TEMPERATURA MINIMA DE 204 C, LA SUPERFICIE DE CONCRETO O ASFALTO NO DEBE PRESENTAR UNA TEMPERATURA MENOR A LOS 10 C, ;TIEMPO DE SECADO EN RANGOS DE TEMPERATURA DE 10 C DEL SUSTRATO 2 MINUTOS, Y NO MAS DE 10 MINUTOS CUANDO EL SUSTRATO OSCILA ALREDEDOR DE 54C, TRAZO, ENMASCARILLADO, MANO DE OBRA, LIMPIEZA PREVIA Y FINAL DE SUPERFICIE, EQUIPO NECESARIO PARA SU EJECUCIÓN, Y TODO LO NECESARIO PARA SU CORRECTA EJECUCIÓN, TRABAJO TERMINADO.	PZA	9.00	9.00		100.00	$1,153.01	$10,377.09	$10,377.09	

No.	Concepto	Unid. Med.	Volumen			% Avanc. Estimado	Precio Contratado	Importe		
			Contratado	Acumulado	Excedente			Contratado	Acumulado	Excedente
GRUPO: SEÑALIZACION										
PARTIDA: SEÑALIZACION HORIZONTAL										
50	SUMINISTRO Y APLICACIÓN DE PINTURA TERMOPLASTICA ALQUIDALICA DE 120 MILESIMAS DE " (in) EN RAYA DE ALTO CLASIFICACIÓN M - 6, PARA INDICAR ALTO EN CRUCEROS, COLOR BLANCO, REFLEJANTE CON MICRO ESFERA DE VIDRIO EN PROPORCIÓN SEGÚN MANUAL DE SEÑALIZACIÓN VIAL Y DISPOSITIVOS DE SEGURIDAD SICT (S.C.T). DE 0.60 MTS DE ANCHO DE LONGITUD VARIABLE, INCLUYE: MATERIALES Y ESPECIFICACIONES QUE CUMPLAN CON LA NORMATIVA N-CMT-5-01-001/13, N-PRY-CAR-10-01-002/13 APLICADAS AL DIA DE HOY, MATERIAL APLICADO EN SU ESTADO DE FUSION A UNA TEMPERATURA MINIMA DE 204 C, LA SUPERFICIE DE CONCRETO O ASFALTO NO DEBE PRESENTAR UNA TEMPERATURA MENOR A LOS 10 C, ;TIEMPO DE SECADO EN RANGOS DE TEMPERATURA DE 10 C DEL SUSTRATO 2 MINUTOS, Y NO MAS DE 10 MINUTOS CUANDO EL SUSTRATO OSCILA ALREDEDOR DE 54C, TRAZO, ENMASCARILLADO, MANO DE OBRA, LIMPIEZA PREVIA Y FINAL DE SUPERFICIE, EQUIPO NECESARIO PARA SU EJECUCIÓN, Y TODO LO NECESARIO PARA SU CORRECTA EJECUCIÓN, TRABAJO TERMINADO.	ML	43.00	43.00		100.00	$279.24	$12,007.32	$12,007.32	
51	SUMINISTRO Y COLOCACION DE VIALETA STANDARD (S-200) DE 10X10CM. COLOR: CUERPO AMARILLO Y REFLEJANTE AMARILLO 1 CARA MARCA SEA O SIMILAR EN CALIDAD Y ESPECIFICACIONES DE FICHA TECNICA, ANCLADO EN PAVIMENTO SISTEMA DE SUJECION DE ALTO AGARRE BASE CUÑAS CON AB PEGAMENTO EPOXICO 50/50 RESISTENTE A ALTA TEMPERATURA (VER PLANO DE DETALLES DE SEÑALAMIENTOS HORIZONTAL Y VERTICAL). INCLUYE: TRAZO, ALINEACION, ELEVACION CUALQUIER ALTURA, TRABAJO TERMINADO, LIMPIEZAS.	PZA	60.00	60.00		100.00	$74.41	$4,464.60	$4,464.60	
52	SUMINISTRO Y COLOCACION DE VIALETA SOLAR DE 1CX10CM. COLOR: CUERPO ALUMINIO 3 LED DOS CARAS REFLEJANTES MARCA CREATIVAL VT-29 O SIMILAR EN CALIDAD Y ESPECIFICACIONES DE FICHA TÉCNICA, FIJADO EN PAVIMENTO CON SISTEMA DE SUJECIÓN DE ALTO AGARRE PEGAMENTO EPOXICO 100 A/B (RESINA EPÓXICA/RESINA POLIAMIDA MODIFICADA), RESISTENTE A ALTA TEMPERATURA (VER PLANO DE DETALLES DE SEÑALAMIENTOS HORIZONTAL), INCLUYE: LIMPIEZA PREVIA DE LA SUPERFICIE+C92, PREPARACIÓN DE LA SUPERFICIE, TRAZO, ALINEACIÓN, Y TODO LO NECESARIO PARA SU CORRECTA EJECUCIÓN, TRABAJO TERMINADO.	PZA	20.00	20.00		100.00	$188.42	$3,768.40	$3,768.40	
						Totales por Partida:		$351,094.43	$351,094.43	$0.00
						Totales por Grupo:		$351,094.43	$351,094.43	$0.00
						Total del Presupuesto		$0.00	$2,404,138.31	$712,244.90

H. AYUNTAMIENTO DE AGUASCALIENTES
SECRETARÍA DE OBRAS PÚBLICAS
DIRECCIÓN DE SUPERVISIÓN DE OBRA

H. AYUNTAMIENTO CONSTITUCIONAL DEL MUNICIPIO DE AGUASCALIENTES 2021-2024


Aguascalientes
LA CIUDAD DE TU VIDA


MEMORIA FOTOGRÁFICA


CBRA:	CONSTRUCCIÓN DE SOBRECARPETA ASFÁLTICA CALLE VALLADOLID, TRAMO: DE CALLE PETRÓLEOS MEXICANOS A CALLE BENJAMÍN DE LA MORA, COLONIA DEL CARMEN Y BARRIO DE GUADALUPE, AGUASCALIENTES Mpio.		
NO. DE CONTRATO:	FISMDF-0135-2022	CONTRATISTA:	ODZ ARQUITECTURA Y CONSTRUCCION S.A. DE C.V.

INICIO



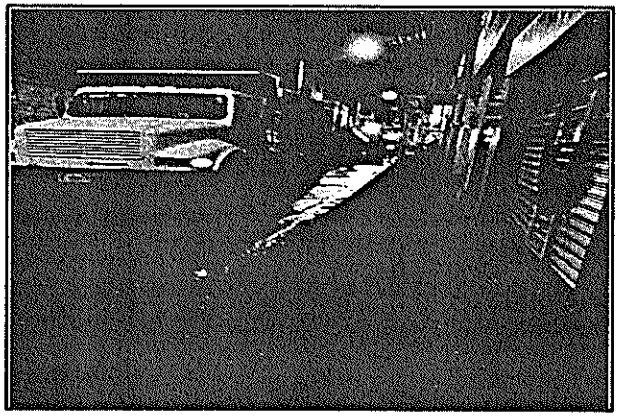

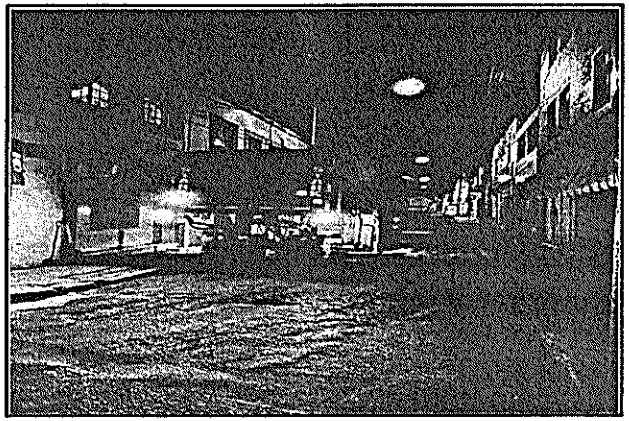

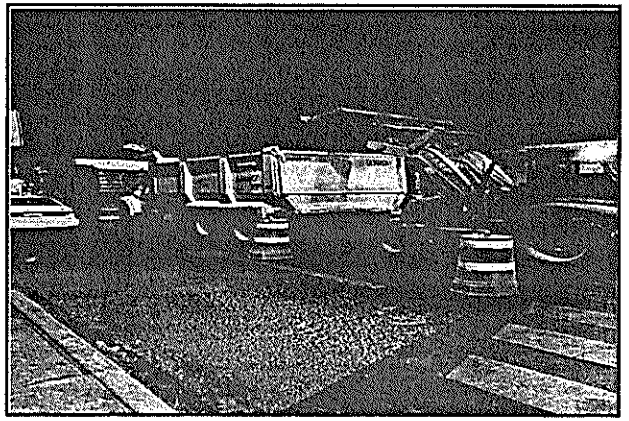

I.C. LAURA CECILIA MARTÍNEZ ALBA
RESIDENTE DE SUPERVISIÓN


H. AYUNTAMIENTO DE AGUASCALIENTES
SECRETARÍA DE OBRAS PÚBLICAS
DIRECCIÓN DE SUPERVISIÓN DE OBRA

Aguascalientes
LA CIUDAD DE TU VIDA

MEMORIA FOTOGRÁFICA

OBRA:	CONSTRUCCIÓN DE SOBRECARPETA ASFÁLTICA CALLE VALLADOLID, TRAMO: DE CALLE PETRÓLEOS MEXICANOS A CALLE BENJAMÍN DE LA MORA, COLONIA DEL CARMEN Y BARRIO DE GUADALUPE, AGUASCALIENTES Mpio.		
NO. DE CONTRATO:	FISMDF-0135-2022	CONTRATISTA:	ODZ ARQUITECTURA Y CONSTRUCCION S.A. DE C.V.

PROCESO

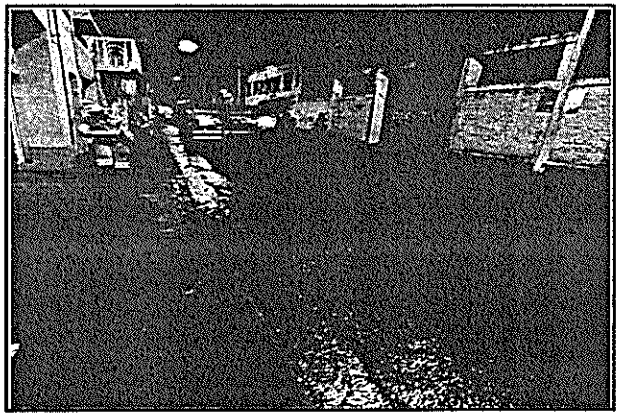







I.C. LAURA CECILIA MARTINEZ ALBA
RESIDENTE DE SUPERVISIÓN

H. AYUNTAMIENTO DE AGUASCALIENTES

SECRETARÍA DE OBRAS PÚBLICAS


DIRECCIÓN DE SUPERVISIÓN DE OBRA

Aguascalientes
LA CIUDAD DE TU VIDA


MEMORIA FOTOGRÁFICA


OBRA:	CONSTRUCCIÓN DE SOBRECARPETA ASFÁLTICA CALLE VALLADOLID, TRAMO: DE CALLE PETRÓLEOS MEXICANOS A CALLE BENJAMÍN DE LA MORA, COLONIA DEL CARMEN Y BARRIO DE GUADALUPE, AGUASCALIENTES Mpio.		
NO. DE CONTRATO:	FISMDF-0135-2022	CONTRATISTA:	ODZ ARQUITECTURA Y CONSTRUCCION S.A. DE C.V.

FINAL

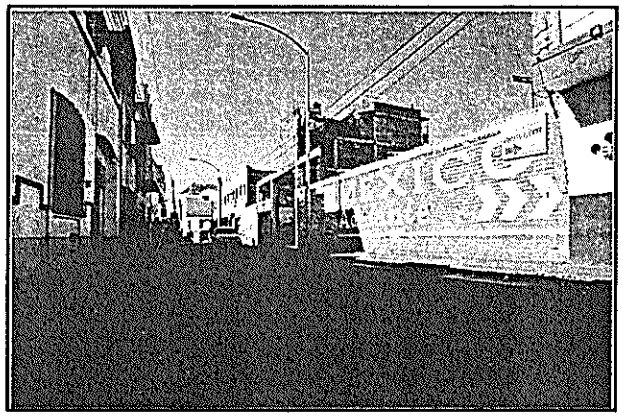



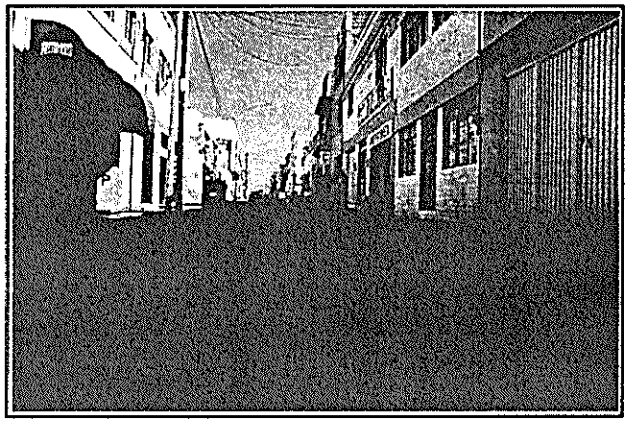

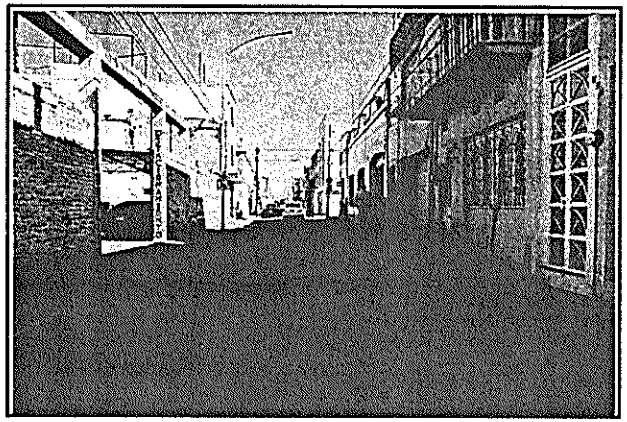

I.C. LAURA CECILIA MARTINEZ ALBA
RESIDENTE DE SUPERVISIÓN

EXPEDIENTE MODIFICADO

SECRETARÍA DE OBRAS PÚBLICAS

DIRECCIÓN DE SUPERVISIÓN DE OBRA

EJERCICIO: 2022

N° DE CONTRATO: FISMDF-0135-2022

NOMBRE DE LA OBRA: CONSTRUCCIÓN DE SOBRECARPETA ASFÁLTICA CALLE VALLADOLID, TRAMO: DE CALLE PETRÓLEOS MEXICANOS A CALLE BENJAMÍN DE LA MORA, COLONIA DEL CARMEN Y BARRIO DE GUADALUPE, AGUASCALIENTES Mpio.

MONTO MODIFICADO FINAL: $2,788,800.44


VOLUMEN	UNIDAD	COMPONENTE DE LA OBRA	MONTO
138.60	M3	FRESADO UNIFORME DE LA SUPERFICIE DE RODADURA EN PAVIMENTO	$ 202,339.29
56.40	M3	BACHEO PROFUNDO AISLADO UTILIZANDO MATERIAL CALIDAD BASE	$ 65,639.45
4473.16	M2	SUMINISTRO Y COLOCACION DE CONCRETO ASFALTICO EN CALIENTE	$ 1,687,846.84
6.00	PZA	CONSTRUCCION DE LOSA DE DIAMANTE DE CONCRETO MR= 45 , T.M.A.	$ 78,907.74
2772.15	M2	LIMPIEZA GENERAL DE LA OBRA, INCLUYE: BARRIDO, CARGA, ACARREOS	$ 12,058.85
25.00	ML	CONSTRUCCION DE GUARNICION RECTA Y/O CURVA TRAPEZOIDAL 15-	$ 6,251.71
381.50	M2	SUMINISTRO Y APLICACIÓN DE PINTURA TERMOPLASTICA ALQUIDALICA	$ 351,094.43


MONTO BASE: $ 2,404,138.31

IVA: $ 384,662.13

TOTAL: $ 2,788,800.44

I.C. Laura Cecilia Martínez Alba
RESIDENTE DE SUPERVISIÓN

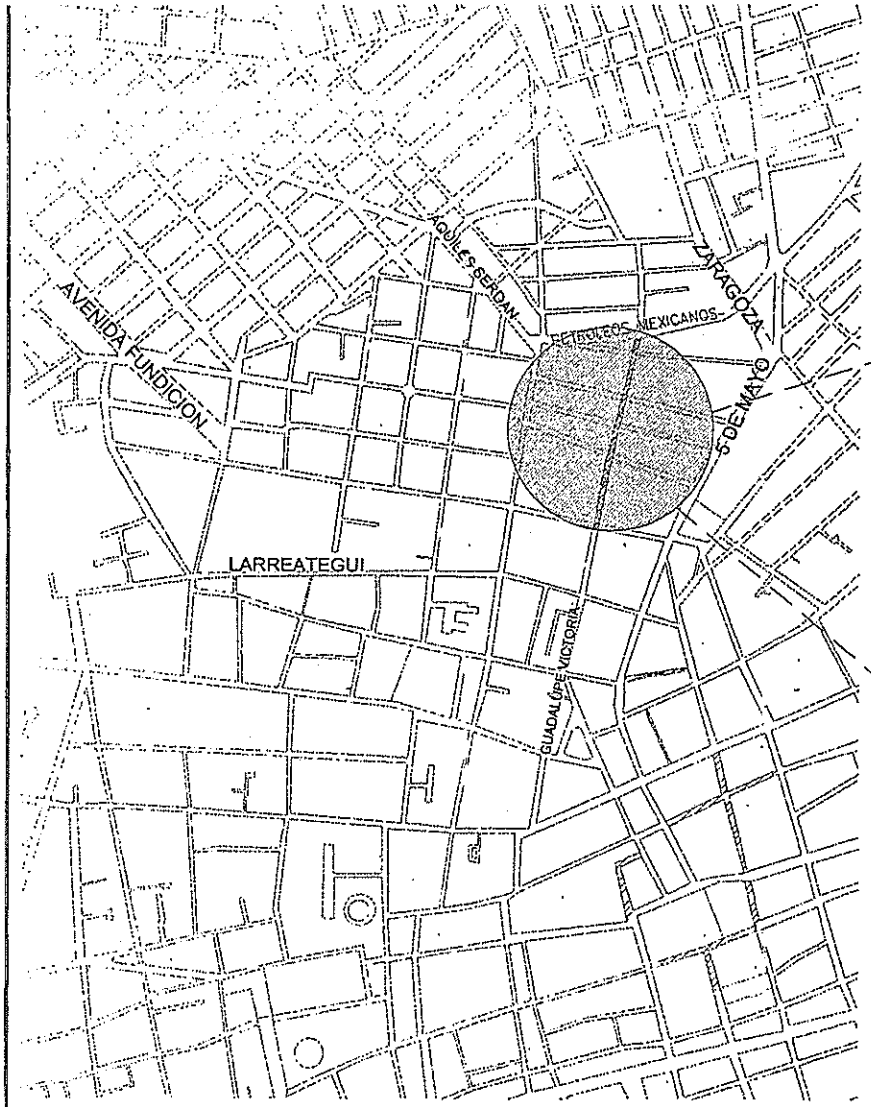

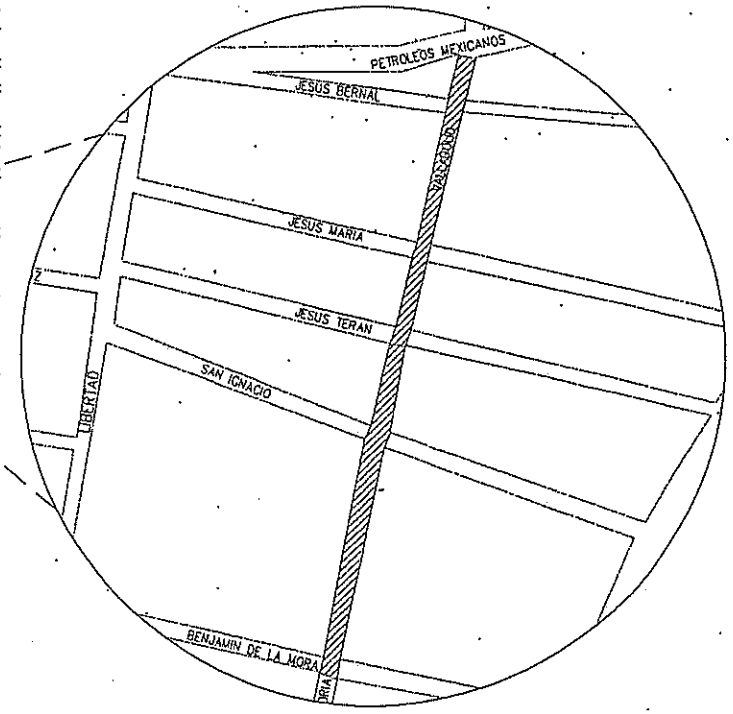



CROQUIS DE LOCALIZACIÓN

SIN ESCALA — CALLE VALLADOLID

TRAMO: DE C.PETRÓLEOS MEXICANOS A C. BENJÁMIN DE LA MORA

La Dirección de Planeación y Proyectos solo autoriza el proyecto ejecutivo, no es responsable de la correcta ejecución de la obra. Este documento no tiene validez si no presenta las firmas de los responsables para su autorización, así como los sellos respectivos.

PRESIDENTE MUNICIPAL
M.P.P. Leonardo Montañez Castro
SECRETARIO DE OBRAS PÚBLICAS
Ing. Miguel Ángel Huizar Botello

REV	FECHA	OBSERVACIONES

V°B°, DE LA DEPENDENCIA

RESP. DE PROY. EXTERNO		LOGO EXTERNO
CED. PROFESIONAL		
PROYECTÓ	REVISÓ	AUTORIZÓ


Dirección de Planeación y Proyectos de Obra — Secretaría de Obras Públicas

PROYECTISTA	COORDINADOR
ING. DIEGO RODRIGO AGUILERA	ARQ. IGNACIO JAIME LEAL
JEFE DE DEP.	DIRECTOR
LIC. OMAR LUJAN GARCÍA	ARQ. ALEJANDRO ROVELO IBARRA

PROYECTO: CONSTRUCCIÓN DE SOBRE CARPETA ASFÁLTICA
CALLE VALLADOLID
UBICACIÓN: TRAMO DE C. PETRÓLEOS MEXICANOS A C. BENJÁMIN DE LA MORA
CALLE VALLADOLID, ZONA CENTRO
CONTENIDO: PLANO DE LOCALIZACIÓN

CLAVE	No. PLANO
LOC 01	01
FECHA NOV 2022	ESCALA INDICADA
ACOTACIÓN METROS	No. EXP. E-000-22

Aguascalientes
LA CIUDAD DE TU VIDA

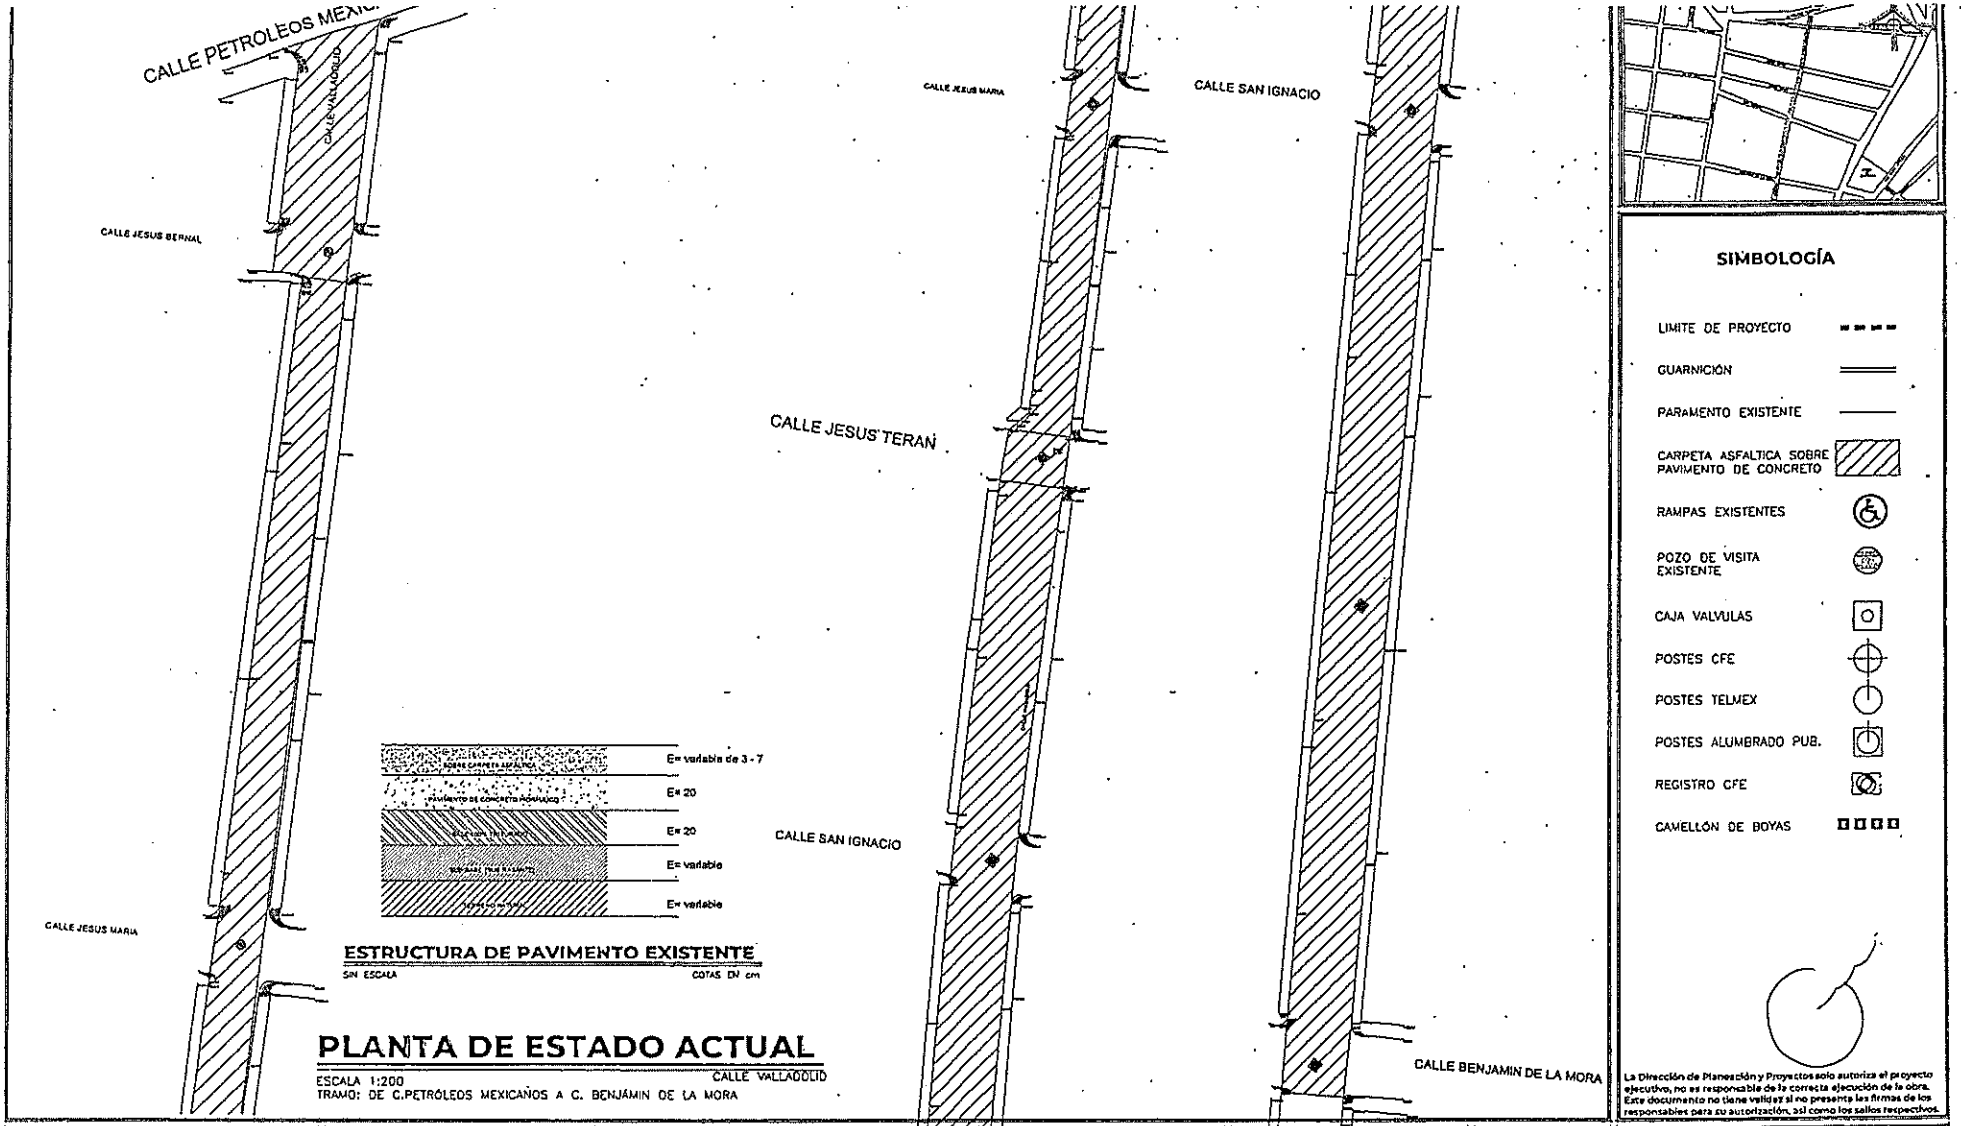

ESTRUCTURA DE PAVIMENTO EXISTENTE

SIN ESCALA — COTAS EN cm

PLANTA DE ESTADO ACTUAL

ESCALA 1:200 — CALLE VALLADOLID

TRAMO: DE C.PETROLEOS MEXICANOS A C. BENJAMÍN DE LA MORA

SIMBOLOGÍA

- LIMITE DE PROYECTO
- GUARNICIÓN
- PARAMENTO EXISTENTE
- CARPETA ASFALTICA SOBRE PAVIMENTO DE CONCRETO
- RAMPAS EXISTENTES
- POZO DE VISITA EXISTENTE
- CAJA VALVULAS
- POSTES CFE
- POSTES TELMEX
- POSTES ALUMBRADO PUB.
- REGISTRO CFE
- CAMELLÓN DE BOYAS

La Dirección de Planeación y Proyectos solo autoriza el proyecto ejecutivo, no es responsable de la correcta ejecución de la obra. Este documento no tiene validez si no presenta las firmas de los responsables para su autorización, así como los sellos respectivos.

PRESIDENTE MUNICIPAL
M.P.P. Leonardo Montañez Castro
SECRETARIO DE OBRAS PÚBLICAS
Ing. Miguel Ángel Huizar Botello

REV.	FECHA	OBSERVACIONES

Vo. Bo. DE LA DEPENDENCIA

RESP. DE PROY. EXTERNO		LOGO EXTERNO
GED. PROFESIONAL		
PROYECTÓ	REVISO	AUTORIZÓ

Dirección de Planeación y Proyectos de Obra — Secretaría de Obras Públicas

PROYECTISTA	COORDINADOR
ING. DIEGO ARTURO AGUILERA	ARQ. ALEJANDRO JUAN ELIAL
JEFE DE DEP.	DIRECTOR
LUCIANO JUAN GARCÍA	ARQ. ALEJANDRO JUAN ELIAL


PROYECTO: CONSTRUCCIÓN DE SOBRE CARPETA ASFÁLTICA CALLE VALLADOLID

UBICACIÓN: TRAMO DE C. PETRÓLEOS MEXICANOS A C. BENJAMÍN DE LA MORA, CALLE VALLADOLID, ZONA CENTRO

CONTENIDO: PLANTA DE ESTADO ACTUAL


CLAVE	No. PLANO
EA 02	02
FECHA NOV 2022	ESCALA INDICADA
ACOTACIÓN METROS	No. EXP. E-000-22

Aguascalientes
LA CIUDAD DE TU VIDA

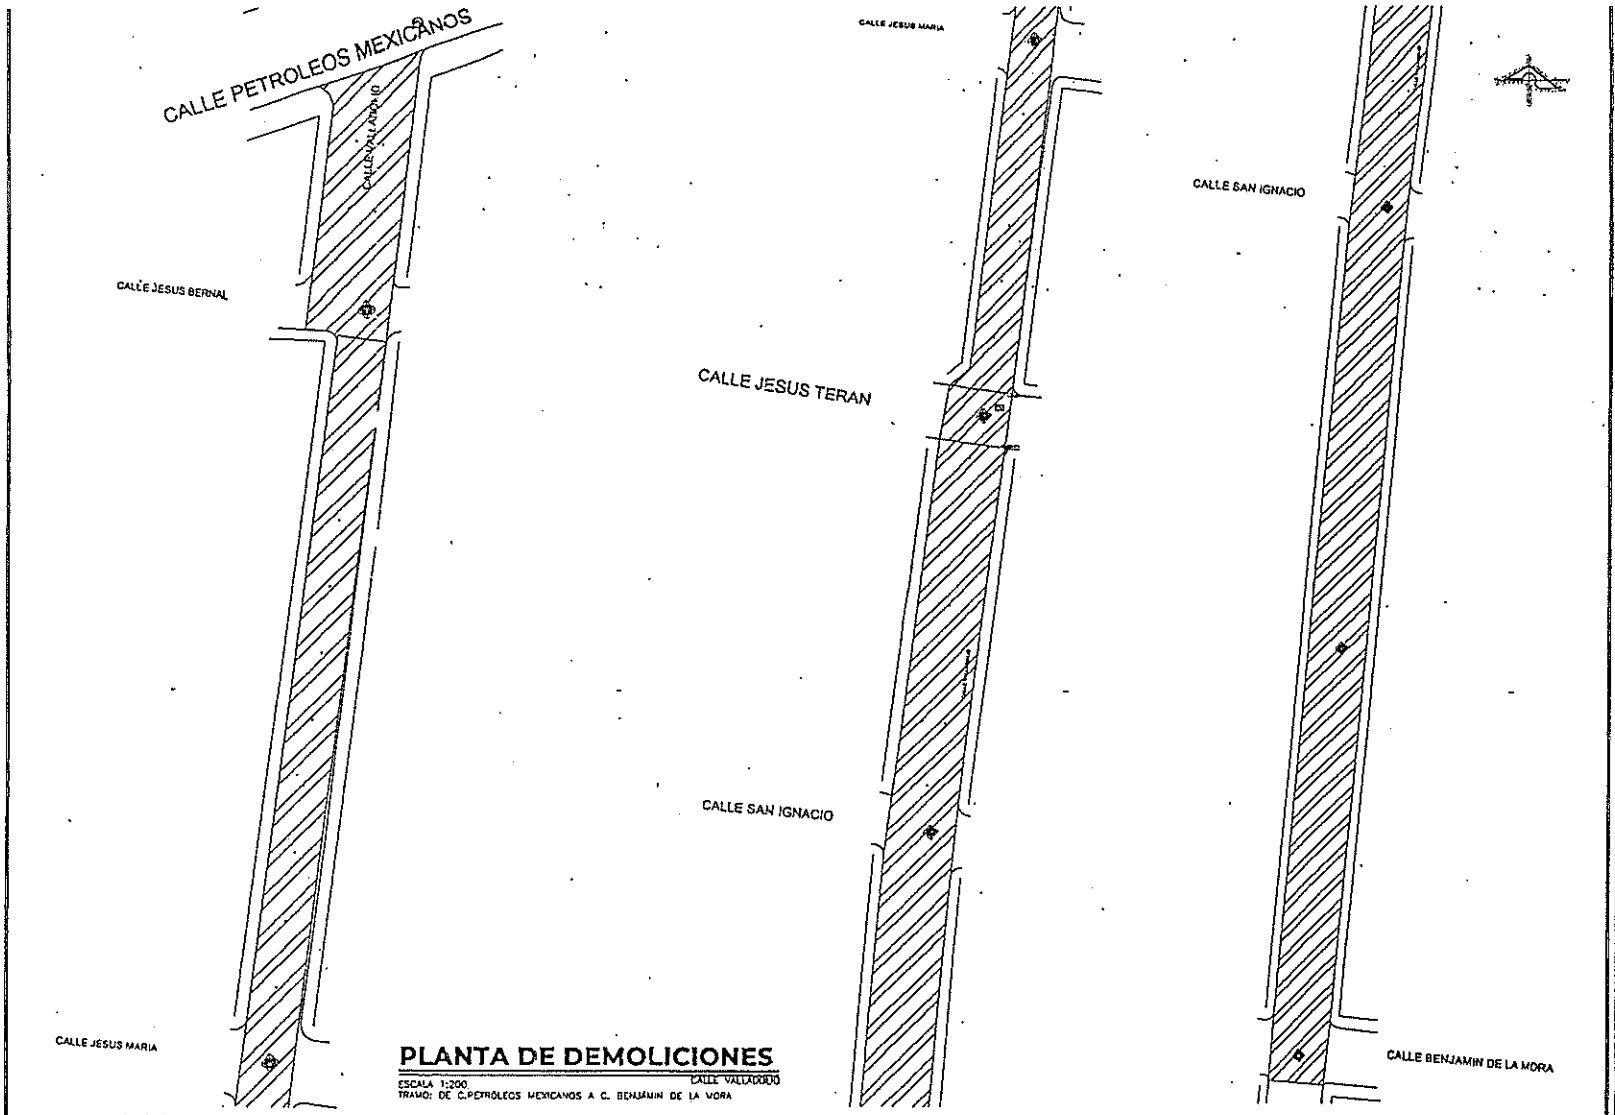

PLANTA DE DEMOLICIONES

ESCALA 1:200
TRAMO: DE C.PETRÓLEOS MEXICANOS A C. BENJAMIN DE LA MORA

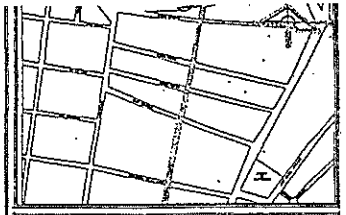

SIMBOLOGÍA

LIMITE DE PROYECTO

GUARNICIÓN

PARAMENTO EXISTENTE

FRESADO DE PAVIMENTO ASFALTICO

FRESADO UNIFORME DE LA SUPERFICIE DE RODADURA EN PAVIMENTOS DE CONCRETO ASFÁLTICO (3-7 CM DE ESPESOR PROMEDIO) , MEDIANTE FRESADORA EN FRIO COMPACTA, EQUIPADA CON BANDA TRANSPORTADORA PARA CARGA DIRECTA SOBRE CAMION DE VOLTEO, INCLUYE: TRAMO DE PRUEBA AL INICIO DEL FRESADO PARA AUTORIZACION DE SUPERVISION, (SUPERFICIE FRESADA UNIFORME Y SIN PROTUBERANCIAS) QUE CUMPLA CON LA NORMATIVA SCT N-CSV-CAR-3-02-006/20 APLICADAS AL DIA DE HOY, ACARREOS LOCALES, CARGA Y ACARREO A KM. SUBSECUENTES (11 A 15 KM APROX) DE MATERIAL PRODUCTO DEL FRESADO DE CARPETA ASFALTICA; EL TRASLADO SERA A PARQUE DE MAQUINARIA DE LA SOPMA, PIEZAS DE DESGASTE, COMBUSTIBLES, CONSUMIBLES, MANO DE OBRA, CUALQUIER VOLUMEN Y AREA, EQUIPO NECESARIO, LIMPIEZAS GRUESA Y FINA, TRABAJO TERMINADO.

NOTA:
LAS GUARNICIONES, BANQUETAS Y/O RAMPAS VEHICULARES A DEMOLER SERÁN INDICADAS EN SITIO A TRÁVES DEL ÁREA DE PROYECTOS Y SUPERVISIÓN, PARA RESPETAR LAS CANTIDADES QUE SE INDICAN EN CATÁLOGO.

La Dirección de Planeación y Proyectos solo autoriza el proyecto ejecutivo, no es responsable de la correcta ejecución de la obra. Este documento no tiene validez si no presenta las firmas de los responsables para su autorización, así como los sellos respectivos.

PRESIDENTE MUNICIPAL
M.P.P. Leonardo Montañez Castro
SECRETARIO DE OBRAS PÚBLICAS
Ing. Miguel Ángel Huizar Botello

REV.	FECHA	OBSERVACIONES


RESP. DE PROY. EXTERNO	LOGO EXTERNO
CED. PROFESIONAL	
PROYECTÓ / REVISÓ / AUTORIZÓ	


Dirección de Planeación y Proyectos de Obra | Secretaría de Obras Públicas
PROYECTISTA | COORDINADOR
ING. DIEGO ROJO AGUILERA / ARQ. ALEJANDRO JAIME LEAL
JEFE DE DEP. | DIRECTOR
LUCINA PULLEN GARCÍA / ARQ. ALEJANDRO PONCE NÚÑEZ

PROYECTO
CONSTRUCCIÓN DE SOBRE CARPETA ASFÁLTICA CALLE VALLADOLID
UBICACIÓN
TRAMO DE C. PETRÓLEOS MEXICANOS A C. BOGUIN DE LA MORA
CALLE VALLADOLID, ZONA CENTRO
CONTENIDO
PLANTA DE DEMOLICIONES

CLAVE	No. PLANO
DEM 01	03
FECHA: NOV 2022	ESCALA: INDICADA
ACOTACIÓN: METROS	No. EXP.: E-000-22

Aguascalientes
LA CIUDAD DE TU VIDA

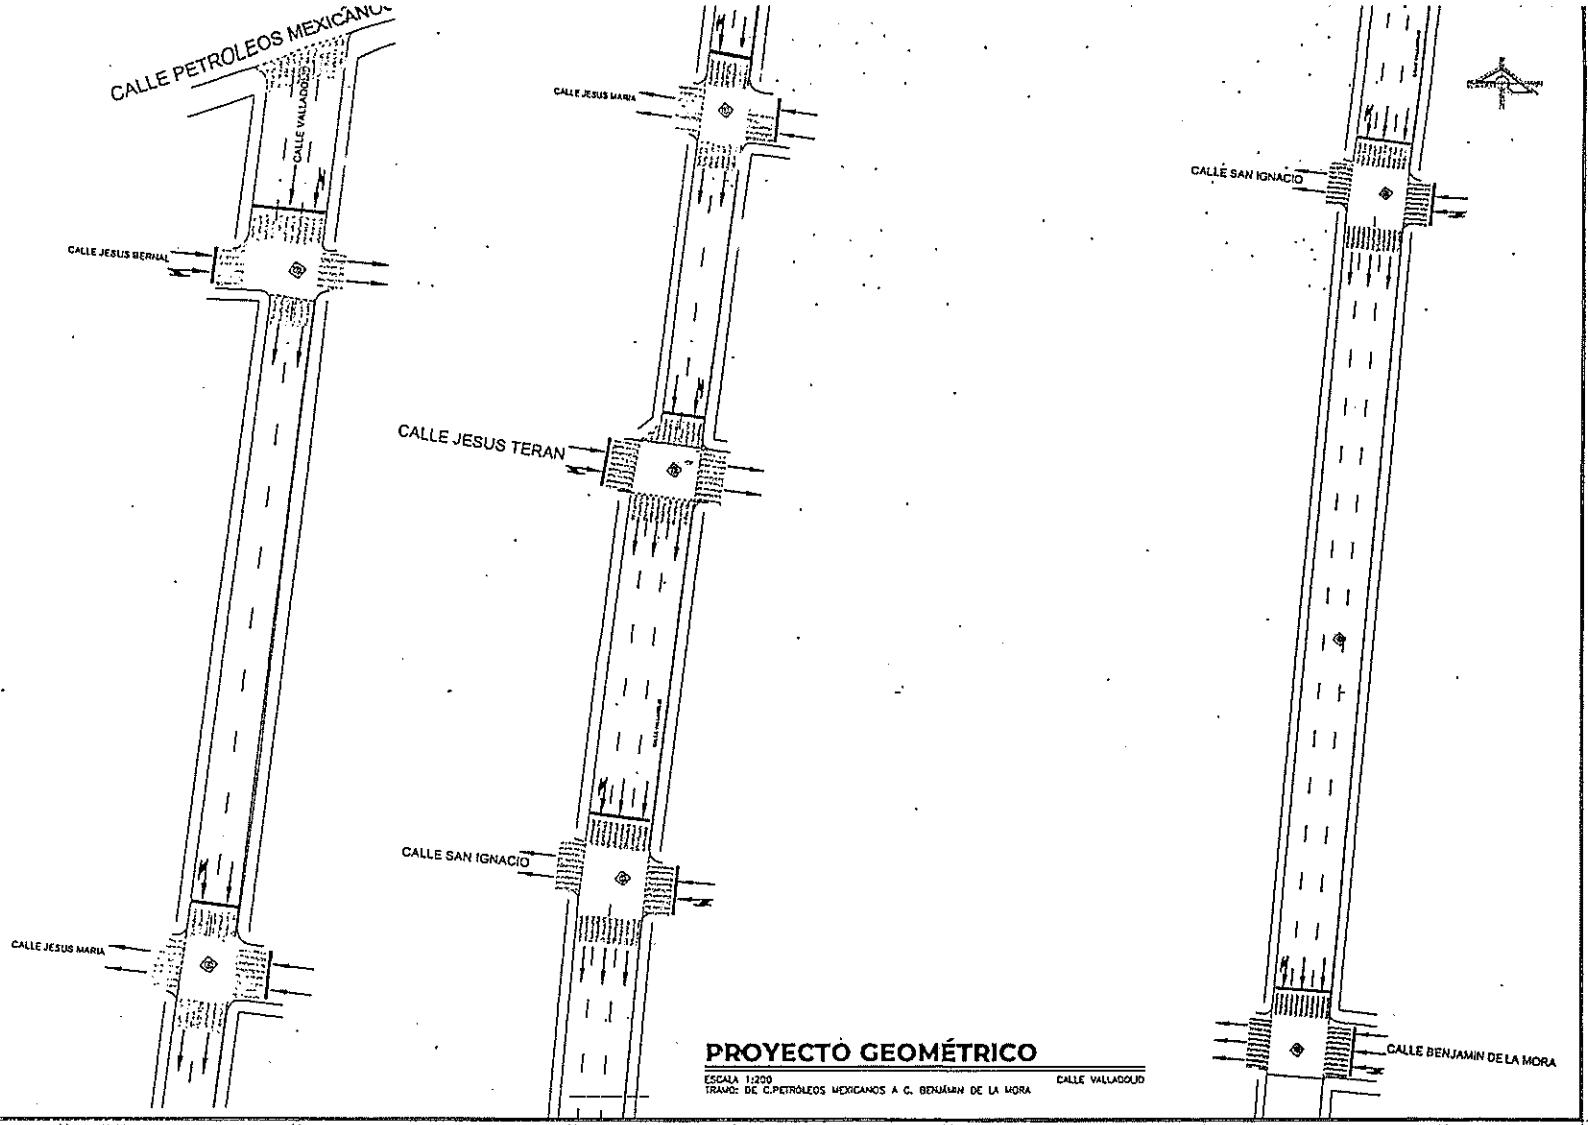

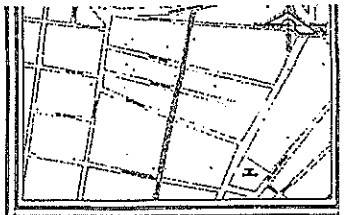

SIMBOLOGÍA

- LIMITE DE PROYECTO
- GUARNICIÓN
- PARAMENTO
- FLECHA DE SENTIDO M-11.1
- LINEAS AMARILLAS DE CRUCE PEATONAL M-7.1
- LINEA DE ALTO M-6
- POZO DE VISITA
- CAJA DE VALVULAS
- RAMPA DISCAPACITADOS
- VIALETA STANDARD (S-200)

PROYECTO GEOMÉTRICO

ESCALA 1:200
TRAMO: DE C.PETROLEOS MEXICANOS A C. BENJAMIN DE LA MORA

CALLE VALLADOLID

La Dirección de Planeación y Proyectos solo autoriza el proyecto ejecutivo, no es responsable de la correcta ejecución de la obra. Este documento no tiene validez si no presenta las firmas de los responsables para su autorización, así como los sellos respectivos.

PRESIDENTE MUNICIPAL
M.P.P. Leonardo Montañez Castro
SECRETARIO DE OBRAS PÚBLICAS
Ing. Miguel Ángel Huizar Botello

REV	FECHA	OBSERVACIONES

Vo. Bo. DE LA DEPENDENCIA

RESP. DE PROY. EXTERNO	LOGO EXTERNO
CED. PROFESIONAL	
PROYECTÓ / REVISÓ / AUTORIZÓ	


Dirección de Planeación y Proyectos de Obra — Secretaría de Obras Públicas

PROYECTISTA	COORDINADOR
M.G. DIEGO ROMO AGUILERA	ARQ. ALEJANDRO JULIO TEAL
JEFE DE DEP.	DIRECTOR
LIC. LUIS LUIAN GARCÍA	ARQ. ALEJANDRO PEREZ DIAZ

PROYECTO
CONSTRUCCIÓN DE SOBRE CARPETA ASFÁLTICA
CALLE VALLADOLID
UBICACIÓN
TRAMO DE C. PETRÓLEOS MEXICANOS A C. BENJAMÍN DE LA MORA
CALLE VALLADOLID, ZONA CENTRO
CONTENIDO
PROYECTO GEOMÉTRICO
SEÑALIZACIÓN HORIZONTAL

CLAVE	No. PLANO
PG 01	04
FECHA NOV 2022	ESCALA INDICADA
ACOTACIÓN METROS	No. EXP. E-000-22

Aguascalientes
LA CIUDAD DE TU VIDA

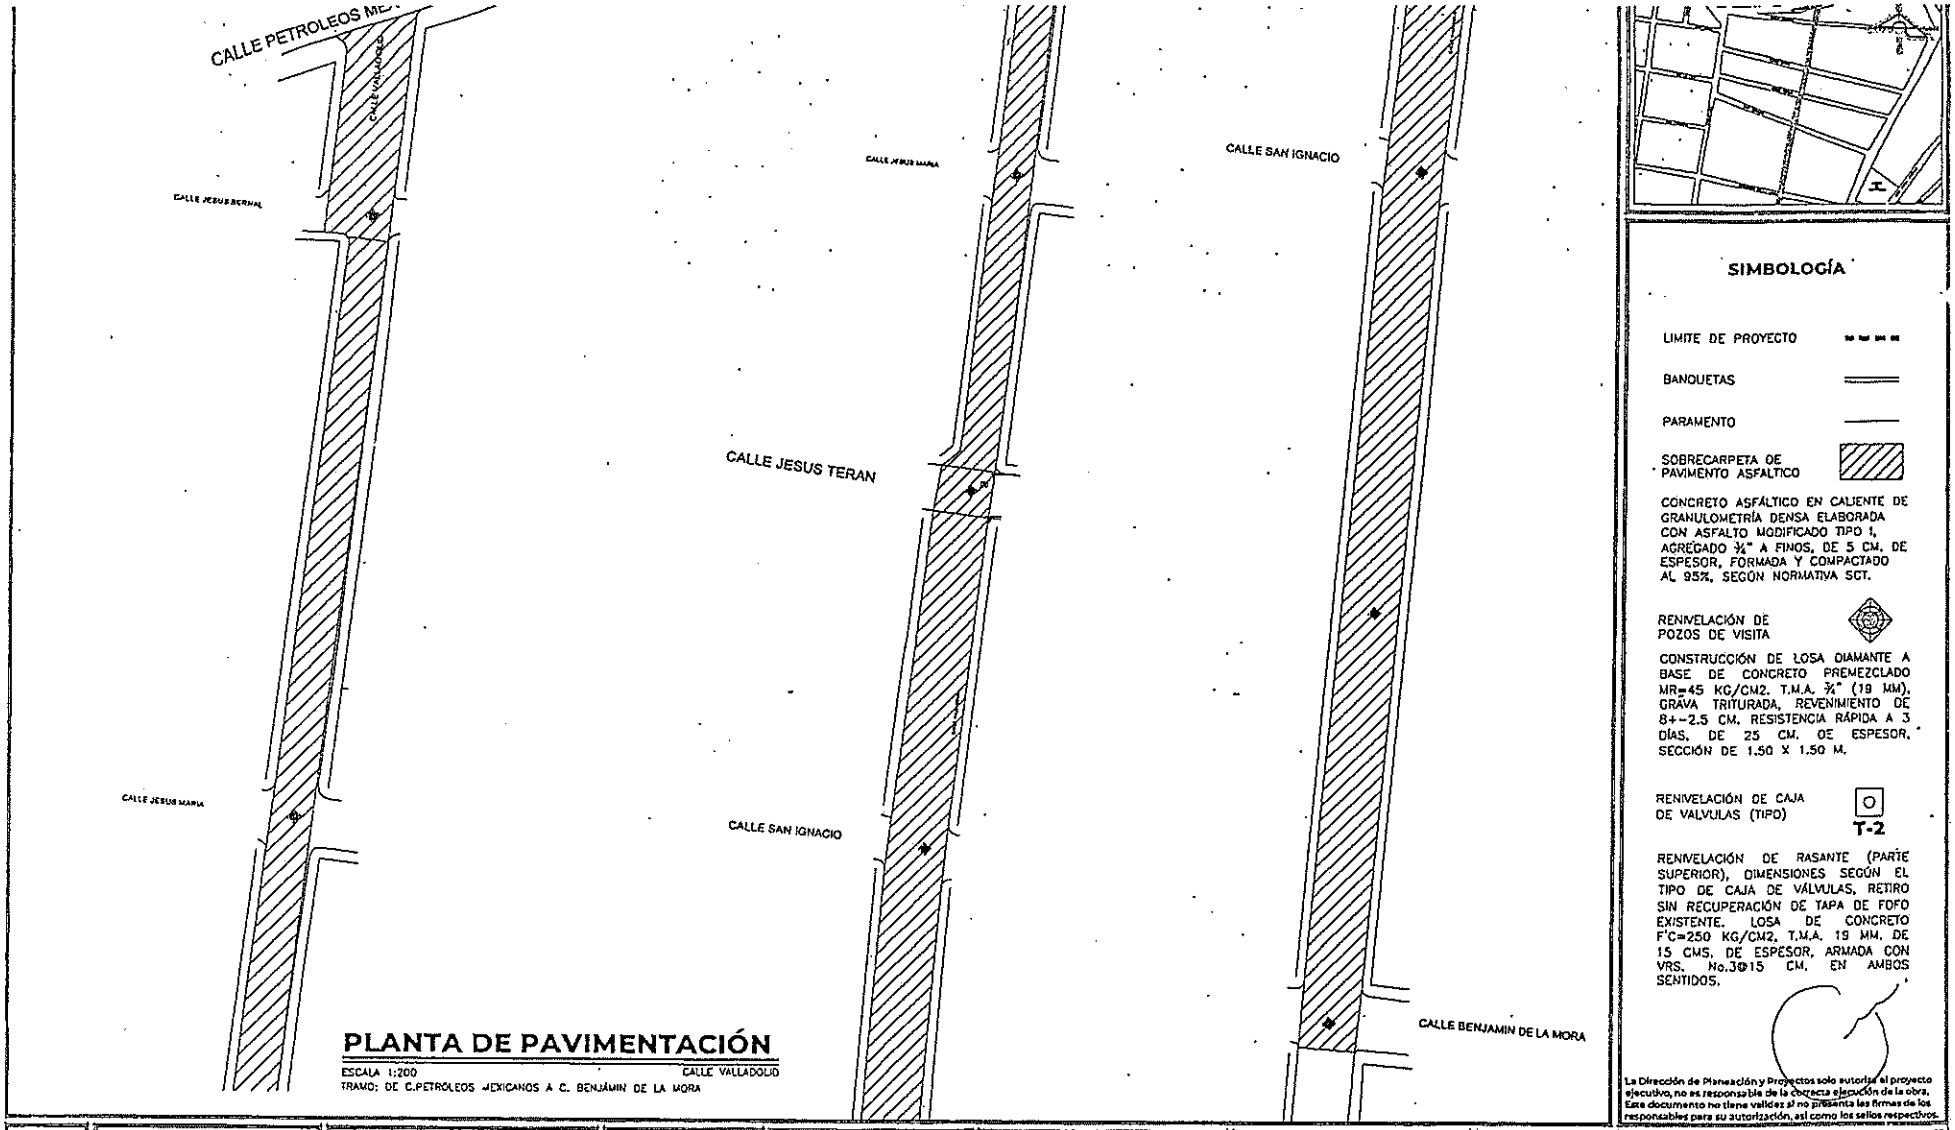

PLANTA DE PAVIMENTACIÓN

ESCALA 1:200

TRAMO: DE C.PETROLEOS MEXICANOS A C. BENJÁMIN DE LA MORA

SIMBOLOGÍA

LIMITE DE PROYECTO

BANQUETAS

PARAMENTO

SOBRECARPETA DE PAVIMENTO ASFALTICO

CONCRETO ASFÁLTICO EN CALIENTE DE GRANULOMETRÍA DENSA ELABORADA CON ASFALTO MODIFICADO TIPO I, AGREGADO ¾" A FINOS, DE 5 CM. DE ESPESOR, FORMADA Y COMPACTADO AL 95%, SEGÚN NORMATIVA SCT.

RENIVELACIÓN DE POZOS DE VISITA

CONSTRUCCIÓN DE LOSA DIAMANTE A BASE DE CONCRETO PREMEZCLADO MR=45 KG/CM2. T.M.A. ¾" (19 MM), GRAVA TRITURADA, REVENIMIENTO DE 8+-2.5 CM. RESISTENCIA RÁPIDA A 3 DÍAS, DE 25 CM. DE ESPESOR, SECCIÓN DE 1.50 X 1.50 M.

RENIVELACIÓN DE CAJA DE VALVULAS (TIPO) T-2

RENIVELACIÓN DE RASANTE (PARTE SUPERIOR), DIMENSIONES SEGÚN EL TIPO DE CAJA DE VÁLVULAS, RETIRO SIN RECUPERACIÓN DE TAPA DE FOFO EXISTENTE. LOSA DE CONCRETO F'C=250 KG/CM2. T.M.A. 19 MM. DE 15 CMS. DE ESPESOR, ARMADA CON VRS. No.3@15 CM. EN AMBOS SENTIDOS.

La Dirección de Planeación y Proyectos solo autoriza el proyecto ejecutivo, no es responsable de la correcta ejecución de la obra. Este documento no tiene validez si no presenta las firmas de los responsables para su autorización, así como los sellos respectivos.

PRESIDENTE MUNICIPAL
M.P.P. Leonardo Montañez Castro
SECRETARIO DE OBRAS PÚBLICAS
Ing. Miguel Ángel Huizar Botello

REV.	FECHA	OBSERVACIONES

V°B° DE LA DEPENDENCIA

RESP. DE PROY. EXTERNO	LOGO EXTERNO
CED. PROFESIONAL	
PROYECTÓ / REVISO / AUTORIZÓ	

Dirección de Planeación y Proyectos de Obra — Secretaría de Obras Públicas

PROYECTISTA	COORDINADOR
ING. DIEGO ERICK AGUILERA	ARQ. ALEJANDRO JAIME LEAL
JEFE DE RED	DIRECTOR
LUCIA MATILDE GARCÍA	ARQ. ALEJANDRO JAIME LEAL

PROYECTO: CONSTRUCCIÓN DE SOBRE CARPETA ASFÁLTICA CALLE VALLADOLID

UBICACIÓN: TRAMO DE C. PETRÓLEOS MEXICANOS A C. BENJÁMIN DE LA MORA — CALLE VALLADOLID, ZONA CENTRO

CONTENIDO: PLANTA DE PAVIMENTACIONES

CLAVE	No. PLANO
PAV 01	05
FECHA: NOV 2022	ESCALA: INDICADA
ACOTACIÓN: METROS	No. EXP.: E-000-22

Aguascalientes
LA CIUDAD DE TU VIDA