Aguascalientes
LA CIUDAD DE TU VIDA

Dirección de Programación Presupuestal
Núm. Oficio AMPP/0392/22
Aguascalientes, Ags. 26 de Septiembre del 2022
Asunto: Validación de Expediente Técnico

C.P. SERGIO ARTURO LOZANO GONZÁLEZ
SECRETARIO DE FINANZAS MUNICIPALES
P R E S E N T E

Con fundamento en los artículos 17 fracción XV, 60 fracción XVI y 76 fracción VI del Reglamento del Sistema Integral de Desarrollo Municipal y del Instituto Municipal de Planeación y Evaluación de Aguascalientes, hago referencia al oficio **SOPMA/2063/2022** recibido por este Instituto el día 21 de Septiembre del 2022 por parte de la **Secretaría de Obras Públicas**, mediante el cual remiten el expediente técnico original de la siguiente obra para su análisis, registro y priorización, conforme al Programa Anual de Obra Pública y Programas Sociales para el ejercicio presupuestal 2022:

DEPENDENCIA EJECUTORA:	SECRETARÍA DE OBRAS PÚBLICAS
NOMBRE DE LA OBRA O PROYECTO:	OBRA COMPLEMENTARIA Y SEÑALIZACIÓN
UBICACIÓN:	AV DE LA CONVENCIÓN 1914 SUR, ENTRE CALLE IGNACIO T. CHÁVEZ Y CALLE REPÚBLICA DE URUGUAY, VARIAS COLONIAS, AGUASCALIENTES, AGS.
FONDO DE INVERSIÓN:	PROGRAMA DIRECTO MUNICIPAL
IMPORTE:	$1,061,931.32 (ET FINAL)
No. DE OBRA:	2022-PDM-0050-UR-05-03
MODALIDAD DE EJECUCIÓN:	CONTRATO
EJE:	MUNICIPIO SOBRESALIENTE
ESTRATEGIA:	OBRA PÚBLICA INTELIGENTE
POLITICA:	5.8.1.REHABILITACIÓN Y MANTENIMIENTO VIALIDADES, CAMINOS, CALLES, ÁREAS DE TERRACERÍA Y CAUCES (COM.

Al respecto, hago de su conocimiento que dicho expediente ha sido analizado en su integración técnica y documental, con base en el artículo 168 fracción I del Reglamento de la Ley de Obras Públicas y Servicios Relacionados para el Estado de Aguascalientes y sus Municipios.

Asimismo, le comento que este Instituto valida dicha obra acorde a lo establecido en los artículos 14, 22 párrafo segundo y 23 de la Ley de Obras Públicas y Servicios Relacionados para el Estado de Aguascalientes y sus Municipios, la cual se encuentra alineada al Plan de Desarrollo Municipal vigente, para dar cumplimiento a las metas establecidas en el mismo.

Cabe hacer mención que los recursos solicitados para este proyecto de inversión, estarán sujetos a la disponibilidad presupuestal para el presente ejercicio fiscal que determine la Secretaría a su digno cargo. Sin otro particular por el momento, le envío un cordial saludo.

A T E N T A M E N T E

DR. en A.P. GUILLERMO DE LA TORRE SIFUENTES
DIRECTOR GENERAL

CAAR / JDBC
C.c.p. I.C. Arq. Gloria Guadalupe Castillo González .- Secretaría de Obras Públicas. Para su conocimiento.
C.c.p. Archivo.

Instituto Municipal de Planeación y Evaluación de Aguascalientes

Antonio Acevedo Escobedo 103 A. Col. Centro
Aguascalientes, Ags. C.P. 20000

(449) 9101010 Ext. 3117

www.implanags.gob.mx

GOBIERNO MUNICIPAL DE AGUASCALIENTES

INSTITUTO MUNICIPAL DE PLANEACION

IMPLAN

ANÁLISIS INTEGRAL DE EXPEDIENTE TÉCNICO

No. DE OBRA (PAOP 2020):	2022-PDM-0050-UR-05-03	REGISTRO No.	217
OFICIO DE VALIDACIÓN:	AMPP/0392/22	FECHA RECIBIDO PARA REVISIÓN:	26 de Septiembre del 2022
PROGRAMA:	URBANIZACIÓN	LOCALIDAD O COLONIA:	VARIAS COLONIAS
SUB-PROGRAMA:	Vialidades Urbanas (Construcción, Ampliación y Rehabilitación)	DELEGACIÓN:	Aguascalientes
DEPENDENCIA:	Secretaría de Obras Públicas	MOD. DE EJECUCIÓN:	CONTRATO
NOMBRE DE LA OBRA:	OBRA COMPLEMENTARIA Y SEÑALIZACIÓN, AV DE LA CONVENCIÓN 1914 SUR, ENTRE CALLE IGNACIO T. CHÁVEZ Y CALLE REPÚBLICA DE URUGUAY		
FUENTE DE FINANCIAMIENTO:	PROGRAMA DIRECTO MUNICIPAL, PDM		
INVERSIÓN:	$1,061,931.32	CLASIFICACIÓN DE OBRA:	BIENES DE DOMINIO PUBLICA

TOTAL	FEDERAL	ESTATAL	MUNICIPAL	BENEFICIARIOS	OTROS	DIFERENCIA ENTRE MOD.
$1,061,931.32	0.00	0.00	$1,061,931.32	0.00	0.00	*$53.813,21*

TIPO DE EXPENDIENTE:	ET FINAL	AÑO: 2022	AÑO:	AÑO:		
AVANCES:	Financiero: 74 %	Físico: 100 %				
FECHA DE INICIO:	11 de Junio del 2022	FECHA DE TÉRMINO:	10 de Julio del 2022	REGISTRO SIMA:	50	

CHEK LIST DE LOS ANEXOS DEL EXPEDIENTE TÉCNICO

CÉDULA DE REGISTRO DE OBRA	✓
DICTAMEN DE FACTIBILIDAD	✓
MEMORIA DESCRIPTIVA	✓
PRESUPUESTO BASE	✓
FACTIBILIDAD VERIFICADA EN CAMPO	✓
CROQUIS DE UBICACIÓN (MACRO)	✓
CROQUIS DE UBICACIÓN (MACRO)	✓
PROGRAMA DE OBRA Y MONTOS MENSUALES	✓
PLANOS O ESTUDIOS TÉCNICOS	✓
PADRÓN DE BENEFICIARIOS	N/A
ACTA DE ACEPTACIÓN DEL PROYECTO	N/A
DICTAMEN DE IMPACTO AMBIENTAL	N/A
CONVENIO DE CONCERTACIÓN	N/A
ACTA CONSTITUTIVA	N/A

METAS		BENEFICIARIOS		PERIODO DE EJECUCION		OBRA PROPUESTA		CLAVE SISCO
UNIDAD DE MEDIDA	CANT	TIPO DE BENEFICIARIOS	CANTIDAD	FECHA DE INICIO	FECHA DE TERMINO	CONCEPTO	JORNALES A GENERAR	
OBRA	1	Personas	450	2022-06-11	2022-07-10	Sobrecarpeta Asfáltica	2761	2325

INCLUIDO EN PLAN DE DESARROLLO MUNICIPAL Y EL PROGRAMA ANUAL DE OBRA PÚBLICA

OBSERVACIONES:

SIN OBSERVACIONES

RECIBIO: ING. JOSÉ DAVID BURGUETE CLAUSTRO
Analista de Programación e Inversión de Obra Pública

26 de Septiembre del 2022
Fecha de validación

26 de Septiembre del 2022
Fecha de validación Expediente

PROCEDE Si ✓ No

H. AYUNTAMIENTO CONSTITUCIONAL DEL MUNICIPIO DE AGUASCALIENTES 2021-2024

AYUNTAMIENTO DE AGUASCALIENTES

CEDULA DE REGISTRO POR OBRA

Aguascalientes

050400-001E00E05-05-2-2-1-00-1-E-0510-0-17-0050-21-1501-6144

2022-PDM-0050-UR-05-005	Obra **OBRA COMPLEMENTARIA Y SEÑALIZACIÓN AV. CONVENCIÓN 1914 SUR**
Tipo DEFINITIVO 1 2022 Folio SISCO **2325**	Ubic. TRAMO: ENTRE AV. IGNACIO T. CHÁVEZ Y CALLE REPÚBLICA DE URUGUAY, AGUASCALIENTES Mpio.

Ent. Ejecutora : **050400001E00E05**

Eje: **05**	MUNICIPIO SOBRESALIENTE
Finalidad: **2**	DESARROLLO SOCIAL
Función: **2**	VIVIENDA Y SERVICIOS A LA COMUNIDAD
Subfunción: **1**	URBANIZACIÓN
Tema: **00**	SIN TEMA
Cuenta del Gasto **1**	GASTO PROGRAMABLE
Clasif. Programatica: **E**	PRESTACIÓN DE SERVICIOS PÚBLICOS
Programa: **0510**	Movilidad Urbana
SubPrograma: **0**	SUBPROGRAMA GENÉRICO
Proyecto: **17**	
Tipo de Gasto: **21**	GASTO INVERSIÓN / OBRA PÚBLICA

INVERSION 2022

Municipal	1501	FONDO GENERAL DE PARTICIPACIONES 2022	$1,061,931.32
		Folio SIMA 50 Total	$1,061,931.32

METAS

Unidad de Medida	Cantidad	Descripción
OBRA	1	OBRA OBRA COMPLEMENTARIA Y SEÑALIZACIÓN AV. CONVENCIÓN 1914 SUR

Inversión Ejercida Total al	31 de Diciembre de 2021	$0.00
Avance Fisico Acumulado al	31 de Diciembre de 2021	
Avance Fisico Acumulado Programado al	31 de Diciembre de 2022	100 %

Fecha de Inicio 11 Jun 2022 Fecha de Terminación 10 Jul 2022

Jornales a Generar en 2022 2761

Modalidad de ejecución CONTRATO

Clasificación de la Obra Bienes de Dominio Público

Registro del Patrimonio: Obras del dominio público

OBRAS PÚBLICAS

Av. Aguascalientes Sur No. 2615
Fracc. Jardines de las Fuentes,
Aguascalientes, Ags. C.P. 20278

(449) 9 78 92 01, 06, 09

www.ags.gob.mx

GENERALES

Nombre del Proyecto : OBRA COMPLEMENTARIA Y SEÑALIZACIÓN AV. CONVENCIÓN 1914 SUR

TRAMO: ENTRE AV. IGNACIO T. CHÁVEZ Y CALLE REPÚBLICA DE URUGUAY, AGUASCALIENTES Mpio.

Programa : UR URBANIZACIÓN

Subprograma : 05 VIALIDADES URBANAS (CONSTRUCCION, AMPLIACION Y REHABILITACION) (c).- Semáforos, Señalización y Sincronización (señales, placas, nomenclatura, pintura y otras))

Clave del Municipio : AGUASCALIENTES

Localidad :

Barrio, Colonia o Ejido : AGUASCALIENTES Mpio.

Tipo de Obra : NUEVA

DESCRIPCIÓN DEL PROYECTO:

OBRA COMPLEMENTARIA Y SEÑALIZACIÓN AV. CONVENCIÓN 1914 SUR 1.00 OBRA

Beneficiarios (No. y Tipo) :

450	PERSONAS

OBRAS PÚBLICAS

Los abajo firmantes, hacen constar que el presente proyecto :

OBRA COMPLEMENTARIA Y SEÑALIZACIÓN AV. CONVENCIÓN 1914 SUR

TRAMO: ENTRE AV. IGNACIO T. CHÁVEZ Y CALLE REPÚBLICA DE URUGUAY, AGUASCALIENTES Mpio.

cumple con los Requisitos y Normas Técnicas establecidas por la Dependencia Normativa, por lo que es viable su ejecución. Comprometiéndose la misma a proporcionar la supervisión y asistencia técnica necesaria durante el proceso administrativo.

Por la Dependencia Ejecutora

Arq. Gloria Guadalupe Castillo González
Encargada de Despacho de la Secretaría de Obras Públicas

Lic. Jaime Gallo Camacho
Secretario de Desarrollo Urbano

LUGAR : AGUASCALIENTES, AGS.

SECRETARÍA DE OBRAS PÚBLICAS

Av. Aguascalientes Sur No. 2615
Fracc. Jardines de las Fuentes,
Aguascalientes, Ags. C.P. 20278

(449) 9 78 92 01, 06, 09

www.ags.gob.mx

No. Folio SISCO 2325

H. AYUNTAMIENTO CONSTITUCIONAL DEL MUNICIPIO DE AGUASCALIENTES 2021-2024

AYUNTAMIENTO DE AGUASCALIENTES

FACTIBILIDAD VERIFICADA EN CAMPO

Aguascalientes LA CIUDAD DE TU VIDA

MUNICIPIO: AGUASCALIENTES

LOCALIZACION: TRAMO: ENTRE AV. IGNACIO T. CHÁVEZ Y CALLE REPÚBLICA DE URUGUAY, AGUASCALIENTES Mpio.

PROGRAMA: URBANIZACIÓN

SUBPROGRAMA: VIALIDADES URBANAS (CONSTRUCCION, AMPLIACION Y REHABILITACION) (c).- Semáforos, Señalización y Sincronización (señales, placas, nomenclatura, pintura y otras))

OBRA A REALIZAR: OBRA COMPLEMENTARIA Y SEÑALIZACIÓN AV. CONVENCIÓN 1914 SUR

DEPENDENCIA EJECUTORA: SECRETARÍA DE OBRAS PUBLICAS DEL MUNICIPIO DE AGUASCALIENTES

FORMA DE EJECUCION: CONTRATO

TIPO DE OBRA PROPUESTA: NUEVA

CONDICIONES ACTUALES DE LA OBRA:

OBRA COMPLEMENTARIA Y SEÑALIZACIÓN AV. CONVENCIÓN 1914 SUR

CARACTERISTICAS DE LA OBRA: Bueno

FACTIBILIDAD DE LA OBRA:

ESTA OBRA SE REQUIERE PARA EL BENEFICIO DE LA CIUDADANÍA

PROCEDE: SI [X] NO [ ]

REVISÓ: Jefa del Departamento de Expedientes Tecnicos y Costos

NOMBRE: Arq. Blanca Margarita Martinez Amador

FIRMA:

FECHA: 12 Sep 2022

SECRETARÍA DE OBRAS PÚBLICAS

Av. Aguascalientes Sur No. 2615
Fracc. Jardines de las Fuentes,
Aguascalientes, Ags. C.P. 20278

(449) 9 78 92 01, 06, 09


www.ags.gob.mx

No. Folio SISCO 2325

H. AYUNTAMIENTO DE AGUASCALIENTES
SECRETARÍA DE OBRAS PÚBLICAS
DIRECCIÓN DE SUPERVISIÓN DE OBRA
UBICACIÓN

OBRA:	DM-0050-2022 - OBRA COMPLEMENTARIA Y SEÑALIZACIÓN AV. CONVENCIÓN 1914 SUR					
NO. DE CONTR	DM-0050-2022	CONTRATISTA:	CASLOP DISEÑO ARTE Y CONSTRUCCION, S.A. DE C.V.			

OBRA COMPLEMENTARIA Y SEÑALIZACIÓN AV. CONVENCIÓN 1914 SUR, TRAMO: ENTRE AV. IGNACIO T. CHÁVEZ Y CALLE 4

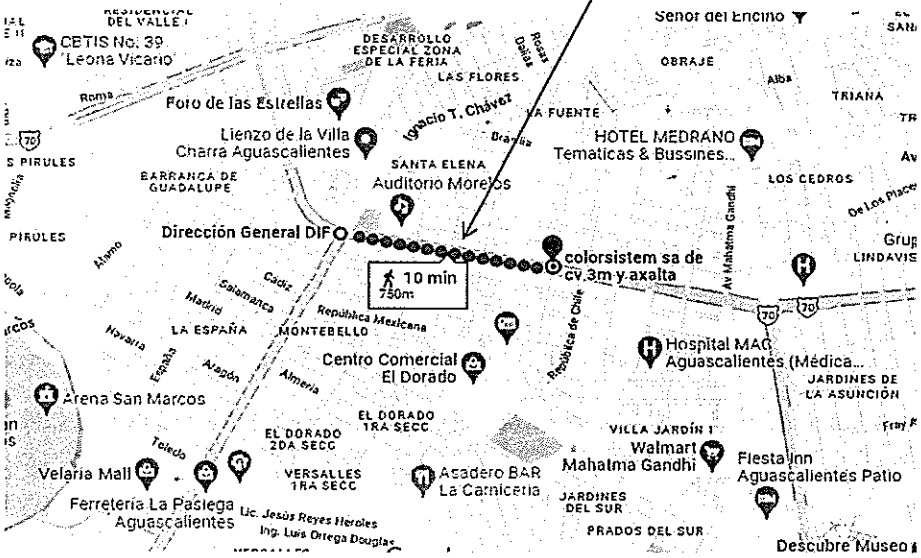

ING. RICARDO MACÍAS MERCADO
SUPERVISOR DE OBRA.

H. AYUNTAMIENTO DE AGUASCALIENTES
SECRETARÍA DE OBRAS PÚBLICAS
DIRECCIÓN DE SUPERVISIÓN DE OBRA
LOCALIZACION

OBRA:	DM-0050-2022 - OBRA COMPLEMENTARIA Y SEÑALIZACIÓN AV. CONVENCIÓN 1914 SUR					
NO. DE CONT	DM-0050-2022	CONTRATISTA:	CASLOP DISEÑO ARTE Y CONSTRUCCION, S.A. DE C.V.			



ING. RICARDO MACÍAS MERCADO
SUPERVISOR DE OBRA.

RO3-POS-SOS-7.5.1-04	
REVISION:	00
FECHA DE REVISION:	
RESPONSABLE:	SUPERVISOR DE OBRA
TIEMPO DE RET:	02 AÑOS

Aguascalientes

PROGRAMA DE OERA DEFINITIVO

No. DE CONTRATO : DM-0050-2022

PROGRAMA: UR-URBANIZACIÓN — INICIO VIGENTE: 11-junio-22

No. OBRA Y NOMBRE DE LA OBRA: DM-0050-2022 - OBRA COMPLEMENTARIA Y SEÑALIZACIÓN AV. CONVENCIÓN 1914 SUR — TERMINO REAL: 10-julio-22

RECURSO: 2022

CONCEPTO			1	2	3	4	5	6	7	8	9	10	11	12	13	14	15	16	PONDERACIÓN %	
			2022																FINANCIERO	FÍSICO
			ENERO	FEBRERO	MARZO	ABRIL	MAYO	JUNIO	JULIO	AGOSTO	SEPTIEMBRE	OCTUBRE	NOVIEMBRE	DICIEMBRE					%	%
								11-jun	10-jul											
DESCRIPCION		INVERSION																		
DM-0050-2022 - OBRA COMPLEMENTARIA Y SEÑALIZACION AV. CONVENCIÓN 1914 SUR.																				
TRAMO: ENTRE AV. ANACAO T. CHÁVEZ Y CALLE REPUBLICA DE URUGUAY, AGUASCALIENTES Mex.																				
PRELIMINARES	$	607.79	100					100											0.07	10.00
OBRA COMPLEMENTARIA	$	138,484.66	100					20	80										15.13	20.00
LIMPIEZAS	$	338.02	100						100										0.04	10.00
SENALIZACION	$	570,001.38	100					50	50										62.26	20.00
GUARNICIONES	$	853.26	100						80	20									0.09	20.00
EXTRAORDINARIOS	$	205,172.93	100						80	20									22.41	20.00
SUBTOTAL SIN IVA	$	915,458.04	$ 10.00	0 0 0 0	0 0 0 0	0 0 0 0	0 0 0 0	0 0 2 2	2 2 2 0	0 0 0 0	0 0 0 0	0 0 0 0	0 0 0 0	0 0 0 0	0 0 0 0	0 0 0 0	0 0 0 0	0 0 0 0		
AVACE SEMANAL %			0% 0% 0% 0%	0% 0% 0% 0%	0% 0% 0% 0%	0% 0% 0% 0%	0% 0% 0% 0%	0% 20% 20% 20%	20% 20% 20% 0%	0% 0% 0% 0%	0% 0% 0% 0%	0% 0% 0% 0%	0% 0% 0% 0%	0% 0% 0% 0%	0% 0% 0% 0%	0% 0% 0% 0%	0% 0% 0% 0%	0% 0% 0% 0%		
AVANCE SEMANAL ACUMULADO %			0% 0% 0% 0%	0% 0% 0% 0%	0% 0% 0% 0%	0% 0% 0% 0%	0% 0% 0% 0%	0% 20% 40% 60%	80% 100% 100% 100%	100% 100% 100% 100%	100% 100% 100% 100%	100% 100% 100% 100%	100% 100% 100% 100%	100% 100% 100% 100%	100% 100% 100% 100%	100% 100% 100% 100%	100% 100% 100% 100%	100% 100% 100% 100%	100,00	100,00
EJERCIDO SEMANAL $			- - - -	- - - -	- - - -	- - - -	- - - -	29,304.72 366,788.42 283,683.30	154,300.00 41,372.60 - -	- - - -	- - - -	- - - -	- - - -	- - - -	- - - -	- - - -	- - - -	- - - -	$ 915,458.04	
EJERCIDO MENSUAL $			$0.00	$0.00	$0.00	$0.00	$0.00	$709,776.44	$195,681.60	$0.00	$0.00	$0.00	$0.00	$0.00	$0.00	$0.00	$0.00	$0.00	$ 146,473.29	IVA 0%
EJERCIDO MENSUAL ACUMULADO $			0.00	0.00	0.00	0.00	0.00	709,776.44	915,458.04	915,458.04	915,458.04	915,458.04	915,458.04	915,458.04	915,458.04	915,458.04	915,458.04	915,458.04		
EJERCIDO SEMANAL %			0% 0% 0% 0%	0% 0% 0% 0%	0% 0% 0% 0%	0% 0% 0% 0%	0% 0% 0% 0%	3% 40% 31% 18%	2% 0% 0% 0%	0% 0% 0% 0%	0% 0% 0% 0%	0% 0% 0% 0%	0% 0% 0% 0%	0% 0% 0% 0%	0% 0% 0% 0%	0% 0% 0% 0%	0% 0% 0% 0%	0% 0% 0% 0%		
EJERCIDO MENSUAL %			0%	0%	0%	0%	0%	78%	22%	0%	0%	0%	0%	0%	0%	0%	0%	0%	GRAN TOTRAL EJERCIDO	
EJERCIDO MENSUAL ACUMULADO %			0%	0%	0%	0%	0%	78%	100%	100%	100%	100%	100%	100%	100%	100%	100%	100%	$ 1,061,931.32	

ING. SEBASTIÁN MACÍAS MERCADO
SUPERVISOR

PRESIDENCIA MUNICIPAL DE AGUASCALIENTES

FACTIBILIDAD VERIFICADA EN CAMPO

GENERALES

EJERCICIO: 2022 APROBACION No: 2022-PDM-0050-UR-05-005
LOCALIDAD: TRAMO: ENTRE AV. IGNACIO T. CHÁVEZ Y CALLE REPÚBLICA DE URUGUAY, AGUASCALIENTES Mpio.
MUNICIPIO: AGUASCALIENTES, AGS
TIPO DE INVERSION PROGRAMA DIRECTO MUNICIPAL (1501 FONDO GENERAL DE PARTICIPACIONES)

PROGRAMA: UR-URBANIZACIÓN
SUB-PROGRAMA: 05-VIALIDADES URBANAS, (CONSTRUCCION, AMPLIACION Y REHABILITACION) (C).- SEMAFOROS, SEÑALIZACION Y SICRONIZACION (SEÑALES, PLACAS, NOMENCLATURA, PINTURA Y OTRAS))

OBRA A REALIZARSE: DM-0050-2022 - OBRA COMPLEMENTARIA Y SEÑALIZACIÓN AV. CONVENCIÓN 1914 SUR

DEPENDENCIA EJECUTORA: SECRETARÍA DE OBRAS PÚBLICAS MUNICIPALES (S.O.P.M.A)
FORMACIÓN DE EJECUCION: CONTRATO NO. DE CONTRATO: DM-0050-2022
NOMBRE CONTRATISTA: CASLOP DISEÑO ARTE Y CONSTRUCCION, S.A. DE C.V.
REPRESENTANTE: JAIME FRANCISCO CASTAÑEDA LÓPEZ, ING.
MONTO CONT. ORIGEN $1,097,018.59 ANTICIPO: $283,711.71 30 DIAS
1A AMPLIACION $: 0 1 AMPL DIAS 0
2A AMPLIACION $: 0 2 AMPL DIAS 0
FIRMA CONTRATO: 08/06/2022
INICIO CONT: dd/mm/aa 9 de junio de 2022 TERMINO CONT 8 de julio de 2022
INICIO REAL: dd/mm/aa 11 de junio de 2022 TERMINO REAL: 10 de julio de 2022

TIPO DE OBRA PROPUESTA

NUEVA CREACIÓN		CONSOLIDACIÓN	
COMPLEMENTARIA		AMPLIACIÓN	
REHABILITACIÓN	X	EQUIPAMIENTO	

CARACTERÍSTICAS DE LA OBRA:

OBRA COMPLEMENTARIA Y SEÑALIZACIÓN AV. CONVENCIÓN 1914 SUR en el tramo entre Av. Ignacio T. Chavez y C. República de Uruguay, ya que las bases de la vialidad se encuentras en buen estado (funcionables), se renivelarán los brocales y tapas de registros existentes en la calzada y se pintará la distribución vial según las normas de la SCT. la distribución vial con pintura de trafico según las normas de la SCT.

BUEN ESTADO X REGULAR PESIMO ESTADO

FACTIBILIDAD DE LA OBRA: (CONDICIONES ACTUALES DE LA OBRA)

ESTA OBRA SE ENCUENTRA EN CONDICIONES PARA OPERARSE

PROCEDE: SI: X NO:
MARQUE SOLO UNA

ING. RICARDO MACÍAS MERCADO
SUPERVISOR

PRESIDENCIA MUNICIPAL DE AGUASCALIENTES

FACTIBILIDAD VERIFICADA EN CAMPO

GENERALES

LOCALIDAD: TRAMO: ENTRE AV. IGNACIO T. CHÁVEZ Y CALLE REPÚBLICA DE URUGUAY, AGUASCALIENTES Mpio.
MUNICIPIO: AGUASCALIENTES, AGS
PROGRAMA: UR-URBANIZACIÓN
SUB-PROGRAMA: 05-VIALIDADES URBANAS, (CONSTRUCCION, AMPLIACION Y REHABILITACION) (C).- SEMAFOROS, SEÑALIZACION Y SICRONIZACION (SEÑALES, PLACAS, NOMENCLATURA, PINTURA Y OTRAS))
OBRA A REALIZARSE: DM-0050-2022 - OBRA COMPLEMENTARIA Y SEÑALIZACIÓN AV. CONVENCIÓN 1914 SUR

DEPENDENCIA EJECUTORA: SECRETARÍA DE OBRAS PÚBLICAS MUNICIPALES (S.O.P.M.A)
FORMACIÓN DE EJECUCION: CONTRATO

TIPO DE OBRA PROPUESTA

NUEVA CREACIÓN		CONSOLIDACIÓN	
COMPLEMENTARIA		AMPLIACIÓN	
REHABILITACIÓN	X	EQUIPAMIENTO	

CARACTERÍSTICAS DE LA OBRA:

OBRA COMPLEMENTARIA Y SEÑALIZACIÓN AV. CONVENCIÓN 1914 SUR en el tramo entre Av. Ignacio T. Chavez y C. República de Uruguay, ya que las bases de la vialidad se encuentras en buen estado (funcionables), se renivelarán los brocales y tapas de registros existentes en la calzada y se pintará la distribución vial según las normas de la SCT. la distribución vial con pintura de trafico según las normas de la SCT.

CONDICIONES ACTUALES DE LA OBRA:

BUEN ESTADO:	X	REGULAR:		PESIMO ESTADO:	

FACTIBILIDAD DE LA OBRA:

ESTA OBRA SE ENCUENTRA EN CONDICIONES PARA OPERARSE

PROCEDE	**SI:**	X	**NO:**	

ING. RICARDO MACÍAS MERCADO
SUPERVISOR

PRESUPUESTO MODIFICADO

Obra: **OBRA COMPLEMENTARIA Y SEÑALIZACIÓN AV. CONVENCIÓN 1914 SUR**

Ubicación: **TRAMO: ENTRE AV. IGNACIO T. CHÁVEZ Y CALLE REPÚBLICA DE URUGUAY, AGUASCALIENTES Mpio.**

Contratista: **CASLOP DISEÑO ARTE Y CONSTRUCCION, S.A. DEC.V. (502)**

No.	Concepto	Unidad	Cantidad	Precio Unitario	Importe Total
	GRUPO: **OBRA COMPLEMENTARIA Y SEÑALIZACION**				
	PARTIDA: **PRELIMINARES**				
1	CORTE CON DISCO DIAMANTADO DE 14" EN PISOS DE CONCRETO ASFÁLTICO DE HASTA (HASTA 8.00 cm. DE PROFUNDIDAD). INCLUYE: TRAZO, EQUIPO Y OPERACIÓN, LIMPIEZAS.	ML	0	$52.59	$0.00
2	DEMOLICIÓN A MANO Y MECÁNICA DE PAVIMENTO HIDRÁULICO Y/O ASFÁLTICO EN CUALQUIER ESPESOR, EN PAVIMENTOS, LOSAS DIAMANTE, LOSAS DE CAJAS DE VÁLVULAS, LOSAS DE LLAVE HIDRAULICA, CAIMANES, ETC., CON O SIN ARMADO DE ACERO SIN RECUPERACIÓN., INCLUYE: CARGA Y ACARREO LOCAL DE MATERIAL AL LUGAR DE ACOPIO, HERRAMIENTA NECESARIA, CORTES CON DISCO Y TODO LO NECESARIO PARA SU CORRECTA EJECUCIÓN, LIMPIEZA, TRABAJO TERMINADO.	M3	0.91	$667.90	$607.79
			Totales por Partida		**$607.79**
	PARTIDA: **OBRA COMPLEMENTARIA**				
6	RE NIVELACIÓN DE POZO DE VISITA HASTA 30 cm DE ALTURA. INCLUYE: RETIRO SIN RECUPERACIÓN DE BROCAL EXISTENTE, DEMOLICIONES, NIVELADO CON TABIQUE ROJO RECOCIDO 7X14X28, ASENTADO CON MORTERO CEMENTO-ARENA 1:3 DE 28 cm DE ESPESOR, APLANADO CON MORTERO CEMENTO-ARENA 1:3 , PLOMEADO, NIVELADO, DEMOLICIONES, CARGAS Y ACARREOS DENTRO DE LA OBRA, LIMPIEZA PREVIA Y FINAL.	PZA	4	$1,756.00	$7,024.00
7	CONSTRUCCIÓN DE LOSA DIAMANTE A BASE DE CONCRETO PREMEZCLADO MR= 45 KG/CM2, T.M.A. 3/4" (19 mm), GRAVA TRITURADA, REVENIMIENTO DE 8+-2.5 cm, RESISTENCIA RÁPIDA A 3 DÍAS, DE 25 CM DE ESPESOR, EN POZO DE VISITA, SECCIÓN DE 1.50 M X 1.50 M , INCLUYE: TRAZO, NIVELACIÓN, LIMPIEZA PREVIA Y PREPARACIÓN DE LA SUPERFICIE, COMPACTACIÓN DE TERRENO AL 95% DE SU PVSM, ESCARIFICADO, SUMINISTRO DE MATERIALES, DEMOLICIÓN Y RECONSTRUCCIÓN DE APROCHES, ESPUMA DE POLIURETANO DE ALTA DENSIDAD EN TODO EL PERÍMETRO EXTERIOR DE 1/2", ASÍ COMO EN LAS JUNTAS DIAGONALES PARA FORMAR 4 PARTES, BROCAL Y TAPA DE Fo. Fo. TIPO PESADO (165 KG), CIMBRADO, COLADO, VIBRADO, DESCIMBRADO, CURADO CON MEMBRANA QUÍMICA BASE AGUA, APLANADO FINO EN RECEPCIÓN DE BROCAL, CORTES CON CORTADORA DE DISCO DE 5 CM ENTRE JUNTAS DIAGONALES FORMANDO 8 PIEZAS Y SELLADO DE JUNTAS, CORTES RELLENOS CON MATERIAL PREFORMADO Y SELLADOR AUTONIVELANTE, MANO DE OBRA, CARGA Y ACARREOS DE MATERIAL DENTRO Y FUERA DE LA OBRA, LIMPIEZA FINAL, TRABAJO TERMINADO P.U.O.T	PZA	4	$8,705.86	$34,823.44
8	RENIVELACIÓN DE RASANTE (PARTE SUPERIOR) DE CAJA DE VÁLVULAS TIPO 2, ó DE HASTA 1.20 X 1. 30 MTS, NIVELADO HASTA UNA ALTURA MAXIMA DE 10 CM, Y MINIMA DE 5 CM. MEDIDAS INTERIORES INCLUYE: TRAZO, EXCAVACIÓN, NIVELACIÓN, PREPARACIONES , Y DEMOLICIONES, RETIRO SIN RECUPERACIÓN DE TAPA DE FOFO EXISTENTE, MURO DE TABIQUE ROJO RECOCIDO COMÚN 7X14X28 CM DE 14 CM DE ESPESOR, JUNTEADO CON MORTERO CEMENTO-ARENA 1:3 APLANADO INTERIOR CON MORTERO CEMENTO ARENA 1:3 DE 2.00 CM DE ESPESOR ACABADO PULIDO, LOSA DE CONCRETO F´C= 250 KG/CM2 T.M.A. 19 MM DE 15 CM DE ESPESOR ARMADA CON VRS No. 3 @15 cm EN AMBOS SENTIDOS, CONTRAMARCO SENCILLO DE CANAL FoFo DE 100 mm, CONTRAMARCO CON TAPA DE FOFO, TIPO PESADO DE 50X50 CM, DEMOLICIÓN Y RECONSTRUCCIÓN DE APROCHES, CARGA Y ACARREOS DENTRO DE LA OBRA, CIMBRADO, DESCIMBRADO, COLADO, VIBRADO, LIMPIEZA PREVIA, FINAL, Y TODO LO NECESARIO PARA LA CORRECTA EJECUCIÓN DEL CONCEPTO.	PZA	2	$9,291.56	$18,583.12

Obra: **OBRA COMPLEMENTARIA Y SEÑALIZACIÓN AV. CONVENCIÓN 1914 SUR**

Ubicación: **TRAMO: ENTRE AV. IGNACIO T. CHÁVEZ Y CALLE REPÚBLICA DE URUGUAY, AGUASCALIENTES Mpio.**

Contratista: **CASLOP DISEÑO ARTE Y CONSTRUCCION, S.A. DEC.V. (502)**

No.	Concepto	Unidad	Cantidad	Precio Unitario	Importe Total
	GRUPO: **OBRA COMPLEMENTARIA Y SEÑALIZACION**				
	PARTIDA: **OBRA COMPLEMENTARIA**				
9	LIMPIEZA Y DESAZOLVE DE POZOS DE VISITA Y LÍNEAS DE ALCANTARILLADO EXISTENTE CON CAMIÓN TIPO VACTOR. INCLUYE: RESANE INTERIOR DEL POZO Y REMATE DE POZO CON TUBO SELLADOR FESTER Y MORTERO 1:3, MANO DE OBRA, SUMINISTRO DE AGUA EN PIPA, HERRAMIENTAS Y EQUIPO PARA SU CORRECTA EJECUCIÓN, LIMPIEZAS, RENTA DE CAMIÓN VACTOR HASTA LA CORRECTA LIMPIEZA DE LAS LÍNEAS EXISTENTES DE POZO A POZO ASÍ COMO EL TRASLADO DE LOS DESECHOS HASTA TIRADERO AUTORIZADO, LA UNIDAD DE MEDIDA SE PAGARA DE POZO A POZO.	LOTE	10	$7,805.41	$78,054.10
			Totales por Partida		**$138,484.66**
	PARTIDA: **LIMPIEZAS**				
11	LIMPIEZA FINAL DE LA OBRA, INCLUYE: BARRIDO, CARGA, ACARREOS Y RETIRO DE ESCOMBROS FUERA DE LA OBRA, TRABAJO TERMINADO.	M2	32.07	$10.54	$338.02
			Totales por Partida		**$338.02**
	PARTIDA: **SEÑALIZACION HORIZONTAL**				
12	SUMINISTRO Y APLICACIÓN DE PINTURA BASE SOLVENTE (ESMALTE) COLOR AZUL (PANTONE 294) EN RAMPAS PARA PERSONAS CON DISCAPACIDAD CUALQUIER SECCIÓN SEGÚN PLANOS. INCLUYE: TRAZO, MANO DE OBRA, LIMPIEZA PREVIA Y FINAL DE SUPERFICIE, EQUIPO NECESARIO PARA SU EJECUCIÓN, Y TODO LO NECESARIO PARA SU CORRECTA EJECUCIÓN, TRABAJO TERMINADO. (pintura esmalte, area efectiva)	M2	32.07	$103.18	$3,308.98
13	SUMINISTRO Y APLICACIÓN DE LOGOTIPO A (SILLA DE RUEDAS) EN PINTURA BASE SOLVENTE (ESMALTE) COLOR BLANCO EN RAMPAS PARA PERSONAS CON DISCAPACIDAD TAMAÑO Y DISEÑO SEGÚN PLANOS. INCLUYE: TRAZO, ENMASCARILLADO, PLANTILLA, MANO DE OBRA, LIMPIEZA PREVIA Y FINAL DE SUPERFICIE, EQUIPO NECESARIO PARA SU EJECUCIÓN, Y TODO LO NECESARIO PARA SU CORRECTA EJECUCIÓN, TRABAJO TERMINADO.	PZA	17	$371.17	$6,309.89
14	SUMINISTRO Y APLICACIÓN DE PINTURA BASE SOLVENTE (ESMALTE) PARA MARCAS EN GUARNICIONES CLASIFICACION M-12.1, M12.2 APLICADA SOBRE GUARNICIONES Y DENTELLONES DE CUALQUIER COLOR, SEGÚN SE REQUIERA Y SEGÚN NORMA S.C.T. SECADO AL TACTO EN 5 MIN Y AL DURO EN 30 MIN CON MICRO ESFERA , DESARROLLO DE 35 CM. INCLUYE: MATERIALES Y ESPECIFICACIONES QUE CUMPLAN CON LA NORMATIVA N-CMT-5-01-001/05, N-PRY-CAR-10-01-002/13 APLICADAS AL DIA DE HOY, TRAZO, MANO DE OBRA, LIMPIEZA PREVIA Y FINAL DE SUPERFICIE, EQUIPO NECESARIO PARA SU EJECUCIÓN, Y TODO LO NECESARIO PARA SU CORRECTA EJECUCIÓN, TRABAJO TERMINADO. (pintura esmalte, ML efectivo)	ML	1360.15	$44.08	$59,955.41
15	SUMINISTRO Y APLICACIÓN DE PINTURA BASE SOLVENTE " EN RAYA SEPARADORA CLASIFICACIÓN M - 1.1, LÍNEA CONTINUA SENCILLA DE DIVISIÓN DE CARRILES DE FRENTE EN PISO, DE 10 CM DE ANCHO, COLOR BLANCO Y/O AMARILLO CON MICRO ESFERA SEGÚN NORMA SCT, SECADO AL TACTO EN 5 MIN Y AL DURO EN 30 MIN. INCLUYE: MATERIALES Y ESPECIFICACIONES QUE CUMPLAN CON LA NORMATIVA N-CMT-5-01-001/05, N-PRY-CAR-10-01-002/13 APLICADAS AL DIA DE HOY, MATERIAL, TRAZO, ENMASCARILLADO, MANO DE OBRA, LIMPIEZA PREVIA DE SUPERFICIE, EQUIPO NECESARIO PARA SU EJECUCIÓN, Y TODO LO NECESARIO PARA SU CORRECTA EJECUCIÓN, TRABAJO TERMINADO.	ML	273.4	$27.89	$7,625.13

Obra: **OBRA COMPLEMENTARIA Y SEÑALIZACIÓN AV. CONVENCIÓN 1914 SUR**

Ubicación: **TRAMO: ENTRE AV. IGNACIO T. CHÁVEZ Y CALLE REPÚBLICA DE URUGUAY, AGUASCALIENTES Mpio.**

Contratista: **CASLOP DISEÑO ARTE Y CONSTRUCCION, S.A. DEC.V. (502)**

No.	Concepto	Unidad	Cantidad	Precio Unitario	Importe Total
	GRUPO: **OBRA COMPLEMENTARIA Y SEÑALIZACION**				
	PARTIDA: **SEÑALIZACION HORIZONTAL**				
16	SUMINISTRO Y APLICACIÓN DE PINTURA BASE SOLVENTE " EN RAYA SEPARADORA CLASIFICACIÓN M - 1.2, DISCONTINUA SENCILLA, DE DIVISIÓN DE CARRILES PARA VELOCIDADES MENORES A 60 KM/HR DE FRENTE EN PISO, DESARROLLO DE 2.50 ML X 0.10 MTS DE ANCHO, CON UNA SEPARACIÓN DE 5.00 MTS ENTRE SI PROMEDIO, A BASE DE PINTURA PARA TRAFICO COLOR BLANCO CON MICRO ESFERA SEGÚN NORMA SCT, INCLUYE: MATERIALES Y ESPECIFICACIONES QUE CUMPLAN CON LA NORMATIVA N-CMT-5-01-001/05, N-PRY-CAR-10-01-002/13 APLICADAS AL DIA DE HOY, MATERIAL, TRAZO, ENMASCARILLADO, MANO DE OBRA, LIMPIEZA PREVIA DE SUPERFICIE, EQUIPO NECESARIO PARA SU EJECUCIÓN, Y TODO LO NECESARIO PARA SU CORRECTA EJECUCIÓN, TRABAJO TERMINADO.	ML	605	$27.89	$16,873.45
17	SUMINISTRO Y APLICACIÓN DE PINTURA BASE SOLVENTE " EN RAYA SEPARADORA CLASIFICACIÓN M -1.6, CONTINUA DOBLE, PARA DELIMITAR CARRIL EXCLUSIVO DE FRENTE EN PISO, 0.10 MTS DE ANCHO, CON UNA SEPARACIÓN IGUAL AL ANCHO DE LA LINEA A BASE DE PINTURA PARA TRAFICO COLOR AMARILLO CON MICRO ESFERA SEGÚN NORMA SCT, INCLUYE: MATERIALES Y ESPECIFICACIONES QUE CUMPLAN CON LA NORMATIVA N-CMT-5-01-001/05, N-PRY-CAR-10-01-002/13 APLICADAS AL DIA DE HOY, MATERIAL, TRAZO, ENMASCARILLADO, MANO DE OBRA, LIMPIEZA PREVIA DE SUPERFICIE, EQUIPO NECESARIO PARA SU EJECUCIÓN, Y TODO LO NECESARIO PARA SU CORRECTA EJECUCIÓN, TRABAJO TERMINADO.	ML	168	$55.74	$9,364.32
18	SUMINISTRO Y APLICACIÓN DE PINTURA BASE SOLVENTE " EN RAYA SEPARADORA CLASIFICACIÓN M - 3.3, CONTINUA IZQUIERDA, PARA VIALIDADES URBANAS DE FRENTE EN PISO, SEPARADA 15 CM. DE LA GUARNICION, A BASE DE PINTURA PARA TRAFICO COLOR BLANCO CON MICRO ESFERA SEGÚN NORMA SCT, INCLUYE: MATERIALES Y ESPECIFICACIONES QUE CUMPLAN CON LA NORMATIVA N-CMT-5-01-001/05, N-PRY-CAR-10-01-002/13 APLICADAS AL DIA DE HOY, MATERIAL, TRAZO, ENMASCARILLADO, MANO DE OBRA, LIMPIEZA PREVIA DE SUPERFICIE, EQUIPO NECESARIO PARA SU EJECUCIÓN, Y TODO LO NECESARIO PARA SU CORRECTA EJECUCIÓN, TRABAJO TERMINADO.	ML	936.3	$27.89	$26,113.41
20	SUMINISTRO Y APLICACIÓN DE PINTURA BASE SOLVENTE " EN RAYA DE ALTO CLASIFICACIÓN M - 6, PARA INDICAR ALTO EN CRUCEROS, COLOR BLANCO, REFLEJANTE CON MICRO ESFERA DE VIDRIO EN PROPORCIÓN SEGÚN NORMA SCT DE 0.60 MTS DE ANCHO DE LONGITUD VARIABLE, INCLUYE: MATERIALES Y ESPECIFICACIONES QUE CUMPLAN CON LA NORMATIVA N-CMT-5-01-001/05, N-PRY-CAR-10-01-002/13 APLICADAS AL DIA DE HOY, MATERIAL, TRAZO, ENMASCARILLADO, MANO DE OBRA, LIMPIEZA PREVIA DE SUPERFICIE, EQUIPO NECESARIO PARA SU EJECUCIÓN, Y TODO LO NECESARIO PARA SU CORRECTA EJECUCIÓN, TRABAJO TERMINADO.	ML	59.05	$167.23	$9,874.93
21	SUMINISTRO Y APLICACIÓN DE PINTURA BASE SOLVENTE " EN RAYA PARA CRUCE PEATONAL CLASIFICACIÓN M - 7.1, PARA INDICAR " CRUCE PEATONAL EN VIAS PRIMARIAS", COLOR AMARILLO, REFLEJANTE CON MICRO ESFERA DE VIDRIO EN PROPORCIÓN SEGÚN NORMA SCT DE 0.40 MTS DE ANCHO Y 3.5 MTS. DE LONGITUD POR EL ANCHO DE LA VIALIDAD, CON UNA SEPARACIÓN DE 0.40 MTS. ENTRE ELLAS, INCLUYE: MATERIALES Y ESPECIFICACIONES QUE CUMPLAN CON LA NORMATIVA N-CMT-5-01-001/05, N-PRY-CAR-10-01-002/13 APLICADAS AL DIA DE HOY, MATERIAL, TRAZO, ENMASCARILLADO, MANO DE OBRA, LIMPIEZA PREVIA DE SUPERFICIE, EQUIPO NECESARIO PARA SU EJECUCIÓN, Y TODO LO NECESARIO PARA SU CORRECTA EJECUCIÓN, TRABAJO TERMINADO.	M2	310.2	$184.35	$57,185.37

Obra: **OBRA COMPLEMENTARIA Y SEÑALIZACIÓN AV. CONVENCIÓN 1914 SUR**

Ubicación: **TRAMO: ENTRE AV. IGNACIO T. CHÁVEZ Y CALLE REPÚBLICA DE URUGUAY, AGUASCALIENTES Mpio.**

Contratista: **CASLOP DISEÑO ARTE Y CONSTRUCCION, S.A. DEC.V. (502)**

No.	Concepto	Unidad	Cantidad	Precio Unitario	Importe Total
	GRUPO: **OBRA COMPLEMENTARIA Y SEÑALIZACION**				
	PARTIDA: **SEÑALIZACION HORIZONTAL**				
22	SUMINISTRO Y APLICACIÓN DE PINTURA BASE SOLVENTE " EN FLECHAS CLASIFICACIÓN M - 11.1, "FLECHA SENCILLA" PARA INDICAR SENTIDO DE CIRCULACIÓN , EN VIALIDADES PARA VELOCIDAD MENOR A 60KM POR HORA DIFERENTES DIMENSIONES (VER PLANO DE SEÑALAMIENTOS) COLOR BLANCO, REFLEJANTE CON MICRO ESFERA DE VIDRIO EN PROPORCIÓN SEGÚN NORMA SCT, INCLUYE: MATERIALES Y ESPECIFICACIONES QUE CUMPLAN CON LA NORMATIVA N-CMT-5-01-001/05, N-PRY-CAR-10-01-002/13 APLICADAS AL DIA DE HOY, MATERIAL, TRAZO, ENMASCARILLADO, MANO DE OBRA, LIMPIEZA PREVIA DE SUPERFICIE, EQUIPO NECESARIO PARA SU EJECUCIÓN, Y TODO LO NECESARIO PARA SU CORRECTA EJECUCIÓN, TRABAJO TERMINADO.	PZA	55	$296.22	$16,292.10
23	SUMINISTRO Y APLICACIÓN DE PINTURA BASE SOLVENTE " EN FLECHAS CLASIFICACIÓN M - 11.1, " FLECHA CABEZA DOBLE" PARA INDICAR SENTIDO DE CIRCULACIÓN (VUELTA IZQUIERDA O DERECHA) , EN VIALIDADES PARA VELOCIDAD MENOR A 60KM POR HORA DIFERENTES DIMENSIONES (VER PLANO DE SEÑALAMIENTOS) COLOR BLANCO, REFLEJANTE CON MICRO ESFERA DE VIDRIO EN PROPORCIÓN SEGÚN NORMA SCT, INCLUYE: MATERIALES Y ESPECIFICACIONES QUE CUMPLAN CON LA NORMATIVA N-CMT-5-01-001/05, N-PRY-CAR-10-01-002/13 APLICADAS AL DIA DE HOY, MATERIAL, TRAZO, ENMASCARILLADO, MANO DE OBRA, LIMPIEZA PREVIA DE SUPERFICIE, EQUIPO NECESARIO PARA SU EJECUCIÓN, Y TODO LO NECESARIO PARA SU CORRECTA EJECUCIÓN, TRABAJO TERMINADO.	PZA	3	$462.23	$1,386.69
24	SUMINISTRO Y APLICACIÓN DE PINTURA BASE SOLVENTE " EN LETRAS Y NUMEROS CLASIFICACIÓN M - 11.1 "LETRAS Y NUMEROS" EN VIALIDADES PARA VELOCIDAD MENOR A 60KM POR HORA DIFERENTES DIMENSIONES (VER PLANO DE SEÑALAMIENTOS) COLOR BLANCO, REFLEJANTE CON MICRO ESFERA DE VIDRIO EN PROPORCIÓN SEGÚN NORMA SCT DE (VER DETALLES EN PLANOS) INCLUYE: MATERIALES Y ESPECIFICACIONES QUE CUMPLAN CON LA NORMATIVA N-CMT-5-01-001/05, N-PRY-CAR-10-01-002/13 APLICADAS AL DIA DE HOY, MATERIAL, TRAZO, ENMASCARILLADO, MANO DE OBRA, LIMPIEZA PREVIA DE SUPERFICIE, EQUIPO NECESARIO PARA SU EJECUCIÓN, Y TODO LO NECESARIO PARA SU CORRECTA EJECUCIÓN, TRABAJO TERMINADO.	PZA	384	$462.23	$177,496.32
25	SUMINISTRO Y APLICACIÓN DE PINTURA BASE SOLVENTE " EN LETRAS Y NUMEROS CLASIFICACIÓN M - 11.2 "FLECHA SIN CUERPO" PARA ESTABLECER LUGARES DE PARADA, (VER PLANO DE SEÑALAMIENTOS) COLOR BLANCO, REFLEJANTE CON MICRO ESFERA DE VIDRIO EN PROPORCIÓN SEGÚN NORMA SCT DE (VER DETALLES EN PLANOS) INCLUYE: MATERIALES Y ESPECIFICACIONES QUE CUMPLAN CON LA NORMATIVA N-CMT-5-01-001/05, N-PRY-CAR-10-01-002/13 APLICADAS AL DIA DE HOY, MATERIAL, TRAZO, ENMASCARILLADO, MANO DE OBRA, LIMPIEZA PREVIA DE SUPERFICIE, EQUIPO NECESARIO PARA SU EJECUCIÓN, Y TODO LO NECESARIO PARA SU CORRECTA EJECUCIÓN, TRABAJO TERMINADO.	PZA	15	$514.63	$7,719.45
26	SUMINISTRO Y APLICACIÓN DE PINTURA BASE SOLVENTE " EN LETRAS Y NUMEROS CLASIFICACIÓN M - 11.2 "LEYENDA SOLO BUS" PARA VELOCIDAD MENOR A 60KM POR HORA DIFERENTES DIMENSIONES (VER PLANO DE SEÑALAMIENTOS) COLOR BLANCO, REFLEJANTE CON MICRO ESFERA DE VIDRIO EN PROPORCIÓN SEGÚN NORMA SCT DE (VER DETALLES EN PLANOS) INCLUYE: MATERIALES Y ESPECIFICACIONES QUE CUMPLAN CON LA NORMATIVA N-CMT-5-01-001/05, N-PRY-CAR-10-01-002/13 APLICADAS AL DIA DE HOY, MATERIAL, TRAZO, ENMASCARILLADO, MANO DE OBRA, LIMPIEZA PREVIA DE SUPERFICIE, EQUIPO NECESARIO PARA SU EJECUCIÓN, Y TODO LO NECESARIO PARA SU CORRECTA EJECUCIÓN, TRABAJO TERMINADO.	PZA	5	$1,406.13	$7,030.65

Obra: **OBRA COMPLEMENTARIA Y SEÑALIZACIÓN AV. CONVENCIÓN 1914 SUR**

Ubicación: **TRAMO: ENTRE AV. IGNACIO T. CHÁVEZ Y CALLE REPÚBLICA DE URUGUAY, AGUASCALIENTES Mpio.**

Contratista: **CASLOP DISEÑO ARTE Y CONSTRUCCION, S.A. DEC.V. (502)**

No.	Concepto	Unidad	Cantidad	Precio Unitario	Importe Total
	GRUPO: **OBRA COMPLEMENTARIA Y SEÑALIZACION**				
	PARTIDA: **SEÑALIZACION HORIZONTAL**				
27	SUMINISTRO Y APLICACIÓN DE PINTURA BASE SOLVENTE " EN LETRAS Y NUMEROS CLASIFICACIÓN M - 11.4 "L INVERTIDA" PARA ESTABLECER LUGAR DE PARADA CUYO LADO MAYOR EN UNA LÍNEA DE 20 CM DE ANCHO POR 20 MTS DE LARGO Y SU LADO MENOR EN UNA LÍNEA DE 50 CM DE ANCHO POR EL ANCHO DEL CARRIL, SOBRE PAVIMENTO EN VIALIDADES PARA VELOCIDAD MENOR A 60KM POR HORA DIFERENTES DIMENSIONES (VER PLANO DE SEÑALAMIENTOS) COLOR BLANCO, REFLEJANTE CON MICRO ESFERA DE VIDRIO EN PROPORCIÓN SEGÚN NORMA SCT DE (VER DETALLES EN PLANOS) INCLUYE: MATERIALES Y ESPECIFICACIONES QUE CUMPLAN CON LA NORMATIVA N-CMT-5-01-001/05, N-PRY-CAR-10-01-002/13 APLICADAS AL DIA DE HOY, MATERIAL, TRAZO, ENMASCARILLADO, MANO DE OBRA, LIMPIEZA PREVIA DE SUPERFICIE, EQUIPO NECESARIO PARA SU EJECUCIÓN, Y TODO LO NECESARIO PARA SU CORRECTA EJECUCIÓN, TRABAJO TERMINADO.	PZA	5	$1,321.99	$6,609.95
28	SUMINISTRO Y COLOCACIÓN DE VIALETA STANDARD (S-200) DE 10X10CM. COLOR: CUERPO AMARILLO Y/O BLANCO Y REFLEJANTE AMARILLO 1 CARA MARCA SEA O SIMILAR EN CALIDAD Y ESPECIFICACIONES DE FICHA TÉCNICA, FIJADO EN PAVIMENTO CON SISTEMA DE SUJECIÓN DE ALTO AGARRE PEGAMENTO EPOXICO 100 A/B (RESINA EPÓXICA/RESINA POLIAMIDA MODIFICADA), RESISTENTE A ALTA TEMPERATURA (VER PLANO DE DETALLES DE SEÑALAMIENTOS HORIZONTAL), INCLUYE: LIMPIEZA PREVIA Y FINAL DE LA SUPERFICIE, PREPARACIÓN DE LA SUPERFICIE, TRAZO, ALINEACIÓN, Y TODO LO NECESARIO PARA SU CORRECTA EJECUCIÓN, TRABAJO TERMINADO.	PZA	418	$114.57	$47,890.26
29	SUMINISTRO Y COLOCACION DE VIALETA SOLAR DE 10X10CM. COLOR: CUERPO ALUMINIO 3 LED DOS CARAS REFLEJANTES MARCA CREATIVAL VT-29 O SIMILAR EN CALIDAD Y ESPECIFICACIONES DE FICHA TÉCNICA, FIJADO EN PAVIMENTO CON SISTEMA DE SUJECIÓN DE ALTO AGARRE PEGAMENTO EPOXICO 100 A/B (RESINA EPÓXICA/RESINA POLIAMIDA MODIFICADA), RESISTENTE A ALTA TEMPERATURA (VER PLANO DE DETALLES DE SEÑALAMIENTOS HORIZONTAL), INCLUYE: LIMPIEZA PREVIA Y FINAL DE LA SUPERFICIE+C92, PREPARACIÓN DE LA SUPERFICIE, TRAZO, ALINEACIÓN, Y TODO LO NECESARIO PARA SU CORRECTA EJECUCIÓN, TRABAJO TERMINADO.	PZA	153	$712.19	$108,965.07
				Totales por Partida	**$570,001.38**
	PARTIDA: **GUARNICIONES**				
30	EXCAVACION A MAQUINA Y/O A MANO EN MATERIAL TIPO II, EN SECO O PRESENCIA DE AGUA, INCLUYE. CORTE DE RAIZ DE CUALQUIER TAMAÑO Y GROSOR, HASTA UNA PROFUNDIDAD DE 40 CM DESPUES DE DESMONTE, DESPALME Y/O DEMOLICION DE SUPERFICIE O ELEMENTO ESTRUCTURAL O DE ACABADO, PROTECCION DE AREAS ADYACENTES, SIN DAÑAR AREAS ALEDAÑAS, CARGA Y ACARREO A TIRADERO OFICIAL, CONSERVACION DE LA MISMA, TRABAJO TERMINADO, LIMPIEZAS.	M3	2.21	$386.09	$853.26
				Totales por Partida	**$853.26**
				Totales por Grupo	**$710,285.10**

Obra: **OBRA COMPLEMENTARIA Y SEÑALIZACIÓN AV. CONVENCIÓN 1914 SUR**

Ubicación: **TRAMO: ENTRE AV. IGNACIO T. CHÁVEZ Y CALLE REPÚBLICA DE URUGUAY, AGUASCALIENTES Mpio.**

Contratista: **CASLOP DISEÑO ARTE Y CONSTRUCCION, S.A. DEC.V. (502)**

No.	Concepto	Unidad	Cantidad	Precio Unitario	Importe Total
	GRUPO: **EXTRAORDINARIO**				
	PARTIDA: **EXTRAORDINARIO**				
36	CONSTRUCCION DE SOBREGUARNICION ARMADA RECTA Y/O CURVA DE 15 X 15 CM DE ALTURA DE SECCION CON CONCRETO PREMEZCLADO MR=38 KGF/CM2, R.N., REVENIMIENTO DE 8 A 10 CM, T.M.A. 3/4", GRAVA TRITURADA, ACABADO PULIDO EN LA PARTE SUPERIOR Y DOBLADOR EN ARISTAS, INCLUYE: VARILLA DEL No. 3 DE 30 CM @ 50 CM ANCLADA A LA GUARNICION EXISTENTE Y UNA LINEA DE VARILLA DE 3/8" HORIZONTAL, CIMBRADO, COLADO, VIBRADO, ACABADO, DESCIMBRADO, DESMOLDANTE, ALINEADO, NIVELADO Y CURADO EN SU PARTE SUPERIOR CON MEMBRANA BASE AGUA A RAZON DE 1 LT/M2, JUNTA DE AISLAMIENTO LONGITUDINAL AL COMBINAR CON OTRO ELEMENTO Y TRANSVERSAL @ 30 MTS MAXIMO, SELLADO CON SELLADOR AUTONIVELANTE LONGITUDINAL, TRABAJO TERMINADO, P.U.O.T.	ML	254	$296.09	$75,206.86
37	SUMINISTRO Y COLOCACION DE CONCRETO ASFALTICO EN CALIENTE DE GRANULOMETRIA DENSA ELABORADA CON ASFALTO AGREGADO 3/42 A FINOS, DESDE 0.00 HASTA 20 CM DE ESPESODR, FORMADA Y COMPACTADA AL 95%, INCLUYE: MATERIALES, TRAMO DE PRUEBA AL INICIO PARA REVISION Y AUTORIZACION DEL ESPESOR POR PARTE DEL SUPERVISOR, EL CONTRATISTA DEBERA PREVEER EL SUMINISTRO Y TIEMPOS MUERTOS PARA MOVIMIENTO DE TREN DE MAQUINAS DE TRABAJO EN TRAMOS AISLADOS, TRABAJO TERMINADO, P.U.O.T., LIMPIEZAS DE GRANZON	M2	256.79	$518.75	$133,209.81
38	DEDUCTIVA POR CONCEPTO DE INDIRECTOS NO COMPROBADOS	LOTE	-3.24374	$1,000.00	-$3,243.74

Totales por Partida		**$205,172.93**
Totales por Grupo		**$205,172.93**
Totales Presup.		**$915,458.04**
Anticipo	**+**	**$283,711.71**
Amortizac. Ant.	**-**	**$283,711.71**
SubTotal. Ant.	**=**	**$915,458.04**
IVA	**+**	**$146,473.28**
Total	**=**	**$1,061,931.32**

PRESUPUESTO MODIFICADO

Obra: **OBRA COMPLEMENTARIA Y SEÑALIZACIÓN AV. CONVENCIÓN 1914 SUR**

Ubicación: **TRAMO: ENTRE AV. IGNACIO T. CHÁVEZ Y CALLE REPÚBLICA DE URUGUAY, AGUASCALIENTES Mpio.**

Contratista: **CASLOP DISEÑO ARTE Y CONSTRUCCION, S.A. DEC.V. (502)**

Grupo	Partida	Importe
OBRA COMPLEMENTARIA Y SEÑALIZACION		
	PRELIMINARES	$607.79
	OBRA COMPLEMENTARIA	$138,484.66
	LIMPIEZAS	$338.02
	SEÑALIZACION HORIZONTAL	$570,001.38
	GUARNICIONES	$853.26
	Subtotal por Grupo	**$710,285.10**
EXTRAORDINARIO		
	EXTRAORDINARIO	$205,172.93
	Subtotal por Grupo	**$205,172.93**

Totales Presup.		**$915,458.04**
Anticipo	+	**$283,711.71**
Amortizac. Ant.	-	**$283,711.71**
SubTotal. Ant.	=	**$915,458.04**
IVA	+	**$146,473.28**
Total	=	**$1,061,931.32**

MUNICIPIO DE AGUASCALIENTES

SECRETARIA DE OBRA PUBLICAS MUNICIPALES

DIRECCION DE COSTOS Y LICITACION DE OBRA

CONTRATO: DM-0050-2022

OBRA: OBRA COMPLEMENTARIA Y SEÑALIZACIÓN AV. CONVENCIÓN 1914 SUR, TRAMO: ENTRE AV. IGNACIO T. CHÁVEZ Y CALLE REPÚBLICA DE URUGUAY, AGUASCALIENTES Mpio.

MONTO MODIFICADO FINAL: $1,061,931.32

VOLUMEN	UNIDAD	COMPONENTE DE OBRA	MONTO	PU
0.91	M3	LIMPIA, CORTE CON DISCO, DEMOLICION, CARGA Y ACARREO	$ 607.79	$ 667.90
16.00	PZAS	RENIVELACIONES DE TAPAS DE INFRAESTRUCTURA EXISTENTE (POZOS, CAJAS DE VALVULAS, REGISTROS DE VOZ	$ 268,450.73	$ 16,778.17
32.07	M2	LIMPIEZAS GENERAL DE OBRA A DETALLE Y DESASOLVE DE POZOS DE VISITA EN LINEAS DE ALCANTARILLADO	$ 338.02	$ 10.54
4177.40	ML	SEÑALIZACION HORIZONTAL SEGÚN NORMA SCT	$ 570,001.38	$ 136.45
254.00	ML	CONSTRUCCION DE GUARNICIONES	$ 76,060.12	$ 299.45
			$ 915,458.04	

H. AYUNTAMIENTO DE AGUASCALIENTES
SECRETARÍA DE OBRAS PÚBLICAS
DIRECCIÓN DE SUPERVISIÓN DE OBRA


Aguascalientes
LA CIUDAD DE TU VIDA


MEMORIA FOTOGRAFICA


OBRA:	DM-0050-2022 - OBRA COMPLEMENTARIA Y SEÑALIZACIÓN AV. CONVENCIÓN 1914 SUR					
NO. DE CONTRATO:	DM-0050-2022		CONTRATISTA:	CASLOP DISEÑO ARTE Y CONSTRUCCION, S.A. DE C.V.		

INICIO.



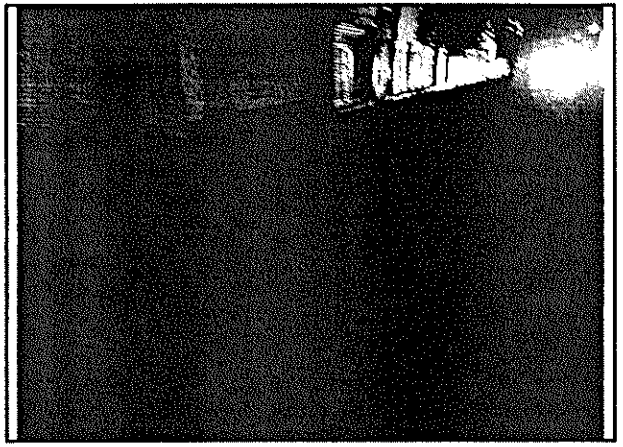

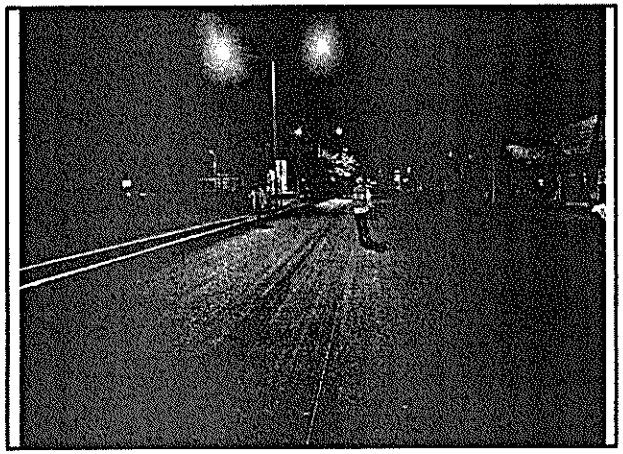

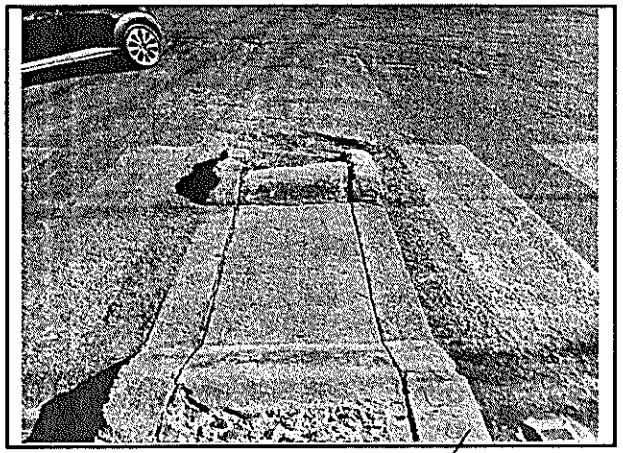

ING. RICARDO MACÍAS MERCADO
SUPERVISOR DE OBRA.


SECRETARÍA DE OBRAS PÚBLICAS
DIRECCIÓN DE SUPERVISIÓN DE OBRA

Aguascalientes
LA CIUDAD DE TU VIDA

MEMORIA FOTOGRAFICA

OBRA:	DM-0050-2022 - OBRA COMPLEMENTARIA Y SEÑALIZACIÓN AV. CONVENCIÓN 1914 SUR					
NO. DE CONTRATO:	DM-0050-2022		CONTRATISTA:	CASLOP DISEÑO ARTE Y CONSTRUCCION, S.A. DE C.V.		

PROCESO

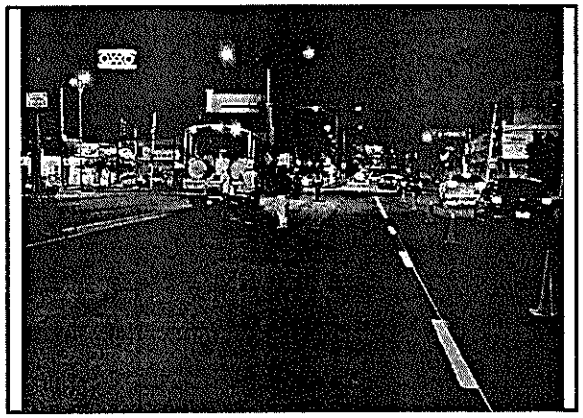







ING. RICARDO MACÍAS MERCADO
SUPERVISOR DE OBRA.

H. AYUNTAMIENTO DE AGUASCALIENTES

SECRETARÍA DE OBRAS PÚBLICAS


DIRECCIÓN DE SUPERVISIÓN DE OBRA


Aguascalientes
LA CIUDAD DE TU VIDA


MEMORIA FOTOGRAFICA


OBRA:	DM-0050-2022 - OBRA COMPLEMENTARIA Y SEÑALIZACIÓN Av. CONVENCIÓN 1914 SUR					
NO. DE CONTRATO:	DM-0050-2022		CONTRATISTA:	CASLOP DISEÑO ARTE Y CONSTRUCCION, S.A. DE C.V.		

TERMINO

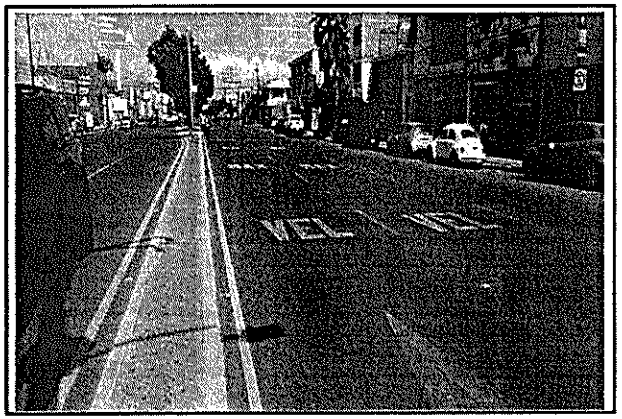


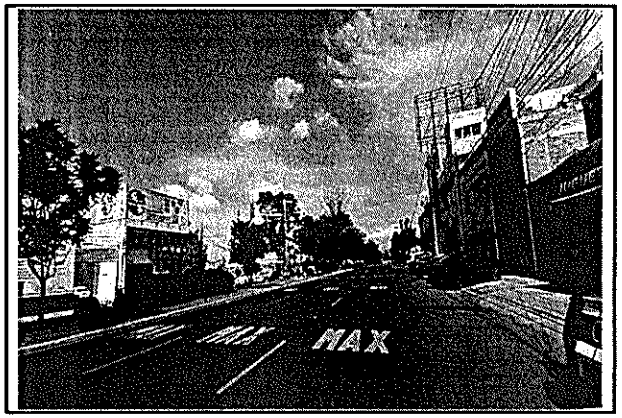


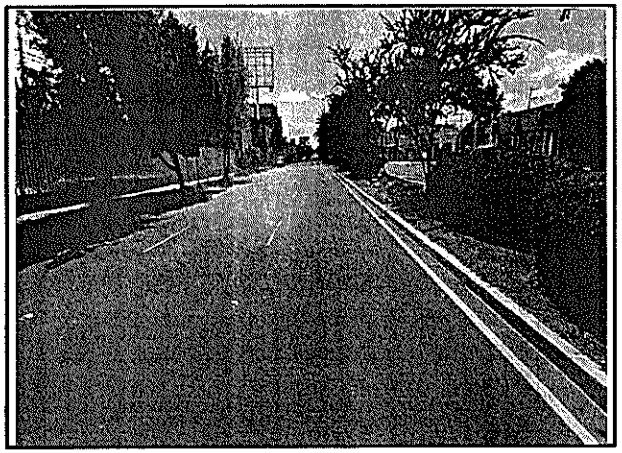

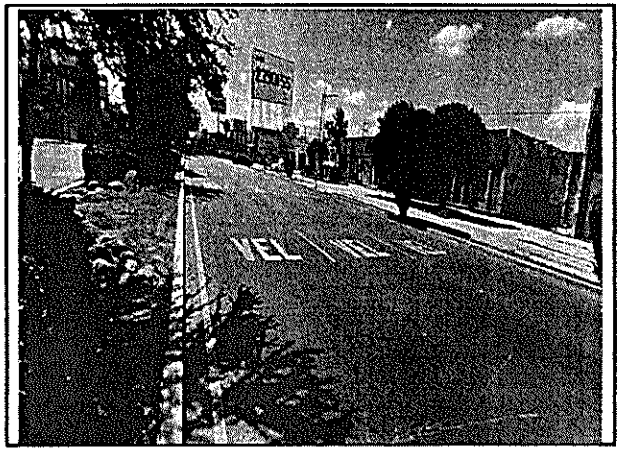

ING. RICARDO MACÍAS MERCADO
SUPERVISOR DE OBRA.

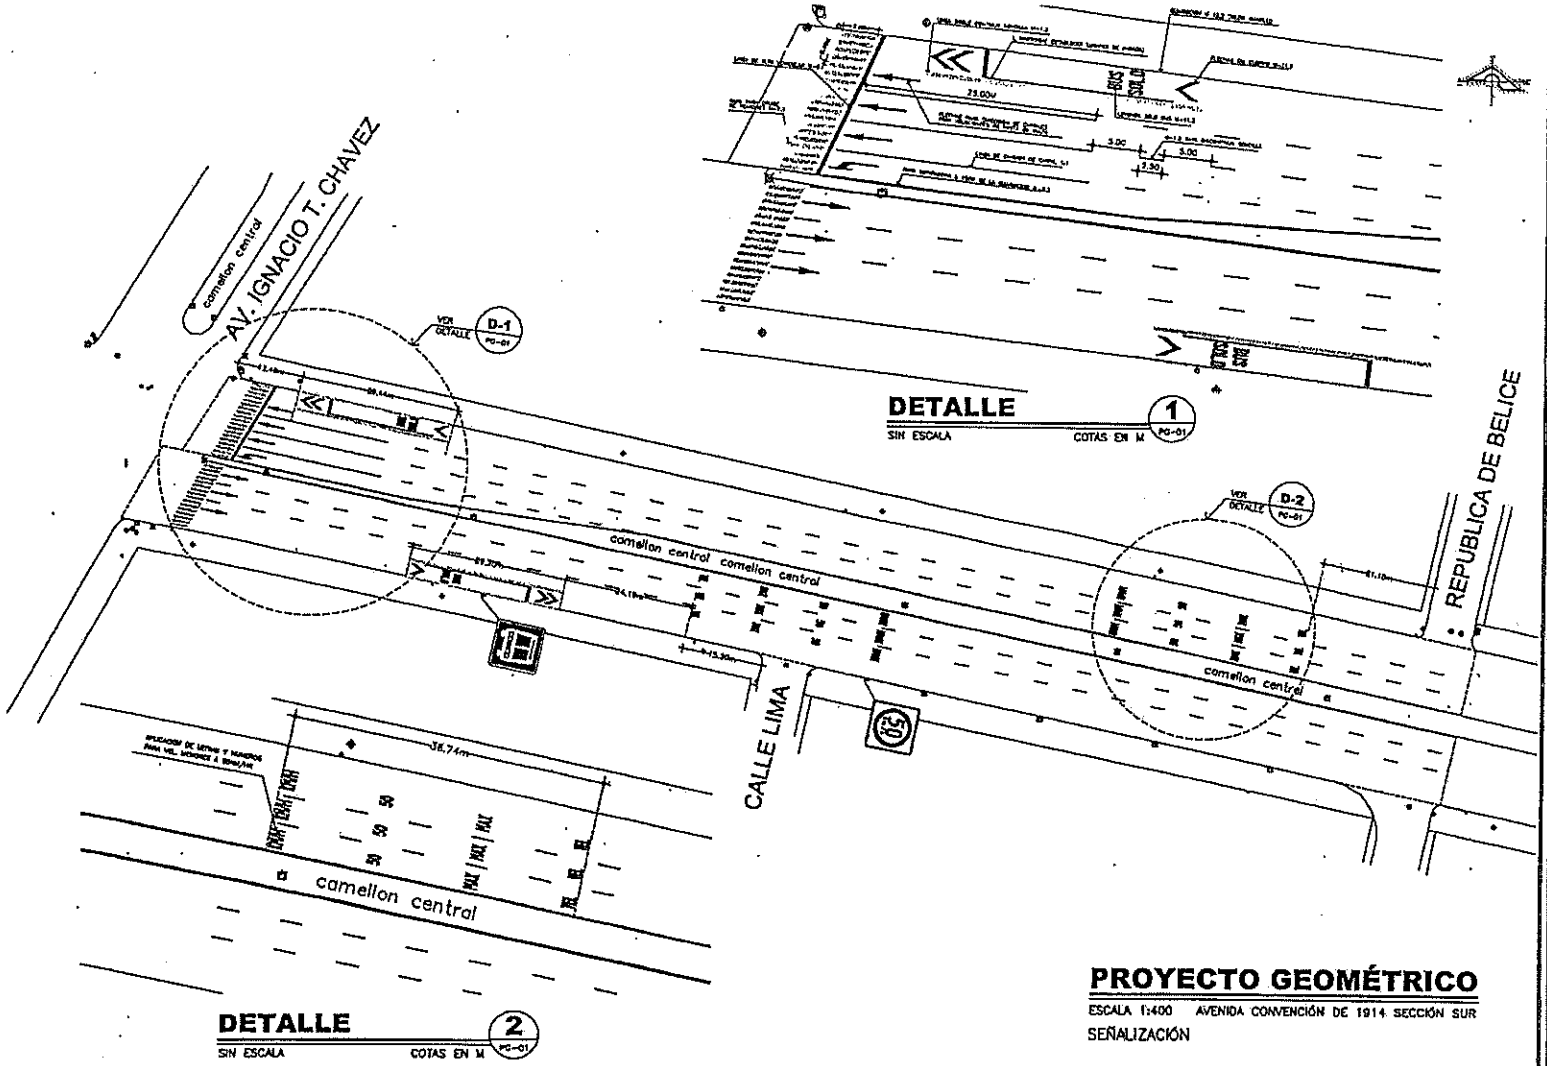
AV. IGNACIO T. CHAVEZ
camellon central
VER DETALLE D-1 PG-01
VER DETALLE D-2 PG-01
camellon central camellon central
camellon central
CALLE LIMA
REPUBLICA DE BELICE
camellon central
36.74m
50
50
50

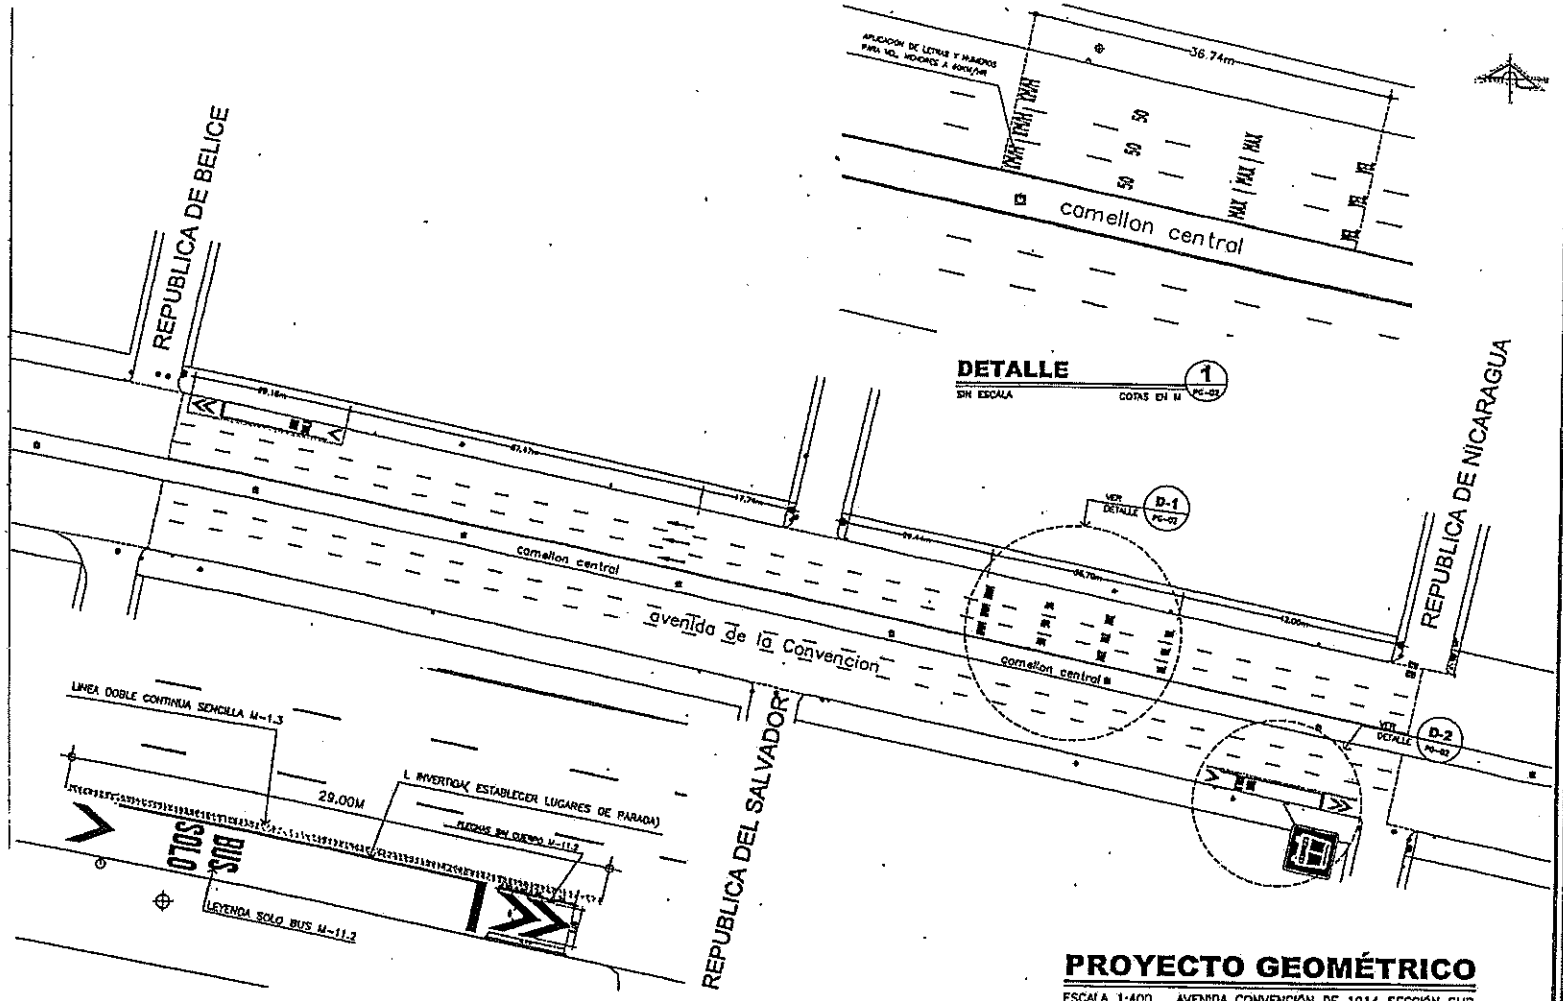


DETALLE 1
SIN ESCALA — COTAS EN M — PG-02

DETALLE 2
SIN ESCALA — COTAS EN M — PG-02

PROYECTO GEOMÉTRICO

ESCALA 1:400 AVENIDA CONVENCIÓN DE 1914 SECCIÓN SUR

SEÑALIZACIÓN

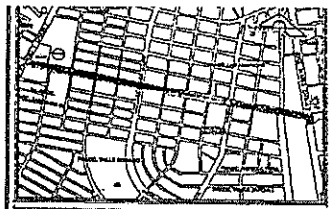

SIMBOLOGÍA

NOTA:

1.- VER DETALLES DE TRAZO ASI COMO SUS DESCRIPCIONES RESPECTIVAS EN LOS PLANOS 10,11 Y 12.

La Dirección de Planeación y Proyectos solo autoriza el proyecto ejecutivo, no es responsable de la correcta ejecución de la obra. Este documento no tiene validez si no presenta las firmas de los responsables para su autorización, así como los sellos respectivos.

PRESIDENTE MUNICIPAL
M.P.P. Leonardo Montañez Castro
ENCARGADA DE DESPACHO DE LA SOFMA
Arq. Gloria Guadalupe Castillo González

REV	FECHA	OBSERVACIONES

VO. BO. DE LA DEPENDENCIA

RESP. DE PROY. EXTERNO		LOGO EXTERNO
CED. PROFESIONAL		
PROYECTÓ	REVISÓ	AUTORIZÓ


Dirección de Planeación y Proyectos de Obra — Secretaría de Obras Públicas


PROYECTISTA	COORDINADOR
ING. DIEGO BRAVO AGUILERA	ARQ. ALEJANDRO JAIME LEAL
JEFE DE DEP.	DIRECTOR
ARQ. [illegible]	ING. [illegible]

PROYECTO	OBRA COMPLEMENTARIA Y SEÑALIZACIÓN AV. DE LA CONVENCIÓN DE 1914 SECCION SUR TRAMO 1
UBICACIÓN	AV. CONVENCIÓN DE 1914 SECCIÓN SUR, TRAMO DE CALLE REPUBLICA DE BELICE A CALLE REPUBLICA DE NICARAGUA
CONTENIDO	SEÑALIZACIÓN HORIZONTAL TRAMO "B"

CLAVE	No. PLANO
SEÑ 02	04
FECHA: MAR 2022	ESCALA: INDICADA
ACOTACIÓN: METROS	No. EXP.: E-005-22

Aguascalientes
LA CIUDAD DE TU VIDA

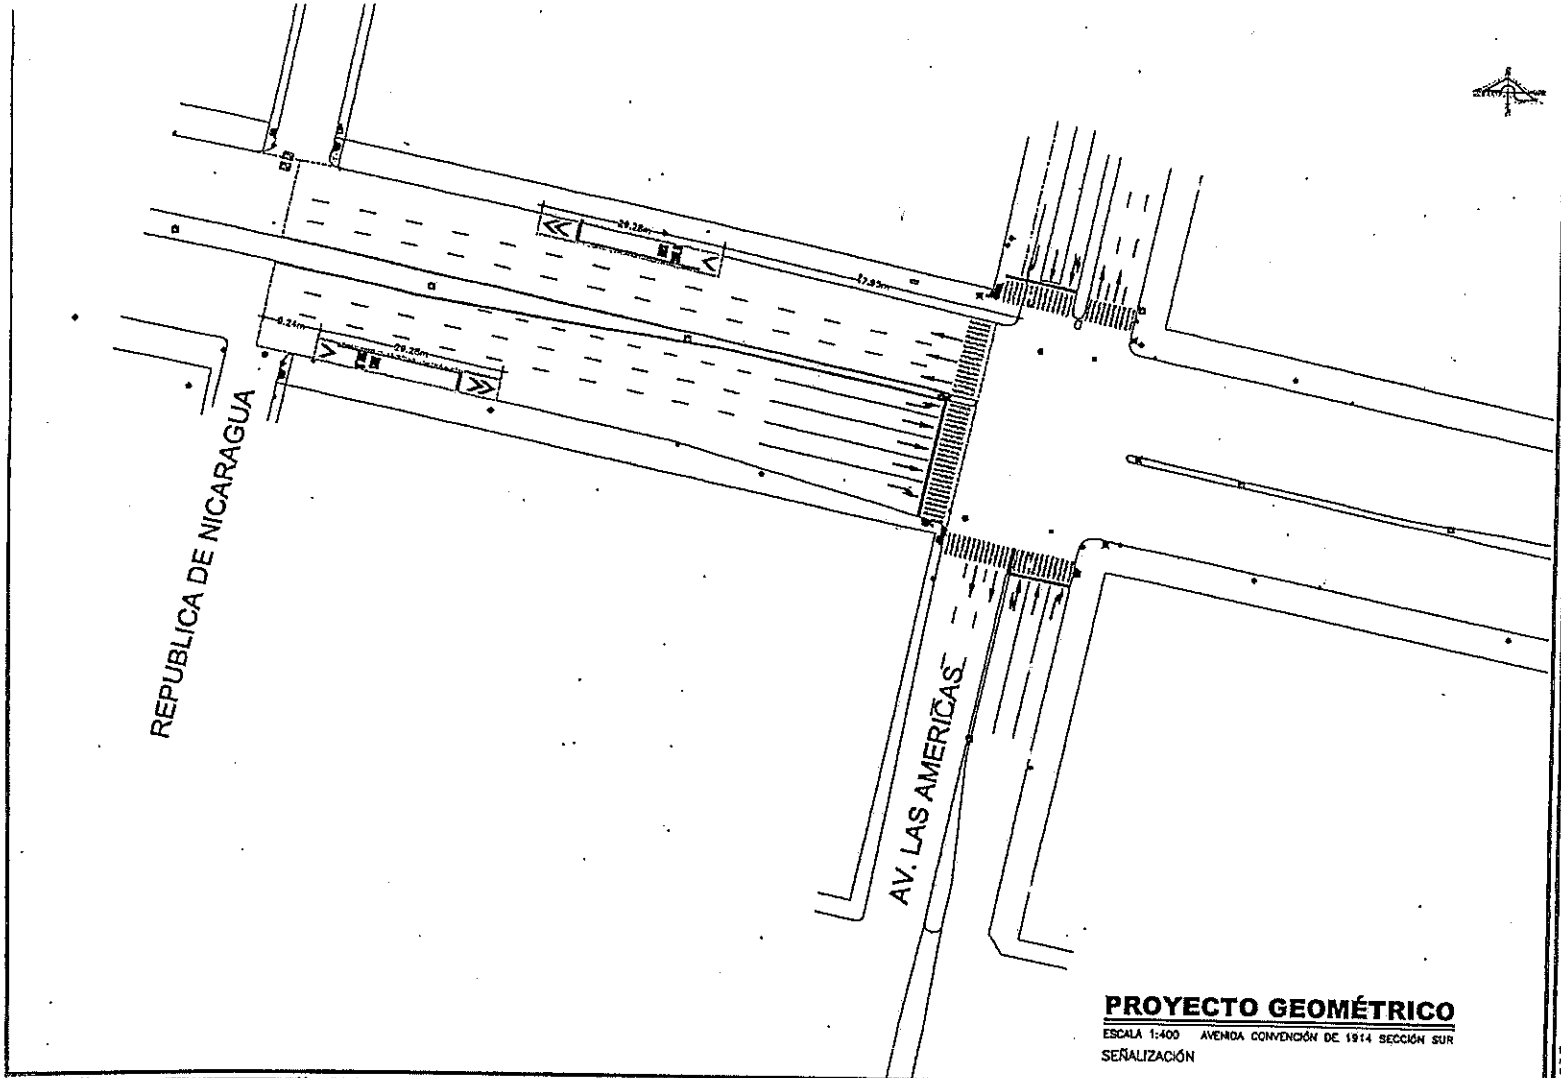

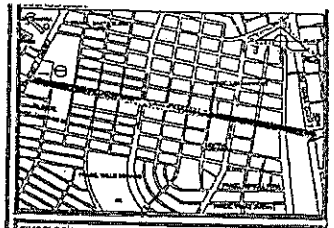

SIMBOLOGIA

NOTA:

1.- VER DETALLES DE TRAZO AS: COMO SUS DESCRIPCIONES RESPECTIVAS EN LOS PLANOS 10,11 Y 12.

PROYECTO GEOMÉTRICO

ESCALA 1:400 AVENIDA CONVENCIÓN DE 1914 SECCIÓN SUR

SEÑALIZACIÓN

La Dirección de Planeación y Proyectos solo autoriza el proyecto ejecutivo, no es responsable de la correcta ejecución de la obra. Este documento no tiene validez si no presenta los firmas de los responsables para su autorización, así como los sellos respectivos.

PRESIDENTE MUNICIPAL
M.P.P. Leonardo Montañez Castro
ENCARGADA DE DESPACHO DE LA SOPHA
Arq. Gloria Guadalupe Castillo González

REV	FECHA	OBSERVACIONES

Vo. Bo. DE LA DEPENDENCIA

RESP. DE PROY. EXTERNO		LOGO EXTERNO
DES. PROFESIONAL		
PROYECTO	REVISÓ	AUTORIZÓ

Dirección de Planeación y Proyectos de Obra — Secretaría de Obras Públicas

PROYECTISTA	COORDINADOR
ING. DIEGO ROMO AGUILERA	ARQ. ALEJANDRO JAIME LEAL
JEFE DE DEPT.	DIRECTOR
ARQ. L. JESÚS MURO GONZÁLEZ	ING. JOSÉ LUIS JIMÉNEZ GARCÍA


PROYECTO
OBRA COMPLEMENTARIA Y SEÑALIZACIÓN AV. DE LA CONVENCIÓN DE 1914 SECCIÓN SUR TRAMO 1


UBICACIÓN
AV. CONVENCIÓN DE 1914 SECCIÓN SUR, ENTRE CALLE REPUBLICA DE NICARAGUA Y AV. LAS AMERICAS

CONTENIDO
PLANTA SEÑALIZACIÓN TRAMO "C"

CLAVE	No. PLANO
SEÑ 03	05
FECHA: MAR 2022	ESCALA: INDICADA
ACOTACIÓN: METROS	No. EXP.: E-020-22

Aguascalientes
LA CIUDAD DE TU VIDA

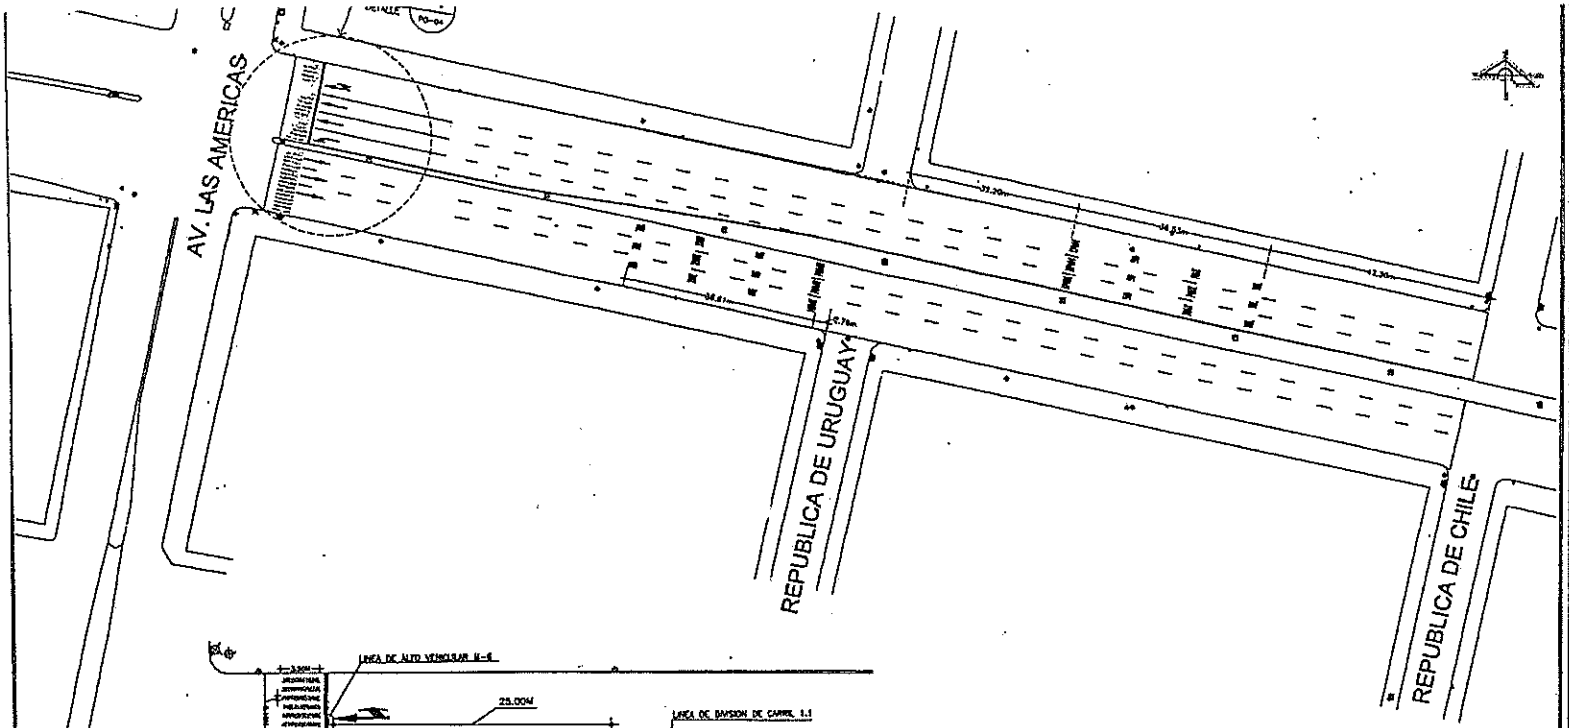


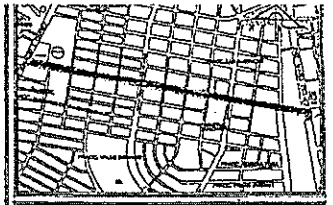

SIMBOLOGÍA

NOTA:

1.- VER DETALLES DE TRAZO ASI COMO SUS DESCRIPCIONES RESPECTIVAS EN LOS PLANOS 10,11 Y 12.

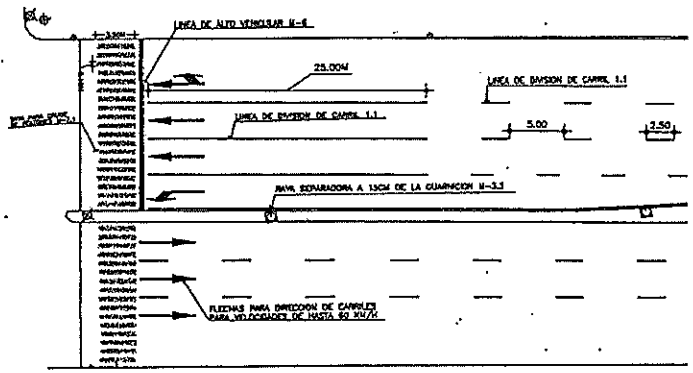

DETALLE 1 PD-01

SIN ESCALA COTAS EN M

PROYECTO GEOMÉTRICO

ESCALA 1:400 AVENIDA CONVENCIÓN DE 1914 SECCIÓN SUR

SEÑALIZACIÓN

La Dirección de Planeación y Proyectos solo autoriza el proyecto ejecutivo, no es responsable de la correcta ejecución de la obra. Este documento no tiene validez si no presenta los firmas de los responsables para su autorización, así como los sellos respectivos.

PRESIDENTE MUNICIPAL
M.P.P. Leonardo Montañez Castro
ENCARGADA DE DESPACHO DE LA SOPMA
Arq. Gloria Guadalupe Castillo González

REV.	FECHA	OBSERVACIONES

V.o. Bo. DE LA DEPENDENCIA

REGP. DE PROY. EXTERNO		LOGO EXTERNO
CED. PROFESIONAL		
PROYECTÓ	REVISÓ	AUTORIZÓ

Dirección de Planeación y Proyectos de Obra — Secretaría de Obras Públicas

PROYECTISTA	COORDINADOR
ING. DIEGO ROJO AGUILERA	ARQ. ALEJANDRO RAMÍREZ LEAL
JEFE DE DEP.	DIRECTOR
ING. L. ARMANDO ARVIZU GONZÁLEZ	M. en ARQ. JOSÉ LUIS NÚÑEZ CHACÓN

PROYECTO: CONV. COMPLEMENTARIA Y SEÑALIZACIÓN AV. DE LA CONVENCIÓN DE 1914 SECCIÓN SUR TRAMO 1

UBICACIÓN: AV. CONVENCIÓN DE 1914 SECCIÓN SUR TRAMO: DE AV. LAS AMERICAS A CALLE REPUBLICA DE CHILE

CONTENIDO: PLANTA SEÑALIZACIÓN TRAMO "D"

CLAVE	NO. PLANO
SEÑ 04	06
FECHA: MAR 2022	ESCALA: INDICADA
ACOTACIÓN: METROS	No. EXP.: E-000-22

Aguascalientes
LA CIUDAD DE TU VIDA