Aguascalientes
LA CIUDAD DE TU VIDA

Dirección de Programación Presupuestal
Núm. Oficio AMPP/0576/22
Aguascalientes, Ags. 8 de Diciembre del 2022
Asunto: Validación de Expediente Técnico

C.P. SERGIO ARTURO LOZANO GONZÁLEZ
SECRETARIO DE FINANZAS MUNICIPALES
P R E S E N T E

Con fundamento en los artículos 17 fracción XV, 60 fracción XVI y 76 fracción VI del Reglamento del Sistema Integral de Desarrollo Municipal y del Instituto Municipal de Planeación y Evaluación de Aguascalientes, hago referencia al oficio SOPMA/2733/2022 recibido por este Instituto el día 8 de Diciembre del 2022 por parte de la Secretaría de Obras Públicas Municipales, mediante el cual remiten el expediente técnico original de la siguiente obra para su análisis, registro y priorización, conforme al Programa Anual de Obra Pública y Programas Sociales para el ejercicio presupuestal 2022:

DEPENDENCIA EJECUTORA:	SOPMA
NOMBRE DE LA OBRA O PROYECTO:	OBRA COMPLEMENTARIA Y SEÑALIZACIÓN
UBICACIÓN:	BLVD. LUIS DONALDO COLOSIO MURRIETA, TRAMO: DE AV. UNIVERSIDAD A CALLE M. CORONADO, VARIAS COLONIAS, AGUASCALIENTES, AGS.
FONDO DE INVERSIÓN:	FONDO DE INFRAESTRUCTURA SOCIAL MUNICIPAL Y DE LAS DEMARCACIONES TERRITORIALES DEL DISTRITO FEDERAL
IMPORTE:	$548,573.00 (ET FINAL)
No. DE OBRA:	2022-FISMDF-0079-04-1101
MODALIDAD DE EJECUCIÓN:	CONTRATO
EJE:	MUNICIPIO SOBRESALIENTE
ESTRATEGIA:	OBRA PÚBLICA INTELIGENTE
POLITICA:	5.8.1.REHABILITACIÓN Y MANTENIMIENTO VIALIDADES, CAMINOS, CALLES, ÁREAS DE TERRACERÍA Y CAUCES (C

Al respecto, hago de su conocimiento que dicho expediente ha sido analizado en su integración técnica y documental, con base en el artículo 168 fracción I del Reglamento de la Ley de Obras Públicas y Servicios Relacionados para el Estado de Aguascalientes y sus Municipios.

Asimismo, le comento que este Instituto valida dicha obra acorde a lo establecido en los artículos 14, 22 párrafo segundo y 23 de la Ley de Obras Públicas y Servicios Relacionados para el Estado de Aguascalientes y sus Municipios, la cual se encuentra alineada al Plan de Desarrollo Municipal vigente, para dar cumplimiento a las metas establecidas en el mismo, y a los Lineamientos Generales para la Operación de este Fondo de Inversión, toda vez que la misma cuente con la autorización del CODEMUN. De igual manera, se hace de su conocimiento que deberá cumplir con lo establecido en los ordenamientos aplicables en lo que respecta al ejercicio, control e información de los recursos de este Fondo. Cabe hacer mención que los recursos solicitados para este proyecto de inversión, estarán sujetos a la disponibilidad presupuestal para el presente ejercicio fiscal que determine la Secretaría a su digno cargo. Sin otro particular por el momento, le envío un cordial saludo.

A T E N T A M E N T E

ARQ. AUSTRIA GABRIELA DÁVILA DE LA LLAVE
DIRECTORA GENERAL DEL IMPLAN

SEDR/ CAAR / JDBC
C.c.p. I.C. ING. MIGUEL ÁNGEL HUIZAR BOTELLO .- Secretaría de Obras Públicas Municipales .Para su conocimiento.
C.c.p. Archivo.

Instituto Municipal de Planeación y Evaluación de Aguascalientes
Antonio Acevedo Escobedo 103 A, Col. Centro
Aguascalientes, Ags. C.P. 20000
(449) 9101010 Ext. 3117
www.implanags.gob.mx

GOBIERNO MUNICIPAL DE AGUASCALIENTES

INSTITUTO MUNICIPAL DE PLANEACION

IMPLAN

ANÁLISIS INTEGRAL DE EXPEDIENTE TÉCNICO

No. DE OBRA (PAOP 2020):	2022-FISMDF-0079-04-1101	REGISTRO No.	248
OFICIO DE VALIDACIÓN:	AMPP/0576/22	FECHA RECIBIDO PARA REVISIÓN:	8 de Diciembre del 2022
PROGRAMA:	URBANIZACION MUNICIPAL	LOCALIDAD O COLONIA:	VARIAS COLONIAS
SUB-PROGRAMA:	0411- Calles y Caminos	DELEGACIÓN:	Aguascalientes
DEPENDENCIA:	Secretaría de Obras Públicas Municipales	MOD. DE EJECUCIÓN:	CONTRATO
NOMBRE DE LA OBRA:	OBRA COMPLEMENTARIA Y SEÑALIZACIÓN, BLVD. LUIS DONALDO COLOSIO MURRIETA, TRAMO: DE AV. UNIVERSIDAD A CALLE M. CORONADO		
FUENTE DE FINANCIAMIENTO:	FONDO DE INFRAESTRUCTURA SOCIAL MUNICIPAL Y DE LAS DEMARCACIONES TERRITORIALES DEL DISTRITO FEDERAL, FISMDF		
INVERSIÓN:	$548,573.00	CLASIFICACIÓN DE OBRA:	BIENES DE DOMINIO PUBLICA

TOTAL	FEDERAL	ESTATAL	MUNICIPAL	BENEFICIARIOS	OTROS	DIFERENCIA ENTRE MOD.
$548,573.00	$548,573.00	0.00	0.00	0.00	0.00	*$21.961,84*

TIPO DE EXPENDIENTE:	ET FINAL	AÑO: 2022	AÑO:	AÑO:
AVANCES:	Financiero: 5 %	Físico: 5 %		
FECHA DE INICIO:	11 de Noviembre del 2022	FECHA DE TÉRMINO:	10 de Diciembre del 2022	REGISTRO SIMA: 79

CHEK LIST DE LOS ANEXOS DEL EXPEDIENTE TÉCNICO

CÉDULA DE REGISTRO DE OBRA	✓
DICTAMEN DE FACTIBILIDAD	✓
MEMORIA DESCRIPTIVA	✓
PRESUPUESTO BASE	✓
FACTIBILIDAD VERIFICADA EN CAMPO	✓
CROQUIS DE UBICACIÓN (MACRO)	✓
CROQUIS DE UBICACIÓN (MACRO)	✓
PROGRAMA DE OBRA Y MONTOS MENSUALES	✓
PLANOS O ESTUDIOS TÉCNICOS	✓
PADRÓN DE BENEFICIARIOS	N/A
ACTA DE ACEPTACIÓN DEL PROYECTO	N/A
DICTAMEN DE IMPACTO AMBIENTAL	N/A
CONVENIO DE CONCERTACIÓN	N/A
ACTA CONSTITUTIVA	N/A

METAS		BENEFICIARIOS		PERIODO DE EJECUCION		OBRA PROPUESTA		CLAVE SISCO
UNIDAD DE MEDIDA	CANT	TIPO DE BENEFICIARIOS	CANTIDAD	FECHA DE INICIO	FECHA DE TERMINO	CONCEPTO	JORNALES A GENERAR	
OBRA	1	Personas	150	2022-11-11	2022-12-10	Obra Complementaria y/o Señalización	1426	2350

INCLUIDO EN PLAN DE DESARROLLO MUNICIPAL Y EL PROGRAMA ANUAL DE OBRA PÚBLICA

OBSERVACIONES:

SIN OBSERVACIONES

RECIBIO: ING. JOSÉ DAVID BURGUETE CLAUSTRO
Analista de Programación e Inversión de Obra Pública

8 de Diciembre del 2022
Fecha de validación

8 de Diciembre del 2022
Fecha de validación Expediente

PROCEDE Si ✓ No

H. AYUNTAMIENTO CONSTITUCIONAL DEL MUNICIPIO DE AGUASCALIENTES 2021-2024

AYUNTAMIENTO DE AGUASCALIENTES

CEDULA DE REGISTRO POR OBRA

Aguascalientes

050400-001E00E05-05-2-2-1-00-1-E-0510-0-17-0079-21-2502-6144

2022-FISMDF-0079-0411109-034	Obra **OBRA COMPLEMENTARIA Y SEÑALIZACIÓN BLVD. LUIS DONALDO COLOSIO**
Tipo DEFINITIVO 1 2022 Folio SISCO **2350**	Ubic. TRAMO: ENTRE BLVD. MIGUEL DE LA MADRID Y CALLE MONTE CORONADO, AGUASCALIENTES Mpio.

Ent. Ejecutora : **050400001E00E05**

Eje: **05**	MUNICIPIO SOBRESALIENTE
Finalidad: **2**	DESARROLLO SOCIAL
Función: **2**	VIVIENDA Y SERVICIOS A LA COMUNIDAD
Subfunción: **1**	URBANIZACIÓN
Tema: **00**	SIN TEMA
Cuenta del Gasto **1**	GASTO PROGRAMABLE
Clasif. Programatica: **E**	PRESTACIÓN DE SERVICIOS PÚBLICOS
Programa: **0510**	Movilidad Urbana
SubPrograma: **0**	SUBPROGRAMA GENÉRICO
Proyecto: **17**	
Tipo de Gasto: **21**	GASTO INVERSIÓN / OBRA PÚBLICA

I N V E R S I O N 2022

Municipal	2502	FONDO PARA LA INFRAESTRUCTURA SOCIAL MUNICIPAL Y DE LAS DEMARCACIONES TERRITORIALES DEL DISTRITO FEDERAL 2022	$548,573.00

Folio SIMA 79 Total $548,573.00

M E T A S

Unidad de Medida	Cantidad	Descripción
OBRA	1	OBRA OBRA COMPLEMENTARIA Y SEÑALIZACIÓN BLVD. LUIS DONALDO COLOSIO

Inversión Ejercida Total al 31 de Diciembre de 2021 $0.00

Avance Fisico Acumulado al 31 de Diciembre de 2021

Avance Fisico Acumulado Programado al 31 de Diciembre de 2022 100 %

Fecha de Inicio 11 Nov 2022 Fecha de Terminación 10 Dic 2022

Jornales a Generar en 2022 1426

Modalidad de ejecución CONTRATO

Clasificación de la Obra Bienes de Dominio Público

Registro del Patrimonio: Obras del dominio público

OBRAS PÚBLICAS

Av. Aguascalientes Sur No. 2615
Fracc. Jardines de las Fuentes,
Aguascalientes, Ags. C.P. 20278

(449) 9 78 92 01, 06, 09

www.ags.gob.mx

GENERALES

Nombre del Proyecto : OBRA COMPLEMENTARIA Y SEÑALIZACIÓN BLVD. LUIS DONALDO COLOSIO

TRAMO: ENTRE BLVD. MIGUEL DE LA MADRID Y CALLE MONTE CORONADO, AGUASCALIENTES Mpio.

Programa : 04 URBANIZACION MUNICIPAL

Subprograma : 11 Calles y caminos (428.- Rehabilitación: 0411208- Señalización)

Clave del Municipio : AGUASCALIENTES

Localidad :

Barrio, Colonia o Ejido : AGUASCALIENTES Mpio.

Tipo de Obra : NUEVA

DESCRIPCIÓN DEL PROYECTO:

OBRA COMPLEMENTARIA Y SEÑALIZACIÓN BLVD. LUIS DONALDO COLOSIO

SEÑALIZACIÓN HORIZONTAL 1.00 OBRA

Beneficiarios (No. y Tipo) :

150	PERSONAS

Hombres: 70 Mujeres: 80

OBRAS PÚBLICAS

Los abajo firmantes, hacen constar que el presente proyecto :

OBRA COMPLEMENTARIA Y SEÑALIZACIÓN BLVD. LUIS DONALDO COLOSIO

TRAMO: ENTRE BLVD. MIGUEL DE LA MADRID Y CALLE MONTE CORONADO, AGUASCALIENTES Mpio.

cumple con los Requisitos y Normas Técnicas establecidas por la Dependencia Normativa, por lo que es viable su ejecución. Comprometiéndose la misma a proporcionar la supervisión y asistencia técnica necesaria durante el proceso administrativo.

Por la Dependencia Ejecutora

Ing. Miguel Angel Huizar Botello
Secretario de Obras Públicas

Lic. Jaime Gallo Camacho
Secretario de Desarrollo Urbano

LUGAR :AGUASCALIENTES, AGS.

SECRETARÍA DE OBRAS PÚBLICAS

Av. Aguascalientes Sur No. 2615
Fracc. Jardines de las Fuentes,
Aguascalientes, Ags. C.P. 20278

(449) 9 78 92 01, 06, 09

www.ags.gob.mx

H. AYUNTAMIENTO CONSTITUCIONAL DEL MUNICIPIO DE AGUASCALIENTES 2021-2024

AYUNTAMIENTO DE AGUASCALIENTES

FACTIBILIDAD VERIFICADA EN CAMPO

Aguascalientes
LA CIUDAD DE TU VIDA

MUNICIPIO: AGUASCALIENTES

LOCALIZACION: TRAMO: ENTRE BLVD. MIGUEL DE LA MADRID Y CALLE MONTE CORONADO, AGUASCALIENTES Mpio.

PROGRAMA: URBANIZACION MUNICIPAL

SUBPROGRAMA: Calles y caminos (428.- Rehabilitación: 0411208- Señalización)

OBRA A REALIZAR: OBRA COMPLEMENTARIA Y SEÑALIZACIÓN BLVD. LUIS DONALDO COLOSIO

DEPENDENCIA EJECUTORA: SECRETARÍA DE OBRAS PUBLICAS DEL MUNICIPIO DE AGUASCALIENTES

FORMA DE EJECUCION: CONTRATO

TIPO DE OBRA PROPUESTA: NUEVA

CONDICIONES ACTUALES DE LA OBRA:

OBRA COMPLEMENTARIA Y SEÑALIZACIÓN BLVD. LUIS DONALDO COLOSIO

CARACTERISTICAS DE LA OBRA: Bueno

FACTIBILIDAD DE LA OBRA:

ESTA OBRA SE REQUIERE PARA EL BENEFICIO DE LA CIUDADANÍA

PROCEDE: SI [X] NO [ ]

REVISÓ: Jefa del Departamento de Expedientes Tecnicos y Costos

NOMBRE: Arq. Blanca Margarita Martinez Amador

FIRMA:

FECHA: 29 Nov 2022

SECRETARÍA DE OBRAS PÚBLICAS

Av. Aguascalientes Sur No. 2615
Fracc. Jardines de las Fuentes,
Aguascalientes, Ags. C.P. 20278

(449) 9 78 92 01, 06, 09

www.ags.gob.mx

No. Folio SISCO 2350

H. AYUNTAMIENTO CONSTITUCIONAL DEL MUNICIPIO DE AGUASCALIENTES 2021-2024

H. AYUNTAMIENTO DE AGUASCALIENTES
SECRETARÍA DE OBRAS PÚBLICAS
DIRECCIÓN DE SUPERVISIÓN DE OBRA
LOCALIZACION

Aguascalientes
LA CIUDAD DE TU VIDA

OBRA:	OBRA COMPLEMENTARIA Y SEÑALIZACIÓN BLVD, LUIS DONALDO COLOSIO,TRAMO ENTRE MIGUEL DE LA MADRID Y CALLE MONTE COLORADO ., AGUASCALIENTES Mpio.					
NO. DE CONTR	FISMDF-0079-2022		CONTRATISTA:	AVACO ARQUITECTOS S.A DE C.V		



ING.DAVID ALONSO MONTOYA
SUPERVISOR DE OBRA.

H. AYUNTAMIENTO CONSTITUCIONAL DEL MUNICIPIO DE AGUASCALIENTES 2021-2024

H. AYUNTAMIENTO DE AGUASCALIENTES
SECRETARÍA DE OBRAS PÚBLICAS
DIRECCIÓN DE SUPERVISIÓN DE OBRA
LOCALIZACION

Aguascalientes
LA CIUDAD DE TU VIDA

OBRA:	OBRA COMPLEMENTARIA Y SEÑALIZACIÓN BLVD, LUIS DONALDO COLOSIO,TRAMO ENTRE MIGUEL DE LA MADRID Y CALLE MONTE COLORADO ., AGUASCALIENTES Mpio.					
NO. DE CONTR	FISMDF-0079-2022		CONTRATISTA:	AVACO ARQUITECTOS S.A DE C.V		



ING.DAVID ALONSO MONTOYA
SUPERVISOR DE OBRA.

R03-POS-SOS-7.5.1-04	
REVISION:	00
FECHA DE REVISION:	
RESPONSABLE:	SUPERVISOR DE OBRA
TIEMPO DE RET:	02 AÑOS

PROGRAMA DE OBRA DEFINITIVO

No. DE CONTRATO : FISMDF-0079-2022

PROGRAMA: 04 URBANIZACION MUNICIPAL

No. OBRA Y NOMBRE DE LA OBRA: OBRA COMPLEMENTARIA Y SEÑALIZACIÓN BLVD, LUIS LEONALDO COLOSIO,TRAMO ENTRE MIGUEL DE LA MADRID Y CALLE MONTE COLORADO ., AGUASCALIENTES Mpio.

INICIO VIGENTE: 11-noviembre-22

TERMINO REAL: 10-diciembre-22

RECURSO 2022

CONCEPTO			1	2	3	4	5	6	7	8	9	10	11	12	13	14	15	16	PONDERACIÓN %	
			2021																	
			OCTUBRE	NOVIEMBRE	DICIEMBRE	ENERO	FEBRERO	MARZO	ABRIL	MAYO	JUNIO	JULIO	AGOSTO	SEPTIEMBRE	OCTUBRE	NOVIEMBRE	DICIEMBRE	ENERO	FINANCIERO	FÍSICO
DESCRIPCION	INVERSION																			
OBRA COMPLEMENTARIA Y SEÑALIZACIÓN BLVD, LUIS LEONALDO COLOSIO,TRAMO ENTRE MIGUEL DE LA MADRID Y CALLE MONTE COLORADO ., AGUASCALIENTES Mpio.																				
TRAMO;ENTRE BLVD;MIGUEL DE LA MADRID Y CALLE MONTE COLORADO																				
SEÑALIZACION HORIZONTAL	$ 472,907.76	100														25	25	25	100.00	100.00
																			0.00	0.00
SUBTOTAL SIN IVA	$ 472,907.76		0	0	0	0	0	0	0	0	0	0	0	0	0	1	1	1		
AVANCE SEMANAL %			0%	0%	0%	0%	0%	0%	0%	0%	0%	0%	0%	0%	0%	25%	25%	25%		
AVANCE SEMANAL ACUMULADO %			0%	0%	0%	0%	0%	0%	0%	0%	0%	0%	0%	0%	0%	25%	50%	75%	100.00	100.00
EJERCIDO SEMANAL $																118,226.94	118,226.94	118,226.94		
EJERCIDO MENSUAL $			$0.00	$0.00	$0.00	$0.00	$0.00	$0.00	$0.00	$0.00	$0.00	$0.00	$0.00	$0.00	$0.00	$354,680.82	$118,226.94	$0.00	$ 472,907.76	
EJERCIDO MENSUAL ACUMULADO $			0.00	0.00	0.00	0.00	0.00	0.00	0.00	0.00	0.00	0.00	0.00	0.00	0.00	354,680.82	472,907.76	472,907.76	$ 75,665.24	IVA 16%
EJERCIDO SEMANAL %			0%	0%	0%	0%	0%	0%	0%	0%	0%	0%	0%	0%	0%	25%	25%	25%		
EJERCIDO MENSUAL %			0%	0%	0%	0%	0%	0%	0%	0%	0%	0%	0%	0%	0%	75%	25%	0%	GRAN TOTAL EJERCIDO	
EJERCIDO MENSUAL ACUMULADO %			0%	0%	0%	0%	0%	0%	0%	0%	0%	0%	0%	0%	0%	75%	100%	100%	$	548,573.00

PRE

ING DAVID ALONSO MONTOYA
SUPERVISOR

PRESIDENCIA MUNICIPAL DE AGUASCALIENTES

FACTIBILIDAD VERIFICADA EN CAMPO

GENERALES

EJERCICIO:	2022	APROBACION No:	2022-FISMDF-0079-0411
LOCALIDAD:	TRAMO:ENTRE BLVD,MIGUEL DE LA MADRID Y CALLE MONTE COLORADO		
MUNICIPIO:	AGUASCALIENTES, Mpio.		
TIPO DE INVERSION	FONDO PARA LA INFRAESTRUCTURA SOCIAL MUNICIPAL Y DE LAS DEMARCACIONES TERRITORIALES DEL DISTRITO FEDERAL (100%) (MUNICIPAL)		
PROGRAMA:	04 URBANIZACION MUNICIPAL		
SUB-PROGRAMA:	11 Calles y caminos		
OBRA A REALIZARSE:	OBRA COMPLEMENTARIA Y SEÑALIZACIÓN BLVD, LUIS DONALDO COLOSIO,TRAMO ENTRE MIGUEL DE LA MADRID Y CALLE MONTE COLORADO ., AGUASCALIENTES Mpio.		
DEPENDENCIA EJECUTORA:	SECRETARÍA DE OBRAS PÚBLICAS MUNICIPALES (S.O.P.M.A)		
FORMACIÓN DE EJECUCION:	CONTRATO	NO. DE CONTRATO:	FISMDF-0079-2022
NOMBRE CONTRATISTA:	AVACO ARQUITECTOS S.A DE C.V		
REPRESENTANTE:	AVACO ARQUITECTOS S.A DE C.V		
MONTO CONT. ORIGEN	$ 558,743.00	ANTICIPO:	$ 144,502.50 PLAZO 30 DIAS
1A AMPLIACION $:	$ -		
2A AMPLIACION $:			
FIRMA CONTRATO:	17/10/2022		
INICIO CONT: dd/mm/aa	18/10/2022	TERMINO CONT:	17/11/2022
INICIO REAL: dd/mm/aa	11/11/2022	TERMINO REAL:	10/12/2022

TIPO DE OBRA PROPUESTA

NUEVA CREACIÓN		CONSOLIDACIÓN	
COMPLEMENTARIA	X	AMPLIACIÓN	
REHABILITACIÓN		EQUIPAMIENTO	

CARACTERÍSTICAS DE LA OBRA:

PINTURA EN GUARNICION
PINTURA PARADA DE CAMIONES, LINEA DIVISION DE CARRIL
VIALETAS SOLARES, SEÑALIZACION VERTICAL

CONDICIONES ACTUALES DE LA OBRA: (SELECCIONAR UNO OBLIGATORIO)

BUEN ESTADO X REGULAR PESIMO ESTADO

FACTIBILIDAD DE LA OBRA: (CONDICIONES ACTUALES DE LA OBRA)

ESTA OBRA SE ENCUENTRA EN CONDICIONES PARA OPERARSE

PROCEDE: SI: X NO:
MARQUE SOLO UNA

ING.DAVID ALONSO MONTOYA
SUPERVISOR

PRESIDENCIA MUNICIPAL DE AGUASCALIENTES

FACTIBILIDAD VERIFICADA EN CAMPO

GENERALES

LOCALIDAD: TRAMO:ENTRE BLVD,MIGUEL DE LA MADRID Y CALLE MONTE COLORADO
MUNICIPIO: AGUASCALIENTES, Mpio.
PROGRAMA: 04 URBANIZACION MUNICIPAL
SUB-PROGRAMA: 11 Calles y caminos
OBRA A REALIZARSE: OBRA COMPLEMENTARIA Y SEÑALIZACIÓN BLVD, LUIS DONALDO COLOSIO,TRAMO ENTRE MIGUEL DE LA MADRID Y CALLE MONTE COLORADO ., AGUASCALIENTES Mpio.

DEPENDENCIA EJECUTORA: SECRETARÍA DE OBRAS PÚBLICAS MUNICIPALES (S.O.P.M.A)
FORMACIÓN DE EJECUCION: CONTRATO

TIPO DE OBRA PROPUESTA

NUEVA CREACIÓN		CONSOLIDACIÓN	
COMPLEMENTARIA	X	AMPLIACIÓN	
REHABILITACIÓN		EQUIPAMIENTO	

CARACTERÍSTICAS DE LA OBRA:

PINTURA EN GUARNICION
PINTURA PARADA DE CAMIONES, LINEA DIVISION DE CARRIL
VIALETAS SOLARES, SEÑALIZACION VERTICAL

CONDICIONES ACTUALES DE LA OBRA:

BUEN ESTADO:	X	REGULAR:		PESIMO ESTADO:	

FACTIBILIDAD DE LA OBRA:

ESTA OBRA SE ENCUENTRA EN CONDICIONES PARA OPERARSE

PROCEDE	**SI:**	X	**NO:**		

ING.DAVID ALONSO MONTOYA
SUPERVISOR

PRESUPUESTO MODIFICADO

Obra: OBRA COMPLEMENTARIA Y SEÑALIZACIÓN BLVD. LUIS DONALDO COLOSIO

Ubicación: TRAMO: ENTRE BLVD. MIGUEL DE LA MADRID Y CALLE MONTE CORONADO, AGUASCALIENTES Mpio.

Contratista: AVACO ARQUITECTOS, S.A. DE C.V. (59)

No.	Concepto	Unidad	Cantidad	Precio Unitario	Importe Total
	GRUPO: OBRA COMPLEMENTARIA Y SEÑALIZACION				
	PARTIDA: SEÑALIZACION HORIZONTAL				
1	SUMINISTRO Y APLICACIÓN DE PINTURA BASE SOLVENTE (ESMALTE) PARA MARCAS EN GUARNICIONES CLASIFICACION M-12.1, M12.2 APLICADA SOBRE GUARNICIONES Y DENTELLONES COLOR BLANCA Y/O AMARILLA, SEGÚN SE REQUIERA Y SEGÚN MANUAL DE SEÑALIZACIÓN VIAL Y DISPOSITIVOS DE SEGURIDAD SICT (S.C.T). SECADO AL TACTO EN 5 MIN Y AL DURO EN 30 MIN CON MICRO ESFERA , DESARROLLO DE 35 CM. INCLUYE: MATERIALES Y ESPECIFICACIONES QUE CUMPLAN CON LA NORMATIVA N-CMT-5-01-001/13, N-PRY-CAR-10-01-002/13 APLICADAS AL DIA DE HOY, TRAZO, MANO DE OBRA, LIMPIEZA PREVIA Y FINAL DE SUPERFICIE, EQUIPO NECESARIO PARA SU EJECUCIÓN, Y TODO LO NECESARIO PARA SU CORRECTA EJECUCIÓN, TRABAJO TERMINADO.	ML	1650	$52.51	$86,641.50
2	SUMINISTRO Y APLICACIÓN DE PINTURA TERMOPLASTICA ALQUIDALICA DE 120 MILESIMAS DE " (in) EN RAYA SEPARADORA DE SENTIDOS DE CIRCULACION CLASIFICACIÓN M - 1.1, LÍNEA CONTINUA SENCILLA DE DIVISIÓN DE CARRILES DE FRENTE EN PISO, DE 10 CM DE ANCHO, COLOR BLANCO Y/O AMARILLO CON MICRO ESFERA SEGÚN MANUAL DE SEÑALIZACIÓN VIAL Y DISPOSITIVOS DE SEGURIDAD SICT, SECADO AL TACTO EN 5 MIN Y AL DURO EN 30 MIN. INCLUYE: MATERIALES Y ESPECIFICACIONES QUE CUMPLAN CON LA NORMATIVA N-CMT-5-01-001/13, N-PRY-CAR-10-01-002/13 APLICADAS AL DIA DE HOY, MATERIAL APLICADO EN SU ESTADO DE FUSION A UNA TEMPERATURA MINIMA DE 204 C, LA SUPERFICIE DE CONCRETO O ASFALTO NO DEBE PRESENTAR UNA TEMPERATURA MENOR A LOS 10 C, ;TIEMPO DE SECADO EN RANGOS DE TEMPERATURA DE 10 C DEL SUSTRATO 2 MINUTOS, Y NO MAS DE 10 MINUTOS CUANDO EL SUSTRATO OSCILA ALREDEDOR DE 54C, TRAZO, ENMASCARILLADO, MANO DE OBRA, LIMPIEZA PREVIA Y FINAL DE SUPERFICIE, EQUIPO NECESARIO PARA SU EJECUCIÓN, Y TODO LO NECESARIO PARA SU CORRECTA EJECUCIÓN, TRABAJO TERMINADO.	ML	150	$85.52	$12,828.00
3	SUMINISTRO Y APLICACIÓN DE PINTURA TERMOPLASTICA ALQUIDALICA DE 120 MILESIMAS DE " (in) EN RAYA SEPARADORA DE SENTIDOS DE CIRCULACION CLASIFICACIÓN M - 1.2, RAYA DISCONTINUA SENCILLA, DE DIVISIÓN DE CARRILES PARA VELOCIDADES MENORES A 60 KM/HR DE FRENTE EN PISO, DESARROLLO DE 2.50 ML X 0.10 MTS DE ANCHO, CON UNA SEPARACIÓN DE 5.00 MTS ENTRE SI PROMEDIO, A BASE DE PINTURA PARA TRAFICO COLOR BLANCO CON MICRO ESFERA SEGÚN MANUAL DE SEÑALIZACIÓN VIAL Y DISPOSITIVOS DE SEGURIDAD SICT (S.C.T). INCLUYE: MATERIALES Y ESPECIFICACIONES QUE CUMPLAN CON LA NORMATIVA N-CMT-5-01-001/13, N-PRY-CAR-10-01-002/13 APLICADAS AL DIA DE HOY, MATERIAL APLICADO EN SU ESTADO DE FUSION A UNA TEMPERATURA MINIMA DE 204 C, LA SUPERFICIE DE CONCRETO O ASFALTO NO DEBE PRESENTAR UNA TEMPERATURA MENOR A LOS 10 C, ;TIEMPO DE SECADO EN RANGOS DE TEMPERATURA DE 10 C DEL SUSTRATO 2 MINUTOS, Y NO MAS DE 10 MINUTOS CUANDO EL SUSTRATO OSCILA ALREDEDOR DE 54C, TRAZO, ENMASCARILLADO, MANO DE OBRA, LIMPIEZA PREVIA Y FINAL DE SUPERFICIE, EQUIPO NECESARIO PARA SU EJECUCIÓN, Y TODO LO NECESARIO PARA SU CORRECTA EJECUCIÓN, TRABAJO TERMINADO.	ML	255	$85.52	$21,807.60

Obra: OBRA COMPLEMENTARIA Y SEÑALIZACIÓN BLVD. LUIS DONALDO COLOSIO

Ubicación: TRAMO: ENTRE BLVD. MIGUEL DE LA MADRID Y CALLE MONTE CORONADO, AGUASCALIENTES Mpio.

Contratista: AVACO ARQUITECTOS, S.A. DE C.V. (59)

No.	Concepto	Unidad	Cantidad	Precio Unitario	Importe Total
	GRUPO: OBRA COMPLEMENTARIA Y SEÑALIZACION				
	PARTIDA: SEÑALIZACION HORIZONTAL				
6	SUMINISTRO Y APLICACIÓN DE PINTURA TERMOPLASTICA ALQUIDALICA DE 120 MILESIMAS DE " (in) EN RAYA DE ALTO CLASIFICACIÓN M - 6, PARA INDICAR ALTO EN CRUCEROS, COLOR BLANCO, REFLEJANTE CON MICRO ESFERA DE VIDRIO EN PROPORCIÓN SEGÚN MANUAL DE SEÑALIZACIÓN VIAL Y DISPOSITIVOS DE SEGURIDAD SICT (S.C.T). DE 0.60 MTS DE ANCHO DE LONGITUD VARIABLE, INCLUYE: MATERIALES Y ESPECIFICACIONES QUE CUMPLAN CON LA NORMATIVA N-CMT-5-01-001/13, N-PRY-CAR-10-01-002/13 APLICADAS AL DIA DE HOY, MATERIAL APLICADO EN SU ESTADO DE FUSION A UNA TEMPERATURA MINIMA DE 204 C, LA SUPERFICIE DE CONCRETO O ASFALTO NO DEBE PRESENTAR UNA TEMPERATURA MENOR A LOS 10 C, ;TIEMPO DE SECADO EN RANGOS DE TEMPERATURA DE 10 C DEL SUSTRATO 2 MINUTOS, Y NO MAS DE 10 MINUTOS CUANDO EL SUSTRATO OSCILA ALREDEDOR DE 54C, TRAZO, ENMASCARILLADO, MANO DE OBRA, LIMPIEZA PREVIA Y FINAL DE SUPERFICIE, EQUIPO NECESARIO PARA SU EJECUCIÓN, Y TODO LO NECESARIO PARA SU CORRECTA EJECUCIÓN, TRABAJO TERMINADO.	ML	105.6	$435.10	$45,946.56
7	SUMINISTRO Y APLICACIÓN DE PINTURA TERMOPLASTICA ALQUIDALICA DE 120 MILESIMAS DE " (in) EN RAYA PARA CRUCE PEATONAL CLASIFICACIÓN M - 7.1, PARA INDICAR " CRUCE PEATONAL EN VIAS PRIMARIAS", COLOR AMARILLO, REFLEJANTE CON MICRO ESFERA DE VIDRIO EN PROPORCIÓN SEGÚN MANUAL DE SEÑALIZACIÓN VIAL Y DISPOSITIVOS DE SEGURIDAD SICT (S.C.T). DE 0.40 MTS DE ANCHO Y 3.5 MTS. DE LONGITUD POR EL ANCHO DE LA VIALIDAD, CON UNA SEPARACIÓN DE 0.40 MTS. ENTRE ELLAS, INCLUYE: MATERIALES Y ESPECIFICACIONES QUE CUMPLAN CON LA NORMATIVA N-CMT-5-01-001/13, N-PRY-CAR-10-01-002/13 APLICADAS AL DIA DE HOY, MATERIAL APLICADO EN SU ESTADO DE FUSION A UNA TEMPERATURA MINIMA DE 204 C, LA SUPERFICIE DE CONCRETO O ASFALTO NO DEBE PRESENTAR UNA TEMPERATURA MENOR A LOS 10 C, ;TIEMPO DE SECADO EN RANGOS DE TEMPERATURA DE 10 C DEL SUSTRATO 2 MINUTOS, Y NO MAS DE 10 MINUTOS CUANDO EL SUSTRATO OSCILA ALREDEDOR DE 54C, TRAZO, ENMASCARILLADO, MANO DE OBRA, LIMPIEZA PREVIA Y FINAL DE SUPERFICIE, EQUIPO NECESARIO PARA SU EJECUCIÓN, Y TODO LO NECESARIO PARA SU CORRECTA EJECUCIÓN, TRABAJO TERMINADO.	M2	93	$720.15	$66,973.95
8	SUMINISTRO Y APLICACIÓN DE PINTURA TERMOPLASTICA ALQUIDALICA DE 120 MILESIMAS DE " (in) EN FLECHAS CLASIFICACIÓN M - 11.1, "FLECHA SENCILLA" PARA INDICAR SENTIDO DE CIRCULACIÓN , EN VIALIDADES PARA VELOCIDAD MENOR A 60KM POR HORA DIMENSION NORMATIVA SEGUN MANUAL DE SEÑALIZACIÓN VIAL Y DISPOSITIVOS DE SEGURIDAD SICT (SCT) Y/O (VER PLANO DE SEÑALAMIENTOS), COLOR BLANCO, REFLEJANTE CON MICRO ESFERA DE VIDRIO EN PROPORCIÓN SEGÚN NORMA SCT, INCLUYE: MATERIALES Y ESPECIFICACIONES QUE CUMPLAN CON LA NORMATIVA N-CMT-5-01-001/13, N-PRY-CAR-10-01-002/13 APLICADAS AL DIA DE HOY, MATERIAL APLICADO EN SU ESTADO DE FUSION A UNA TEMPERATURA MINIMA DE 204 C, LA SUPERFICIE DE CONCRETO O ASFALTO NO DEBE PRESENTAR UNA TEMPERATURA MENOR A LOS 10 C, ;TIEMPO DE SECADO EN RANGOS DE TEMPERATURA DE 10 C DEL SUSTRATO 2 MINUTOS, Y NO MAS DE 10 MINUTOS CUANDO EL SUSTRATO OSCILA ALREDEDOR DE 54C, TRAZO, ENMASCARILLADO, MANO DE OBRA, LIMPIEZA PREVIA Y FINAL DE SUPERFICIE, EQUIPO NECESARIO PARA SU EJECUCIÓN, Y TODO LO NECESARIO PARA SU CORRECTA EJECUCIÓN, TRABAJO TERMINADO.	PZA	18	$960.20	$17,283.60

Obra: OBRA COMPLEMENTARIA Y SEÑALIZACIÓN BLVD. LUIS DONALDO COLOSIO

Ubicación: TRAMO: ENTRE BLVD. MIGUEL DE LA MADRID Y CALLE MONTE CORONADO, AGUASCALIENTES Mpio.

Contratista: AVACO ARQUITECTOS, S.A. DE C.V. (59)

No.	Concepto	Unidad	Cantidad	Precio Unitario	Importe Total
	GRUPO: OBRA COMPLEMENTARIA Y SEÑALIZACION				
	PARTIDA: SEÑALIZACION HORIZONTAL				
10	SUMINISTRO Y APLICACIÓN DE PINTURA TERMOPLASTICA ALQUIDALICA DE 120 MILESIMAS DE " (in) EN LETRAS Y NUMEROS CLASIFICACIÓN M - 11.1 "LETRAS Y NUMEROS" EN VIALIDADES PARA VELOCIDAD MENOR A 60KM POR HORA SEGUN MANUAL DE SEÑALIZACIÓN VIAL Y DISPOSITIVOS DE SEGURIDAD SICT (SCT), (VER PLANO DE SEÑALAMIENTOS) EN COLOR BLANCO, REFLEJANTE CON MICRO ESFERA DE VIDRIO EN PROPORCIÓN SEGÚN NORMA SCT DE (VER DETALLES EN PLANOS) INCLUYE: MATERIALES Y ESPECIFICACIONES QUE CUMPLAN CON LA NORMATIVA N-CMT-5-01-001/13, N-PRY-CAR-10-01-002/13 APLICADAS AL DIA DE HOY, MATERIAL APLICADO EN SU ESTADO DE FUSION A UNA TEMPERATURA MINIMA DE 204 C, LA SUPERFICIE DE CONCRETO O ASFALTO NO DEBE PRESENTAR UNA TEMPERATURA MENOR A LOS 10 C, ;TIEMPO DE SECADO EN RANGOS DE TEMPERATURA DE 10 C DEL SUSTRATO 2 MINUTOS, Y NO MAS DE 10 MINUTOS CUANDO EL SUSTRATO OSCILA ALREDEDOR DE 54C, TRAZO, ENMASCARILLADO, MANO DE OBRA, LIMPIEZA PREVIA Y FINAL DE SUPERFICIE, EQUIPO NECESARIO PARA SU EJECUCIÓN, Y TODO LO NECESARIO PARA SU CORRECTA EJECUCIÓN, TRABAJO TERMINADO.	PZA	50	$1,050.23	$52,511.50
11	SUMINISTRO Y COLOCACIÓN DE VIALETA STANDARD (S-200) DE 10X10CM. COLOR: CUERPO AMARILLO Y/O BLANCO Y REFLEJANTE AMARILLO 1 CARA MARCA SEA O SIMILAR EN CALIDAD Y ESPECIFICACIONES DE FICHA TÉCNICA, FIJADO EN PAVIMENTO CON SISTEMA DE SUJECIÓN DE ALTO AGARRE PEGAMENTO EPOXICO 100 A/B (RESINA EPÓXICA/RESINA POLIAMIDA MODIFICADA), RESISTENTE A ALTA TEMPERATURA (VER PLANO DE DETALLES DE SEÑALAMIENTOS HORIZONTAL), INCLUYE: LIMPIEZA PREVIA Y FINAL DE LA SUPERFICIE, PREPARACIÓN DE LA SUPERFICIE, TRAZO, ALINEACIÓN, Y TODO LO NECESARIO PARA SU CORRECTA EJECUCIÓN, TRABAJO TERMINADO.	PZA	75	$103.52	$7,764.00
12	SUMINISTRO Y COLOCACION DE VIALETA SOLAR DE 10X10CM. COLOR: CUERPO ALUMINIO 3 LED DOS CARAS REFLEJANTES MARCA CREATIVAL VT-29 O SIMILAR EN CALIDAD Y ESPECIFICACIONES DE FICHA TÉCNICA, FIJADO EN PAVIMENTO CON SISTEMA DE SUJECIÓN DE ALTO AGARRE PEGAMENTO EPOXICO 100 A/B (RESINA EPÓXICA/RESINA POLIAMIDA MODIFICADA), RESISTENTE A ALTA TEMPERATURA (VER PLANO DE DETALLES DE SEÑALAMIENTOS HORIZONTAL), INCLUYE: LIMPIEZA PREVIA Y FINAL DE LA SUPERFICIE+C92, PREPARACIÓN DE LA SUPERFICIE, TRAZO, ALINEACIÓN, Y TODO LO NECESARIO PARA SU CORRECTA EJECUCIÓN, TRABAJO TERMINADO.	PZA	37	$1,095.25	$40,524.25
13	SUMINISTRO Y COLOCACIÓN DE BOTON DH-3 CERAMICO DE ALTA RESISTENCIA COLOR BLANCO, SEGÚN NORMA SCT. INCLUYE: MATERIAL, MANO DE OBRA, LIMPIEZA DE LA SUPERFICIE, ANCLADO A PAVIMENTO, ELEMENTOS DE SUJECION Y PEGAMENTO, ACARREOS DENTRO DE LA OBRA, LIMPIEZAS Y TODO LO NECESARIO PARA SU CORRECTA EJECUCION.	PZA	1340	$90.02	$120,626.80

Totales por Partida		$472,907.76
Totales por Grupo		$472,907.76
Totales Presup.		$472,907.76
Anticipo	+	$144,502.50
Amortizac. Ant.	-	$144,502.50
SubTotal. Ant.	=	$472,907.76
IVA	+	$75,665.24
Total	=	$548,573.00

H. AYUNTAMIENTO CONSTITUCIONAL DEL MUNICIPIO DE AGUASCALIENTES 2021-2024

PRESUPUESTO MODIFICADO

Aguascalientes

Obra: OBRA COMPLEMENTARIA Y SEÑALIZACIÓN BLVD. LUIS DONALDO COLOSIO

Ubicación: TRAMO: ENTRE BLVD. MIGUEL DE LA MADRID Y CALLE MONTE CORONADO, AGUASCALIENTES Mpio.

Contratista: AVACO ARQUITECTOS, S.A. DE C.V. (59)

Grupo	Partida	Importe
OBRA COMPLEMENTARIA Y SEÑALIZACION		
	SEÑALIZACION HORIZONTAL	$472,907.76
	Subtotal por Grupo	$472,907.76

Totales Presup.		$472,907.76
Anticipo	+	$144,502.50
Amortizac. Ant.	-	$144,502.50
SubTotal. Ant.	=	$472,907.76
IVA	+	$75,665.24
Total	=	$548,573.00

H. AYUNTAMIENTO CONSTITUCIONAL DEL MUNICIPIO DE AGUASCALIENTES 2021-2024

H. AYUNTAMIENTO DE AGUASCALIENTES

SECRETARÍA DE OBRAS PÚBLICAS


DIRECCIÓN DE SUPERVISIÓN DE OBRA


Aguascalientes
LA CIUDAD DE TU VIDA


MEMORIA FOTOGRAFICA


OBRA:	OBRA COMPLEMENTARIA Y SEÑALIZACIÓN BLVD, LUIS LEONALDO COLOSIO,TRAMO ENTRE MIGUEL DE LA MADRID Y CALLE MONTE COLORADO ., AGUASCALIENTES Mpio.					
NO. DE CONTRATO:	FISMDF-0079-2022		CONTRATISTA:	AVACO ARQUITECTOS S.A DE C.V		

INICIO.

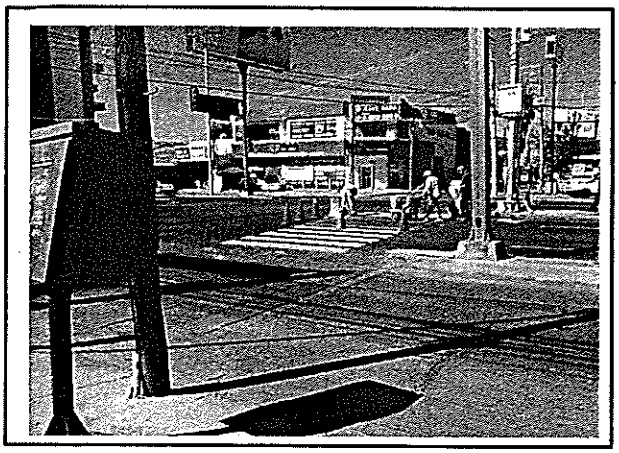

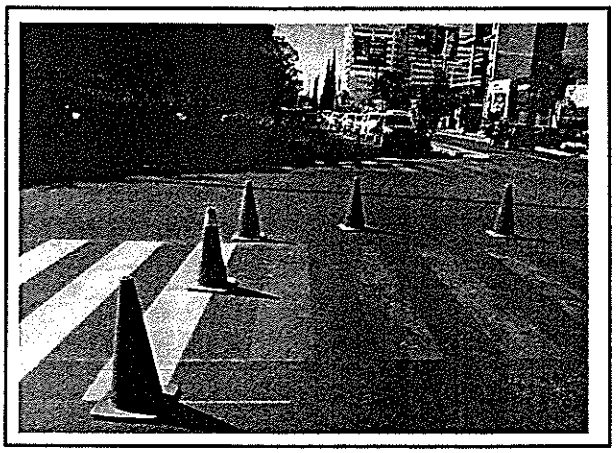

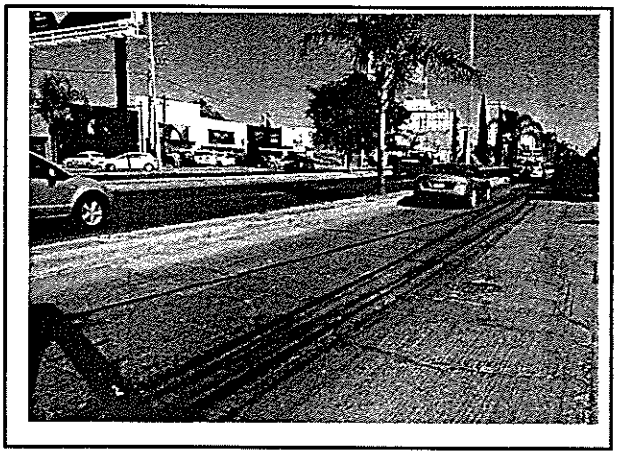

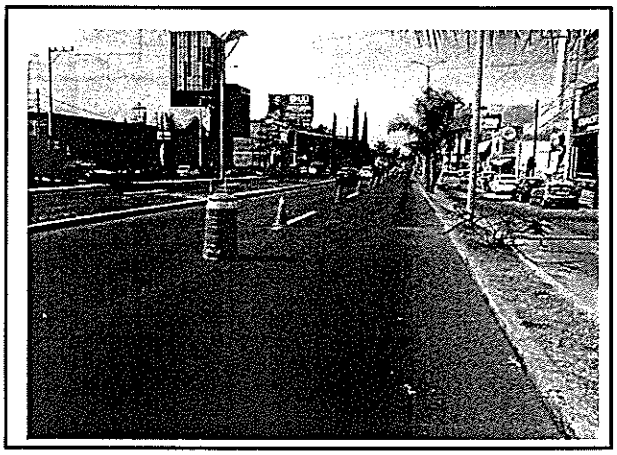

ING.DAVID ALONSO MONTOYA
SUPERVISOR DE OBRA.

H. AYUNTAMIENTO CONSTITUCIONAL DEL MUNICIPIO DE AGUASCALIENTES 2021-2024

H. AYUNTAMIENTO DE AGUASCALIENTES

SECRETARÍA DE OBRAS PÚBLICAS

DIRECCIÓN DE SUPERVISIÓN DE OBRA

Aguascalientes
LA CIUDAD DE TU VIDA


MEMORIA FOTOGRAFICA

OBRA:	OBRA COMPLEMENTARIA Y SEÑALIZACIÓN BLVD, LUIS LEONALDO COLOSIO,TRAMO ENTRE MIGUEL DE LA MADRID Y CALLE MONTE COLORADO ., AGUASCALIENTES Mpio.					
NO. DE CONTRATO:	FISMDF-0079-2022		CONTRATISTA:	AVACO ARQUITECTOS S.A DE C.V		

TERMINO





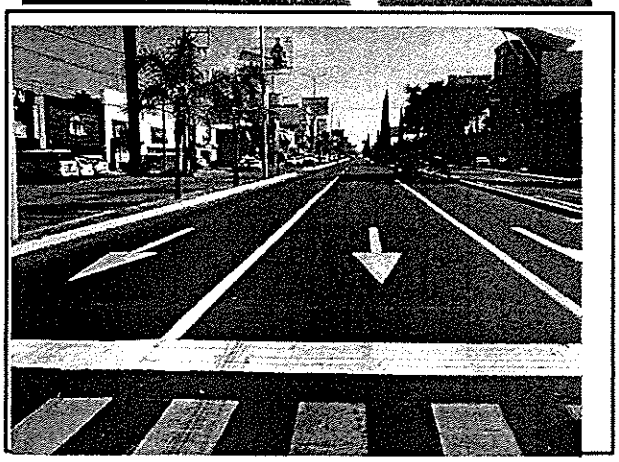



ING.DAVID ALONSO MONTOYA
SUPERVISOR DE OBRA.

H. AYUNTAMIENTO DE AGUASCALIENTES

SECRETARÍA DE OBRAS PÚBLICAS

DIRECCIÓN DE SUPERVISIÓN DE OBRA


H. AYUNTAMIENTO CONSTITUCIONAL DEL MUNICIPIO DE AGUASCALIENTES 2021-2024

Aguascalientes LA CIUDAD DE TU VIDA


MEMORIA FOTOGRAFICA

OBRA:	OBRA COMPLEMENTARIA Y SEÑALIZACIÓN BLVD, LUIS LEONALDO COLOSIO,TRAMO ENTRE MIGUEL DE LA MADRID Y CALLE MONTE COLORADO ., AGUASCALIENTES Mpio.					
NO. DE CONTRATO:	FISMDF-0079-2022		CONTRATISTA:	AVACO ARQUITECTOS S.A DE C.V		

PROCESO

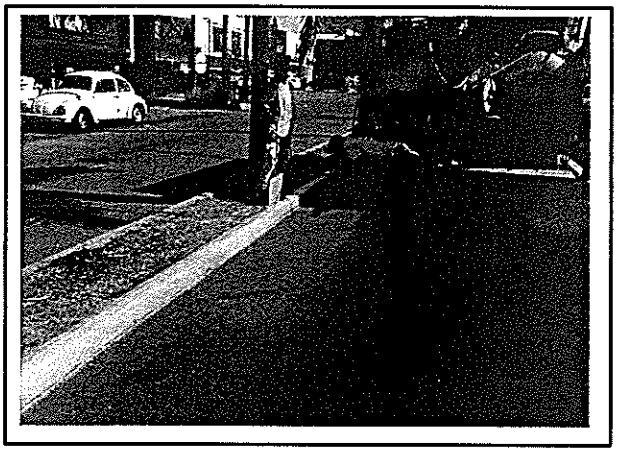



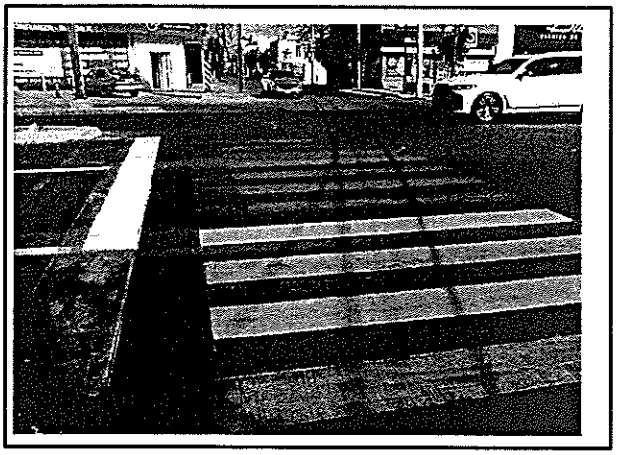



ING.DAVID ALONSO MONTOYA
SUPERVISOR DE OBRA.

MODIFICADO

SECRETARÍA DE OBRAS PÚBLICAS

DIRECCIÓN DE SUPERVISIÓN DE OBRA

EJERCICIO 2022

N° DE CONTRATO: **FISMDF-0079-2022**


NOMBRE DE LA OBRA: **OBRA COMPLEMENTARIA Y SEÑALIZACIÓN BLVD, LUIS DONALDO COLOSIO,TRAMO ENTRE MIGUEL DE LA MADRID Y CALLE MONTE COLORADO ., AGUASCALIENTES Mpio.**

MONTO MODIFICADO FINAL: **$ 548,573.00**

VOLUMEN	UNIDAD	COMPONENTE DE LA OBRA	MONTO
		SEÑALIZACION HORIZONTAL	$ 472,907.76


TOTAL PRESUP.	$	472,907.76
IVA	$	75,665.24
TOTAL	$	548,573.00

NOMBRE DEL SUPERVISOR: ING.DAVID ALONSO MONTOYA

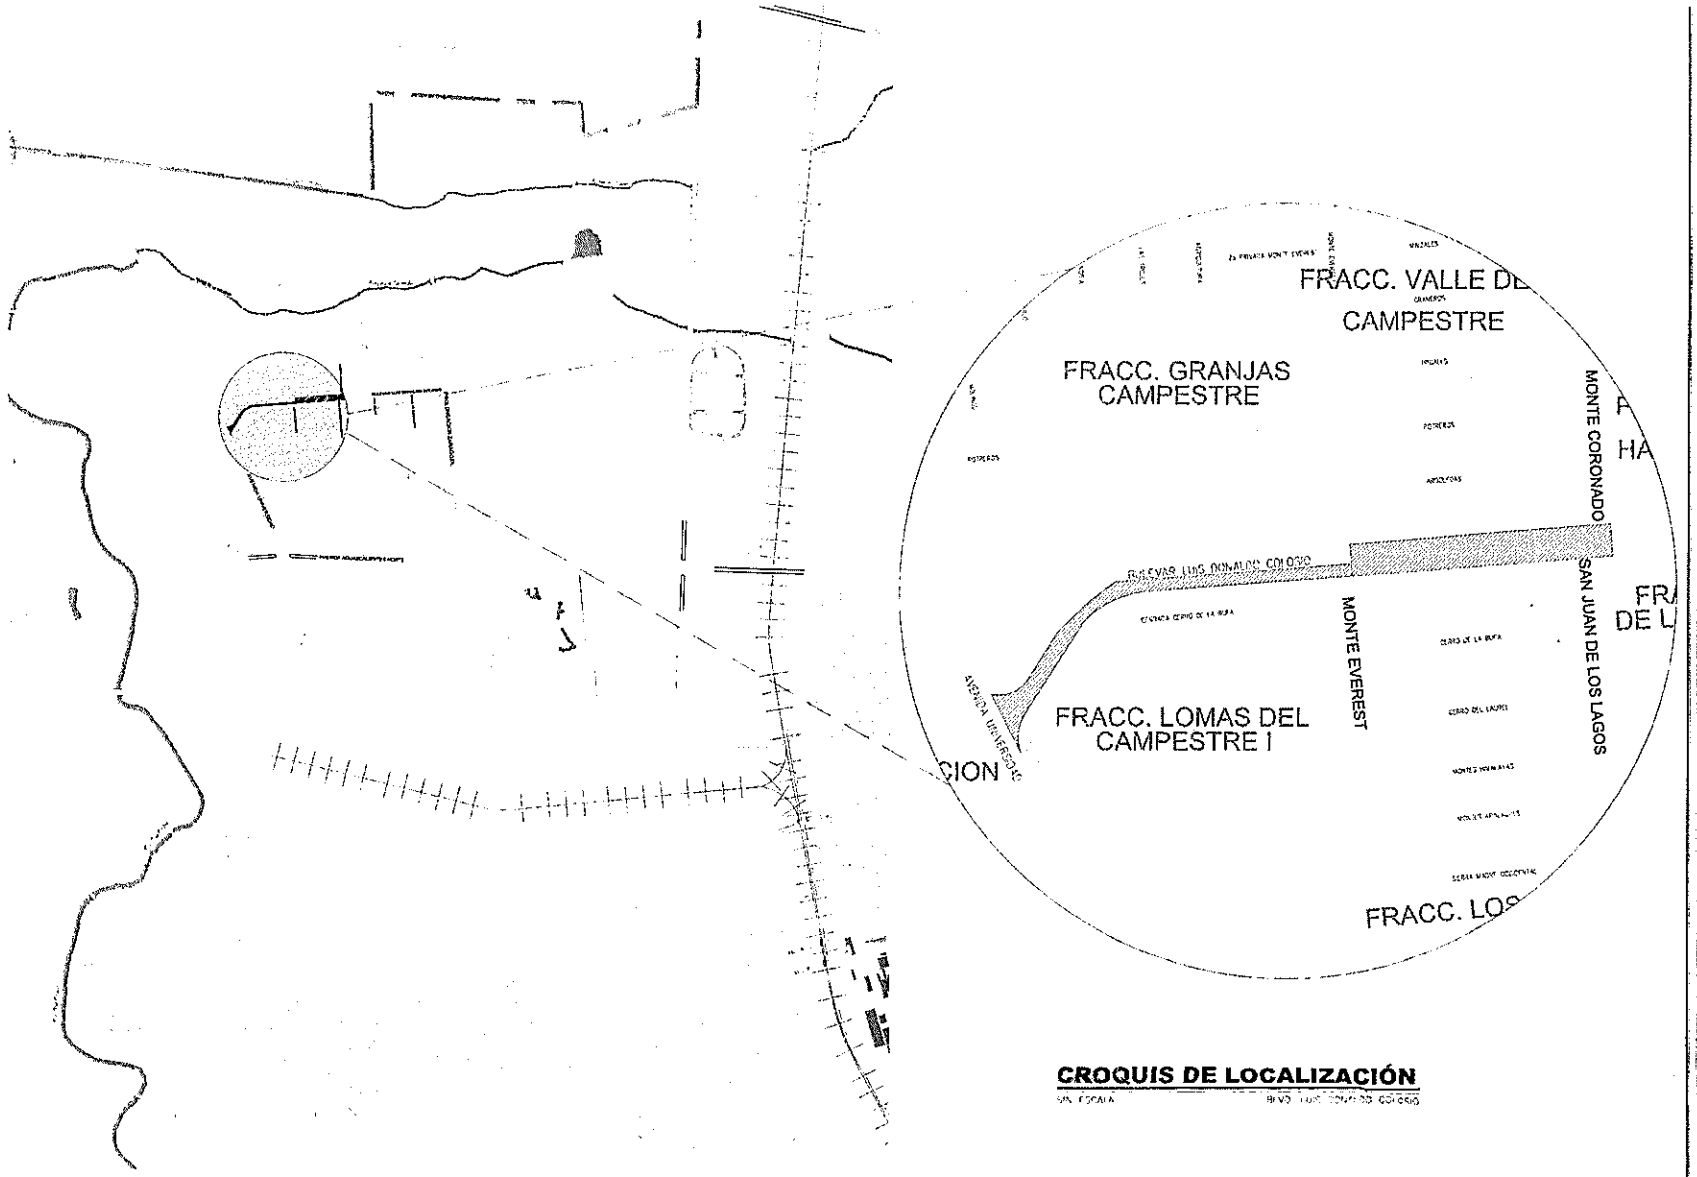

CROQUIS DE LOCALIZACIÓN

SIN ESCALA

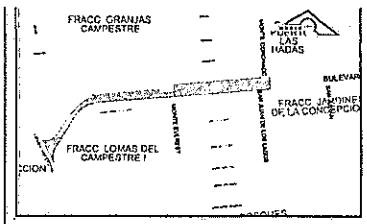

SIMBOLOGÍA

La Dirección de Planeación y Proyectos solo autoriza el proyecto ejecutivo, no es responsable de la correcta ejecución de la obra. Este documento no tiene validez si no presenta las firmas de los responsables para su autorización, así como los sellos respectivos.

PRESIDENTE MUNICIPAL
M.P.P. Leonardo Montañez Castro
ENCARGADA DE DESPACHO DE LA SOPMA
Arq. Gloria Guadalupe Castillo González

Vo. Bo. DE LA DEPENDENCIA

RESP. DE PROY. EXTERNO		LOGO EXTERNO
CED. PROFESIONAL		
PROYECTÓ	REVISÓ	AUTORIZÓ


Dirección de Planeación y Proyectos de Obra — Secretaría de Obras Públicas


PROYECTISTA	COORDINADOR
ING. DIEGO ENRIQUE ROMO AGUILERA	ARQ. ALEJANDRO JAIME LEAL
JEFE DE DEP	DIRECTOR

PROYECTO
OBRA COMPLEMENTARIA Y SEÑALIZACIÓN
BLVD. LUIS DONALDO COLOSIO
UBICACIÓN
BLVD. LUIS DONALDO COLOSIO
ENTRE BLVD. MIGUEL DE LA MADRID HASTA CALLE MONTE CORONADO
CONTENIDO
CROQUIS DE LOCALIZACIÓN

CLAVE	No. PLANO
LOC 01	01
FECHA: ABRIL 2022	ESCALA: INDICADA
ACOTACIÓN:	No. EXP.

Aguascalientes

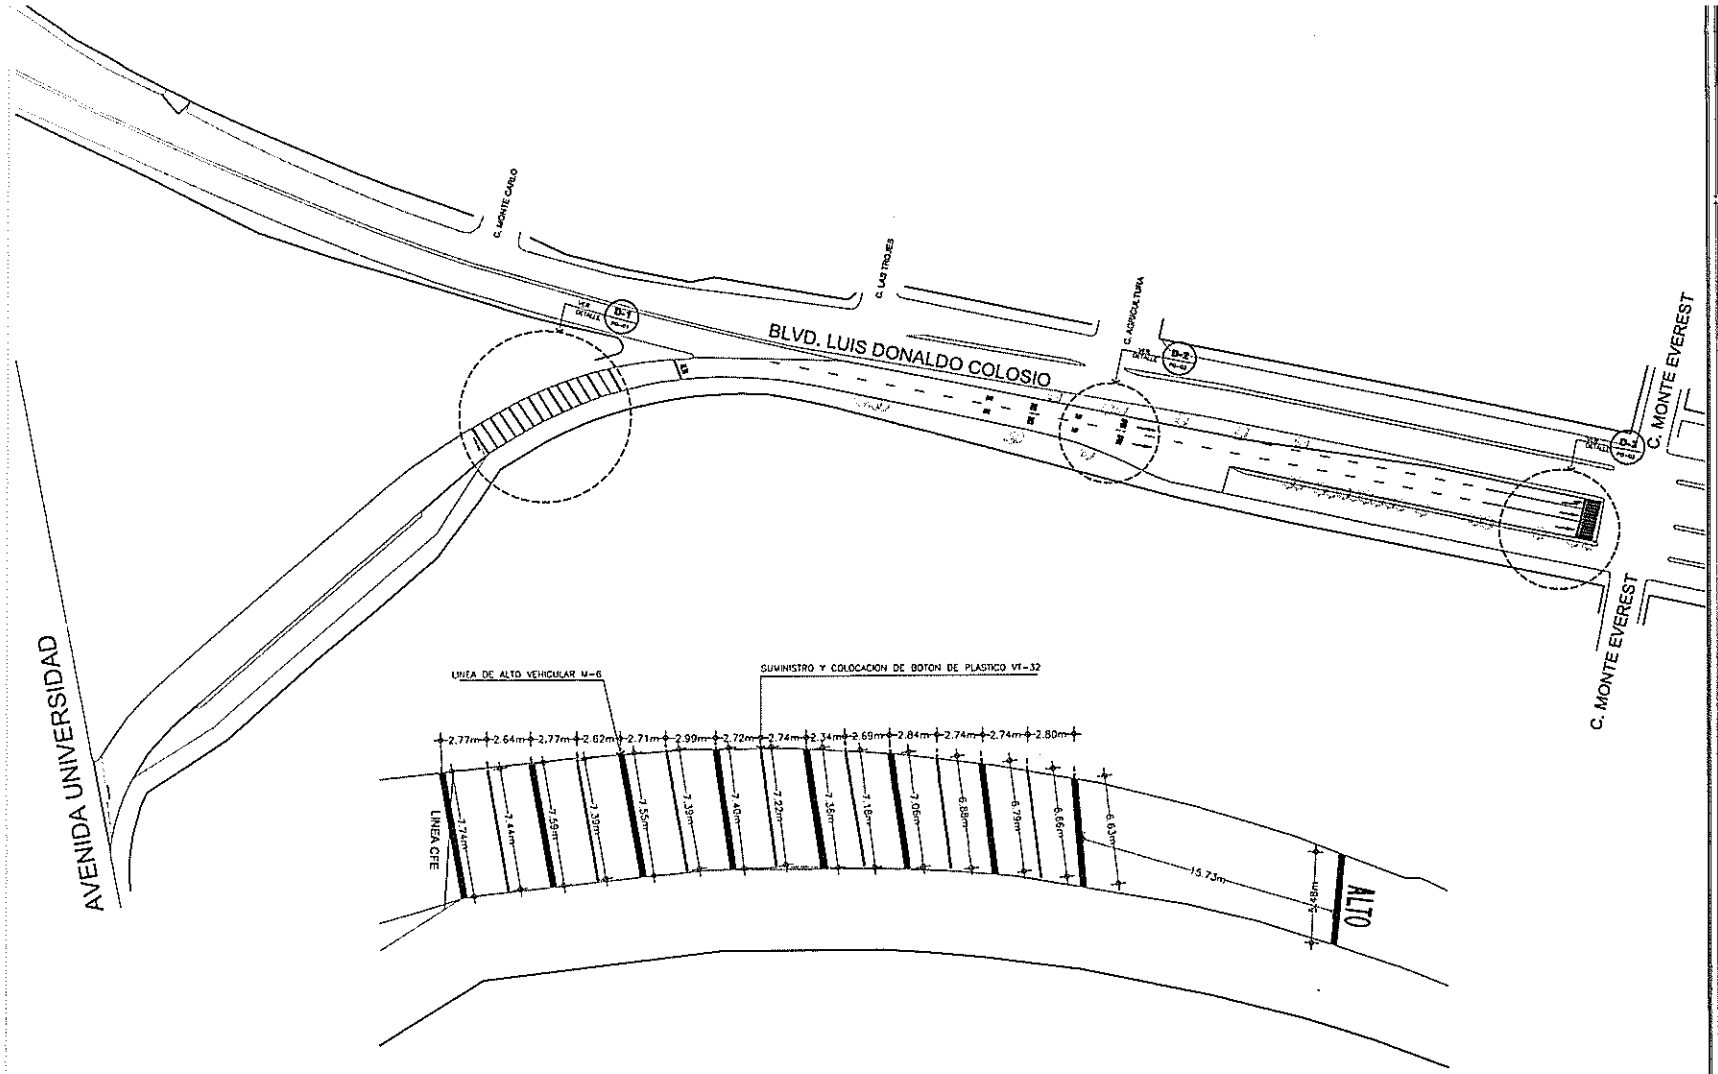

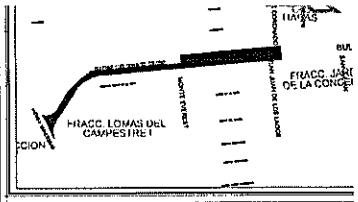

SIMBOLOGÍA

NOTA:

1.- VER DETALLES DE TRAZO ASI COMO SUS DESCRIPCIONES RESPECTIVAS EN LOS PLANOS 6 Y 7

DETALLE TIPO 1

SIN ESCALA — COTAS EN M — PG-01

PLANTA DE SEÑALIZACIÓN

ESCALA 1:450 — BLVD. LUIS DONALDO COLOSIO

La Dirección de Planeación y Proyectos solo autoriza el proyecto ejecutivo, no es responsable de la correcta ejecución de la obra. Este documento no tiene validez si no presenta las firmas de los responsables para su autorización, así como los sellos respectivos.

PRESIDENTE MUNICIPAL
M.P.P. Leonardo Montañez Castro
ENCARGADA DE DESPACHO DE LA SOPMA
Arq. Gloria Guadalupe Castillo González

Vo. Bo. DE LA DEPENDENCIA

RESP. DE PROY. EXTERNO		LOGO EXTERNO
CED. PROFESIONAL		
PROYECTÓ	REVISÓ	AUTORIZÓ


Dirección de Planeación y Proyectos de Obra — Secretaría de Obras Públicas

PROYECTISTA	COORDINADOR
ING. DIEGO ENRIQUE ROMO AGUILERA	ARQ. ALEJANDRO JAIME LEAL
JEFE DE DEP.	DIRECTOR

PROYECTO: OBRA COMPLEMENTARIA Y SEÑALIZACIÓN BLVD. LUIS DONALDO COLOSIO
UBICACIÓN: BLVD. LUIS DONALDO COLOSIO ENTRE BLVD. MIGUEL DE LA MADRID HASTA CALLE MONTE EVEREST
CONTENIDO: PLANTA DE SEÑALIZACIÓN TRAMO "A"

CLAVE	No. PLANO
SEÑ 01	03
FECHA: ABRIL 2022	ESCALA: INDICADA
ACOTACIÓN	No. EXP.

Aguascalientes

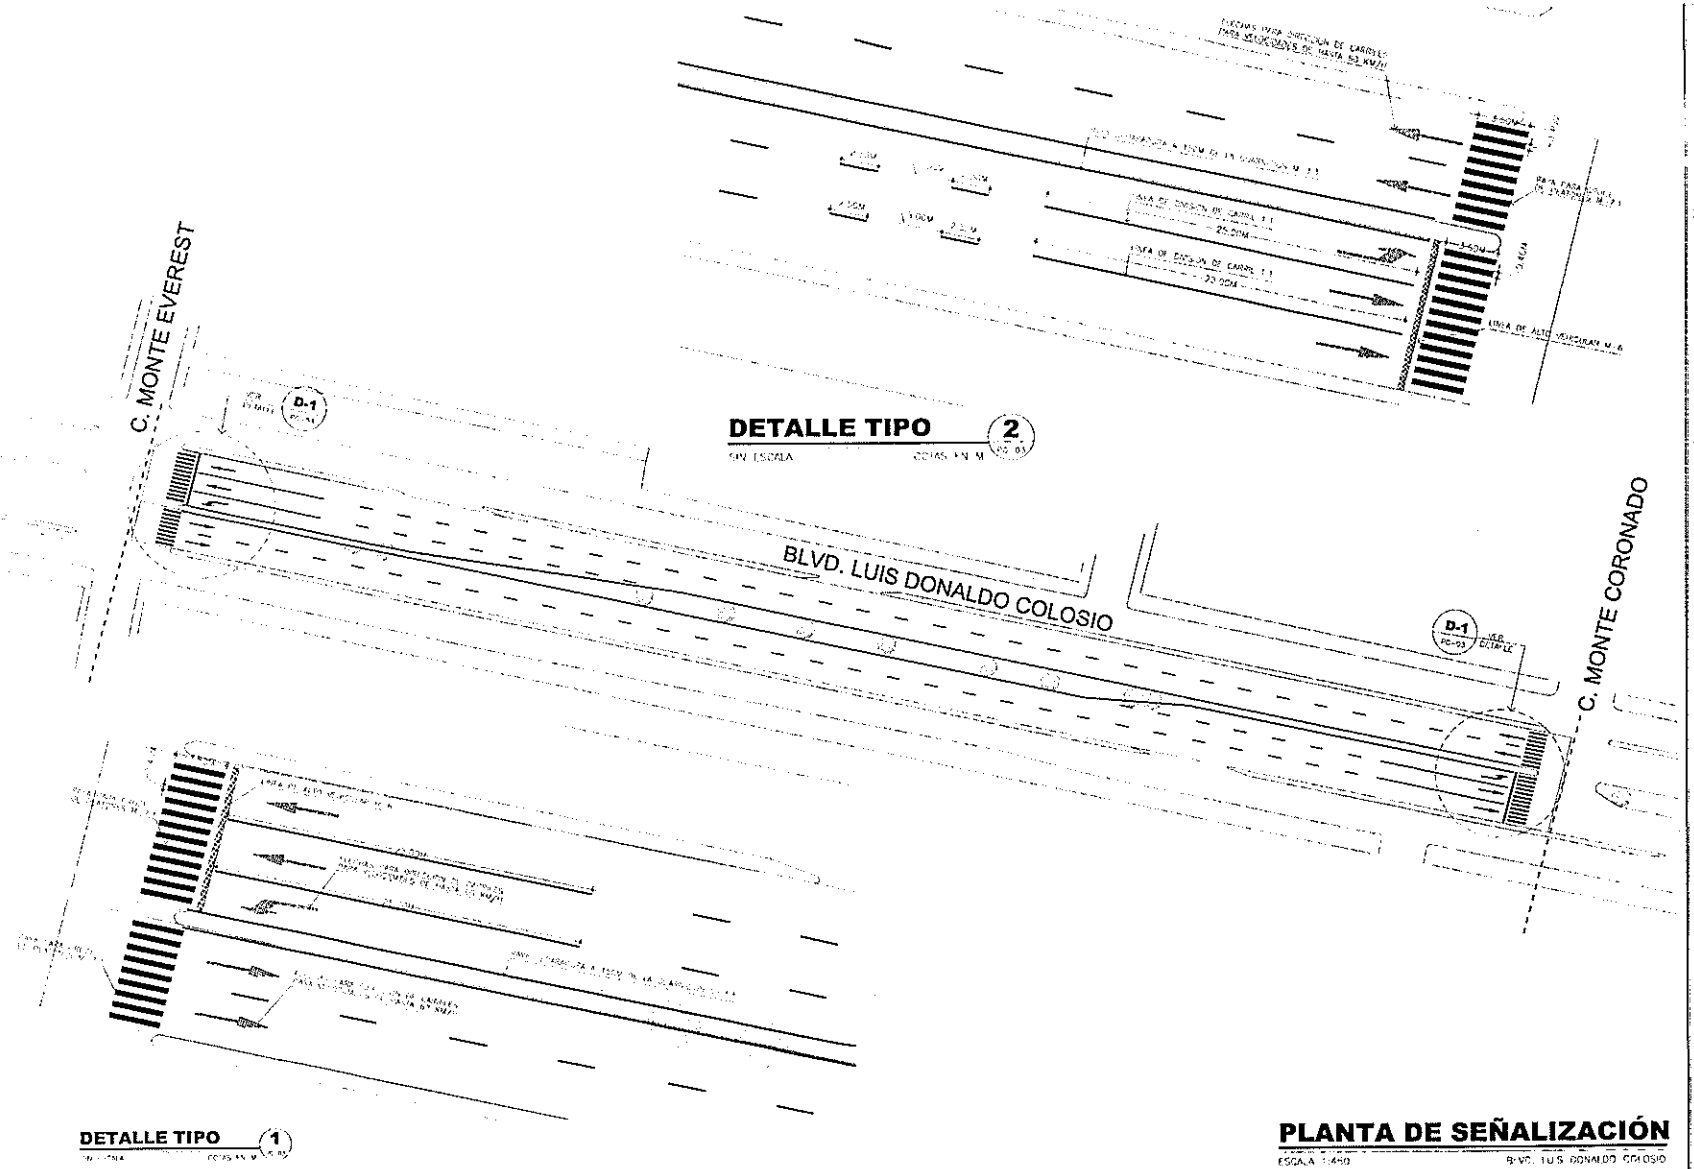

DETALLE TIPO 2


SIN ESCALA COTAS EN M

DETALLE TIPO 1

SIN ESCALA COTAS EN M

PLANTA DE SEÑALIZACIÓN

ESCALA 1:450 BLVD. LUIS DONALDO COLOSIO

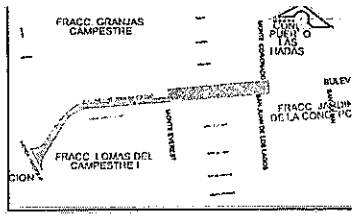

SIMBOLOGÍA

NOTA:

1.- VER DETALLES DE TRAZO ASI COMO SUS DESCRIPCIONES RESPECTIVAS EN LOS PLANOS 6 Y 7

La Dirección de Planeación y Proyectos solo autoriza el proyecto ejecutivo, no es responsable de la correcta ejecución de la obra. Este documento no tiene validez si no presenta las firmas de los responsables para su autorización, así como los sellos respectivos.

PRESIDENTE MUNICIPAL
M.P.P. Leonardo Montañez Castro
ENCARGADA DE DESPACHO DE LA SOPMA
Arq. Gloria Guadalupe Castillo González

V° B° DE LA DEPENDENCIA


RESP. DE PROY. EXTERNO | LOGO EXTERNO
CED. PROFESIONAL
PROYECTÓ | REVISÓ | AUTORIZÓ

Dirección de Planeación y Proyectos de Obra | Secretaría de Obras Públicas
PROYECTISTA | COORDINADOR
ING. DIEGO ENRIQUE ROMO AGUILERA | ARQ. ALEJANDRO JAIME LEAL
JEFE DE DEP | DIRECTOR

PROYECTO
OBRA COMPLEMENTARIA Y SEÑALIZACIÓN BLVD. LUIS DONALDO COLOSIO
UBICACIÓN
BLVD. LUIS DONALDO COLOSIO
TRAMO DE CALLE MONTE EVEREST A CALLE MONTE CORONADO
CONTENIDO
PLANTA DE SEÑALIZACIÓN TRAMO "B"


CLAVE SEÑ 03 | No. PLANO 05
FECHA ABRIL 2022 | ESCALA 06
ACOTACIÓN | No. EXP

Aguascalientes

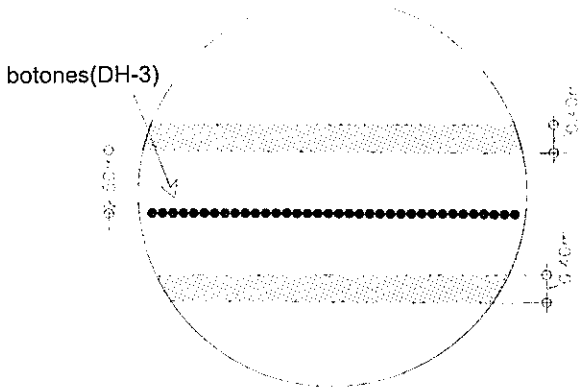

DETALLE DE REDUCTORES DE VELOCIDAD

SUMINISTRO Y COLOCACION DE BOTON PLASTICO (V-32) COLOR BLANCO DE 10 CM DE DIAMETRO Y 2 CM DE ALTURA, INCLUYE: MANO DE OBRA, EQUIPO Y HERRAMIENTA NECESARIA, CUMPLIR CON LA CALIDAD Y ESPECIFICACIONES DE LA OBRA, TRABAJO TERMINADO CON BASE EN CATALOGO CONCEPTOS, INCLUYE: SUMINISTRO Y APLICACION DE BASE EPOXICA 100 A/B (RESINA EPOXICA/RESINA POLIAMIDA MODIFICADA), RESISTENTE A ALTA TEMPERATURA (VER PLANO DE DETALLES DE SEÑALAMIENTOS HORIZONTAL), INCLUYE: LIMPIEZA PREVIA Y FINAL DE LA SUPERFICIE CON, PREPARACIÓN DE LA SUPERFICIE, TRAZO, ALINEACION, Y TODO LO NECESARIO PARA SU CORRECTA EJECUCIÓN, TRABAJO TERMINADO.

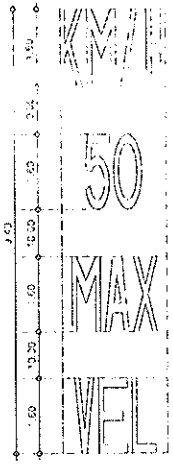


SEÑALAMIENTO VELOCIDAD MÁXIMA

ESCALA 1:50 COTAS EN m




DETALLE DE TRAZO DE TEXTO PARA SEÑALIZACIÓN HORIZONTAL

ESCALA 1:20 COTAS EN m

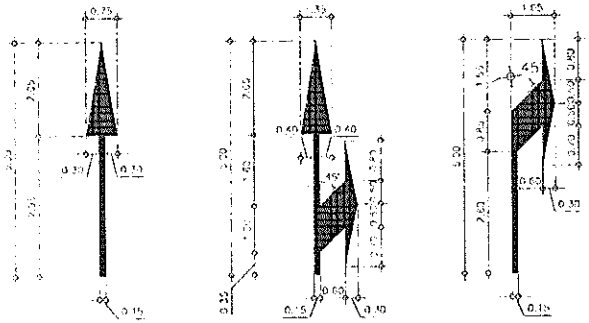

DETALLE DE FLECHAS EN PAVIMENTO PARA VELOCIDADES HASTA DE 60KM/H

ESCALA 1:20 COTAS EN m

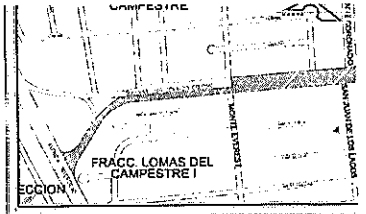

SIMBOLOGIA

Notas para planos de señalización:

Nota 1: Se aplicará en todos los señalamientos horizontales pintura para trafico termoplastica alquidalica de 120 milesimas cualquier color, reflejante con micro esferas segur norma de la SCT marca comex o similar en precio y calidad secado al tacto de 5min y al duro en 30min que cumpla con las especificaciones n-cmt-5-01-001/05, n-pry-car-10-01-002/13 de la SCT aplicadas al día de hoy.

Nota 2: Dosificación de micro esfera La cantidad de esferas de vidrio en la película de pintura en húmedo, según su tipo, será la que se indica en la Tabla

Nota 3: Se aplicara en guamiciones pintura para trafico base solvente tipo alquidal de secado rapido, que cumpla con las especificaciones n-cmt-5-01-001/005, n-py-car-10-01-002/13 de la SCT, aplicadas al dia de hoy La cantidad de esferas de vidrio en la película de pintura en húmedo, según su tipo, será la que se indica en la Tabla

TABLA 8. Cantidad de esferas de vidrio en la película de pintura en humedo.

Tipo de pintura	Espesor de la película de pintura en húmedo mm	cantidad de esferas kg/m2 Integradas	Sembradas, mínimo	Tipo de granulometría
Base solvente	0,38 a 0,50	----	0,330	I
Base agua	0,38 a 0,50	----	0,330	I o II
Termoplástica	1,50 a 3,00	0,57 a 0,69	0,330	II

La Dirección de Planeación y Proyectos solo autoriza el proyecto ejecutivo, no es responsable de la correcta ejecución de la obra. Este documento no tiene validez si no presenta las firmas de los responsables para su autorización, así como los sellos respectivos.

PRESIDENTE MUNICIPAL
M.P.P. Leonardo Montañez Castro
ENCARGADA DE DESPACHO DE LA SOPMA
Arq. Gloria Guadalupe

Vo. Bo. DE LA DEPENDENCIA

RESP. DE PROY. EXTERNO	LOGO EXTERNO
CED. PROFESIONAL	
PROYECTÓ REVISÓ	AUTORIZÓ

Dirección de Planeación y Proyectos de Obra — Secretaría de Obras Públicas

PROYECTISTA	COORDINADOR
ING. DIEGO ENRIQUE ROMO AGUILERA	ARQ. ALEJANDRO JAIME LEAL
JEFE DE DEP.	DIRECTOR

PROYECTO
OBRA COMPLEMENTARIA Y SEÑALIZACIÓN BLVD. LUIS DONALDO COLOSIO
UBICACIÓN
BLVD. LUIS DONALDO COLOSIO
ENTRE BLVD. MIGUEL DE LA MADRID HASTA CALLE MONTE CORONADO
CONTENIDO
DETALLES DE TRAZO SEÑALIZACIÓN HORIZONTAL

CLAVE	No. PLANO
SEÑ 05	07
FECHA JUNIO 2022	ESCALA INDICADA
ACOTACIÓN	No. EXP.

Aguascalientes