Aguascalientes
LA CIUDAD DE TU VIDA

Dirección de Programación Presupuestal
Núm. Oficio AMPP/0537/22
Aguascalientes, Ags. 29 de Noviembre del 2022
Asunto: Validación de Expediente Técnico

C.P. SERGIO ARTURO LOZANO GONZÁLEZ
SECRETARIO DE FINANZAS MUNICIPALES
P R E S E N T E

Con fundamento en los artículos 17 fracción XV, 60 fracción XVI y 76 fracción VI del Reglamento del Sistema Integral de Desarrollo Municipal y del Instituto Municipal de Planeación y Evaluación de Aguascalientes, hago referencia al oficio SOPMA/2578/2022 recibido por este Instituto el día 25 de Noviembre del 2022 por parte de la Secretaría de Obras Públicas Municipales, mediante el cual remiten el expediente técnico original de la siguiente obra para su análisis, registro y priorización, conforme al Programa Anual de Obra Pública y Programas Sociales para el ejercicio presupuestal 2022:

DEPENDENCIA EJECUTORA:	SOPMA
NOMBRE DE LA OBRA O PROYECTO:	OBRA COMPLEMENTARIA Y SEÑALIZACIÓN
UBICACIÓN:	BLVD. ADOLFO RUÍZ CORTINES, ENTRE SALIDA PUENTE PIRULES Y AV ABELARDO LÓPEZ RODRÍGUEZ, LA SOLEDAD, AGUASCALIENTES, AGS.
FONDO DE INVERSIÓN:	FONDO DE INFRAESTRUCTURA SOCIAL MUNICIPAL Y DE LAS DEMARCACIONES TERRITORIALES DEL DISTRITO FEDERAL
IMPORTE:	$1,398,331.09 (ET FINAL)
No. DE OBRA:	2022-FISMDF-0098-04-1101
MODALIDAD DE EJECUCIÓN:	CONTRATO
EJE:	MUNICIPIO SOBRESALIENTE
ESTRATEGIA:	OBRA PÚBLICA INTELIGENTE
POLITICA:	5.8.1.REHABILITACIÓN Y MANTENIMIENTO VIALIDADES, CAMINOS, CALLES, ÁREAS DE TERRACERÍA Y CAUCES (COM.

Al respecto, hago de su conocimiento que dicho expediente ha sido analizado en su integración técnica y documental, con base en el artículo 168 fracción I del Reglamento de la Ley de Obras Públicas y Servicios Relacionados para el Estado de Aguascalientes y sus Municipios.

Asimismo, le comento que este Instituto valida dicha obra acorde a lo establecido en los artículos 14, 22 párrafo segundo y 23 de la Ley de Obras Públicas y Servicios Relacionados para el Estado de Aguascalientes y sus Municipios, la cual se encuentra alineada al Plan de Desarrollo Municipal vigente, para dar cumplimiento a las metas establecidas en el mismo, y a los Lineamientos Generales para la Operación de este Fondo de Inversión, toda vez que la misma cuente con la autorización del CODEMUN. De igual manera, se hace de su conocimiento que deberá cumplir con lo establecido en los ordenamientos aplicables en lo que respecta al ejercicio, control e información de los recursos de este Fondo. Cabe hacer mención que los recursos solicitados para este proyecto de inversión, estarán sujetos a la disponibilidad presupuestal para el presente ejercicio fiscal que determine la Secretaría a su digno cargo. Sin otro particular por el momento, le envío un cordial saludo.

A T E N T A M E N T E

ARQ. AUSTRIA GABRIELA DAVILA DE LA LLAVE
DIRECTORA GENERAL DEL IMPLAN

CAAR / JDBC
C.c.p. I.C. ING. MIGUEL ÁNGEL HUIZAR BOTELLO .- Secretaría de Obras Públicas Municipales .Para su conocimiento.
C.c.p. Archivo.

Instituto Municipal de Planeación y Evaluación de Aguascalientes
Antonio Acevedo Escobedo 103 A. Col. Centro
Aguascalientes. Ags. C.P. 20000
(449) 9101010 Ext. 3117
www.implanags.gob.mx

GOBIERNO MUNICIPAL DE AGUASCALIENTES

INSTITUTO MUNICIPAL DE PLANEACION

IMPLAN

ANÁLISIS INTEGRAL DE EXPEDIENTE TÉCNICO

No. DE OBRA (PAOP 2020):	2022-FISMDF-0098-04-1101	REGISTRO No.	261
OFICIO DE VALIDACIÓN:	AMPP/0537/22	FECHA RECIBIDO PARA REVISIÓN:	29 de Noviembre del 2022
PROGRAMA:	URBANIZACION MUNICIPAL	LOCALIDAD O COLONIA:	LA SOLEDAD
SUB-PROGRAMA:	0411- Calles y Caminos	DELEGACIÓN:	San Marcos
DEPENDENCIA:	Secretaría de Obras Públicas Municipales	MOD. DE EJECUCIÓN:	CONTRATO
NOMBRE DE LA OBRA:	OBRA COMPLEMENTARIA Y SEÑALIZACIÓN, BLVD. ADOLFO RUÍZ CORTINES, ENTRE SALIDA PUENTE PIRULES Y AV ABELARDO LÓPEZ RODRÍGUEZ		
FUENTE DE FINANCIAMIENTO:	FONDO DE INFRAESTRUCTURA SOCIAL MUNICIPAL Y DE LAS DEMARCACIONES TERRITORIALES DEL DISTRITO FEDERAL, FISMDF		
INVERSIÓN:	$1,398,331.09	CLASIFICACIÓN DE OBRA:	BIENES DE DOMINIO PUBLICA

TOTAL	FEDERAL	ESTATAL	MUNICIPAL	BENEFICIARIOS	OTROS	DIFERENCIA ENTRE MOD.
$1,398,331.09	$1,398,331.09	0.00	0.00	0.00	0.00	*$0,00*

TIPO DE EXPENDIENTE:	ET FINAL	AÑO: 2022	AÑO:	AÑO:		
AVANCES:	Financiero: 100 %		Físico: 100 %			
FECHA DE INICIO:	23 de Septiembre del 2022	FECHA DE TÉRMINO:	22 de Octubre del 2022	REGISTRO SIMA:	98	

CHEK LIST DE LOS ANEXOS DEL EXPEDIENTE TÉCNICO

CÉDULA DE REGISTRO DE OBRA	✓
DICTAMEN DE FACTIBILIDAD	✓
MEMORIA DESCRIPTIVA	✓
PRESUPUESTO BASE	✓
FACTIBILIDAD VERIFICADA EN CAMPO	✓
CROQUIS DE UBICACIÓN (MACRO)	✓
CROQUIS DE UBICACIÓN (MACRO)	✓
PROGRAMA DE OBRA Y MONTOS MENSUALES	✓
PLANOS O ESTUDIOS TÉCNICOS	✓
PADRÓN DE BENEFICIARIOS	N/A
ACTA DE ACEPTACIÓN DEL PROYECTO	N/A
DICTAMEN DE IMPACTO AMBIENTAL	N/A
CONVENIO DE CONCERTACIÓN	N/A
ACTA CONSTITUTIVA	N/A

METAS		BENEFICIARIOS		PERIODO DE EJECUCION		OBRA PROPUESTA		CLAVE SISCO
UNIDAD DE MEDIDA	CANT	TIPO DE BENEFICIARIOS	CANTIDAD	FECHA DE INICIO	FECHA DE TERMINO	CONCEPTO	JORNALES A GENERAR	
OBRA	1	Personas	400	2022-09-23	2022-10-22	Señalética	3635	2367

INCLUIDO EN PLAN DE DESARROLLO MUNICIPAL Y EL PROGRAMA ANUAL DE OBRA PÚBLICA

OBSERVACIONES:

SIN OBSERVACIONES

RECIBIO: ING. JOSÉ DAVID BURGUETE CLAUSTRO
Analista de Programación e Inversión de Obra Pública

29 de Noviembre del 2022
Fecha de validación

29 de Noviembre del 2022
Fecha de validación Expediente

PROCEDE Si ✓ No

H. AYUNTAMIENTO CONSTITUCIONAL DEL MUNICIPIO DE AGUASCALIENTES 2021-2024

AYUNTAMIENTO DE AGUASCALIENTES

CEDULA DE REGISTRO POR OBRA

Aguascalientes

050400-001E00E05-05-2-2-1-00-1-E-0510-0-17-0098-21-2502-6144

2022-FISMDF-0098-0411109-052	Obra **OBRA COMPLEMENTARIA Y SEÑALIZACIÓN BLVD. ADOLFO RUÍZ CORTINES**
Tipo DEFINITIVO 2 2022 Folio SISCO **2367**	Ubic. TRAMO: ENTRE SALIDA PUENTE PIRULES Y AV. ABELARDO L. RODRÍGUEZ, LA SOLEDAD Fracc. , Deleg. Pocitos

Ent. Ejecutora : **050400001E00E05**

Eje: **05**	MUNICIPIO SOBRESALIENTE
Finalidad: **2**	DESARROLLO SOCIAL
Función: **2**	VIVIENDA Y SERVICIOS A LA COMUNIDAD
Subfunción: **1**	URBANIZACIÓN
Tema: **00**	SIN TEMA
Cuenta del Gasto **1**	GASTO PROGRAMABLE
Clasif. Programatica: **E**	PRESTACIÓN DE SERVICIOS PÚBLICOS
Programa: **0510**	Movilidad Urbana
SubPrograma: **0**	SUBPROGRAMA GENÉRICO
Proyecto: **17**	
Tipo de Gasto: **21**	GASTO INVERSIÓN / OBRA PÚBLICA

I N V E R S I O N 2022

Municipal	2502	FONDO PARA LA INFRAESTRUCTURA SOCIAL MUNICIPAL Y DE LAS DEMARCACIONES TERRITORIALES DEL DISTRITO FEDERAL 2022	$1,398,331.09

Folio SIMA 98 Total $1,398,331.09

M E T A S

Unidad de Medida	Cantidad	Descripción
OBRA	1	OBRA OBRA COMPLEMENTARIA Y SEÑALIZACIÓN BLVD ADOLFO RUÍZ CORTINES

Inversión Ejercida Total al 31 de Diciembre de 2021 $0.00

Avance Fisico Acumulado al 31 de Diciembre de 2021

Avance Fisico Acumulado Programado al 31 de Diciembre de 2022 100 %

Fecha de Inicio 23 Sep 2022 Fecha de Terminación 22 Oct 2022

Jornales a Generar en 2022 3635

Modalidad de ejecución CONTRATO

Clasificación de la Obra Bienes de Dominio Público

Registro del Patrimonio: Obras del dominio público

OBRAS PÚBLICAS

Av. Aguascalientes Sur No. 2615
Fracc. Jardines de las Fuentes,
Aguascalientes, Ags. C.P. 20278

(449) 9 78 92 01, 06, 09

www.ags.gob.mx

GENERALES

Nombre del Proyecto : OBRA COMPLEMENTARIA Y SEÑALIZACIÓN BLVD. ADOLFO RUÍZ CORTINES

TRAMO: ENTRE SALIDA PUENTE PIRULES Y AV. ABELARDO L. RODRÍGUEZ, LA SOLEDAD Fracc. , Deleg. Pocitos

Programa : 04 URBANIZACION MUNICIPAL

Subprograma : 11 Calles y caminos (428.- Rehabilitación: 0411208- Señalización)

Clave del Municipio : AGUASCALIENTES

Localidad :

Barrio, Colonia o Ejido : LA SOLEDAD Fracc.

Tipo de Obra : NUEVA

DESCRIPCIÓN DEL PROYECTO:

OBRA COMPLEMENTARIA Y SEÑALIZACIÓN BLVD. ADOLFO RUÍZ CORTINES 1.00 OBRA

Beneficiarios (No. y Tipo) :

400	PERSONAS

Hombres: 190 Mujeres: 210

OBRAS PÚBLICAS

Av. Aguascalientes Sur No. 2615
Fracc. Jardines de las Fuentes,
Aguascalientes, Ags. C.P. 20278

(449) 9 78 92 01, 06, 09

www.ags.gob.mx

Los abajo firmantes, hacen constar que el presente proyecto :

OBRA COMPLEMENTARIA Y SEÑALIZACIÓN BLVD. ADOLFO RUÍZ CORTINES

TRAMO: ENTRE SALIDA PUENTE PIRULES Y AV. ABELARDO L. RODRÍGUEZ, LA SOLEDAD Fracc. , Deleg. Pocitos

cumple con los Requisitos y Normas Técnicas establecidas por la Dependencia Normativa, por lo que es viable su ejecución. Comprometiéndose la misma a proporcionar la supervisión y asistencia técnica necesaria durante el proceso administrativo.

Por la Dependencia Ejecutora

Ing. Miguel Angel Huizar Botello
Secretario de Obras Públicas

Lic. Jaime Gallo Camacho
Secretario de Desarrollo Urbano

LUGAR :AGUASCALIENTES, AGS.

Av. Aguascalientes Sur No. 2615
Fracc. Jardines de las Fuentes,
Aguascalientes, Ags. C.P. 20278

(449) 9 78 92 01, 06, 09

www.ags.gob.mx

H. AYUNTAMIENTO CONSTITUCIONAL DEL MUNICIPIO DE AGUASCALIENTES 2021-2024

AYUNTAMIENTO DE AGUASCALIENTES

FACTIBILIDAD VERIFICADA EN CAMPO

Aguascalientes
LA CIUDAD DE TU VIDA

MUNICIPIO: AGUASCALIENTES

LOCALIZACION: TRAMO: ENTRE SALIDA PUENTE PIRULES Y AV. ABELARDO L. RODRÍGUEZ, LA SOLEDAD Fracc. , Deleg. Pocitos

PROGRAMA: URBANIZACION MUNICIPAL

SUBPROGRAMA: Calles y caminos (428.- Rehabilitación: 0411208- Señalización)

OBRA A REALIZAR: OBRA COMPLEMENTARIA Y SEÑALIZACIÓN BLVD. ADOLFO RUÍZ CORTINES

DEPENDENCIA EJECUTORA: SECRETARÍA DE OBRAS PUBLICAS DEL MUNICIPIO DE AGUASCALIENTES

FORMA DE EJECUCION: CONTRATO

TIPO DE OBRA PROPUESTA: NUEVA

CONDICIONES ACTUALES DE LA OBRA:

OBRA COMPLEMENTARIA Y SEÑALIZACIÓN BLVD. ADOLFO RUÍZ CORTINES

CARACTERISTICAS DE LA OBRA: Bueno

FACTIBILIDAD DE LA OBRA:

ESTA OBRA SE REQUIERE PARA EL BENEFICIO DE LA CIUDADANÍA

PROCEDE: SI [X] NO [ ]

REVISÓ: Jefa del Departamento de Expedientes Tecnicos y Costos

NOMBRE: Arq. Blanca Margarita Martinez Amador

FIRMA: _____

FECHA: 04 Nov 2022

SECRETARIA DE OBRAS PÚBLICAS

Av. Aguascalientes Sur No. 2615
Fracc. Jardines de las Fuentes,
Aguascalientes, Ags. C.P. 20278

(449) 9 78 92 01, 06, 09

www.ags.gob.mx

No. Folio SISCO 2367

H. AYUNTAMIENTO CONSTITUCIONAL DEL MUNICIPIO DE AGUASCALIENTES 2021 2024

Aguascalientes
LA CIUDAD DE TU VIDA

MACRO LOCALIZACIÓN

APROBACIÓN	**2022-FISMDF-0098-0411109-052**
NOMBRE DE LA OBRA:	**OBRA COMPLEMENTARIA Y SEÑALIZACIÓN BLVD. ADOLFO RUÍZ CORTINES**
UBICACIÓN:	**TRAMO: ENTRE SALIDA PUENTE PIRULES Y AV. ABELARDO L. RODRÍGUEZ, LA SOLEDAD Fracc.**
PROGRAMA:	**04 - URBANIZACION MUNICIPAL**




I.C. LAURA CECILIA MARTÍNEZ ALBA
RESIDENTE DE SUPERVISIÓN

H. AYUNTAMIENTO CONSTITUCIONAL DEL MUNICIPIO DE AGUASCALIENTES 2021 2024

Aguascalientes
LA CIUDAD DE TU VIDA

MICRO LOCALIZACIÓN

APROBACIÓN	**2022-FISMDF-0098-0411109-052**
NOMBRE DE LA OBRA:	**OBRA COMPLEMENTARIA Y SEÑALIZACIÓN BLVD. ADOLFO RUÍZ CORTINES**
UBICACIÓN:	**TRAMO: ENTRE SALIDA PUENTE PIRULES Y AV. ABELARDO L. RODRÍGUEZ, LA SOLEDAD Fracc.**
PROGRAMA:	**04 - URBANIZACION MUNICIPAL**

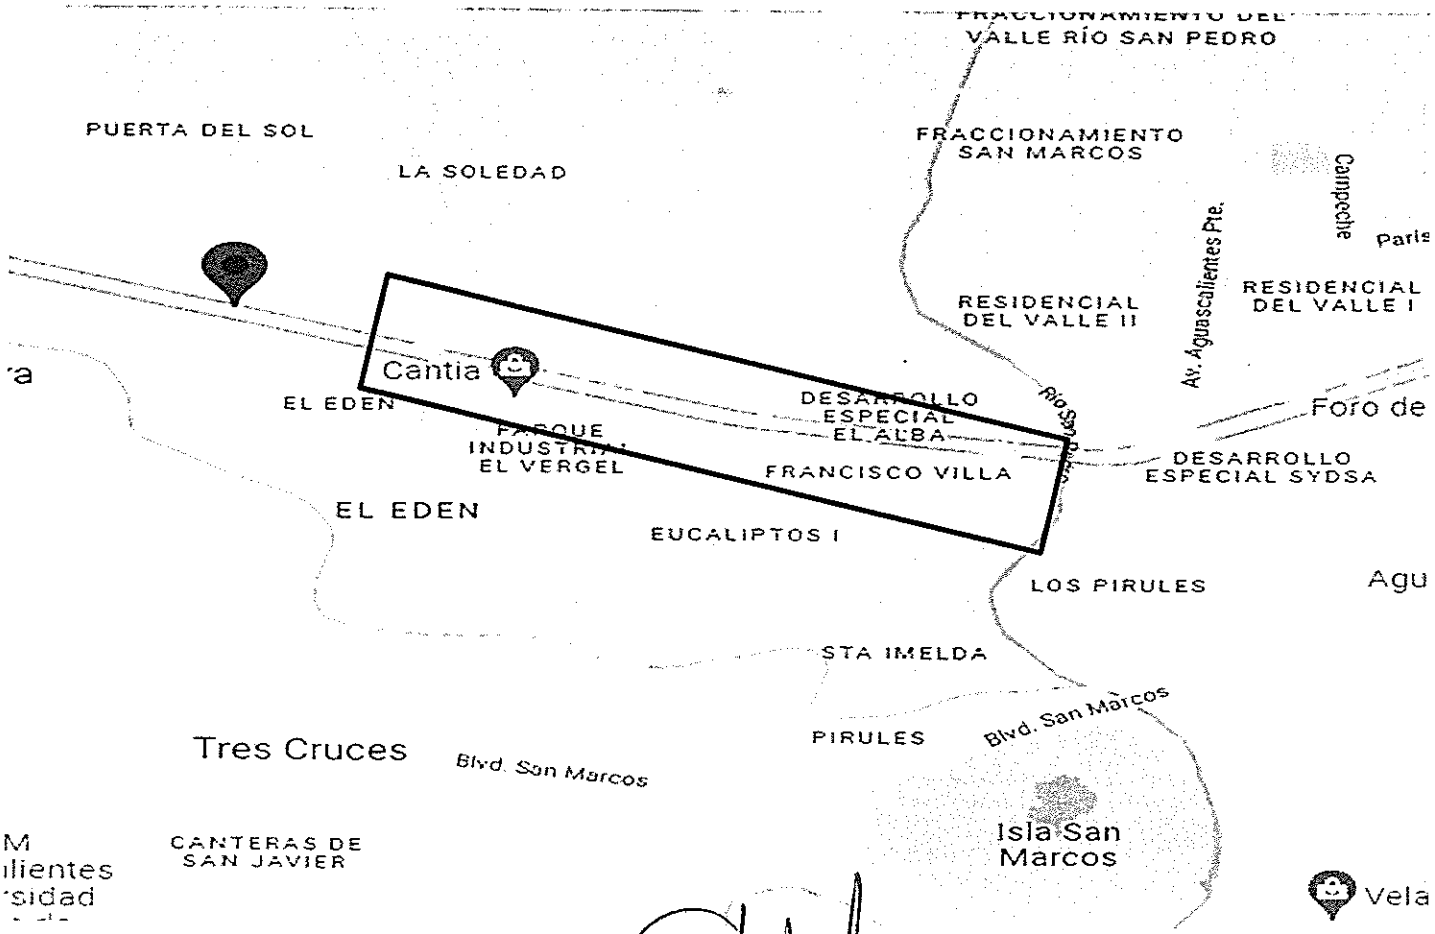

I.C. LAURA CECILIA MARTÍNEZ ALBA
RESIDENTE DE SUPERVISIÓN

PRESIDENCIA MUNICIPAL DE AGUASCALIENTES

FACTIBILIDAD VERIFICADA EN CAMPO

GENERALES

LOCALIDAD: BLVD. ADOLFO RUÍZ CORTINES, TRAMO: ENTRE SALIDA PUENTE PIRULES Y AV. ABELARDO L. RODRÍGUEZ, LA SOLEDAD Fracc.

MUNICIPIO: AGUASCALIENTES

PROGRAMA: 04 - URBANIZACION MUNICIPAL

SUB-PROGRAMA:

OBRA A REALIZARSE: OBRA COMPLEMENTARIA Y SEÑALIZACIÓN BLVD. ADOLFO RUÍZ CORTINES

DEPENDENCIA EJECUTORA: SECRETARÍA DE OBRAS PÚBLICAS MUNICIPALES (S.O.P.M.A)

FORMACIÓN DE EJECUCION: CONTRATO

TIPO DE OBRA PROPUESTA

NUEVA CREACIÓN		CONSOLIDACIÓN	
COMPLEMENTARIA	X	AMPLIACIÓN	
REHABILITACIÓN		EQUIPAMIENTO	

CARACTERÍSTICAS DE LA OBRA:

OBRA COMPLEMENTARIA Y SEÑALIZACIÓN BLVD. ADOLFO RUÍZ CORTINES

CONDICIONES ACTUALES DE LA OBRA:

BUEN ESTADO	X	REGULAR		PESIMO ESTADO	

FACTIBILIDAD DE LA OBRA:

SE HACE ENTREGA DE LA OBRA DE ACUERDO A LAS METAS INICIALES, ATENDIENDO EL CONTRATISTA LOS DETALLES MARCADOS PREVIOS A LA ENTREGA.

PROCEDE SI X NO

Aguascalientes
LA CIUDAD DE TU VIDA

I.C. LAURA CECILIA MARTINEZ ALBA
SUPERVISOR

H. AYUNTAMIENTO CONSTITUCIONAL DEL MUNICIPIO DE AGUASCALIENTES 2021-2024

PRESUPUESTO MODIFICADO

Aguascalientes

Obra: **OBRA COMPLEMENTARIA Y SEÑALIZACIÓN BLVD. ADOLFO RUÍZ CORTINES**

Ubicación: **TRAMO: ENTRE SALIDA PUENTE PIRULES Y AV. ABELARDO L. RODRÍGUEZ, LA SOLEDAD Fracc.**

Contratista: **CONSTRUCTORA VALDEZ RODRIGUEZ, S.A. DE C.V. (124)**

Grupo	Partida	Importe
OBRA COMPLEMENTARIA Y SEÑALIZACION		
	PRELIMINARES	$13,823.81
	OBRA COMPLEMENTARIA	$389,608.95
	LIMPIEZAS	$1,944.74
	SEÑALIZACION HORIZONTAL	$800,080.33
	Subtotal por Grupo	**$1,205,457.83**

Totales Presup.		$1,205,457.83
Anticipo	+	$361,637.35
Amortizac. Ant.	-	$361,637.35
SubTotal. Ant.	=	$1,205,457.83
IVA	+	$192,873.26
Total	=	$1,398,331.09

PRESUPUESTO MODIFICADO

Obra: **OBRA COMPLEMENTARIA Y SEÑALIZACIÓN BLVD. ADOLFO RUÍZ CORTINES**

Ubicación: **TRAMO: ENTRE SALIDA PUENTE PIRULES Y AV. ABELARDO L. RODRÍGUEZ, LA SOLEDAD Fracc.**

Contratista: **CONSTRUCTORA VALDEZ RODRIGUEZ, S.A. DE C.V. (124)**

No.	Concepto	Unidad	Cantidad	Precio Unitario	Importe Total
	GRUPO: **OBRA COMPLEMENTARIA Y SEÑALIZACION**				
	PARTIDA: **PRELIMINARES**				
1	CORTE CON DISCO DIAMANTADO DE 14" EN PISOS DE CONCRETO ASFÁLTICO DE HASTA (HASTA 8.00 cm. DE PROFUNDIDAD). INCLUYE: TRAZO, EQUIPO Y OPERACIÓN, LIMPIEZAS.	ML	160	$26.86	$4,297.60
2	DEMOLICIÓN A MANO Y MECÁNICA DE PAVIMENTO HIDRÁULICO Y/O ASFÁLTICO EN CUALQUIER ESPESOR, EN PAVIMENTOS, LOSAS DIAMANTE, LOSAS DE CAJAS DE VÁLVULAS, LOSAS DE LLAVE HIDRAULICA, CAIMANES, ETC., CON O SIN ARMADO DE ACERO SIN RECUPERACIÓN., INCLUYE: CARGA Y ACARREO LOCAL DE MATERIAL AL LUGAR DE ACOPIO, HERRAMIENTA NECESARIA, CORTES CON DISCO Y TODO LO NECESARIO PARA SU CORRECTA EJECUCIÓN, LIMPIEZA, TRABAJO TERMINADO.	M3	17.31	$399.27	$6,911.36
3	CARGA MECANICA Y ACARREO DE MATERIAL PRODUCTO DE EXCAVACION Y DEMOLICION EN CAMION DE VOLTEO AL 1er. KM, VOLUMEN MEDIDO COMPACTO.	M3	17.31	$43.15	$746.93
4	ACARREO DE MATERIAL PRODUCTO DE EXCAVACION Y/O DEMOLICION EN CAMION DE VOLTEO A KILOMETROS SUBSECUENTES, AL TIRADERO OFICIAL AUTORIZADO MAS CERCANO AUTORIZADO POR LA SUPERVISION, VOLUMEN MEDIDO COMPACTO.	M3-KM	190.41	$9.81	$1,867.92
				Totales por Partida	**$13,823.81**
	PARTIDA: **OBRA COMPLEMENTARIA**				
5	RE NIVELACIÓN DE POZO DE VISITA HASTA 30 cm DE ALTURA. INCLUYE: RETIRO SIN RECUPERACIÓN DE BROCAL EXISTENTE, DEMOLICIONES, NIVELADO CON TABIQUE ROJO RECOCIDO 7X14X28, ASENTADO CON MORTERO CEMENTO-ARENA 1:3 DE 28 cm DE ESPESOR, APLANADO CON MORTERO CEMENTO-ARENA 1:3 , PLOMEADO, NIVELADO, DEMOLICIONES, CARGAS Y ACARREOS DENTRO DE LA OBRA, LIMPIEZA PREVIA Y FINAL.	PZA	20	$2,791.04	$55,820.80
6	CONSTRUCCIÓN DE LOSA DIAMANTE A BASE DE CONCRETO PREMEZCLADO MR= 45 KG/CM2, T.M.A. 3/4" (19 mm), GRAVA TRITURADA, REVENIMIENTO DE 8+-2.5 cm, RESISTENCIA RÁPIDA A 3 DÍAS, DE 25 CM DE ESPESOR, EN POZO DE VISITA, SECCIÓN DE 1.50 M X 1.50 M , INCLUYE: TRAZO, NIVELACIÓN, LIMPIEZA PREVIA Y PREPARACIÓN DE LA SUPERFICIE, COMPACTACIÓN DE TERRENO AL 95% DE SU PVSM, ESCARIFICADO, SUMINISTRO DE MATERIALES, DEMOLICIÓN Y RECONSTRUCCIÓN DE APROCHES, ESPUMA DE POLIURETANO DE ALTA DENSIDAD EN TODO EL PERÍMETRO EXTERIOR DE 1/2", ASÍ COMO EN LAS JUNTAS DIAGONALES PARA FORMAR 4 PARTES, BROCAL Y TAPA DE Fo. Fo. TIPO PESADO (165 KG), CIMBRADO, COLADO, VIBRADO, DESCIMBRADO, CURADO CON MEMBRANA QUÍMICA BASE AGUA, APLANADO FINO EN RECEPCIÓN DE BROCAL, CORTES CON CORTADORA DE DISCO DE 5 CM ENTRE JUNTAS DIAGONALES FORMANDO 8 PIEZAS Y SELLADO DE JUNTAS, CORTES RELLENOS CON MATERIAL PREFORMADO Y SELLADOR AUTONIVELANTE, MANO DE OBRA, CARGA Y ACARREOS DE MATERIAL DENTRO Y FUERA DE LA OBRA, LIMPIEZA FINAL, TRABAJO TERMINADO P.U.O.T	PZA	20	$8,153.34	$163,066.80

Obra: **OBRA COMPLEMENTARIA Y SEÑALIZACIÓN BLVD. ADOLFO RUÍZ CORTINES**

Ubicación: **TRAMO: ENTRE SALIDA PUENTE PIRULES Y AV. ABELARDO L. RODRÍGUEZ, LA SOLEDAD Fracc.**

Contratista: **CONSTRUCTORA VALDEZ RODRIGUEZ, S.A. DE C.V. (124)**

No.	Concepto	Unidad	Cantidad	Precio Unitario	Importe Total
	GRUPO: **OBRA COMPLEMENTARIA Y SEÑALIZACION**				
	PARTIDA: **OBRA COMPLEMENTARIA**				
7	RENIVELACIÓN DE RASANTE (PARTE SUPERIOR) DE CAJA DE VÁLVULAS TIPO 2, ó DE HASTA 1.20 X 1. 30 MTS, NIVELADO HASTA UNA ALTURA MAXIMA DE 10 CM, Y MINIMA DE 5 CM. MEDIDAS INTERIORES INCLUYE: TRAZO, EXCAVACIÓN, NIVELACIÓN, PREPARACIONES , Y DEMOLICIONES, RETIRO SIN RECUPERACIÓN DE TAPA DE FOFO EXISTENTE, MURO DE TABIQUE ROJO RECOCIDO COMÚN 7X14X28 CM DE 14 CM DE ESPESOR, JUNTEADO CON MORTERO CEMENTO-ARENA 1:3 APLANADO INTERIOR CON MORTERO CEMENTO ARENA 1:3 DE 2.00 CM DE ESPESOR ACABADO PULIDO, LOSA DE CONCRETO F´C= 250 KG/CM2 T.M.A. 19 MM DE 15 CM DE ESPESOR ARMADA CON VRS No. 3 @15 cm EN AMBOS SENTIDOS, CONTRAMARCO SENCILLO DE CANAL FoFo DE 100 mm, CONTRAMARCO CON TAPA DE FOFO, TIPO PESADO DE 50X50 CM, DEMOLICIÓN Y RECONSTRUCCIÓN DE APROCHES, CARGA Y ACARREOS DENTRO DE LA OBRA, CIMBRADO, DESCIMBRADO, COLADO, VIBRADO, LIMPIEZA PREVIA, FINAL, Y TODO LO NECESARIO PARA LA CORRECTA EJECUCIÓN DEL CONCEPTO.	PZA	3	$13,597.52	$40,792.56
8	RENIVELACION DE CAJA PARA VALVULA Y O LLAVE HIDRAULICA DE FOFO CORTA OBLARGA DE HASTA 145 MM DE DIAMETRO, INCLUYE: TRAZO, EXCAVACION, PREPARACIONES, Y DEMOLICIONES, LOSA DE CONCRETO SECCION 90X90 CM F'C= 250 KG/CM2 DE 15 CM. DE ESPESOR, ARMADA CON VS. NO.3 @ 30 CM. EN AMBOS SENTIDOS, ACARREOS DENTRO DE LA OBRA, CIMBRADO, DESCIMBRADO, COLADO, VIBRADO, LIMPIEZAS Y TODO LO NECESARIO PARA LA CORRECTA EJECUCION DEL CONCEPTO	PZA	1	$12,452.07	$12,452.07
9	RENIVELACION DE RASANTE (PARTE SUPERIOR DE CAIMAN) DE 6.5 M2 A MAXIMO 9.0 M2 Y HASTA 0.3 MTS DE ALTURA. INCLUYE: DESMONTAJE, DEMOLICION Y RETIRO CON RECUPERACION DE REJILLA EXISTENTE, NIVELADO CON TABIQUE ASENTADO CON MORTERO CEMENTO-ARENA 1:3 DE 28 cm DE ESPESOR, APLANADO CON MORTERO CEMENTO-ARENA 1:3, ACABADO PULIDO, COLOCACION DE REJILLA RECUPERADA Y REHABILITADA SEGUN PROYECTO O SIMILAR A LA EXISTENTE, CONSIDERAR LA CONSTRUCCION DE UNA CADENA DE CERRAMIENTO SECCION 28*20, CON 4 VRS No 4 y ESTRIBOS DEL No. 2 @ 20, CONCRETO F´c= 250 KG/CM2 TMA 19 MM RN. EN EL PEIMETRO DEL CAIMAN, PLOMEADO, CORTES, ANCLAS DE ACERO, REPOSICIONES, SOLDADURA EN TALLER Y CAMPO, DESPERDICIOS, NIVELADO, DEMOLICIONES, CARGAS Y ACARREOS DENTRO Y FUERA DE LA OBRA MAQUINARIA, MANO DE OBRA MATERIALES, LIMPIEZAS TRABAJO TERMINADO. PUOT.	PZA	1	$16,909.54	$16,909.54
11	LIMPIEZA Y DESAZOLVE DE POZOS DE VISITA Y LÍNEAS DE ALCANTARILLADO EXISTENTE CON CAMIÓN TIPO VACTOR. INCLUYE: RESANE INTERIOR DEL POZO Y REMATE DE POZO CON TUBO SELLADOR FESTER Y MORTERO 1:3, MANO DE OBRA, SUMINISTRO DE AGUA EN PIPA, HERRAMIENTAS Y EQUIPO PARA SU CORRECTA EJECUCIÓN, LIMPIEZAS, RENTA DE CAMIÓN VACTOR HASTA LA CORRECTA LIMPIEZA DE LAS LÍNEAS EXISTENTES DE POZO A POZO ASÍ COMO EL TRASLADO DE LOS DESECHOS HASTA TIRADERO AUTORIZADO, LA UNIDAD DE MEDIDA SE PAGARA DE POZO A POZO.	LOTE	14	$7,183.37	$100,567.18
			Totales por Partida		**$389,608.95**
	PARTIDA: **LIMPIEZAS**				
12	LIMPIEZA FINAL DE LA OBRA, INCLUYE: BARRIDO, CARGA, ACARREOS Y RETIRO DE ESCOMBROS FUERA DE LA OBRA, TRABAJO TERMINADO.	M2	160.7223140496	$12.10	$1,944.74
			Totales por Partida		**$1,944.74**

Obra: **OBRA COMPLEMENTARIA Y SEÑALIZACIÓN BLVD. ADOLFO RUÍZ CORTINES**

Ubicación: **TRAMO: ENTRE SALIDA PUENTE PIRULES Y AV. ABELARDO L. RODRÍGUEZ, LA SOLEDAD Fracc.**

Contratista: **CONSTRUCTORA VALDEZ RODRIGUEZ, S.A. DE C.V. (124)**

No.	Concepto	Unidad	Cantidad	Precio Unitario	Importe Total
	GRUPO: **OBRA COMPLEMENTARIA Y SEÑALIZACION**				
	PARTIDA: **SEÑALIZACION HORIZONTAL**				
13	SUMINISTRO Y APLICACIÓN DE PINTURA BASE SOLVENTE COLOR AZUL (PANTONE 294) EN RAMPAS PARA PERSONAS CON DISCAPACIDAD CUALQUIER SECCIÓN SEGÚN PLANOS. INCLUYE: TRAZO, MANO DE OBRA, LIMPIEZA PREVIA Y FINAL DE SUPERFICIE, EQUIPO NECESARIO PARA SU EJECUCIÓN, Y TODO LO NECESARIO PARA SU CORRECTA EJECUCIÓN, TRABAJO TERMINADO.	M2	27.8	$346.72	$9,638.82
14	SUMINISTRO Y APLICACIÓN DE LOGOTIPO A (SILLA DE RUEDAS) EN PINTURA BASE SOLVENTE COLOR BLANCO EN RAMPAS PARA PERSONAS CON DISCAPACIDAD TAMAÑO Y DISEÑO SEGÚN PLANOS Y PROYECTO. INCLUYE: TRAZO, ENMASCARILLADO, PLANTILLA, MANO DE OBRA, LIMPIEZA PREVIA Y FINAL DE SUPERFICIE, EQUIPO NECESARIO PARA SU EJECUCIÓN, Y TODO LO NECESARIO PARA SU CORRECTA EJECUCIÓN, TRABAJO TERMINADO.	PZA	13	$221.04	$2,873.52
15	SUMINISTRO Y APLICACIÓN DE PINTURA BASE SOLVENTE (ESMALTE) PARA MARCAS EN GUARNICIONES CLASIFICACION M-12.1, M12.2 APLICADA SOBRE GUARNICIONES Y DENTELLONES COLOR BLANCA Y/O AMARILLA, SEGÚN SE REQUIERA Y SEGÚN MANUAL DE SEÑALIZACIÓN VIAL Y DISPOSITIVOS DE SEGURIDAD SICT (S.C.T). SECADO AL TACTO EN 5 MIN Y AL DURO EN 30 MIN CON MICRO ESFERA , DESARROLLO DE 35 CM. INCLUYE: MATERIALES Y ESPECIFICACIONES QUE CUMPLAN CON LA NORMATIVA N-CMT-5-01-001/13, N-PRY-CAR-10-01-002/13 APLICADAS AL DIA DE HOY, TRAZO, MANO DE OBRA, LIMPIEZA PREVIA Y FINAL DE SUPERFICIE, EQUIPO NECESARIO PARA SU EJECUCIÓN, Y TODO LO NECESARIO PARA SU CORRECTA EJECUCIÓN, TRABAJO TERMINADO.	ML	2451.6	$45.01	$110,356.32
16	SUMINISTRO Y APLICACIÓN DE PINTURA TERMOPLASTICA ALQUIDALICA DE 120 MILESIMAS DE " (in) EN RAYA EN LA ORILLA DEL ARROYO VIAL CLASIFICACIÓN M - 3.3, CONTINUA IZQUIERDA, PARA VIALIDADES URBANAS DE FRENTE EN PISO, DE 10 CM DE ANCHO Y SEPARADA 15 CM. DE LA GUARNICION, A BASE DE PINTURA PARA TRAFICO COLOR BLANCO CON MICRO ESFERA SEGÚN MANUAL DE SEÑALIZACIÓN VIAL Y DISPOSITIVOS DE SEGURIDAD SICT (S.C.T)., INCLUYE: MATERIALES Y ESPECIFICACIONES QUE CUMPLAN CON LA NORMATIVA N-CMT-5-01-001/13, N-PRY-CAR-10-01-002/13 APLICADAS AL DIA DE HOY, MATERIAL APLICADO EN SU ESTADO DE FUSION A UNA TEMPERATURA MINIMA DE 204 C, LA SUPERFICIE DE CONCRETO O ASFALTO NO DEBE PRESENTAR UNA TEMPERATURA MENOR A LOS 10 C, ;TIEMPO DE SECADO EN RANGOS DE TEMPERATURA DE 10 C DEL SUSTRATO 2 MINUTOS, Y NO MAS DE 10 MINUTOS CUANDO EL SUSTRATO OSCILA ALREDEDOR DE 54C, TRAZO, ENMASCARILLADO, MANO DE OBRA, LIMPIEZA PREVIA Y FINAL DE SUPERFICIE, EQUIPO NECESARIO PARA SU EJECUCIÓN, Y TODO LO NECESARIO PARA SU CORRECTA EJECUCIÓN, TRABAJO TERMINADO.	ML	2423.8903	$91.14	$220,913.36
17	SUMINISTRO Y APLICACIÓN DE PINTURA TERMOPLASTICA ALQUIDALICA DE 120 MILESIMAS DE " (in) EN RAYA DE ALTO CLASIFICACIÓN M - 6, PARA INDICAR ALTO EN CRUCEROS, COLOR BLANCO, REFLEJANTE CON MICRO ESFERA DE VIDRIO EN PROPORCIÓN SEGÚN MANUAL DE SEÑALIZACIÓN VIAL Y DISPOSITIVOS DE SEGURIDAD SICT (S.C.T). DE 0.60 MTS DE ANCHO DE LONGITUD VARIABLE, INCLUYE: MATERIALES Y ESPECIFICACIONES QUE CUMPLAN CON LA NORMATIVA N-CMT-5-01-001/13, N-PRY-CAR-10-01-002/13 APLICADAS AL DIA DE HOY, MATERIAL APLICADO EN SU ESTADO DE FUSION A UNA TEMPERATURA MINIMA DE 204 C, LA SUPERFICIE DE CONCRETO O ASFALTO NO DEBE PRESENTAR UNA TEMPERATURA MENOR A LOS 10 C, ;TIEMPO DE SECADO EN RANGOS DE TEMPERATURA DE 10 C DEL SUSTRATO 2 MINUTOS, Y NO MAS DE 10 MINUTOS CUANDO EL SUSTRATO OSCILA ALREDEDOR DE 54C, TRAZO, ENMASCARILLADO, MANO DE OBRA, LIMPIEZA PREVIA Y FINAL DE SUPERFICIE, EQUIPO NECESARIO PARA SU EJECUCIÓN, Y TODO LO NECESARIO PARA SU CORRECTA EJECUCIÓN, TRABAJO TERMINADO.	ML	62.95	$502.42	$31,627.34



Obra: **OBRA COMPLEMENTARIA Y SEÑALIZACIÓN BLVD. ADOLFO RUÍZ CORTINES**

Ubicación: **TRAMO: ENTRE SALIDA PUENTE PIRULES Y AV. ABELARDO L. RODRÍGUEZ, LA SOLEDAD Fracc.**

Contratista: **CONSTRUCTORA VALDEZ RODRIGUEZ, S.A. DE C.V. (124)**

No.	Concepto	Unidad	Cantidad	Precio Unitario	Importe Total
	GRUPO: **OBRA COMPLEMENTARIA Y SEÑALIZACION**				
	PARTIDA: **SEÑALIZACION HORIZONTAL**				
18	SUMINISTRO Y APLICACIÓN DE PINTURA TERMOPLASTICA ALQUIDALICA DE 120 MILESIMAS DE " (in) EN RAYA PARA CRUCE PEATONAL CLASIFICACIÓN M - 7.1, PARA INDICAR " CRUCE PEATONAL EN VIAS PRIMARIAS", COLOR AMARILLO, REFLEJANTE CON MICRO ESFERA DE VIDRIO EN PROPORCIÓN SEGÚN MANUAL DE SEÑALIZACIÓN VIAL Y DISPOSITIVOS DE SEGURIDAD SICT (S.C.T). DE 0.40 MTS DE ANCHO Y 3.5 MTS. DE LONGITUD POR EL ANCHO DE LA VIALIDAD, CON UNA SEPARACIÓN DE 0.40 MTS. ENTRE ELLAS, INCLUYE: MATERIALES Y ESPECIFICACIONES QUE CUMPLAN CON LA NORMATIVA N-CMT-5-01-001/13, N-PRY-CAR-10-01-002/13 APLICADAS AL DIA DE HOY, MATERIAL APLICADO EN SU ESTADO DE FUSION A UNA TEMPERATURA MINIMA DE 204 C, LA SUPERFICIE DE CONCRETO O ASFALTO NO DEBE PRESENTAR UNA TEMPERATURA MENOR A LOS 10 C, ;TIEMPO DE SECADO EN RANGOS DE TEMPERATURA DE 10 C DEL SUSTRATO 2 MINUTOS, Y NO MAS DE 10 MINUTOS CUANDO EL SUSTRATO OSCILA ALREDEDOR DE 54C, TRAZO, ENMASCARILLADO, MANO DE OBRA, LIMPIEZA PREVIA Y FINAL DE SUPERFICIE, EQUIPO NECESARIO PARA SU EJECUCIÓN, Y TODO LO NECESARIO PARA SU CORRECTA EJECUCIÓN, TRABAJO TERMINADO.	M2	372.99	$575.97	$214,831.05
19	SUMINISTRO Y APLICACIÓN DE PINTURA TERMOPLASTICA ALQUIDALICA DE 120 MILESIMAS DE " (in) EN FLECHAS CLASIFICACIÓN M - 11.1, "FLECHA SENCILLA" PARA INDICAR SENTIDO DE CIRCULACIÓN , EN VIALIDADES PARA VELOCIDAD MENOR A 60KM POR HORA DIMENSION NORMATIVA SEGUN MANUAL DE SEÑALIZACIÓN VIAL Y DISPOSITIVOS DE SEGURIDAD SICT (SCT) Y/O (VER PLANO DE SEÑALAMIENTOS), COLOR BLANCO, REFLEJANTE CON MICRO ESFERA DE VIDRIO EN PROPORCIÓN SEGÚN NORMA SCT, INCLUYE: MATERIALES Y ESPECIFICACIONES QUE CUMPLAN CON LA NORMATIVA N-CMT-5-01-001/13, N-PRY-CAR-10-01-002/13 APLICADAS AL DIA DE HOY, MATERIAL APLICADO EN SU ESTADO DE FUSION A UNA TEMPERATURA MINIMA DE 204 C, LA SUPERFICIE DE CONCRETO O ASFALTO NO DEBE PRESENTAR UNA TEMPERATURA MENOR A LOS 10 C, ;TIEMPO DE SECADO EN RANGOS DE TEMPERATURA DE 10 C DEL SUSTRATO 2 MINUTOS, Y NO MAS DE 10 MINUTOS CUANDO EL SUSTRATO OSCILA ALREDEDOR DE 54C, TRAZO, ENMASCARILLADO, MANO DE OBRA, LIMPIEZA PREVIA Y FINAL DE SUPERFICIE, EQUIPO NECESARIO PARA SU EJECUCIÓN, Y TODO LO NECESARIO PARA SU CORRECTA EJECUCIÓN, TRABAJO TERMINADO.	PZA	39	$2,117.58	$82,585.62
20	SUMINISTRO Y APLICACIÓN DE PINTURA TERMOPLASTICA ALQUIDALICA DE 120 MILESIMAS DE " (in) EN FLECHAS CLASIFICACIÓN M - 11.1, " FLECHA CABEZA DOBLE" PARA INDICAR SENTIDO DE CIRCULACIÓN (VUELTA IZQUIERDA O DERECHA), EN VIALIDADES PARA VELOCIDAD MENOR A 60KM POR HORA SEGUN MANUAL DE SEÑALIZACIÓN VIAL Y DISPOSITIVOS DE SEGURIDAD SICT (SCT), (VER PLANO DE SEÑALAMIENTOS), EN COLOR BLANCO, REFLEJANTE CON MICRO ESFERA DE VIDRIO EN PROPORCIÓN SEGÚN NORMA SCT, INCLUYE: MATERIALES Y ESPECIFICACIONES QUE CUMPLAN CON LA NORMATIVA N-CMT-5-01-001/13, N-PRY-CAR-10-01-002/13 APLICADAS AL DIA DE HOY, MATERIAL APLICADO EN SU ESTADO DE FUSION A UNA TEMPERATURA MINIMA DE 204 C, LA SUPERFICIE DE CONCRETO O ASFALTO NO DEBE PRESENTAR UNA TEMPERATURA MENOR A LOS 10 C, ;TIEMPO DE SECADO EN RANGOS DE TEMPERATURA DE 10 C DEL SUSTRATO 2 MINUTOS, Y NO MAS DE 10 MINUTOS CUANDO EL SUSTRATO OSCILA ALREDEDOR DE 54C, TRAZO, ENMASCARILLADO, MANO DE OBRA, LIMPIEZA PREVIA Y FINAL DE SUPERFICIE, EQUIPO NECESARIO PARA SU EJECUCIÓN, Y TODO LO NECESARIO PARA SU CORRECTA EJECUCIÓN, TRABAJO TERMINADO.	PZA	2	$2,808.91	$5,617.82




Obra: **OBRA COMPLEMENTARIA Y SEÑALIZACIÓN BLVD. ADOLFO RUÍZ CORTINES**

Ubicación: **TRAMO: ENTRE SALIDA PUENTE PIRULES Y AV. ABELARDO L. RODRÍGUEZ, LA SOLEDAD Fracc.**

Contratista: **CONSTRUCTORA VALDEZ RODRIGUEZ, S.A. DE C.V. (124)**

No.	Concepto	Unidad	Cantidad	Precio Unitario	Importe Total
	GRUPO: **OBRA COMPLEMENTARIA Y SEÑALIZACION**				
	PARTIDA: **SEÑALIZACION HORIZONTAL**				
22	SUMINISTRO Y COLOCACIÓN DE VIALETA STANDARD (S-200) DE 10X10CM. COLOR: CUERPO AMARILLO Y/O BLANCO Y REFLEJANTE AMARILLO 1 CARA MARCA SEA O SIMILAR EN CALIDAD Y ESPECIFICACIONES DE FICHA TÉCNICA, FIJADO EN PAVIMENTO CON SISTEMA DE SUJECIÓN DE ALTO AGARRE PEGAMENTO EPOXICO 100 A/B (RESINA EPÓXICA/RESINA POLIAMIDA MODIFICADA), RESISTENTE A ALTA TEMPERATURA (VER PLANO DE DETALLES DE SEÑALAMIENTOS HORIZONTAL), INCLUYE: LIMPIEZA PREVIA Y FINAL DE LA SUPERFICIE, PREPARACIÓN DE LA SUPERFICIE, TRAZO, ALINEACIÓN, Y TODO LO NECESARIO PARA SU CORRECTA EJECUCIÓN, TRABAJO TERMINADO.	PZA	318	$94.62	$30,089.16
23	SUMINISTRO Y COLOCACION DE VIALETA SOLAR DE 10X10CM. COLOR: CUERPO ALUMINIO 3 LED DOS CARAS REFLEJANTES MARCA CREATIVAL VT-29 O SIMILAR EN CALIDAD Y ESPECIFICACIONES DE FICHA TÉCNICA, FIJADO EN PAVIMENTO CON SISTEMA DE SUJECIÓN DE ALTO AGARRE PEGAMENTO EPOXICO 100 A/B (RESINA EPÓXICA/RESINA POLIAMIDA MODIFICADA), RESISTENTE A ALTA TEMPERATURA (VER PLANO DE DETALLES DE SEÑALAMIENTOS HORIZONTAL), INCLUYE: LIMPIEZA PREVIA Y FINAL DE LA SUPERFICIE+C92, PREPARACIÓN DE LA SUPERFICIE, TRAZO, ALINEACIÓN, Y TODO LO NECESARIO PARA SU CORRECTA EJECUCIÓN, TRABAJO TERMINADO.	PZA	163	$561.64	$91,547.32

Totales por Partida		**$800,080.33**
Totales por Grupo		**$1,205,457.83**
Totales Presup.		**$1,205,457.83**
Anticipo	**+**	**$361,637.35**
Amortizac. Ant.	**-**	**$361,637.35**
SubTotal. Ant.	**=**	**$1,205,457.83**
IVA	**+**	**$192,873.26**
Total	**=**	**$1,398,331.09**

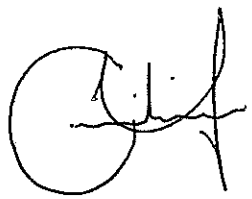

PROGRAMA DE OBRA DEFINITIVO

Aguascalientes
LA CIUDAD DE TU VIDA

H. AYUNTAMIENTO CONSTITUCIONAL DEL MUNICIPIO DE AGUASCALIENTES 2021-2024

No. DE CONTRATO : FISMDF-0098-2022

PROGRAMA: 04 URBANIZACION MUNICIPAL

No. OBRA Y NOMBRE DE LA OBRA: 2022-FISMDF-0058-0411109-052 OBRA COMPLEMENTARIA Y SEÑALIZACIÓN BLVD. ADOLFO RUIZ CORTINES, TRAMO: ENTRE SALIDA PUENTE PIRULES Y AV. ABELARDO L. RODRÍGUEZ, LA SOLEDAD Fracc.

INICIO VIGENTE: 23-septiembre-22

TERMINO REAL: 22-octubre-22

RECURSO 2022

CONCEPTO				1	2	3	4	5	6	7	8	9	10	11	12	13	14	15	16	PONDERACIÓN %	
				2021																	
				OCTUBRE	NOVIEMBRE	DICIEMBRE	ENERO	FEBRERO	MARZO	ABRIL	MAYO	JUNIO	JULIO	AGOSTO	SEPTIEMBRE	OCTUBRE	NOVIEMBRE	DICIEMBRE	ENERO	FINANCIERO	FÍSICO
																				%	%
DESCRIPCION	INVERSION																				
OBRA COMPLEMENTARIA Y SENALIZACION BLVD. ADOLFO RUIZ CORTINES																					
TRAMO: ENTRE SALIDA PUENTE PIRULES Y AV. ABELARDO L. RODRÍGUEZ, LA SOLEDAD Fracc.																					
PRELIMINARES	$ 12,823.81	100																		1.15	11.11
OBRA COMPLEMENTARIA	$ 359,605.95	100																		32.32	22.22
LIMPIEZAS	$ 1,944.74	100																		0.18	22.22
SEÑALIZACION HORIZONTAL	$ 800,080.33	100																		66.37	44.44
SUBTOTAL SIN IVA	$ 1,205,457.83																				
AVANCE SEMANAL %																					
AVANCE SEMANAL ACUMULADO %																				100.00	100.0
EJERCICIO SEMANAL $															409,620.74	204,474.56	200,022.08	200,991.45		$ 1,205,457.83	
EJERCICIO MENSUAL $				$0.00	$0.00	$0.00	$0.00	$0.00	$0.00	$0.00	$0.00	$0.00	$0.00	$0.00	$409,620.74	$795,637.00	$0.00	$0.00	$0.00	$ 192,873.26	IVA 16
EJERCICIO MENSUAL ACUMULADO $				0.00	0.00	0.00	0.00	0.00	0.00	0.00	0.00	0.00	0.00	0.00	409,620.74	1,205,457.83	1,205,457.83	1,205,457.83	1,205,457.83		
EJERCIDO SEMANAL %																					
EJERCIDO MENSUAL %				0%	0%	0%	0%	0%	0%	0%	0%	0%	0%	0%	34%	66%	0%	0%	0%	GRAN TOTAL EJERCIDO	
EJERCIDO MENSUAL ACUMULADO %				0%	0%	0%	0%	0%	0%	0%	0%	0%	0%	0%	34%	100%	100%	100%	100%	$	1,398,331.0

ING. LAURA CECILIA MARTÍNEZ ARBA
RESIDENTE DE SUPERVISIÓN


H. AYUNTAMIENTO DE AGUASCALIENTES
SECRETARÍA DE OBRAS PÚBLICAS
DIRECCIÓN DE SUPERVISIÓN DE OBRA


Aguascalientes
LA CIUDAD DE TU VIDA


MEMORIA FOTOGRÁFICA

OBRA:	**OBRA COMPLEMENTARIA Y SEÑALIZACIÓN BLVD. ADOLFO RUÍZ CORTINES, TRAMO: ENTRE SALIDA PUENTE PIRULES Y AV. ABELARDO L. RODRÍGUEZ, LA SOLEDAD Fracc.**		
NO. DE CONTRATO:	**FISMDF-0098-2022**	CONTRATISTA:	**CONSTRUCTORA VALDEZ RODRIGUEZ, S.A. DE C.V.**

INICIO

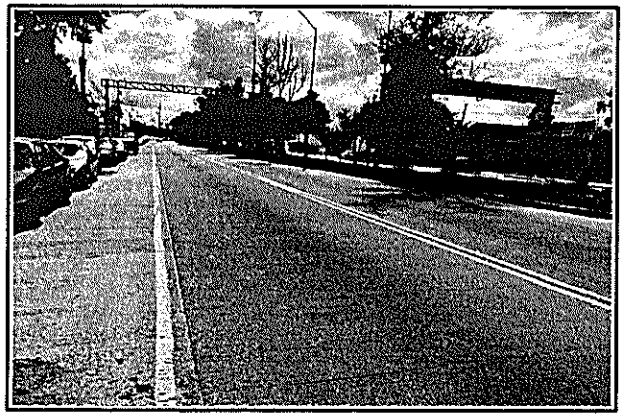

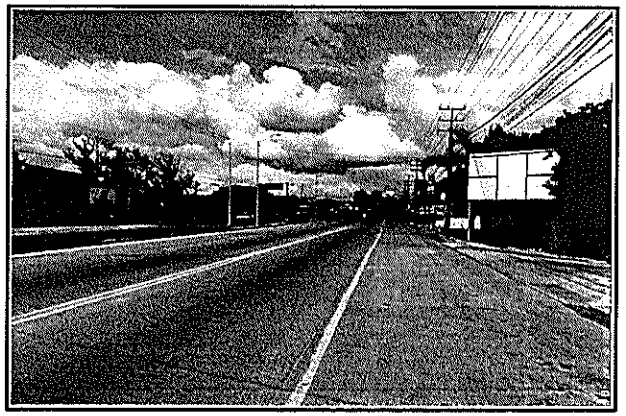

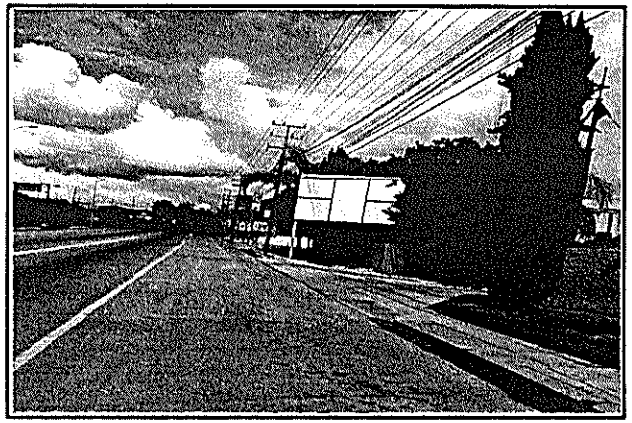



I.C. LAURA CECILIA MARTINEZ ALBA
RESIDENTE DE SUPERVISIÓN


H. AYUNTAMIENTO DE AGUASCALIENTES
SECRETARÍA DE OBRAS PÚBLICAS
DIRECCIÓN DE SUPERVISIÓN DE OBRA


MEMORIA FOTOGRÁFICA


OBRA:	OBRA COMPLEMENTARIA Y SEÑALIZACIÓN BLVD. ADOLFO RUÍZ CORTINES, TRAMO: ENTRE SALIDA PUENTE PIRULES Y AV. ABELARDO L. RODRÍGUEZ, LA SOLEDAD Fracc.		
NO. DE CONTRATO:	FISMDF-0098-2022	CONTRATISTA:	CONSTRUCTORA VALDEZ RODRIGUEZ, S.A. DE C.V.

PROCESO



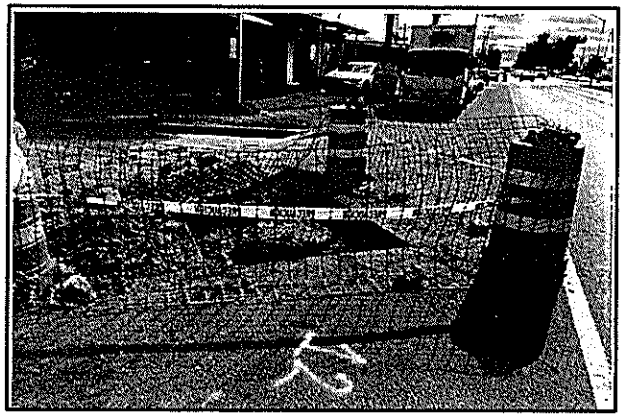

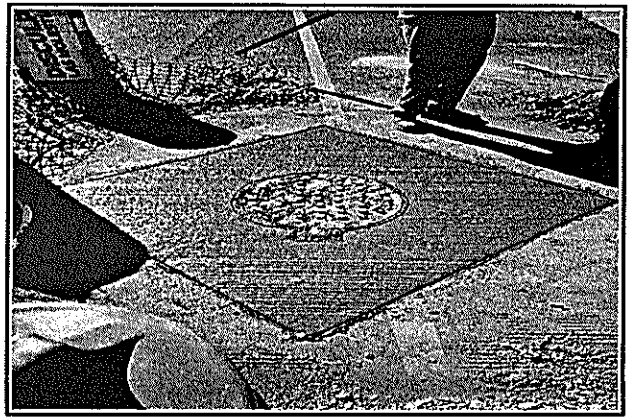

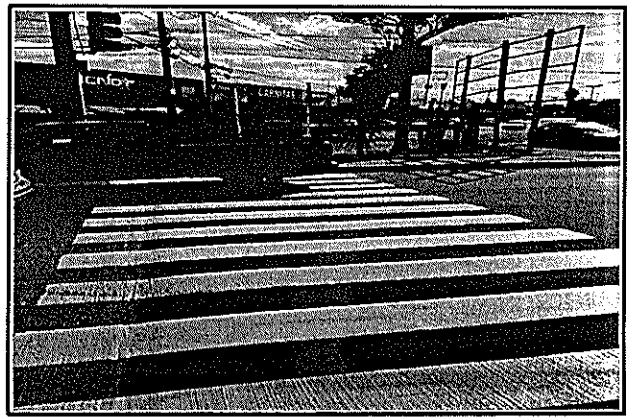

I.C. LAURA CECILIA MARTINEZ ALBA
RESIDENTE DE SUPERVISIÓN

H. AYUNTAMIENTO DE AGUASCALIENTES
SECRETARÍA DE OBRAS PÚBLICAS
DIRECCIÓN DE SUPERVISIÓN DE OBRA


Aguascalientes
LA CIUDAD DE TU VIDA


MEMORIA FOTOGRÁFICA

OBRA:	**OBRA COMPLEMENTARIA Y SEÑALIZACIÓN BLVD. ADOLFO RUÍZ CORTINES, TRAMO: ENTRE SALIDA PUENTE PIRULES Y AV. ABELARDO L. RODRÍGUEZ, LA SOLEDAD Fracc.**		
NO. DE CONTRATO:	**FISMDF-0098-2022**	CONTRATISTA:	**CONSTRUCTORA VALDEZ RODRIGUEZ, S.A. DE C.V.**

FINAL



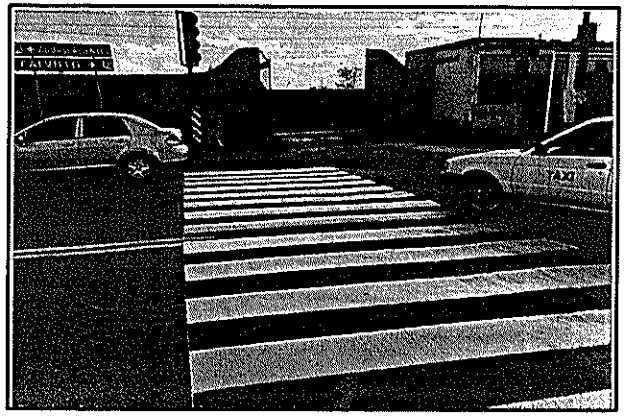

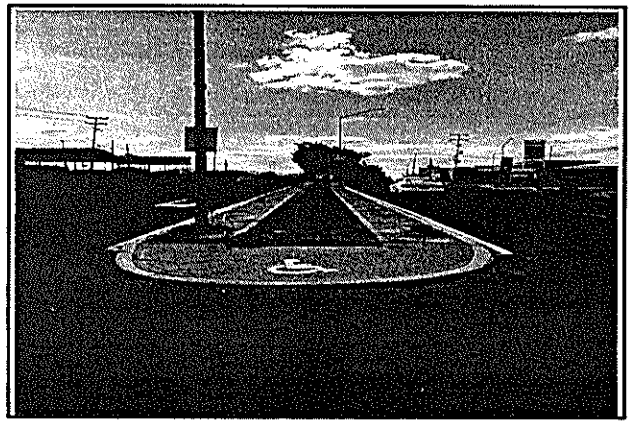



I.C. LAURA CECILIA MARTINEZ ALBA
RESIDENTE DE SUPERVISIÓN

EXPEDIENTE MODIFICADO

SECRETARÍA DE OBRAS PÚBLICAS

DIRECCIÓN DE SUPERVISIÓN DE OBRA

EJERCICIO: 2022

N° DE CONTRATO: FISMDF-0098-2022

NOMBRE DE LA OBRA: OBRA COMPLEMENTARIA Y SEÑALIZACIÓN BLVD. ADOLFO RUÍZ CORTINES, TRAMO: ENTRE SALIDA PUENTE PIRULES Y AV. ABELARDO L. RODRÍGUEZ, LA SOLEDAD Fracc.

MONTO MODIFICADO FINAL: $1,398,331.09

VOLUMEN	UNIDAD	COMPONENTE DE LA OBRA	MONTO
17.31	M³	ASFALTICO EN CUALQUIER ESPESOR, EN PAVIMENTOS, LOSAS DIAMANTE,	$ 13,823.81
20.00	PZA	CONSTRUCCIÓN DE LOSA DIAMANTE A BASE DE CONCRETO	$ 389,608.95
152.13	M2	LIMPIEZA FINAL DE LA OBRA, INCLUYE: BARRIDO, CARGA, ACARREOS Y	$ 1,944.74
2416.70	ML	SUMINISTRO Y APLICACIÓN DE PINTURA TERMOPLASTICA ALQUIDALICA	$ 800,080.33


MONTO BASE: $ 1,205,457.83


IVA: $ 192,873.26

TOTAL: $ 1,398,331.09

I.C. Laura Cecilia Martínez Alba
RESIDENTE DE SUPERVISIÓN



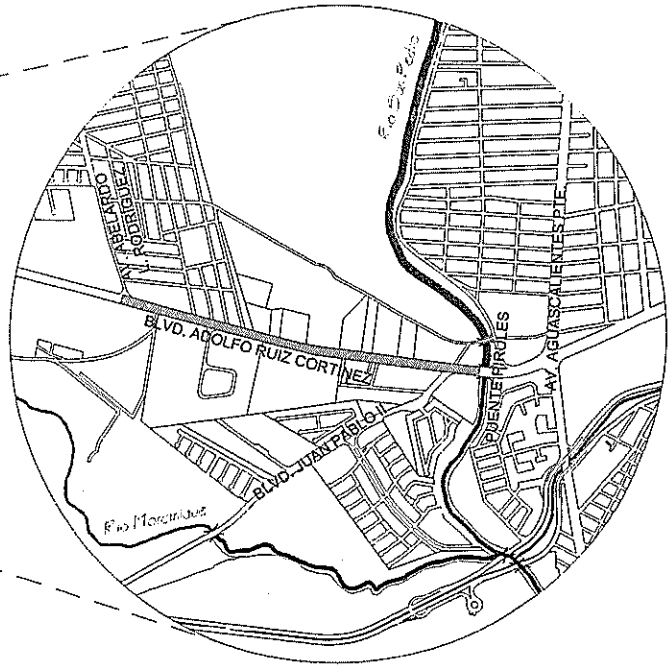

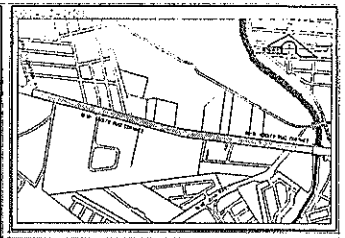

CROQUIS DE LOCALIZACIÓN

SIN ESCALA

BLVD. ADOLFO RUIZ CORTINEZ

PRESIDENTE MUNICIPAL
M.P.P. Leonardo Montañez Castro
ENCARGADA DE DESPACHO DE LA SOPMA
Ing. Miguel Angel Huizar Estello

CONSTRUCTORA VALDEZ-ROZ
REPRESENTANTE LEGAL
C. José Armando Valdez Rodríguez
RESIDENTE A CARGO
M. en I.C. Luis Eduardo Cadenas López

V°B° DE LA DEPENDENCIA

RESP. DE PROY. EXTERNO		LOGO EXTERNO
CED. PROFESIONAL		
PROYECTÓ	REVISÓ	AUTORIZÓ

Dirección de Planeación y Proyectos de Obra — Secretaría de Obras Públicos

PROYECTISTA	COORDINADOR
ARQ. MA. DOLORES HERNÁNDEZ DE LIRA	ARQ. ALEJANDRO JAIME LEAL
JEFE DE DEP.	DIRECTOR
ARQ. J. JESÚS PALAFOX GONZÁLEZ	ING. en ARQ. JOSÉ LUIS JIMÉNEZ GARCÍA

PROYECTO
OBRA COMPLEMENTARIA Y SEÑALIZACIÓN EN BLVD. ADOLFO RUIZ CORTINEZ
UBICACIÓN
BLVD. ADOLFO RUIZ CORTINEZ, ENTRE PUENTE PIRULES Y AV. ABELARDO L. RODRIGUEZ, FRACC. LA SOLEDAD
CONTENIDO
PLANO DE LOCALIZACIÓN


CLAVE	No. PLANO
LOC 01	01
FECHA	ESCALA
JUNIO 2022	INDICADA
ACOTACIÓN	No. EXP.
METROS	E-000-22

Aguascalientes
LA CIUDAD DE TU VIDA

PROYECTO GEOMÉTRICO

ESCALA 1:500 — BLVD. ADOLFO RUIZ CORTINEZ


TRAMO: DE AV. ABELARDO L. RODRIGUEZ A CALLE CIUDAD GUZMAN

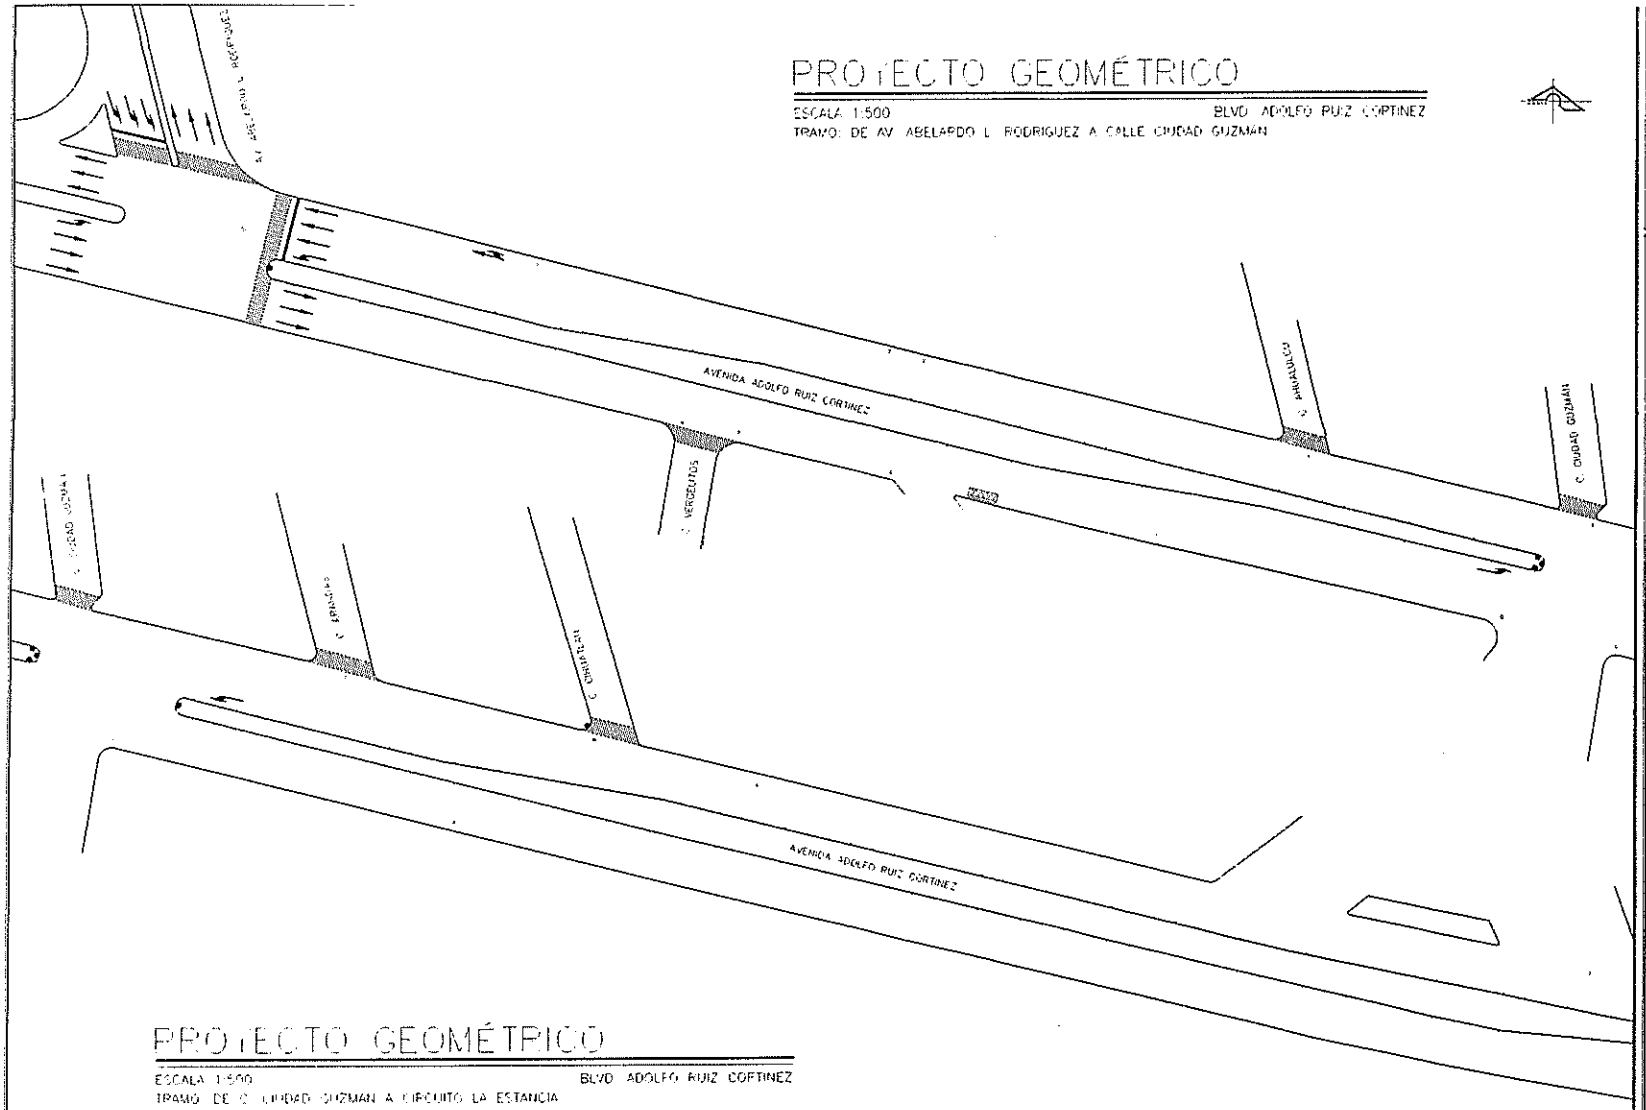

PROYECTO GEOMÉTRICO

ESCALA 1:500 — BLVD. ADOLFO RUIZ CORTINEZ

TRAMO: DE C. CIUDAD GUZMAN A CIRCUITO LA ESTANCIA

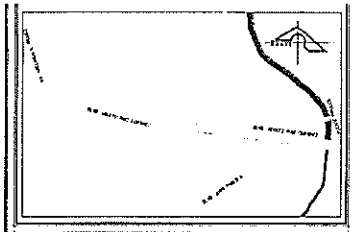

SIMBOLOGIA

- GUARNICIÓN
- FLECHA DE SENTIDO M-11.1
- LINEAS AMARILLAS DE CRUCE PEATCIAL M-7.1
- LINEA DE ALTO M-6
- POZO DE VISITA
- CAJA DE VALVULAS (TIPO 2)
- PAMPA DISCAPACITADOS
- VIALETA STANDARD (S-200)
- VIALETA SOLAR
- CAIMAN
- REGISTRO GAS NATURAL
- BOTA HIDRAULICA

M. en C. Leonardo Martínez Castro
Ing. Miguel Angel Huizar Botello

CONSTRUCTORA VALDEZ RDZ.
C. Juan Armando Valdez Rodriguez
M. en I.C. Luis Eduardo Cadenas López

V° Bo DE LA DEPENDENCIA

RESP. DE PROY. EXTERNO		LOGO EXTERNO
CED. PROFESIONAL		
PROYECTO	REVISÓ	AUTORIZÓ

Dirección de Planeación y Proyectos de Obra — Secretaría de Obras Públicas

ARQ. MA. DOLORES HERNANDEZ DE LIRA — ARQ. ALEJANDRO JAIME LEAL

ARQ. J. JESÚS PANIAGUA GONZALEZ — V.B. en ARQ. JOSE LUIS JIMENEZ GARCIA


OBRA COMPLEMENTARIA Y SEÑALIZACION EN BLVD. ADOLFO RUIZ CORTINEZ

BLVD. ADOLFO RUIZ CORTINEZ, ENTRE PUENTE PIRULES Y AV. ABELARDO L. RODRIGUEZ, FRACC. LA SOLEDAD

PROYECTO GEOMÉTRICO SEÑALIZACION HORIZONTAL

PG 01	05
JUNIO 2022	INDICADA
METROS	E-000-22

Aguascalientes
LA CIUDAD DE TU VIDA

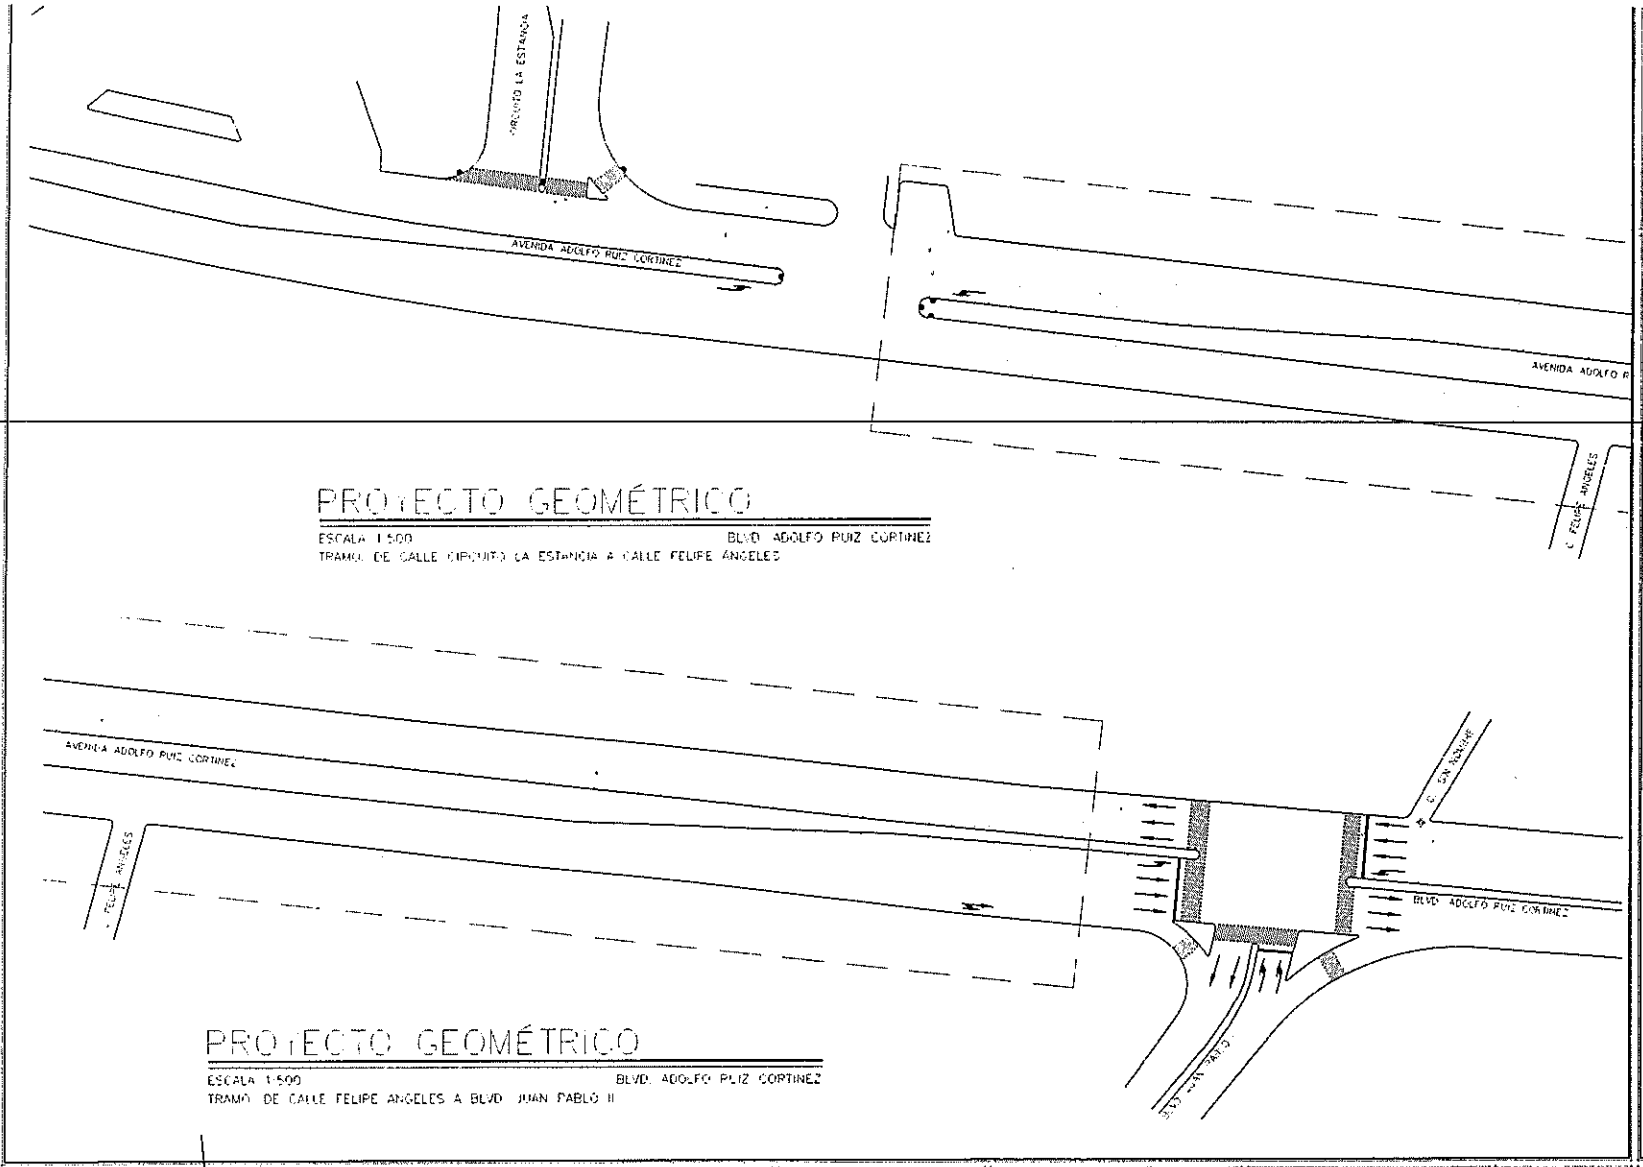

PROYECTO GEOMÉTRICO


ESCALA 1:500 BLVD. ADOLFO RUIZ CORTINEZ

TRAMO DE CALLE CIRCUITO LA ESTANCIA A CALLE FELIPE ANGELES

PROYECTO GEOMÉTRICO

ESCALA 1:500 BLVD. ADOLFO RUIZ CORTINEZ

TRAMO DE CALLE FELIPE ANGELES A BLVD. JUAN PABLO II

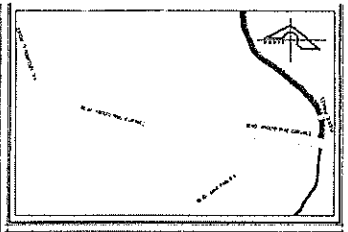

SIMBOLOGIA

- GUARNICIÓN
- FLECHA DE SENTIDO M-11.1
- LINEAS AMARILLAS DE CRUCE PEATONAL M-7.1
- LINEA DE ALTO M-6
- POZO DE VISITA
- CAJA DE VALVULAS (TIPO 2)
- RAMPA DISCAPACITADOS
- VIALETA STANDARD (S-200)
- VIALETA SOLAR
- CAIMAN
- REGISTRO GAS NATURAL
- BOTA HIDRÁULICA

M.P.P. Leonardo Montañez Castro

Ing. Miguel Angel Huizar Botello

CONSTRUCTORA VALDEZ RDZ.

C. José Armando Valdez Rodríguez

M. en I.C. Luis Eduardo Cadenas López

V°B° DE LA DEPENDENCIA

RESP DE PROY EXTERNO		LOGO EXTERNO
CED. PROFESIONAL		
PROYECTÓ	REVISO	AUTORIZÓ

Dirección de Planeación y Proyectos de Obra — Secretaría de Obras Públicas

ARQ. MA. DOLORES HERNANDEZ DE UBA — ARQ. ALEJANDRO JAIME LEAL

ARQ. J. JESUS PANIAGUA GONZALEZ — M. en ARQ. JOSE LUIS JUAREZ GARCIA

OBRA COMPLEMENTARIA Y SEÑALIZACIÓN EN BLVD. ADOLFO RUIZ CORTINEZ

BLVD. ADOLFO RUIZ CORTINEZ, ENTRE PUENTE PIRULES Y AV. ABELARDO L. RODRIGUEZ, FRACC. LA SOLEDAD

PROYECTO GEOMÉTRICO SEÑALIZACIÓN HORIZONTAL

PG 02	06
JUNIO 2022	INDICADA
METROS	E-000-22


Aguascalientes
LA CIUDAD DE TU VIDA


PROYECTO GEOMÉTRICO

ESCALA 1:500

BLVD ADOLFO RUIZ CORTINEZ

TRAMO DE BLVD. JUAN PABLO I A PUENTE PIPIOLES

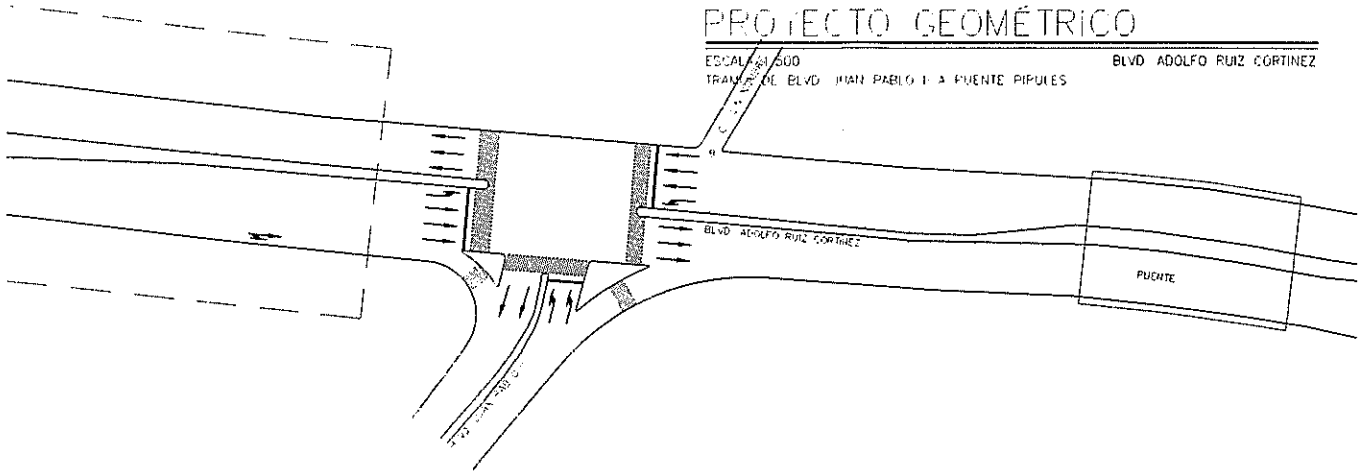

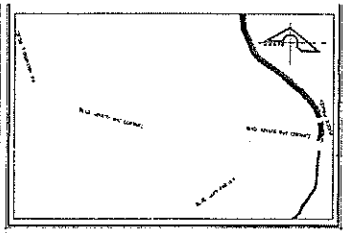

SIMBOLOGIA

SUAPENCIÓN

FLECHA DE SENTIDO N-11.1

LINEAS AMARILLAS DE CRUCE PEATONAL M-7.1

LINEA DE ALTO M-6

POZO DE VISITA

CAJA DE VALVULAS (TIPO 2)

RAMPA DISCAPACITADOS

VIALETA STANDARD (S-200)

VIALETA SOLAR

CAIMÁN

REGISTRO GAS NATURAL

BOTA HIDRÁULICA

REVELACIÓN DE POZOS DE VISITA

CONSTRUCCIÓN DE LOSA DIAMANTE A BASE DE CONCRETO PREMEZCLADO MR=45 KG/CM2, T.M.A ¾" (19 MM), GRAVA TRITURADA, PEVENIMENTO DE 8A=2.5 CM. RESISTENCIA RAPIDA A 3 DIAS, DE 25 CM. DE ESPESOR. SECCIÓN DE 1.50 X 1.50 M.

REVELACIÓN DE CAJA DE VALVULAS (TIPO)

REVELACIÓN DE PASANTE (PARTE SUPERIOR), DIMENCIONES SEGÚN EL TIPO DE CAJA DE VALVULAS, RETIRO SIN RECUPERACIÓN DE TAPA DE POZO EXISTENTE, LOSA DE CONCRETO F'C=250 KG/CM2, T.M.A 19 MM DE 15 CMS DE ESPESOR, ARMADA CON VRS No.3@15 CM EN AMBOS SENTIDOS.

CAIMÁN

REVELACIÓN DE PASANTE (PARTE SUPERIOR), DIMENSIONES HASTA 6.00X1.50 M. Y 30 CM DE ALTURA INCLUYE DESMONTAJE, RETIRO DE REJILLA Y CONSERVACIÓN DE LA MISMA, DEMOLICIONES NECESARIAS, NIVELADO CON TABIQUE, APLANADO, ANCLAJES Y TRASLAPES EN CASTILLOS, CONCRETO F'C=250 KG/CM2.

REGISTRO GAS NATURAL

REVELACIÓN DE PASANTE (PARTE SUPERIOR), DIMENSIONES HASTA 2.50X2.40 M. Y 10 CM DE ALTURA INCLUYE TRAZO, EXCAVACIÓN, NIVELACIÓN, PREPARACIONES Y DEMOLICIONES, RETIRO CON RECUPERACIÓN DE MARCO Y TAPA METALICA, MURO DE TABIQUE, APLANADO INTERIOR, LOSA DE CONCRETO PREMEZCLADO MR=45 KG/CM2, DE 15 CM. DE ESPESOR

BOTA HIDRAULICA

REVELACIÓN DE PASANTE (PARTE SUPERIOR) LLAVE HIDRAULICA DE FOFO CORTA O LARGA DE HASTA 145 MM. DE DIÁMETRO, NIVELADO HASTA UNA ALTURA MAXIMA DE 10 CM LOSA DE CONCRETO F'C=250 KG/CM2, T.M.A 19 MM DE 15 CMS. DE ESPESOR, ARMADA CON VRS No.3 @30 CM EN AMBOS SENTIDOS.

NOTA:

VER PLANOS PG-01, PG-02 Y PG-03

M.P.P. Leonardo Montano Castro

Ing. Miguel Angel Huizar Botello

CONSTRUCTORA VALDEZ RDZ.

C. José Armando Valdez Rodriguez

M. en I.C. Luis Eduardo Cadenza López

V0 Bo DE LA DEPENDENCIA

RESP. DE PROY. EXTERNO		LOGO EXTERNO
CED. PROFESIONAL		
PROYECTÓ	REVISÓ	AUTORIZÓ

Dirección de Planeación y Proyectos de Obra — Secretaría de Obras Públicas

ARQ. MA. DOLORES HERNANDEZ DE LIRA — ARQ. ALEJANDRO JAIME LEAL

ARQ. J. JESÚS PALAFOX GONZALEZ M. en ARQ. JOSÉ LUIS JUAREZ GARCIA

OBRA COMPLEMENTARIA Y SEÑALIZACION EN BLVD. ADOLFO RUIZ CORTINEZ


BLVD. ADOLFO RUIZ CORTINEZ, ENTRE PUENTE PIPIOLES Y AV. ABELARDO L. RODRIGUEZ, FRACC. LA SOLEDAD


PROYECTO GEOMETRICO SEÑALIZACION HORIZONTAL

PG 03	07
JUNIO 2022	INDICADA
METROS	E-000-22

Aguascalientes

LA CIUDAD DE TU VIDA

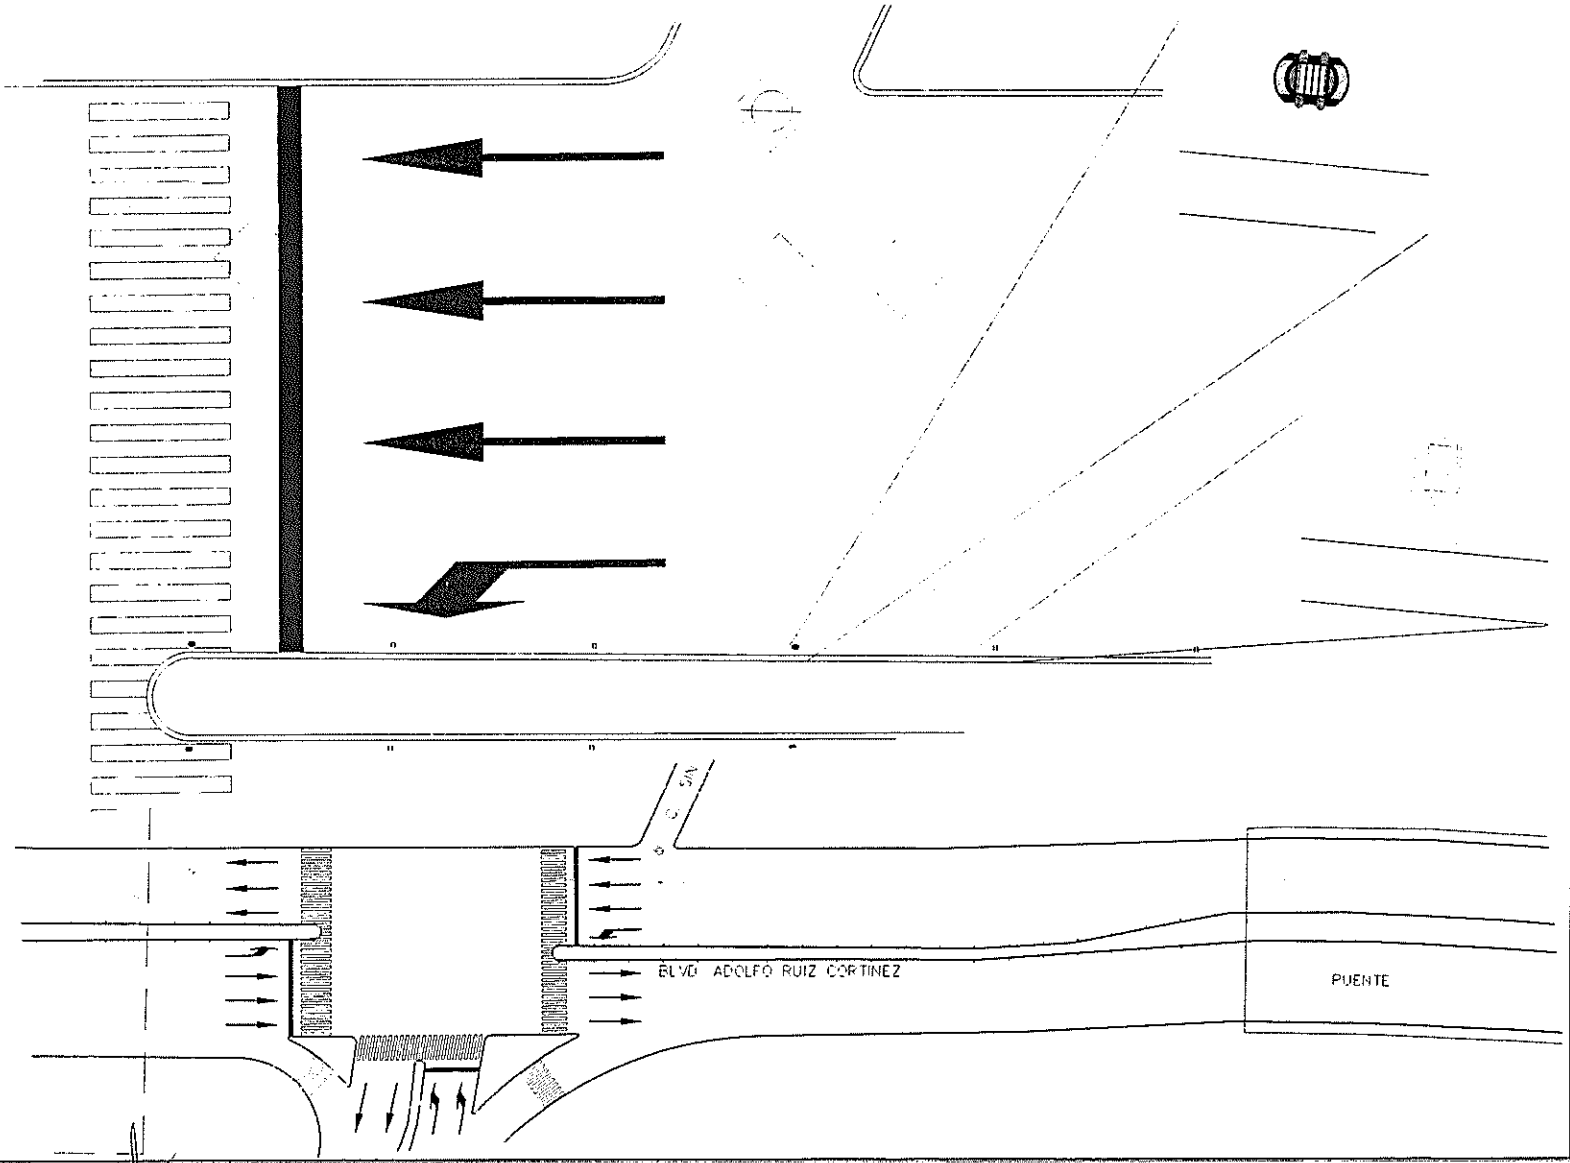

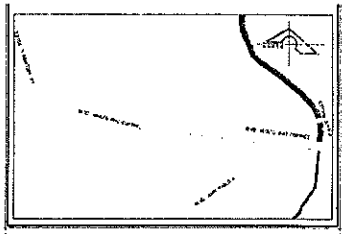

SIMBOLOGIA

- GUARNICIÓN
- FLECHA DE SENTIDO M-11.1
- LINEAS AMARILLAS DE CRUCE PEATONAL M-7.1
- LINEA DE ALTO M-6
- POZO DE VISTA
- CAJA DE VALVULAS (TIPO 2)
- RAMPA DISCAPACITADOS
- VIALETA STANDARD (S-200)
- VIALETA SOLAR
- CAIMAN
- REGISTRO GAS NATURAL
- BOTA HIDRÁULICA

NOTA 1: SE APLICARA EN TODOS LOS SEÑALAMIENTOS HORIZONTALES PINTURA PARA TRAFICO TERMOPLASTICA BASE ALQUIDALICA DE SECADO RAPIDO, QUE CUMPLA CON LAS ESPECIFICACIONES N-CMT-5-01-001/05, N-PRY-CAR-10-C-002/13 DE LA SCT APLICADAS AL DIA DE HOY, A EXCEPCION DE RAMPAS PARA DISCAPACITADOS Y GUARNICIONES, A LAS CUALES SE APLICARÁ PINTURA PARA TRÁFICO BASE SOLVENTE.

NOTA 2: DOSIFICACIÓN DE MICRO ESFERA
LA CANTIDAD DE ESFERAS DE VIDRIO EN LA PELICULA DE PINTURA EN HÚMEDO, SEGÚN SU TIPO, SERÁ LA QUE SE INDICA EN LA TABLA

CONSULTAR MANUAL DE SEÑALAMIENTO VIAL Y DISPOSITIVOS DE SEGURIDAD DE LA SCT.

M.P.P. Leonardo Montaño Castro
Ing. Miguel Angel Huizar Botello

CONSTRUCTORA VALDEZ RDZ
C. José Armando Valdez Rodriguez
M. en I.C. Luis Eduardo Cadenga López

V° B° DE LA DEPENDENCIA	RESP. DE PROY. EXTERNO		LOGO EXTERNO
	CED. PROFESIONAL		
	PROYECTÓ	REVISÓ	AUTORIZÓ

Dirección de Planeación y Proyectos de Obra — Secretaría de Obras Públicas

MTRO. MA. DOLORES HERNANDEZ DE LEAL — ARQ. ALEJANDRO JAIME LEAL

ARQ. J. JESUS PANIAGUA GONZALEZ — M. en ARQ. JOSE LUIS JIMENEZ GARCIA


OBRA COMPLEMENTARIA Y SEÑALIZACION EN BLVD. ADOLFO RUIZ CORTINEZ


BLVD. ADOLFO RUIZ CORTINEZ, ENTRE PUENTE PIRULES Y AV. ABELARDO L. RODRIGUEZ, FRACC. LA SOLEDAD


DETALLES DE TRAZO SEÑALIZACION HORIZONTAL

SEÑ 01	08
JUNIO 2022	INDICADA
METROS	E-000-22

Aguascalientes
LA CIUDAD DE TU VIDA

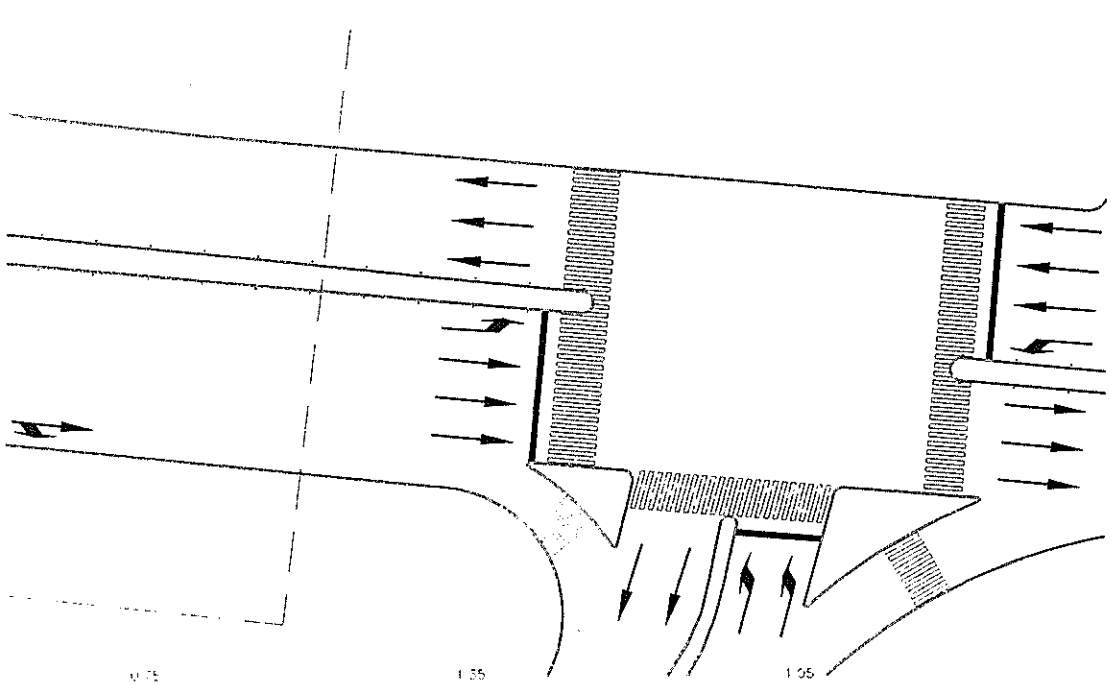

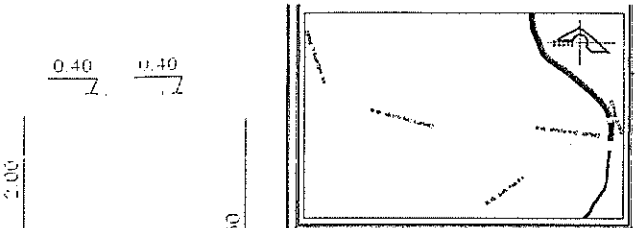

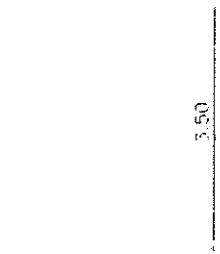


RAYA PARA CRUCE PEATONAL

SIN ESCALA — COTAS EN m

PINTURA TERMOPLASTICA EN RAYA PARA CRUCE PEATONAL EN VIAS PRIMARIAS CLASIFICACION M-7.1, COLOR AMARILLO, REFLEJANTE CON MICRO ESFERA DE VIDRIO EN PROPORCIÓN SEGÚN NORMA SCT, DE 0.40 MTS. DE ANCHO Y 3.5 MTS. DE LONGITUD POR EL ANCHO DE LA VIALIDAD, CON UNA SEPARACIÓN DE 0.40 MTS. ENTRE ELLAS.

VER PLANOS PG-01, PG-02 Y PG-03

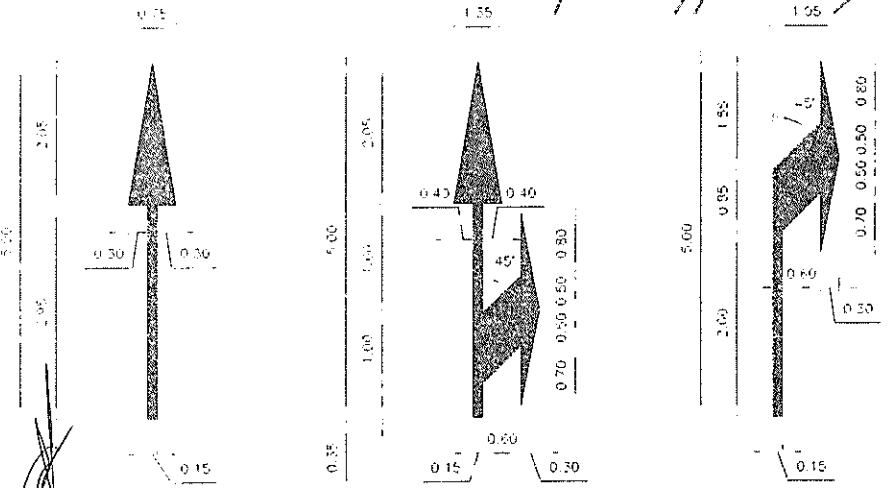

DETALLE DE FLECHA EN PAVIMENTO PARA VELOCIDADES HASTA DE 60 KM/HP

ESCALA 1:75 — COTAS EN m

PINTURA TERMOPLASTICA EN FLECHA SENCILLA DE SENTIDO DE CIRCULACIÓN, CLASIFICACIÓN M-11.1 COLOR BLANCO CON MICROESFERA SEGÚN NORMA SCT.

SIMBOLOGIA

- GUARNICIÓN
- FLECHA DE SENTIDO M-11.1
- LINEAS AMARILLAS DE CRUCE PEATONAL M-7.1
- LINEA DE ALTO M-6
- POZO DE VISITA
- CAJA DE VALVULAS (TIPO 2)
- RAMPA DISCAPACITADOS
- VIALETA STANDARD (S-300)
- VIALETA SOLAR
- CANTAN
- REGISTRO GAS NATURAL
- BOTA HIDRAULICA

NOTA 1: SE APLICARA EN TODOS LOS SEÑALAMIENTOS HORIZONTALES PINTURA PARA TRAFICO TERMOPLÁSTICA BASE ALQUIDÁLICA DE SECADO RÁPIDO, QUE CUMPLA CON LAS ESPECIFICACIONES N-CMT-5-01-001/08, N-PRY-CAP-10-01-002/13 DE LA SCT APLICADAS AL DIA DE HOY A EXCEPCIÓN DE RAMPAS PARA DISCAPACITADOS GUARNICIONES, A LAS CUALES SE APLICARA PINTURA PARA TRAFICO BASE SOLVENTE.

NOTA 2: DOSIFICACION DE MICRO ESFERA
LA CANTIDAD DE ESFERAS DE VIDRIO EN LA PELICULA DE PINTURA EN HUMEDO, SEGÚN SU TIPO, SERA LA QUE SE INDICA EN LA TABLA

CONSULTAR MANUAL DE SEÑALAMIENTO VIAL Y DISPOSITIVOS DE SEGURIDAD DE LA SCT.

M.P.P. Leonardo Montañez Castro

Ing. Miguel Angel Huizar Botello

CONSTRUCTORA VALDEZ RDZ

C. José Armando Valdez Rodríguez

M. en I.C. Luis Eduardo Cadenas López

V° B° DE LA DEPENDENCIA	

RESP. DE PROY. EXTERNO		LOGO EXTERNO
CED. PROFESIONAL		
PROYECTÓ	REVISÓ	AUTORIZÓ

Evolución de Planeación y Proyectos de Obra — Secretaría de Obras Públicas

ARQ. MA. DOLORES HERNÁNDEZ DE LIRA — ARQ. ALEJANDRO JAIME LEAL

ARQ. J. JESÚS PALAFOX GONZÁLEZ — M. en ARQ. JOSÉ LUIS JIMÉNEZ GARCÍA


OBRA COMPLEMENTARIA Y SEÑALIZACIÓN EN BLVD. ADOLFO RUIZ CORTINEZ

BLVD. ADOLFO RUIZ CORTINEZ, ENTRE PUENTE PIRULES Y AV. ABELARDO L. RODRIGUEZ, FRACC. LA SOLEDAD

DETALLES DE TRAZO SEÑALIZACIÓN HORIZONTAL

SEM 02	09
JUNIO 2022	INDICADA
METROS	E-009-22

Aguascalientes
LA CIUDAD DE TU VIDA

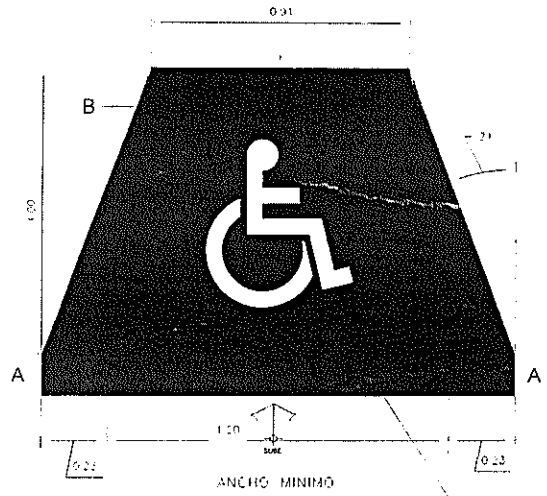

A SUMINISTRO Y APLICACION DE PINTURA EPÓXICA BASE SOLVENTE COLOR AZUL (PANTONE 294) EN RAMPAS PARA DISCAPACITADOS


B SUMINISTRO Y APLICACIÓN DE LOGOTIPO "A" (SILLA DE RUEDAS) EN PINTUPA BASE SOLVENTE COLOR BLANCO EN RAMPAS PARA DISCAPACITADOS TAMAÑO Y DISEÑO SEGÚN P L A N O S

DETALLE DE LOGOTIPO "A"

SIN ESCALA — ACOTACIÓN EN m

DETALLE DE LOGOTIPO ''A'' EN RAMPA


VISTA EN PLANTA

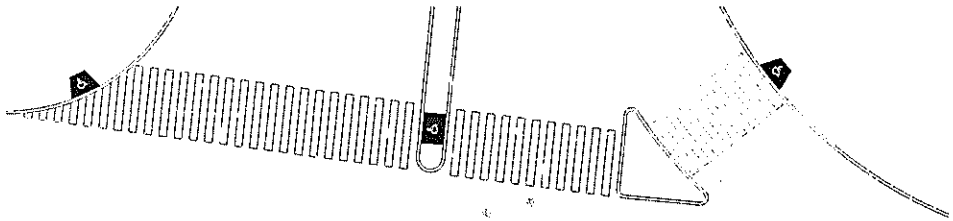



NOTA 1: SE APLICARA EN TODOS LOS SEÑALAMIENTOS HORIZONTALES PINTURA PARA TRAFICO TERMOPLASTICA BASE ALQUIDÁLICA DE SECADO RÁPIDO, QUE CUMPLA CON LAS ESPECIFICACIONES N-CMT-5-01-001/08, N-PRY-CAR-10-01-002/13 DE LA SCT APLICADAS AL DIA DE HOY, A EXCEPCION DE RAMPAS PARA DISCAPACITADOS Y GUARNICIONES, A LAS CUALES SE APLICARÁ PINTURA PARA TRÁFICO BASE SOLVENTE.

NOTA 2: DOSIFICACIÓN DE MICRO ESFERA
LA CANTIDAD DE ESFERAS DE VIDRIO EN LA PELICULA DE PINTURA EN HÚMEDO, SEGÚN SU TIPO, SERÁ LA QUE SE INDICA EN LA TABLA.

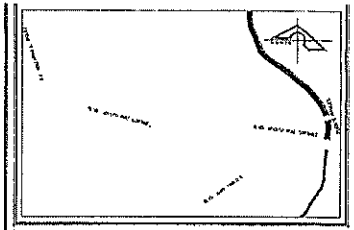

SIMBOLOGIA

GUARNICIÓN

FLECHA DE SENTIDO M-11.1

LINEAS AMARILLAS DE CRUCE PEATONAL M-7.1

LINEA DE ALTO M-6

POZO DE VISITA

CAJA DE VALVULAS (TIPO 2)

PAMPA DISCAPACITADOS

VIALETA STANDARD (S-300)

VIALETA SOLAR

CAIMÁN

REGISTRO GAS NATURAL

BOTA HIDRAULICA

CONSULTAR MANUAL DE SEÑALAMIENTO VIAL Y DISPOSITIVOS DE SEGURIDAD DE LA SCT.

M.P.F. Leonardo Montañez Castro Ing. Miguel Angel Huizar Estella	CONSTRUCTORA VALDEZ RDZ C. José Armando Valdez Rodríguez M. en I.C. Luis Eduardo Cadenas López	Vo. Bo. DE LA DEPENDENCIA	RESP. DE PROY. EXTERNO / CED. PROFESIONAL / PROYECTÓ / REVISÓ / AUTORIZÓ / LOGO EXTERNO	Dirección de Planeación y Proyectos de Obra / Secretaría de Obras Públicas ARQ. MA. DOLORES HERNÁNDEZ DE LIRA / ARQ. ALEJANDRO JAIME LEAL ARQ. J. JESÚS PARAFOX GONZÁLEZ / M. en ARQ. JOSE LUIS JIMENEZ GARCIA	OBRA COMPLEMENTARIA Y SEÑALIZACIÓN EN BLVD. ADOLFO RUIZ CORTINEZ BLVD. ADOLFO RUIZ CORTINEZ, ENTRE PUENTE PIRULES Y AV. ABELARDO L. RODRIGUEZ, FRACC. LA SOLEDAD DETALLES DE TRAZO SEÑALIZACIÓN HORIZONTAL	SEÑ 03 / 10 JUNIO 2022 / INDICADA METROS / E-000-22	Aguascalientes LA CIUDAD DE TU VIDA