Aguascalientes
LA CIUDAD DE TU VIDA

Dirección de Programación Presupuestal
Núm. Oficio AMPP/0572/22
Aguascalientes, Ags. 8 de Diciembre del 2022
Asunto: Validación de Expediente Técnico

C.P. SERGIO ARTURO LOZANO GONZÁLEZ
SECRETARIO DE FINANZAS MUNICIPALES
P R E S E N T E

Con fundamento en los artículos 17 fracción XV, 60 fracción XVI y 76 fracción VI del Reglamento del Sistema Integral de Desarrollo Municipal y del Instituto Municipal de Planeación y Evaluación de Aguascalientes, hago referencia al oficio SOPMA/2729/22 recibido por este Instituto el día 8 de Diciembre del 2022 por parte de la Secretaría de Obras Públicas Municipales, mediante el cual remiten el expediente técnico original de la siguiente obra para su análisis, registro y priorización, conforme al Programa Anual de Obra Pública y Programas Sociales para el ejercicio presupuestal 2022:

DEPENDENCIA EJECUTORA:	SECRETARÍA DE OBRAS PÚBLICAS MUNICIPALES
NOMBRE DE LA OBRA O PROYECTO:	PAVIMENTO HIDRÁULICO, ETAPA 02
UBICACIÓN:	CALLE SANTA MÓNICA, ENTRE MARCOS CORONADO Y CADENAMIENTO 0+180 Y 0+335, LOS POCITOS, AGUASCALIENTES, AGS.
FONDO DE INVERSIÓN:	PROGRAMA DIRECTO MUNICIPAL
IMPORTE:	$1,449,369.09 (ET FINAL)
No. DE OBRA:	2022-PDM-0116-UR-0101
MODALIDAD DE EJECUCIÓN:	CONTRATO
EJE:	MUNICIPIO SOBRESALIENTE
ESTRATEGIA:	OBRA PÚBLICA INTELIGENTE
POLITICA:	5.8.1.REHABILITACIÓN Y MANTENIMIENTO VIALIDADES, CAMINOS, CALLES, ÁREAS DE TERRACERÍA Y CAUCES (C

Al respecto, hago de su conocimiento que dicho expediente ha sido analizado en su integración técnica y documental, con base en el artículo 168 fracción I del Reglamento de la Ley de Obras Públicas y Servicios Relacionados para el Estado de Aguascalientes y sus Municipios.

Asimismo, le comento que este Instituto valida dicha obra acorde a lo establecido en los artículos 14, 22 párrafo segundo y 23 de la Ley de Obras Públicas y Servicios Relacionados para el Estado de Aguascalientes y sus Municipios, la cual se encuentra alineada al Plan de Desarrollo Municipal vigente, para dar cumplimiento a las metas establecidas en el mismo.

Cabe hacer mención que los recursos solicitados para este proyecto de inversión, estarán sujetos a la disponibilidad presupuestal para el presente ejercicio fiscal que determine la Secretaría a su digno cargo. Sin otro particular por el momento, le envío un cordial saludo.

A T E N T A M E N T E

ARQ. AUSTRIA GABRIELA DÁVILA DE LA LLAVE
DIRECTORA GENERAL DEL IMPLAN

CAAR / JDBC
C.c.p. I.C. ING. MIGUEL ÁNGEL HUIZAR BOTELLO .- Secretaría de Obras Públicas Municipales .Para su conocimiento.
C.c.p. Archivo.

Instituto Municipal de Planeación y Evaluación de Aguascalientes

Antonio Acevedo Escobedo 103 A. Col. Centro
Aguascalientes. Ags. C.P. 20000

(449) 9101010 Ext. 3117

www.implanags.gob.mx

GOBIERNO MUNICIPAL DE AGUASCALIENTES

INSTITUTO MUNICIPAL DE PLANEACION

IMPLAN

ANÁLISIS INTEGRAL DE EXPEDIENTE TÉCNICO

No. DE OBRA (PAOP 2020):	2022-PDM-0116-UR-0101	REGISTRO No.	289
OFICIO DE VALIDACIÓN:	AMPP/0572/22	FECHA RECIBIDO PARA REVISIÓN:	8 de Diciembre del 2022
PROGRAMA:	URBANIZACIÓN	LOCALIDAD O COLONIA:	LOS POCITOS
SUB-PROGRAMA:	Pavimentación (Const., Ampliación y Rehabilitación)	DELEGACIÓN:	Pocitos
DEPENDENCIA:	Secretaría de Obras Públicas Municipales	MOD. DE EJECUCIÓN:	CONTRATO
NOMBRE DE LA OBRA:	PAVIMENTO HIDRÁULICO, ETAPA 02, CALLE SANTA MÓNICA, ENTRE MARCOS CORONADO Y CADENAMIENTO 0+180 Y 0+335		
FUENTE DE FINANCIAMIENTO:	PROGRAMA DIRECTO MUNICIPAL, PDM		
INVERSIÓN:	$1,449,369.09	CLASIFICACIÓN DE OBRA:	BIENES DE DOMINIO PUBLICA

TOTAL	FEDERAL	ESTATAL	MUNICIPAL	BENEFICIARIOS	OTROS	DIFERENCIA ENTRE MOD.
$1,449,369.09	0.00	0.00	$1,449,369.09	0.00	0.00	*$74.598,99*

TIPO DE EXPENDIENTE:	ET FINAL	AÑO: 2022	AÑO:	AÑO:
AVANCES:	Financiero: 1 %	Físico: 1 %		
FECHA DE INICIO:	9 de Noviembre del 2022	FECHA DE TÉRMINO:	23 de Diciembre del 2022	REGISTRO SIMA: 116

CHEK LIST DE LOS ANEXOS DEL EXPEDIENTE TÉCNICO

CÉDULA DE REGISTRO DE OBRA	✓
DICTAMEN DE FACTIBILIDAD	✓
MEMORIA DESCRIPTIVA	✓
PRESUPUESTO BASE	✓
FACTIBILIDAD VERIFICADA EN CAMPO	✓
CROQUIS DE UBICACIÓN (MACRO)	✓
CROQUIS DE UBICACIÓN (MACRO)	✓
PROGRAMA DE OBRA Y MONTOS MENSUALES	✓
PLANOS O ESTUDIOS TÉCNICOS	✓
PADRÓN DE BENEFICIARIOS	N/A
ACTA DE ACEPTACIÓN DEL PROYECTO	N/A
DICTAMEN DE IMPACTO AMBIENTAL	N/A
CONVENIO DE CONCERTACIÓN	N/A
ACTA CONSTITUTIVA	N/A

METAS		BENEFICIARIOS		PERIODO DE EJECUCION		OBRA PROPUESTA		CLAVE SISCO
UNIDAD DE MEDIDA	CANT	TIPO DE BENEFICIARIOS	CANTIDAD	FECHA DE INICIO	FECHA DE TERMINO	CONCEPTO	JORNALES A GENERAR	
M2	1082.35	Personas	110	2022-11-09	2022-12-23	Pavimentación	3768	2378

INCLUIDO EN PLAN DE DESARROLLO MUNICIPAL Y EL PROGRAMA ANUAL DE OBRA PÚBLICA

OBSERVACIONES:

SIN OBSERVACIONES

RECIBIO: ING. JOSÉ DAVID BURGUETE CLAUSTRO
Analista de Programación e Inversión de Obra Pública

8 de Diciembre del 2022
Fecha de validación

8 de Diciembre del 2022
Fecha de validación Expediente

PROCEDE Si ✓ No

H. AYUNTAMIENTO CONSTITUCIONAL DEL MUNICIPIO DE AGUASCALIENTES 2021-2024

AYUNTAMIENTO DE AGUASCALIENTES

CEDULA DE REGISTRO POR OBRA

Aguascalientes

050400-001E00E05-05-2-2-1-00-1-E-0510-0-17-0116-21-1521-6144

2022-PDM-0116-UR-01-021	Obra **PAVIMENTO HIDRÁULICO, CALLE SANTA MÓNICA. ETAPA 02**
Tipo DEFINITIVO 1 2022 Folio SISCO **2378**	Ubic. TRAMO: ENTRE CADENAMIENTO 0+180 Y 0+335 (CALLE MARCOS CORONADO), LOS POCITOS Ej. , Deleg. Pocitos

Ent. Ejecutora : **050400001E00E05**

Eje: **05**	MUNICIPIO SOBRESALIENTE
Finalidad: **2**	DESARROLLO SOCIAL
Función: **2**	VIVIENDA Y SERVICIOS A LA COMUNIDAD
Subfunción: **1**	URBANIZACIÓN
Tema: **00**	SIN TEMA
Cuenta del Gasto **1**	GASTO PROGRAMABLE
Clasif. Programatica: **E**	PRESTACIÓN DE SERVICIOS PÚBLICOS
Programa: **0510**	Movilidad Urbana
SubPrograma: **0**	SUBPROGRAMA GENÉRICO
Proyecto: **17**	
Tipo de Gasto: **21**	GASTO INVERSIÓN / OBRA PÚBLICA

I N V E R S I O N 2022

Municipal	1521	EXCEDENTES PARTICIPACIONES 2022 2022	$1,449,369.09
		Folio SIMA 116 Total	$1,449,369.09

M E T A S

Unidad de Medida	Cantidad	Descripción
M2	1082.35	CONSTRUCCIÓN DE PAVIMENTO PAVIMENTO HIDRÁULICO, CALLE SANTA MÓNICA. ETAPA 02

Inversión Ejercida Total al	31 de Diciembre de 2021	$0.00
Avance Fisico Acumulado al	31 de Diciembre de 2021	
Avance Fisico Acumulado Programado al	31 de Diciembre de 2022	100 %

Fecha de Inicio 09 Nov 2022 Fecha de Terminación 23 Dic 2022

Jornales a Generar en 2022 3768

Modalidad de ejecución CONTRATO

Clasificación de la Obra Bienes de Dominio Público

Registro del Patrimonio: Obras del dominio público

OBRAS PÚBLICAS

Av. Aguascalientes Sur No. 2615
Fracc. Jardines de las Fuentes,
Aguascalientes, Ags. C.P. 20278

(449) 9 78 92 01, 06, 09

www.ags.gob.mx

GENERALES

Nombre del Proyecto : PAVIMENTO HIDRÁULICO, CALLE SANTA MÓNICA. ETAPA 02

TRAMO: ENTRE CADENAMIENTO 0+180 Y 0+335 (CALLE MARCOS CORONADO), LOS POCITOS Ej. , Deleg. Pocitos

Programa : UR URBANIZACIÓN

Subprograma : 01 PAVIMENTACIÓN (CONST., AMPLIACIÓN Y REHABILITACIÓN) (c).- Hidráulica)

Clave del Municipio : AGUASCALIENTES

Localidad :

Barrio, Colonia o Ejido : LOS POCITOS Ej.

Tipo de Obra : NUEVA

DESCRIPCIÓN DEL PROYECTO:

PAVIMENTO HIDRÁULICO, CALLE SANTA MÓNICA. ETAPA 02

PRELIMINARES 1,465.67 M2
EXCAVACIONES, ACARREOS Y TERRACERÍAS 240.00 M3
PAVIMENTO HIDRÁULICO 1,082.35 M2
OBRA COMPLEMENTARIA 1.00 OBRA
LIMPIEZAS 1,099.25 M2
SEÑALAMIENTO HORIZONTAL 1.00 OBRA
SEÑALAMIENTO VERTICAL 1.00 PZA

Beneficiarios (No. y Tipo) :

110	PERSONAS

OBRAS PÚBLICAS

No. Folio SISCO 2378

Los abajo firmantes, hacen constar que el presente proyecto :

PAVIMENTO HIDRÁULICO, CALLE SANTA MÓNICA. ETAPA 02

TRAMO: ENTRE CADENAMIENTO 0+180 Y 0+335 (CALLE MARCOS CORONADO), LOS POCITOS Ej. , Deleg. Pocitos

cumple con los Requisitos y Normas Técnicas establecidas por la Dependencia Normativa, por lo que es viable su ejecución. Comprometiéndose la misma a proporcionar la supervisión y asistencia técnica necesaria durante el proceso administrativo.

Por la Dependencia Ejecutora

Ing. Miguel Angel Huizar Botello
Secretario de Obras Públicas

Lic. Jaime Gallo Camacho
Secretario de Desarrollo Urbano

LUGAR :AGUASCALIENTES, AGS.

Av. Aguascalientes Sur No. 2615
Fracc. Jardines de las Fuentes,
Aguascalientes, Ags. C.P. 20278

(449) 9 78 92 01, 06, 09

www.ags.gob.mx

No. Folio SISCO 2378

H. AYUNTAMIENTO CONSTITUCIONAL DEL MUNICIPIO DE AGUASCALIENTES 2021-2024

AYUNTAMIENTO DE AGUASCALIENTES

FACTIBILIDAD VERIFICADA EN CAMPO

Aguascalientes LA CIUDAD DE TU VIDA

MUNICIPIO: AGUASCALIENTES

LOCALIZACION: TRAMO: ENTRE CADENAMIENTO 0+180 Y 0+335 (CALLE MARCOS CORONADO), LOS POCITOS Ej. , Deleg. Pocitos

PROGRAMA: URBANIZACIÓN

SUBPROGRAMA: PAVIMENTACIÓN (CONST., AMPLIACIÓN Y REHABILITACIÓN) (c).- Hidráulica)

OBRA A REALIZAR: PAVIMENTO HIDRÁULICO, CALLE SANTA MÓNICA. ETAPA 02

DEPENDENCIA EJECUTORA: SECRETARÍA DE OBRAS PUBLICAS DEL MUNICIPIO DE AGUASCALIENTES

FORMA DE EJECUCION: CONTRATO

TIPO DE OBRA PROPUESTA: NUEVA

CONDICIONES ACTUALES DE LA OBRA:

PAVIMENTO HIDRÁULICO, CALLE SANTA MÓNICA. ETAPA 02

CARACTERISTICAS DE LA OBRA: Bueno

FACTIBILIDAD DE LA OBRA:

ESTA OBRA SE REQUIERE PARA EL BENEFICIO DE LA CIUDADANÍA

PROCEDE: SI [X] NO [ ]

REVISÓ: Jefa del Departamento de Expedientes Tecnicos y Costos

NOMBRE: Arq. Blanca Margarita Martinez Amador

FIRMA:

FECHA: 28 Nov 2022

SECRETARIA DE OBRAS PÚBLICAS

Av. Aguascalientes Sur No. 2615
Fracc. Jardines de las Fuentes,
Aguascalientes, Ags. C.P. 20278

(449) 9 78 92 01, 06, 09

www.ags.gob.mx


No. Folio SISCO 2378

H. AYUNTAMIENTO CONSTITUCIONAL DEL MUNICIPIO DE AGUASCALIENTES 2021-2024

H. AYUNTAMIENTO DE AGUASCALIENTES
SECRETARÍA DE OBRAS PÚBLICAS
DIRECCIÓN DE SUPERVISIÓN DE OBRA
LOCALIZACION

Aguascalientes
LA CIUDAD ES TU VIDA

OBRA:	PAVIMENTO HIDRÁULICO, CALLE SANTA MÓNICA. ETAPA 02, TRAMO: ENTRE CADENAMIENTO 0+180 Y 0+335 (CALLE MARCOS CORONADO), LOS POCITOS Ej.					
NO. DE CONTR	DM-0116-2022		CONTRATISTA:	GRUPO ARO INGENIUM, S.A. DE C.V.		

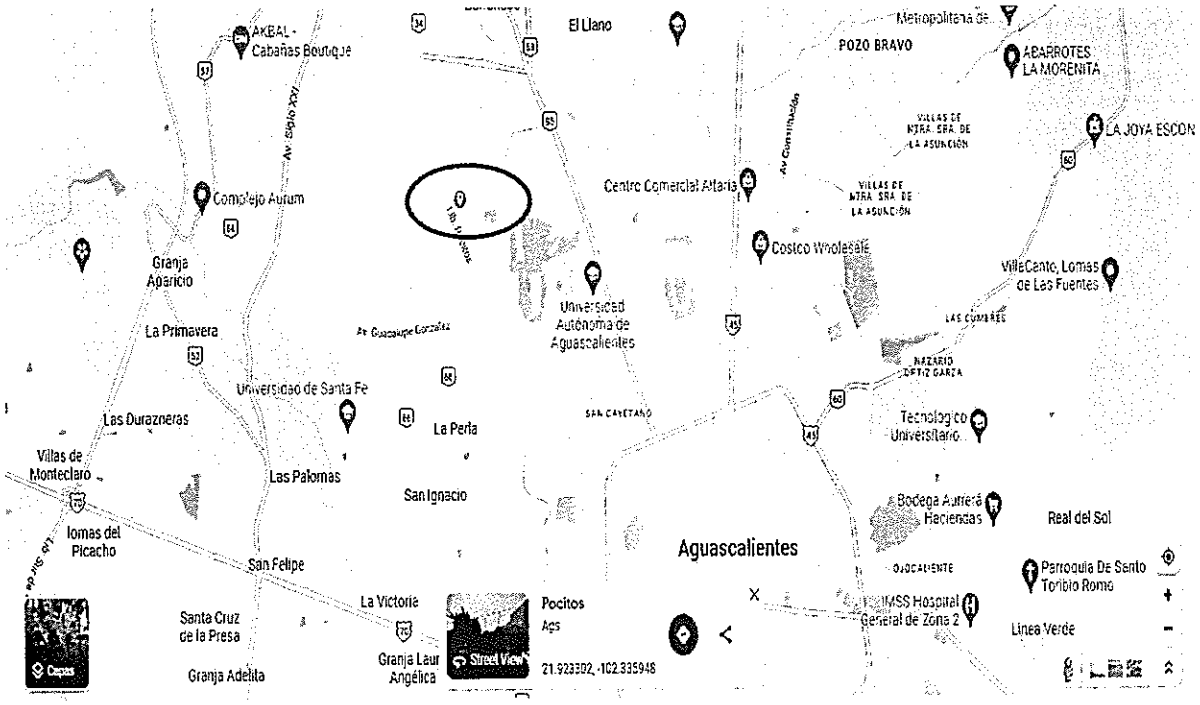


ING. IVAN ALEJANDRO RUIZ ESPARZA SOLIS
SUPERVISOR DE OBRA.

H. AYUNTAMIENTO CONSTITUCIONAL DEL MUNICIPIO DE AGUASCALIENTES 2021-2024

H. AYUNTAMIENTO DE AGUASCALIENTES
SECRETARÍA DE OBRAS PÚBLICAS
DIRECCIÓN DE SUPERVISIÓN DE OBRA
LOCALIZACION

Aguascalientes
LA CIUDAD DE TU VIDA

OBRA:	PAVIMENTO HIDRÁULICO, CALLE SANTA MÓNICA. ETAPA 02, TRAMO: ENTRE CADENAMIENTO 0+180 Y 0+335 (CALLE MARCOS CORONADO), LOS POCITOS EJ.					
NO. DE CONTR	DM-0116-2022		CONTRATISTA:	GRUPO ARO INGENIUM, S.A. DE C.V.		

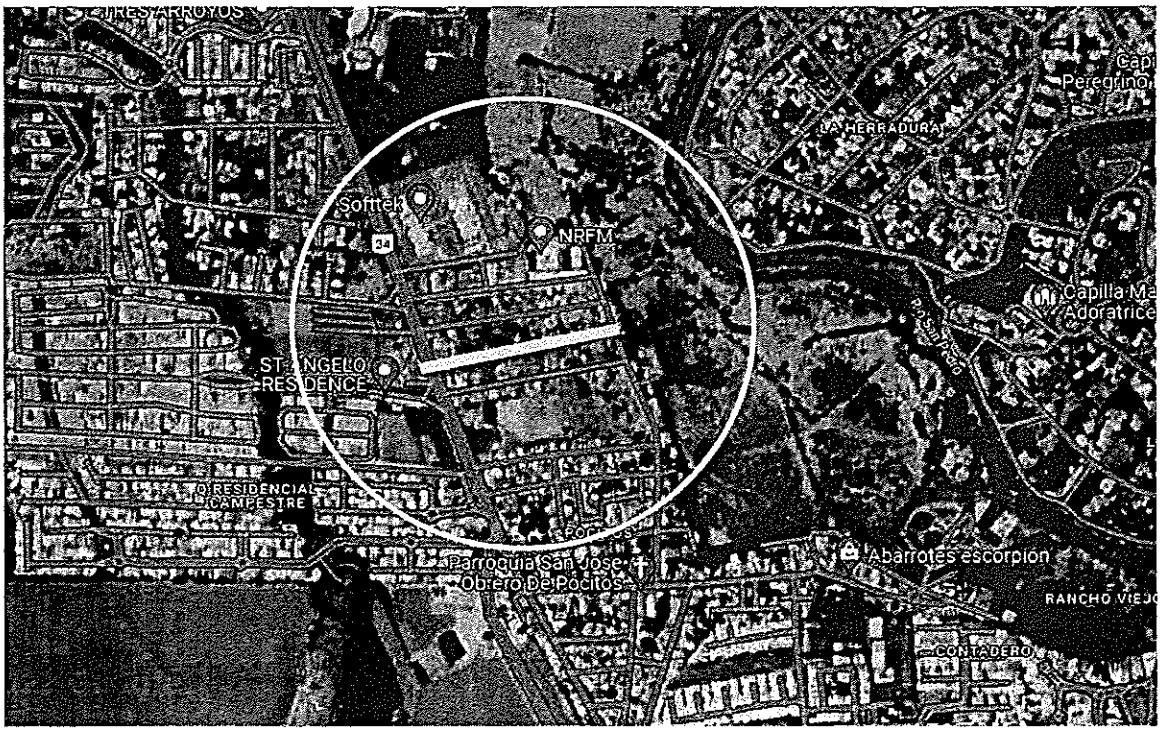

ING. IVAN ALEJANDRO RUIZ ESPARZA SOLIS
SUPERVISOR DE OBRA.

R03-POS-SOS-7.5.1-04	
REVISION:	04
FECHA DE RETENCION: RESPONSABLE:	SUPERVISOR DE OBRA
TIEMPO DE RET:	03 AÑOS

PROGRAMA DE OBRA DEFINITIVO

Aguascalientes
LA CIUDAD DE TU VIDA

No. DE CONTRATO : DM-0116-2022

PROGRAMA: UR URBANIZACIÓN

No. OBRA Y NOMBRE DE LA OBRA: PAVIMENTO HIDRAULICO, CALLE SANTA MÓNICA. ETAPA 02, TRAMO: ENTRE CADENAMIENTO 0+180 Y 0+335 (CALLE MARCOS CORONADO), LOS POCITOS EJ.

INICIO VIGENTE: 09-noviembre-22

TERMINO REAL: 23-diciembre-22

RECURSO 2022

CONCEPTO			1	2	3	4	5	6	7	8	9	10	11	12	13	14	15	16	PONDERACIÓN %	
			2022																	
			OCTUBRE	NOVIEMBRE	DICIEMBRE	ENERO	FEBRERO	MARZO	ABRIL	MAYO	JUNIO	JULIO	AGOSTO	SEPTIEMBRE	OCTUBRE	NOVIEMBRE	DICIEMBRE	ENERO	FINANCIERO $	FÍSICO %
DESCRIPCION	INVERSION																20	6		
PAVIMENTO HIDRAULICO, CALLE SANTA MÓNICA. ETAPA 02, TRAMO: ENTRE CADENAMIENTO 0+180 Y 0+335 (CALLE MARCOS CORONADO), LOS POCITOS EJ.																				
TRAMO: ENTRE CADENAMIENTO 0+180 Y 0+335 (CALLE MARCOS CORONADO), LOS POCITOS EJ.																				
PAVIMENTO HIDRAULICO	$ 1,185,035.45	100														20 40 20 20			94.84	44.44
LIMPIEZAS	$ 11,256.32	100															70 10	20	0.90	33.33
SEÑALIZACION	$ 53,164.34	100															50 10		4.25	22.22
																			0.00	0.00
		-																		
		-																		
		-																		
		-																		
		-																		
SUBTOTAL SIN IVA	$ 1,249,456.10		0 0 0 0	0 0 0 0	0 0 0 0	0 0 0 0	0 0 0 0	0 0 0 0	0 0 0 0	0 0 0 0	0 0 0 0	0 0 0 0	0 0 0 0	0 0 0 0	0 0 0 0	1 1 1 2	1 1 1 1	0 0 0 0		
AVANCE SEMANAL %			0% 0% 0% 0%	0% 0% 0% 0%	0% 0% 0% 0%	0% 0% 0% 0%	0% 0% 0% 0%	0% 0% 0% 0%	0% 0% 0% 0%	0% 0% 0% 0%	0% 0% 0% 0%	0% 0% 0% 0%	0% 0% 0% 0%	0% 0% 0% 0%	0% 0% 0% 0%	0% 0% 0% 0%	11% 11% 11% 22%	11% 11% 11% 11%	5% 2% 5% 5%		
AVANCE SEMANAL ACUMULADO %			0% 0% 0% 0%	0% 0% 0% 0%	0% 0% 0% 0%	0% 0% 0% 0%	0% 0% 0% 0%	0% 0% 0% 0%	0% 0% 0% 0%	0% 0% 0% 0%	0% 0% 0% 0%	0% 0% 0% 0%	0% 0% 0% 0%	0% 0% 0% 0%	0% 0% 0% 0%	0% 0% 0% 0%	11% 22% 33% 56%	67% 78% 89% 100%	105% 107% 112% 117%	100.00	100.00
EJERCIDO SEMANAL $			- - - -	- - - -	- - - -	- - - -	- - - -	- - - -	- - - -	- - - -	- - - -	- - - -	- - - -	- - - -	- - - -	237,007.09 474,454.18 237,007.09 244,596.51	1,125.63 47,847.81 5,318.43 2,251.26	- - - -	$ 1,249,456.10	
EJERCIDO MENSUAL $			$0.00	$0.00	$0.00	$0.00	$0.00	$0.00	$0.00	$0.00	$0.00	$0.00	$0.00	$0.00	$0.00	$1,192,914.97	$56,541.24	$0.00	$ 199,912.98	IVA 16%
EJERCIDO MENSUAL ACUMULADO $			0.00	0.00	0.00	0.00	0.00	0.00	0.00	0.00	0.00	0.00	0.00	0.00	0.00	1,192,914.97	1,249,456.11	1,249,456.11		
EJERCIDO SEMANAL %			0% 0% 0% 0%	0% 0% 0% 0%	0% 0% 0% 0%	0% 0% 0% 0%	0% 0% 0% 0%	0% 0% 0% 0%	0% 0% 0% 0%	0% 0% 0% 0%	0% 0% 0% 0%	0% 0% 0% 0%	0% 0% 0% 0%	0% 0% 0% 0%	0% 0% 0% 0%	19% 38% 19% 20%	1% 4% 0% 0%	0% 0% 0% 0%		
EJERCIDO MENSUAL %			0%	0%	0%	0%	0%	0%	0%	0%	0%	0%	0%	0%	0%	95%	5%	0%	GRAN TOTAL EJERCIDO	
EJERCIDO MENSUAL ACUMULADO %			0%	0%	0%	0%	0%	0%	0%	0%	0%	0%	0%	0%	0%	95%	100%	100%	$	1,449,369.09

PRE

ING. IVAN ALEJANDRO RUIZ ZARATE SOLIS
SUPERVISOR

PRESIDENCIA MUNICIPAL DE AGUASCALIENTES

FACTIBILIDAD VERIFICADA EN CAMPO

GENERALES

EJERCICIO: 2022 APROBACION No: 2022-PDM-0116-UR-01-021
LOCALIDAD: TRAMO: ENTRE CADENAMIENTO 0+180 Y 0+335 (CALLE MARCOS CORONADO), LOS POCITOS Ej.
MUNICIPIO: AGUASCALIENTES, Mpio.
TIPO DE INVERSION: EXCEDENTES PARTICIPACIONES (100%) (MUNICIPAL)
PROGRAMA: UR URBANIZACIÓN
SUB-PROGRAMA: 01 PAVIMENTACIÓN (CONST., AMPLIACIÓN Y REHABILITACIÓN) Inciso c) .Hidráulica
OBRA A REALIZARSE: PAVIMENTO HIDRÁULICO, CALLE SANTA MÓNICA. ETAPA 02, TRAMO: ENTRE CADENAMIENTO 0+180 Y 0+335 (CALLE MARCOS CORONADO), LOS POCITOS Ej.

DEPENDENCIA EJECUTORA: SECRETARÍA DE OBRAS PÚBLICAS MUNICIPALES (S.O.P.M.A)
FORMACIÓN DE EJECUCION: CONTRATO NO. DE CONTRATO: DM-0116-2022
NOMBRE CONTRATISTA: GRUPO ARO INGENIUM, S.A. DE C.V.
REPRESENTANTE: I.C. GERARDO ALEJANDRO ROSALES GUTIERREZ
MONTO CONT. ORIGEN $ 1,449,369.09 ANTICIPO: $ 624,728.06 PLAZO 45 DIAS
1A AMPLIACION $: $ - 1 AMPL DIAS
2A AMPLIACION $: 2 AMPL DIAS
FIRMA CONTRATO: 04/11/2022
INICIO CONT: dd/mm/aa 05/11/2022 TERMINO CONT: 19/12/2022
INICIO REAL: dd/mm/aa 09/11/2022 TERMINO REAL: 23/12/2022

TIPO DE OBRA PROPUESTA

NUEVA CREACIÓN	X	CONSOLIDACIÓN	
COMPLEMENTARIA		AMPLIACIÓN	
REHABILITACIÓN		EQUIPAMIENTO	

CARACTERÍSTICAS DE LA OBRA:

FORMACION Y COMPACTACION DE SUB-RASANTE, SUB-BASE Y BASE HIDRAULICA
PAVIMENTO HIDRAULICO A BASE CONCRETO PREMEZCLADO MR=38 KG/CM2
SEÑALAMIENTO HORIZONTAL
SEÑALAMIENTO VERTICAL

CONDICIONES ACTUALES DE LA OBRA: (SELECCIONAR UNO OBLIGATORIO)

BUEN ESTADO X REGULAR PESIMO ESTADO

FACTIBILIDAD DE LA OBRA: (CONDICIONES ACTUALES DE LA OBRA)

ESTA OBRA SE ENCUENTRA EN CONDICIONES PARA OPERARSE

PROCEDE: SI: X NO:
MARQUE SOLO UNA

ING. IVAN ALEJANDRO RUIZ ESPARZA SOLIS
SUPERVISOR

PRESIDENCIA MUNICIPAL DE AGUASCALIENTES

FACTIBILIDAD VERIFICADA EN CAMPO

GENERALES

LOCALIDAD: TRAMO: ENTRE CADENAMIENTO 0+180 Y 0+335 (CALLE MARCOS CORONADO), LOS POCITOS Ej.
MUNICIPIO: AGUASCALIENTES, Mpio.
PROGRAMA: UR URBANIZACIÓN
SUB-PROGRAMA: 01 PAVIMENTACIÓN (CONST., AMPLIACIÓN Y REHABILITACIÓN) Inciso c) .Hidráulica
OBRA A REALIZARSE: PAVIMENTO HIDRÁULICO, CALLE SANTA MÓNICA. ETAPA 02, TRAMO: ENTRE CADENAMIENTO 0+180 Y 0+335 (CALLE MARCOS CORONADO), LOS POCITOS Ej.

DEPENDENCIA EJECUTORA: SECRETARÍA DE OBRAS PÚBLICAS MUNICIPALES (S.O.P.M.A)
FORMACIÓN DE EJECUCION: CONTRATO

TIPO DE OBRA PROPUESTA

NUEVA CREACIÓN	X	CONSOLIDACIÓN	
COMPLEMENTARIA		AMPLIACIÓN	
REHABILITACIÓN		EQUIPAMIENTO	

CARACTERÍSTICAS DE LA OBRA:

FORMACION Y COMPACTACION DE SUB-RASANTE, SUB-BASE Y BASE HIDRAULICA
PAVIMENTO HIDRAULICO A BASE CONCRETO PREMEZCLADO MR=38 KG/CM2
SEÑALAMIENTO HORIZONTAL
SEÑALAMIENTO VERTICAL

CONDICIONES ACTUALES DE LA OBRA:

BUEN ESTADO:	REGULAR:	PESIMO ESTADO:
X		

FACTIBILIDAD DE LA OBRA:

ESTA OBRA SE ENCUENTRA EN CONDICIONES PARA OPERARSE

PROCEDE **SI:** X **NO:**

ING. IVAN ALEJANDRO RUIZ ESPARZA SOLIS
SUPERVISOR

PRESUPUESTO MODIFICADO

Obra: **PAVIMENTO HIDRÁULICO, CALLE SANTA MÓNICA. ETAPA 02**

Ubicación: **TRAMO: ENTRE CADENAMIENTO 0+180 Y 0+335 (CALLE MARCOS CORONADO), LOS POCITOS Ej.**

Contratista: **GRUPO ARO INGENIUM, S.A. DE C.V. (367)**

No.	Concepto	Unidad	Cantidad	Precio Unitario	Importe Total
	GRUPO: **PAVIMENTO HIDRAULICO**				
	PARTIDA: **PRELIMINARES**				
1	LIMPIA, TRAZO Y NIVELACION EN PAVIMENTOS, CALLES Y VIALIDADES CON EQUIPO TOPOGRAFICO, INCLUYE: EJES, BANCO DE NIVEL, RENIVELACIONES LAS VECES NECESARIAS, CORRECCION DE RASANTE A PUNTOS OBLIGADOS (AUTORIZADOS POR LA SUPERVISION), ESTACAS, VARILLAS, MANO DE OBRA CALIFICADA, HERRAMIENTA NECESARIA, EQUIPO DE PRECISION CALIBRADO, TRABAJO TERMINADO.P.U.O.T.	M2	1465.67	$10.36	$15,184.34
			Totales por Partida		**$15,184.34**
	PARTIDA: **EXCAVACIONES, ACARREOS Y TERRACERIAS**				
2	EXCAVACION EN CORTE CON MAQUINA HASTA UNA PROFUNDIDAD DE 75 CM, EN MATERIAL TIPO II, INCLUYE: AFLOJE Y EXTRACCION DE MATERIAL, ACARREOS AL LUGAR DE ACOPIO PARA SU CARGA Y ACARREO FUERA DE LA OBRA, VOLUMEN MEDIDO COMPACTO.	M3	916	$24.61	$22,542.76
3	COMPACTACION DE TERRENO NATURAL AL 90% DE SU P.V.S.M EN SU COMPACTACION., INCLUYE ESCARIFICADO, TENDIDO, HOMOGENIZADO, HUMEDECIDO OPTIMO NIVELADO Y COMPACTADO EN CAPAS DE 20 CM, CALIDAD Limite liquido máximo 50%, Valor de Soporte California (CBR) mínimo 15%, Expansión máxima 5%, Grado de Compactación mínimo 90% ± 2, Y TODO LO NECESARIO PARA SU CORRECTA EJECUCION,	M2	1219	$79.29	$96,654.51
4	FORMACION Y COMPACTACION DE SUB-RRASANTE, CON EL USO DE EQUIPO MAYOR, HASTA ALCANZAR EL 100% AASHTO MODIFICADA. EN CAPAS DE 20 CM MAXIMO, INCLUYE: SUMINISTRO DE MATERIAL DE BANCO QUE CUMPLA CON LA NORMA, HUMEDAD OPTIMA Y TODO LO NECESARIO PARA SU CORRECTA COLOCACION, EL MATERIAL DEBERA CUMPLIR CON UN C.B.R. DEL 60% PARA LO CUAL EL CONTRATISTA DEBERA PROPONER UN BANCO DE MATERIAL Y UN FRENTE, DEBERA PRESENTAR EL ESTUDIO DE CALIDAD QUE AVALE EL CUMPLIMIENTO AL 100 % DE LA NORMA Y DEMAS CARACTERISTICAS SOLICITADAS, P.U.O.T.	M3	240	$309.12	$74,188.80
5	FORMACION Y COMPACTACION DE SUB-BASE PARA MAS DE UN MILLON DE EJES EQUIVALENTES, CON EL USO DE EQUIPO MAYOR, HASTA ALCANZAR EL 100% AASHTO MODIFICADA. EN CAPAS DE 20 CM MAXIMO, INCLUYE: SUMINISTRO DE MATERIAL DE BANCO QUE CUMPLA CON LA NORMA, HUMEDAD OPTIMA Y TODO LO NECESARIO PARA SU CORRECTA COLOCACION, EL MATERIAL DEBERA CUMPLIR CON UN C.B.R. DEL 60% PARA LO CUAL EL CONTRATISTA DEBERA PROPONER UN BANCO DE MATERIAL Y UN FRENTE, DEBERA PRESENTAR EL ESTUDIO DE CALIDAD QUE AVALE EL CUMPLIMIENTO AL 100 % DE LA NORMA N-CMT-4-02-001. Y DEMAS CARACTERISTICAS SOLICITADAS, P.U.O.T.	M3	240	$311.96	$74,870.40
6	FORMACION Y COMPACTACION DE BASE HIDRAULICA PARA MAS DE UN MILLON DE EJES EQUIVALENTES DE 20 CMS. DE ESPESOR, PARA CARPETA DE CONCRETO HIDRAULICO, CON MATERIAL 100% TRITURADO (SOLAMENTE) 1 1/2" A FINOS QUE CUMPLA CON LA NORMA COMPACTADA AL 100 % DE PRUEBA AASHTO. COMBINANDO COMPACTADOR DE RODILLO EN BAJA Y MUERTO Y LLANTEO CON EQUIPO PESADO (CAMION DE VOLTEO CARGADO AL MAXIMO), INCLUYE HOMOGENEIZADO, TENDIDO, COMPACTADO, E INCORPORACION DE AGUA HASTA ALCANZAR LA HUMEDAD OPTIMA Y NIVELACIONES,	M3	240	$913.62	$219,268.80
7	CARGA MECANICA Y ACARREO DE MATERIAL PRODUCTO DE EXCAVACION Y DEMOLICION EN CAMION DE VOLTEO AL 1er. KM, VOLUMEN MEDIDO COMPACTO.	M3	923	$33.88	$31,271.24
8	ACARREO DE MATERIAL PRODUCTO DE EXCAVACION Y/O DEMOLICION EN CAMION DE VOLTEO A KILOMETROS SUBSECUENTES, AL TIRADERO OFICIAL AUTORIZADO MAS CERCANO AUTORIZADO POR LA SUPERVISION, VOLUMEN MEDIDO COMPACTO.	M3-KM	3692	$9.22	$34,040.24
			Totales por Partida		**$552,836.75**

Obra: **PAVIMENTO HIDRÁULICO, CALLE SANTA MÓNICA. ETAPA 02**

Ubicación: **TRAMO: ENTRE CADENAMIENTO 0+180 Y 0+335 (CALLE MARCOS CORONADO), LOS POCITOS Ej.**

Contratista: **GRUPO ARO INGENIUM, S.A. DE C.V. (367)**

No.	Concepto	Unidad	Cantidad	Precio Unitario	Importe Total
	GRUPO: **PAVIMENTO HIDRAULICO**				
	PARTIDA: **PAVIMENTO HIDRAULICO**				
9	CONSTRUCCION DE PAVIMENTO HIDRAULICO A BASE DE CONCRETO PREMEZCLADO MR=38 KG/CM2 TMA 1 1/2" GRAVA TRITURADA, REVENIMIENTO DE 6 A 8 CM FRAGUADO NORMAL DE 15 CM DE ESPESOR MODULADO EN LOSAS DE 3.5 MTS. (ANCHO) X 3.5 MTS (LARGO) COMO MAXIMO, CON CORTES EN LAS LOSAS DE 1/3 DEL ESPESOR DE LA LOSA (5 CM) Y SELLADO CON COLA DE RATA Y MATERIAL ELASTOMERICO Y TIRA PREFORMADA (FOAMTECH DE 1/2X15) EN JUNTAS Y CORTES LONGITUDINALES Y TRANSVERSALES, ASI COMO EL APROCHE CON GUARNICION Y DENTELLON. INCLUYE: CIMBRADO, COLADO, VIBRADO CON INMERSION Y REGLA VIBRATORIA, DESCIMBRADO, REGLEADO FINAL, ACABADO CEPILLO DE ALUMINIO Y CON DOBLADOR, CALAFATEO, CURADO CON MEMBRANA BASE AGUA Y TODO LO NECESARIO PARA SU CORRECTA COLOCACION, P.U.O.T.	M2	1082.34667	$498.83	$539,906.99
10	SUMINISTRO Y COLOCACION DE RELLENO PARA JUNTAS DE EXPANSION A BASE DE ESPUMA DE POLIETILENO DE CELDAS CERRADAS (FOAMTECH) DE 1/2" DE ESPESOR Y 15 CM DE ALTURA DE ACUERDO AL DISEÑO ANEXO EN PLANOS, INCLUYE: MATERIAL, SELLADOR AUTONIVELANTE,MANO DE OBRA, CORTES, AJUSTES, DESPERDICIOS, ACARREO, FLETES DENTRO Y FUERA DE LA OBRA DE ACUERDO A ESPECIFICACIONES DE CONTROL DE CALIDAD (LA FICHA TECNICA DEL FABRICANTE DEBERA CUMPLIR CON LAS ESPECIFICACIONES DE LA NORMA)	ML	244.28	$93.95	$22,950.11
				Totales por Partida	**$562,857.09**
	PARTIDA: **OBRA COMPLEMENTARIA**				
11	RENIVELACION DE POZO DE VISITA HASTA 0.30 m DE ALTURA. INCLUYE: RETIRO SIN RECUPERACION DE BROCAL EXISTENTE, NIVELADO CON TABIQUE ROJO RECOCIDO 7X14X28, ASENTADO CON MORTERO CEMENTO-ARENA 1:3 DE 28 cm DE ESPESOR, APLANADO CON MORTERO CEMENTO-ARENA 1:3, PLOMEADO, NIVELADO, DEMOLICIONES, CARGAS Y ACARREOS DENTRO DE LA OBRA, LIMPIEZAS	PZA	2	$3,468.79	$6,937.58
12	CONSTRUCCION DE LOSA DE DIAMANTE DE CONCRETO MR= 45 , T.M.A. DE 3/4" (19MM), GRAVA TRITURADA, REVENIMIENTO DE 8+-2.5CM CM, FRAGUADO RAPIDOA A 3 DIAS, DE 25 CM DE ESPESOR, EN POZO DE VISITA, Y 1.50 M POR LADO, INCLUYE: SUMINISTRO DE MATERIALES, ESPUMA DE POLIURETANO DE ALTA DENSIDAD EN TODO EL PERIMETRO EXTERIOR DE 1/2" ASI COMO DE LAS JUNTAS DIAGONALES PARA FORMAR 4 PARTES, BROCAL Y TAPA DE Fo. Fo. TIPO PESADO, (165 KG), CIMBRADO, COLADO, VIBRADO, DESCIMBRADO, CURADO CON MEMBRANA QUIMICA BASE AGUA, APLANADO FINO EN RECEPCION DE BROCAL, CORTES CON CORTADORA DE DISCO DE 5 CM ENTRE JUNTAS DIAGONALES FORMADO 8 PIEZAS Y SELLADO DE JUNTAS Y CORTES CON MATERIAL PREFORMADO Y SELLADOR AUTONIVELANTE, MANO DE OBRA, ACARREOS DE MATERIAL DENTRO Y FUERA DE LA OBRA, TRABAJO TERMINADO. P.U.O.T.	PZA	2	$9,990.55	$19,981.10
13	LIMPIEZA Y DESASOLVE DE POZOS DE VISITA Y LINEAS DE ALCANTARILLADO EXISTENTE CON CAMION TIPO VACTOR. INCLUYE: RESANE INTERIOR DEL POZO Y REMTE DE POZO CO TUBO CON SELLADOR, FESTER Y MORTERO 1:3, MANO DE OBRA, SUMINISTRO DE AGUA EN PIPA, HERRAMIENTAS Y EQUIPO PARA SU CORRECTA EJECUCION, LIMPIEZAS, RENTA DE CAMION VACTOR HASTA LA CORRECTA LIMPIEZA DE LAS LINEAS EXISTENTES DE POZO A POZO, ASI COMO EL TRASLADO DE LOS DESECHOS HASTA TIRADERO AUTORIZADO MEDIDO POZO A POZO.	LOTE	2	$13,619.29	$27,238.58
				Totales por Partida	**$54,157.26**
				Totales por Grupo	**$1,185,035.45**

Obra: **PAVIMENTO HIDRÁULICO, CALLE SANTA MÓNICA. ETAPA 02**

Ubicación: **TRAMO: ENTRE CADENAMIENTO 0+180 Y 0+335 (CALLE MARCOS CORONADO), LOS POCITOS Ej.**

Contratista: **GRUPO ARO INGENIUM, S.A. DE C.V. (367)**

No.	Concepto	Unidad	Cantidad	Precio Unitario	Importe Total
	GRUPO: **LIMPIEZAS**				
	PARTIDA: **LIMPIEZAS**				
14	LIMPIEZA GENERAL Y A DETALLE DE LA OBRA, INCLUYE: BARRIDO Y ACARREOS DE ESCOMBROS, RETIRO FUERA DE LA OBRA DEL MISMO, DESVIO VEHICULAR, SEÑALETICA, A MANO Y A MAQUINA.	M2	1099.25	$10.24	$11,256.32
			Totales por Partida		**$11,256.32**
			Totales por Grupo		**$11,256.32**

Obra: **PAVIMENTO HIDRÁULICO, CALLE SANTA MÓNICA. ETAPA 02**

Ubicación: **TRAMO: ENTRE CADENAMIENTO 0+180 Y 0+335 (CALLE MARCOS CORONADO), LOS POCITOS Ej.**

Contratista: **GRUPO ARO INGENIUM, S.A. DE C.V. (367)**

No.	Concepto	Unidad	Cantidad	Precio Unitario	Importe Total
	GRUPO: **SEÑALIZACION**				
	PARTIDA: **SEÑALAMIENTO HORIZONTAL**				
15	SUMINISTRO Y APLICACIÓN DE PINTURA BASE SOLVENTE " EN RAYA DE ALTO CLASIFICACIÓN M - 6, PARA INDICAR ALTO EN CRUCEROS, COLOR BLANCO, REFLEJANTE CON MICRO ESFERA DE VIDRIO EN PROPORCIÓN SEGÚN NORMA SCT DE 0.60 MTS DE ANCHO DE LONGITUD VARIABLE, INCLUYE: MATERIALES Y ESPECIFICACIONES QUE CUMPLAN CON LA NORMATIVA N-CMT-5-01-001/05, N-PRY-CAR-10-01-002/13 APLICADAS AL DIA DE HOY, MATERIAL, TRAZO, ENMASCARILLADO, MANO DE OBRA, LIMPIEZA PREVIA DE SUPERFICIE, EQUIPO NECESARIO PARA SU EJECUCIÓN, Y TODO LO NECESARIO PARA SU CORRECTA EJECUCIÓN, TRABAJO TERMINADO.	ML	10	$56.02	$560.20
16	SUMINISTRO Y APLICACIÓN DE PINTURA BASE SOLVENTE PARA INDICAR "CRUCE PEATONAL EN CAJON DE ESTACIONAMIENTO PARA PERSONAS CON DISCAPACIDAD" COLOR AZUL PANTONE 294 DE 0.40 MTS DE ANCHO Y LONGITUD VARIABLE, CON UNA SEPARACION DE 0.40 MTS. ENTRE ELLAS, SECADO AL TACTO EN 5 MIN Y AL DURO EN 30 MIN. INCLUYE: MATERIAL, Y ESPECIFICACIONES QUE CUMPLAN CON LA NORMATIVA N-CMT-5-01-001/05,N-PRY-CAR-10-01-002/13 APLICADAS AL DIA DE HOY MANO DE OBRA, TRAZO, ENMASCARILLADO, LIMPIEZAS PREVIAS Y POSTERIORES DE LA SUPERFICIE, Y TODO LO NECESARIO PARA SU CORRECTA EJECUCION, TRABAJO TERMINADO.	M2	30	$164.18	$4,925.40
17	SUMINISTRO Y APLICACIÓN DE PINTURA BASE SOLVENTE " EN FLECHAS CLASIFICACIÓN M - 11.1, "FLECHA SENCILLA" PARA INDICAR SENTIDO DE CIRCULACIÓN , EN VIALIDADES PARA VELOCIDAD MENOR A 60KM POR HORA DIFERENTES DIMENSIONES (VER PLANO DE SEÑALAMIENTOS) COLOR BLANCO, REFLEJANTE CON MICRO ESFERA DE VIDRIO EN PROPORCIÓN SEGÚN NORMA SCT, INCLUYE: MATERIALES Y ESPECIFICACIONES QUE CUMPLAN CON LA NORMATIVA N-CMT-5-01-001/05, N-PRY-CAR-10-01-002/13 APLICADAS AL DIA DE HOY, MATERIAL, TRAZO, ENMASCARILLADO, MANO DE OBRA, LIMPIEZA PREVIA DE SUPERFICIE, EQUIPO NECESARIO PARA SU EJECUCIÓN, Y TODO LO NECESARIO PARA SU CORRECTA EJECUCIÓN, TRABAJO TERMINADO.	PZA	2	$414.97	$829.94
18	SUMINISTRO Y COLOCACION DE VIALETA STANDARD (S-200) DE 10X10CM. COLOR: CUERPO AMARILLO Y REFLEJANTE AMARILLO 1 CARA MARCA SEA O SIMILAR EN CALIDAD Y ESPECIFICACIONES DE FICHA TECNICA, ANCLADO EN PAVIMENTO SISTEMA DE SUJECION DE ALTO AGARRE BASE CUÑAS CON AB PEGAMENTO EPOXICO 50/50 RESISTENTE A ALTA TEMPERATURA (VER PLANO DE DETALLES DE SEÑALAMIENTOS HORIZONTAL Y VERTICAL). INCLUYE: TRAZO, ALINEACION, ELEVACION CUALQUIER ALTURA, TRABAJO TERMINADO, LIMPIEZAS.	PZA	86	$62.94	$5,412.84
19	SUMINISTRO Y APLICACIÓN DE LOGOTIPO A (SILLA DE RUEDAS) EN PINTURA EPOXICA BASE SOLVENTE COLOR BLANCO EN RAMPAS PARA PERSONAS CON DISCAPACIDAD TAMAÑO Y DISEÑO SEGÚN PLANOS. INCLUYE: TRAZO, ENMASCARILLADO, PLANTILLA, MANO DE OBRA, LIMPIEZA PREVIA DE SUPERFICIE, EQUIPO NECESARIO PARA SU EJECUCIÓN, Y TODO LO NECESARIO PARA SU CORRECTA EJECUCIÓN, TRABAJO TERMINADO.	PZA	4	$1,365.21	$5,460.84
20	SUMINISTRO Y APLICACIÓN DE PINTURA EPOXICA BASE SOLVENTE COLOR AZUL (PANTONE 294) EN RAMPAS PARA PERSONAS CON DISCAPACIDAD CUALQUIER SECCIÓN SEGÚN PLANOS. INCLUYE: TRAZO, MANO DE OBRA, LIMPIEZA PREVIA DE SUPERFICIE, EQUIPO NECESARIO PARA SU EJECUCIÓN, Y TODO LO NECESARIO PARA SU CORRECTA EJECUCIÓN, TRABAJO TERMINADO.	M2	5.76	$240.23	$1,383.72

Obra: **PAVIMENTO HIDRÁULICO, CALLE SANTA MÓNICA. ETAPA 02**

Ubicación: **TRAMO: ENTRE CADENAMIENTO 0+180 Y 0+335 (CALLE MARCOS CORONADO), LOS POCITOS Ej.**

Contratista: **GRUPO ARO INGENIUM, S.A. DE C.V. (367)**

No.	Concepto	Unidad	Cantidad	Precio Unitario	Importe Total
	GRUPO: **SEÑALIZACION**				
	PARTIDA: **SEÑALAMIENTO HORIZONTAL**				
21	SUMINISTRO Y APLICACIÓN DE PINTURA BASE SOLVENTE " EN RAYA SEPARADORA CLASIFICACIÓN M -1.6, CONTINUA DOBLE, PARA DELIMITAR CARRIL EXCLUSIVO DE FRENTE EN PISO, 0.10 MTS DE ANCHO, CON UNA SEPARACIÓN IGUAL AL ANCHO DE LA LINEA A BASE DE PINTURA PARA TRAFICO COLOR AMARILLO CON MICRO ESFERA SEGÚN NORMA SCT, INCLUYE: MATERIALES Y ESPECIFICACIONES QUE CUMPLAN CON LA NORMATIVA N-CMT-5-01-001/05, N-PRY-CAR-10-01-002/13 APLICADAS AL DIA DE HOY, MATERIAL, TRAZO, ENMASCARILLADO, MANO DE OBRA, LIMPIEZA PREVIA DE SUPERFICIE, EQUIPO NECESARIO PARA SU EJECUCIÓN, Y TODO LO NECESARIO PARA SU CORRECTA EJECUCIÓN, TRABAJO TERMINADO.	ML	140	$15.11	$2,115.40
22	SUMINISTRO Y APLICACIÓN DE PINTURA BASE SOLVENTE PARA MARCAS EN GUARNICIONES CLASIFICACION M-12.1, M12.2 APLICADA SOBRE GUARNICIONES Y DENTELLONES DE CUALQUIER COLOR, SEGÚN SE REQUIERA Y SEGÚN NORMA S.C.T. SECADO AL TACTO EN 5 MIN Y AL DURO EN 30 MIN CON MICRO ESFERA , DESARROLLO DE 35 CM. INCLUYE: MATERIALES Y ESPECIFICACIONES QUE CUMPLAN CON LA NORMATIVA N-CMT-5-01-001/05, N-PRY-CAR-10-01-002/13 APLICADAS AL DIA DE HOY, TRAZO, MANO DE OBRA, LIMPIEZA PREVIA DE SUPERFICIE, EQUIPO NECESARIO PARA SU EJECUCIÓN, Y TODO LO NECESARIO PARA SU CORRECTA EJECUCIÓN, TRABAJO TERMINADO.	ML	280	$47.25	$13,230.00
23	SUMINISTRO Y COLOCACION DE BOYA DE PLASTICO OJO DE GATO (VT-38), MARCA CREATIVAL O SIMILAR EN CALIDAD Y PRECIO, CON REFLEJANTE COLOR BLANCO, GRADO ALTA INTENSIDAD, FIJACION A SUPERFICIE CON CLAVOS DE ACERO ALTA RESISTENCIA, INCLUYE: MATERIAL, MANO DE OBRA, HERRAMIENTA, ELEMENTOS DE FIJACION, ALINEADO, LIMPIEZAS Y TODO LO NECESARIO PARA SU CORRECTA EJEUCION, TRABAJO TERMINADO.	PZA	86	$197.92	$17,021.12
				Totales por Partida	**$50,939.46**
	PARTIDA: **SEÑALAMIENTO VERTICAL**				
24	SUMINISTRO Y COLOCACION DE SEÑALAMIENTO VERTICAL DE RESTRICCION SR-9 (VELOCIDAD MAXIMA), DISEÑO NORMATIVO SCT, HECHO A ABASE DE LAMINA GALVANIZADA CON CEJA DE 72 X 72 CM CALIBRE 16, CON TERMINADO GRADO INGENIERIA EN SU TOTALIDAD, EL COLOR SERA REFLEJANTE GRADO INGENIERIA Y SIMBOLOS EN COLOR REFLEJANTE, TODOS LOS COLORES RESISTENTES A LA INTEMPERIE, FIJADA MEDIANTE BARRENADO Y TORNILLOS DE 2 1/2" X 5/16" A UN POSTE DE PTR DE 2 X 2" CALIBRE 14 EN ACABADO GALVANIZADO Y CON UNA ALTURA DE 2.5 MTS AL NIVEL DE BANQUETA A LA PARTE INFERIOR DE LA LAMINA MAS EL EXCEDENTE REQUERIDO PARA FIJAR LAS LAMINAS Y ANCLADO DE 50 CM DE PROFUNDIDAD CON ANGULO TRANSVERSAL DE 1 X 1" DE 25 CM, EN DADO DE CONCRETO F´c=150 KG/CM2 DE 30 CM DE LADO (VER PLANO DE DETALLES CRITERIOS DE ANCLAJE DE SEÑALAMIENTO VERTICAL, DETALLE SEÑ-02 Y SEÑ 03), MCA ASEA O SIMILAR EN CALIDAD Y ESPECIFICACIONES, INCLUYE: MANO DE OBRA, FLETES, MANIOBRAS LIMPIEZAS Y RETIRO DEL SOBRANTE FUERA DE LA OBRA HASTA TIRADERO OFICIAL, TRABAJO TERMINADO.	PZA	1	$2,224.88	$2,224.88
				Totales por Partida	**$2,224.88**
				Totales por Grupo	**$53,164.34**

Obra: PAVIMENTO HIDRÁULICO, CALLE SANTA MÓNICA. ETAPA 02

Ubicación: TRAMO: ENTRE CADENAMIENTO 0+180 Y 0+335 (CALLE MARCOS CORONADO), LOS POCITOS Ej.

Contratista: GRUPO ARO INGENIUM, S.A. DE C.V. (367)

No.	Concepto	Unidad	Cantidad	Precio Unitario	Importe Total

Totales Presup.		$1,249,456.11
Anticipo	+	$624,728.06
Amortizac. Ant.	-	$624,728.06
SubTotal. Ant.	=	$1,249,456.11
IVA	+	$199,912.98
Total	=	$1,449,369.09

H. AYUNTAMIENTO CONSTITUCIONAL DEL MUNICIPIO DE AGUASCALIENTES 2021-2024

PRESUPUESTO MODIFICADO

Aguascalientes

Obra: **PAVIMENTO HIDRÁULICO, CALLE SANTA MÓNICA. ETAPA 02**

Ubicación: **TRAMO: ENTRE CADENAMIENTO 0+180 Y 0+335 (CALLE MARCOS CORONADO), LOS POCITOS Ej.**

Contratista: **GRUPO ARO INGENIUM, S.A. DE C.V. (367)**

Grupo	Partida	Importe
PAVIMENTO HIDRAULICO		
	PRELIMINARES	$15,184.34
	EXCAVACIONES, ACARREOS Y TERRACERIAS	$552,836.75
	PAVIMENTO HIDRAULICO	$562,857.09
	OBRA COMPLEMENTARIA	$54,157.26
	Subtotal por Grupo	**$1,185,035.45**
LIMPIEZAS		
	LIMPIEZAS	$11,256.32
	Subtotal por Grupo	**$11,256.32**
SEÑALIZACION		
	SEÑALAMIENTO HORIZONTAL	$50,939.46
	SEÑALAMIENTO VERTICAL	$2,224.88
	Subtotal por Grupo	**$53,164.34**

Totales Presup.		**$1,249,456.11**
Anticipo	+	**$624,728.06**
Amortizac. Ant.	-	**$624,728.06**
SubTotal. Ant.	=	**$1,249,456.11**
IVA	+	**$199,912.98**
Total	=	**$1,449,369.09**

H. AYUNTAMIENTO CONSTITUCIONAL DEL MUNICIPIO DE AGUASCALIENTES 2021-2024


H. AYUNTAMIENTO DE AGUASCALIENTES
SECRETARÍA DE OBRAS PÚBLICAS
DIRECCIÓN DE SUPERVISIÓN DE OBRA


Aguascalientes
LA CIUDAD DE TU VIDA


MEMORIA FOTOGRAFICA


OBRA:	PAVIMENTO HIDRÁULICO, CALLE SANTA MÓNICA. ETAPA 02, TRAMO: ENTRE CADENAMIENTO 0+180 Y 0+335 (CALLE MARCOS CORONADO), LOS POCITOS Ej.					
NO. DE CONTRATO:	DM-0116-2022		CONTRATISTA:	GRUPO ARO INGENIUM, S.A. DE C.V.		

INICIO.

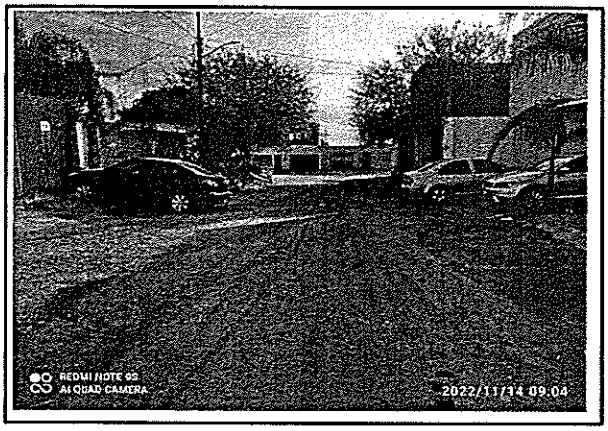

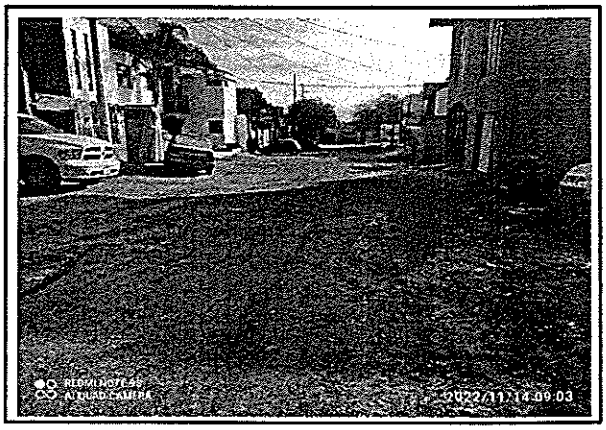

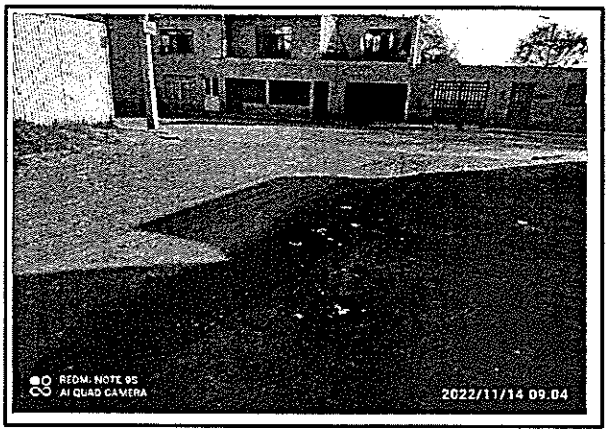

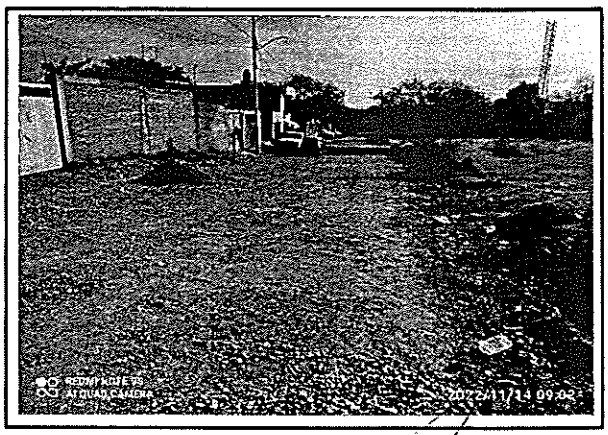

ING. IVAN ALEJANDRO RUIZ ESPARZA SOLIS
SUPERVISOR DE OBRA.

H. AYUNTAMIENTO CONSTITUCIONAL DEL MUNICIPIO DE AGUASCALIENTES 2021-2024

H. AYUNTAMIENTO DE AGUASCALIENTES

SECRETARÍA DE OBRAS PÚBLICAS


DIRECCIÓN DE SUPERVISIÓN DE OBRA

Aguascalientes
LA CIUDAD DE TU VIDA


MEMORIA FOTOGRAFICA

OBRA:	PAVIMENTO HIDRÁULICO, CALLE SANTA MÓNICA. ETAPA 02, TRAMO: ENTRE CADENAMIENTO 0+180 Y 0+335 (CALLE MARCOS CORONADO), LOS POCITOS Ej.					
NO. DE CONTRATO:	DM-0116-2022		CONTRATISTA:	GRUPO ARO INGENIUM, S.A. DE C.V.		

PROCESO

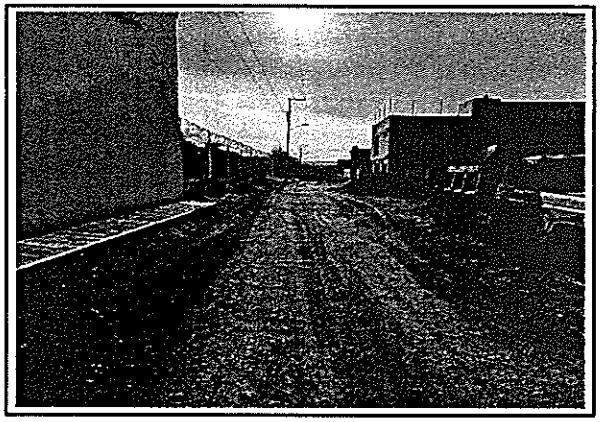



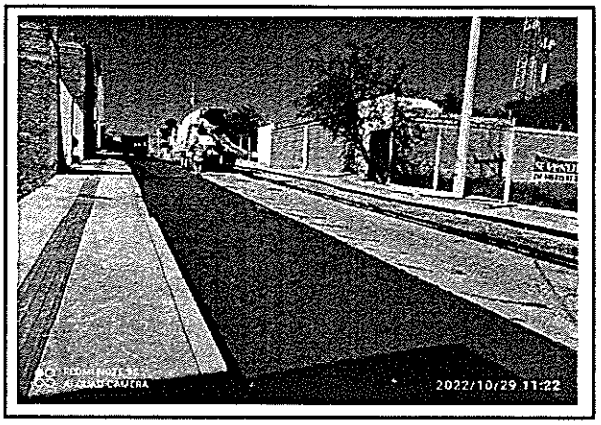



ING. IVAN ALEJANDRO RUIZ ESPARZA SOLIS
SUPERVISOR DE OBRA.

H. AYUNTAMIENTO CONSTITUCIONAL DEL MUNICIPIO DE AGUASCALIENTES 2021-2024


H. AYUNTAMIENTO DE AGUASCALIENTES
SECRETARÍA DE OBRAS PÚBLICAS
DIRECCIÓN DE SUPERVISIÓN DE OBRA


Aguascalientes
LA CIUDAD DE TU VIDA


MEMORIA FOTOGRAFICA


OBRA:	PAVIMENTO HIDRÁULICO, CALLE SANTA MÓNICA. ETAPA 02, TRAMO: ENTRE CADENAMIENTO 0+180 Y 0+335 (CALLE MARCOS CORONADO), LOS POCITOS Ej.					
NO. DE CONTRATO:	DM-0116-2022		CONTRATISTA:	GRUPO ARO INGENIUM, S.A. DE C.V.		

TERMINO

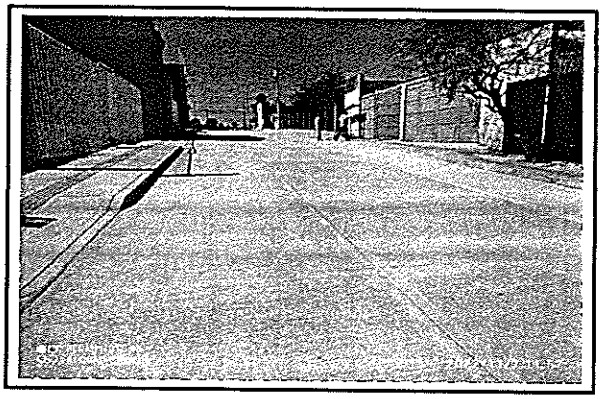

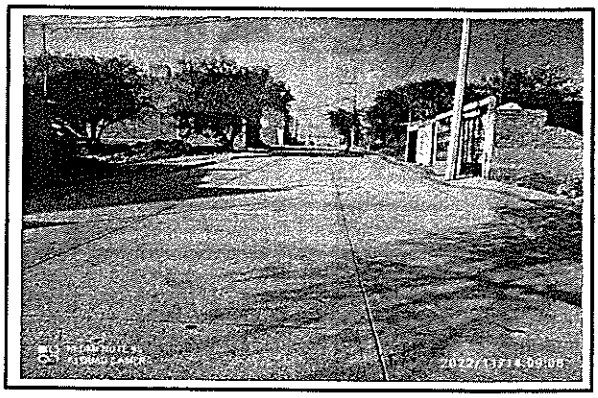

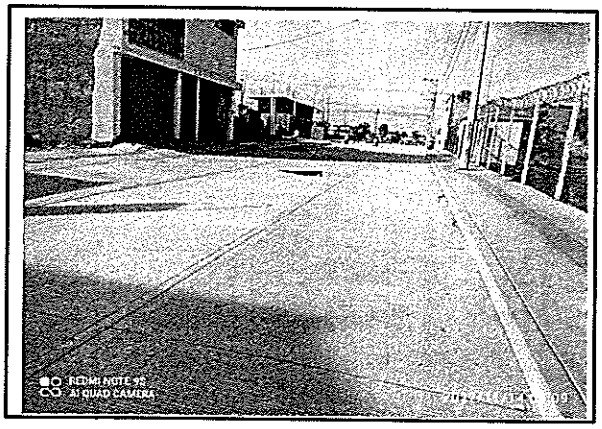

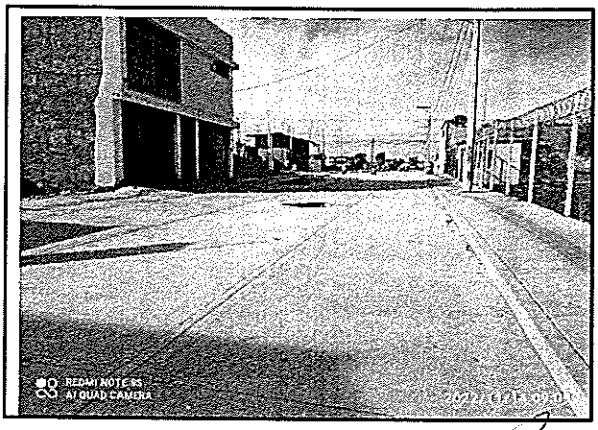

ING. IVAN ALEJANDRO RUIZ ESPARZA SOLIS
SUPERVISOR DE OBRA.

MODIFICADO

SECRETARÍA DE OBRAS PÚBLICAS

DIRECCIÓN DE SUPERVISIÓN DE OBRA

EJERCICIO 2022

N° DE CONTRATO: DM-0116-2022


NOMBRE DE LA OBRA: PAVIMENTO HIDRÁULICO, CALLE SANTA MÓNICA. ETAPA 02, TRAMO: ENTRE CADENAMIENTO 0+180 Y 0+335 (CALLE MARCOS CORONADO), LOS POCITOS EJ.

MONTO MODIFICADO FINAL: $ 1,449,369.09

VOLUMEN	UNIDAD	COMPONENTE DE LA OBRA	MONTO
1082.35	M2	CONSTRUCCION DE PAVIMENTO HIDRAULICO A BASE DE CONCRETO PREMEZCLADO MR=38 KG/CM2 TMA 1 1/2" GRAVA TRITURADA, REVENIMIENTO DE 6 A 8 CM FRAGUADO NORMAL DE 15 CM DE ESPESOR MODULADO EN LOSAS DE 3.5 MTS. (ANCHO) X 3.5 MTS (LARGO) COMO MAXIMO, CON CORTES EN LAS LOSAS DE 1/3 DEL	$ 1,185,035.45
1099.25	M2	LIMPIEZA GENERAL Y A DETALLE DE LA OBRA, INCLUYE: BARRIDO Y ACARREOS DE ESCOMBROS, RETIRO FUERA DE LA OBRA DEL MISMO, DESVIO VEHICULAR, SEÑALETICA, A MANO Y A MAQUINA.	$ 11,256.32
86.00	PZA	SUMINISTRO Y APLICACIÓN DE PINTURA BASE SOLVENTE " EN FLECHAS CLASIFICACIÓN M - 11.1, "FLECHA SENCILLA" PARA INDICAR SENTIDO DE CIRCULACIÓN , EN VIALIDADES PARA VELOCIDAD MENOR A 60KM POR HORA DIFERENTES DIMENSIONES (VER PLANO DE SEÑALAMIENTOS) COLOR BLANCO, REFLEJANTE	$ 53,164.34


TOTAL PRESUP.	$	1,249,456.11
IVA	$	199,912.98
TOTAL	$	1,449,369.09

NOMBRE DEL SUPERVISOR: ING. IVAN ALEJANDRO RUIZ ESPARZA SOLIS

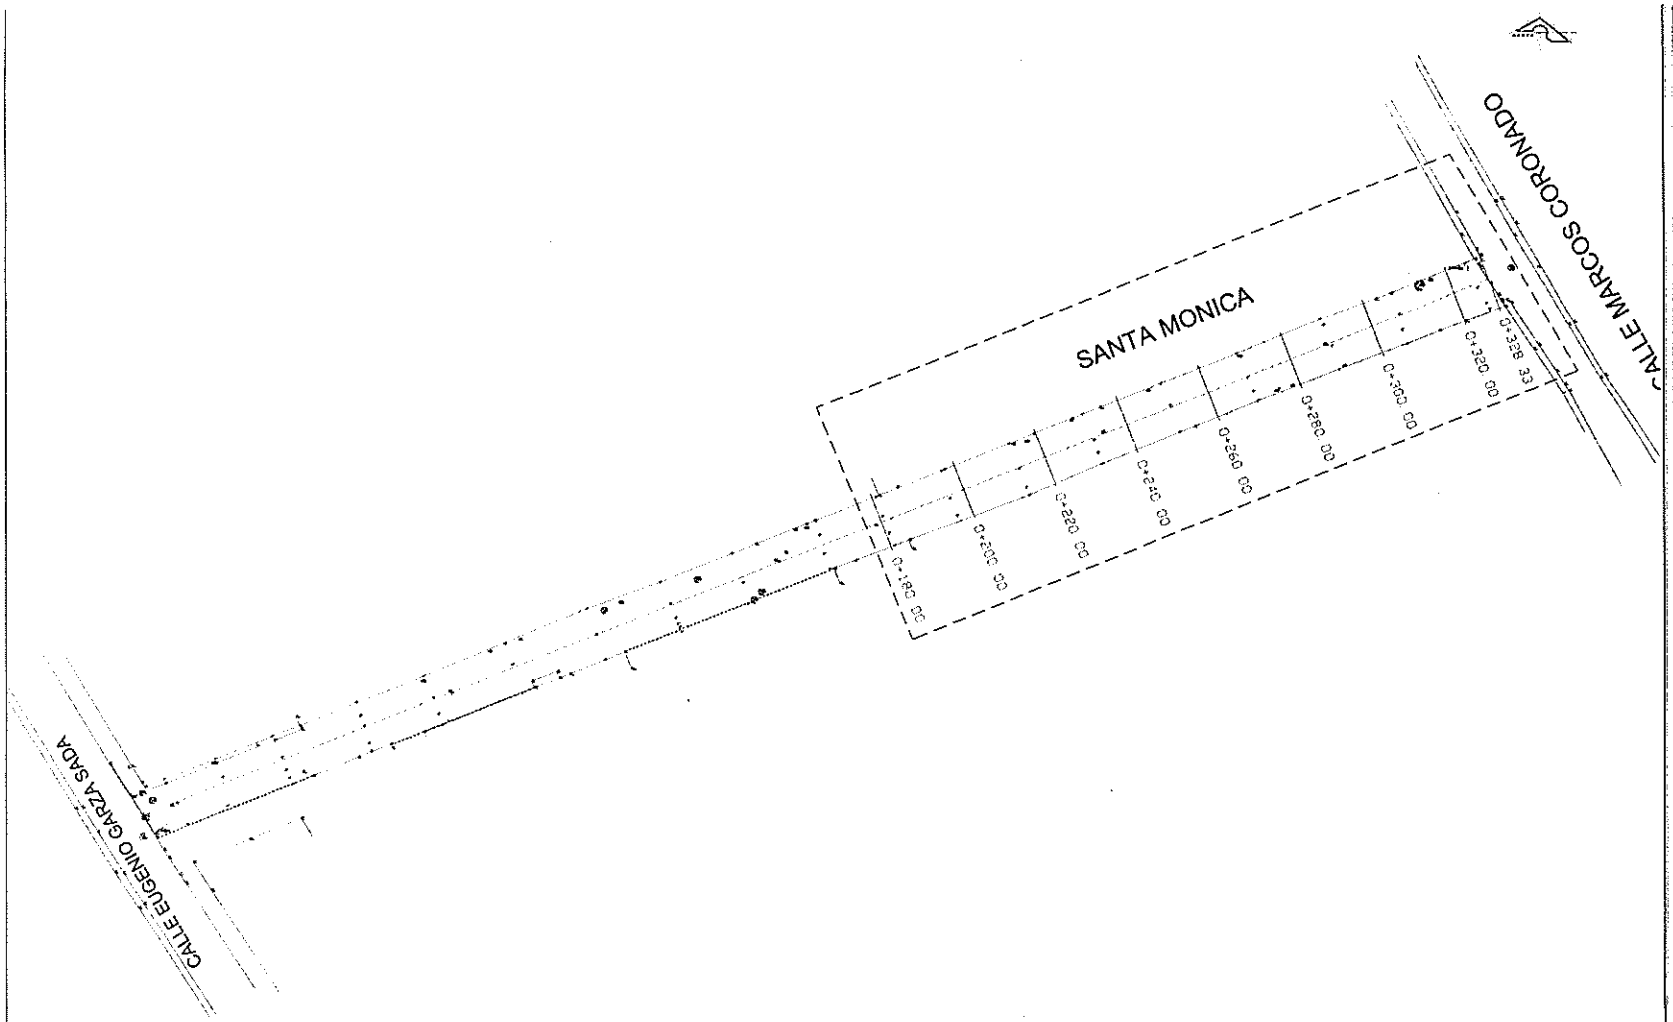

LEVANTAMIENTO TOPOGRAFICO

PLANTA DE CONJUNTO — CALLE SANTA MONICA

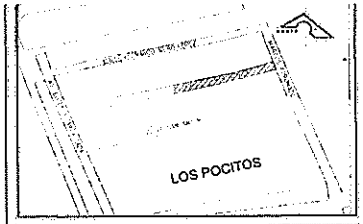

SIMBOLOGIA

- EJE DE PROYECTO
- LIMITE DE PROYECTO
- GUARNICION EXISTENTE
- POSTE LUMINARIA
- POSTE DE CFE
- POSTE DE TELMEX
- REGISTRO
- POSTE
- REGISTROS CFE
- REGISTROS TELMEX
- REGISTROS TELMEX
- TELEFONO
- POZO DE VISITA
- CAJA DE VALVULAS
- SEMAFOROS
- RETENIDA
- ANUNCIO
- RETENIDA POSTE
- RETIRO DE ARBOL EXISTENTE

La Dirección de Planeación y Proyectos solo autoriza el proyecto ejecutivo, no es responsable de la correcta ejecución de la obra. Este documento no tiene validez si no presenta las firmas de los responsables para su autorización, así como los sellos respectivos.

PRESIDENTE MUNICIPAL
M.P.P. Leonardo Montañez Castro
ENCARGADA DE DESPACHO DE LA SOPMA
Arq. Gloria Guadalupe Castillo González

REV. FECHA — OBSERVACIONES

Vo. Bo. DE LA DEPENDENCIA

RESP. DE PROY. EXTERNO		LOGO EXTERNO
CED. PROFESIONAL		
PROYECTO	REVISO	AUTORIZO


Dirección de Planeación y Proyectos de Obra — Secretaría de Obras Públicas


PROYECTISTA	COORDINADOR
ING. DIEGO ROMO AGUILERA	ARQ. ALEJANDRO JAIME LEAL
JEFE DE DEP.	DIRECTOR
ARQ. J. JESUS PALAFOX GONZÁLEZ	M. en ARQ. JOSÉ LUIS JIMÉNEZ GARCÍA


PROYECTO
CONSTRUCCIÓN DE CONCRETO HIDRAULICO CALLE SANTA MONICA ETAPA 2 (LOS POCITOS)
UBICACIÓN
COLONIA LOS POCITOS
TRAMO ENTRE CADENAMIENTO 0+180 Y 0+338 C. MARCOS CORONADO
CONTENIDO
LEVANTAMIENTO TOPOGRAFICO

CLAVE	No. PLANO
LEV 01	02
FECHA: OCT 2022	ESCALA: INDICADA
ACOTACIÓN: METROS	No. EXP.: E-000-22

Aguascalientes
LA CIUDAD DE TU VIDA

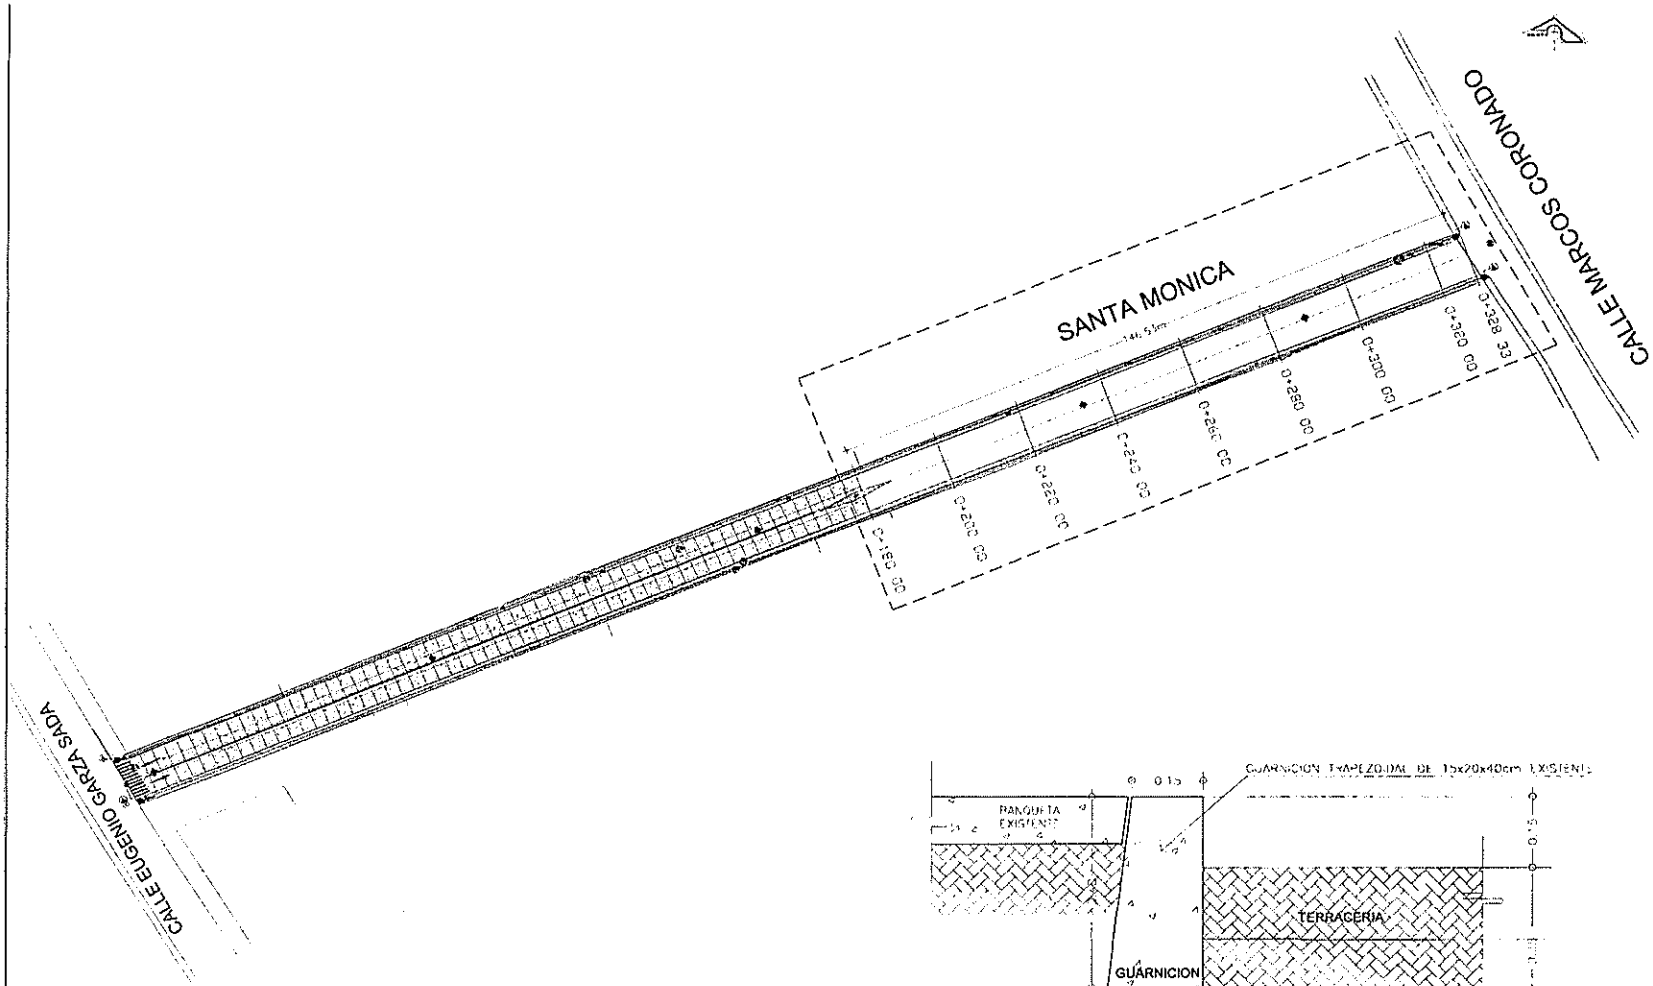

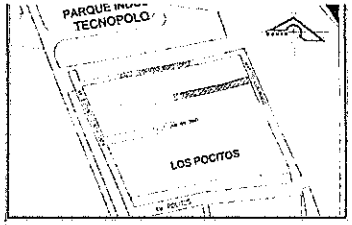

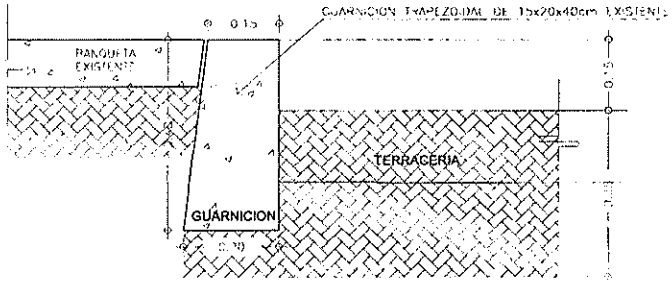

DETALLE DE GUARNICION

ESC: S/E

PLANTA DE ESTADO ACTUAL

CALLE SANTA MONICA

SIMBOLOGÍA

- EJE DE PROYECTO
- LIMITE DE PROYECTO
- GUARNICION EXISTENTE
- SUPERF. DE SIN TRATAMIENTO (TERRACERIA)
- CONCRETO EXISTENTE
- POSTE LUMINARIA
- POSTE DE CFE
- POSTE DE TELMEX
- REGISTRO
- POSTE
- REGISTROS CFE
- REGISTROS TELMEX
- REGISTROS TELMEX
- TELEFONO
- POZO DE VISITA
- CAJA DE VALVULAS
- SEMAFOROS
- RETENIDA
- ANUNCIO
- RETENIDA POSTE
- RETIRO DE ARBOL EXISTENTE

La Dirección de Planeación y Proyectos solo autoriza el proyecto ejecutivo, no es responsable de la correcta ejecución de la obra. Este documento no tiene validez si no presenta las firmas de los responsables para su autorización, así como los sellos respectivos.

PRESIDENTE MUNICIPAL
M.P.P. Leonardo Montañez Castro
ENCARGADA DE DESPACHO DE LA SOPMA
Arq. Gloria Guadalupe Castillo González

REV. FECHA OBSERVACIONES

Vo Bo. DE LA DEPENDENCIA


RESP. DE PROY. EXTERNO | LOGO EXTERNO
CED. PROFESIONAL
PROYECTÓ | REVISÓ | AUTORIZÓ


Dirección de Planeación y Proyectos de Obra | Secretaría de Obras Públicas
PROYECTISTA: ING. DIEGO ROMO AGUILERA — COORDINADOR: ARQ. ALEJANDRO JAIME LEAL
JEFE DE DEP.: ARQ. J. JESÚS PALAFOX GONZÁLEZ — DIRECTOR: M. en ARQ. JOSÉ LUIS JIMÉNEZ GARCÍA


PROYECTO: CONSTRUCCIÓN DE CONCRETO HIDRAULICO CALLE SANTA MONICA ETAPA 2 (LOS POCITOS)
UBICACIÓN: COLONIA LOS POCITOS — TRAMO ENTRE CADENAMIENTO 0+160 Y 0+328 C. MARCOS CORONADO
CONTENIDO: PLANTA DE ESTADO ACTUAL

CLAVE	No. PLANO
EA 01	03
FECHA: OCT 2022	ESCALA: INDICADA
ACOTACIÓN: METROS	No. EXP: E-000-22

Aguascalientes — LA CIUDAD DE TU VIDA

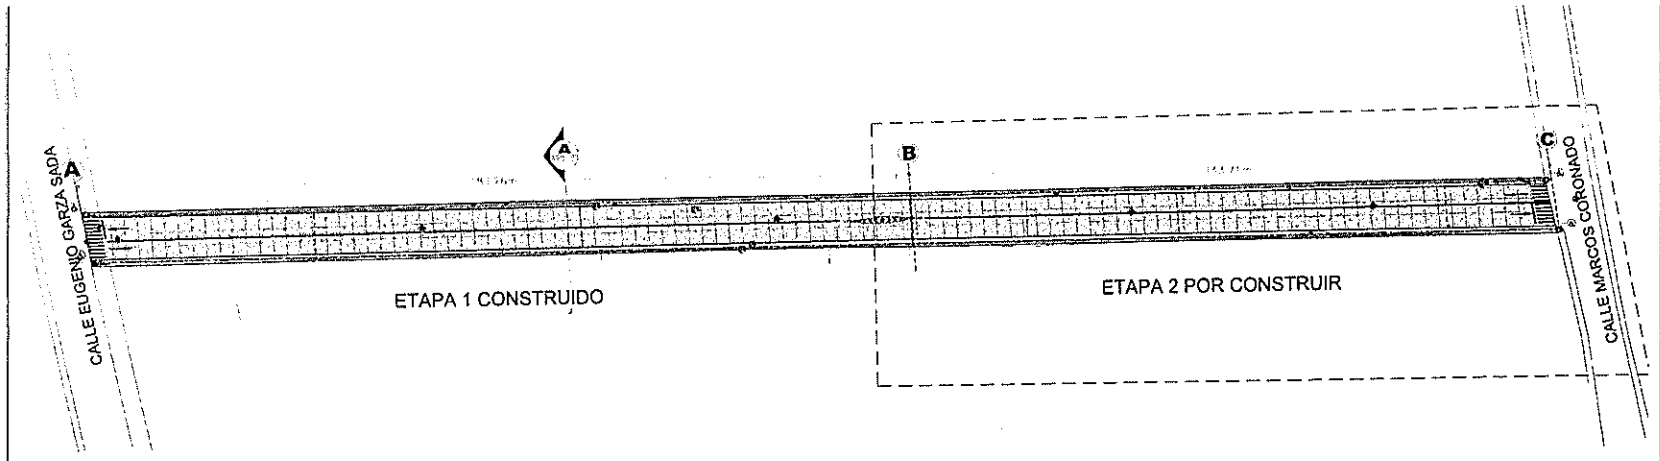

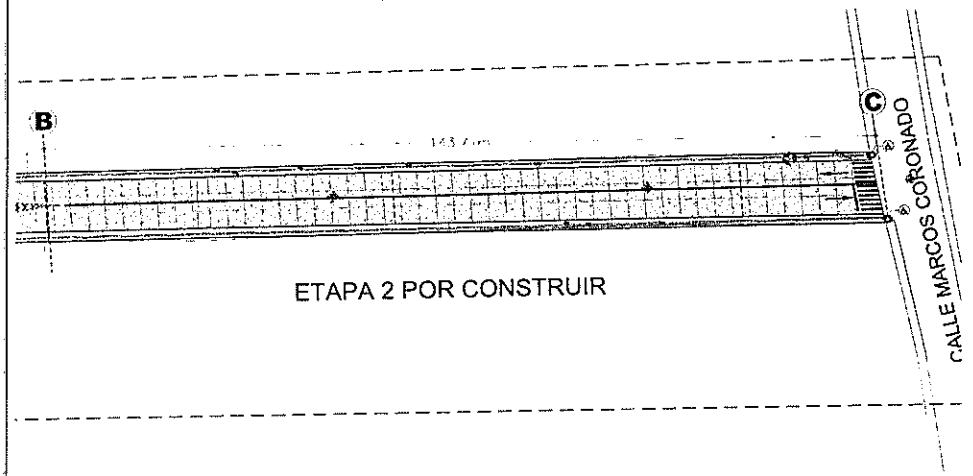


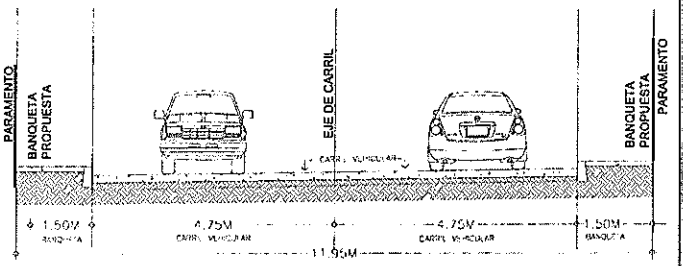

CORTE A

PROYECTO GEOMÉTRICO

ESCALA 1:250 CALLE SANTA MONICA

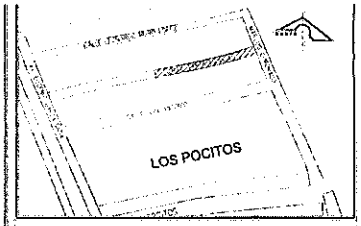


SIMBOLOGÍA


SIMBOLOGIA

- EJE DE PROYECTO
- BENTELLON PROPUESTO
- PAVIMENTO HIDRAULICO (MR=38) 15 CM ESPESOR
- GUARNICION PROPUESTA
- APLICAR PINTURA EN RAMPA EXISTENTE
- 1,685.83 M2 TOTAL DE PAVIMENTACION
- BANQUETA DE CONCRETO
- LOSA DIAMANTE A BASE DE CONCRETO PREMEZCLADO (MR=45) 25 CM ESPESOR
- SUPERFICIE SIN TRATAMIENTO (TERRACERIA)
- FLECHA DE SENTIDO
- FRANJAS AMARILLAS DE CRUCE PEATONAL
- RAMPA
- GUIA TACTIL
- MOLDE PARA ESTAMPADO EN CONCRETO TIPO GUIA
- DOBLE LINEA CONTINUA
- BOYA DE PLASTICO DUO DE GATO(VER DET)

La Dirección de Planeación y Proyectos solo autoriza el proyecto ejecutivo, no es responsable de la correcta ejecución de la obra. Este documento no tiene validez si no presenta las firmas de los responsables para su autorización, así como los sellos respectivos.


PRESIDENTE MUNICIPAL M.P.P. Leonardo Montañez Castro ENCARGADA DE DESPACHO DE LA SOPMA Arq. Gloria Guadalupe Castillo González	REV. FECHA OBSERVACIONES	Vo. Bo. DE LA DEPENDENCIA	RESP. DE PROY. EXTERNO / CED. PROFESIONAL / PROYECTÓ / REVISÓ / AUTORIZÓ / LOGO EXTERNO	Dirección de Planeación y Proyectos de Obra Secretaría de Obras Públicas PROYECTISTA: ING. DIEGO ROMO AGUILERA COORDINADOR: ARQ. ALEJANDRO JAIME LEAL JEFE DE DEP.: ARQ. J. JESÚS PALAFOX GONZÁLEZ DIRECTOR: M. en ARQ. JOSÉ LUIS JIMÉNEZ GARCÍA	PROYECTO: CONSTRUCCIÓN DE CONCRETO HIDRAULICO CALLE SANTA MONICA ETAPA 2 (LOS POCITOS) UBICACIÓN: COLONIA LOS POCITOS TRAMO ENTRE CADENAMIENTO 0+183 Y 0+332(C. MARCOS CORONADO) CONTENIDO: PROYECTO GEOMETRICO	CLAVE: PG 01 No. PLANO: 04 FECHA: OCT 2022 ESCALA: INDICADA ACOTACIÓN: METROS No. EXP.: E-000-22	Aguascalientes LA CIUDAD DE TU VIDA

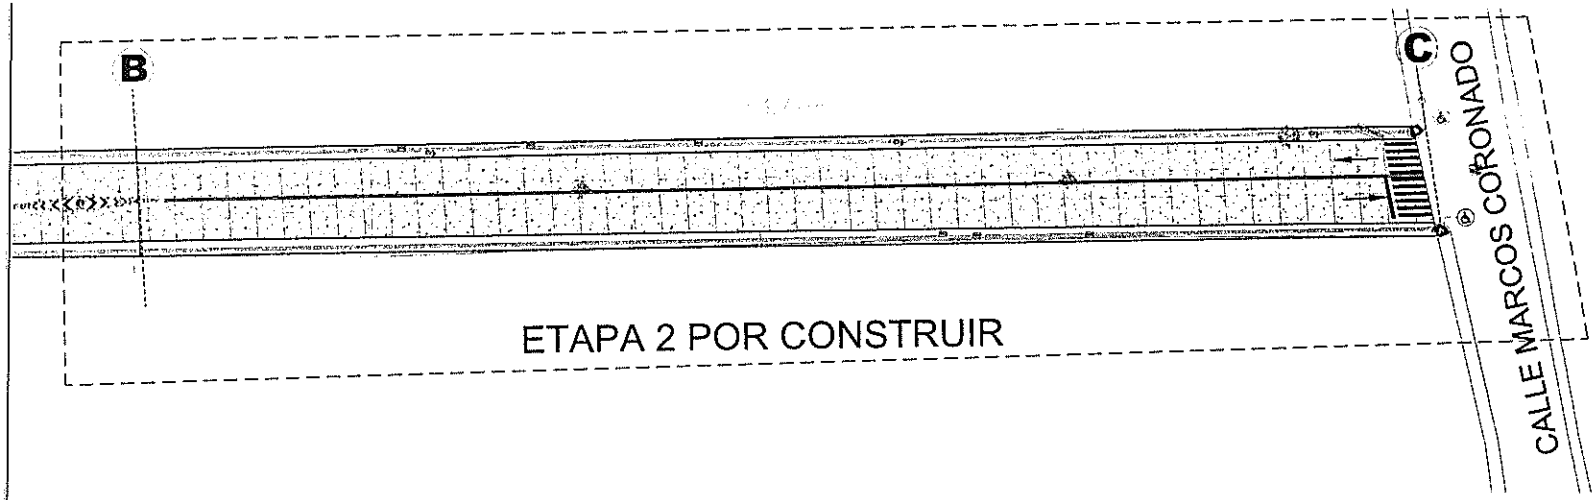

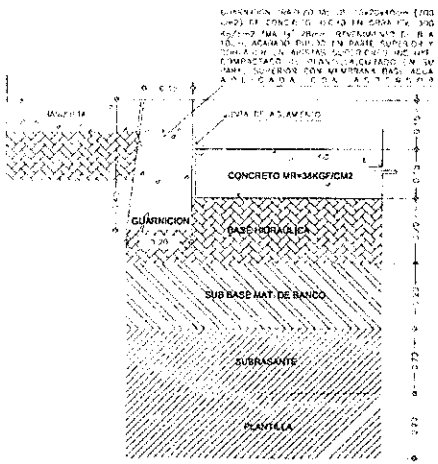


ESTRUCTURA 1

S/E

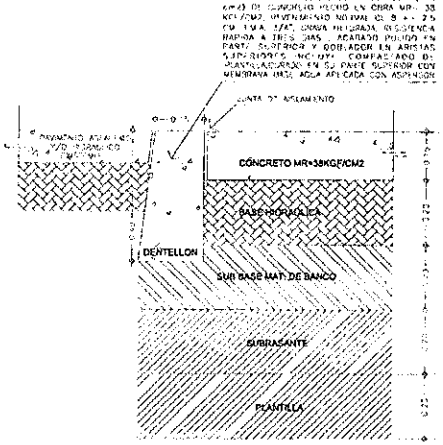


ESTRUCTURA 1-A

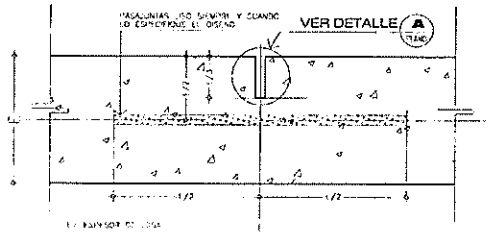

SELLADO DE JUNTAS

S/E

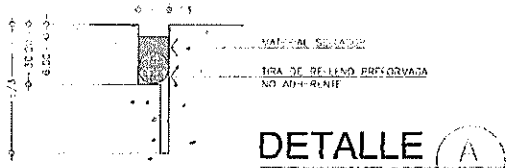

DETALLE A PLANO


S/E

COTAS EN mm

E= ESPESOR DE LOSA

PAVIMENTACION

ESCALA 1:250 CALLE SANTA MONICA

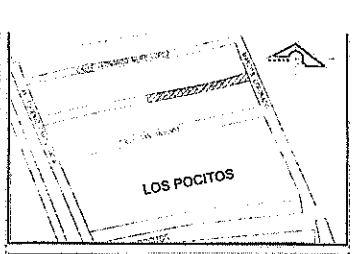

SIMBOLOGÍA

- EJE DE PROYECTO
- IDENTIFICACION PROPUESTO
- GUARNICION PROPUESTA
- PAVIMENTO HIDRAULICO (MR=38) 15 CM ESPESOR
- 1,099.25 M2 SUPERFICIE TOTAL
- FLECHA DE SENTIDO
- LINEAS AMARILLAS DEL CRUCE PEATONAL
- LINEA DE ALTO VEHICULAR
- DOBLE LINEA CONTINUA

La Dirección de Planeación y Proyectos solo autoriza el proyecto ejecutivo, no es responsable de la correcta ejecución de la obra. Este documento no tiene validez si no presenta las firmas de los responsables para su autorización, así como los sellos respectivos.

PRESIDENTE MUNICIPAL
M.P.P. Leonardo Montañez Castro
ENCARGADA DE DESPACHO DE LA SOPMA
Arq. Gloria Guadalupe Castillo González

REV. FECHA OBSERVACIONES

V.o.Bo DE LA DEPENDENCIA

RESP. DE PROY. EXTERNO	LOGO EXTERNO
CED. PROFESIONAL	
PROYECTO / REVISO	AUTORIZO


Dirección de Planeación y Proyectos de Obra — Secretaría de Obras Públicas

PROYECTISTA	COORDINADOR
ING. DIEGO ROMO AGUILERA	ARQ. ALEJANDRO JAIME LEAL
JEFE DE DEP.	DIRECTOR
ARQ. J. JESÚS PALAFOX GONZÁLEZ	M. en ARQ. JOSÉ LUIS JIMÉNEZ GARCÍA

PROYECTO
CONSTRUCCIÓN DE CONCRETO HIDRAULICO CALLE SANTA MONICA ETAPA 2 (LOS POCITOS)
UBICACIÓN
COLONIA LOS POCITOS
TRAMO ENTRE CADENAMIENTO 0+160 Y 0+330 C. MARCOS CORONADO
CONTENIDO
PROYECTO GEOMETRICO "DETALLES CONSTRUCTIVOS"

CLAVE	No. PLANO
PG 02	05
FECHA: OCT 2022	ESCALA: INDICADA
ACOTACIÓN: METROS	No. EXP.: E-006-22

Aguascalientes
LA CIUDAD DE TU VIDA

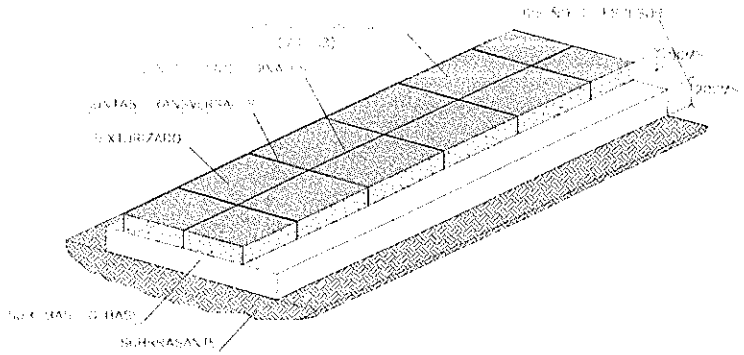


ESTRUCTURA DEL PAVIMENTO ISOMETRICO

SIN ESCALA




ESTRUCTURA DEL PAVIMENTO

SIN ESCALA

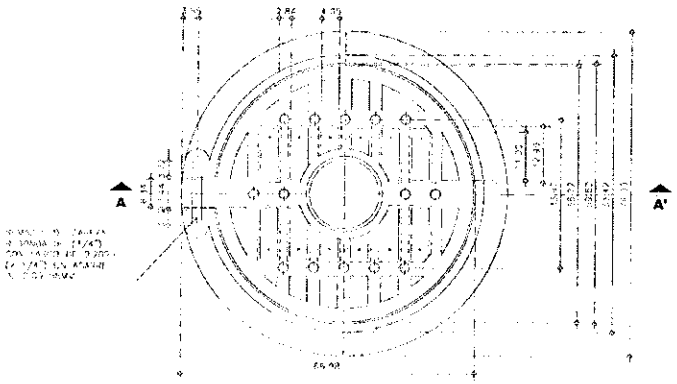


DETALLE DE BROCAL Y TAPA EN PLANTA

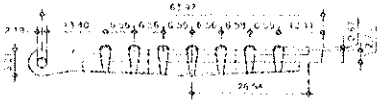


BROCAL Y TAPA EN ALZADO

CONSTRUCCIÓN DE LOSA DIAMANTE A BASE DE CONCRETO PREMEZCLADO MR= 45 KG/CM2, T.M.A. 3/4" (19 mm), GRAVA TRITURADA, REVENIMIENTO DE 8± 2.5 cm, RESISTENCIA RAPIDA A 3 DIAS, DE 20 CM DE ESPESOR, EN POZO DE VISITA SECCION DE 1.50 M X 1.50 M., INCLUYE: TRAZO, NIVELACIÓN, LIMPIEZA PRIMA Y PREPARACIÓN DE LA SUPERFICIE, COMPACTACIÓN DE TERRENO AL 95% DE SU PVSM, DESCARGADO, SUMINISTRO DE MATERIALES, DEMOLICIÓN Y RECONSTRUCCIÓN DE ARMADOS, LECHADA DE ADHERENTANTE DE ALTA DENSIDAD EN TODO EL PERIMETRO EXTERIOR DE 1/2", ASÍ COMO EN LAS JUNTAS DIAGONALES PARA FORMAR 4 PAÑOS, BROCA Y TAPA DE Fo Fo CON PESADO (165 KG).

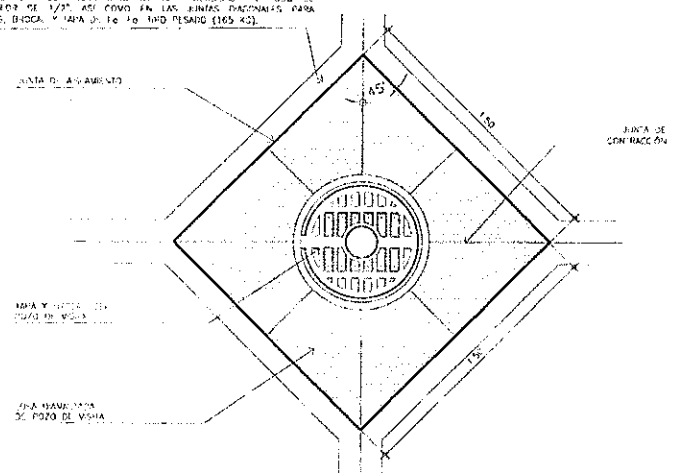

DETALLE LOSA DIAMANTE

SIN ESCALA

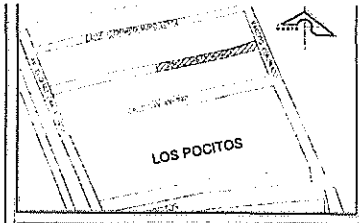

SIMBOLOGÍA

La Dirección de Planeación y Proyectos solo autoriza el proyecto ejecutivo, no es responsable de la correcta ejecución de la obra. Este documento no tiene validez si no presenta las firmas de los responsables para su autorización, así como los sellos respectivos.

PRESIDENTE MUNICIPAL
M.P.P. Leonardo Montañez Castro
ENCARGADA DE DESPACHO DE LA SOPMA
Arq. Gloria Guadalupe Castillo González

REV. | FECHA | OBSERVACIONES

Vo. Bo. DE LA DEPENDENCIA


RESP. DE PROY. EXTERNO | LOGO EXTERNO
CED. PROFESIONAL
PROYECTÓ | REVISÓ | AUTORIZÓ

Dirección de Planeación y Proyectos de Obra | Secretaría de Obras Públicas
PROYECTISTA | COORDINADOR
ING. DIEGO ROMO AGUILERA | ARQ. ALEJANDRO JAIME LEAL
JEFE DE DEP. | DIRECTOR
ARQ. J. JESÚS PALAFOX GONZÁLEZ | M. en ARQ. JOSÉ LUIS JIMÉNEZ GARCÍA


PROYECTO
CONSTRUCCIÓN DE CONCRETO HIDRAULICO CALLE SANTA MONICA ETAPA 2 (LOS POCITOS)
UBICACIÓN
COLONIA LOS POCITOS
TRAMO ENTRE CADENAMIENTO 0+180 Y 0+332 (C. MARCOS CORONADO)
CONTENIDO
DETALLES DEL PAVIMENTO

CLAVE: PG 03 | No. PLANO: 06
FECHA: OCT 2022 | ESCALA INDICADA
ACOTACIÓN METROS | No. EXP. E-000-22


Aguascalientes
LA CIUDAD DE TU VIDA

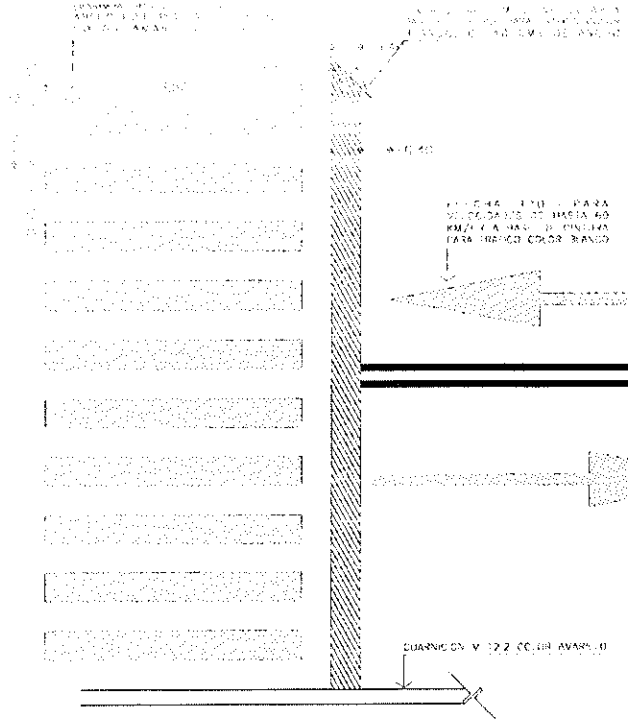

DETALLE TIPO 2

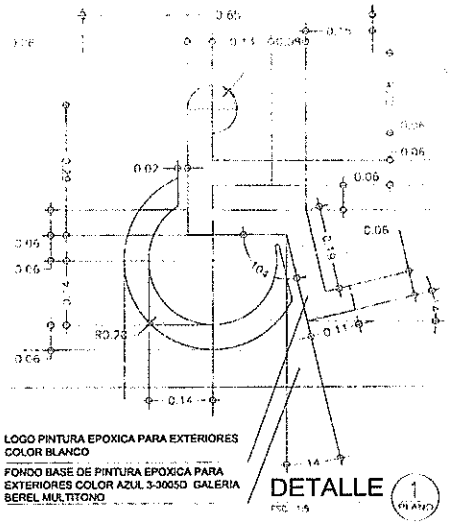

DETALLE (1 PLANO)

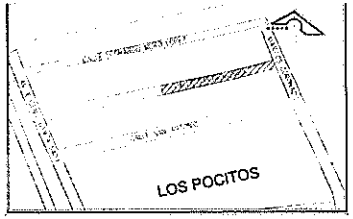

SIMBOLOGÍA


Notas para planos de señalización:

Nota 1: Se aplicará en todos los señalamientos horizontales pintura para trafico base solvente tipo alquidal de secado rápido, que cumpla con las especificaciones n-cmt-5-01-001/05, n-pry-car-10-01-002/13 de la SCT aplicadas al día de hoy.

Nota 2: Dosificación de micro esfera La cantidad de esferas de vidrio en la película de pintura en húmedo, según su tipo, será la que se indica en la Tabla

Cantidad de esferas de vidrio en la película de pintura en húmedo

Tipo de pintura	Espesor de la película de pintura en húmedo mm	cantidad de esferas kg/m2 Integradas	Sembradas, mínimo	Tipo de granulometría
Base solvente	0,38 a 0,50	—	0,330	I
Base agua	0,38 a 0,50	—	0,330	I o II
Termoplástica	1,50 a 3,00	0,57 a 0,69	0,330	II

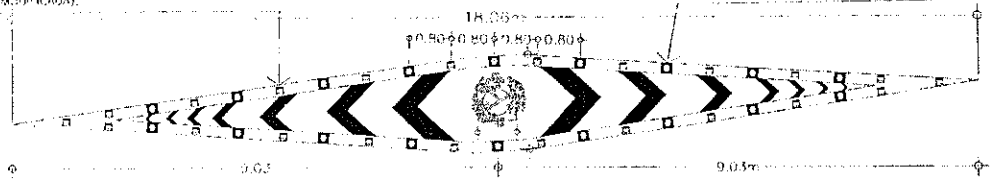

DETALLE CONSTRUCTIVO DE ARRIATE

SIN ESCALA

La Dirección de Planeación y Proyectos solo autoriza el proyecto ejecutivo, no es responsable de la correcta ejecución de la obra. Este documento no tiene validez si no presenta las firmas de los responsables para su autorización, así como los sellos respectivos.

PRESIDENTE MUNICIPAL
M.P.P. Leonardo Montañez Castro
ENCARGADA DE DESPACHO DE LA SOPMA
Arq. Gloria Guadalupe Castillo González

REV. FECHA OBSERVACIONES

Vo. Bo. DE LA DEPENDENCIA

RESP. DE PROY. EXTERNO | LOGO EXTERNO
CED. PROFESIONAL
PROYECTÓ | REVISÓ | AUTORIZÓ

Dirección de Planeación y Proyectos de Obra | Secretaría de Obras Públicas
PROYECTISTA: ING. DIEGO ROMO AGUILERA | COORDINADOR: ARQ. ALEJANDRO JAIME LEAL
JEFE DE DEP.: ARQ. J. JESÚS PALAFOX GONZÁLEZ | DIRECTOR: M. en ARQ. JOSÉ LUIS JIMÉNEZ GARCÍA

PROYECTO: CONSTRUCCIÓN DE CONCRETO HIDRAULICO CALLE SANTA MONICA (COL. LOS POCITOS)
UBICACIÓN: COLONIA LOS POCITOS TRAMO ENTRE AV. EUGENIO GARZA SADA Y MARCOS CORONADO
CONTENIDO: SEÑALIZACION HORIZONTAL

CLAVE	No. PLANO
SEÑ 01	11
FECHA: MAYO 2022	ESCALA: INDICADA
ACOTACIÓN: METROS	No. EXP.: E-000-22

Aguascalientes
LA CIUDAD DE TU VIDA