Aguascalientes
LA CIUDAD DE TU VIDA

Dirección de Programación Presupuestal
Núm. Oficio AMPP/0580/22
Aguascalientes, Ags. 8 de Diciembre del 2022
Asunto: Validación de Expediente Técnico

C.P. SERGIO ARTURO LOZANO GONZÁLEZ
SECRETARIO DE FINANZAS MUNICIPALES
P R E S E N T E

Con fundamento en los artículos 17 fracción XV, 60 fracción XVI y 76 fracción VI del Reglamento del Sistema Integral de Desarrollo Municipal y del Instituto Municipal de Planeación y Evaluación de Aguascalientes, hago referencia al oficio SOPMA/2737/2022 recibido por este Instituto el día 8 de Diciembre del 2022 por parte de la Secretaría de Obras Públicas Municipales, mediante el cual remiten el expediente técnico original de la siguiente obra para su análisis, registro y priorización, conforme al Programa Anual de Obra Pública y Programas Sociales para el ejercicio presupuestal 2022:

DEPENDENCIA EJECUTORA:	SOPMA
NOMBRE DE LA OBRA O PROYECTO:	PAVIMENTO HIDRÁULICO
UBICACIÓN:	CALLE EL GRULLO, TRAMO: ENTRE AMECA Y CALLE AMATITÁN, LA SOLEDAD, AGUASCALIENTES, AGS.
FONDO DE INVERSIÓN:	FONDO DE INFRAESTRUCTURA SOCIAL MUNICIPAL Y DE LAS DEMARCACIONES TERRITORIALES DEL DISTRITO FEDERAL
IMPORTE:	$2,262,515.63 (ET FINAL)
No. DE OBRA:	2022-FISMDF-0114-04-1101
MODALIDAD DE EJECUCIÓN:	CONTRATO
EJE:	MUNICIPIO SOBRESALIENTE
ESTRATEGIA:	OBRA PÚBLICA INTELIGENTE
POLITICA:	5.8.1.REHABILITACIÓN Y MANTENIMIENTO VIALIDADES, CAMINOS, CALLES, ÁREAS DE TERRACERÍA Y CAUCES (C

Al respecto, hago de su conocimiento que dicho expediente ha sido analizado en su integración técnica y documental, con base en el artículo 168 fracción I del Reglamento de la Ley de Obras Públicas y Servicios Relacionados para el Estado de Aguascalientes y sus Municipios.

Asimismo, le comento que este Instituto valida dicha obra acorde a lo establecido en los artículos 14, 22 párrafo segundo y 23 de la Ley de Obras Públicas y Servicios Relacionados para el Estado de Aguascalientes y sus Municipios, la cual se encuentra alineada al Plan de Desarrollo Municipal vigente, para dar cumplimiento a las metas establecidas en el mismo, y a los Lineamientos Generales para la Operación de este Fondo de Inversión, toda vez que la misma cuente con la autorización del CODEMUN. De igual manera, se hace de su conocimiento que deberá cumplir con lo establecido en los ordenamientos aplicables en lo que respecta al ejercicio, control e información de los recursos de este Fondo. Cabe hacer mención que los recursos solicitados para este proyecto de inversión, estarán sujetos a la disponibilidad presupuestal para el presente ejercicio fiscal que determine la Secretaría a su digno cargo. Sin otro particular por el momento, le envío un cordial saludo.

A T E N T A M E N T E

ARQ. AUSTRIA GABRIELA DÁVILA DE LA LLAVE
DIRECTORA GENERAL DEL IMPLAN

SEDR/ CAAR / JDBC
C.c.p. I.C. ING. MIGUEL ÁNGEL HUIZAR BOTELLO .- Secretaría de Obras Públicas Municipales .Para su conocimiento.
C.c.p. Archivo.

Instituto Municipal de Planeación y Evaluación de Aguascalientes
Antonio Acevedo Escobedo 103 A. Col. Centro
Aguascalientes. Ags. C.P. 20000
(449) 9101010 Ext. 3117
www.implanags.gob.mx

GOBIERNO MUNICIPAL DE AGUASCALIENTES

INSTITUTO MUNICIPAL DE PLANEACION

IMPLAN

ANÁLISIS INTEGRAL DE EXPEDIENTE TÉCNICO

No. DE OBRA (PAOP 2020):	2022-FISMDF-0114-04-1101	REGISTRO No.	287
OFICIO DE VALIDACIÓN:	AMPP/0580/22	FECHA RECIBIDO PARA REVISIÓN:	8 de Diciembre del 2022
PROGRAMA:	URBANIZACION MUNICIPAL	LOCALIDAD O COLONIA:	LA SOLEDAD
SUB-PROGRAMA:	0411- Calles y Caminos	DELEGACIÓN:	San Marcos
DEPENDENCIA:	Secretaría de Obras Públicas Municipales	MOD. DE EJECUCIÓN:	CONTRATO
NOMBRE DE LA OBRA:	PAVIMENTO HIDRÁULICO, CALLE EL GRULLO, TRAMO: ENTRE AMECA Y CALLE AMATITÁN		
FUENTE DE FINANCIAMIENTO:	FONDO DE INFRAESTRUCTURA SOCIAL MUNICIPAL Y DE LAS DEMARCACIONES TERRITORIALES DEL DISTRITO FEDERAL, FISMDF		
INVERSIÓN:	$2,262,515.63	CLASIFICACIÓN DE OBRA:	BIENES DE DOMINIO PUBLICA

TOTAL	FEDERAL	ESTATAL	MUNICIPAL	BENEFICIARIOS	OTROS	DIFERENCIA ENTRE MOD.
$2,262,515.63	$2,262,515.63	0.00	0.00	0.00	0.00	*$0,00*

TIPO DE EXPENDIENTE:	ET FINAL	AÑO: 2022	AÑO:	AÑO:		
AVANCES:	Financiero: 1 %	Físico: 1 %				
FECHA DE INICIO:	1 de Noviembre del 2022	FECHA DE TÉRMINO:	15 de Diciembre del 2022	REGISTRO SIMA:	114	

CHEK LIST DE LOS ANEXOS DEL EXPEDIENTE TÉCNICO

CÉDULA DE REGISTRO DE OBRA	✓
DICTAMEN DE FACTIBILIDAD	✓
MEMORIA DESCRIPTIVA	✓
PRESUPUESTO BASE	✓
FACTIBILIDAD VERIFICADA EN CAMPO	✓
CROQUIS DE UBICACIÓN (MACRO)	✓
CROQUIS DE UBICACIÓN (MACRO)	✓
PROGRAMA DE OBRA Y MONTOS MENSUALES	✓
PLANOS O ESTUDIOS TÉCNICOS	✓
PADRÓN DE BENEFICIARIOS	N/A
ACTA DE ACEPTACIÓN DEL PROYECTO	N/A
DICTAMEN DE IMPACTO AMBIENTAL	N/A
CONVENIO DE CONCERTACIÓN	N/A
ACTA CONSTITUTIVA	N/A

METAS		BENEFICIARIOS		PERIODO DE EJECUCION		OBRA PROPUESTA		CLAVE SISCO
UNIDAD DE MEDIDA	CANT	TIPO DE BENEFICIARIOS	CANTIDAD	FECHA DE INICIO	FECHA DE TERMINO	CONCEPTO	JORNALES A GENERAR	
M2	1050	Personas	120	2022-11-01	2022-12-15	Pavimentación	5882	2376

INCLUIDO EN PLAN DE DESARROLLO MUNICIPAL Y EL PROGRAMA ANUAL DE OBRA PÚBLICA

OBSERVACIONES:

SIN OBSERVACIONES

RECIBIO: ING. JOSÉ DAVID BURGUETE CLAUSTRO
Analista de Programación e Inversión de Obra Pública

8 de Diciembre del 2022
Fecha de validación

8 de Diciembre del 2022
Fecha de validación Expediente

PROCEDE Si ✓ No

H. AYUNTAMIENTO CONSTITUCIONAL DEL MUNICIPIO DE AGUASCALIENTES 2021-2024

AYUNTAMIENTO DE AGUASCALIENTES

CEDULA DE REGISTRO POR OBRA

Aguascalientes
LA CIUDAD DE TU VIDA

050400-001E00E05-05-2-2-1-00-1-E-0510-0-17-0114-21-2502-6144

2022-FISMDF-0114-04111101-060	Obra **PAVIMENTO HIDRÁULICO, CALLE EL GRULLO**
Tipo DEFINITIVO 1 2022 Folio SISCO **2376**	Ubic. TRAMO: ENTRE CALLE AMECA Y CALLE AMATITÁN, LA SOLEDAD Fracc. , Deleg. Pocitos

Ent. Ejecutora : **050400001E00E05**

Eje: **05**	MUNICIPIO SOBRESALIENTE
Finalidad: **2**	DESARROLLO SOCIAL
Función: **2**	VIVIENDA Y SERVICIOS A LA COMUNIDAD
Subfunción: **1**	URBANIZACIÓN
Tema: **00**	SIN TEMA
Cuenta del Gasto **1**	GASTO PROGRAMABLE
Clasif. Programatica: **E**	PRESTACIÓN DE SERVICIOS PÚBLICOS
Programa: **0510**	Movilidad Urbana
SubPrograma: **0**	SUBPROGRAMA GENÉRICO
Proyecto: **17**	
Tipo de Gasto: **21**	GASTO INVERSIÓN / OBRA PÚBLICA

I N V E R S I O N 2022

Municipal	2502	FONDO PARA LA INFRAESTRUCTURA SOCIAL MUNICIPAL Y DE LAS DEMARCACIONES TERRITORIALES DEL DISTRITO FEDERAL 2022	$2,262,515.63

Folio SIMA 114 Total $2,262,515.63

M E T A S

Unidad de Medida	Cantidad	Descripción
M2	1129.7	CONSTRUCCIÓN DE PAVIMENTO PAVIMENTO HIDRÁULICO, CALLE EL GRULLO

Inversión Ejercida Total al	31 de Diciembre de 2021	$0.00
Avance Fisico Acumulado al	31 de Diciembre de 2021	
Avance Fisico Acumulado Programado al	31 de Diciembre de 2022	

Fecha de Inicio 11 Nov 2022 Fecha de Terminación 20 Nov 2022

Jornales a Generar en 2022 5882

Modalidad de ejecución CONTRATO

Clasificación de la Obra Bienes de Dominio Público

Registro del Patrimonio: Obras del dominio público

OBRAS PÚBLICAS

Av. Aguascalientes Sur No. 2615
Fracc. Jardines de las Fuentes,
Aguascalientes, Ags. C.P. 20278

(449) 9 78 92 01, 06, 09

www.ags.gob.mx

GENERALES

Nombre del Proyecto : PAVIMENTO HIDRÁULICO, CALLE EL GRULLO

TRAMO: ENTRE CALLE AMECA Y CALLE AMATITÁN, LA SOLEDAD Fracc. , Deleg. Pocitos

Programa : 04 URBANIZACION MUNICIPAL

Subprograma : 11 Calles y caminos (1.- Construcción; 01- Concreto Hidraúlico)

Clave del Municipio : AGUASCALIENTES

Localidad :

Barrio, Colonia o Ejido : LA SOLEDAD Fracc.

Tipo de Obra :

DESCRIPCIÓN DEL PROYECTO:

PAVIMENTO HIDRÁULICO, CALLE EL GRULLO

PRELIMINARES Y DEMOLICIONES 1050.00 M2
EXCAVACIONES, ACAERREOS Y TERRACERÍAS 23,625.00 M3-KM
PAVIMENTO 1,129.70 M2
DENTELLONES DE CONCRETO 55.00 ML
GUARNICIONES 45.60 ML
BANQUETA Y RAMPA 73.40 M2
OBRA COMPLEMENTARIA 1.00 OBRA
LIMPIEZA 1,123.40 M2
SEÑALIZACIÓN HORIZONTAL 1.00 OBRA
SEÑALIZACIÓN VERTICAL 3.00 PZAS
LÍNEA DE ALCANTARILLADO 112.00 ML
DESCARGAS DOMICILIARIAS 7.00 PZAS
LÍNEA DE AGUA POTABLE 112.00 ML
TOMAS DOMICILIARIAS 13.00 PZAS

Beneficiarios (No. y Tipo) :

120	PERSONAS

Hombres: 60 Mujeres: 60

OBRAS PÚBLICAS

Los abajo firmantes, hacen constar que el presente proyecto :

PAVIMENTO HIDRÁULICO, CALLE EL GRULLO

TRAMO: ENTRE CALLE AMECA Y CALLE AMATITÁN, LA SOLEDAD Fracc. , Deleg. Pocitos

cumple con los Requisitos y Normas Técnicas establecidas por la Dependencia Normativa, por lo que es viable su ejecución. Comprometiéndose la misma a proporcionar la supervisión y asistencia técnica necesaria durante el proceso administrativo.

Por la Dependencia Ejecutora

Ing. Miguel Angel Huizar Botello
Secretario de Obras Públicas

Lic. Jaime Gallo Camacho
Secretario de Desarrollo Urbano

LUGAR :AGUASCALIENTES, AGS.

Av. Aguascalientes Sur No. 2615
Fracc. Jardines de las Fuentes,
Aguascalientes, Ags. C.P. 20278

(449) 9 78 92 01, 06, 09

www.ags.gob.mx

H. AYUNTAMIENTO CONSTITUCIONAL DEL MUNICIPIO DE AGUASCALIENTES 2021-2024

AYUNTAMIENTO DE AGUASCALIENTES

FACTIBILIDAD VERIFICADA EN CAMPO

Aguascalientes
LA CIUDAD DE TU VIDA

MUNICIPIO: AGUASCALIENTES

LOCALIZACION: TRAMO: ENTRE CALLE AMECA Y CALLE AMATITÁN, LA SOLEDAD Fracc. , Deleg. Pocitos

PROGRAMA: URBANIZACION MUNICIPAL

SUBPROGRAMA: Calles y caminos (1.- Construcción; 01- Concreto Hidraúlico)

OBRA A REALIZAR: PAVIMENTO HIDRÁULICO, CALLE EL GRULLO

DEPENDENCIA EJECUTORA: SECRETARÍA DE OBRAS PUBLICAS DEL MUNICIPIO DE AGUASCALIENTES

FORMA DE EJECUCION: CONTRATO

TIPO DE OBRA PROPUESTA:

CONDICIONES ACTUALES DE LA OBRA:

PAVIMENTO HIDRÁULICO, CALLE EL GRULLO

CARACTERISTICAS DE LA OBRA: Bueno

FACTIBILIDAD DE LA OBRA:

ESTA OBRA SE REQUIERE PARA EL BENEFICIO DE LA CIUDADANÍA

PROCEDE: SI [X] NO [ ]

REVISÓ: Jefa del Departamento de Expedientes Tecnicos y Costos

NOMBRE: Arq. Blanca Margarita Martinez Amador

FIRMA:

FECHA: 29 Nov 2022

SECRETARIA DE OBRAS PÚBLICAS

Av. Aguascalientes Sur No. 2615
Fracc. Jardines de las Fuentes,
Aguascalientes, Ags. C.P. 20278

(449) 9 78 92 01, 06, 09

www.ags.gob.mx

No. Folio SISCO 2376

H. AYUNTAMIENTO DE AGUASCALIENTES
SECRETARÍA DE OBRAS PÚBLICAS
DIRECCIÓN DE SUPERVISIÓN DE OBRA
LOCALIZACION

H. AYUNTAMIENTO CONSTITUCIONAL DEL MUNICIPIO DE AGUASCALIENTES 2021-2024

Aguascalientes LA CIUDAD DE TU VIDA

OBRA:	**PAVIMENTO HIDRÁULICO, CALLE EL GRULLO, TRAMO: ENTRE CALLE AMECA Y CALLE AMATITÁN, LA SOLEDAD Fracc.**					
NO. DE CONTR	FISMDF-0114-2022		CONTRATISTA:	**SERVICIOS Y TRANSPORTES ESPECIALES ROOT, S.A. DE C**		




ING. IVAN ALEJANDRO RUIZ ESPARZA SOLIS
SUPERVISOR DE OBRA.

H. AYUNTAMIENTO CONSTITUCIONAL DEL MUNICIPIO DE AGUASCALIENTES 2021-2024

H. AYUNTAMIENTO DE AGUASCALIENTES
SECRETARÍA DE OBRAS PÚBLICAS
DIRECCIÓN DE SUPERVISIÓN DE OBRA
LOCALIZACION

Aguascalientes
LA CIUDAD DE TU VIDA

OBRA:	PAVIMENTO HIDRÁULICO, CALLE EL GRULLO, TRAMO: ENTRE CALLE AMECA Y CALLE AMATITÁN, LA SOLEDAD Fracc.					
NO. DE CONTR	FISMDF-0114-2022		CONTRATISTA:	SERVICIOS Y TRANSPORTES ESPECIALES ROOT, S.A. DE C		

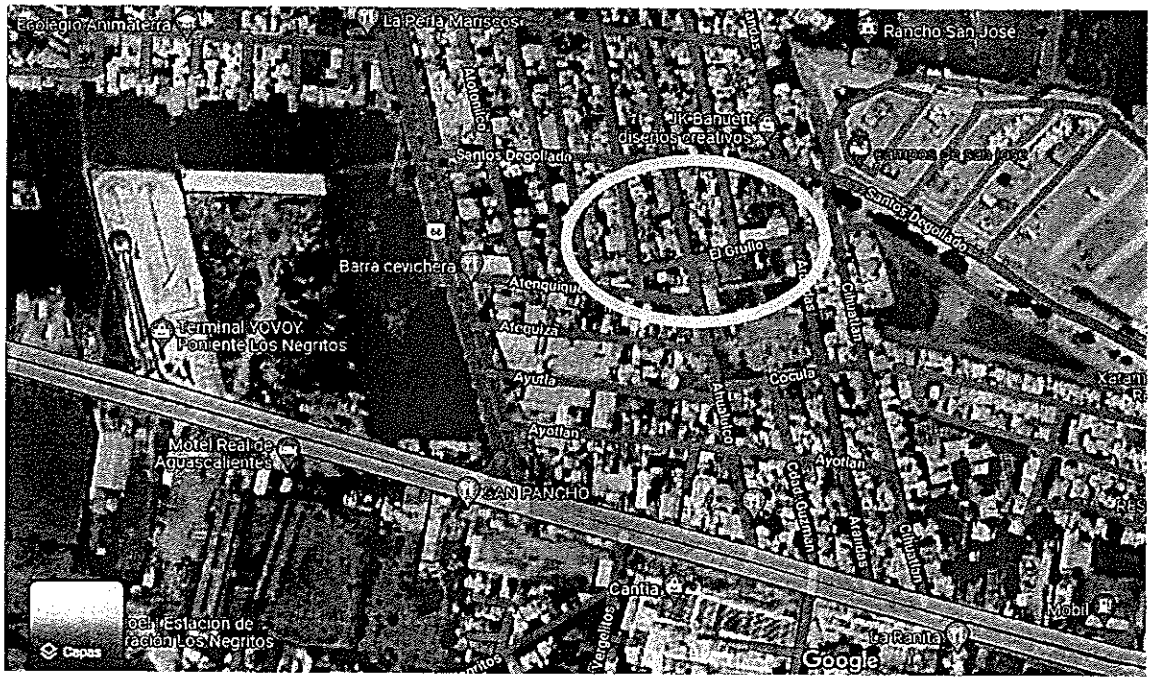

ING. IVAN ALEJANDRO RUIZ ESPARZA SOLIS
SUPERVISOR DE OBRA.

R03-POS-SOS-7.5.1-04	
REVISION:	00
ELAB.& INF. REVISIÓN RESPONSABLE:	SUPERVISOR DE OBRA
TIEMPO DE RET:	02 AÑOS

PROGRAMA DE OBRA DEFINITIVO

Aguascalientes
LA CIUDAD DE TU VIDA

H. AYUNTAMIENTO CONSTITUCIONAL DEL MUNICIPIO DE AGUASCALIENTES 2021-2024

No. DE CONTRATO : FISMDF-0114-2022

PROGRAMA: 04 URBANIZACION MUNICIPAL

No. OBRA Y NOMBRE DE LA OBRA: PAVIMENTO HIDRÁULICO, CALLE EL GRULLO, TRAMO: ENTRE CALLE AMECA Y CALLE AMATITÁN, LA SOLEDAD Fracc.

INICIO VIGENTE: 11-noviembre-22

TERMINO REAL: 28-noviembre-22

RECURSO 2022

CONCEPTO			1	2	3	4	5	6	7	8	9	10	11	12	13	14	15	16	PONDERACIÓN %	
			2022																FINANCIERO	FISICO
			OCTUBRE	NOVIEMBRE	DICIEMBRE	ENERO	FEBRERO	MARZO	ABRIL	MAYO	JUNIO	JULIO	AGOSTO	SEPTIEMBRE	OCTUBRE	NOVIEMBRE	DICIEMBRE	ENERO	%	%
DESCRIPCION	INVERSION																			
PAVIMENTO HIDRÁULICO, CALLE EL GRULLO, TRAMO: ENTRE CALLE AMECA Y CALLE AMATITÁN, LA SOLEDAD Fracc.																				
TRAMO: ENTRE CALLE AMECA Y CALLE AMATITÁN, LA SOLEDAD Fracc.																				
PAVIMENTO HIDRAULICO	$ 1,575,377.15	100			20 70 10														80.77	25.00
SEÑALIZACION	$ 32,905.74	100			50 30 10 10														1.69	33.33
HIDRAULICO SANITARIO	$ 342,161.63	100		20 20 20	20 20														17.54	41.67
		-																		
		-																		
		-																		
		-																	0.00	0.00
		-																		
		-																		
		-																		
		-																		
		-																		
		-																		
SUBTOTAL SIN IVA	$ 1,950,444.51		0 0 0 0	0 1 1 7	3 3 1 1	0 0 0 0	0 0 0 0	0 0 0 0	0 0 0 0	0 0 0 0	0 0 0 0	0 0 0 0	0 0 0 0	0 0 0 0	0 0 0 0	0 0 0 0	0 0 0 0	0 0 0 0		
AVACE SEMANAL %			0% 0% 0% 0%	0% 8% 8% 33%	56% 8% 2% 2%	100% 0% 0% 0%	100% 0% 0% 0%	100% 0% 0% 0%	100% 0% 0% 0%	100% 0% 0% 0%	100% 0% 0% 0%	100% 0% 0% 0%	100% 0% 0% 0%	100% 0% 0% 0%	100% 0% 0% 0%	100% 0% 0% 0%	100% 0% 0% 0%	100% 0% 0% 0%		
AVANCE SEMANAL ACUMULADO %			0% 0% 0% 0%	0% 8% 17% 33%	56% 63% 65% 67%	100% 100% 100% 100%	100% 100% 100% 100%	100% 100% 100% 100%	100% 100% 100% 100%	100% 100% 100% 100%	100% 100% 100% 100%	100% 100% 100% 100%	100% 100% 100% 100%	100% 100% 100% 100%	100% 100% 100% 100%	100% 100% 100% 100%	100% 100% 100% 100%	100% 100% 100% 100%	100.00	100.00
EJERCIDO SEMANAL $			- - - -	- 66,432.33 66,432.33 353,507.78	1,107,640.20 225,641.78 3,290.57 3,290.57	- - - -	- - - -	- - - -	- - - -	- - - -	- - - -	- - - -	- - - -	- - - -	- - - -	- - - -	- - - -	- - - -	$ 1,950,444.51	
EJERCIDO MENSUAL $			$0.00	$529,372.41	$1,430,072.11	$0.00	$0.00	$0.00	$0.00	$0.00	$0.00	$0.00	$0.00	$0.00	$0.00	$0.00	$0.00	$0.00	$ 312,071.12	IVA 16%
EJERCIDO MENSUAL ACUMULADO $			0.00	529,372.41	1,950,444.52	1,950,444.52	1,950,444.52	1,950,444.52	1,950,444.52	1,950,444.52	1,950,444.52	1,950,444.52	1,950,444.52	1,950,444.52	1,950,444.52	1,950,444.52	1,950,444.52	1,950,444.52		
EJERCIDO SEMANAL %			% % % %	% 3% 3% 17%	81% 11% 0% 0%	% % GRAN TOTAL EJERCIDO	
EJERCIDO MENSUAL %			0%	27%	73%	0%	0%	0%	0%	0%	0%	0%	0%	0%	0%	0%	0%	0%	$	2,262,515.63
EJERCIDO MENSUAL ACUMULADO %			0%	27%	100%	100%	100%	100%	100%	100%	100%	100%	100%	100%	100%	100%	100%	100%		

PRE

ING. IVAN ALEJANDRO RUIZ ESPARZA SOLIS
SUPERVISOR

PRESIDENCIA MUNICIPAL DE AGUASCALIENTES

FACTIBILIDAD VERIFICADA EN CAMPO

GENERALES

EJERCICIO:	2022 APROBACION No: 2022-FISMDF-0114-0411101-060
LOCALIDAD:	TRAMO: ENTRE CALLE AMECA Y CALLE AMATITÁN, LA SOLEDAD Fracc.
MUNICIPIO:	AGUASCALIENTES, Mpio.
TIPO DE INVERSION	FONDO PARA LA INFRAESTRUCTURA SOCIAL MUNICIPAL Y DE LAS DEMARCACIONES TERRITORIALES DEL DISTRITO FEDERAL (100%) (MUNICIPAL)
PROGRAMA:	04 URBANIZACION MUNICIPAL
SUB-PROGRAMA:	11 Calles y caminos Inciso 1 .Construcción; 01- Concreto Hidraúlico
OBRA A REALIZARSE:	PAVIMENTO HIDRÁULICO, CALLE EL GRULLO, TRAMO: ENTRE CALLE AMECA Y CALLE AMATITÁN, LA SOLEDAD Fracc.
DEPENDENCIA EJECUTORA:	SECRETARÍA DE OBRAS PÚBLICAS MUNICIPALES (S.O.P.M.A)
FORMACIÓN DE EJECUCION:	CONTRATO NO. DE CONTRATO: FISMDF-0114-2022
NOMBRE CONTRATISTA:	SERVICIOS Y TRANSPORTES ESPECIALES ROOT, S.A. DE C.V.
REPRESENTANTE:	C. JUAN PABLO RAMIREZ RANGEL
MONTO CONT. ORIGEN	$ 2,143,683.60 ANTICIPO: $ 924,001.55 PLAZO 40 DIAS
1A AMPLIACION $:	$ 118,832.03 1 AMPL DIAS
2A AMPLIACION $:	2 AMPL DIAS
FIRMA CONTRATO:	04/11/2022
INICIO CONT: dd/mm/aa	05/11/2022 TERMINO CONT: 14/11/2022
INICIO REAL: dd/mm/aa	11/11/2022 TERMINO REAL: 20/11/2022

TIPO DE OBRA PROPUESTA

NUEVA CREACIÓN	X	CONSOLIDACIÓN	
COMPLEMENTARIA		AMPLIACIÓN	
REHABILITACIÓN		EQUIPAMIENTO	

CARACTERÍSTICAS DE LA OBRA:

FORMACION Y COMPACTACION DE SUB-RASANTE, SUB-BASE Y BASE HIDRAULICA
PAVIMENTO HIDRAULICO A BASE CONCRETO PREMEZCLADO MR=38 KG/CM2
RED DE ALCANTARILLADO PVC SERIE 20 RED DE AGUA POTABLE PVC HIDRAULICO RD-26
CONSTRUCCION DE BANQUETAS RAMPAS Y GUARNICIONES

CONDICIONES ACTUALES DE LA OBRA: (SELECCIONAR UNO OBLIGATORIO)

BUEN ESTADO X REGULAR PESIMO ESTADO

FACTIBILIDAD DE LA OBRA: (CONDICIONES ACTUALES DE LA OBRA)

ESTA OBRA SE ENCUENTRA EN CONDICIONES PARA OPERARSE

PROCEDE: SI: X NO:
MARQUE SOLO UNA

ING. IVAN ALEJANDRO RUIZ ESPARZA SOLIS
SUPERVISOR

PRESIDENCIA MUNICIPAL DE AGUASCALIENTES

FACTIBILIDAD VERIFICADA EN CAMPO

GENERALES

LOCALIDAD: TRAMO: ENTRE CALLE AMECA Y CALLE AMATITÁN, LA SOLEDAD Fracc.
MUNICIPIO: AGUASCALIENTES, Mpio.
PROGRAMA: 04 URBANIZACION MUNICIPAL
SUB-PROGRAMA: 11 Calles y caminos Inciso 1 .Construcción; 01- Concreto Hidraúlico
OBRA A REALIZARSE: PAVIMENTO HIDRÁULICO, CALLE EL GRULLO, TRAMO: ENTRE CALLE AMECA Y CALLE AMATITÁN, LA SOLEDAD Fracc.

DEPENDENCIA EJECUTORA: SECRETARÍA DE OBRAS PÚBLICAS MUNICIPALES (S.O.P.M.A)
FORMACIÓN DE EJECUCION: CONTRATO

TIPO DE OBRA PROPUESTA

NUEVA CREACIÓN	X	CONSOLIDACIÓN	
COMPLEMENTARIA		AMPLIACIÓN	
REHABILITACIÓN		EQUIPAMIENTO	

CARACTERÍSTICAS DE LA OBRA:

FORMACION Y COMPACTACION DE SUB-RASANTE, SUB-BASE Y BASE HIDRAULICA
PAVIMENTO HIDRAULICO A BASE CONCRETO PREMEZCLADO MR=38 KG/CM2
RED DE ALCANTARILLADO PVC SERIE 20 RED DE AGUA POTABLE PVC HIDRAULICO RD-26
CONSTRUCCION DE BANQUETAS RAMPAS Y GUARNICIONES

CONDICIONES ACTUALES DE LA OBRA:

BUEN ESTADO:	X	REGULAR:		PESIMO ESTADO:	

FACTIBILIDAD DE LA OBRA:

ESTA OBRA SE ENCUENTRA EN CONDICIONES PARA OPERARSE

PROCEDE	**SI:**	X	**NO:**		

ING. IVAN ALEJANDRO RUIZ ESPARZA SOLIS
SUPERVISOR

H. AYUNTAMIENTO CONSTITUCIONAL DEL MUNICIPIO DE AGUASCALIENTES 2021-2024

PRESUPUESTO MODIFICADO

Aguascalientes

Obra: **PAVIMENTO HIDRÁULICO, CALLE EL GRULLO**

Ubicación: **TRAMO: ENTRE CALLE AMECA Y CALLE AMATITÁN, LA SOLEDAD Fracc.**

Contratista: **SERVICIOS Y TRANSPORTES ESPECIALES ROOT, S.A. DE C.V. (75)**

No.	Concepto	Unidad	Cantidad	Precio Unitario	Importe Total
	GRUPO: **PAVIMENTO HIDRAULICO**				
	PARTIDA: **PRELIMINARES Y DEMOLICIONES**				
1	LIMPIA, TRAZO Y NIVELACION EN PAVIMENTOS, CALLES Y VIALIDADES CON EQUIPO TOPOGRAFICO, INCLUYE: EJES, BANCO DE NIVEL, RENIVELACIONES LAS VECES NECESARIAS, CORRECCION DE RASANTE A PUNTOS OBLIGADOS (AUTORIZADOS POR LA SUPERVISION), ESTACAS, VARILLAS, MANO DE OBRA CALIFICADA, HERRAMIENTA NECESARIA, EQUIPO DE PRECISION CALIBRADO, TRABAJO TERMINADO.P.U.O.T.	M2	1050	$6.21	$6,520.50
2	SONDEO A MANO O A MAQUINA PARA LOCALIZACION DE TUBERIAS CUALQUIER PROFUNDIDAD Y MATERIAL PARA VERIFICAR LA CALIDAD DE LAS INSTALACIONES HIDRAULICO SANITARIAS CUIDANDO NO DAÑARLAS PARA NO INTERFERIR EN LOS SERVICIOS, INCLUYE: EXCAVACION, EQUIPO, MANO DE OBRA, REPORTE A LA SUPERVISION, RELLENOS, COMPACTACIONES, TRABAJO TERMINADO.	SONDE	4	$1,510.33	$6,041.32
3	CORTE CON DISCO DIAMANTADO DE 14" EN PISOS DE CONCRETO ASFALTICO DE HASTA 8.00 cm. DE PROFUNDIDAD. INCLUYE: TRAZO, EQUIPO Y OPERACION, LIMPIEZAS.	ML	78	$63.55	$4,956.90
4	DEMOLICION PARCIAL DE PAVIMENTO HIDRAULICO Y/O ASFALTICO DE HASTA 15 CM. DE ESPESOR PROMEDIO EN PAVIMENTOS Y (BANQUETAS, LOSAS DIAMANTE Y CAJAS DE VALVULAS, TOPES) CON O SIN ARMADO DE ACERO, SIN RECUPERACION, MUROS, MOJONERAS, ANCLAJES, ETC, DE FORMA MANUAL Y MECANICA, INCLUYE ACARREO DE MATERIAL AL LUGAR DE ACOPIO, HERRAMIENTA NECESARIA Y TODO LO NECESARIO PARA SU CORRECTA EJECUCION, LIMPIEZA, TRABAJO TERMINADO	M3	42.66	$145.60	$6,211.30
5	DEMOLICION CONTROLADA DE CONCRETO HIDRAULICO EN DENTELLONES Y GUARNICIONES DE 15 x 20 x 40 CM. DE FORMA MANUAL Y MECÁNICA, INCLUYE: CORTES CON DISCO, ACARREO DEL MATERIAL AL LUGAR DE ACOPIO PARA SU CARGA Y ACARREO FUERA DE LA OBRA.	ML.	45.6	$90.86	$4,143.22
6	DEMOLICION A MANO DE REGISTRO SANITARIO DE 0.40x0.60x HASTA 1.25 m (MEDIDAS INTERIORES) DE TABIQUE ROJO RECOCIDO (14 cm DE ESPESOR),INCLUYE: ACARREOS DENTRO DE LA OBRA, LIMPIEZAS.	PZA	3	$464.45	$1,393.35
7	DESPALME DE TERRENO CON MAQUINA CUALQUIER SECCIÓN HASTA EL NIVEL O PROFUNDIDAD QUE MARQUE SUPERVISIÓN EN MATERIAL TIPO 1 TODAS LAS ZONAS. INCLUYE: ACARREOS LOCALES a 1 estacion Y LIMPIEZAS.	M3	105	$64.93	$6,817.65
8	CARGA MECANICA Y ACARREO DE MATERIAL PRODUCTO DE EXCAVACION Y DEMOLICION EN CAMION DE VOLTEO AL 1er. KM, VOLUMEN MEDIDO COMPACTO.	M3	152.43	$29.77	$4,537.84
9	ACARREO DE MATERIAL PRODUCTO DE EXCAVACION Y/O DEMOLICION EN CAMION DE VOLTEO A KILOMETROS SUBSECUENTES, AL TIRADERO OFICIAL AUTORIZADO MAS CERCANO AUTORIZADO POR LA SUPERVISION, VOLUMEN MEDIDO COMPACTO.	M3-KM	4572.99	$9.50	$43,443.40
				Totales por Partida	**$84,065.48**
	PARTIDA: **EXCAVACIONES, ACARREOS Y TERRACERIAS**				
10	EXCAVACION EN CORTE CON MAQUINA HASTA UNA PROFUNDIDAD DE 75 CM, EN MATERIAL TIPO II, INCLUYE: AFLOJE Y EXTRACCION DE MATERIAL, ACARREOS AL LUGAR DE ACOPIO PARA SU CARGA Y ACARREO FUERA DE LA OBRA, VOLUMEN MEDIDO COMPACTO.	M3	825	$37.98	$31,333.50
11	COMPACTACION DE TERRENO NATURAL AL 90% DE SU P.V.S.M EN SU COMPACTACION., INCLUYE ESCARIFICADO, TENDIDO, HOMOGENIZADO, HUMEDECIDO OPTIMO NIVELADO Y COMPACTADO EN CAPAS DE 20 CM, CALIDAD Limite liquido máximo 50%, Valor de Soporte California (CBR) mínimo 15%, Expansión máxima 5%, Grado de Compactación minimo 90% ± 2, Y TODO LO NECESARIO PARA SU CORRECTA EJECUCION,	M2	1100	$18.11	$19,921.00

Obra: **PAVIMENTO HIDRÁULICO, CALLE EL GRULLO**

Ubicación: **TRAMO: ENTRE CALLE AMECA Y CALLE AMATITÁN, LA SOLEDAD Fracc.**

Contratista: **SERVICIOS Y TRANSPORTES ESPECIALES ROOT, S.A. DE C.V. (75)**

No.	Concepto	Unidad	Cantidad	Precio Unitario	Importe Total
	GRUPO: **PAVIMENTO HIDRAULICO**				
	PARTIDA: **EXCAVACIONES, ACARREOS Y TERRACERIAS**				
12	FORMACION Y COMPACTACION DE SUB-RRASANTE, CON EL USO DE EQUIPO MAYOR, HASTA ALCANZAR EL 100% AASHTO MODIFICADA. EN CAPAS DE 20 CM MAXIMO, INCLUYE: SUMINISTRO DE MATERIAL DE BANCO QUE CUMPLA CON LA NORMA, HUMEDAD OPTIMA Y TODO LO NECESARIO PARA SU CORRECTA COLOCACION, EL MATERIAL DEBERA CUMPLIR CON UN C.B.R. DEL 60% PARA LO CUAL EL CONTRATISTA DEBERA PROPONER UN BANCO DE MATERIAL Y UN FRENTE, DEBERA PRESENTAR EL ESTUDIO DE CALIDAD QUE AVALE EL CUMPLIMIENTO AL 100 % DE LA NORMA Y DEMAS CARACTERISTICAS SOLICITADAS, P.U.O.T.	M3	330	$288.05	$95,056.50
13	FORMACION Y COMPACTACION DE SUB-BASE PARA MAS DE UN MILLON DE EJES EQUIVALENTES, CON EL USO DE EQUIPO MAYOR, HASTA ALCANZAR EL 100% AASHTO MODIFICADA. EN CAPAS DE 20 CM MAXIMO, INCLUYE: SUMINISTRO DE MATERIAL DE BANCO QUE CUMPLA CON LA NORMA, HUMEDAD OPTIMA Y TODO LO NECESARIO PARA SU CORRECTA COLOCACION, EL MATERIAL DEBERA CUMPLIR CON UN C.B.R. DEL 60% PARA LO CUAL EL CONTRATISTA DEBERA PROPONER UN BANCO DE MATERIAL Y UN FRENTE, DEBERA PRESENTAR EL ESTUDIO DE CALIDAD QUE AVALE EL CUMPLIMIENTO AL 100 % DE LA NORMA N-CMT-4-02-001. Y DEMAS CARACTERISTICAS SOLICITADAS, P.U.O.T.	M3	210	$288.05	$60,490.50
14	FORMACION Y COMPACTACION DE BASE HIDRAULICA PARA MAS DE UN MILLON DE EJES EQUIVALENTES DE 20 CMS. DE ESPESOR, PARA CARPETA DE CONCRETO HIDRAULICO, CON MATERIAL 100% TRITURADO (SOLAMENTE) 1 1/2" A FINOS QUE CUMPLA CON LA NORMA COMPACTADA AL 100 % DE PRUEBA AASHTO. COMBINANDO COMPACTADOR DE RODILLO EN BAJA Y MUERTO Y LLANTEO CON EQUIPO PESADO (CAMION DE VOLTEO CARGADO AL MAXIMO), INCLUYE HOMOGENEIZADO, TENDIDO, COMPACTADO, E INCORPORACION DE AGUA HASTA ALCANZAR LA HUMEDAD OPTIMA Y NIVELACIONES.	M3	210	$684.66	$143,778.60
15	CARGA MECANICA Y ACARREO DE MATERIAL PRODUCTO DE EXCAVACION Y DEMOLICION EN CAMION DE VOLTEO AL 1er. KM, VOLUMEN MEDIDO COMPACTO.	M3	787.5	$29.77	$23,443.88
16	ACARREO DE MATERIAL PRODUCTO DE EXCAVACION Y/O DEMOLICION EN CAMION DE VOLTEO A KILOMETROS SUBSECUENTES, AL TIRADERO OFICIAL AUTORIZADO MAS CERCANO AUTORIZADO POR LA SUPERVISION, VOLUMEN MEDIDO COMPACTO.	M3-KM	23625	$9.50	$224,437.50
			Totales por Partida		**$598,461.47**
	PARTIDA: **PAVIMENTO**				
17	CONSTRUCCION DE PAVIMENTO HIDRAULICO A BASE DE CONCRETO PREMEZCLADO MR=38 KG/CM2 TMA 1 1/2" GRAVA TRITURADA, REVENIMIENTO DE 6 A 8 CM FRAGUADO NORMAL DE 15 CM DE ESPESOR MODULADO EN LOSAS DE 3.5 MTS. (ANCHO) X 3.5 MTS (LARGO) COMO MAXIMO, CON CORTES EN LAS LOSAS DE 1/3 DEL ESPESOR DE LA LOSA (5 CM) Y SELLADO CON COLA DE RATA Y MATERIAL ELASTOMERICO Y TIRA PREFORMADA (FOAMTECH DE 1/2X15) EN JUNTAS Y CORTES LONGITUDINALES Y TRANSVERSALES, ASI COMO EL APROCHE CON GUARNICION Y DENTELLON. INCLUYE: CIMBRADO, COLADO, VIBRADO CON INMERSION Y REGLA VIBRATORIA, DESCIMBRADO, REGLEADO FINAL, ACABADO CEPILLO DE ALUMINIO Y CON DOBLADOR, CALAFATEO, CURADO CON MEMBRANA BASE AGUA Y TODO LO NECESARIO PARA SU CORRECTA COLOCACION, P.U.O.T.	M2	1129.70082	$601.48	$679,492.45

Obra: **PAVIMENTO HIDRÁULICO, CALLE EL GRULLO**

Ubicación: **TRAMO: ENTRE CALLE AMECA Y CALLE AMATITÁN, LA SOLEDAD Fracc.**

Contratista: **SERVICIOS Y TRANSPORTES ESPECIALES ROOT, S.A. DE C.V. (75)**

No.	Concepto	Unidad	Cantidad	Precio Unitario	Importe Total
	GRUPO: **PAVIMENTO HIDRAULICO**				
	PARTIDA: **PAVIMENTO**				
18	SUMINISTRO Y COLOCACION DE RELLENO PARA JUNTAS DE EXPANSION A BASE DE ESPUMA DE POLIETILENO DE CELDAS CERRADAS (FOAMTECH) DE 1/2" DE ESPESOR Y 20 CM DE ALTURA DE ACUERDO AL DISEÑO ANEXO EN PLANOS, INCLUYE: MATERIAL, SELLADOR AUTONIVELANTE,MANO DE OBRA, CORTES, AJUSTES, DESPERDICIOS, ACARREO, FLETES DENTRO Y FUERA DE LA OBRA DE ACUERDO A ESPECIFICACIONES DE CONTROL DE CALIDAD (LA FICHA TECNICA DEL FABRICANTE DEBERA CUMPLIR CON LAS ESPECIFICACIONES DE LA NORMA)	ML	239.96	$114.24	$27,413.03
				Totales por Partida	**$706,905.48**
	PARTIDA: **DENTELLONES DE CONCRETO**				
19	EXCAVACION A MANO EN MATERIAL TIPO B DE 0.00 A 2.00 M DE PROFUNDIDAD, INCLUYE: TRASPALEO VERTICAL, AFINE DE TALUDES CONSERVACION DE LA EXCAVACION Y ACARREO DE MATERIAL AL LUGAR DE ACOPIO PARA SU POSTERIOR CARGA Y ACARREO FUERA DE LA OBRA.	M3	5.55	$289.77	$1,608.22
20	COMPACTACION DE TERRENO NATURAL AL 90% DE SU P.V.S.M EN SU COMPACTACION., INCLUYE ESCARIFICADO, TENDIDO, HOMOGENIZADO, HUMEDECIDO OPTIMO NIVELADO Y COMPACTADO EN CAPAS DE 20 CM, CALIDAD Limite liquido máximo 50%, Valor de Soporte California (CBR) mínimo 15%, Expansión máxima 5%, Grado de Compactación minimo 90% ± 2, Y TODO LO NECESARIO PARA SU CORRECTA EJECUCION,	M2	27.5	$18.11	$498.02
21	RELLENO COMPACTADO AL 90% CON MATERIAL DE BANCO EN CAPAS DE 20 CM UTILIZANDO BAILARINA. INCLUYE: SUMINISTRO DE TEPETATE (MATERIAL DE BANCO) EN LA OBRA, ABUNDAMIENTO, ACARREOS DENTRO DE LA OBRA, CRIBADO, RETIRO DE MATERIAL, MANO DE OBRA Y EQUIPO, LIMPIEZAS, TRABAJO TERMINADO.	M3	3.3	$304.91	$1,006.20
22	CARGA MECANICA Y ACARREO DE MATERIAL PRODUCTO DE EXCAVACION Y DEMOLICION EN CAMION DE VOLTEO AL 1er. KM, VOLUMEN MEDIDO COMPACTO.	M3	2.2	$29.77	$65.49
23	ACARREO DE MATERIAL PRODUCTO DE EXCAVACION Y/O DEMOLICION EN CAMION DE VOLTEO A KILOMETROS SUBSECUENTES, AL TIRADERO OFICIAL AUTORIZADO MAS CERCANO AUTORIZADO POR LA SUPERVISION, VOLUMEN MEDIDO COMPACTO.	M3-KM	66	$9.50	$627.00
24	CONSTRUCCION DE DENTELLON RECTO Y/O CURVO 20-20X40 CM DE SECCION, CON CONCRETO PREMEZCLADO MR=38 KGF/CM2, TMA 1 1/2", R.N. REVENIMIENTO NORMAL DE 10+-2 CM, GRAVA TRITURADA, ACABADO CON DOBLADOR Y PULIDO. INCLUYE: TRAZO, NIVELACION, CIMBRADO, COLADO, VIBRADO, DESCIMBRADO, JUNTA A BASE DE ESPUMA DE POLIETILENO DE CELDAS CERRADAS DE 1/2" EN JUNTAS FRIAS LONGITUDINALES NO MAYOR A 30 MTS CORTE TRANSVERSAL CON CORTADORA A 1/3 DE SU ESPESOR MAXIMO @ 3 MTS, RELLENO PREFORMADOY SELLADOR AUTONIVELANTE ASI COMO DE AISLAMIENTO CON OTRO ELEMENTO, Y CURADO CON MEMBRANA QUIMICA APLICADA CON ASPERSOR Y LIMPIEZA, REMATE CON PAVIMENTO EXISTENTE DEL MISMO MATERIAL Y TIPO, TRABAJO TERMINADO P.U.O.T.	ML	55	$391.39	$21,526.45
				Totales por Partida	**$25,331.40**

Obra: **PAVIMENTO HIDRÁULICO, CALLE EL GRULLO**

Ubicación: **TRAMO: ENTRE CALLE AMECA Y CALLE AMATITÁN, LA SOLEDAD Fracc.**

Contratista: **SERVICIOS Y TRANSPORTES ESPECIALES ROOT, S.A. DE C.V. (75)**

No.	Concepto	Unidad	Cantidad	Precio Unitario	Importe Total
	GRUPO: **PAVIMENTO HIDRAULICO**				
	PARTIDA: **GUARNICIONES**				
25	EXCAVACION A MANO EN MATERIAL TIPO B DE 0.00 A 2.00 M DE PROFUNDIDAD, INCLUYE: TRASPALEO VERTICAL, AFINE DE TALUDES CONSERVACION DE LA EXCAVACION Y ACARREO DE MATERIAL AL LUGAR DE ACOPIO PARA SU POSTERIOR CARGA Y ACARREO FUERA DE LA OBRA.	M3	2.74	$289.77	$793.97
26	COMPACTACION DE TERRENO NATURAL AL 90% DE SU P.V.S.M EN SU COMPACTACION., INCLUYE ESCARIFICADO, TENDIDO, HOMOGENIZADO, HUMEDECIDO OPTIMO NIVELADO Y COMPACTADO EN CAPAS DE 20 CM, CALIDAD Limite liquido máximo 50%, Valor de Soporte California (CBR) mínimo 15%, Expansión máxima 5%, Grado de Compactación minimo 90% ± 2, Y TODO LO NECESARIO PARA SU CORRECTA EJECUCION,	M2	18.24	$18.11	$330.33
27	CONSTRUCCION DE GUARNICION RECTA Y/O CURVA TRAPEZOIDAL 15-20X40 CM DE SECCION CON CONCRETO PREMEZCLADO MR=38 KGF/CM2, R.N.REVENIMIENTO DE 8 A 10 CM, T.M.A. 3/4", GRAVA TRITURADA, ACABADO PULIDO EN PARTE DE SUPERIOR Y DOBLADOR EN ARISTAS, INCLUYE: COMPACTADO DE PLANTILLA, CIMBRADO, COLADO, VIBRADO, ACABADO, DESCIMBRADO, ALINEADO, NIVELADO, Y CURADO EN SU PARTE SUPERIOR CON MEMBRANA BASE AGUA A RAZON DE 1 LTO/M2, JUNTA DE AISLAMIENTO LONGITUDINAL AL COMBINAR CON OTRO ELEMENTO Y TRANSVERSAL @ 30 MT MAXIMO, SELLADO CON SELLADOR AUTONIVELANTE LONGITUDINAL, TRABAJO TERMINADO, .P.U.O.T.	ML	45.6	$277.09	$12,635.30
28	RELLENO COMPACTADO AL 90% CON MATERIAL DE BANCO EN CAPAS DE 20 CM UTILIZANDO BAILARINA. INCLUYE: SUMINISTRO DE TEPETATE (MATERIAL DE BANCO) EN LA OBRA, ABUNDAMIENTO, ACARREOS DENTRO DE LA OBRA, CRIBADO, RETIRO DE MATERIAL, MANO DE OBRA Y EQUIPO, LIMPIEZAS, TRABAJO TERMINADO.	M3	1.37	$304.91	$417.73
29	CARGA MECANICA Y ACARREO DE MATERIAL PRODUCTO DE EXCAVACION Y DEMOLICION EN CAMION DE VOLTEO AL 1er. KM, VOLUMEN MEDIDO COMPACTO.	M3	1.37	$29.77	$40.78
30	ACARREO DE MATERIAL PRODUCTO DE EXCAVACION Y/O DEMOLICION EN CAMION DE VOLTEO A KILOMETROS SUBSECUENTES, AL TIRADERO OFICIAL AUTORIZADO MAS CERCANO AUTORIZADO POR LA SUPERVISION, VOLUMEN MEDIDO COMPACTO.	M3-KM	41.04	$9.50	$389.88
				Totales por Partida	**$14,607.99**
	PARTIDA: **BANQUETA Y RAMPA**				
31	LIMPIA, TRAZO Y NIVELACION EN PAVIMENTOS, CALLES Y VIALIDADES CON EQUIPO TOPOGRAFICO, INCLUYE: EJES, BANCO DE NIVEL, RENIVELACIONES LAS VECES NECESARIAS, CORRECCION DE RASANTE A PUNTOS OBLIGADOS (AUTORIZADOS POR LA SUPERVISION), ESTACAS, VARILLAS, MANO DE OBRA CALIFICADA, HERRAMIENTA NECESARIA, EQUIPO DE PRECISION CALIBRADO, TRABAJO TERMINADO.P.U.O.T.	M2	73.4	$6.21	$455.81
32	EXCAVACION A MAQUINA Y/O A MANO EN MATERIAL TIPO II, EN SECO O PRESENCIA DE AGUA, INCLUYE. CORTE DE RAIZ DE CUALQUIER TAMAÑO Y GROSOR, HASTA UNA PROFUNDIDAD DE 40 CM DESPUES DE DESMONTE, DESPALME Y/O DEMOLICION DE SUPERFICIE O ELEMENTO ESTRUCTURAL O DE ACABADO, PROTECCION DE AREAS ADYACENTES, SIN DAÑAR AREAS ALEDAÑAS, CARGA Y ACARREO A TIRADERO OFICIAL, CONSERVACION DE LA MISMA, TRABAJO TERMINADO, LIMPIEZAS.	M3	14.68	$54.61	$801.67
33	CARGA MECANICA Y ACARREO DE MATERIAL PRODUCTO DE EXCAVACION Y DEMOLICION EN CAMION DE VOLTEO AL 1er. KM, VOLUMEN MEDIDO COMPACTO.	M3	14.68	$29.77	$437.02

Obra: **PAVIMENTO HIDRÁULICO, CALLE EL GRULLO**

Ubicación: **TRAMO: ENTRE CALLE AMECA Y CALLE AMATITÁN, LA SOLEDAD Fracc.**

Contratista: **SERVICIOS Y TRANSPORTES ESPECIALES ROOT, S.A. DE C.V. (75)**

No.	Concepto	Unidad	Cantidad	Precio Unitario	Importe Total
	GRUPO: **PAVIMENTO HIDRAULICO**				
	PARTIDA: **BANQUETA Y RAMPA**				
34	ACARREO DE MATERIAL PRODUCTO DE EXCAVACION Y/O DEMOLICION EN CAMION DE VOLTEO A KILOMETROS SUBSECUENTES, AL TIRADERO OFICIAL AUTORIZADO MAS CERCANO AUTORIZADO POR LA SUPERVISION, VOLUMEN MEDIDO COMPACTO.	M3-KM	440.4	$9.50	$4,183.80
35	COMPACTACION POR MEDIOS MECANICOS DEL TERRENO NATURAL AL 95% DE SU PVSM EN UN ESPESOR DE 20 cm. INCLUYE: ESCARIFICACION, MANIOBRAS, HUMEDECIDO, SELECCION DE MATERIAL, ACARREOS DENTRO DE LA OBRA, MEDIDO COMPACTO, LIMPIEZAS, Y TODO LO NECESARIO PARA SU CORRECTA APLICACION, TRABAJO TERMINADO.	M2	73.4	$21.01	$1,542.13
36	RELLENO COMPACTADO AL 90% CON MATERIAL DE BANCO EN CAPAS DE 20 CM UTILIZANDO BAILARINA. INCLUYE: SUMINISTRO DE TEPETATE (MATERIAL DE BANCO) EN LA OBRA, ABUNDAMIENTO, ACARREOS DENTRO DE LA OBRA, CRIBADO, RETIRO DE MATERIAL, MANO DE OBRA Y EQUIPO, LIMPIEZAS, TRABAJO TERMINADO.	M3	14.68	$304.91	$4,476.08
37	SUMINISTRO Y COLOCACION DE HULE DE POLIETILENO CAL 600 PARA IMPERMEABILIZAR, INCLUYE: SUMINISTRO DEL MATERIAL A LA OBRA, MANO DE OBRA Y TODO LO NECESARIO PARA SU CORRECTA COLOCACION, P.U.O.T. SEGUN FICHA TECNICA FT-206	M2	73.4	$20.18	$1,481.21
38	CONSTRUCCION DE BANQUETA DE 10 CM DE ESPESOR A BASE DE CONCRETO PREMEZCLADO F'C=150 KG/CM2, T.M.A. 3/4", R.N. GRAVA TRITURADA, REVENIMIENTI DE 10+-2 CM, ACABADO RAYADO FINO CON BROCHA DE PELO, JUNTAS FRIAS CON DOBLADOR DE 2" SECCION DE LOSAS COMO INDIQUE PROYECTO, INCLUYE: JUNTA A BASE DE ESPUMA DE POLIETILENO DE CELDAS CERRADAS DE 1/2" EN JUNTAS FRIAS LONGITUDINALES CON MUROS Y TRANSVERSALES DEL ELEMENTO, ASI COMO SU UNION CON ELEMENTOS VIEJOS O CAMBIO DE ELEMENTO, CIMBRADO, COLADO, DESCIMBRADO, CORTES CON CORTADORA DE DISCO, SELLADO DE CORTES CON SELLADOR AUTONIVELANTE Y TIRA DE RELLENO PREFORMADA NO ADHERENTE DE 1/8" (EN TODAS LAS JUNTAS DE CONTRACCCION Y CONSTRUCCION TRANSVERSALES), CURADO CON MEMBRANA QUIMICA APLICADA CON ASPERSOR, TRABAJO TERMINADO	M2	73.4	$392.15	$28,783.81
				Totales por Partida	**$42,161.55**
	PARTIDA: **OBRA COMPLEMENTARIA**				
39	RENIVELACION DE POZO DE VISITA HASTA 0.50 m DE ALTURA. INCLUYE: RETIRO SIN RECUPERACION DE BROCAL EXISTENTE, NIVELADO CON TABIQUE ROJO RECOCIDO 7X14X28, ASENTADO CON MORTERO CEMENTO-ARENA 1:3 DE 28 cm DE ESPESOR, APLANADO CON MORTERO CEMENTO-ARENA 1:3, PLOMEADO, NIVELADO, DEMOLICIONES, CARGAS Y ACARREOS DENTRO DE LA OBRA, LIMPIEZAS	PZA	1	$6,408.90	$6,408.90
40	CONSTRUCCION DE LOSA DE DIAMANTE DE CONCRETO MR= 45 , T.M.A. DE 3/4" (19MM), GRAVA TRITURADA, REVENIMIENTO DE 8+-2.5CM CM, FRAGUADO RAPIDOA A 3 DIAS, DE 25 CM DE ESPESOR, EN POZO DE VISITA, Y 1.50 M POR LADO, INCLUYE: SUMINISTRO DE MATERIALES, ESPUMA DE POLIURETANO DE ALTA DENSIDAD EN TODO EL PERIMETRO EXTERIOR DE 1/2" ASI COMO DE LAS JUNTAS DIAGONALES PARA FORMAR 4 PARTES, BROCAL Y TAPA DE Fo. Fo. TIPO PESADO, (165 KG), CIMBRADO, COLADO, VIBRADO, DESCIMBRADO, CURADO CON MEMBRANA QUIMICA BASE AGUA, APLANADO FINO EN RECEPCION DE BROCAL, CORTES CON CORTADORA DE DISCO DE 5 CM ENTRE JUNTAS DIAGONALES FORMADO 8 PIEZAS Y SELLADO DE JUNTAS Y CORTES CON MATERIAL PREFORMADO Y SELLADOR AUTONIVELANTE, MANO DE OBRA, ACARREOS DE MATERIAL DENTRO Y FUERA DE LA OBRA, TRABAJO TERMINADO. P.U.O.T.	PZA	2	$7,025.59	$14,051.18

Obra: **PAVIMENTO HIDRÁULICO, CALLE EL GRULLO**

Ubicación: **TRAMO: ENTRE CALLE AMECA Y CALLE AMATITÁN, LA SOLEDAD Fracc.**

Contratista: **SERVICIOS Y TRANSPORTES ESPECIALES ROOT, S.A. DE C.V. (75)**

No.	Concepto	Unidad	Cantidad	Precio Unitario	Importe Total
	GRUPO: **PAVIMENTO HIDRAULICO**				
	PARTIDA: **OBRA COMPLEMENTARIA**				
41	CONSTRUCCION DE POZO DE VISITA DE 1.75 A 2.00 M DE PROFUNDIDAD, CON PLANTILLA DE MAMPOSTERIA DE PIEDRA ASENTADA CON MORTERO CEM-ARENA 1:3, CON MURO DE TABIQUE ROJO RECOCIDO DE 28 CM DE ESPESOR JUNTEADO CON MORTERO CEMENTO-ARENA 1:3 NO MAYOR DE 1.5 CM DE ESPESOR EN FORMA CUATRAPEADA, APLANADO INTERIOR DE MORTERO CEM-ARENA 1:3 DE UN ESPESOR MINIMO DE 1 CM, ACABADO PULIDO FINO DE CEMENTO, LAS INSERCIONES DE LAS TUBERIAS SE EMBOQUILLARAN, LOS ESCALONES DE VARILLA DEL No. 5 (5/8"), LA HECHURA DE LA MEDIA CAÑA DE CONCRETO HECHO EN OBRA F'c= 150 KG/CM2, DONDE SE AHOGARA TUBERIA CORTADA A MEDIA CAÑA Y SE PULIRA CUIDADOSAMENTE, INCLUYE: EXCAVACION, RELLENO, MATERIALES, ACARREOS, FLETES, MANO DE OBRA, MANIOBRAS LOCALES Y TODO LO NECESARIOA PARA SU CORRECTA CONSTRUCCION Y FUNCIONAMIENTO SEGUN NORMA.	PZA	2	$16,509.07	$33,018.14
42	RENIVELACIÓN DE RASANTE (PARTE SUPERIOR) DE CAJA DE VÁLVULAS TIPO 3 DE HASTA 1.96 X 1. 75 MTS, NIVELADO HASTA UNA ALTURA MAXIMA DE 10 CM, Y MINIMA DE 5 CM. MEDIDAS INTERIORES INCLUYE: TRAZO, EXCAVACIÓN, NIVELACIÓN, PREPARACIONES , Y DEMOLICIONES, RETIRO SIN RECUPERACIÓN DE TAPA DE FOFO EXISTENTE, MURO DE TABIQUE ROJO RECOCIDO COMÚN 7X14X28 CM DE 14 CM DE ESPESOR, JUNTEADO CON MORTERO CEMENTO-ARENA 1:3 APLANADO INTERIOR CON MORTERO CEMENTO ARENA 1:3 DE 2.00 CM DE ESPESOR ACABADO PULIDO, LOSA DE CONCRETO F´C= 250 KG/CM2 T.M.A. 19 MM DE 15 CM DE ESPESOR ARMADA CON VRS No. 3 @15 cm EN AMBOS SENTIDOS, CONTRAMARCO SENCILLO DE CANAL FoFo DE 100 mm, CONTRAMARCO CON TAPA DE FOFO, TIPO PESADO DE 50X50 CM, DEMOLICIÓN Y RECONSTRUCCIÓN DE APROCHES, CARGA Y ACARREOS DENTRO DE LA OBRA, CIMBRADO, DESCIMBRADO, COLADO, VIBRADO, LIMPIEZA PREVIA, FINAL, Y TODO LO NECESARIO PARA LA CORRECTA EJECUCIÓN DEL CONCEPTO. PZA 2.00	PZA	1	$16,774.30	$16,774.30
43	LIMPIEZA Y DESASOLVE DE POZOS DE VISITA Y LINEAS DE ALCANTARILLADO EXISTENTE CON CAMION TIPO VACTOR. INCLUYE: RESANE INTERIOR DEL POZO Y REMTE DE POZO CO TUBO CON SELLADOR, FESTER Y MORTERO 1:3, MANO DE OBRA, SUMINISTRO DE AGUA EN PIPA, HERRAMIENTAS Y EQUIPO PARA SU CORRECTA EJECUCION, LIMPIEZAS, RENTA DE CAMION VACTOR HASTA LA CORRECTA LIMPIEZA DE LAS LINEAS EXISTENTES DE POZO A POZO, ASI COMO EL TRASLADO DE LOS DESECHOS HASTA TIRADERO AUTORIZADO MEDIDO POZO A POZO.	LOTE	3	$7,508.59	$22,525.77
			Totales por Partida		**$92,778.29**
	PARTIDA: **LIMPIEZAS**				
44	LIMPIEZA GENERAL DE LA OBRA, INCLUYE: BARRIDO, CARGA, ACARREOS Y RETIRO DE ESCOMBROS FUERA DE LA OBRA, TRABAJO TERMINADO.	M2	1123.4	$9.85	$11,065.49
			Totales por Partida		**$11,065.49**
			Totales por Grupo		**$1,575,377.15**

Obra: **PAVIMENTO HIDRÁULICO, CALLE EL GRULLO**

Ubicación: **TRAMO: ENTRE CALLE AMECA Y CALLE AMATITÁN, LA SOLEDAD Fracc.**

Contratista: **SERVICIOS Y TRANSPORTES ESPECIALES ROOT, S.A. DE C.V. (75)**

No.	Concepto	Unidad	Cantidad	Precio Unitario	Importe Total
	GRUPO: **SEÑALIZACION**				
	PARTIDA: **SEÑALIZACION HORIZONTAL**				
45	SUMINISTRO Y APLICACIÓN DE PINTURA EPOXICA BASE SOLVENTE COLOR AZUL (PANTONE 294) EN RAMPAS PARA PERSONAS CON DISCAPACIDAD CUALQUIER SECCIÓN SEGÚN PLANOS. INCLUYE: TRAZO, MANO DE OBRA, LIMPIEZA PREVIA DE SUPERFICIE, EQUIPO NECESARIO PARA SU EJECUCIÓN, Y TODO LO NECESARIO PARA SU CORRECTA EJECUCIÓN, TRABAJO TERMINADO.	M2	10.5	$189.61	$1,990.90
46	SUMINISTRO Y APLICACIÓN DE LOGOTIPO A (SILLA DE RUEDAS) EN PINTURA EPOXICA BASE SOLVENTE COLOR BLANCO EN RAMPAS PARA PERSONAS CON DISCAPACIDAD TAMAÑO Y DISEÑO SEGÚN PLANOS. INCLUYE: TRAZO, ENMASCARILLADO, PLANTILLA, MANO DE OBRA, LIMPIEZA PREVIA DE SUPERFICIE, EQUIPO NECESARIO PARA SU EJECUCIÓN, Y TODO LO NECESARIO PARA SU CORRECTA EJECUCIÓN, TRABAJO TERMINADO.	PZA	7	$162.36	$1,136.52
47	SUMINISTRO Y APLICACIÓN DE PINTURA BASE SOLVENTE PARA MARCAS EN GUARNICIONES CLASIFICACION M-12.1, M12.2 APLICADA SOBRE GUARNICIONES Y DENTELLONES DE CUALQUIER COLOR, SEGÚN SE REQUIERA Y SEGÚN NORMA S.C.T. SECADO AL TACTO EN 5 MIN Y AL DURO EN 30 MIN CON MICRO ESFERA , DESARROLLO DE 35 CM. INCLUYE: MATERIALES Y ESPECIFICACIONES QUE CUMPLAN CON LA NORMATIVA N-CMT-5-01-001/05, N-PRY-CAR-10-01-002/13 APLICADAS AL DIA DE HOY, TRAZO, MANO DE OBRA, LIMPIEZA PREVIA DE SUPERFICIE, EQUIPO NECESARIO PARA SU EJECUCIÓN, Y TODO LO NECESARIO PARA SU CORRECTA EJECUCIÓN, TRABAJO TERMINADO.	ML	224	$33.82	$7,575.68
48	SUMINISTRO Y APLICACIÓN DE PINTURA TERMOPLASTICA ALQUIDALICA DE 120 MILESIMAS DE " (in) EN RAYA PARA CRUCE PEATONAL CLASIFICACIÓN M - 7.1, PARA INDICAR " CRUCE PEATONAL EN VIAS PRIMARIAS", COLOR AMARILLO, REFLEJANTE CON MICRO ESFERA DE VIDRIO EN PROPORCIÓN SEGÚN MANUAL DE SEÑALIZACIÓN VIAL Y DISPOSITIVOS DE SEGURIDAD SICT (S.C.T). DE 0.40 MTS DE ANCHO Y 3.5 MTS. DE LONGITUD POR EL ANCHO DE LA VIALIDAD, CON UNA SEPARACIÓN DE 0.40 MTS. ENTRE ELLAS, INCLUYE: MATERIALES Y ESPECIFICACIONES QUE CUMPLAN CON LA NORMATIVA N-CMT-5-01-001/13, N-PRY-CAR-10-01-002/13 APLICADAS AL DIA DE HOY, MATERIAL APLICADO EN SU ESTADO DE FUSION A UNA TEMPERATURA MINIMA DE 204 C, LA SUPERFICIE DE CONCRETO O ASFALTO NO DEBE PRESENTAR UNA TEMPERATURA MENOR A LOS 10 C, ;TIEMPO DE SECADO EN RANGOS DE TEMPERATURA DE 10 C DEL SUSTRATO 2 MINUTOS, Y NO MAS DE 10 MINUTOS CUANDO EL SUSTRATO OSCILA ALREDEDOR DE 54C, TRAZO, ENMASCARILLADO, MANO DE OBRA, LIMPIEZA PREVIA Y FINAL DE SUPERFICIE, EQUIPO NECESARIO PARA SU EJECUCIÓN, Y TODO LO NECESARIO PARA SU CORRECTA EJECUCIÓN, TRABAJO TERMINADO.	ML	70	$213.80	$14,966.00
			Totales por Partida		**$25,669.10**

Obra: **PAVIMENTO HIDRÁULICO, CALLE EL GRULLO**

Ubicación: **TRAMO: ENTRE CALLE AMECA Y CALLE AMATITÁN, LA SOLEDAD Fracc.**

Contratista: **SERVICIOS Y TRANSPORTES ESPECIALES ROOT, S.A. DE C.V. (75)**

No.	Concepto	Unidad	Cantidad	Precio Unitario	Importe Total
	GRUPO: **SEÑALIZACION**				
	PARTIDA: **SEÑALAMIENTO VERTICAL**				
49	SUMINISTRO Y COLOCACION DE SEÑALAMIENTO VERTICAL DE RESTRICCION SR-6 (ALTO), DISEÑO NORMATIVO SCT, HECHO A ABASE DE LAMINA GALVANIZADA CON CEJA DE 30 CM POR CADA LADO CALIBRE 16, CON TERMINADO GRADO INGENIERIA EN SU TOTALIDAD, EL COLOR SERA REFLEJANTE GRADO INGENIERIA Y SIMBOLOS EN COLOR REFLEJANTE, TODOS LOS COLORES RESISTENTES A LA INTEMPERIE, FIJADA MEDIANTE BARRENADO Y TORNILLOS DE 2 1/2" X 5/16" A UN POSTE DE PTR DE 2 X 2" CALIBRE 14 EN ACABADO GALVANIZADO Y CON UNA ALTURA DE 2.5 MTS AL NIVEL DE BANQUETA A LA PARTE INFERIOR DE LA LAMINA MAS EL EXCEDENTE REQUERIDO PARA FIJAR LAS LAMINAS Y ANCLADO DE 50 CM DE PROFUNDIDAD CON ANGULO TRANSVERSAL DE 1 X 1" DE 25 CM, EN DADO DE CONCRETO F´c=150 KG/CM2 DE 30 CM DE LADO (VER PLANO DE DETALLES CRITERIOS DE ANCLAJE DE SEÑALAMIENTO VERTICAL, DETALLE SEÑ-02 Y SEÑ 03), MCA ASEA O SIMILAR EN CALIDAD Y ESPECIFICACIONES, INCLUYE: MANO DE OBRA, FLETES, MANIOBRAS LIMPIEZAS Y RETIRO DEL SOBRANTE FUERA DE LA OBRA HASTA TIRADERO OFICIAL, TRABAJO TERMINADO.	PZA	3	$2,412.21	$7,236.63
			Totales por Partida		**$7,236.63**
			Totales por Grupo		**$32,905.74**

Obra: **PAVIMENTO HIDRÁULICO, CALLE EL GRULLO**

Ubicación: **TRAMO: ENTRE CALLE AMECA Y CALLE AMATITÁN, LA SOLEDAD Fracc.**

Contratista: **SERVICIOS Y TRANSPORTES ESPECIALES ROOT, S.A. DE C.V. (75)**

No.	Concepto	Unidad	Cantidad	Precio Unitario	Importe Total
	GRUPO: **HIDRAULICO SANITARIO**				
	PARTIDA: **LINEA DE ALCANTARILLADO**				
50	TRAZO Y NIVELACION DE TERRENO CON APARATO TOPOGRAFICO, PARA LINEAS DE AGUA POTABLE Y ALCANTARILLADO, INCLUYE: EJES, BANCOS DE NIVEL, RENIVELACIONES, CORRECCION DE ARRASTRES Y NIVELES A PUNTOS OBLIGADOS (AUTORIZADOS POR LA SUPERVISION), ESTACAS, VARILLAS, MANO DE OBRA CALIFICADA, HERRAMIENTA NECESARIA, EQUIPO DE PRECISION CALIBRADO, (SE ENTREGARA A LA DEPENDENCIA PLANO DE PERFIL Y SECCIONES ORIGINAL Y FINAL CON PUNTOS X,Y,Z) TRABAJO TERMINADO.P.U.O.T.	ML	112	$5.08	$568.96
51	EXCAVACION A MAQUINA EN ZANJAS EN MATERIAL TIPO II DE 0.00 A 2.00 M DE PROFUNDIDAD, INCLUYE: AFLOJE Y EXTRACCION DEL MATERIAL, AFINE, TRASPALEO VERTICAL PARA SU EXTRACCION, CONSERVACION DE LA EXCAVACION, ACARREO HASTA EL LUGAR DE ACOPIO PARA SU CARGA Y ACARREO FUERA DE LA OBRA, SEÑALAMIENTOS, COLOCACION DE PASOS PEATONALES Y PROTECCION PERIMETRAL DE LA ZANJA.	M3	134.4	$51.95	$6,982.08
52	PLANTILLA Y ACOSTILLADO CON ARENA Y PISON DE MANO, INCLUYE: SUMINISTRO DE MATERIAL EN LA OBRA, ACARREO EN CARRETILLA, DESCARGA EN LA ZANJA, EXTENDIDO, NIVELADO Y APISONADO, APOYO SEMICIRCULAR PARA LA TUBERIA SE CONSTRUIRA INMEDIATAMENTE ANTES DE TENDER LA TUBERIA, DEBIENDO COLOCAR HILOS LONGITUDINALMENTE PARA VERIFICAR LA UNIFORMIDAD DE LA PLANTILLA.	M3	10.08	$745.57	$7,515.35
53	ACOSTILLADO CON MATERIAL DE PROD. DE EXCAVACION EN CAPAS DE 20 CMS. AL 85% DE SU P.V.M.S. CON EL USO DE BAILARINA, HOMOGENIZACION DEL MATERIAL, AGUA LA NECESARIA, EXTENDIDO Y COMPACTADO.	M3	13.44	$199.52	$2,681.55
54	RELLENO COMPACTADO AL 90% CON MATERIAL DE BANCO EN CAPAS DE 20 CM UTILIZANDO BAILARINA. INCLUYE: SUMINISTRO DE TEPETATE (MATERIAL DE BANCO) EN LA OBRA, ABUNDAMIENTO, ACARREOS DENTRO DE LA OBRA, CRIBADO, RETIRO DE MATERIAL, MANO DE OBRA Y EQUIPO, LIMPIEZAS, TRABAJO TERMINADO.	M3	97.44	$304.91	$29,710.43
55	RELLENO COMPACTADO AL 95% CON MATERIAL DE BANCO EN CAPAS DE 20 CM UTILIZANDO BAILARINA, INCLUYE: SELECCION DEL MATERIAL, ABUNDAMIENTO, ACARREOS DENTRO DE LA OBRA, CRIBADO, MANO DE OBRA Y EQUIPO, PRUEBA DE CONTROL DE CALIDAD.	M3	13.44	$298.95	$4,017.89
56	CARGA MECANICA Y ACARREO DE MATERIAL PRODUCTO DE EXCAVACION Y DEMOLICION EN CAMION DE VOLTEO AL 1er. KM, VOLUMEN MEDIDO COMPACTO.	M3	120.96	$29.77	$3,600.98
57	ACARREO DE MATERIAL PRODUCTO DE EXCAVACION Y/O DEMOLICION EN CAMION DE VOLTEO A KILOMETROS SUBSECUENTES, AL TIRADERO OFICIAL AUTORIZADO MAS CERCANO AUTORIZADO POR LA SUPERVISION, VOLUMEN MEDIDO COMPACTO.	M3-KM	3628.8	$9.50	$34,473.60
58	SUMINISTRO DE TUBERIA DE PVC PARA ALCANTARILLADO SERIE 20 DE 8", CON JUNTA HERMETICA, CON COPLES, TEES, CODOS, EXTREMIDADES, INCLUYE: FLETES Y ACARREO HASTA EL SITIO DE SU COLOCACION, ALINEADO, MATERIAL, MANO DE OBRA.	ML	112	$230.28	$25,791.36
59	INSTALACION DE TUBERIA DE PVC PARA ALCANTARILLADO SERIE 20 DE 8", CON JUNTA HERMETICA. INCLUYE: FLETES Y ACARREO HASTA EL SITIO DE SU COLOCACION, MATERIALES DE LIMPIEZA, LUBRICACION, PEGAMENTO DE ALTA HUMEDAD, NIVELADO, MATERIAL Y MANO DE OBRA.	ML	112	$84.62	$9,477.44
60	CONEXION DE TUBERIA DE PVC DE 8-16" A POZO DE VISITA, INCLUYE: DEMOLICION DE MURO DE POZO, CONEXION Y NIVELACION DEL TUBO, RESANE DEL MURO, APLANADO INTERIOR ACABADO PULIDO, LIGAS, LIMPIEZA Y RETIRO DE ESCOMBRO A 20 M.	PZA	6	$1,269.09	$7,614.54
				Totales por Partida	**$132,434.17**

Obra: **PAVIMENTO HIDRÁULICO, CALLE EL GRULLO**

Ubicación: **TRAMO: ENTRE CALLE AMECA Y CALLE AMATITÁN, LA SOLEDAD Fracc.**

Contratista: **SERVICIOS Y TRANSPORTES ESPECIALES ROOT, S.A. DE C.V. (75)**

GRUPO: **HIDRAULICO SANITARIO**

PARTIDA: **DESCARGAS DOMICILIARIAS**

No.	Concepto	Unidad	Cantidad	Precio Unitario	Importe Total
61	EXCAVACION A MAQUINA EN ZANJAS EN MATERIAL TIPO II DE 0.00 A 2.00 M DE PROFUNDIDAD, INCLUYE: AFLOJE Y EXTRACCION DEL MATERIAL, AFINE, TRASPALEO VERTICAL PARA SU EXTRACCION, CONSERVACION DE LA EXCAVACION, ACARREO HASTA EL LUGAR DE ACOPIO PARA SU CARGA Y ACARREO FUERA DE LA OBRA, SEÑALAMIENTOS, COLOCACION DE PASOS PEATONALES Y PROTECCION PERIMETRAL DE LA ZANJA.	M3	57.56	$51.95	$2,990.24
62	PLANTILLA Y ACOSTILLADO CON ARENA Y PISON DE MANO, INCLUYE: SUMINISTRO DE MATERIAL EN LA OBRA, ACARREO EN CARRETILLA, DESCARGA EN LA ZANJA, EXTENDIDO, NIVELADO Y APISONADO, APOYO SEMICIRCULAR PARA LA TUBERIA SE CONSTRUIRA INMEDIATAMENTE ANTES DE TENDER LA TUBERIA, DEBIENDO COLOCAR HILOS LONGITUDINALMENTE PARA VERIFICAR LA UNIFORMIDAD DE LA PLANTILLA.	M3	16.79	$745.57	$12,518.12
63	RELLENO COMPACTADO AL 90% CON MATERIAL DE BANCO EN CAPAS DE 20 CM UTILIZANDO BAILARINA. INCLUYE: SUMINISTRO DE TEPETATE (MATERIAL DE BANCO) EN LA OBRA, ABUNDAMIENTO, ACARREOS DENTRO DE LA OBRA, CRIBADO, RETIRO DE MATERIAL, MANO DE OBRA Y EQUIPO, LIMPIEZAS, TRABAJO TERMINADO.	M3	31.18	$304.91	$9,507.09
64	RELLENO COMPACTADO AL 95% CON MATERIAL DE BANCO EN CAPAS DE 20 CM UTILIZANDO BAILARINA, INCLUYE: SELECCION DEL MATERIAL, ABUNDAMIENTO, ACARREOS DENTRO DE LA OBRA, CRIBADO, MANO DE OBRA Y EQUIPO, PRUEBA DE CONTROL DE CALIDAD.	M3	9.59	$298.95	$2,866.93
65	CARGA MECANICA Y ACARREO DE MATERIAL PRODUCTO DE EXCAVACION Y DEMOLICION EN CAMION DE VOLTEO AL 1er. KM, VOLUMEN MEDIDO COMPACTO.	M3	57.56	$29.77	$1,713.56
66	ACARREO DE MATERIAL PRODUCTO DE EXCAVACION Y/O DEMOLICION EN CAMION DE VOLTEO A KILOMETROS SUBSECUENTES, AL TIRADERO OFICIAL AUTORIZADO MAS CERCANO AUTORIZADO POR LA SUPERVISION, VOLUMEN MEDIDO COMPACTO.	M3-KM	1726.92	$9.50	$16,405.74
67	DESCARGA DOMICILIARIA NUEVA PARA REMPLAZO DE 6.00 M DE LONGITUD (NOMINAL), A BASE DE TUBO DE PVC ALCANTARILLADO SERIE 20 DE 6" DE DIAMETRO, INCLUYE: SILLETA DE 8" X 6", CODO DE 6" X 45°, CONEXION A REGISTRO NUEVO O EXISTENTE, ALINEACION, PRUEBAS DE ESCURRIMIENTO, SUMINISTROS, ACARREOS, TRABAJO TERMINADO.	PZA	7	$1,650.13	$11,550.91
68	REGISTRO SANTARIO DE 0.40X0.60X0.80 M (MEDIDAS INTERIORES) DE TABIQUE ROJO RECOCIDO (14 CM DE ESPESOR) JUNTEADO CON MORTERO CEMENTO-ARENA 1:4 Y APLANADO DE 2.00 CM CON EL MISMO MORTERO, ACABADO PULIDO INTERIOR, PLANTILLA DE 7.00 CM DE ESPESOR DE CONCRETO F'C=150 KG/CM2, HECHO EN OBRA, TMA 19 MM. INCLUYE: MARCO Y CONTRAMARCO DE ANGULO DE 2" X 3/16" COLADA CON EL MISMO CONCRETO, PLOMEADO, ALINEADO, NIVELADO, ACARREOS DENTRO DE LA OBRA Y CONEXION A RED EXISTENTE, LIMPIEZAS.	PZA	10	$2,632.08	$26,320.80
69	RENIVELACION DE REGISTRO SANTARIO DE 0.40X0.60 M (MEDIDAS INTERIORES) A UNA ALTURA DE 0.05 A 0.20 MTS A BASE DE TABIQUE ROJO RECOCIDO (14 CM DE ESPESOR) JUNTEADO CON MORTERO CEMENTO-ARENA 1:4 Y APLANADO DE 2.00 CM CON EL MISMO MORTERO, ACABADO PULIDO INTERIOR, INCLUYE: MARCO Y CONTRAMARCO DE ANGULO DE 2" X 3/16" COLADA CON EL MISMO CONCRETO, PLOMEADO, ALINEADO, NIVELADO, ACARREOS DENTRO DE LA OBRA, IMPIEZAS.	PZA	3	$1,398.37	$4,195.11
			Totales por Partida		$88,068.51

Obra: **PAVIMENTO HIDRÁULICO, CALLE EL GRULLO**

Ubicación: **TRAMO: ENTRE CALLE AMECA Y CALLE AMATITÁN, LA SOLEDAD Fracc.**

Contratista: **SERVICIOS Y TRANSPORTES ESPECIALES ROOT, S.A. DE C.V. (75)**

No.	Concepto	Unidad	Cantidad	Precio Unitario	Importe Total
	GRUPO: **HIDRAULICO SANITARIO**				
	PARTIDA: **LINEA DE AGUA POTABLE**				
70	TRAZO Y NIVELACION DE TERRENO CON APARATO TOPOGRAFICO, PARA LINEAS DE AGUA POTABLE Y ALCANTARILLADO, INCLUYE: EJES, BANCOS DE NIVEL, RENIVELACIONES, CORRECCION DE ARRASTRES Y NIVELES A PUNTOS OBLIGADOS (AUTORIZADOS POR LA SUPERVISION), ESTACAS, VARILLAS, MANO DE OBRA CALIFICADA, HERRAMIENTA NECESARIA, EQUIPO DE PRECISION CALIBRADO, (SE ENTREGARA A LA DEPENDENCIA PLANO DE PERFIL Y SECCIONES ORIGINAL Y FINAL CON PUNTOS X,Y,Z) TRABAJO TERMINADO.P.U.O.T.	ML	112	$5.08	$568.96
71	EXCAVACION A MAQUINA EN ZANJAS EN MATERIAL TIPO II DE 0.00 A 2.00 M DE PROFUNDIDAD, INCLUYE: AFLOJE Y EXTRACCION DEL MATERIAL, AFINE, TRASPALEO VERTICAL PARA SU EXTRACCION, CONSERVACION DE LA EXCAVACION, ACARREO HASTA EL LUGAR DE ACOPIO PARA SU CARGA Y ACARREO FUERA DE LA OBRA, SEÑALAMIENTOS, COLOCACION DE PASOS PEATONALES Y PROTECCION PERIMETRAL DE LA ZANJA.	M3	61.6	$51.95	$3,200.12
72	BOMBEO DE ACHIQUE CON BOMBA DE 3" Y 8 H.P., OPERACION BOMBA Y EQUIPO COMPLEMENTARIO CON MANGUERA Y PICHANCHA.	HR	2	$158.89	$317.78
73	PLANTILLA Y ACOSTILLADO CON ARENA Y PISON DE MANO, INCLUYE: SUMINISTRO DE MATERIAL EN LA OBRA, ACARREO EN CARRETILLA, DESCARGA EN LA ZANJA, EXTENDIDO, NIVELADO Y APISONADO, APOYO SEMICIRCULAR PARA LA TUBERIA SE CONSTRUIRA INMEDIATAMENTE ANTES DE TENDER LA TUBERIA, DEBIENDO COLOCAR HILOS LONGITUDINALMENTE PARA VERIFICAR LA UNIFORMIDAD DE LA PLANTILLA.	M3	22.79	$745.57	$16,991.54
74	RELLENO COMPACTADO AL 90% CON MATERIAL DE BANCO EN CAPAS DE 20 CM UTILIZANDO BAILARINA. INCLUYE: SUMINISTRO DE TEPETATE (MATERIAL DE BANCO) EN LA OBRA, ABUNDAMIENTO, ACARREOS DENTRO DE LA OBRA, CRIBADO, RETIRO DE MATERIAL, MANO DE OBRA Y EQUIPO, LIMPIEZAS, TRABAJO TERMINADO.	M3	26.49	$304.91	$8,077.07
75	RELLENO COMPACTADO AL 95% CON MATERIAL DE BANCO EN CAPAS DE 20 CM UTILIZANDO BAILARINA, INCLUYE: SELECCION DEL MATERIAL, ABUNDAMIENTO, ACARREOS DENTRO DE LA OBRA, CRIBADO, MANO DE OBRA Y EQUIPO, PRUEBA DE CONTROL DE CALIDAD.	M3	12.32	$298.95	$3,683.06
76	CARGA MECANICA Y ACARREO DE MATERIAL PRODUCTO DE EXCAVACION Y DEMOLICION EN CAMION DE VOLTEO AL 1er. KM, VOLUMEN MEDIDO COMPACTO.	M3	61.6	$29.77	$1,833.83
77	ACARREO DE MATERIAL PRODUCTO DE EXCAVACION Y/O DEMOLICION EN CAMION DE VOLTEO A KILOMETROS SUBSECUENTES, AL TIRADERO OFICIAL AUTORIZADO MAS CERCANO AUTORIZADO POR LA SUPERVISION, VOLUMEN MEDIDO COMPACTO.	M3-KM	1848	$9.50	$17,556.00
78	SUMINISTRO DE TUBERIA DE PVC HIDRAULICO RD-26 DE 2.5" CON CAMPANA INTEGRAL, COPLES, CODOS, TEES, INCLUYE:ACARREOS HASTA EL SITIO DE SU COLOCACION, BAJADO, ALINEADO, INSTALACION DE COPLES, ANILLO Y PRUEBA HIDROSTATICA.	ML	112	$64.10	$7,179.20
79	INSTALACION DE TUBERIA DE PVC HIDRAULICO RD-26 DE 2.5" CON CAMPANA INTEGRAL. INCLUYE: ACARREO HASTA EL SITIO DE SU COLOCACION, BAJADO, ALINEAMIENTO, INSTALACION DE COPLES, ANILLO Y PRUEBA HIDROSTATICA.	ML	112	$67.07	$7,511.84
80	SUMINISTRO Y COLOCACION DE EXTREMIDAD ESPIGA DE 2.5", INCLUYE: SUMINISTROS, MANO DE OBRA, NIVELACION, MATERIALES, PRUEBA HIDROSTATICA JUNTO CON LA TUBERIA, ACARREOS LOCALES, HERRAMIENTA NECESARIA Y TODO LO NECESARIO PARA SU CORRECTA EJECUCION, LIMPIEZA, TRABAJO TERMINADO.	PZA	2	$363.25	$726.50
81	SUMINISTRO Y COLOCACION DE TAPON CAMPANA DE PVC HIDRAULICO DE 2.5". INCLUYE: SUMINISTRO, MANO DE OBRA, NIVELACION, PRUEBA JUNTO CON LA TUBERIA, ACARREOS LOCALES, TRABAJO TERMINADO.	PZA	1	$197.00	$197.00

Obra: **PAVIMENTO HIDRÁULICO, CALLE EL GRULLO**

Ubicación: **TRAMO: ENTRE CALLE AMECA Y CALLE AMATITÁN, LA SOLEDAD Fracc.**

Contratista: **SERVICIOS Y TRANSPORTES ESPECIALES ROOT, S.A. DE C.V. (75)**

No.	Concepto	Unidad	Cantidad	Precio Unitario	Importe Total
	GRUPO: **HIDRAULICO SANITARIO**				
	PARTIDA: **LINEA DE AGUA POTABLE**				
82	CONEXION A RED HIDRAULICA EXISTENTE. INCLUYE: CORTE DE TUBERIA EN LINEA VIVA, CONEXION, EN TUBO DE 2 1/2" LIMPIEZA, MATERIAL Y MANO DE OBRA NECESARIA, TRABAJO TERMINADO.	LOTE	1	$3,444.01	$3,444.01
83	CONSTRUCCION DE ATRAQUE PARA CRUCERO Y TUBERIAS HECHO A BASE DE CONCRETO HECHO EN OBRA F'c=150 KG/CM2, TMA 3/4" GRAVA TRITURADA SEGUN NORMAS OFICIALES PARA UN DIAMETRO DE HASTA 14", INCLUYE: MATERIALES DE BANCO, MANO DEOBRA, CARGA Y ACARREOS LOCALES, ELEVACIONES, MANIOBRAS LOCALES, TRABAJO TERMINADO, LIMPIEZAS	M3	0.02	$3,419.10	$68.38
84	SUMINISTRO Y COLOCACION DE ADAPTADOR BRIDADO UNIVERSAL PARA TUBERIA DE 2" Y HASTA 2 1/2", INCLUYE: SUMINISTROS, MANO DE OBRA, TORNILLOS, NIVELACION, PRUEBA JUNTO CON LA TUBERIA, ACARREOS LOCALES, TRABAJO TERMINADO	PZA	1	$799.19	$799.19
				Totales por Partida	**$72,154.48**
	PARTIDA: **TOMAS DOMICILIARIAS**				
85	EXCAVACION A MAQUINA EN ZANJAS EN MATERIAL TIPO II DE 0.00 A 2.00 M DE PROFUNDIDAD, INCLUYE: AFLOJE Y EXTRACCION DEL MATERIAL, AFINE, TRASPALEO VERTICAL PARA SU EXTRACCION, CONSERVACION DE LA EXCAVACION, ACARREO HASTA EL LUGAR DE ACOPIO PARA SU CARGA Y ACARREO FUERA DE LA OBRA, SEÑALAMIENTOS, COLOCACION DE PASOS PEATONALES Y PROTECCION PERIMETRAL DE LA ZANJA.	M3	47.97	$51.95	$2,492.04
86	RELLENO COMPACTADO AL 90% CON MATERIAL DE BANCO EN CAPAS DE 20 CM UTILIZANDO BAILARINA. INCLUYE: SUMINISTRO DE TEPETATE (MATERIAL DE BANCO) EN LA OBRA, ABUNDAMIENTO, ACARREOS DENTRO DE LA OBRA, CRIBADO, RETIRO DE MATERIAL, MANO DE OBRA Y EQUIPO, LIMPIEZAS, TRABAJO TERMINADO.	M3	38.38	$304.91	$11,702.45
87	RELLENO COMPACTADO AL 95% CON MATERIAL DE BANCO EN CAPAS DE 20 CM UTILIZANDO BAILARINA, INCLUYE: SELECCION DEL MATERIAL, ABUNDAMIENTO, ACARREOS DENTRO DE LA OBRA, CRIBADO, MANO DE OBRA Y EQUIPO, PRUEBA DE CONTROL DE CALIDAD.	M3	9.59	$298.95	$2,866.93
88	CARGA MECANICA Y ACARREO DE MATERIAL PRODUCTO DE EXCAVACION Y DEMOLICION EN CAMION DE VOLTEO AL 1er. KM, VOLUMEN MEDIDO COMPACTO.	M3	47.97	$29.77	$1,428.07
89	ACARREO DE MATERIAL PRODUCTO DE EXCAVACION Y/O DEMOLICION EN CAMION DE VOLTEO A KILOMETROS SUBSECUENTES, AL TIRADERO OFICIAL AUTORIZADO MAS CERCANO AUTORIZADO POR LA SUPERVISION, VOLUMEN MEDIDO COMPACTO.	M3-KM	1439.1	$9.50	$13,671.45
90	CONSTRUCCION DE TOMA DOMICILIARIA DE REMPLAZO DE 10 A 12 MTS DE LONGITUD (NOMINAL) A BASE DE TUBO KITEC DE 5/8" AZUL, CONECTORES PHILMAC MACHO Y HEMBRA, ABRAZADERAS SIN FIN, CONEXION A TUBO GALVANIZADO O EXISTENTE, ABRAZADERA DE PVC DE 2 1/2" X 1/2", INCLUYE: ENCAMISADO CON POLIDUCTO ELECTRICO DE 1 1/2", PRUEBAS, SUMINISTROS, ACARREOS LOCALES, MANO DE OBRA, TRABAJO TERMINADO.	PZA	7	$1,441.01	$10,087.07
91	CONSTRUCCION DE TOMA DOMICILIARIA DE REMPLAZO DE 4 A 6 MTS DE LONGITUD (NOMINAL) A BASE DE TUBO KITEC DE 5/8" AZUL, CONECTORES PHILMAC MACHO Y HEMBRA, ABRAZADERAS SIN FIN, CONEXION A TUBO GALVANIZADO O EXISTENTE, ABRAZADERA DE PVC DE 2 1/2" X 1/2", INCLUYE: ENCAMISADO CON POLIDUCTO ELECTRICO DE 1 1/2", PRUEBAS, SUMINISTROS, ACARREOS LOCALES, MANO DE OBRA, TRABAJO TERMINADO.	PZA	6	$1,209.41	$7,256.46
				Totales por Partida	**$49,504.46**

Obra: **PAVIMENTO HIDRÁULICO, CALLE EL GRULLO**

Ubicación: **TRAMO: ENTRE CALLE AMECA Y CALLE AMATITÁN, LA SOLEDAD Fracc.**

Contratista: **SERVICIOS Y TRANSPORTES ESPECIALES ROOT, S.A. DE C.V. (75)**

No.	Concepto	Unidad	Cantidad	Precio Unitario	Importe Total

GRUPO: **HIDRAULICO SANITARIO**

Totales por Grupo		$342,161.63
Totales Presup.		$1,950,444.51
Anticipo	+	$924,001.55
Amortizac. Ant.	-	$924,001.55
SubTotal. Ant.	=	$1,950,444.51
IVA	+	$312,071.12
Total	=	$2,262,515.63

PRESUPUESTO MODIFICADO

Obra: **PAVIMENTO HIDRÁULICO, CALLE EL GRULLO**

Ubicación: **TRAMO: ENTRE CALLE AMECA Y CALLE AMATITÁN, LA SOLEDAD Fracc.**

Contratista: **SERVICIOS Y TRANSPORTES ESPECIALES ROOT, S.A. DE C.V. (75)**

Grupo	Partida		Importe
PAVIMENTO HIDRAULICO			
	PRELIMINARES Y DEMOLICIONES		$84,065.48
	EXCAVACIONES, ACARREOS Y TERRACERIAS		$598,461.47
	PAVIMENTO		$706,905.48
	DENTELLONES DE CONCRETO		$25,331.40
	GUARNICIONES		$14,607.99
	BANQUETA Y RAMPA		$42,161.55
	OBRA COMPLEMENTARIA		$92,778.29
	LIMPIEZAS		$11,065.49
		Subtotal por Grupo	**$1,575,377.15**
SEÑALIZACION			
	SEÑALIZACION HORIZONTAL		$25,669.10
	SEÑALAMIENTO VERTICAL		$7,236.63
		Subtotal por Grupo	**$32,905.74**
HIDRAULICO SANITARIO			
	LINEA DE ALCANTARILLADO		$132,434.17
	DESCARGAS DOMICILIARIAS		$88,068.51
	LINEA DE AGUA POTABLE		$72,154.48
	TOMAS DOMICILIARIAS		$49,504.46
		Subtotal por Grupo	**$342,161.63**
		Totales Presup.	**$1,950,444.51**
		Anticipo +	**$924,001.55**
		Amortizac. Ant. -	**$924,001.55**
		SubTotal. Ant. =	**$1,950,444.51**
		IVA +	**$312,071.12**
		Total =	**$2,262,515.63**

H. AYUNTAMIENTO CONSTITUCIONAL DEL MUNICIPIO DE AGUASCALIENTES 2021-2024

H. AYUNTAMIENTO DE AGUASCALIENTES

SECRETARÍA DE OBRAS PÚBLICAS

DIRECCIÓN DE SUPERVISIÓN DE OBRA


Aguascalientes
LA CIUDAD DE TU VIDA


MEMORIA FOTOGRAFICA


OBRA:	PAVIMENTO HIDRÁULICO, CALLE EL GRULLO, TRAMO: ENTRE CALLE AMECA Y CALLE AMATITÁN, LA SOLEDAD Fracc.					
NO. DE CONTRATO:	FISMDF-0114-2022		CONTRATISTA:	SERVICIOS Y TRANSPORTES ESPECIALES ROOT, S.A. DE C.V.		

INICIO.



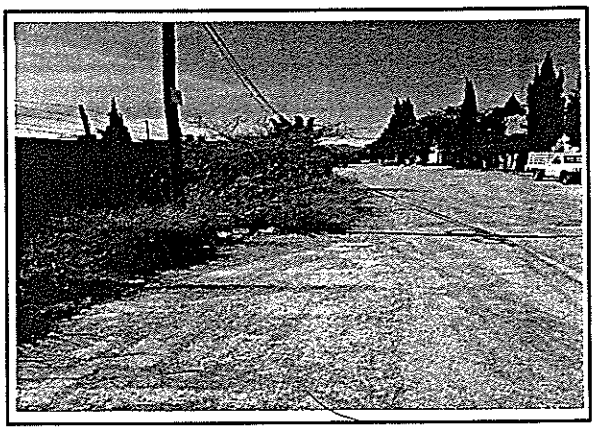

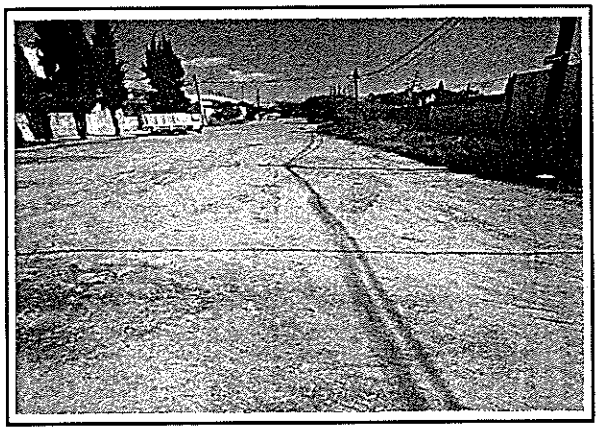

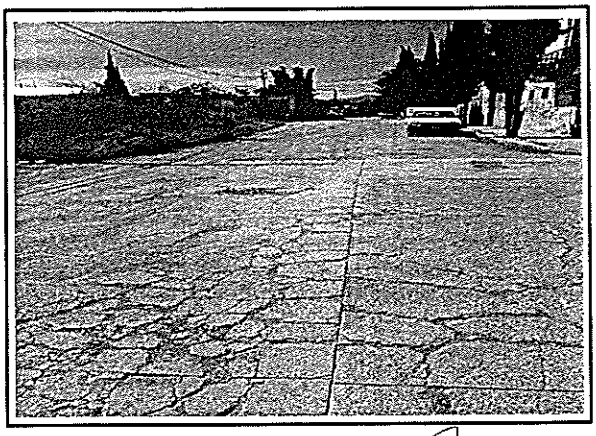

ING. IVAN ALEJANDRO RUIZ ESPARZA SOLIS
SUPERVISOR DE OBRA.

H. AYUNTAMIENTO CONSTITUCIONAL DEL MUNICIPIO DE AGUASCALIENTES 2021-2024

H. AYUNTAMIENTO DE AGUASCALIENTES

SECRETARÍA DE OBRAS PÚBLICAS


DIRECCIÓN DE SUPERVISIÓN DE OBRA

Aguascalientes
LA CIUDAD DE TU VIDA


MEMORIA FOTOGRAFICA

OBRA:	PAVIMENTO HIDRÁULICO, CALLE EL GRULLO, TRAMO: ENTRE CALLE AMECA Y CALLE AMATITÁN, LA SOLEDAD Fracc.					
NO. DE CONTRATO:	FISMDF-0114-2022		CONTRATISTA:	SERVICIOS Y TRANSPORTES ESPECIALES ROOT, S.A. DE C.V.		

PROCESO

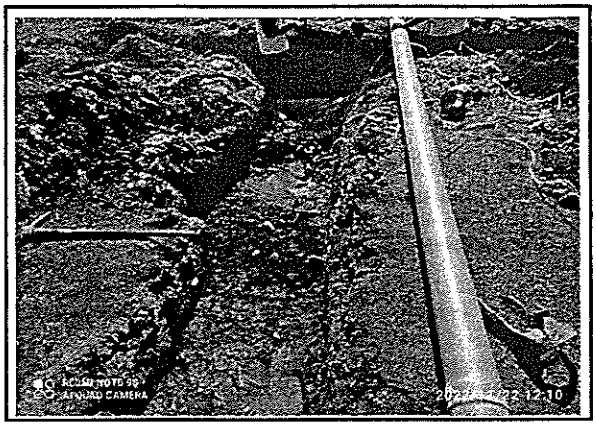



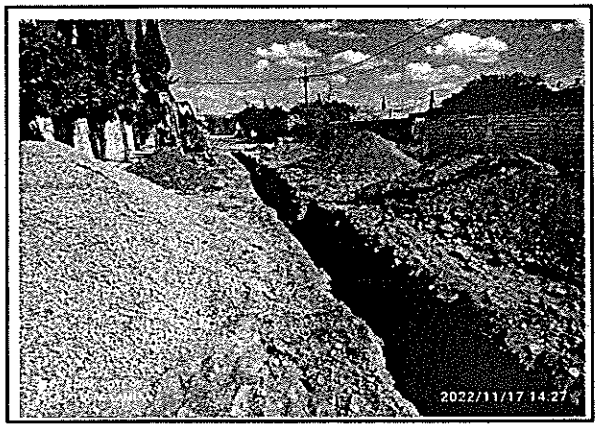



ING. IVAN ALEJANDRO RUIZ ESPARZA SOLIS
SUPERVISOR DE OBRA.

H. AYUNTAMIENTO CONSTITUCIONAL DEL MUNICIPIO DE AGUASCALIENTES 2021-2024

H. AYUNTAMIENTO DE AGUASCALIENTES

SECRETARÍA DE OBRAS PÚBLICAS

DIRECCIÓN DE SUPERVISIÓN DE OBRA


Aguascalientes
LA CIUDAD DE TU VIDA

MEMORIA FOTOGRAFICA

OBRA:	PAVIMENTO HIDRÁULICO, CALLE EL GRULLO, TRAMO: ENTRE CALLE AMECA Y CALLE AMATITÁN, LA SOLEDAD Fracc.					
NO. DE CONTRATO:	FISMDF-0114-2022		CONTRATISTA:	SERVICIOS Y TRANSPORTES ESPECIALES ROOT, S.A. DE C.V.		

TERMINO



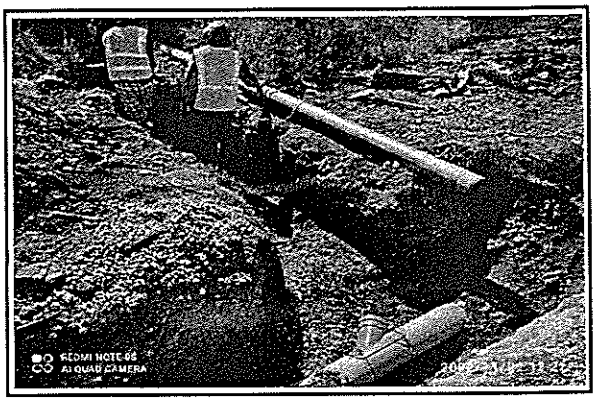





ING. IVAN ALEJANDRO RUIZ ESPARZA SOLIS
SUPERVISOR DE OBRA.

SECRETARÍA DE OBRAS PÚBLICAS

DIRECCIÓN DE SUPERVISIÓN DE OBRA

EJERCICIO 2022

N° DE CONTRATO: FISMDF-0114-2022


NOMBRE DE LA OBRA: PAVIMENTO HIDRÁULICO, CALLE EL GRULLO, TRAMO: ENTRE CALLE AMECA Y CALLE AMATITÁN, LA SOLEDAD Fracc.


MONTO MODIFICADO FINAL: $ 2,262,515.63

VOLUMEN	UNIDAD	COMPONENTE DE LA OBRA	MONTO
1129.70	M2	CONSTRUCCION DE PAVIMENTO HIDRAULICO A BASE DE CONCRETO PREMEZCLADO MR=38 KG/CM2 TMA 1 1/2" GRAVA TRITURADA, REVENIMIENTO DE 6 A 8 CM FRAGUADO NORMAL DE 15 CM DE ESPESOR MODULADO EN LOSAS DE 3.5 MTS. (ANCHO) X 3.5 MTS (LARGO) COMO MAXIMO, CON CORTES EN LAS LOSAS DE 1/3 DEL ESPESOR DE LA LOSA (5 CM) Y SELLADO CON COLA DE RATA Y	$ 1,575,377.15
70.00	ML	SUMINISTRO Y APLICACIÓN DE PINTURA TERMOPLASTICA ALQUIDALICA DE 120 MILESIMAS DE " (in) EN RAYA PARA CRUCE PEATONAL CLASIFICACIÓN M - 7.1, PARA INDICAR " CRUCE PEATONAL EN VIAS PRIMARIAS", COLOR AMARILLO, REFLEJANTE CON MICRO ESFERA DE VIDRIO EN PROPORCIÓN SEGÚN MANUAL DE SEÑALIZACIÓN VIAL Y DISPOSITIVOS DE SEGURIDAD SICT (6.0 T), DE 0.40 MTS. DE ANCHO Y	$ 32,905.74
3628.80	M3-KM	ACARREO DE MATERIAL PRODUCTO DE EXCAVACION Y/O DEMOLICION EN CAMION DE VOLTEO A KILOMETROS SUBSECUENTES, AL TIRADERO OFICIAL AUTORIZADO MAS CERCANO AUTORIZADO POR LA SUPERVISION, VOLUMEN MEDIDO COMPACTO.	$ 342,161.63

TOTAL PRESUP.	$	1,950,444.51
IVA	$	312,071.12
TOTAL	$	2,262,515.63

NOMBRE DEL SUPERVISOR: ING. IVAN ALEJANDRO RUIZ ESPARZA SOLIS

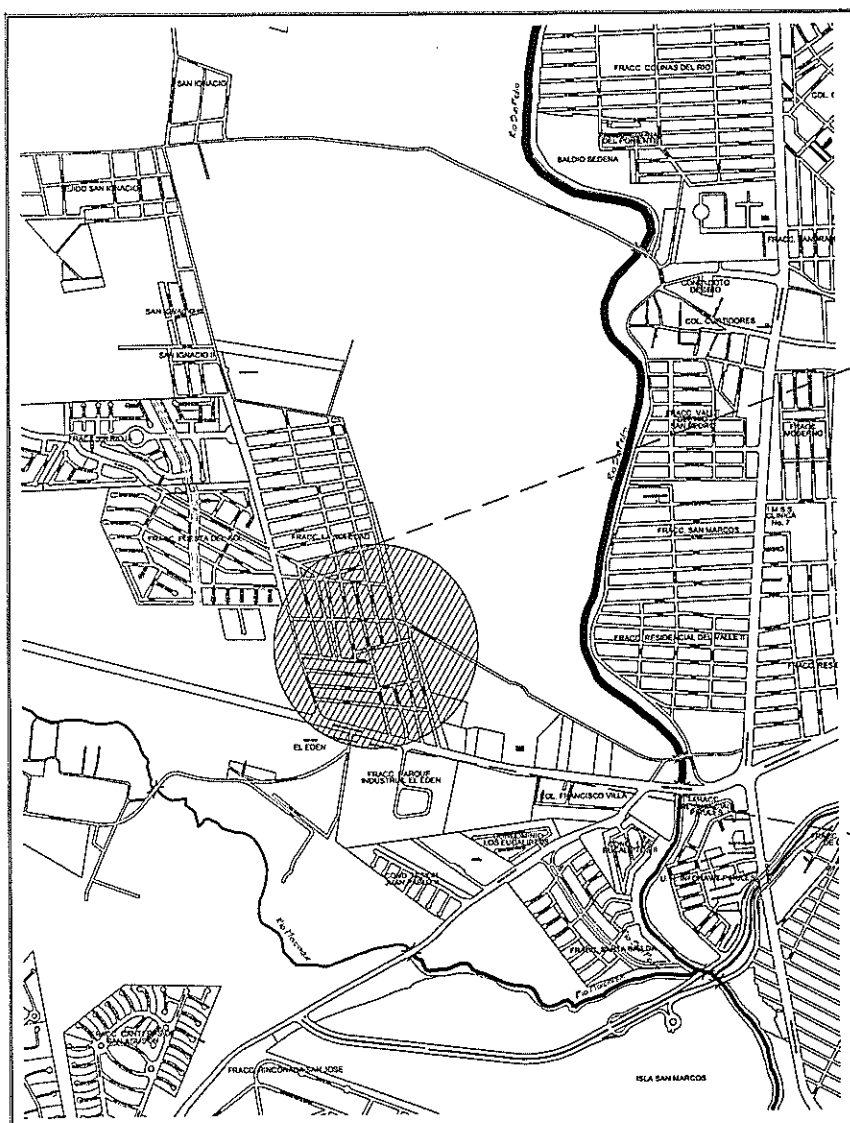


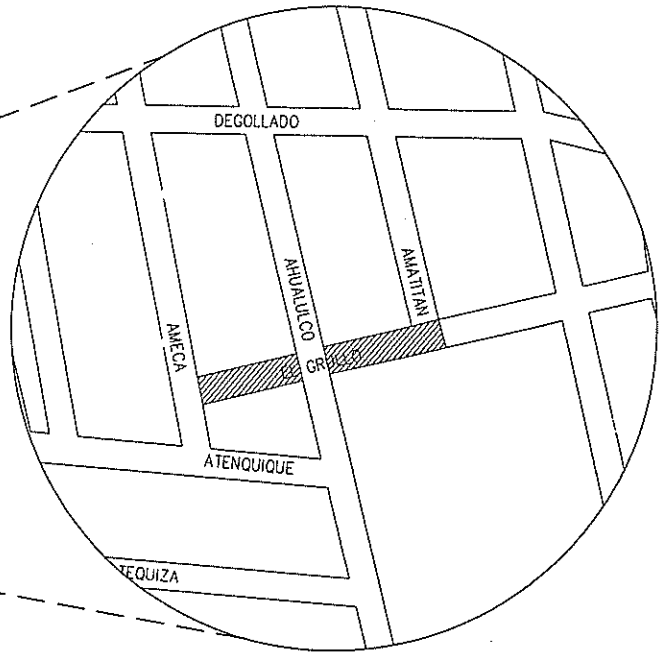

CROQUIS DE LOCALIZACIÓN

SIN ESCALA — CALLE EL GRULLO

LOCALIZACION:

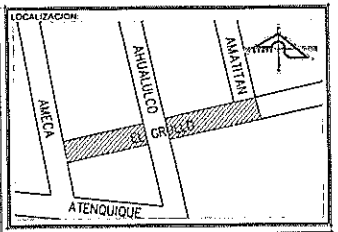

SIMBOLOGÍA

La Dirección de Planeación y Proyectos solo autoriza el proyecto ejecutivo, no es responsable de la correcta ejecución de la obra. Este documento no tiene validez si no presenta las firmas de los responsables para su autorización, así como los sellos respectivos.

PRESIDENTE MUNICIPAL
M.P.P. Leonardo Montañez Castro
SECRETARIO DE OBRAS PUBLICAS DEL MUNICIPIO DE AGUASCALIENTES
Ing. Miguel Ángel Huizar Botello

REV	FECHA	OBSERVACIONES

NO. DE LA REFERENCIA

RESP. DE PROY. EXTERNO		LOGO EXTERNO
CED. PROFESIONAL		
PROYECTÓ	REVISO	AUTORIZÓ


Dirección de Planeación y Proyectos de Obra — Secretaría de Obras Públicas

PROYECTISTA	COORDINADOR
ARQ. ALVARO DAVID MEZA CONTRERAS	ARQ. ALEJANDRO JAIME LEAL
JEFE DE DEP.	DIRECTOR
ARQ. J. JESÚS PALAFOX GONZÁLEZ	M. en ARQ. JOSÉ LUIS JIMÉNEZ GARCÍA

PROYECTO
PAVIMENTO HIDRAULICO CALLE EL GRULLO COLONIA LA SOLEDAD.
UBICACIÓN
ENTRE CALLE AMECA. Y CALLE AMATITAN.
CONTENIDO
CROQUIS DE LOCALIZACIÓN

CLAVE	No. PLANO
LOC 01	01
FECHA: OCT 2022	ESCALA: INDICADA
ACOTACIÓN: METROS	No. EXP.: E-000-22


Aguascalientes
LA CIUDAD DE TU VIDA

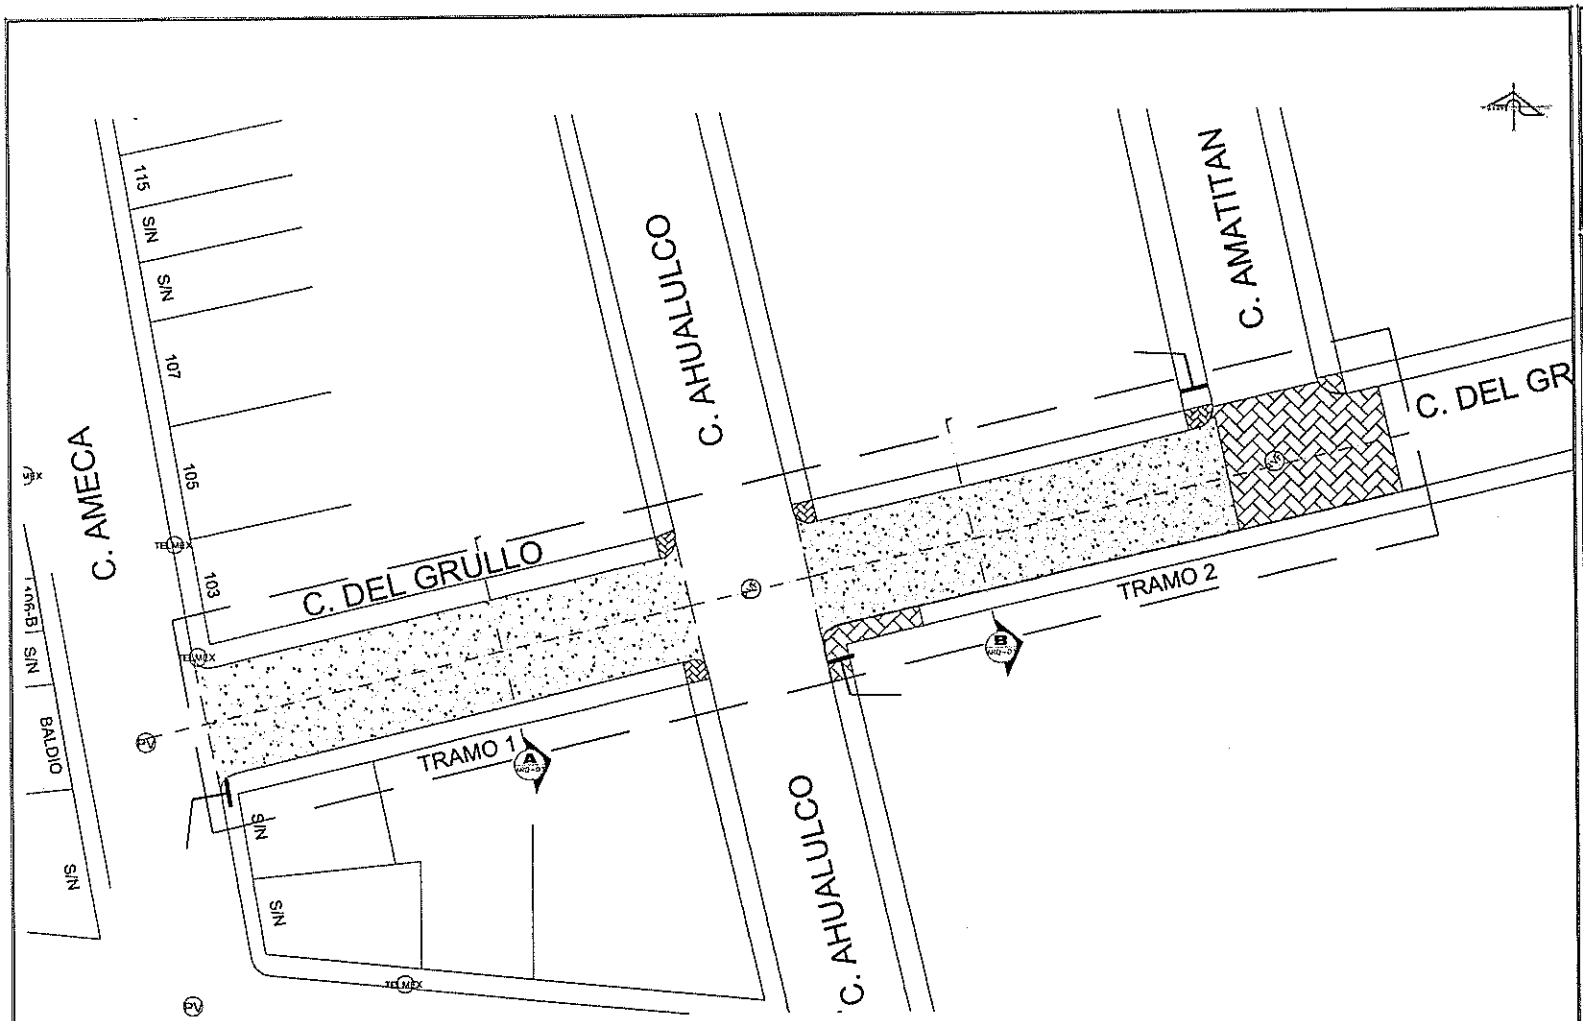

PLANTA DE DEMOLICIONES

ESCALA 1:200 CALLE EL GRULLO

LOCALIZACION:

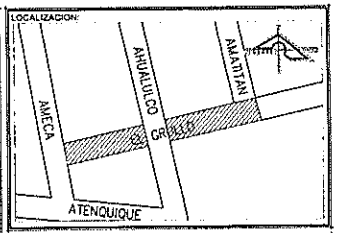

SIMBOLOGÍA

SIMBOLOGIA

DDESPALME DE TERRENO CON MAQUINA CUALQUIER SECCIÓN HASTA EL NIVEL O PROFUNDIDAD QUE MARQUE SUPERVISIÓN EN MATERIAL T I P O 1

DEMOLICION CON EQUIPO PESADO DE BANQUETAS Y/O CONCRETO EXITENTE

NOTA: LA DEMOLICION SE INDICARA EN SITIO AL UBICAR SOLO DESCARGAS Y TOMAS DOMICILIARIAS.

DEMOLICION DE GUARNICIONES

EJE DE PROYECYO

LIMITE DE PROYECTO

NOTAS

LAS DEMOLICIONES DE GUARNICIONES Y DENTELLONES SE DETERMINARA EN EL SITIO DE LA OBRA (SI NO SE ESPECIFICARA EN PROYECTO) UBICANDO Y DANDO PRIORIDAD A LAS MAS DANADAS, DANDO LA AUTORIZACION AL EJECUTOR EL SUPERVISOR DE OBRA DE LA SOPMA

La Dirección de Planeación y Proyectos solo autoriza el proyecto ejecutivo, no es responsable de la correcta ejecución de la obra. Este documento no tiene validez si no presenta las firmas de los responsables para su autorización, así como los sellos respectivos.

PRESIDENTE MUNICIPAL
M.P.P. Leonardo Montañez Castro
SECRETARIO DE OBRAS PÚBLICAS DEL MUNICIPIO DE AGUASCALIENTES
Ing. Miguel Ángel Hulzar Botello

REV	FECHA	OBSERVACIONES

No. Ref. DE LA DEPENDENCIA

RESP. DE PROY. EXTERNO		LOGO EXTERNO
CED. PROFESIONAL		
PROYECTÓ	REVISÓ	AUTORIZÓ


Dirección de Planeación y Proyectos de Obra — Secretaría de Obras Públicas

PROYECTISTA	COORDINADOR
ARQ. ALVARO DAVID MEZA CONTRERAS	ARQ. ALEJANDRO JAIME LEAL
JEFE DE DEP.	DIRECTOR
ARQ. J. JESÚS PALAFOX GONZÁLEZ	M. en ARQ. JOSÉ LUIS JIMÉNEZ GARCÍA

PROYECTO: PAVIMENTO HIDRAULICO CALLE EL GRULLO COLONIA LA SOLEDAD.
UBICACIÓN: ENTRE CALLE AMECA. Y CALLE AMATITAN.
CONTENIDO: PLANTA DE DEMOLICIONES


CLAVE	No. PLANO
DEM 01	04
FECHA: OCT 2022	ESCALA: INDICADA
ACOTACIÓN: METROS	No. EXP.: E-000-22

Aguascalientes
LA CIUDAD DE TU VIDA

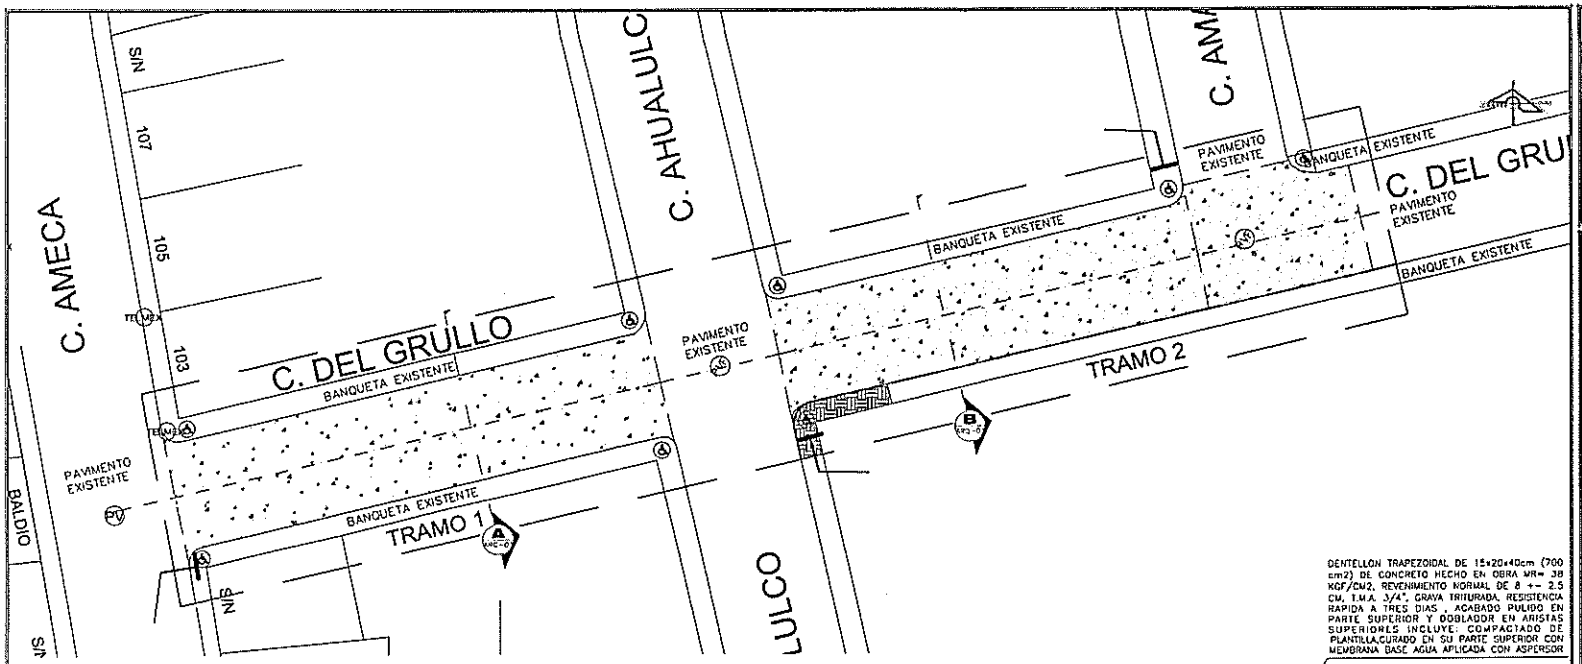

PROYECTO GEOMETRICO

ESCALA 1:200 CALLE EL GRULLO

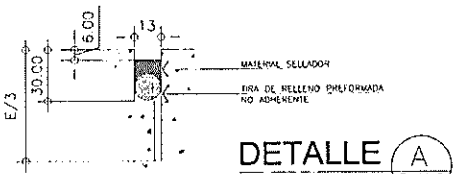


DETALLE A

S/E

COTAS EN mm


E= ESPESOR DE LOSA

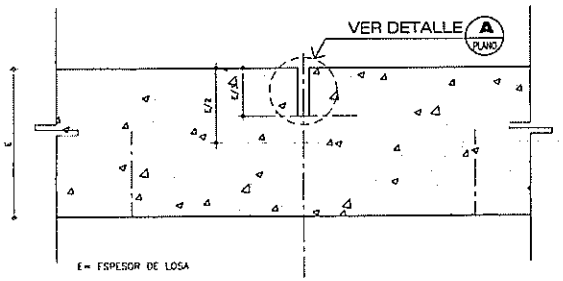

SELLADO DE JUNTAS


S/E

DENTELLON TRAPEZOIDAL DE 15×20×40cm (700 cm2) DE CONCRETO HECHO EN OBRA MR= 38 KGF/CM2, REVENIMIENTO NORMAL DE 8 +- 2.5 CM, T.M.A. 3/4", GRAVA TRITURADA, RESISTENCIA RAPIDA A TRES DIAS , ACABADO PULIDO EN PARTE SUPERIOR Y DOBLADOR EN ARISTAS SUPERIORES INCLUYE: COMPACTADO DE PLANTILLA,CURADO EN SU PARTE SUPERIOR CON MEMBRANA BASE AGUA APLICADA CON ASPERSOR

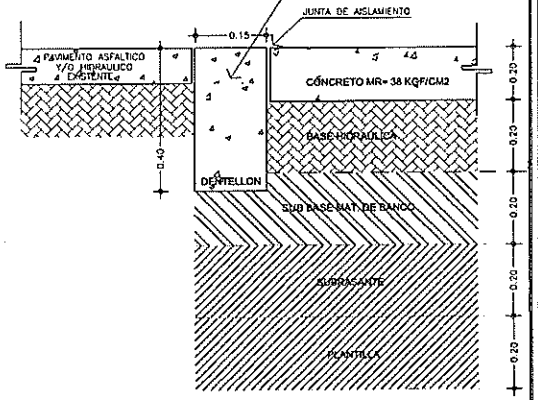

ESTRUCTURA DE PAVIMENTO

MR= 42 KGF/CM2 ESCALA S/E

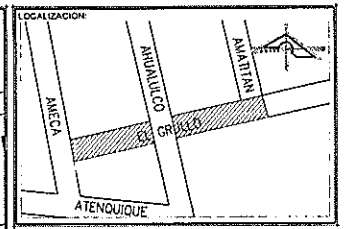

SIMBOLOGIA

SIMBOLOGIA

- EJE DE PROYECTO
- DENTELLON PROPUESTO
- PAVIMENTO HIDRAULICO (MR=38) 15 CM ESPESOR
- BANQUETA PROPUESTA 10 CM ESPESOR
- GUARNICION PROPUESTA SOLO DONDE SE AFECTE PARA TOMAS Y DESCARGAS DOMICILIARIAS
- APLICAR PINTURA EN RAMPA EXISTENTE
- LOSA DIAMANTE A BASE DE CONCRETO PREMEZCLADO (MR=45) 25 CM ESPESOR

CONSTRUCCION DE PAVIMENTO HIDRAULICO A BASE DE CONCRETO PREMEZCLADO MR=38 KG/CM2 TMA 1 1/2" GRAVA TRITURADA, REVENIMIENTO DE 6 A 8 CM FRAGUADO NORMAL DE 15 CM DE ESPESOR MODULADO EN LOSAS DE 3.5 MTS. (ANCHO) X 3.5 MTS (LARGO) COMO MAXIMO, CON CORTES EN LAS LOSAS DE 1/3 DEL ESPESOR DE LA LOSA (5 CM) Y SELLADO CON COLA DE RATA Y MATERIAL ELASTOMERICO Y TIRA PREFORMADA (FOAMTECH DE 1/2X15) EN JUNTAS Y CORTES LONGITUDINALES Y TRANSVERSALES, ASI COMO EL APROCHE CON GUARNICION Y DENTELLON

NOTA 1:

TODOS LOS TRABAJOS SE EJECUTARAN CONFORME LO ESTABLECIDO EN LAS FICHAS TECNICAS DE EL DEPARTAMENTO DE CALIDAD, DIRECCION DE CONSTRUCCION Y CONSERVACION:

- -FT 200 BANQUETAS
- -FT 201 DENTELLON
- -FT 204 GUARNICION TRAPEZOIDAL
- -FT 209 LOSA DIAMANTE
- -FT 218 RAMPA BANQUETA
- -FT 303 BASES
- -FT 306 PLANTILLA
- -FT 309 SUB BASES
- -FT 310 SUB RASANTE
- -FT 505 SELLADO DE GRIETAS Y JUNTAS EN LOSAS DE CONCRETO

NOTA 2:

RESPETAR NIVELES DE PAVIMENTO EXISTENTES, EN SU CASO TOMAR NIVEL DE CORONA DE GUARNICION -15cm COMO REFERENCIA, RENIVELAR TAPAS DE POZOS DE VISITA SEGUN NIVELES EXISTENTES O NUEVOS.

La Dirección de Planeación y Proyectos solo autoriza el proyecto ejecutivo, no es responsable de la correcta ejecución de la obra. Este documento no tiene validez si no presenta las firmas de los responsables para su autorización, así como los sellos respectivos.

PRESIDENTE MUNICIPAL
M.P.P. Leonardo Montañez Castro
SECRETARIO DE OBRAS PUBLICAS DEL MUNICIPIO DE AGUASCALIENTES
Ing. Miguel Ángel Huizar Botello

REV.	FECHA	OBSERVACIONES

V°B° DE LA DEPENDENCIA

RESP. DE PROY. EXTERNO		LOGO EXTERNO
CED. PROFESIONAL		
PROYECTÓ	REVISÓ	AUTORIZÓ

Dirección de Planeación y Proyectos de Obra — Secretaría de Obras Públicas

PROYECTISTA	COORDINADOR
ARQ. ALVARO DAVID MEZA CONTRERAS	ARQ. ALEJANDRO JAIME LEAL
JEFE DE DEP.	DIRECTOR
ARQ. J. JESÚS PALAFOX GONZÁLEZ	M. en ARQ. JOSÉ LUIS JIMÉNEZ GARCÍA


PROYECTO
PAVIMENTO HIDRAULICO CALLE EL GRULLO COLONIA LA SOLEDAD.

UBICACIÓN
ENTRE CALLE AMECA. Y CALLE AMATITAN.

CONTENIDO
PROYECTO GEOMETRICO


CLAVE	No. PLANO
GEO 01	05
FECHA OCT 2022	ESCALA INDICADA
ACOTACIÓN METROS	No. EXP. E-000-22

Aguascalientes
LA CIUDAD DE TU VIDA

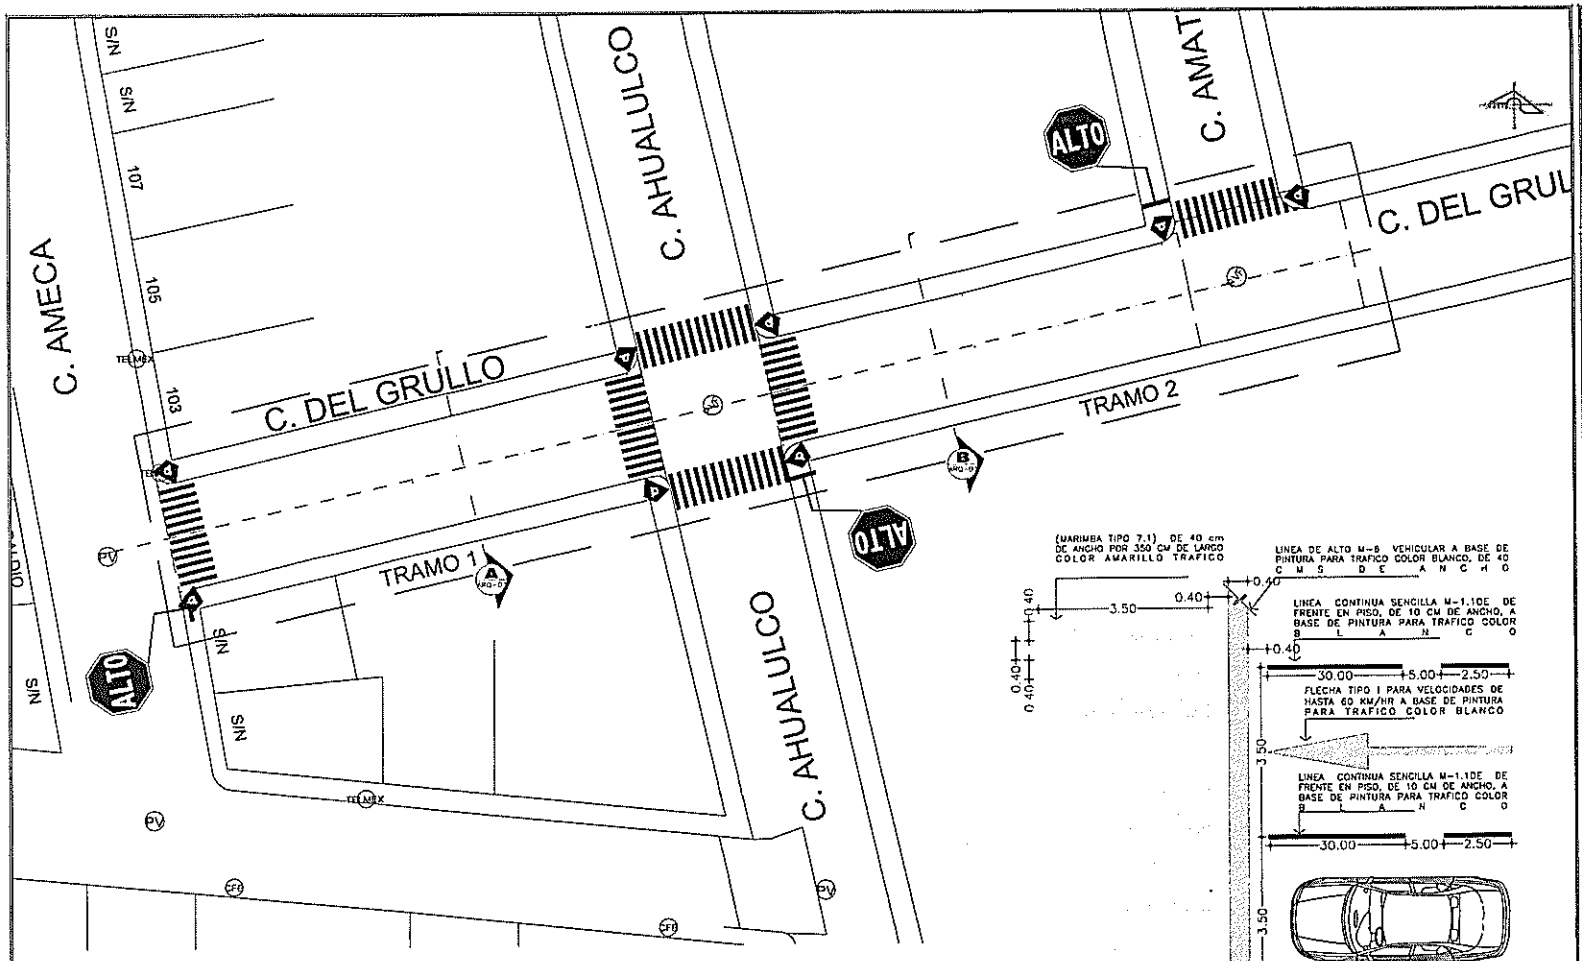

PROYECTO GEOMETRICO


ESCALA 1:200 CALLE EL GRULLO

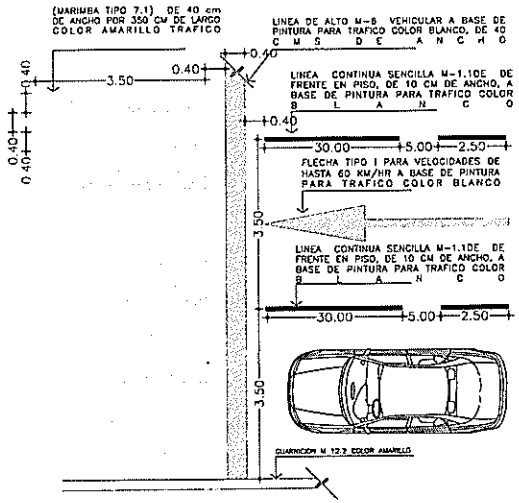

DETALLE TIPO

TRAZO PINTURA EN CRUCEROS SIN ESCALA

LOCALIZACION:

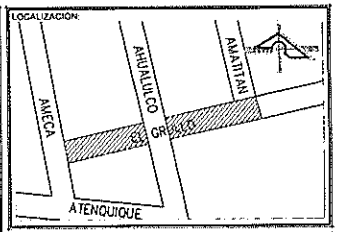

SIMBOLOGÍA

NOTA:
Se aplicará en todos los señalamientos horizontales pintura para trafico base solvente tipo alquidal de secado rápido, que cumpla con las especificaciones n-cmt-5-01-001/05, n-pry-car-10-01-002/13 de la SCT aplicadas al día de hoy.

M-12.1, M12.2 APLICADA SOBRE GUARNICIONES Y DENTELLONES DE CUALQUIER COLOR

Se aplicará en todos los señalamientos horizontales pintura para trafico Termoplastica tipo alquidal de secado rápido, que cumpla con las especificaciones n-cmt-5-01-001/05, n-pry-car-10-01-002/13 de la SCT aplicadas al día de hoy.

M - 1.2, LÍNEA DISCONTINUA SENCILLA DE DIVISIÓN DE CARRILES DE FRENTE EN PISO, DE 10 CM DE ANCHO
M - 3.3, CONTINUA IZQUIERDA, PARA VIALIDADES URBANAS DE FRENTE EN PISO, SEPARADA 15 CM. DE LA GUARNICION, COLOR AMARILLO
M - 4, PARA INDICAR LÍNEA GUÍA EN ZONA DE TRANSICIÓN DE FRENTE EN PISO, DESARROLLO DE 2.00 X 0.10 MTS, CON UNA SEPARACIÓN DE 4.00 MTS ENTRE SI PROMEDIO
M - 5, PARA INDICAR ENTRADA Y SALIDA EN BIFURCACIONES
M - 6, PARA INDICAR ALTO EN CRUCEROS, COLOR BLANCO
M - 7.1, PARA INDICAR " CRUCE PEATONAL EN VIAS PRIMARIAS" COLOR AMARILLO
M - 11.1, "FLECHA SENCILLA" PARA INDICAR SENTIDO DE CIRCULACIÓN
M - 11.1, "FLECHA CABEZA DOBLE" PARA INDICAR SENTIDO DE CIRCULACIÓN (VUELTA IZQUIERDA O DERECHA)

NOTA:
Nota1: Se aplicará en todos los señalamientos horizontales pintura para trafico base solvente tipo alquidal de secado rápido, que cumpla con las especificaciones n-cmt-5-01-001/05, n-pry-car-10-01-002/13 de la SCT aplicadas al día de hoy.

Nota2: Dosificación de micro esfera
La cantidad de esferas de vidrio en la película de pintura en húmedo, según su tipo, será la que se indica en la Tabla.

TABLA B: Cantidad de esferas de vidrio en la película de pintura en humedo.

TIPO DE PINTURA	ESPESOR DE LA PELICULA DE PINTURA EN HÚMEDO U.U.	CANTIDAD DE ESFERAS kg/m2		TIPO DE GRANULOMETRIA
		INTEGRADAS	SEMBRADAS, MINIMO	
BASE SOLVENTE	0.38 A 0.50	---	0.330	I
BASE AGUA	0.38 A 0.50	---	0.330	I o II
TERMOPLASTICA	1.50 A 0.88	0.57 A 0.89	0.330	II

La Dirección de Planeación y Proyectos solo autoriza el proyecto ejecutivo, no es responsable de la correcta ejecución de la obra. Este documento no tiene validez si no presenta las firmas de los responsables para su autorización, así como los sellos respectivos.

PRESIDENTE MUNICIPAL
M.P.P. Leonardo Montañez Castro
SECRETARIO DE OBRAS PUBLICAS DEL MUNICIPIO DE AGUASCALIENTES
Ing. Miguel Ángel Huizar Botello

REV	FECHA	OBSERVACIONES

Vo. Bo. DE LA DEPENDENCIA

RESP. DE PROY. EXTERNO		LOGO EXTERNO
CED. PROFESIONAL		
PROYECTÓ	REVISÓ	AUTORIZÓ


Dirección de Planeación y Proyectos de Obra — Secretaría de Obras Públicas

PROYECTISTA	COORDINADOR
ARQ. ALVARO DAVID MEZA CONTRERAS	ARQ. ALEJANDRO JAIME LEAL
JEFE DE DEP.	DIRECTOR
ARQ. J. JESÚS PALAFOX GONZÁLEZ	M. en ARQ. JOSÉ LUIS SÁNCHEZ GARCÍA

PROYECTO
PAVIMENTO HIDRAULICO CALLE EL GRULLO COLONIA LA SOLEDAD.
UBICACIÓN
ENTRE CALLE AMECA, Y CALLE AMATITAN.
CONTENIDO
PROYECTO GEOMETRICO

CLAVE	No. PLANO
GEO 02	06
FECHA OCT 2022	ESCALA INDICADA
ACOTACIÓN METROS	No. EXP. E-000-22

Aguascalientes
LA CIUDAD DE TU VIDA

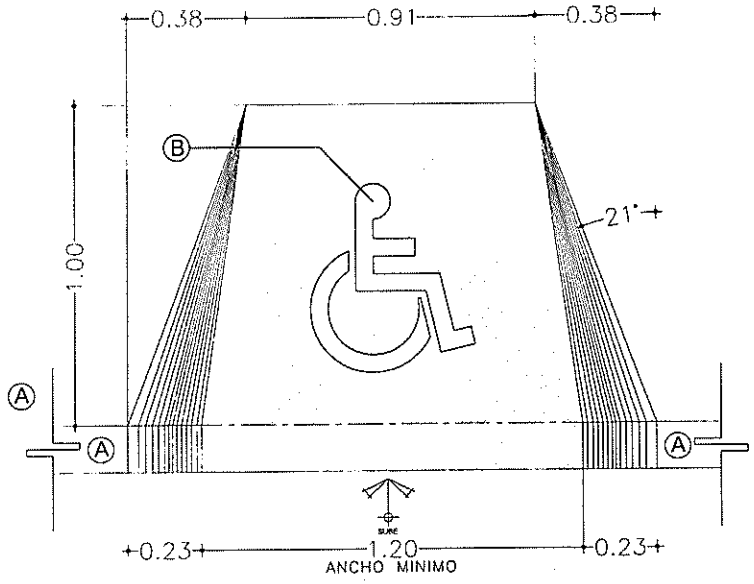


DETALLE DE LOGOTIPO ''A'' EN RAMPA

VISTA EN PLANTA S/E

Ⓐ SUMINISTRO Y APLICACIÓN DE PINTURA BASE SOLVENTE COLOR AZUL (PANTONE 294) EN RAMPAS PARA DISCAPACITADOS


Ⓑ SUMINISTRO Y APLICACIÓN DE LOGOTIPO ''A'' (SILLA DE RUEDAS) EN PINTURA BASE SOLVENTE COLOR BLANCO EN RAMPAS PARA DISCAPACITADOS TAMAÑO Y DISEÑO SEGÚN PLANOS.

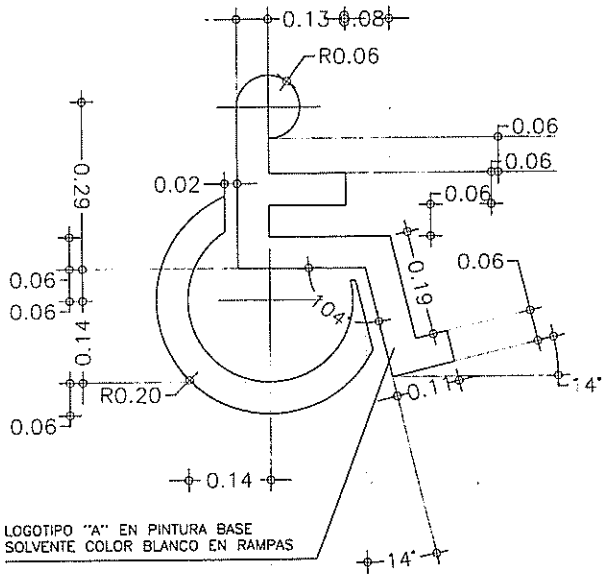

LOGOTIPO "A" EN PINTURA BASE SOLVENTE COLOR BLANCO EN RAMPAS

DETALLE DE LOGOTIPO ''A'' EN RAMPA

VISTA EN PLANTA S/E

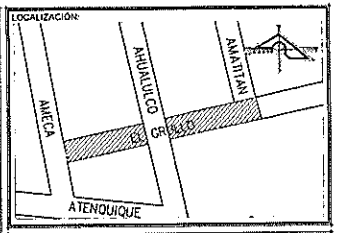

SIMBOLOGÍA

NOTA:
Nota1: Se aplicará en todos los señalamientos horizontales pintura para tráfico base solvente tipo alquídal de secado rápido, que cumpla con las especificaciones n-cmt-5-01-001/05, n-pry-car-10-01-002/13 de la SCT aplicadas al día de hoy.

Nota2: Dosificación de micro esfera
La cantidad de esferas de vidrio en la película de pintura en húmedo, según su tipo, será la que se indica en la Tabla.

TABLA B: Cantidad de esferas de vidrio en la película de pintura en humedo.

TIPO DE PINTURA	ESPESOR DE LA PELICULA DE PINTURA EN HUMEDO um	CANTIDAD DE ESFERAS kg/m2		TIPO DE GRANULOMETRIA
		INTEGRADAS	SEMBRADAS, MINIMO	
BASE SOLVENTE	0.38 A 0.58	----	0.350	I
BASE AGUA	0.38 A 0.58	----	0.350	IAB
TERMOPLASTICA	1.50 A 0.69	0.51 A 0.69	0.350	E

La Dirección de Planeación y Proyectos solo autoriza el proyecto ejecutivo, no es responsable de la correcta ejecución de la obra. Este documento no tiene validez si no presenta las firmas de los responsables para su autorización, así como los sellos respectivos.

PRESIDENTE MUNICIPAL
M.P.P. Leonardo Montañez Castro
SECRETARIO DE OBRAS PÚBLICAS DEL MUNICIPIO DE AGUASCALIENTES
Ing. Miguel Ángel Huizar Botello

REV	FECHA	OBSERVACIONES

No. DE LA PERSPECTIVA

RESP. DE PROY. EXTERNO		LOGO EXTERNO
CED. PROFESIONAL		
PROYECTO	REVISO	AUTORIZO

Dirección de Planeación y Proyectos de Obra — Secretaría de Obras Públicas

PROYECTISTA	COORDINADOR
ARQ. ALVARO DAVID MEZA CONTRERAS	ARQ. ALEJANDRO JAIME LEAL
JEFE DE DEP.	DIRECTOR
ARQ. J. JESÚS PALAFOX GONZÁLEZ	M. en ARQ. JOSÉ LUIS JIMÉNEZ GARCÍA

PROYECTO
PAVIMENTO HIDRAULICO CALLE EL GRULLO COLONIA LA SOLEDAD.
UBICACIÓN
ENTRE CALLE AMECA, Y CALLE AMATITAN.
CONTENIDO
DETALLES SEÑALETICA HORIONTAL


CLAVE	No. PLANO
DSH 01	07
FECHA OCT 2022	ESCALA INDICADA
ACOTACIÓN METROS	No. EXP. E-000-22

Aguascalientes
LA CIUDAD DE TU VIDA

SEÑALES RESTRICTIVAS

SIMBOLO	CLAVE	DESCRIPCIÓN	DIMENSIÓN (cm)	UNIDAD	COLOR	CANTIDAD
ALTO	SR-6	ALTO	30 X LADO	PZA	ROJO REFLEJANTE	3
CEDA EL PASO	SR-7	CEDA EL PASO	85 X LADO	PZA	BLANCO REFLEJANTE	0
50 KM/H	SR-9	VELOCIDAD 50 KM/H	71 X 71	PZA	BLANCO REFLEJANTE CON ANILLO ROJO REFLEJANTE	0
60 KM/H	SR-9	VELOCIDAD 60 KM/H	71 X 71	PZA	BLANCO REFLEJANTE CON ANILLO ROJO REFLEJANTE	0
E	SR-21	ESTACIONAMIENTO PERMITIDO	71 X 71	PZA	BLANCO REFLEJANTE CON ANILLO ROJO REFLEJANTE	0


DISPOSICIÓN DE LAS OREJAS DE SUJECIÓN EN SEÑALES BAJAS

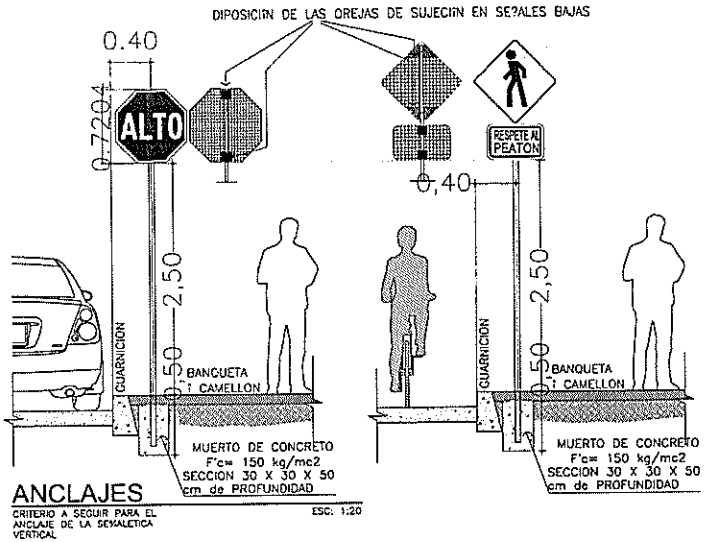

ANCLAJES


CRITERIO A SEGUIR PARA EL ANCLAJE DE LA SEÑALETICA VERTICAL

ESC. 1:20

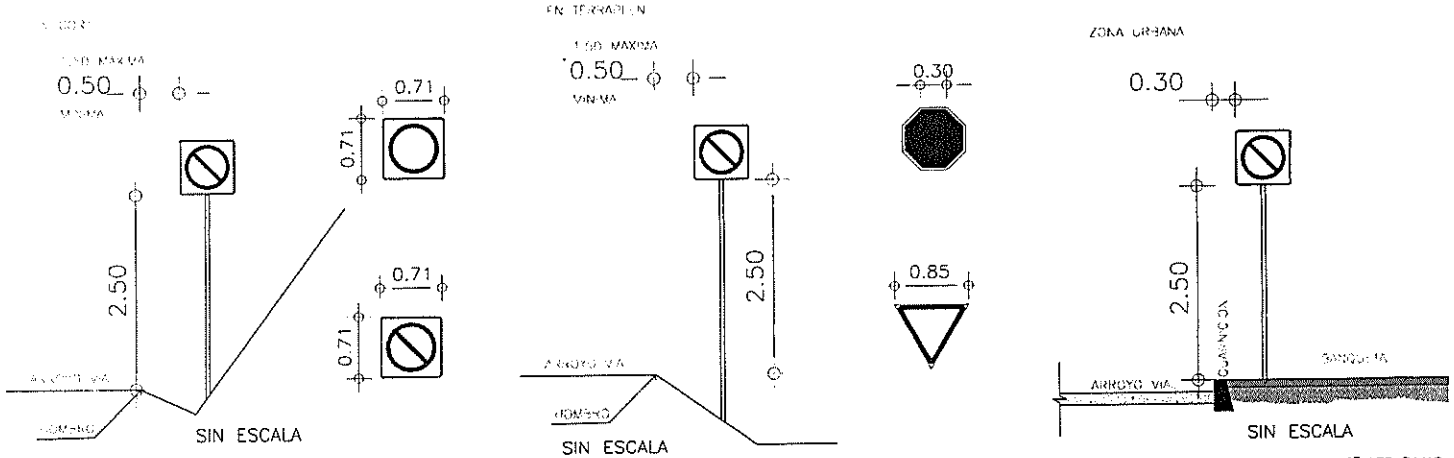

NOTA: LAS SECCIONES ESTRUCTURALES SE ENCUENTRAN EL APARTADO II.7.3. ESTRUCTURA DE SOPORTE DE SEÑALES BAJAS. DEL MANUAL DE SEÑALAMIENTO VIAL DE LA SCT

LOCALIZACION.

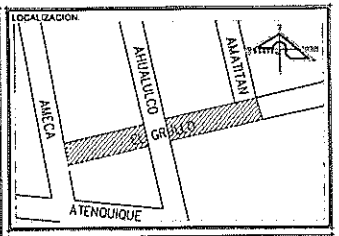

SIMBOLOGÍA

NOTA:
Nota1: Se aplicará en todos los señalamientos horizontales pintura para tráfico base solvente tipo alquidal de secado rápido, que cumpla con las especificaciones n-cmt-5-01-001/05, n-pry-car-10-01-002/13 de la SCT aplicadas al día de hoy.

Nota2: Dosificación de micro esfera
La cantidad de esferas de vidrio en la película de pintura en húmedo, según su tipo, será la que se indica en la Tabla.

TABLA 8: Cantidad de esferas de vidrio en la película de pintura en humedo.

TIPO DE PINTURA	ESPESOR DE LA PELICULA DE PINTURA EN HÚMEDO MM	CANTIDAD DE ESFERAS kg/m2		TIPO DE GRANULOMETRIA
		INTEGRADAS	SEMBRADAS, MINIMO	
BASE SOLVENTE	0.38 A 0.50	----	0.330	I
BASE AGUA	0.38 A 0.50	----	0.330	I o II
TERMOPLASTICA	1.50 A 0.68	0.57 A 0.89	0.330	II

La Dirección de Planeación y Proyectos solo autoriza el proyecto ejecutivo, no es responsable de la correcta ejecución de la obra. Este documento no tiene validez si no presenta las firmas de los responsables para su autorización, así como los sellos respectivos.

PRESIDENTE MUNICIPAL
M.P.P. Leonardo Montañez Castro
SECRETARIO DE OBRAS PÚBLICAS DEL MUNICIPIO DE AGUASCALIENTES
Ing. Miguel Ángel Hulzar Botello

REV	FECHA	OBSERVACIONES

No. De DEPENDENCIA

RESP. DE PROY. EXTERNO		LOGO EXTERNO
CED PROFESIONAL		
PROYECTO	REVISO	AUTORIZÓ

Dirección de Planeación y Proyectos de Obra — Secretaría de Obras Públicas

PROYECTISTA	COORDINADOR
ARQ. ALVARO DAVID MEZA CONTRERAS	ARQ. ALEJANDRO JAIME LEAL
JEFE DE DEP.	DIRECTOR
ARQ. J. JESÚS PALAFOX GONZÁLEZ	M. en ARQ. JOSÉ LUIS JIMÉNEZ GARCÍA

PROYECTO
PAVIMENTO HIDRAULICO CALLE EL GRULLO COLONIA LA SOLEDAD.

UBICACIÓN
ENTRE CALLE AMECA, Y CALLE AMATITAN.

CONTENIDO
DETALLES SEÑALETICA VERTICAL


CLAVE	No. PLANO
DSV 01	08
FECHA OCT 2022	ESCALA INDICADA
ACOTACIÓN METROS	No. EXP. E-000-22

Aguascalientes
LA CIUDAD DE TU VIDA

PISO EN RAMPAS DE 10.00 cm DE ESPESOR DE CONCRETO SIMPLE F'c=150 Kg/cm2, HECHO EN OBRA, TMA 3/4 19mm, GRAVA TRITURADA, ACABADO LAVADERO, INCLUYE: ESTAMPADO DE SIMBOLOGÍA COMO INDICA EL PROYECTO, CIMBRADO, NIVELADO, VIBRADO, CURADO CON MEMBRANA BASE AGUA

RAMPA PEATONAL TIPO 1


VISTA EN PLANTA ESC. 1:10

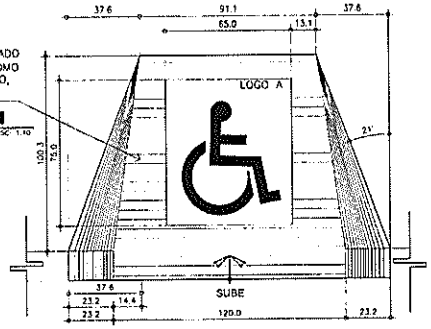

PISO EN RAMPAS DE 10.00 cm DE ESPESOR DE CONCRETO SIMPLE F'c=150 Kg/cm2, HECHO EN OBRA, TMA 3/4 19mm, GRAVA TRITURADA, ACABADO LAVADERO, INCLUYE: ESTAMPADO DE SIMBOLOGÍA COMO INDICA EL PROYECTO, CIMBRADO, NIVELADO, VIBRADO, CURADO CON MEMBRANA BASE AGUA

RAMPA PEATONAL TIPO 1


VISTA FRONTAL

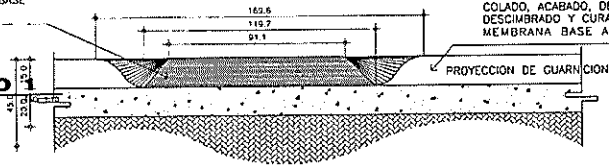

PISO EN RAMPAS DE 10.00 cm DE ESPESOR DE CONCRETO SIMPLE F'c=150 Kg/cm2, HECHO EN OBRA, TMA 3/4 19mm, GRAVA TRITURADA, ACABADO LAVADERO, INCLUYE: ESTAMPADO DE SIMBOLOGÍA COMO INDICA EL PROYECTO, CIMBRADO, NIVELADO, VIBRADO, CURADO CON MEMBRANA BASE AGUA

RAMPA PEATONAL TIPO 1

VISTA LATERAL ESC. 1:10

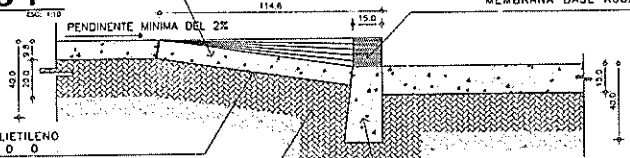

MEMBRANA IMPERMEABLE A BASE DE POLIETILENO
N E G R O No. 6 0 0


RELLENO COMPACTADO AL 90% CON MATERIAL DE BANCO EN CAPAS DE 20 CM UTILIZANDO BAILARINA, INCLUYE: SUMINISTRO DE TEPETATE EN LA OBRA, ABUNDAMIENTO, ACARREOS DENTRO DE LA OBRA, CRIBADO, RETIRO DE MATERIAL, MANO DE OBRA Y EQUIPO, PRUEBA DE CONTROL DE CALIDAD.

CONSTRUCCION DE GUARNICION RECTA Y/O CURVA TRAPEZOIDAL DE 15X20X40 CM DE SECCION CON CONCRETO PREMEZCLADO F'C= 150 KG/CM2, REVENIMIENTO DE 8 A 10 CM, T.M.A. 1 1/2" 38 MM, GRAVA TRITURADA, ACABADO PULIDO EN PARTE DE SUPERIOR Y DOBLADOR EN ARISTAS SUPERIORES, INCLUYE: COMPACTADO DE PLANTILLA, CIMBRADO, COLADO, ACABADO, DESCIMBRADO, ALINEADO, NIVELADO, DESCIMBRADO Y CURADO EN SU PARTE SUPERIOR CON MEMBRANA BASE AGUA A RAZON DE 1 LTO/M2.

CONSTRUCCION DE GUARNICION RECTA Y/O CURVA TRAPEZOIDAL DE 15X20X40 CM DE SECCION CON CONCRETO PREMEZCLADO F'C= 150 KG/CM2, REVENIMIENTO DE 8 A 10 CM, T.M.A. 1 1/2" 38 MM, GRAVA TRITURADA, ACABADO PULIDO EN PARTE DE SUPERIOR Y DOBLADOR EN ARISTAS SUPERIORES, INCLUYE: COMPACTADO DE PLANTILLA, CIMBRADO, COLADO, ACABADO, DESCIMBRADO, ALINEADO, NIVELADO, DESCIMBRADO Y CURADO EN SU PARTE SUPERIOR CON MEMBRANA BASE AGUA A RAZON DE 1 LTO/M2.


DENTELLON TRAPEZOIDAL DE 15-20X40 CM DE SECCIÓN, CON CONCRETO PREMEZCLADO MR=38 KGF/CM2, TMA 1 1/2", R.R 14 DÍAS. REVENIMIENTO NORMAL DE 10+-2 CM, GRAVA TRITURADA, ACABADO CON DOBLADOR Y PULIDO. INCLUYE: TRAZO, NIVELACIÓN, CIMBRADO, COLADO, VIBRADO, DESCIMBRADO, JUNTA A BASE DE ESPUMA DE POLIETILENO DE CELDAS CERRADAS DE 1/2" EN JUNTAS FRÍAS LONGITUDINALES NO MAYOR A 30 MTS CORTE TRANSVERSAL CON CORTADORA A 1/3 DE SU ESPESOR MÁXIMO @ 3 MTS, RELLENO PREFORMADO Y SELLADOR AUTONIVELANTE ASÍ COMO DE AISLAMIENTO CON OTRO ELEMENTO, Y CURADO CON MEMBRANA QUÍMICA APLICADA CON ASPERSOR Y LIMPIEZA, SE DEBERÁ TENER CUIDADO EN EL NIVEL DE DESPLANTE PUES NO SE ACEPTAN ELLENOS FUERA DE LA BASE NUEVA, TRABAJO T E R M I N A D O

DENTELLON TRAPEZOIDAL DE 15-20X40 CM DE SECCION, CON CONCRETO PREMEZCLADO MR=38 KGF/CM2, TMA 1 1/2", R.R 14 DIAS. REVENIMIENTO NORMAL DE 10+-2 CM, GRAVA TRITURADA, ACABADO CON DOBLADOR Y PULIDO. INCLUYE: TRAZO, NIVELACION, CIMBRADO, COLADO, VIBRADO, DESCIMBRADO, JUNTA A BASE DE ESPUMA DE POLIETILENO DE CELDAS CERRADAS DE 1/2" EN JUNTAS FRIAS LONGITUDINALES NO MAYOR A 30 MTS CORTE TRANSVERSAL CON CORTADORA A 1/3 DE SU ESPESOR MAXIMO @ 3 MTS, RELLENO PREFORMADO Y SELLADOR AUTONIVELANTE ASI COMO DE AISLAMIENTO CON OTRO ELEMENTO, Y CURADO CON MEMBRANA QUIMICA APLICADA CON ASPERSOR Y LIMPIEZA, SE DEBERA TENER CUIDADO EN EL NIVEL DE DESPLANTE PUES NO SE ACEPTAN ELLENOS FUERA DE LA BASE NUEVA, TRABAJO T E R M I N A D O

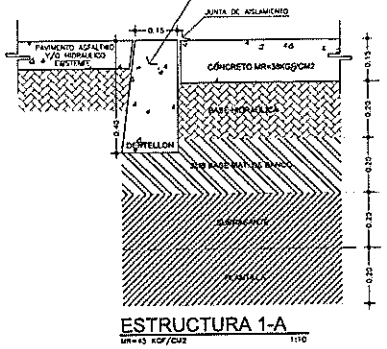

ESTRUCTURA 1-A


MR=45 KGF/CM2 1:10

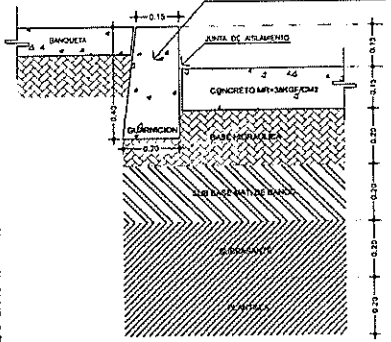

ESTRUCTURA 1

MR=45 KGF/CM2 S/E

LOCALIZACIÓN

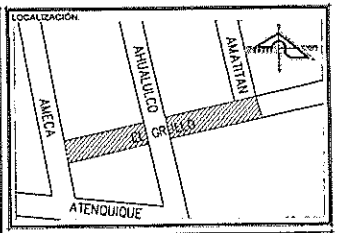

SIMBOLOGÍA

NOTA 1:

TODOS LOS TRABAJOS SE EJECUTARAN CONFORME LO ESTABLECIDO EN LAS FICHAS TECNICAS DE EL DEPARTAMENTO DE CALIDAD, DIRECCION DE CONSTRUCCION Y CONSERVACION:

- FT 200 BANQUETAS
- FT 201 DENTELLON
- FT 204 GUARNICION TRAPEZOIDAL
- FT 209 LOSA DIAMANTE
- FT 216 RAMPA BANQUETA
- FT 303 BASES
- FT 308 PLANTILLA
- FT 309 SUB BASES
- FT 310 SUB RASANTE
- FT 505 SELLADO DE GRIETAS Y JUNTAS EN LOSAS DE CONCRETO

NOTA 2:

RESPETAR NIVELES DE PAVIMENTO EXISTENTES, EN SU CASO TOMAR NIVEL DE CORONA DE GUARNICION -15cm COMO REFERENCIA, REINSTALAR TAPAS DE POZOS DE VISITA SEGUN NIVELES EXISTENTES O NUEVOS.

La Dirección de Planeación y Proyectos solo autoriza el proyecto ejecutivo, no es responsable de la correcta ejecución de la obra. Este documento no tiene validez si no presenta las firmas de los responsables para su autorización, así como los sellos respectivos.

PRESIDENTE MUNICIPAL
M.P.P. Leonardo Montañez Castro
SECRETARIO DE OBRAS PÚBLICAS DEL MUNICIPIO DE AGUASCALIENTES
Ing. Miguel Ángel Huizar Botello

REV	FECHA	OBSERVACIONES

Vo. Bo. DE LA DEPENDENCIA

RESP. DE PROY. EXTERNO		LOGO EXTERNO
CED. PROFESIONAL		
PROYECTÓ	REVISÓ	AUTORIZÓ

Dirección de Planeación y Proyectos de Obra — Secretaría de Obras Públicas

PROYECTISTA	COORDINADOR
ARQ. ALVARO DAVID MEZA CONTRERAS	ARQ. ALEJANDRO JAIME LEAL
JEFE DE DEP.	DIRECTOR
ARQ. J. JESUS PALAFOX GONZÁLEZ	M. en ARQ. JOSE LUIS JIMÉNEZ GARCÍA


PROYECTO
PAVIMENTO HIDRAULICO CALLE EL GRULLO COLONIA LA SOLEDAD.

UBICACIÓN
ENTRE CALLE AMECA, Y CALLE AMATITAN.

CONTENIDO
PLANO DE DETALLES RAMPA

CLAVE	No. PLANO
DETC 02	10
FECHA: OCT 2022	ESCALA: INDICADA
ACOTACION: METROS	No. EXP.: E-000-22


Aguascalientes
LA CIUDAD DE TU VIDA

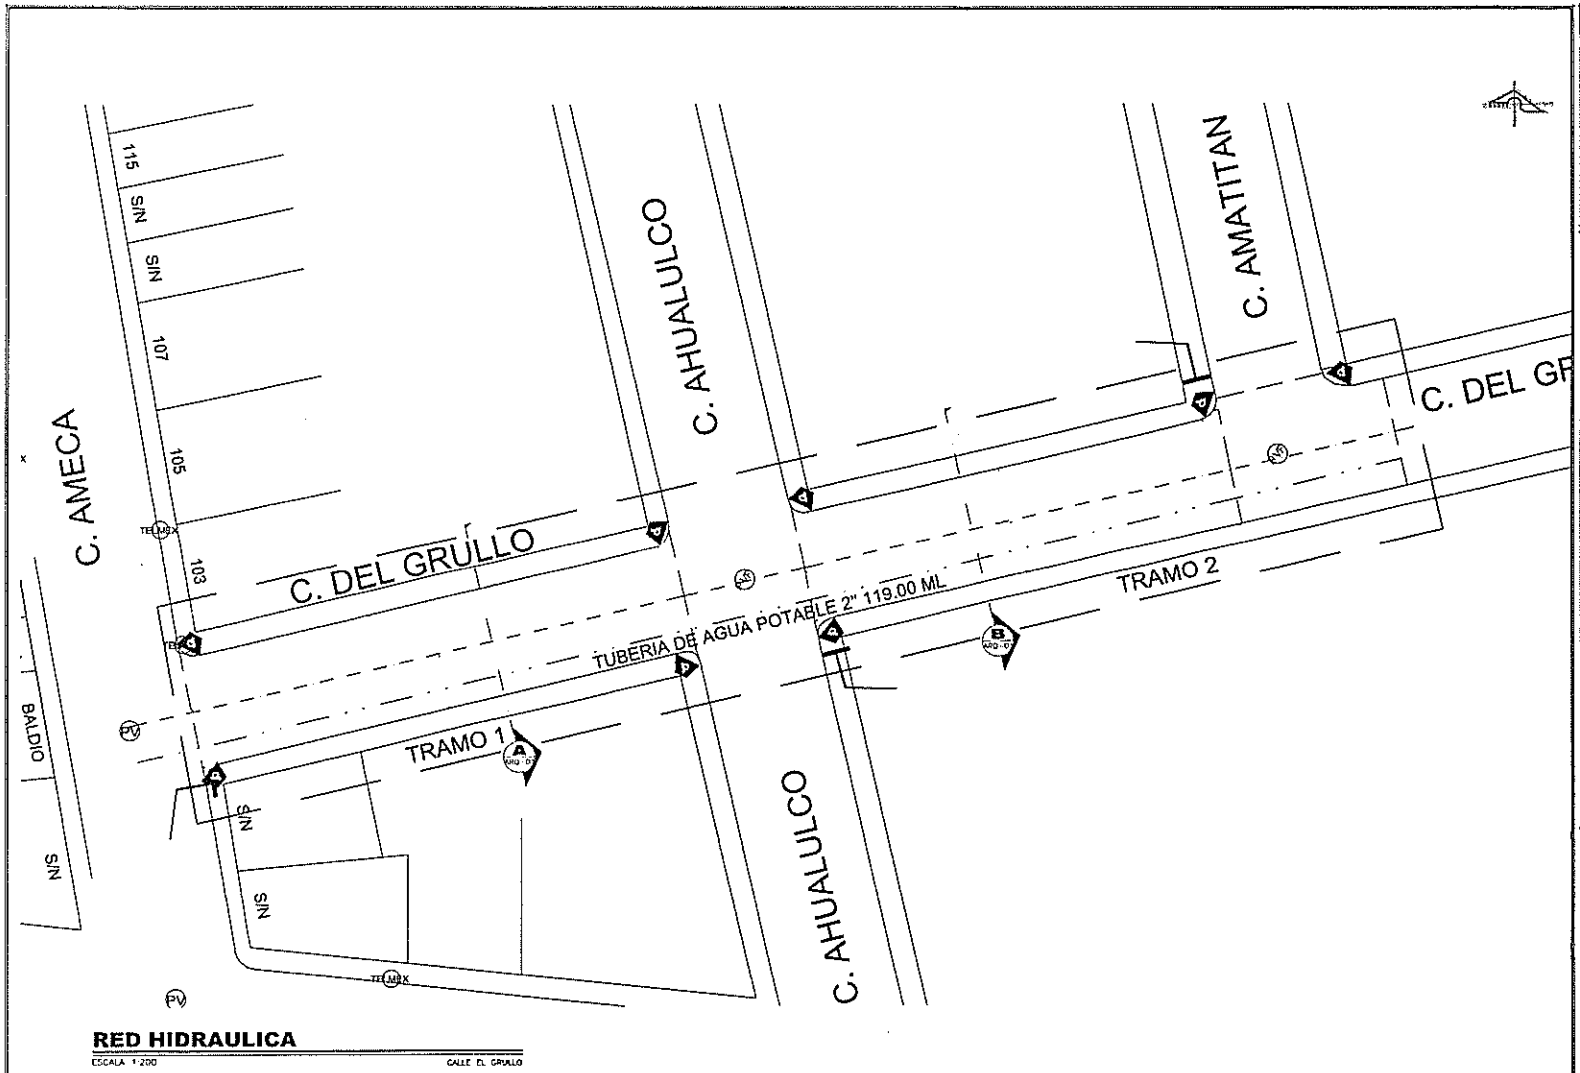

RED HIDRAULICA

ESCALA 1:200 — CALLE EL GRULLO

LOCALIZACIÓN:

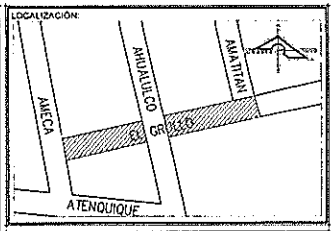

SIMBOLOGIA

- LIMITE DE PROYECTO
- NUMERO DE CASA
- CAJA DE VALVULAS
- INDICA LA LONGITUD DEL TRAMO EN METROS
- RED AGUA POTABLE
- INDICA EL DIAMETRO DEL TUBO EN PULGADAS

FoFo: TUBERIA DE ACERO FUNDIDO
A.C: TUBERIA ASBESTO CONCRETO

SIMBOLOGIA DE RED EXISTENTE

- RED AGUA POTABLE P.V.C. 12"
- RED AGUA POTABLE P.V.C. 8"
- RED AGUA POTABLE P.V.C. 6"
- RED AGUA POTABLE P.V.C. 4"
- RED AGUA POTABLE P.V.C. 3"
- RED AGUA POTABLE P.V.C. 2.5"
- RED AGUA POTABLE P.V.C. 2"

ESPECIFICACIONES

1. ESTE PLANO SE USARA SOLAMENTE PARA LA INSTALACION DE AGUA POTABLE.
2. CUALQUIER CAMBIO DE PROYECTO DEBERA SER AVALADO POR PROYECTOS SOPMA Y/O CCAPAMA.
3. LAS REVISIONES DEBERAN HACERSE CON LA MINUCIOSIDAD NECESARIA PARA COMPROBAR LA EXACTA CORRESPONDENCIA DE LOS TRABAJOS CON LO INDICADO EN EL PROYECTO; LAS ESPECIFICACIONES Y ORDENES COMPLEMENTARIAS.
4. TODA LA INSTALACIÓN DEBERÁ DE CUMPLIR CON LOS REQUISITOS Y LINEAMIENTOS QUE MARCA EL "MANUAL DE AGUA POTABLE, ALCANTARILLADO Y SANEAMIENTO", DE LA COMISIÓN NACIONAL DEL AGUA.
5. SE DEBE DE CUMPLIR CON LA HERMETICIDAD DE LA INSTALACIÓN DE ACUERDO A LA NORMA NT-001-CNA-2001 Y NOM-013-CONAGUA-2000.
6. LAS TUBERIAS DEBEN DE CUMPLIR CON LA NORMA NMX-E-143 Y LAS CONEXIONES CON LA NORMA NMX-E-211/2-1993.
7. LA PROFUNDIDAD MINIMA DE COLOCACION DE TUBERIA SERA DE 0.70 M DE NIVEL DE TERRENO O PISO TERMINADO A LOMO SUPERIOR DE TUBO.
8. TODOS LOS MATERIALES CON LOS QUE SE EJECUTEN LAS INSTALACIONES SERAN NUEVOS Y DE PRIMERA CALIDAD Y CUANDO EXISTA ALGUNA DUDA O DISCREPANCIA RESPECTO A DICHA CALIDAD, ESTA SERA RESUELTA POR EL SUPERVISOR, POR LO QUE SE REFIERE A LA CALIDAD DE LOS MATERIALES DEBERA SUJETARSE A LO ESTABLECIDO AL EFECTO EN LAS NORMAS OFICIALES MEXICANAS Y DE LA DIRECCION GENERAL DE NORMAS DE LA SECRETARIA DE COMERCIO Y FOMENTO.
9. LA TUBERIA NO SE DEBERA DOBLAR, PARA EVITAR REDUCCION DE SU SUCCION Y DE SU UNIFORMIDAD EN SU ESPESOR DEL MATERIAL.
10. LAS TUBERIAS DEBERAN DE CONSERVARSE LIMPIAS TANTO EN SU EXTERIOR COMO EN SU INTERIOR HASTA LA TERMINACION TOTAL Y ENTREGA DE LOS TRABAJOS.
11. LOS TRAMOS RECTOS DE TUBERIA ENTRE CONEXIONES, DEBERAN QUEDAR ALINEADOS SEAN VERTICALES U HORIZONTALES.
12. LOS CORTES EN LOS TUBOS SE EJECUTARAN EN ANGULO RECTO CON RESPECTO AL EJE LONGITUDINAL DEL MISMO.

La Dirección de Planeación y Proyectos solo autoriza el proyecto ejecutivo, no es responsable de la correcta ejecución de la obra. Este documento no tiene validez si no presenta las firmas de los responsables para su autorización, así como los sellos respectivos.

PRESIDENTE MUNICIPAL
M.P.P. Leonardo Montañez Castro
SECRETARIO DE OBRAS PUBLICAS DEL MUNICIPIO DE AGUASCALIENTES
Ing. Miguel Ángel Huizar Botello

REV	FECHA	OBSERVACIONES

Vo. Bo. DE LA DEPENDENCIA

RESP. DE PROY. EXTERNO		LOGO EXTERNO
CED. PROFESIONAL		
PROYECTO	REVISO	AUTORIZO

Dirección de Planeación y Proyectos de Obra — Secretaría de Obras Públicas

PROYECTISTA	COORDINADOR
ARQ. ALVARO DAVID MEZA CONTRERAS	ARQ. ALEJANDRO JAIME LEAL
JEFE DE DEP.	DIRECTOR
ARQ. J. JESÚS PALAFOX GONZÁLEZ	M. en ARQ. JOSÉ LUIS JIMÉNEZ GARCÍA

PROYECTO: PAVIMENTO HIDRAULICO CALLE EL GRULLO COLONIA LA SOLEDAD.
UBICACIÓN: ENTRE CALLE AMECA, Y CALLE AMATITAN.
CONTENIDO: RED HIDRAULICA

CLAVE	No. PLANO
HID 01	15
FECHA: OCT 2022	ESCALA: INDICADA
ACOTACIÓN: METROS	No. EXP.: E-000-22

Aguascalientes — LA CIUDAD DE TU VIDA