Aguascalientes
LA CIUDAD DE TU VIDA

Dirección de Programación Presupuestal
Núm. Oficio AMPP/0457/22
Aguascalientes, Ags. 20 de Octubre del 2022
Asunto: Validación de Expediente Técnico

C.P. SERGIO ARTURO LOZANO GONZÁLEZ
SECRETARIO DE FINANZAS MUNICIPALES
P R E S E N T E

Con fundamento en los artículos 17 fracción XV, 60 fracción XVI y 76 fracción VI del Reglamento del Sistema Integral de Desarrollo Municipal y del Instituto Municipal de Planeación y Evaluación de Aguascalientes, hago referencia al oficio SOPMA/2262/2022 recibido por este Instituto el día 19 de Octubre del 2022 por parte de la Secretaría de Obras Públicas, mediante el cual remiten el expediente técnico original de la siguiente obra para su análisis, registro y priorización, conforme al Programa Anual de Obra Pública y Programas Sociales para el ejercicio presupuestal 2022:

DEPENDENCIA EJECUTORA:	SOPMA
NOMBRE DE LA OBRA O PROYECTO:	CAMBIO DE CUBIERTA MERCADO V.N.S.A.
UBICACIÓN:	CALLE ERMITA DE SAN SEBASTIÁN Y CALLE ROGELIO GALINDO DE LA TORRE, VILLA DE NUESTRA SEÃ'ORA DE LA ASUNCION SECTOR GU, AGUASCALIENTES, AGS.
FONDO DE INVERSIÓN.	FONDO DE INFRAESTRUCTURA SOCIAL MUNICIPAL Y DE LAS DEMARCACIONES TERRITORIALES DEL DISTRITO FEDERAL
IMPORTE:	$2,458,459.16 (ET FINAL)
No. DE OBRA:	2022-FISMDF-0057-04-4001
MODALIDAD DE EJECUCIÓN:	CONTRATO
EJE:	MUNICIPIO SOBRESALIENTE
ESTRATEGIA:	OBRA PÚBLICA INTELIGENTE
POLITICA:	5.8.2.REHABILITACIÓN Y MANTENIMIENTO ESPACIOS PÚBLICOS E INFRAESTRUCTURA URBANA.

Al respecto, hago de su conocimiento que dicho expediente ha sido analizado en su integración técnica y documental, con base en el artículo 168 fracción I del Reglamento de la Ley de Obras Públicas y Servicios Relacionados para el Estado de Aguascalientes y sus Municipios.

Asimismo, le comento que este Instituto valida dicha obra acorde a lo establecido en los artículos 14, 22 párrafo segundo y 23 de la Ley de Obras Públicas y Servicios Relacionados para el Estado de Aguascalientes y sus Municipios, la cual se encuentra alineada al Plan de Desarrollo Municipal vigente, para dar cumplimiento a las metas establecidas en el mismo, y a los Lineamientos Generales para la Operación de este Fondo de Inversión, toda vez que la misma cuente con la autorización del CODEMUN. De igual manera, se hace de su conocimiento que deberá cumplir con lo establecido en los ordenamientos aplicables en lo que respecta al ejercicio, control e información de los recursos de este Fondo. Cabe hacer mención que los recursos solicitados para este proyecto de inversión, estarán sujetos a la disponibilidad presupuestal para el presente ejercicio fiscal que determine la Secretaría a su digno cargo. Sin otro particular por el momento, le envío un cordial saludo.

A T E N T A M E N T E

DR. RAMÓN RODRIGO RODRÍGUEZ CAMACHO
ENCARGADO DE DESPACHO DE LA DIRECCIÓN GENERAL DEL IMPLAN

CAAR / JDBC
C.c.p. I.C. Arq. Gloria Guadalupe Castillo González .- Secretaría de Obras Públicas .Para su conocimiento.
C.c.p. Archivo.

Instituto Municipal de Planeación y Evaluación de Aguascalientes

Antonio Acevedo Escobedo 103 A. Col. Centro
Aguascalientes. Ags. C.P. 20000

(449) 9101010 Ext. 3117

www.implanags.gob.mx

GOBIERNO MUNICIPAL DE AGUASCALIENTES

INSTITUTO MUNICIPAL DE PLANEACION

IMPLAN

ANÁLISIS INTEGRAL DE EXPEDIENTE TÉCNICO

No. DE OBRA (PAOP 2020):	2022-FISMDF-0057-04-4001	REGISTRO No.	229
OFICIO DE VALIDACIÓN:	AMPP/0457/22	FECHA RECIBIDO PARA REVISIÓN:	20 de Octubre del 2022
PROGRAMA:	URBANIZACION MUNICIPAL	LOCALIDAD O COLONIA:	VILLA DE NUESTRA SEÑORA DE LA ASUNCION SECTOR GU
SUB-PROGRAMA:	0440- Otros (Contenedores para Basura)	DELEGACIÓN:	Pozo Bravo
DEPENDENCIA:	Secretaría de Obras Públicas	MOD. DE EJECUCIÓN:	CONTRATO
NOMBRE DE LA OBRA:	CAMBIO DE CUBIERTA MERCADO V.N.S.A., CALLE ERMITA DE SAN SEBASTIÁN Y CALLE ROGELIO GALINDO DE LA TORRE		
FUENTE DE FINANCIAMIENTO:	FONDO DE INFRAESTRUCTURA SOCIAL MUNICIPAL Y DE LAS DEMARCACIONES TERRITORIALES DEL DISTRITO FEDERAL, FISMDF		
INVERSIÓN:	$2,458,459.16	CLASIFICACIÓN DE OBRA:	BIENES DE DOMINIO PUBLICA

TOTAL	FEDERAL	ESTATAL	MUNICIPAL	BENEFICIARIOS	OTROS	DIFERENCIA ENTRE MOD.
$2,458,459.16	$2,458,459.16	0.00	0.00	0.00	0.00	*$144.432,65*

TIPO DE EXPENDIENTE:	ET FINAL	AÑO: 2022	AÑO:	AÑO:		
AVANCES:	Financiero: 85 %		Físico: 99 %			
FECHA DE INICIO:	8 de Julio del 2022		FECHA DE TÉRMINO:	5 de Septiembre del 2022	REGISTRO SIMA:	57

CHEK LIST DE LOS ANEXOS DEL EXPEDIENTE TÉCNICO

CÉDULA DE REGISTRO DE OBRA	✓
DICTAMEN DE FACTIBILIDAD	✓
MEMORIA DESCRIPTIVA	✓
PRESUPUESTO BASE	✓
FACTIBILIDAD VERIFICADA EN CAMPO	✓
CROQUIS DE UBICACIÓN (MACRO)	✓
CROQUIS DE UBICACIÓN (MACRO)	✓
PROGRAMA DE OBRA Y MONTOS MENSUALES	✓
PLANOS O ESTUDIOS TÉCNICOS	✓
PADRÓN DE BENEFICIARIOS	N/A
ACTA DE ACEPTACIÓN DEL PROYECTO	N/A
DICTAMEN DE IMPACTO AMBIENTAL	N/A
CONVENIO DE CONCERTACIÓN	N/A
ACTA CONSTITUTIVA	N/A

METAS		BENEFICIARIOS		PERIODO DE EJECUCION		OBRA PROPUESTA		CLAVE SISCO
UNIDAD DE MEDIDA	CANT	TIPO DE BENEFICIARIOS	CANTIDAD	FECHA DE INICIO	FECHA DE TERMINO	CONCEPTO	JORNALES A GENERAR	
OBRA	1	Personas	250	2022-07-08	2022-09-05	Mercados	6391	2331

INCLUIDO EN PLAN DE DESARROLLO MUNICIPAL Y EL PROGRAMA ANUAL DE OBRA PÚBLICA

OBSERVACIONES:

SIN OBSERVACIONES

RECIBIO: ING. JOSÉ DAVID BURGUETE CLAUSTRO
Analista de Programación e Inversión de Obra Pública

20 de Octubre del 2022
Fecha de validación

PROCEDE Si ✓ No

20 de Octubre del 2022
Fecha de validación Expediente

H. AYUNTAMIENTO CONSTITUCIONAL DEL MUNICIPIO DE AGUASCALIENTES 2021-2024

AYUNTAMIENTO DE AGUASCALIENTES

CEDULA DE REGISTRO POR OBRA

050400-001E00E05-05-2-2-2-00-1-E-0508-0-17-0057-21-2502-6125

Aguascalientes
LA CIUDAD DE TU VIDA

2022-FISMDF-0057-04401-020	Obra **CAMBIO DE CUBIERTA MERCADO V.N.S.A.**
Tipo DEFINITIVO 1 2022 Folio SISCO **2331**	Ubic. CALLE ERMITA DE SAN SEBASTIÁN Y CALLE ROGELIO DE LA TORRE, VILLA DE NUESTRA SEÑORA DE LA ASUNCION SECTOR GUADALUPE Fracc. 1a. Secc. , Deleg. Jesus Teran

Ent. Ejecutora : **050400001E00E05**

Eje: **05**	MUNICIPIO SOBRESALIENTE
Finalidad: **2**	DESARROLLO SOCIAL
Función: **2**	VIVIENDA Y SERVICIOS A LA COMUNIDAD
Subfunción: **2**	DESARROLLO COMUNITARIO
Tema: **00**	SIN TEMA
Cuenta del Gasto **1**	GASTO PROGRAMABLE
Clasif. Programatica: **E**	PRESTACIÓN DE SERVICIOS PÚBLICOS
Programa: **0508**	Obra Pública Inteligente
SubPrograma: **0**	SUBPROGRAMA GENÉRICO
Proyecto: **17**	
Tipo de Gasto: **21**	GASTO INVERSIÓN / OBRA PÚBLICA

INVERSION 2022

Municipal	2502	FONDO PARA LA INFRAESTRUCTURA SOCIAL MUNICIPAL Y DE LAS DEMARCACIONES TERRITORIALES DEL DISTRITO FEDERAL 2022	$2,458,459.16

Folio SIMA 57 Total $2,458,459.16

METAS

Unidad de Medida	Cantidad	Descripción
OBRA	1	OBRA CAMBIO DE CUBIERTA MERCADO V.N.S.A.

Inversión Ejercida Total al 31 de Diciembre de 2021 $0.00

Avance Fisico Acumulado al 31 de Diciembre de 2021

Avance Fisico Acumulado Programado al 31 de Diciembre de 2022 100 %

Fecha de Inicio 08 Jul 2022 Fecha de Terminación 05 Sep 2022

Jornales a Generar en 2022 6391

Modalidad de ejecución CONTRATO

Clasificación de la Obra Bienes de Dominio Público

Registro del Patrimonio: Infraestructura

SECRETARIA DE OBRAS PÚBLICAS

Av. Aguascalientes Sur No. 2615
Fracc. Jardines de las Fuentes,
Aguascalientes, Ags. C.P. 20278

(449) 9 78 92 01, 06, 09

www.ags.gob.mx

GENERALES

Nombre del Proyecto : CAMBIO DE CUBIERTA MERCADO V.N.S.A.

CALLE ERMITA DE SAN SEBASTIÁN Y CALLE ROGELIO DE LA TORRE, VILLA DE NUESTRA SEÑORA DE LA ASUNCION SECTOR GUADALUPE Fracc. 1a. Secc. , Deleg. Jesus Teran

Programa : 04 URBANIZACION MUNICIPAL

Subprograma : 044 Otros (especificar) (1.- Mannto./Rehab.)

Clave del Municipio : AGUASCALIENTES

Localidad :

Barrio, Colonia o Ejido : VILLA DE NUESTRA SEÑORA DE LA ASUNCION SECTOR GUADALUPE Fracc. 1a. Secc.

Tipo de Obra : NUEVA

DESCRIPCIÓN DEL PROYECTO:

CAMBIO DE CUBIERTA MERCADO V.N.S.A. 1.00 OBRA

Beneficiarios (No. y Tipo) :

250	PERSONAS

Los abajo firmantes, hacen constar que el presente proyecto :

CAMBIO DE CUBIERTA MERCADO V.N.S.A.

CALLE ERMITA DE SAN SEBASTIÁN Y CALLE ROGELIO DE LA TORRE, VILLA DE NUESTRA SEÑORA DE LA ASUNCION SECTOR GUADALUPE Fracc. 1a. Secc. , Deleg. Jesus Teran

cumple con los Requisitos y Normas Técnicas establecidas por la Dependencia Normativa, por lo que es viable su ejecución. Comprometiéndose la misma a proporcionar la supervisión y asistencia técnica necesaria durante el proceso administrativo.

Por la Dependencia Ejecutora

Arq. Gloria Guadalupe Castillo González
Encargada de Despacho de la Secretaría de Obras Públicas

Lic. Jaime Gerardo Beltrán Martínez
Secretario del H. Ayuntamiento y Dir. General de Gobierno

LUGAR :AGUASCALIENTES, AGS.

H. AYUNTAMIENTO CONSTITUCIONAL DEL MUNICIPIO DE AGUASCALIENTES 2021-2024

AYUNTAMIENTO DE AGUASCALIENTES

FACTIBILIDAD VERIFICADA EN CAMPO

Aguascalientes
LA CIUDAD DE TU VIDA

MUNICIPIO: AGUASCALIENTES

LOCALIZACION: CALLE ERMITA DE SAN SEBASTIÁN Y CALLE ROGELIO DE LA TORRE, VILLA DE NUESTRA SEÑORA DE LA ASUNCION SECTOR GUADALUPE Fracc. 1a. Secc. , Deleg. Jesus Teran

PROGRAMA: URBANIZACION MUNICIPAL

SUBPROGRAMA: Otros (especificar) (1.- Mannto./Rehab.)

OBRA A REALIZAR: CAMBIO DE CUBIERTA MERCADO V.N.S.A.

DEPENDENCIA EJECUTORA: SECRETARÍA DE OBRAS PUBLICAS DEL MUNICIPIO DE AGUASCALIENTES

FORMA DE EJECUCION: CONTRATO

TIPO DE OBRA PROPUESTA: NUEVA

CONDICIONES ACTUALES DE LA OBRA:

CAMBIO DE CUBIERTA MERCADO V.N.S.A.

CARACTERISTICAS DE LA OBRA: Bueno

FACTIBILIDAD DE LA OBRA:

ESTA OBRA SE REQUIERE PARA EL BENEFICIO DE LA CIUDADANÍA

PROCEDE: SI [X] NO [ ]

REVISÓ: Jefa del Departamento de Expedientes Tecnicos y Costos

NOMBRE: Arq. Blanca Margarita Martinez Amador

FIRMA:

FECHA: 03 Oct 2022

SECRETARIA DE OBRAS PÚBLICAS

Av. Aguascalientes Sur No. 2615
Fracc. Jardines de las Fuentes,
Aguascalientes, Ags. C.P. 20278

(449) 9 78 92 01, 06, 09

www.ags.gob.mx

No. Folio SISCO 2331

UBICACIÓN DE OBRA

Clave Prog.:	050400001E00E0505222001E0508017005721250261 25	FOLIO SISCO: 2331
Acción:	**CAMBIO DE CUBIERTA MERCADO V.N.S.A.**	EXPEDIENTE INICIAL
Ubicación:	CALLE ERMITA DE SAN SEBASTIÁN Y CALLE ROGELIO DE LA TORRE. VILLA DE NUESTRA SEÑORA DE LA ASUNCION SECTOR GUADALUPE	EJERCICIO: 2022



LOCALIZACIÓN DE OBRA

Clave Prog.:	050400001E00E0505222001E0508017005721250261 25	FOLIO SISCO: 2331
Acción:	CAMBIO DE CUBIERTA MERCADO V.N.S.A.	EXPEDIENTE INICIAL
Ubicación:	CALLE ERMITA DE SAN SEBASTIÁN Y CALLE ROGELIO DE LA TORRE. VILLA DE NUESTRA SEÑORA DE LA ASUNCION SECTOR GUADALUPE	EJERCICIO: 2022



Secretaría de Obras Públicas

RO3-POS-SOS-7.5.1-04	
REVISION:	00
FECHA DE REVISION:	
RESPONSABLE:	SUPERVISOR DE OBRA
TIEMPO DE RET:	02 AÑOS

PROGRAMA DE OBRA DEFINITIVO

Aguascalientes
LA CIUDAD ES TU VIDA

No. DE CONTRATO : FISMDF-0057-2022

PROGRAMA: 04.- URBANIZACIÓN MUNICIPAL

INICIO VIGENTE: 08-julio-22

No. OBRA Y NOMBRE DE LA OBRA: FISMDF-0057-2022 CAMBIO DE CUBIERTA MERCADO V.N.S.A.

TERMINO REAL: 05-septiembre-22

CONCEPTO			RECURSO	1	2	3	4	5	6	7	8	9	10	11	12	13	14	15	16	2022	
				FEBRERO	MARZO	ABRIL	MAYO	JUNIO	JULIO	AGOSTO	SEPTIEMBRE	OCTUBRE	NOVIEMBRE	DICIEMBRE	ENERO	FEBRERO	MARZO	ABRIL	MAYO	PONDERACIÓN %	
									08/07/2022		05/09/2022									FINANCIERO	FÍSICO
DESCRIPCION		INVERSION																		%	%
CAMBIO DE CUBIERTA MERCADO V.N.S.A.																					
C. ERMITA DE SAN SEBASTIÁN Y C. ROGELIO DE LA TORRE, V.N.S.A., S. GPE. FRACC. 1A. S.																					
DESMONTAJES	$	237,656.83							20	20	20	20	20							11.21	11.00
ACABADOS	$	1,377,994.42							20	20	20	20	20							65.02	65.00
LIMPIEZAS	$	41,710.45									40	30	30							1.97	2.00
EXTRACTORES SOLARES	$	411,191.80									50	50								19.40	20.00
EXTRAORDINARIOS	$	50,807.85										50	50							2.40	2.00
SUBTOTAL SIN IVA	$	2,119,361.35		0	0	0	0	0	0	1	2	2	2	2	3	3	2	0	0		
AVACE SEMANAL %				0%	0%	0%	0%	0%	0%	0%	0%	0%	0%	0%	0%	0%	0%	0%	0%		
AVANCE SEMANAL ACUMULADO %				0%	0%	0%	0%	0%	0%	0%	0%	0%	0%	0%	0%	0%	0%	0%	0%	100.00	100.00
EJERCIDO SEMANAL $				-	-	-	-	-	47,531.37	323,130.25	323,130.25	323,130.25	497,878.96	243,512.96	37,917.06	-	-	-	-		
EJERCIDO MENSUAL $				$0.00	$0.00	$0.00	$0.00	$0.00	$693,791.87	$1,387,652.42	$37,917.06	$0.00	$0.00	$0.00	$0.00	$0.00	$0.00	$0.00	$0.00	$ 2,119,361.35	
EJERCIDO MENSUAL ACUMULADO $				0.00	0.00	0.00	0.00	0.00	693,791.87	2,081,444.29	2,119,361.35	2,119,361.35	2,119,361.35	2,119,361.35	2,119,361.35	2,119,361.35	2,119,361.35	2,119,361.35	2,119,361.35	$ 339,097.81	IVA 16%
EJERCIDO SEMANAL %				0%	0%	0%	0%	0%	2%	15%	15%	15%	23%	11%	2%	0%	0%	0%	0%		
EJERCIDO MENSUAL %				0%	0%	0%	0%	0%	33%	65%	2%	0%	0%	0%	0%	0%	0%	0%	0%	GRAN TOTAL EJERCIDO	
EJERCIDO MENSUAL ACUMULADO %				0%	0%	0%	0%	0%	33%	98%	100%	100%	100%	100%	100%	100%	100%	100%	100%	$	2,458,459.16

FERNANDO MEDRANO ROQUE
SUPERVISOR

PRESIDENCIA MUNICIPAL DE AGUASCALIENTES

FACTIBILIDAD VERIFICADA EN CAMPO

GENERALES

EJERCICIO: 2022 APROBACION No: 2022-FISMDF-0057-04401-020

LOCALIDAD: C. ERMITA DE SAN SEBASTIÁN Y C. ROGELIO DE LA TORRE, VILLA DE NTRA. SEÑORA DE LA ASUNCIÓN, SECTOR GPE.

MUNICIPIO: AGUASCALIENTES

PROGRAMA: 04.- URBANIZACIÓN MUNICIPAL

SUB-PROGRAMA:

OBRA A REALIZARSE: CAMBIO DE CUBIERTA MERCADO V.N.S.A.

DEPENDENCIA EJECUTORA: SECRETARÍA DE OBRAS PÚBLICAS MUNICIPALES (S.O.P.M.A)

FORMACIÓN DE EJECUCION: CONTRATO NO. DE CONTRATO: FISMDF-0057-2022

NOMBRE CONTRATISTA: CONSTRUCTORA ALV, S.A. DE C.V.

INICIO REAL: dd/mm/aa 8 de julio de 2022 TERMINO REAL: 5 de septiembre de 2022

TIPO DE OBRA PROPUESTA

NUEVA CREACIÓN		CONSOLIDACIÓN	
COMPLEMENTARIA		AMPLIACIÓN	
REHABILITACIÓN	X	EQUIPAMIENTO	

CARACTERÍSTICAS DE LA OBRA:

207.13 M2 DE DESM. DE LÁMINA DE PVC TRASLÚCIDA SEMITRANSPARENTE, 954.34 M2 DE DESM. DE LÁMINA SÓLIDA DE PVC, 622.32 M2 DE DESM. DE LÁMINA TRASLÚCIDA, 1492.65 M2 DE SUM. Y COL. DE LÁMINA DE ACERO GALVANIZADO ONDULAR, 291.15 M2 DE COLOC. DE LÁMINA TRASLÚCIDA DESMONTADA EN BUEN ESTADO, 1492.65 M2 M2 DE SUM. Y COL. DE AISLAMIENTO TÉRMICO, 20.00 PZA. DE SUM. Y COL. DE UNIDAD DE VENTILACIÓN (EXTRACTOR).

CONDICIONES ACTUALES DE LA OBRA: (SELECCIONAR UNO OBLIGATORIO)

BUEN ESTADO X REGULAR PESIMO ESTADO

FACTIBILIDAD DE LA OBRA: (CONDICIONES ACTUALES DE LA OBRA)

ESTA OBRA SE ENCUENTRA EN CONDICIONES PARA OPERARSE

PROCEDE: SI: X NO:

MARQUE SOLO UNA

FERNANDO MEDRANO ROQUE

SUPERVISOR

PRESIDENCIA MUNICIPAL DE AGUASCALIENTES

FACTIBILIDAD VERIFICADA EN CAMPO

GENERALES

LOCALIDAD: C. ERMITA DE SAN SEBASTIÁN Y C. ROGELIO DE LA TORRE, VILLA DE NTRA. SEÑORA DE LA ASUNCIÓN, SECTOR GPE.
MUNICIPIO: AGUASCALIENTES
PROGRAMA: 04.- URBANIZACIÓN MUNICIPAL
SUB-PROGRAMA:
OBRA A REALIZARSE: CAMBIO DE CUBIERTA MERCADO V.N.S.A.
DEPENDENCIA EJECUTORA: SECRETARÍA DE OBRAS PÚBLICAS MUNICIPALES (S.O.P.M.A)
FORMACIÓN DE EJECUCION: CONTRATO

TIPO DE OBRA PROPUESTA

NUEVA CREACIÓN		CONSOLIDACIÓN	
COMPLEMENTARIA		AMPLIACIÓN	
REHABILITACIÓN	X	EQUIPAMIENTO	

CARACTERÍSTICAS DE LA OBRA:

207.13 M2 DE DESM. DE LÁMINA DE PVC TRASLÚCIDA SEMITRANSPARENTE, 954.34 M2 DE DESM. DE LÁMINA SÓLIDA DE PVC, 622.32 M2 DE DESM. DE LÁMINA TRASLÚCIDA, 1492.65 M2 DE SUM. Y COL. DE LÁMINA DE ACERO GALVANIZADO ONDULAR, 291.15 M2 DE COLOC. DE LÁMINA TRASLÚCIDA DESMONTADA EN BUEN ESTADO, 1492.65 M2 M2 DE SUM. Y COL. DE AISLAMIENTO TÉRMICO, 20.00 PZA. DE SUM. Y COL. DE UNIDAD DE VENTILACIÓN (EXTRACTOR).

CONDICIONES ACTUALES DE LA OBRA:

BUEN ESTADO:	X	REGULAR:		PESIMO ESTADO:	

FACTIBILIDAD DE LA OBRA:

ESTA OBRA SE ENCUENTRA EN CONDICIONES PARA OPERARSE

PROCEDE	**SI:**	X	**NO:**	

FERNANDO MEDRANO ROQUE
SUPERVISOR

H. AYUNTAMIENTO CONSTITUCIONAL DEL MUNICIPIO DE AGUASCALIENTES 2021-2024

PRESUPUESTO MODIFICADO

Aguascalientes LA CIUDAD DE TU VIDA

Obra: **CAMBIO DE CUBIERTA MERCADO V.N.S.A.**

Ubicación: **CALLE ERMITA DE SAN SEBASTIÁN Y CALLE ROGELIO DE LA TORRE, VILLA DE NUESTRA SEÑORA DE LA ASUNCION SECTOR GUADALUPE Fracc. 1a. Secc.**

Contratista: **CONSTRUCTORA ALV, S.A. DE C.V. (700)**

No.	Concepto	Unidad	Cantidad	Precio Unitario	Importe Total
	GRUPO: **CAMBIO DE CUBIERTA MERCADO V.N.S.A.**				
	PARTIDA: **DESMONTAJES**				
1	DESMONTAJE DE LAMINA DE PVC TRASLUCIDA SEMITRANSPARENTE, POR MEDIOS MANUALES Y/O MECANICOS. INCLUYE: GENie, ANDAMIOS, PLUMAS, MANO DE OBRA ESPECIALIZADA, EQUIPO DE SEGURIDAD(CASCO, NOTAS, CHALECOS, LINEA DE VIDA), RETIRO DE ELEMENTOS DE SUJECION, ACARREOS DENTRO DE LA OBRA, ENTREGA A ALMACEN QUE DESIGNE LA SUPERVISION DE SOPMA, HERRAMIENTAS, A UNA ALTURA ENTRE 8.00 Y 12.00 METROS, LIMPIEZAS, TRABAJO TERMINADO.	M2	207.13	$133.11	$27,571.07
2	DESMONTAJE DE LAMINA SOLIDA DE PVC., POR MEDIOS MANUALES Y/O MECANICOS. INCLUYE: GENie, ANDAMIOS, PLUMAS, MANO DE OBRA ESPECIALIZADA, EQUIPO DE SEGURIDAD(CASCO, NOTAS, CHALECOS, LINEA DE VIDA), RETIRO DE ELEMENTOS DE SUJECION, ACARREOS DENTRO DE LA OBRA, ENTREGA A ALMACEN QUE DESIGNE LA SUPERVISION DE SOPMA, HERRAMIENTAS, A UNA ALTURA ENTRE 8.00 Y 12.00 METROS, LIMPIEZAS, TRABAJO TERMINADO.	M2	954.34	$133.11	$127,032.20
3	DESMONTAJE DE LAMINA TRASLUCIDA, POR MEDIOS MANUALES Y/O MECANICOS. CON RECUPERACION PARA SU POSTERIOR UTILIZACION, INCLUYE: GENie, ANDAMIOS, PLUMAS, MANO DE OBRA ESPECIALIZADA, EQUIPO DE SEGURIDAD(CASCO, NOTAS, CHALECOS, LINEA DE VIDA), RETIRO DE ELEMENTOS DE SUJECION, ACARREOS DENTRO DE LA OBRA, ENTREGA A ALMACEN QUE DESIGNE LA SUPERVISION DE SOPMA, HERRAMIENTAS, A UNA ALTURA ENTRE 8.00 Y 12.00 METROS, LIMPIEZAS, TRABAJO TERMINADO.	M2	622.32	$133.11	$82,837.02
4	DESMONTAJE DE PANEL COMPUESTO DE ALUMINIO, POR MEDIOS MANUALES Y/O MECANICOS. CON RECUPERACION PARA SU POSTERIOR UTILIZACION, INCLUYE: GENie, ANDAMIOS, PLUMAS, MANO DE OBRA ESPECIALIZADA, EQUIPO DE SEGURIDAD(CASCO, NOTAS, CHALECOS, LINEA DE VIDA), RETIRO DE ELEMENTOS DE SUJECION, ACARREOS DENTRO DE LA OBRA, ENTREGA A ALMACEN QUE DESIGNE LA SUPERVISION DE SOPMA, HERRAMIENTAS, A UNA ALTURA ENTRE 8.00 Y 12.00 METROS, LIMPIEZAS, TRABAJO TERMINADO.	M2	1.2	$180.45	$216.54
				Totales por Partida	**$237,656.83**
	PARTIDA: **ACABADOS**				
7	SUMINISTRO Y COLOCACIÓN DE LAMINA DE ACERO GALVANIZADO ONDULAR TERNIUM TO-100 CALIBRE 26 MARCA TERNIUM O SIMILAR EN CALIDAD Y PRECIO, PARA CUBIERTA DE 952.80MM DE ANCHO.X12.00M. DE LARGO., USO COMERCIAL, INCLUYE: GENie, ANDAMIOS, PLUMAS, MANO DE OBRA ESPECIALIZADA, EQUIPO DE SEGURIDAD(CASCO, NOTAS, CHALECOS, LINEA DE VIDA), ACARREOS DENTRO DE LA OBRA, HERRAMIENTAS, A UNA ALTURA ENTRE 8.00 Y 12.00 METROS, ELEMENTOS DE FIJACIÓN, TORNILLERIA, SELLADO DE JUNTAS ASEGURANDO QUE NO EXISTAN FILTRACIONES, FLETES, ACARREOS, MATERIALES, TRASLAPES, CORTES, DESPERDICIOS, LIMPIEZAS, RETIRO DE SOBRANTES FUERA DE LA OBRA AJUSTES, TRAZOS NIVELACIONES, PLOMOS, PROTECCION DE AREAS ADYACENTES, Y TODO LO NECESARIO PARA SU CORRECTA EJECUCION, TRABAJO TERMINADO.	M2	1492.65	$520.88	$777,491.53

H. AYUNTAMIENTO CONSTITUCIONAL DEL MUNICIPIO DE AGUASCALIENTES 2021-2024

PRESUPUESTO MODIFICADO

Aguascalientes LA CIUDAD DE TU VIDA

Obra: **CAMBIO DE CUBIERTA MERCADO V.N.S.A.**

Ubicación: **CALLE ERMITA DE SAN SEBASTIÁN Y CALLE ROGELIO DE LA TORRE, VILLA DE NUESTRA SEÑORA DE LA ASUNCION SECTOR GUADALUPE Fracc. 1a. Secc.**

Contratista: **CONSTRUCTORA ALV, S.A. DE C.V. (700)**

No.	Concepto	Unidad	Cantidad	Precio Unitario	Importe Total
	GRUPO: **CAMBIO DE CUBIERTA MERCADO V.N.S.A.**				
	PARTIDA: **ACABADOS**				
8	COLOCACIÓN DE LAMINA TRASLUCIDA DESMONTADA EN BUEN ESTADO, INCLUYE: GENie, ANDAMIOS, PLUMAS, MANO DE OBRA ESPECIALIZADA, EQUIPO DE SEGURIDAD(CASCO, NOTAS, CHALECOS, LINEA DE VIDA), ACARREOS DENTRO DE LA OBRA, A UNA ALTURA ENTRE 8.00 Y 12.00 METROS ELEMENTOS DE FIJACIÓN, TORNILLERIA, SELLADO DE JUNTAS ASEGURANDO QUE NO EXISTAN FILTRACIONES, FLETES, ACARREOS, MATERIALES, TRASLAPES, CORTES, DESPERDICIOS, LIMPIEZAS, RETIRO DE SOBRANTES FUERA DE LA OBRA AJUSTES, TRAZOS NIVELACIONES PLOMOS, HERRAMIENTAS, PROTECCION DE AREAS ADYACENTES Y TODO LO NECESARIO PARA SU CORRECTA EJECUCION, TRABAJO TERMINADO.	M2	291.15	$186.35	$54,255.80
9	SUMINISTRO Y COLOCACIÓN DE AISLAMIENTO TERMICO INTERIOR PARA CUBIERTAS, (MBI) de 2", ROLLO FLEXIBLE DE AISLAMIENTO TERMICO, FABRICADO CON FIBRAS DE VIDRIO AGLUTINADAS CON RESINAS TERMOFIJAS RECUBIERTAS CON UNA BARRERA DE VAPOR DE POLIPROPILENO REFORZADO EN UNA DE SUS CARAS DE COLOR ALUMINIO, MARCA OWENS CORNING, FIJADO A ESTRUCTURA DE CUBIERTA CON ALAMBRE GALVANIZADO No. 16, CINTAS ADHESIVAS DE ALUMINIO SENCILLAS Y DOBLE CARA, ROSETONES DE PVC Y TORNILLOS AUTOROSCANTES, INCLUYE: GEnie, ANDAMIOS, PLUMAS, MANO DE OBRA ESPECIALIZADA, EQUIPO DE SEGURIDAD(CASCO, NOTAS, CHALECOS, LINEA DE VIDA), ACARREOS DENTRO DE LA OBRA, HERRAMIENTAS, A UNA ALTURA ENTRE 8.00 Y 12.00 METROS MATERIALES, SISTEMA DE FIJACION Y UNION DE ELEMENTOS, HERRAMIENTAS, PROTECCION DE AREAS ADYACENTES, LIMPIEZAS, TODO LO NECESARIO PARA SU CORRECTA COLOCACIÓN, TRABAJO TERMINADO.	M2	1492.65	$361.06	$538,936.21
10	SUMINISTRO Y COLOCACIÓN DE PANEL COMPUESTO DE ALUMINIO DE 4mm. DE ESPESOR, CONSTA DE 3 CAPAS, DOS DE LAMINAS DE ALUMINIO Y UNA CENTRAL DE POLIETILENO NANOMETRICO MARCA NALUBOND, COLOR IGUAL AL EXISTENTE , INCLUYE: ELEMENTOS DE FIJACIÓN, TORNILLERIA, SELLADO DE JUNTAS ASEGURANDO QUE NO EXISTAN FILTRACIONES CON SELLADOR TIPO INDUSTRIAL, FLETES, ACARREOS, MATERIALES, TRASLAPES, CORTES, DESPERDICIOS, GENie, ANDAMIOS, PLUMAS, MANO DE OBRA ESPECIALIZADA, EQUIPO DE SEGURIDAD(CASCO, NOTAS, CHALECOS, LINEA DE VIDA), ACARREOS DENTRO DE LA OBRA, HERRAMIENTAS, A UNA ALTURA ENTRE 8.00 Y 12.00 METROS MATERIALES, SISTEMA DE FIJACION Y UNION DE ELEMENTOS, HERRAMIENTAS, PROTECCION DE AREAS ADYACENTES, LIMPIEZAS, TODO LO NECESARIO PARA SU CORRECTA COLOCACIÓN, TRABAJO TERMINADO.	M2	1.2	$6,092.40	$7,310.88
				Totales por Partida	**$1,377,994.42**
	PARTIDA: **LIMPIEZAS**				
11	LIMPIEZA GENERAL DE LA OBRA, INCLUYE: ACARREOS DE ESCOMBROS, RETIRO FUERA DE LA OBRA DEL MISMO	M2	1789.38	$23.31	$41,710.45
				Totales por Partida	**$41,710.45**

Obra: **CAMBIO DE CUBIERTA MERCADO V.N.S.A.**

Ubicación: **CALLE ERMITA DE SAN SEBASTIÁN Y CALLE ROGELIO DE LA TORRE, VILLA DE NUESTRA SEÑORA DE LA ASUNCION SECTOR GUADALUPE Fracc. 1a. Secc.**

Contratista: **CONSTRUCTORA ALV, S.A. DE C.V. (700)**

No.	Concepto	Unidad	Cantidad	Precio Unitario	Importe Total
	GRUPO: **CAMBIO DE CUBIERTA MERCADO V.N.S.A.**				
	PARTIDA: **EXTRACTORES SOLARES - EXTRACTORES SOLARES**				
12	SUMINISTRO Y COLOCACION DE UNIDAD DE VENTILACION (EXTRACTOR) MARCA SOLAR STAR, MODELO 1600 PARA INSTALAR EN TECHUMBRE PLANA Y/O INCLINADA INCLUYE: COLOCACION, ELEMENTOS DE FIJACION, ELEVACIONES A CUALQUIER ALTURA, MATERIAL MISCELANEO, PREPARACIONES EN CUBIERTA, CORTES DE LAMINA, SELLADORES, HERRAMIENTAS NECESARIAS PARA SU CORRECTA COLOCACION, LIMPIZA EN EL AREA DE TRABAJO, ACAREOS DENTRO Y FUERA DE LA OBRA, PRUEBAS DE FUNCIONAMIENTO, MANO DE OBRA, PUESTA EN SERVICIO, TRABAJO TERMINADO.	PZA	20	$18,225.26	$364,505.20
13	RETIRO CON RECUPERACION DE EXTRACTOR SOLAR INSTALADO EN CUBIERTA METALICA DE MERCADO, INCLUYE: ELEVACIONES A CUALQUIER ALTURA, DESCONEXIONES, DESMONTAJES, ACARREOS, ENTREGA Y TRASLADOS AL ALMACEN MUNICIPAL, HERRAMIENTAS, MANIOBRAS, MANO DE OBRA TRABAJO TERMINADO.	PZA	20	$2,334.33	$46,686.60
				Totales por Partida	**$411,191.80**
				Totales por Grupo	**$2,068,553.50**

Obra: **CAMBIO DE CUBIERTA MERCADO V.N.S.A.**

Ubicación: **CALLE ERMITA DE SAN SEBASTIÁN Y CALLE ROGELIO DE LA TORRE, VILLA DE NUESTRA SEÑORA DE LA ASUNCION SECTOR GUADALUPE Fracc. 1a. Secc.**

Contratista: **CONSTRUCTORA ALV, S.A. DE C.V. (700)**

No.	Concepto	Unidad	Cantidad	Precio Unitario	Importe Total
	GRUPO: **EXTRAORDINARIO**				
	PARTIDA: **EXTRAORDINARIO**				
14	REPARACION DE CANALON METALICO DE BAJADA DE AGUA PLUVIAL. INCLUYE: RETIRO CON CARDA Y PULIDORA DE SELLOS (SILICON) EXISTENTES EN UNIONES DE LAMINAS Y BAJADAS DE TUBO DE 4" A 6" DE DIAMETRO, CAMNIO DE MINIPIJAS DAÑADAS PARA SELLO UNIFORME, SELLADO SIKAFLEX EN UNIONES DE LAMINAS, BAJADAS DE TUBERIAS Y DONDE SEA NECESARIO, LIMPIEZA GENERAL DE CANALON, TRABAJO TERMINADO.	ML	389.84	$130.33	$50,807.85

Totales por Partida		**$50,807.85**
Totales por Grupo		**$50,807.85**
Totales Presup.		**$2,119,361.34**
Anticipo	+	**$1,098,496.50**
Amortizac. Ant.	-	**$1,098,496.50**
SubTotal. Ant.	=	**$2,119,361.35**
IVA	+	**$339,097.81**
Total	=	**$2,458,459.16**

H. AYUNTAMIENTO CONSTITUCIONAL DEL MUNICIPIO DE AGUASCALIENTES 2021-2024

PRESUPUESTO MODIFICADO

Aguascalientes
LA CIUDAD DE TU VIDA

Obra: **CAMBIO DE CUBIERTA MERCADO V.N.S.A.**

Ubicación: **CALLE ERMITA DE SAN SEBASTIÁN Y CALLE ROGELIO DE LA TORRE, VILLA DE NUESTRA SEÑORA DE LA ASUNCION SECTOR GUADALUPE Fracc. 1a. Secc.**

Contratista: **CONSTRUCTORA ALV, S.A. DE C.V. (700)**

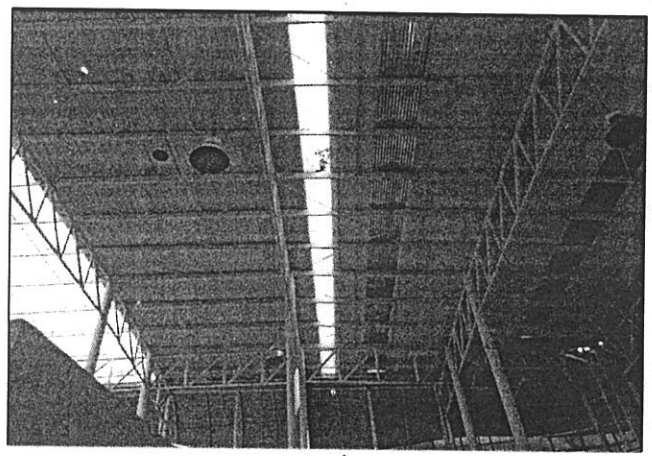
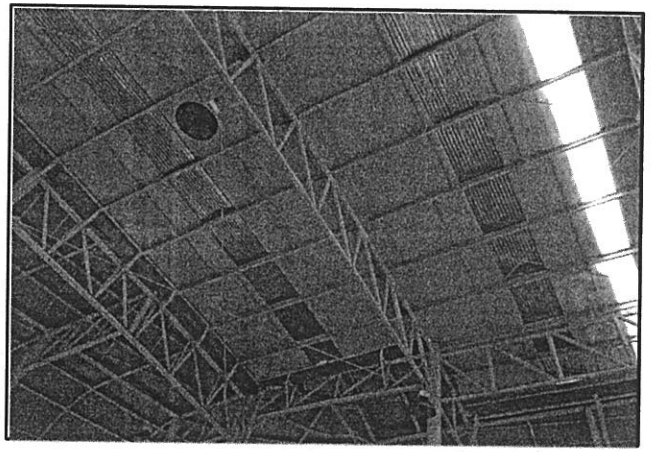
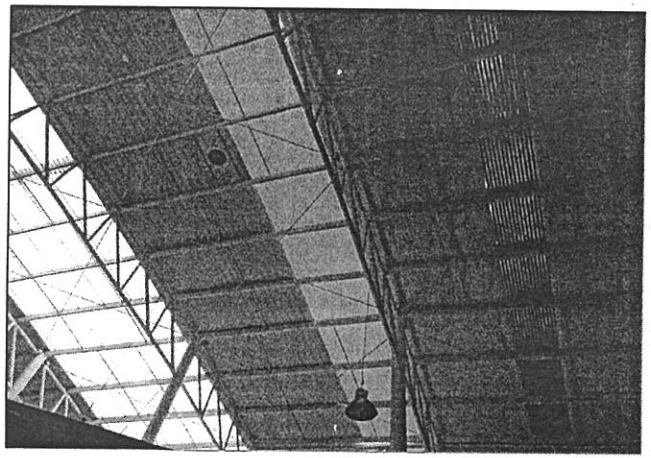
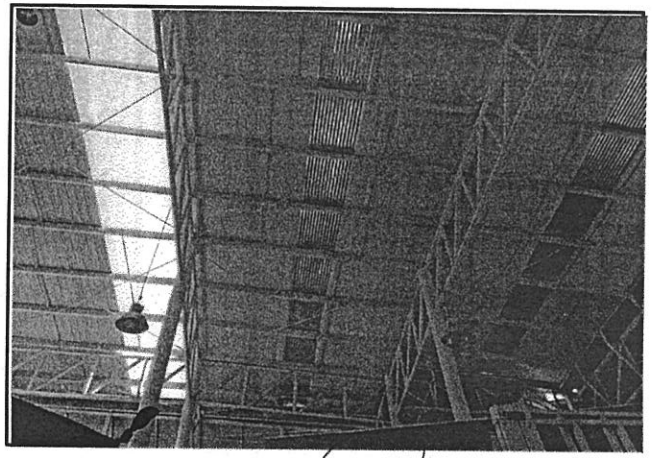
Grupo	Partida		Importe
CAMBIO DE CUBIERTA MERCADO V.N.S.A.			
	DESMONTAJES		$237,656.83
	ACABADOS		$1,377,994.42
	LIMPIEZAS		$41,710.45
	EXTRACTORES SOLARES - EXTRACTORES SOLARES		$411,191.80
		Subtotal por Grupo	**$2,068,553.50**
EXTRAORDINARIO			
	EXTRAORDINARIO		$50,807.85
		Subtotal por Grupo	**$50,807.85**
		Totales Presup.	**$2,119,361.34**
		Anticipo +	**$1,098,496.50**
		Amortizac. Ant. -	**$1,098,496.50**
		SubTotal. Ant. =	**$2,119,361.35**
		IVA +	**$339,097.81**
		Total =	**$2,458,459.16**

H. AYUNTAMIENTO DE AGUASCALIENTES
SECRETARÍA DE OBRAS PÚBLICAS
DIRECCIÓN DE SUPERVISIÓN DE OBRA

MEMORIA FOTOGRÁFICA

OBRA: CAMBIO DE CUBIERTA MERCADO V.N.S.A. **NO. DE CONTRATO:** FISMDF-0057-2022
UBICACIÓN: C. ERMITA DE SAN SEBASTIÁN Y C. ROGELIO DE LA TORRE, VILLA DE NUESTRA SEÑORA DE LA ASUNCIÓN S. GPE. Fracc. 1a. Secc.
CONTRATISTA: CONSTRUCTORA ALV, S.A. DE C.V.

INICIO





ING. FERNANDO MEDRANO FOQUE
SUPERVISOR DE OBRA.

H. AYUNTAMIENTO DE AGUASCALIENTES
SECRETARÍA DE OBRAS PÚBLICAS
DIRECCIÓN DE SUPERVISIÓN DE OBRA

MEMORIA FOTOGRÁFICA

OBRA: CAMBIO DE CUBIERTA MERCADO V.N.S.A. **NO. DE CONTRATO:** FISMDF-0057-2022
UBICACIÓN: C. ERMITA DE SAN SEBASTIÁN Y C. ROGELIO DE LA TORRE, VILLA DE NUESTRA SEÑORA DE LA ASUNCIÓN S. GPE. Fracc. 1a. Secc.
CONTRATISTA: CONSTRUCTORA ALV, S.A. DE C.V.

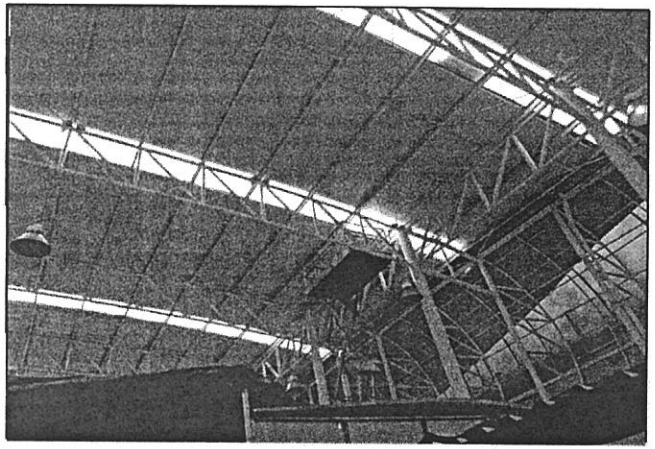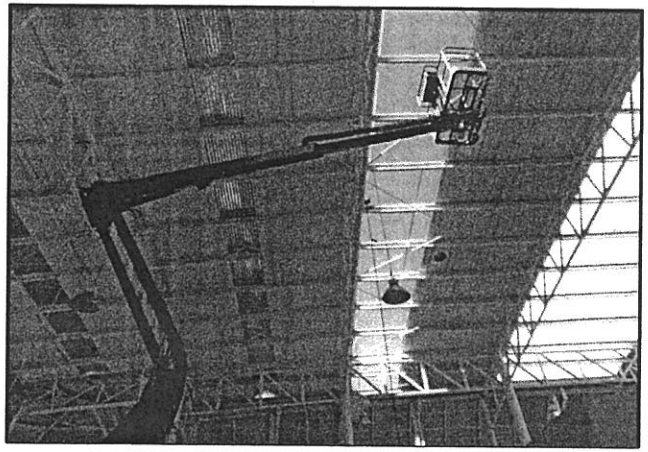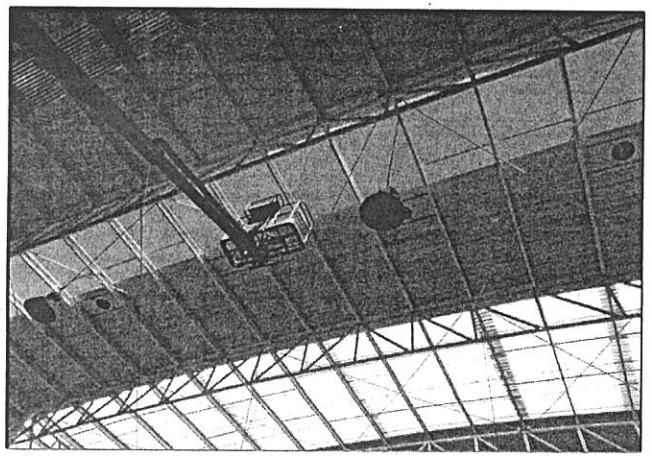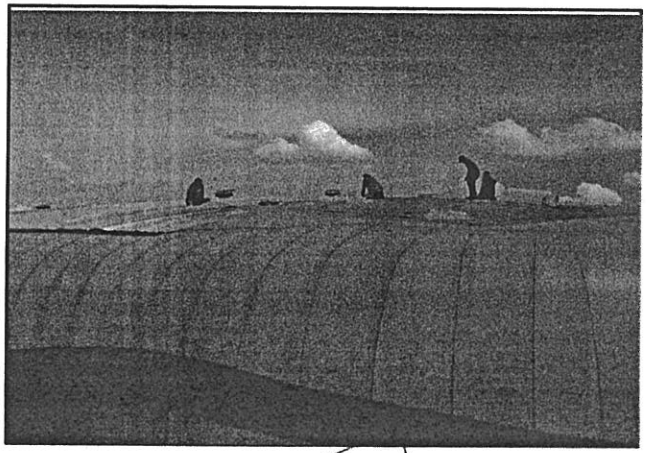PROCESO





ING. FERNANDO MEDRANO ROQUE
SUPERVISOR DE OBRA.

H. AYUNTAMIENTO DE AGUASCALIENTES
SECRETARÍA DE OBRAS PÚBLICAS
DIRECCIÓN DE SUPERVISIÓN DE OBRA

MEMORIA FOTOGRÁFICA

OBRA: CAMBIO DE CUBIERTA MERCADO V.N.S.A. **NO. DE CONTRATO:** FISMDF-0057-2022
UBICACIÓN: C. ERMITA DE SAN SEBASTIÁN Y C. ROGELIO DE LA TORRE, VILLA DE NUESTRA SEÑORA DE LA ASUNCIÓN S. GPE. Fracc. 1a. Secc.
CONTRATISTA: CONSTRUCTORA ALV, S.A. DE C.V.

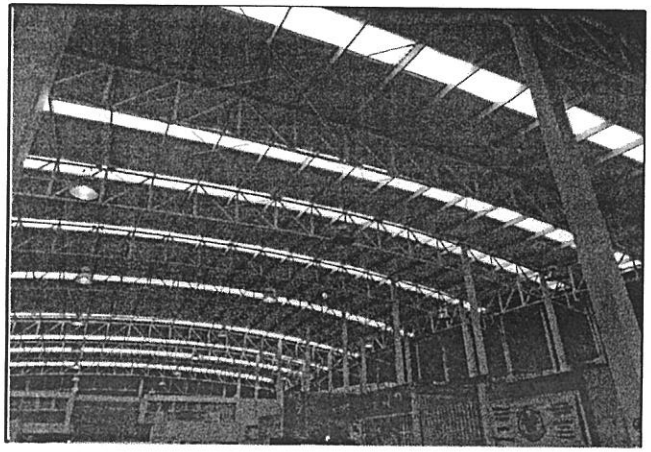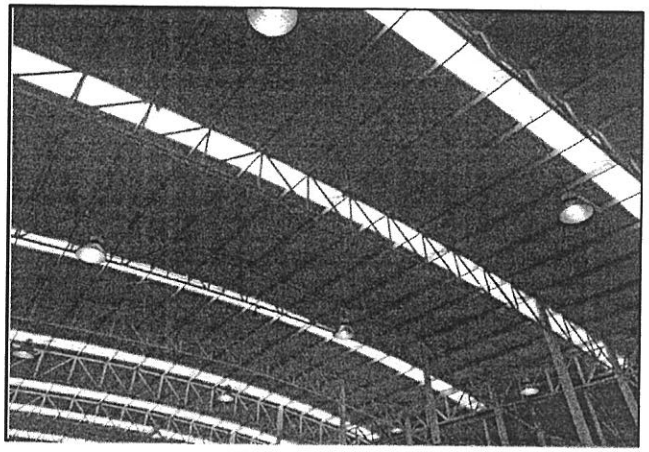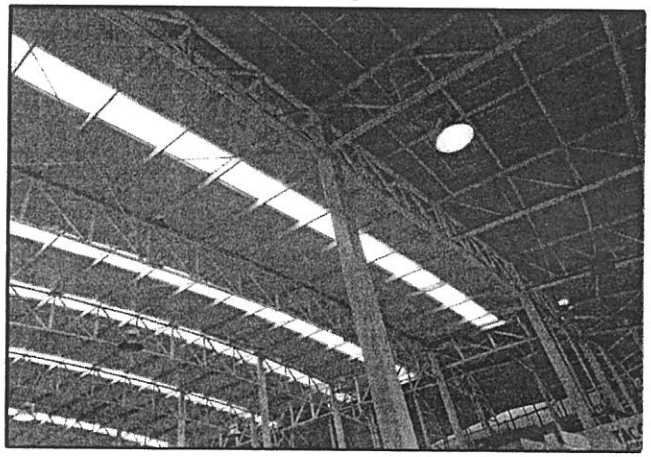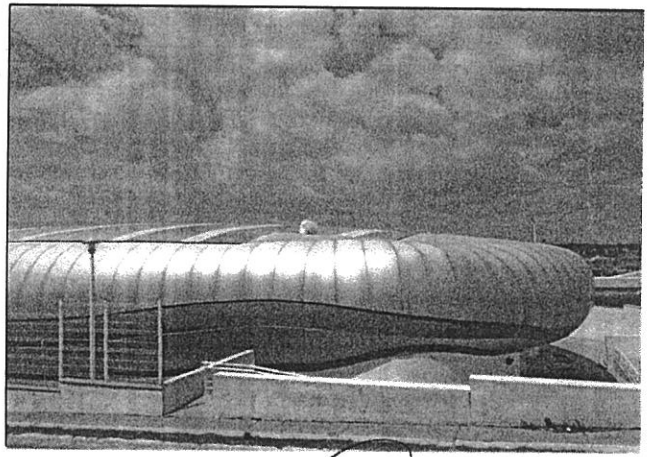TÉRMINO.

ING. FERNANDO MEDRANO ROQUE
SUPERVISOR DE OBRA.


MUNICIPIO DE AGUASCALIENTES
SECRETARIA DE OBRA PUBLICAS MUNICIPALES
DIRECCION DE COSTOS Y LICITACION DE OBRA

Aguascalientes
LA CIUDAD DE TU VIDA

CONTRATO: FISMDF-0057-2022
OBRA: CAMBIO DE CUBIERTA MERCADO V.N.S.A.
MONTO MODIFICADO FINAL: $ 2,458,459.16


VOLUMEN	UNIDAD	COMPONENTE DE OBRA	MONTO
954.34	M2	DESMONTAJE DE LÁMINA SÓLIDA DE PVC, POR MEDIOS MANUALES Y/O MECÁNICOS, INCLUYE: GENie, ANDAMIOS, PLUMAS. MANO DE OBRA ESPECIALIZADA, EQUIPO DE SEGURIDAD (CASCO, BOTAS, CHALECOS, LÍNEA DE VIDA),	$ 275,681.92
1492.65	M2	SUMINISTRO Y COLOCACIÓN DE LÁMINA DE ACERO GALVANIZADO ONDULAR TERNIUM TO-100 CALIBRE 26 MARCA TERNIUM O SIMILAR EN CALIDAD Y PRECIO, PARA CUBIERTA DE 952.80 MM. DE ANCHO X 12.00 M. DE LARGO, USO	$ 1,598,473.53
1789.38	M2	LIMPIEZA GENERAL DE LA OBRA, INCLUYE: ACARREOS DE ESCOMBROS, RETIRO FUERA DE LA OBRA DEL MISMO.	$ 48,384.12
20.00	PZA	SUMINISTRO Y COLOCACIÓN DE UNIDAD DE VENTILACIÓN (EXTRACTOR) MARCA SOLAR STAR, MODELO 1600 PARA INSTALAR EN TECHUMBRE PLANA Y/O INCLINADA, INCLUYE: COLOCACIÓN, ELEMENTOS DE FIJACIÓN, ELEVACIONES A	$ 476,982.49
389.84	ML	REPARACIÓN DE CANALÓN METÁLICO DE BAJADA DE AGUA PLUVIAL, INCLUYE: RETIRO CON CARDA Y PULIDORA DE SELLOS (SILICÓN) EXISTENTES EN UNIONES DE LÁMINAS Y BAJADAS DE TUBO DE 4" A 6" DE DIÁMETRO, CAMBIO DE	$ 58,937.10

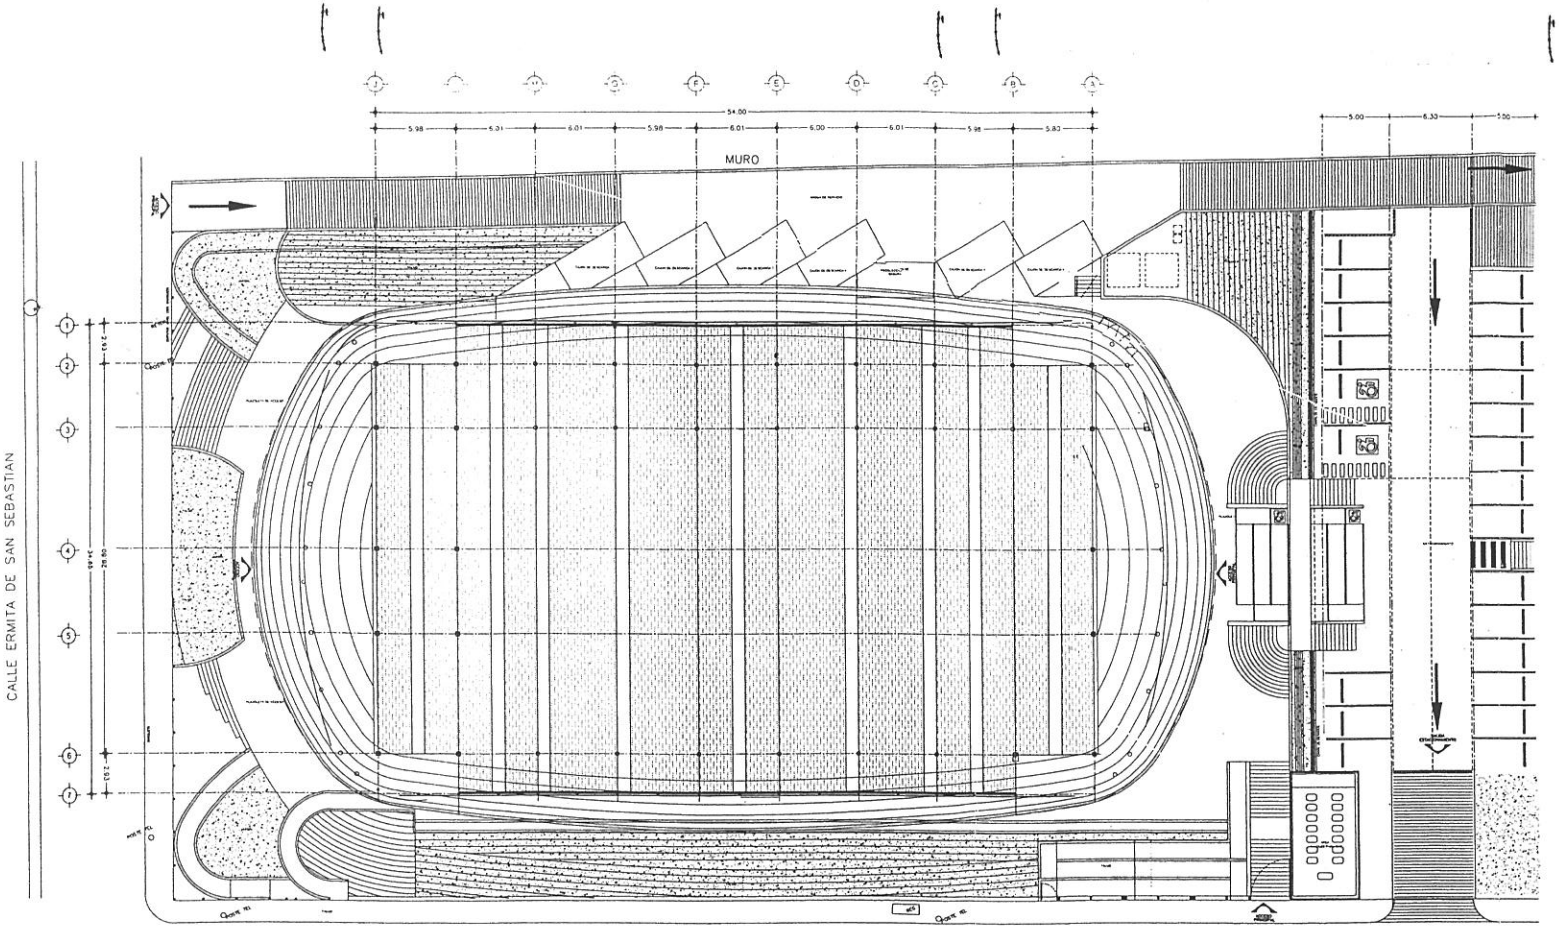$ 2,458,459.16



PLANTA DE COLOCACION DE LAMINA

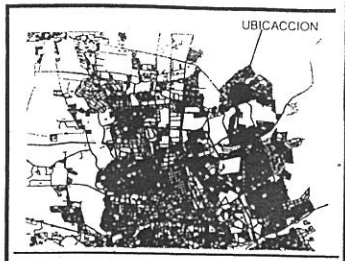ESCALA 1:150 COTAS EN M.



SIMBOLOGIA

NOTAS :

SUMINISTRO Y COLOCACIÓN DE LAMINA DE ACERO GALVANIZADO ONDULAR TERNIUM TO-100 CALIBRE 26 MARCA TERNIUM

SUMINISTRO Y COLOCACIÓN DE AISLAMIENTO TERMICO INTERIOR PARA CUBIERTAS, (MBI) de 2"

COLOCACIÓN DE LAMINA TRASLUCIDA DESMONTADA EN BUEN ESTADO

Aguascalientes
LA CIUDAD DE TU VIDA

DIGITALIZO:

REVISO: [illegible] FERNANDO FEDERICO ROSALES

PROYECTO: CAMBIO DE CUBIERTA HERRADA UNIDAD

UBICACIÓN: CALLE ERMITA DE SAN SEBASTIAN Y CALLE ROGELIO DE LA TORRE, UNIDAD DE NUESTRA SEÑORA DE LA ASUNCIÓN, SECTOR GUADALUPE, Fracc. 10

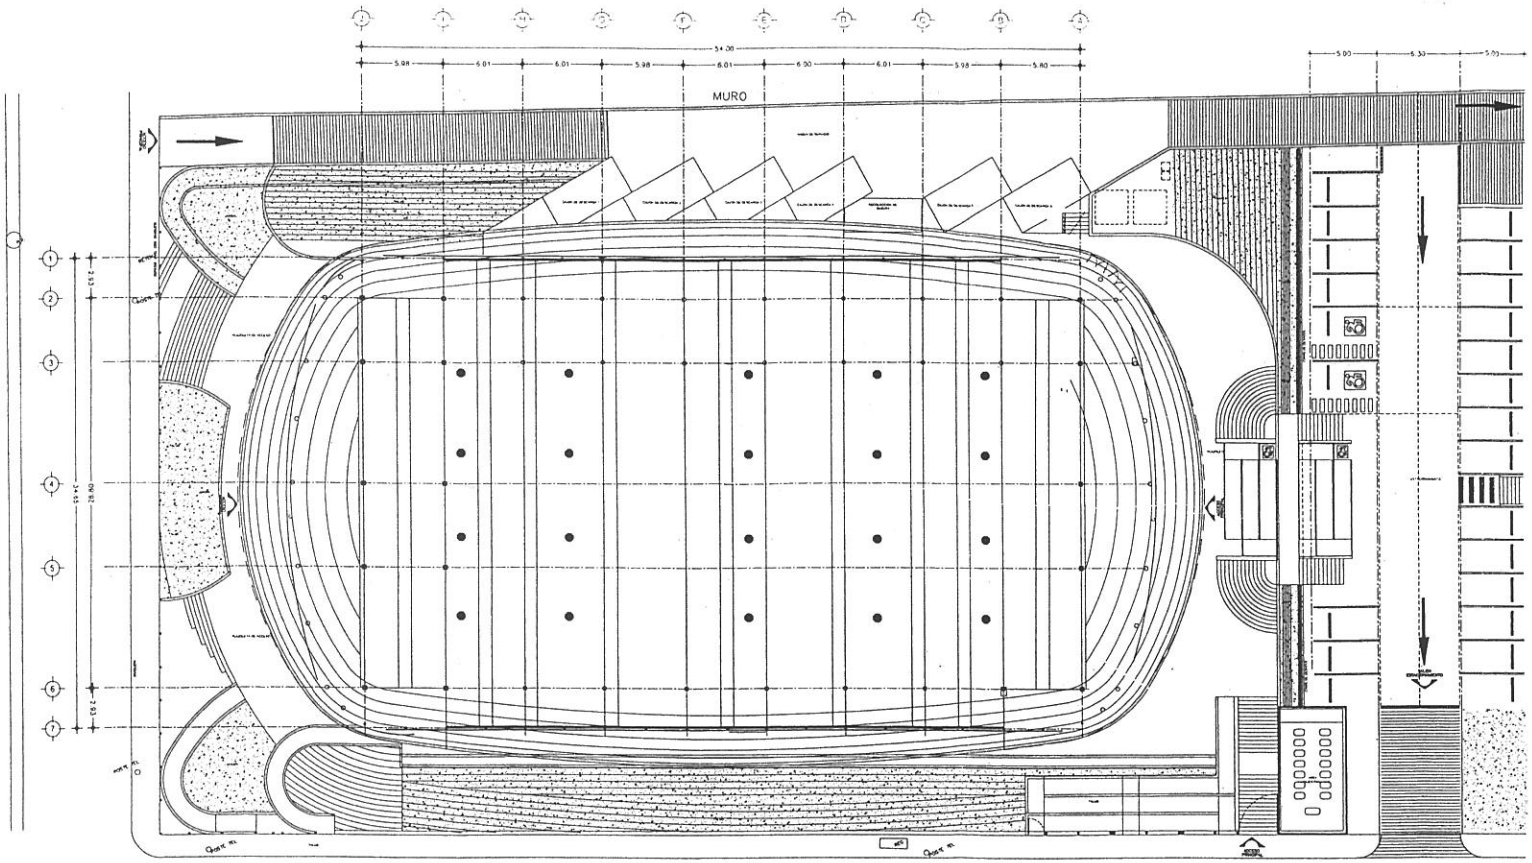
CONTRATO: FIEMDF-0057-2022

CONTENIDO: PLANO DE OBRA TERMINADA

CLAVE: ARQ-01 ESCALA: S/E FECHA: SEP DEL 2022 Nº DE PLANO: 1


ELABORO: [illegible]

CONTRATISTA



PLANTA DE COLOCACION DE EXTRACTORES

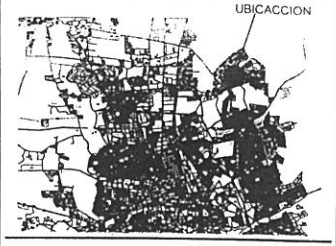ESCALA 1:150 COTAS EN M.



SIMBOLOGIA

NOTAS:

UNIDAD DE VENTILACION (EXTRACTOR) MARCA SOLAR STAR, MODELO 1600 PARA INSTALAR EN TECHUMBRE PLANA Y/O INCLINADA

Aguascalientes
LA CIUDAD DE TU VIDA

DIGITALIZO:

REVISO: ING. FERNANDO MEDRANO PADILLA

PROYECTO: TECHADO DE CUBIERTA MERCADO LA SAL


UBICACIÓN: CALLE ERMITA DE SAN SEBASTIAN Y CALLE ROGELIO DE LA TORRE, ZONA DE HUERTA SENTRA DE LA ASUNCION SECTOR GUADALUPE Fraccs. 10...

CONTRATO: FISMDF-0057-2022

CONTENIDO: PLANO DE OBRA TERMINADA

CLAVE:	ESCALA: S/E	Nº DE PLANO:
ARQ-02	FECHA: SEP DEL 2022	1

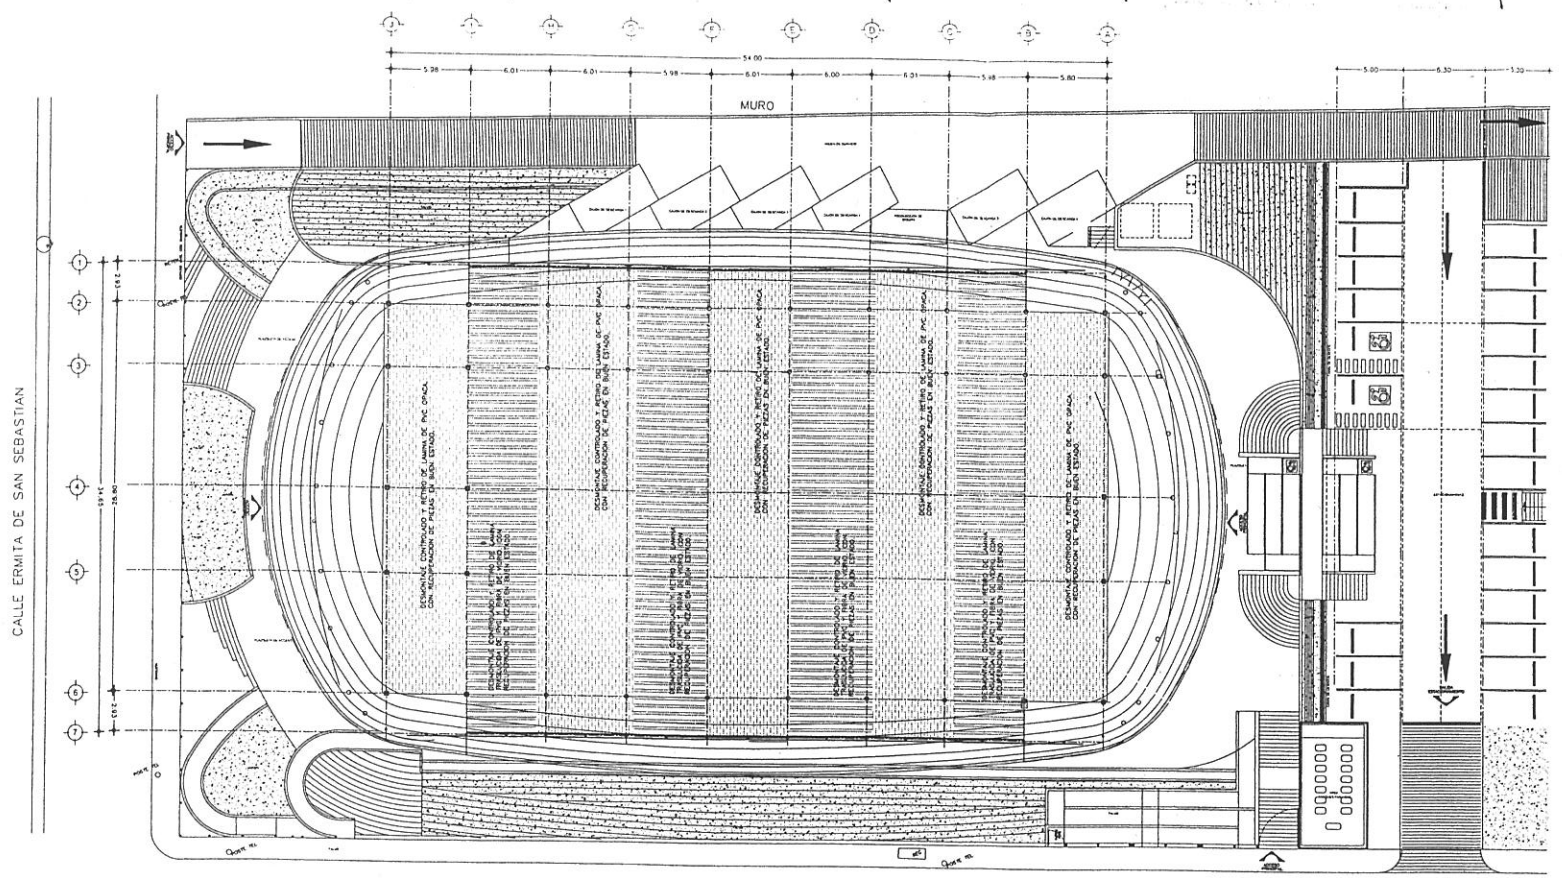
ELABORO: CONTRATISTA



PLANTA DE DESMONTAJES DE AZOTEAS

ESCALA 1:150

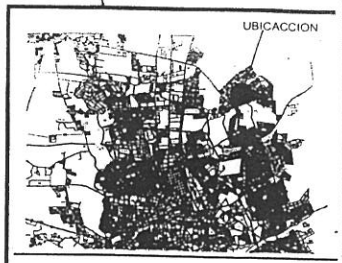COTAS EN M.



SIMBOLOGIA

NOTAS :

DESMONTAJE CONTROLADO Y RETIRO DE LAMINA DE PVC OPACA CON RECUPERACION DE PIEZAS EN BUEN ESTADO.

DESMONTAJE CONTROLADO Y RETIRO DE PANEL COMPUESTO DE ALUMINIO, SOLO PIEZAS DAÑADAS EN EL PUNTO INDICADO.

DESMONTAJE CONTROLADO Y RETIRO DE LAMINA TRASLUCIDA DE PVC Y FIBRA DE VIDRIO. CON RECUPERACION DE PIEZAS EN BUEN ESTADO.

Aguascalientes
LA CIUDAD DE TU VIDA

DIGITALIZO:

REVISO: ING. FERNANDO MEDRANO ROQUE.

PROYECTO: CAMBIO DE CUBIERTA MERCADO "J.M.S.A."

UBICACIÓN: CALLE ERMITA DE SAN SEBASTIAN y CALLE ROGELIO DE LA TORRE, VILLA DE NUESTRA SEÑORA DE LA ASUNCION SECTOR GUADALUPE Fraccionamiento


CONTRATO: FISMDF-0057-2022

CONTENIDO: PLANO DE OBRA TERMINADA

CLAVE:	ESCALA: S/E	Nº DE PLANO:
DM-01	FECHA: SEP DEL 2022	1


ELABORO:

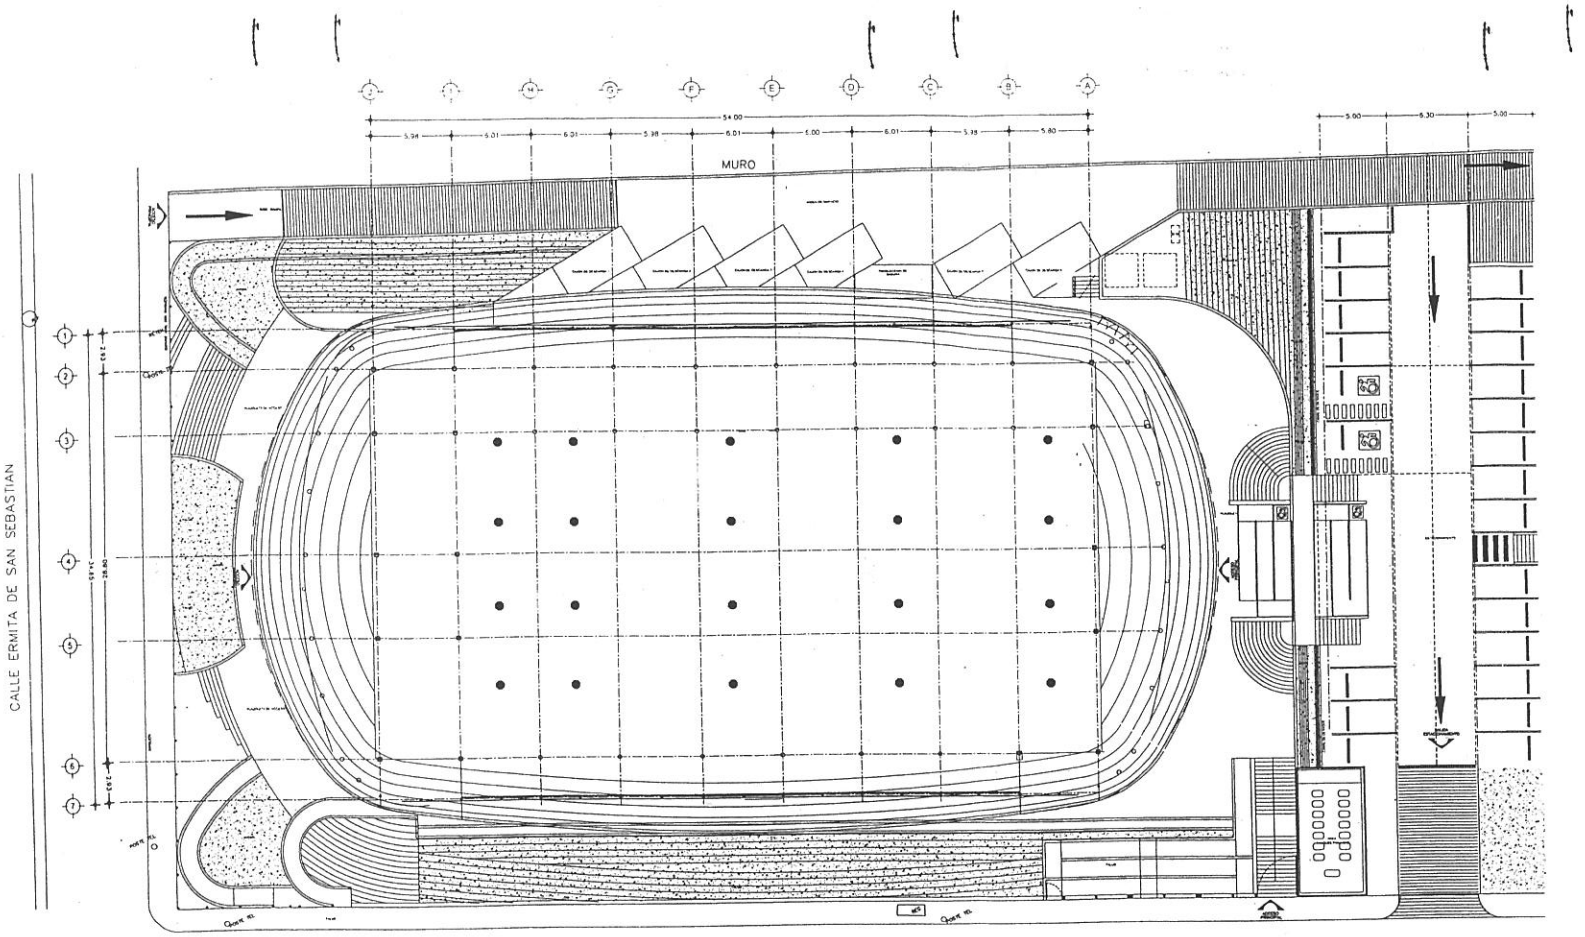CONTRATISTA



PLANTA DE RETIRO DE EXTRACTORES

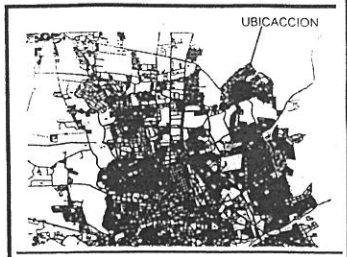ESCALA 1:150 COTAS EN M.



SIMBOLOGIA

NOTAS:

UNIDAD DE VENTILACION SOLAR MODELO RM-1600 PARA LOSA PLANA E INCLINADA MARCA SOLATUBE

Aguascalientes
LA CIUDAD DE TU VIDA

DIGITALIZO:

REVISO: I.C. FERNANDO VIEDRAS RODUEL

PROYECTO: TECHO DE CUBIERTA MERCADO V.N.S.A.

UBICACIÓN: CALLE ERMITA DE SAN SEBASTIÁN Y CALLE ROGELIO DE LA TORRE, COL. DE NUESTRA SEÑORA DE LA ASUNCIÓN SECTOR GUADALUPE FRACC. IV.

CONTRATO: PRMOP-0057-2022

CONTENIDO: PLANO DE OBRA TERMINADA

CLAVE:	ESCALA: S/E	Nº DE PLANO:
DM-02	FECHA: SEP DEL 2022	1

ELABORO:

CONTRATISTA