Aguascalientes
LA CIUDAD DE TU VIDA

Dirección de Programación Presupuestal
Núm. Oficio AMPP/0389/22
Aguascalientes, Ags. 26 de Septiembre del 2022
Asunto: Validación de Expediente Técnico

C.P. SERGIO ARTURO LOZANO GONZÁLEZ
SECRETARIO DE FINANZAS MUNICIPALES
P R E S E N T E

Con fundamento en los artículos 17 fracción XV, 60 fracción XVI y 76 fracción VI del Reglamento del Sistema Integral de Desarrollo Municipal y del Instituto Municipal de Planeación y Evaluación de Aguascalientes, hago referencia al oficio SOPMA/2066/2022 recibido por este Instituto el día 21 de Septiembre del 2022 por parte de la Secretaría de Obras Públicas, mediante el cual remiten el expediente técnico original de la siguiente obra para su análisis, registro y priorización, conforme al Programa Anual de Obra Pública y Programas Sociales para el ejercicio presupuestal 2022:

DEPENDENCIA EJECUTORA:	SECRETARÍA DE OBRAS PÚBLICAS
NOMBRE DE LA OBRA O PROYECTO:	OBRA COMPLEMENTARIA Y SEÑALIZACIÓN
UBICACIÓN:	AV. DE LA CONVENCIÓN 1914 SUR (CALZADA SUR), ENTRE JOSÉ MA. CHÁVEZ Y HÉROE DE NACOZARI, VARIAS COLONIAS, AGUASCALIENTES, AGS.
FONDO DE INVERSIÓN:	PROGRAMA DIRECTO MUNICIPAL
IMPORTE:	$919,284.26 (ET FINAL)
No. DE OBRA:	2022-PDM-0054-UR-0503
MODALIDAD DE EJECUCIÓN:	CONTRATO
EJE:	MUNICIPIO SOBRESALIENTE
ESTRATEGIA:	OBRA PÚBLICA INTELIGENTE
POLITICA:	5.8.1.REHABILITACIÓN Y MANTENIMIENTO VIALIDADES, CAMINOS, CALLES, ÁREAS DE TERRACERÍA Y CAUCES (COM.

Al respecto, hago de su conocimiento que dicho expediente ha sido analizado en su integración técnica y documental, con base en el artículo 168 fracción I del Reglamento de la Ley de Obras Públicas y Servicios Relacionados para el Estado de Aguascalientes y sus Municipios.

Asimismo, le comento que este Instituto valida dicha obra acorde a lo establecido en los artículos 14, 22 párrafo segundo y 23 de la Ley de Obras Públicas y Servicios Relacionados para el Estado de Aguascalientes y sus Municipios, la cual se encuentra alineada al Plan de Desarrollo Municipal vigente, para dar cumplimiento a las metas establecidas en el mismo.

Cabe hacer mención que los recursos solicitados para este proyecto de inversión, estarán sujetos a la disponibilidad presupuestal para el presente ejercicio fiscal que determine la Secretaría a su digno cargo. Sin otro particular por el momento, le envío un cordial saludo.

A T E N T A M E N T E

DR. en A.P. GUILLERMO DE LA TORRE SIFUENTES
DIRECTOR GENERAL

CAAR / JDBC
C.c.p. I.C. Arq. Gloria Guadalupe Castillo González .- Secretaría de Obras Públicas .Para su conocimiento.
C.c.p. Archivo.

Instituto Municipal de Planeación y Evaluación de Aguascalientes

Antonio Acevedo Escobedo 103 A. Col. Centro
Aguascalientes. Ags. C.P. 20000
(449) 9101010 Ext. 3117
www.implanags.gob.mx

GOBIERNO MUNICIPAL DE AGUASCALIENTES

INSTITUTO MUNICIPAL DE PLANEACION

IMPLAN

ANÁLISIS INTEGRAL DE EXPEDIENTE TÉCNICO

No. DE OBRA (PAOP 2020):	2022-PDM-0054-UR-0503	REGISTRO No.	220
OFICIO DE VALIDACIÓN:	AMPP/0389/22	FECHA RECIBIDO PARA REVISIÓN:	26 de Septiembre del 2022
PROGRAMA:	URBANIZACIÓN	LOCALIDAD O COLONIA:	VARIAS COLONIAS
SUB-PROGRAMA:	Vialidades Urbanas (Construcción, Ampliación y Rehabilitación)	DELEGACIÓN:	Aguascalientes
DEPENDENCIA:	Secretaría de Obras Públicas	MOD. DE EJECUCIÓN:	CONTRATO
NOMBRE DE LA OBRA:	OBRA COMPLEMENTARIA Y SEÑALIZACIÓN, AV. DE LA CONVENCIÓN 1914 SUR (CALZADA SUR), ENTRE JOSÉ MA. CHÁVEZ Y HÉROE DE NACOZARI		
FUENTE DE FINANCIAMIENTO:	PROGRAMA DIRECTO MUNICIPAL, PDM		
INVERSIÓN:	$919,284.26	CLASIFICACIÓN DE OBRA:	BIENES DE DOMINIO PUBLICA

TOTAL	FEDERAL	ESTATAL	MUNICIPAL	BENEFICIARIOS	OTROS	DIFERENCIA ENTRE MOD.
$919,284.26	0.00	0.00	$919,284.26	0.00	0.00	*$4.127,73*

TIPO DE EXPENDIENTE:	ET FINAL	AÑO: 2022	AÑO:	AÑO:		
AVANCES:	Financiero: 30 %	Físico: 99 %				
FECHA DE INICIO:	11 de Junio del 2022	FECHA DE TÉRMINO:	10 de Julio del 2022	REGISTRO SIMA:	54	

CHEK LIST DE LOS ANEXOS DEL EXPEDIENTE TÉCNICO

CÉDULA DE REGISTRO DE OBRA	✓
DICTAMEN DE FACTIBILIDAD	✓
MEMORIA DESCRIPTIVA	✓
PRESUPUESTO BASE	✓
FACTIBILIDAD VERIFICADA EN CAMPO	✓
CROQUIS DE UBICACIÓN (MACRO)	✓
CROQUIS DE UBICACIÓN (MACRO)	✓
PROGRAMA DE OBRA Y MONTOS MENSUALES	✓
PLANOS O ESTUDIOS TÉCNICOS	✓
PADRÓN DE BENEFICIARIOS	N/A
ACTA DE ACEPTACIÓN DEL PROYECTO	N/A
DICTAMEN DE IMPACTO AMBIENTAL	N/A
CONVENIO DE CONCERTACIÓN	N/A
ACTA CONSTITUTIVA	N/A

METAS		BENEFICIARIOS		PERIODO DE EJECUCION		OBRA PROPUESTA		CLAVE SISCO
UNIDAD DE MEDIDA	CANT	TIPO DE BENEFICIARIOS	CANTIDAD	FECHA DE INICIO	FECHA DE TERMINO	CONCEPTO	JORNALES A GENERAR	
OBRA	1	Personas	450	2022-06-11	2022-07-10	Señalética	2390	2329

INCLUIDO EN PLAN DE DESARROLLO MUNICIPAL Y EL PROGRAMA ANUAL DE OBRA PÚBLICA

OBSERVACIONES:

SIN OBSERVACIONES

RECIBIO: ING. JOSÉ DAVID BURGUETE CLAUSTRO

Analista de Programación e Inversión de Obra Pública

26 de Septiembre del 2022

Fecha de validación

26 de Septiembre del 2022

Fecha de validación Expediente

PROCEDE Si ✓ No

H. AYUNTAMIENTO CONSTITUCIONAL DEL MUNICIPIO DE AGUASCALIENTES 2021-2024

AYUNTAMIENTO DE AGUASCALIENTES

CEDULA DE REGISTRO POR OBRA

Aguascalientes

050400-001E00E05-05-2-2-1-00-1-E-0510-0-17-0054-21-1520-6144

2022-PDM-0054-UR-05-009	Obra **OBRA COMPLEMENTARIA Y SEÑALIZACIÓN AV. CONVENCIÓN 1914 SUR (CALZADA SUR)**
Tipo DEFINITIVO 1 2022 Folio SISCO **2329**	Ubic. TRAMO: ENTRE AV. JOSÉ MA. CHÁVEZ Y AV. HÉROE DE NACOZARI, AGUASCALIENTES Mpio.

Ent. Ejecutora : **050400001E00E05**

Eje: **05**	MUNICIPIO SOBRESALIENTE
Finalidad: **2**	DESARROLLO SOCIAL
Función: **2**	VIVIENDA Y SERVICIOS A LA COMUNIDAD
Subfunción: **1**	URBANIZACIÓN
Tema: **00**	SIN TEMA
Cuenta del Gasto **1**	GASTO PROGRAMABLE
Clasif. Programatica: **E**	PRESTACIÓN DE SERVICIOS PÚBLICOS
Programa: **0510**	Movilidad Urbana
SubPrograma: **0**	SUBPROGRAMA GENÉRICO
Proyecto: **17**	
Tipo de Gasto: **21**	GASTO INVERSIÓN / OBRA PÚBLICA

INVERSION 2022

Municipal	1520	FONDO DE ESTABILIZACIÓN DE LOS INGRESOS DE LAS ENTIDADES FEDERATIVAS 2022	$919,284.26
		Folio SIMA 54 Total	$919,284.26

METAS

Unidad de Medida	Cantidad	Descripción
OBRA	1	OBRA OBRA COMPLEMENTARIA Y SEÑALIZACIÓN AV. CONVENCIÓN 1914 SUR (CALZADA SUR)

Inversión Ejercida Total al	31 de Diciembre de 2021	$0.00
Avance Fisico Acumulado al	31 de Diciembre de 2021	
Avance Fisico Acumulado Programado al	31 de Diciembre de 2022	100 %

Fecha de Inicio 11 Jun 2022 Fecha de Terminación 10 Jul 2022

Jornales a Generar en 2022 2390

Modalidad de ejecución CONTRATO

Clasificación de la Obra Bienes de Dominio Público

Registro del Patrimonio: Obras del dominio público

SECRETARÍA DE OBRAS PÚBLICAS

Av. Aguascalientes Sur No. 2615
Fracc. Jardines de las Fuentes,
Aguascalientes, Ags. C.P. 20278

(449) 9 78 92 01, 06, 09

www.ags.gob.mx

GENERALES

Nombre del Proyecto : OBRA COMPLEMENTARIA Y SEÑALIZACIÓN AV. CONVENCIÓN 1914 SUR (CALZADA SUR)

TRAMO: ENTRE AV. JOSÉ MA. CHÁVEZ Y AV. HÉROE DE NACOZARI, AGUASCALIENTES Mpio.

Programa : UR URBANIZACIÓN

Subprograma : 05 VIALIDADES URBANAS (CONSTRUCCION, AMPLIACION Y REHABILITACION) (c).- Semáforos, Señalización y Sincronización (señales, placas, nomenclatura, pintura y otras))

Clave del Municipio : AGUASCALIENTES

Localidad :

Barrio, Colonia o Ejido : AGUASCALIENTES Mpio.

Tipo de Obra :

DESCRIPCIÓN DEL PROYECTO:

OBRA COMPLEMENTARIA Y SEÑALIZACIÓN AV. CONVENCIÓN 1914 SUR (CALZADA SUR) 1.00 obra

Beneficiarios (No. y Tipo) :

450	PERSONAS

OBRAS PÚBLICAS

No. Folio SISCO 2329

Los abajo firmantes, hacen constar que el presente proyecto :

OBRA COMPLEMENTARIA Y SEÑALIZACIÓN AV. CONVENCIÓN 1914 SUR (CALZADA SUR)

TRAMO: ENTRE AV. JOSÉ MA. CHÁVEZ Y AV. HÉROE DE NACOZARI, AGUASCALIENTES Mpio.

cumple con los Requisitos y Normas Técnicas establecidas por la Dependencia Normativa, por lo que es viable su ejecución. Comprometiéndose la misma a proporcionar la supervisión y asistencia técnica necesaria durante el proceso administrativo.

Por la Dependencia Ejecutora

Arq. Gloria Guadalupe Castillo González
Encargada de Despacho de la Secretaría de Obras Públicas

Lic. Jaime Gallo Camacho
Secretario de Desarrollo Urbano

LUGAR :AGUASCALIENTES, AGS.

Av. Aguascalientes Sur No. 2615
Fracc. Jardines de las Fuentes,
Aguascalientes, Ags. C.P. 20278

(449) 9 78 92 01, 06, 09

www.ags.gob.mx

No. Folio SISCO 2329

H. AYUNTAMIENTO CONSTITUCIONAL DEL MUNICIPIO DE AGUASCALIENTES 2021-2024

AYUNTAMIENTO DE AGUASCALIENTES

FACTIBILIDAD VERIFICADA EN CAMPO

Aguascalientes
LA CIUDAD DE TU VIDA

MUNICIPIO: AGUASCALIENTES

LOCALIZACION: TRAMO: ENTRE AV. JOSÉ MA. CHÁVEZ Y AV. HÉROE DE NACOZARI, AGUASCALIENTES Mpio.

PROGRAMA: URBANIZACIÓN

SUBPROGRAMA: VIALIDADES URBANAS (CONSTRUCCION, AMPLIACION Y REHABILITACION) (c).- Semáforos, Señalización y Sincronización (señales, placas, nomenclatura, pintura y otras))

OBRA A REALIZAR: OBRA COMPLEMENTARIA Y SEÑALIZACIÓN AV. CONVENCIÓN 1914 SUR (CALZADA SUR)

DEPENDENCIA EJECUTORA: SECRETARÍA DE OBRAS PUBLICAS DEL MUNICIPIO DE AGUASCALIENTES

FORMA DE EJECUCION: CONTRATO

TIPO DE OBRA PROPUESTA:

CONDICIONES ACTUALES DE LA OBRA:

OBRA COMPLEMENTARIA Y SEÑALIZACIÓN AV. CONVENCIÓN 1914 SUR (CALZADA SUR)

CARACTERISTICAS DE LA OBRA: Bueno

FACTIBILIDAD DE LA OBRA:

ESTA OBRA SE REQUIERE PARA EL BENEFICIO DE LA CIUDADANÍA

PROCEDE: SI [X] NO [ ]

REVISÓ: Jefa del Departamento de Expedientes Tecnicos y Costos

NOMBRE: Arq. Blanca Margarita Martinez Amador

FIRMA:

FECHA: 12 Sep 2022

SECRETARÍA DE OBRAS PÚBLICAS

Av. Aguascalientes Sur No. 2615
Fracc. Jardines de las Fuentes,
Aguascalientes, Ags. C.P. 20278


(449) 9 78 92 01, 06, 09

www.ags.gob.mx

No. Folio SISCO 2329

H. AYUNTAMIENTO DE AGUASCALIENTES
SECRETARÍA DE OBRAS PÚBLICAS
DIRECCIÓN DE SUPERVISIÓN DE OBRA
UBICACIÓN

OBRA:	DM-0054-2022 - OBRA COMPLEMENTARIA Y SEÑALIZACIÓN AV. CONVENCIÓN 1914 SUR (CALZADA SUR)					
NO. DE CONT	DM-0054-2022	CONTRATISTA:	JLJ CONSTRUCCIONES, S.A. DE C.V.			

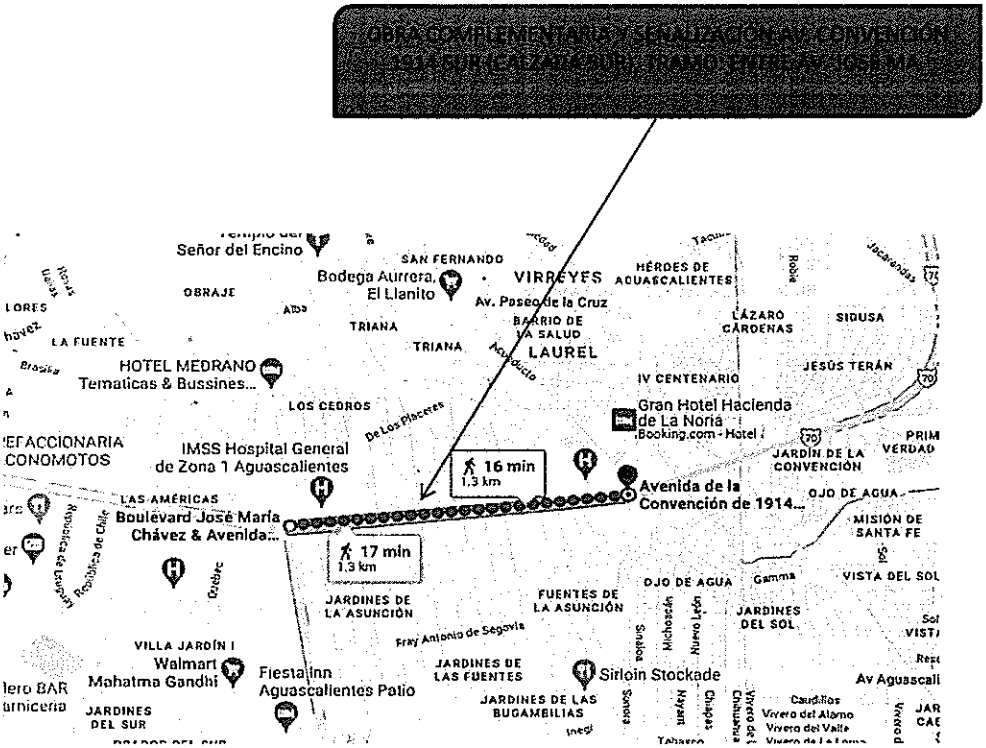


ING. RICARDO MACÍAS MERCADO
SUPERVISOR DE OBRA.

H. AYUNTAMIENTO DE AGUASCALIENTES
SECRETARÍA DE OBRAS PÚBLICAS
DIRECCIÓN DE SUPERVISIÓN DE OBRA
LOCALIZACION

OBRA:	DM-0054-2022 - OBRA COMPLEMENTARIA Y SEÑALIZACIÓN AV. CONVENCIÓN 1914 SUR (CALZADA SUR)					
NO. DE CONT	DM-0054-2022	CONTRATISTA:	JLJ CONSTRUCCIONES, S.A. DE C.V.			

OBRA COMPLEMENTARIA Y SEÑALIZACIÓN AV. CONVENCIÓN 1914 SUR (CALZADA SUR), TRAMO: ENTRE AV. JOSÉ MA. CHÁVEZ Y AV. HÉROE DE NACOZARI

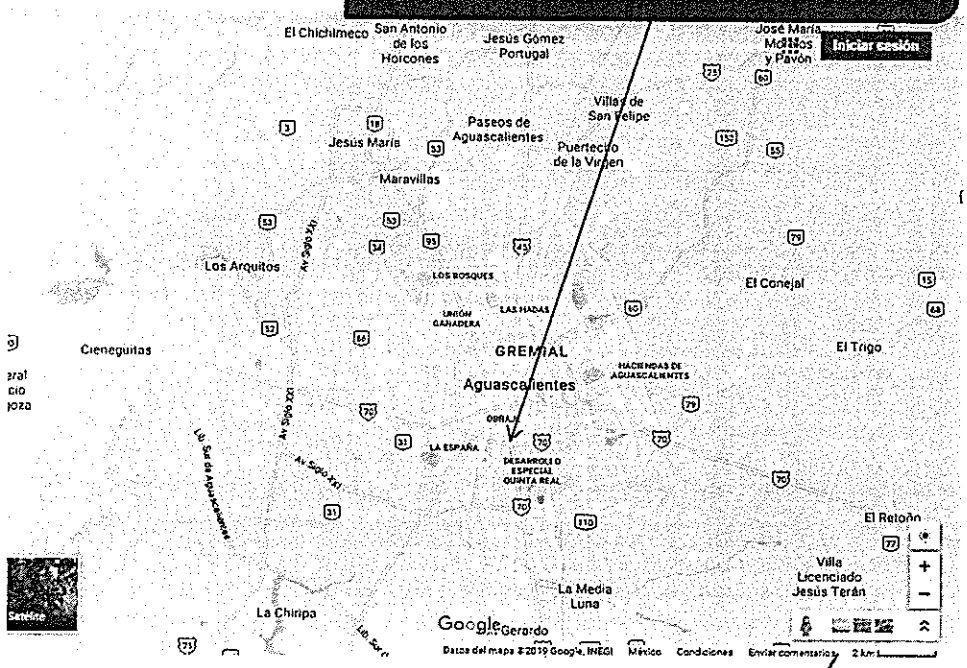

ING. RICARDO MACÍAS MERCADO
SUPERVISOR DE OBRA.

RO3-POS-SOS-7.5.1-04	
REVISION:	00
ESCALA DE RESPONSABLE:	SUPERVISOR DE OBRA
TIEMPO DE RET:	02 AÑOS

Aguascalientes

PROGRAMA DE OBRA DEFINITIVO

No. DE CONTRATO : DM-0054-2022

PROGRAMA: UR-URBANIZACIÓN

INICIO VIGENTE: 11-junio-22

No. OBRA Y NOMBRE DE LA OBRA: DM-0054-2022 - OBRA COMPLEMENTARIA Y SEÑALIZACIÓN AV. CONVENCIÓN 1914 SUR (CALZADA SUR)

TERMINO REAL: 10-julio-22

RECURSO

CONCEPTO				1	2	3	4	5	6	7	8	9	10	11	12	13	14	15	16	PONDERACIÓN %	
				2022																FINANCIERO	FÍSICO
				ENERO	FEBRERO	MARZO	ABRIL	MAYO	JUNIO 11-jun	JULIO 10-jul	AGOSTO	SEPTIEMBRE	OCTUBRE	NOVIEMBRE	DICIEMBRE					%	%
DESCRIPCION		INVERSION																			
DM-0054-2022 - OBRA COMPLEMENTARIA Y SEÑALIZACION AV. CONVENCION 1914 SUR (CALZADA SUR)																					
TRAMO: ENTRE AV. JOSE M.A. CHAVEZ Y AV. HEROE DE NACOZARI, AGUASCALIENTES Norte																					
PRELIMINARES	$	4,086.14	100						100											0.52	11.11
OBRA COMPLEMENTARIA	$	193,348.79	100						50	50										24.40	22.22
LIMPIEZAS	$	521.67	100							100										0.07	11.11
SEÑALIZACION	$	569,851.07	100						40	60										71.78	22.22
SEÑALIZACION VERTICAL	$	7,297.68	100							100										0.92	11.11
EXTRAORDINARIOS	$	18,381.08	100						60	40										2.32	22.22
SUBTOTAL SIN IVA	$	792,486.43	$ 0.00	0	0	0	0	0	21	2	0	0	0	0	0	0	0	0	0		
AVANCE SEMANAL %				0%	0%	0%	0%	0%	22%	22%	0%	0%	0%	0%	0%	0%	0%	0%	0%		
AVANCE SEMANAL ACUMULADO %				0%	0%	0%	0%	0%	22%	44%	44%	44%	44%	44%	44%	44%	44%	44%	44%	100.00	100.00
EJERCIDO SEMANAL $				-	-	-	-	-	100,760.54	214,314.82	362,330.29	-	-	-	-	-	-	-	-		
EJERCIDO MENSUAL $				$0.00	$0.00	$0.00	$0.00	$0.00	$777,314.65	$15,171.78	$0.00	$0.00	$0.00	$0.00	$0.00	$0.00	$0.00	$0.00	$0.00	$ 792,486.43	
EJERCIDO MENSUAL ACUMULADO $				0.00	0.00	0.00	0.00	0.00	777,314.65	792,486.43	792,486.43	792,486.43	792,486.43	792,486.43	792,486.43	792,486.43	792,486.43	792,486.43	792,486.43	$ 126,797.83	IVA 0%
EJERCIDO SEMANAL %				0%	0%	0%	0%	0%	13%	1%	0%	0%	0%	0%	0%	0%	0%	0%	0%		
EJERCIDO MENSUAL %				0%	0%	0%	0%	0%	98%	2%	0%	0%	0%	0%	0%	0%	0%	0%	0%	GRAN TOTRAL EJERCIDO	
EJERCIDO MENSUAL ACUMULADO %				0%	0%	0%	0%	0%	98%	100%	100%	100%	100%	100%	100%	100%	100%	100%	100%	$	918,284.26

ING. RICARDO MACÍAS MERCADO
SUPERVISOR

PRESIDENCIA MUNICIPAL DE AGUASCALIENTES

FACTIBILIDAD VERIFICADA EN CAMPO

GENERALES

EJERCICIO: 2022 APROBACION No: 2022-PDM-0054-UR-05-009
LOCALIDAD: TRAMO: ENTRE AV. JOSÉ MA. CHÁVEZ Y AV. HÉROE DE NACOZARI, AGUASCALIENTES Mpio.
MUNICIPIO: AGUASCALIENTES, AGS
TIPO DE INVERSION: PROGRAMA DIRECTO MUNICIPAL (1520 FONDO DE ESTABILIZACIÓN DE LOS INGRESOS DE LAS ENTIDADES FEDERATIVAS)

PROGRAMA: UR-URBANIZACIÓN
SUB-PROGRAMA: 05-VIALIDADES URBANAS, (CONSTRUCCION, AMPLIACION Y REHABILITACION) (C).- SEMAFOROS, SEÑALIZACION Y SICRONIZACION (SEÑALES, PLACAS, NOMENCLATURA, PINTURA Y OTRAS))

OBRA A REALIZARSE: DM-0054-2022 - OBRA COMPLEMENTARIA Y SEÑALIZACIÓN AV. CONVENCIÓN 1914 SUR (CALZADA SUR)

DEPENDENCIA EJECUTORA: SECRETARÍA DE OBRAS PÚBLICAS MUNICIPALES (S.O.P.M.A)
FORMACIÓN DE EJECUCION: CONTRATO NO. DE CONTRATO: DM-0054-2022
NOMBRE CONTRATISTA: JLJ CONSTRUCCIONES, S.A. DE C.V.
REPRESENTANTE: JOSÉ JULIÁN SERNA QUEZADA, ING.
MONTO CONT. ORIGEN $919,284.26 ANTICIPO: $237,745.93 30 DIAS
1A AMPLIACION $: 0 1 AMPL DIAS 0
2A AMPLIACION $: 0 2 AMPL DIAS 0
FIRMA CONTRATO: 08/06/2022
INICIO CONT: dd/mm/aa 9 de junio de 2022 TERMINO CONT 8 de julio de 2022
INICIO REAL: dd/mm/aa 11 de junio de 2022 TERMINO REAL: 10 de julio de 2022

TIPO DE OBRA PROPUESTA

NUEVA CREACIÓN		CONSOLIDACIÓN	
COMPLEMENTARIA		AMPLIACIÓN	
REHABILITACIÓN	X	EQUIPAMIENTO	

CARACTERÍSTICAS DE LA OBRA:

OBRA COMPLEMENTARIA Y SEÑALIZACIÓN AV. CONVENCIÓN 1914 SUR (CALZADA SUR) en el tramo entre Av. José Ma. Chávez y Av. Héroe de Nacozari, ya que las bases de la vialidad se encuentras en buen estado (funcionables), se renivelarán los brocales, tapas de registros y reparacion de caimanes existentes en la calzada y se pintará la distribución vial según las normas de la SCT. la distribución vial con pintura de trafico según las normas de la SCT.

BUEN ESTADO X REGULAR PESIMO ESTADO

FACTIBILIDAD DE LA OBRA: (CONDICIONES ACTUALES DE LA OBRA)

ESTA OBRA SE ENCUENTRA EN CONDICIONES PARA OPERARSE

PROCEDE: SI: X NO:
MARQUE SOLO UNA

ING. RICARDO MACÍAS MERCADO
SUPERVISOR

PRESIDENCIA MUNICIPAL DE AGUASCALIENTES

FACTIBILIDAD VERIFICADA EN CAMPO

GENERALES

LOCALIDAD: TRAMO: ENTRE AV. JOSÉ MA. CHÁVEZ Y AV. HÉROE DE NACOZARI, AGUASCALIENTES Mpio.

MUNICIPIO: AGUASCALIENTES, AGS

PROGRAMA: UR-URBANIZACIÓN

SUB-PROGRAMA: 05-VIALIDADES URBANAS, (CONSTRUCCION, AMPLIACION Y REHABILITACION) (C).- SEMAFOROS, SEÑALIZACION Y SICRONIZACION (SEÑALES, PLACAS, NOMENCLATURA, PINTURA Y OTRAS))

OBRA A REALIZARSE: DM-0054-2022 - OBRA COMPLEMENTARIA Y SEÑALIZACIÓN AV. CONVENCIÓN 1914 SUR (CALZADA SUR)

DEPENDENCIA EJECUTORA: SECRETARÍA DE OBRAS PÚBLICAS MUNICIPALES (S.O.P.M.A)

FORMACIÓN DE EJECUCION: CONTRATO

TIPO DE OBRA PROPUESTA

NUEVA CREACIÓN		CONSOLIDACIÓN	
COMPLEMENTARIA		AMPLIACIÓN	
REHABILITACIÓN	X	EQUIPAMIENTO	

CARACTERÍSTICAS DE LA OBRA:

OBRA COMPLEMENTARIA Y SEÑALIZACIÓN AV. CONVENCIÓN 1914 SUR (CALZADA SUR) en el tramo entre Av. José Ma. Chávez y Av. Héroe de Nacozari, ya que las bases de la vialidad se encuentras en buen estado (funcionables), se renivelarán los brocales, tapas de registros y reparacion de caimanes existentes en la calzada y se pintará la distribución vial según las normas de la SCT. la distribución vial con pintura de trafico según las normas de la SCT.

CONDICIONES ACTUALES DE LA OBRA:

BUEN ESTADO:	X	REGULAR:		PESIMO ESTADO:	

FACTIBILIDAD DE LA OBRA:

ESTA OBRA SE ENCUENTRA EN CONDICIONES PARA OPERARSE

PROCEDE	**SI:**	X	**NO:**	

ING. RICARDO MACÍAS MERCADO
SUPERVISOR

PRESUPUESTO MODIFICADO

Obra: **OBRA COMPLEMENTARIA Y SEÑALIZACIÓN AV. CONVENCIÓN 1914 SUR (CALZADA SUR)**

Ubicación: **TRAMO: ENTRE AV. JOSÉ MA. CHÁVEZ Y AV. HÉROE DE NACOZARI, AGUASCALIENTES Mpio.**

Contratista: **JLJ CONSTRUCCIONES, S.A. DE C.V. (627)**

No.	Concepto	Unidad	Cantidad	Precio Unitario	Importe Total
	GRUPO: **OBRA COMPLEMENTARIA Y SEÑALIZACION**				
	PARTIDA: **PRELIMINARES**				
1	CORTE CON DISCO DIAMANTADO DE 14" EN PISOS DE CONCRETO ASFÁLTICO DE HASTA (HASTA 8.00 cm. DE PROFUNDIDAD). INCLUYE: TRAZO, EQUIPO Y OPERACIÓN, LIMPIEZAS.	ML	0	$30.22	$0.00
2	DEMOLICIÓN A MANO Y MECÁNICA DE PAVIMENTO HIDRÁULICO Y/O ASFÁLTICO EN CUALQUIER ESPESOR, EN PAVIMENTOS, LOSAS DIAMANTE, LOSAS DE CAJAS DE VÁLVULAS, LOSAS DE LLAVE HIDRAULICA, CAIMANES, ETC., CON O SIN ARMADO DE ACERO SIN RECUPERACIÓN., INCLUYE: CARGA Y ACARREO LOCAL DE MATERIAL AL LUGAR DE ACOPIO, HERRAMIENTA NECESARIA, CORTES CON DISCO Y TODO LO NECESARIO PARA SU CORRECTA EJECUCIÓN, LIMPIEZA, TRABAJO TERMINADO.	M3	6.19	$660.12	$4,086.14
			Totales por Partida		**$4,086.14**
	PARTIDA: **OBRA COMPLEMENTARIA**				
6	RE NIVELACIÓN DE POZO DE VISITA HASTA 30 cm DE ALTURA. INCLUYE: RETIRO SIN RECUPERACIÓN DE BROCAL EXISTENTE, DEMOLICIONES, NIVELADO CON TABIQUE ROJO RECOCIDO 7X14X28, ASENTADO CON MORTERO CEMENTO-ARENA 1:3 DE 28 cm DE ESPESOR, APLANADO CON MORTERO CEMENTO-ARENA 1:3 , PLOMEADO, NIVELADO, DEMOLICIONES, CARGAS Y ACARREOS DENTRO DE LA OBRA, LIMPIEZA PREVIA Y FINAL.	PZA	8	$2,761.87	$22,094.96
7	CONSTRUCCIÓN DE LOSA DIAMANTE A BASE DE CONCRETO PREMEZCLADO MR= 45 KG/CM2, T.M.A. 3/4" (19 mm), GRAVA TRITURADA, REVENIMIENTO DE 8+-2.5 cm, RESISTENCIA RÁPIDA A 3 DÍAS, DE 25 CM DE ESPESOR, EN POZO DE VISITA, SECCIÓN DE 1.50 M X 1.50 M , INCLUYE: TRAZO, NIVELACIÓN, LIMPIEZA PREVIA Y PREPARACIÓN DE LA SUPERFICIE, COMPACTACIÓN DE TERRENO AL 95% DE SU PVSM, ESCARIFICADO, SUMINISTRO DE MATERIALES, DEMOLICIÓN Y RECONSTRUCCIÓN DE APROCHES, ESPUMA DE POLIURETANO DE ALTA DENSIDAD EN TODO EL PERÍMETRO EXTERIOR DE 1/2", ASÍ COMO EN LAS JUNTAS DIAGONALES PARA FORMAR 4 PARTES, BROCAL Y TAPA DE Fo. Fo. TIPO PESADO (165 KG), CIMBRADO, COLADO, VIBRADO, DESCIMBRADO, CURADO CON MEMBRANA QUÍMICA BASE AGUA, APLANADO FINO EN RECEPCIÓN DE BROCAL, CORTES CON CORTADORA DE DISCO DE 5 CM ENTRE JUNTAS DIAGONALES FORMANDO 8 PIEZAS Y SELLADO DE JUNTAS, CORTES RELLENOS CON MATERIAL PREFORMADO Y SELLADOR AUTONIVELANTE, MANO DE OBRA, CARGA Y ACARREOS DE MATERIAL DENTRO Y FUERA DE LA OBRA, LIMPIEZA FINAL, TRABAJO TERMINADO P.U.O.T	PZA	8	$11,215.16	$89,721.28
9	RENIVELACIÓN DE RASANTE (PARTE SUPERIOR) DE CAJA DE VÁLVULAS TIPO 3 DE HASTA 1.96 X 1. 75 MTS, NIVELADO HASTA UNA ALTURA MAXIMA DE 10 CM, Y MINIMA DE 5 CM. MEDIDAS INTERIORES INCLUYE: TRAZO, EXCAVACIÓN, NIVELACIÓN, PREPARACIONES , Y DEMOLICIONES, RETIRO SIN RECUPERACIÓN DE TAPA DE FOFO EXISTENTE, MURO DE TABIQUE ROJO RECOCIDO COMÚN 7X14X28 CM DE 14 CM DE ESPESOR, JUNTEADO CON MORTERO CEMENTO-ARENA 1:3 APLANADO INTERIOR CON MORTERO CEMENTO ARENA 1:3 DE 2.00 CM DE ESPESOR ACABADO PULIDO, LOSA DE CONCRETO F´C= 250 KG/CM2 T.M.A. 19 MM DE 15 CM DE ESPESOR ARMADA CON VRS No. 3 @15 cm EN AMBOS SENTIDOS, CONTRAMARCO SENCILLO DE CANAL FoFo DE 100 mm, CONTRAMARCO CON TAPA DE FOFO, TIPO PESADO DE 50X50 CM, DEMOLICIÓN Y RECONSTRUCCIÓN DE APROCHES, CARGA Y ACARREOS DENTRO DE LA OBRA, CIMBRADO, DESCIMBRADO, COLADO, VIBRADO, LIMPIEZA PREVIA, FINAL, Y TODO LO NECESARIO PARA LA CORRECTA EJECUCIÓN DEL CONCEPTO. PZA 2.00	PZA	1	$9,576.45	$9,576.45

Obra: **OBRA COMPLEMENTARIA Y SEÑALIZACIÓN AV. CONVENCIÓN 1914 SUR (CALZADA SUR)**

Ubicación: **TRAMO: ENTRE AV. JOSÉ MA. CHÁVEZ Y AV. HÉROE DE NACOZARI, AGUASCALIENTES Mpio.**

Contratista: **JLJ CONSTRUCCIONES, S.A. DE C.V. (627)**

No.	Concepto	Unidad	Cantidad	Precio Unitario	Importe Total
	GRUPO: **OBRA COMPLEMENTARIA Y SEÑALIZACION**				
	PARTIDA: **OBRA COMPLEMENTARIA**				
12	LIMPIEZA Y DESAZOLVE DE POZOS DE VISITA Y LÍNEAS DE ALCANTARILLADO EXISTENTE CON CAMIÓN TIPO VACTOR. INCLUYE: RESANE INTERIOR DEL POZO Y REMATE DE POZO CON TUBO SELLADOR FESTER Y MORTERO 1:3, MANO DE OBRA, SUMINISTRO DE AGUA EN PIPA, HERRAMIENTAS Y EQUIPO PARA SU CORRECTA EJECUCIÓN, LIMPIEZAS, RENTA DE CAMIÓN VACTOR HASTA LA CORRECTA LIMPIEZA DE LAS LÍNEAS EXISTENTES DE POZO A POZO ASÍ COMO EL TRASLADO DE LOS DESECHOS HASTA TIRADERO AUTORIZADO, LA UNIDAD DE MEDIDA SE PAGARA DE POZO A POZO.	LOTE	8	$7,195.61	$57,564.88
13	LIMPIEZA Y DESASOLVE DE CAIMANES DE HASTA 6.00 X 1.50 M DE LONGITUD, INCLUYE: MANO DE OBRA, SUMINISTRO DE AGUA EN PIPA, HERRAMIENTAS Y EQUIPO PARA SU CORRECTA EJECUCION, LIMPIEZAS MANUALES, CARGAS Y ACARREOS LOCALES ASI COMO RETIRO DE MATERIAL PRODUCTO DEL DESASOLVE A TIRADERO AUTORIZADO.	PZA	2	$7,195.61	$14,391.22
			Totales por Partida		**$193,348.79**
	PARTIDA: **LIMPIEZAS**				
15	LIMPIEZA FINAL DE LA OBRA, INCLUYE: BARRIDO, CARGA, ACARREOS Y RETIRO DE ESCOMBROS FUERA DE LA OBRA, TRABAJO TERMINADO.	M2	28.29	$18.44	$521.67
			Totales por Partida		**$521.67**
	PARTIDA: **SEÑALIZACION HORIZONTAL**				
18	SUMINISTRO Y APLICACIÓN DE LOGOTIPO A (SILLA DE RUEDAS) EN PINTURA BASE SOLVENTE COLOR BLANCO EN RAMPAS PARA PERSONAS CON DISCAPACIDAD TAMAÑO Y DISEÑO SEGÚN PLANOS. INCLUYE: TRAZO, ENMASCARILLADO, PLANTILLA, MANO DE OBRA, LIMPIEZA PREVIA Y FINAL DE SUPERFICIE, EQUIPO NECESARIO PARA SU EJECUCIÓN, Y TODO LO NECESARIO PARA SU CORRECTA EJECUCIÓN, TRABAJO TERMINADO.	PZA	16	$59.81	$956.96
20	SUMINISTRO Y APLICACIÓN DE PINTURA BASE SOLVENTE PARA MARCAS EN GUARNICIONES CLASIFICACION M-12.1, M12.2 APLICADA SOBRE GUARNICIONES Y DENTELLONES DE CUALQUIER COLOR, SEGÚN SE REQUIERA Y SEGÚN NORMA S.C.T. SECADO AL TACTO EN 5 MIN Y AL DURO EN 30 MIN CON MICRO ESFERA , DESARROLLO DE 35 CM. INCLUYE: MATERIALES Y ESPECIFICACIONES QUE CUMPLAN CON LA NORMATIVA N-CMT-5-01-001/05, N-PRY-CAR-10-01-002/13 APLICADAS AL DIA DE HOY, TRAZO, MANO DE OBRA, LIMPIEZA PREVIA Y FINAL DE SUPERFICIE, EQUIPO NECESARIO PARA SU EJECUCIÓN, Y TODO LO NECESARIO PARA SU CORRECTA EJECUCIÓN, TRABAJO TERMINADO. (pintura esmalte, ML efectivo)	ML	1988.1	$49.12	$97,655.47
21	SUMINISTRO Y APLICACIÓN DE PINTURA BASE SOLVENTE " EN RAYA SEPARADORA CLASIFICACIÓN M - 1.1, LÍNEA CONTINUA SENCILLA DE DIVISIÓN DE CARRILES DE FRENTE EN PISO, DE 10 CM DE ANCHO, COLOR BLANCO Y/O AMARILLO CON MICRO ESFERA SEGÚN NORMA SCT, SECADO AL TACTO EN 5 MIN Y AL DURO EN 30 MIN. INCLUYE: MATERIALES Y ESPECIFICACIONES QUE CUMPLAN CON LA NORMATIVA N-CMT-5-01-001/05, N-PRY-CAR-10-01-002/13 APLICADAS AL DIA DE HOY, MATERIAL, TRAZO, ENMASCARILLADO, MANO DE OBRA, LIMPIEZA PREVIA DE SUPERFICIE, EQUIPO NECESARIO PARA SU EJECUCIÓN, Y TODO LO NECESARIO PARA SU CORRECTA EJECUCIÓN, TRABAJO TERMINADO.	ML	478.821588	$23.81	$11,400.74

Obra: **OBRA COMPLEMENTARIA Y SEÑALIZACIÓN AV. CONVENCIÓN 1914 SUR (CALZADA SUR)**

Ubicación: **TRAMO: ENTRE AV. JOSÉ MA. CHÁVEZ Y AV. HÉROE DE NACOZARI, AGUASCALIENTES Mpio.**

Contratista: **JLJ CONSTRUCCIONES, S.A. DE C.V. (627)**

No.	Concepto	Unidad	Cantidad	Precio Unitario	Importe Total
	GRUPO: **OBRA COMPLEMENTARIA Y SEÑALIZACION**				
	PARTIDA: **SEÑALIZACION HORIZONTAL**				
22	SUMINISTRO Y APLICACIÓN DE PINTURA BASE SOLVENTE " EN RAYA SEPARADORA CLASIFICACIÓN M - 1.2, DISCONTINUA SENCILLA, DE DIVISIÓN DE CARRILES PARA VELOCIDADES MENORES A 60 KM/HR DE FRENTE EN PISO, DESARROLLO DE 2.50 ML X 0.10 MTS DE ANCHO, CON UNA SEPARACIÓN DE 5.00 MTS ENTRE SI PROMEDIO, A BASE DE PINTURA PARA TRAFICO COLOR BLANCO CON MICRO ESFERA SEGÚN NORMA SCT, INCLUYE: MATERIALES Y ESPECIFICACIONES QUE CUMPLAN CON LA NORMATIVA N-CMT-5-01-001/05, N-PRY-CAR-10-01-002/13 APLICADAS AL DIA DE HOY, MATERIAL, TRAZO, ENMASCARILLADO, MANO DE OBRA, LIMPIEZA PREVIA DE SUPERFICIE, EQUIPO NECESARIO PARA SU EJECUCIÓN, Y TODO LO NECESARIO PARA SU CORRECTA EJECUCIÓN, TRABAJO TERMINADO.	ML	645	$23.81	$15,357.45
25	SUMINISTRO Y APLICACIÓN DE PINTURA BASE SOLVENTE " EN RAYA SEPARADORA CLASIFICACIÓN M - 3.3, CONTINUA IZQUIERDA, PARA VIALIDADES URBANAS DE FRENTE EN PISO, SEPARADA 15 CM. DE LA GUARNICION, A BASE DE PINTURA PARA TRAFICO COLOR BLANCO CON MICRO ESFERA SEGÚN NORMA SCT, INCLUYE: MATERIALES Y ESPECIFICACIONES QUE CUMPLAN CON LA NORMATIVA N-CMT-5-01-001/05, N-PRY-CAR-10-01-002/13 APLICADAS AL DIA DE HOY, MATERIAL, TRAZO, ENMASCARILLADO, MANO DE OBRA, LIMPIEZA PREVIA DE SUPERFICIE, EQUIPO NECESARIO PARA SU EJECUCIÓN, Y TODO LO NECESARIO PARA SU CORRECTA EJECUCIÓN, TRABAJO TERMINADO.	ML	946.32	$31.83	$30,121.37
27	SUMINISTRO Y APLICACIÓN DE PINTURA BASE SOLVENTE " EN RAYA CANALIZADORA CLASIFICACIÓN M - 5, PARA INDICAR ENTRADA Y SALIDA EN BIFURCACIONES, COLOR BLANCO, REFLEJANTE CON MICRO ESFERA DE VIDRIO EN PROPORCIÓN SEGÚN NORMA SCT DE 0.20 MTS DE ANCHO DE LONGITUD Y TRAZO VARIABLE (SEGUN PROYECTO), INCLUYE: MATERIALES Y ESPECIFICACIONES QUE CUMPLAN CON LA NORMATIVA N-CMT-5-01-001/05, N-PRY-CAR-10-01-002/13 APLICADAS AL DIA DE HOY, MATERIAL, TRAZO, ENMASCARILLADO, MANO DE OBRA, LIMPIEZA PREVIA DE SUPERFICIE, EQUIPO NECESARIO PARA SU EJECUCIÓN, Y TODO LO NECESARIO PARA SU CORRECTA EJECUCIÓN, TRABAJO TERMINADO.	ML	70.5	$47.61	$3,356.51
28	SUMINISTRO Y APLICACIÓN DE PINTURA BASE SOLVENTE " EN RAYA DE ALTO CLASIFICACIÓN M - 6, PARA INDICAR ALTO EN CRUCEROS, COLOR BLANCO, REFLEJANTE CON MICRO ESFERA DE VIDRIO EN PROPORCIÓN SEGÚN NORMA SCT DE 0.60 MTS DE ANCHO DE LONGITUD VARIABLE, INCLUYE: MATERIALES Y ESPECIFICACIONES QUE CUMPLAN CON LA NORMATIVA N-CMT-5-01-001/05, N-PRY-CAR-10-01-002/13 APLICADAS AL DIA DE HOY, MATERIAL, TRAZO, ENMASCARILLADO, MANO DE OBRA, LIMPIEZA PREVIA DE SUPERFICIE, EQUIPO NECESARIO PARA SU EJECUCIÓN, Y TODO LO NECESARIO PARA SU CORRECTA EJECUCIÓN, TRABAJO TERMINADO.	ML	65.1	$142.85	$9,299.53
29	SUMINISTRO Y APLICACIÓN DE PINTURA BASE SOLVENTE " EN RAYA PARA CRUCE PEATONAL CLASIFICACIÓN M - 7.1, PARA INDICAR " CRUCE PEATONAL EN VIAS PRIMARIAS", COLOR AMARILLO, REFLEJANTE CON MICRO ESFERA DE VIDRIO EN PROPORCIÓN SEGÚN NORMA SCT DE 0.40 MTS DE ANCHO Y 3.5 MTS. DE LONGITUD POR EL ANCHO DE LA VIALIDAD, CON UNA SEPARACIÓN DE 0.40 MTS. ENTRE ELLAS, INCLUYE: MATERIALES Y ESPECIFICACIONES QUE CUMPLAN CON LA NORMATIVA N-CMT-5-01-001/05, N-PRY-CAR-10-01-002/13 APLICADAS AL DIA DE HOY, MATERIAL, TRAZO, ENMASCARILLADO, MANO DE OBRA, LIMPIEZA PREVIA DE SUPERFICIE, EQUIPO NECESARIO PARA SU EJECUCIÓN, Y TODO LO NECESARIO PARA SU CORRECTA EJECUCIÓN, TRABAJO TERMINADO.	M2	459.54	$161.41	$74,174.35

Obra: **OBRA COMPLEMENTARIA Y SEÑALIZACIÓN AV. CONVENCIÓN 1914 SUR (CALZADA SUR)**

Ubicación: **TRAMO: ENTRE AV. JOSÉ MA. CHÁVEZ Y AV. HÉROE DE NACOZARI, AGUASCALIENTES Mpio.**

Contratista: **JLJ CONSTRUCCIONES, S.A. DE C.V. (627)**

No.	Concepto	Unidad	Cantidad	Precio Unitario	Importe Total
	GRUPO: **OBRA COMPLEMENTARIA Y SEÑALIZACION**				
	PARTIDA: **SEÑALIZACION HORIZONTAL**				
30	SUMINISTRO Y APLICACIÓN DE PINTURA BASE SOLVENTE " EN FLECHAS CLASIFICACIÓN M - 11.1, "FLECHA SENCILLA" PARA INDICAR SENTIDO DE CIRCULACIÓN , EN VIALIDADES PARA VELOCIDAD MENOR A 60KM POR HORA DIFERENTES DIMENSIONES (VER PLANO DE SEÑALAMIENTOS) COLOR BLANCO, REFLEJANTE CON MICRO ESFERA DE VIDRIO EN PROPORCIÓN SEGÚN NORMA SCT, INCLUYE: MATERIALES Y ESPECIFICACIONES QUE CUMPLAN CON LA NORMATIVA N-CMT-5-01-001/05, N-PRY-CAR-10-01-002/13 APLICADAS AL DIA DE HOY, MATERIAL, TRAZO, ENMASCARILLADO, MANO DE OBRA, LIMPIEZA PREVIA DE SUPERFICIE, EQUIPO NECESARIO PARA SU EJECUCIÓN, Y TODO LO NECESARIO PARA SU CORRECTA EJECUCIÓN, TRABAJO TERMINADO.	PZA	41	$179.69	$7,367.29
31	SUMINISTRO Y APLICACIÓN DE PINTURA BASE SOLVENTE " EN FLECHAS CLASIFICACIÓN M - 11.1, " FLECHA CABEZA DOBLE" PARA INDICAR SENTIDO DE CIRCULACIÓN (VUELTA IZQUIERDA O DERECHA) , EN VIALIDADES PARA VELOCIDAD MENOR A 60KM POR HORA DIFERENTES DIMENSIONES (VER PLANO DE SEÑALAMIENTOS) COLOR BLANCO, REFLEJANTE CON MICRO ESFERA DE VIDRIO EN PROPORCIÓN SEGÚN NORMA SCT, INCLUYE: MATERIALES Y ESPECIFICACIONES QUE CUMPLAN CON LA NORMATIVA N-CMT-5-01-001/05, N-PRY-CAR-10-01-002/13 APLICADAS AL DIA DE HOY, MATERIAL, TRAZO, ENMASCARILLADO, MANO DE OBRA, LIMPIEZA PREVIA DE SUPERFICIE, EQUIPO NECESARIO PARA SU EJECUCIÓN, Y TODO LO NECESARIO PARA SU CORRECTA EJECUCIÓN, TRABAJO TERMINADO.	PZA	1	$207.67	$207.67
32	SUMINISTRO Y APLICACIÓN DE PINTURA BASE SOLVENTE " EN LETRAS Y NUMEROS CLASIFICACIÓN M - 11.1 "LETRAS Y NUMEROS" EN VIALIDADES PARA VELOCIDAD MENOR A 60KM POR HORA DIFERENTES DIMENSIONES (VER PLANO DE SEÑALAMIENTOS) COLOR BLANCO, REFLEJANTE CON MICRO ESFERA DE VIDRIO EN PROPORCIÓN SEGÚN NORMA SCT DE (VER DETALLES EN PLANOS) INCLUYE: MATERIALES Y ESPECIFICACIONES QUE CUMPLAN CON LA NORMATIVA N-CMT-5-01-001/05, N-PRY-CAR-10-01-002/13 APLICADAS AL DIA DE HOY, MATERIAL, TRAZO, ENMASCARILLADO, MANO DE OBRA, LIMPIEZA PREVIA DE SUPERFICIE, EQUIPO NECESARIO PARA SU EJECUCIÓN, Y TODO LO NECESARIO PARA SU CORRECTA EJECUCIÓN, TRABAJO TERMINADO.	PZA	172	$241.18	$41,482.96
33	SUMINISTRO Y APLICACIÓN DE PINTURA BASE SOLVENTE " EN LETRAS Y NUMEROS CLASIFICACIÓN M - 11.2 "FLECHA SIN CUERPO" PARA ESTABLECER LUGARES DE PARADA, (VER PLANO DE SEÑALAMIENTOS) COLOR BLANCO, REFLEJANTE CON MICRO ESFERA DE VIDRIO EN PROPORCIÓN SEGÚN NORMA SCT DE (VER DETALLES EN PLANOS) INCLUYE: MATERIALES Y ESPECIFICACIONES QUE CUMPLAN CON LA NORMATIVA N-CMT-5-01-001/05, N-PRY-CAR-10-01-002/13 APLICADAS AL DIA DE HOY, MATERIAL, TRAZO, ENMASCARILLADO, MANO DE OBRA, LIMPIEZA PREVIA DE SUPERFICIE, EQUIPO NECESARIO PARA SU EJECUCIÓN, Y TODO LO NECESARIO PARA SU CORRECTA EJECUCIÓN, TRABAJO TERMINADO.	PZA	9	$306.31	$2,756.79
34	SUMINISTRO Y APLICACIÓN DE PINTURA BASE SOLVENTE " EN LETRAS Y NUMEROS CLASIFICACIÓN M - 11.2 "LEYENDA SOLO BUS" PARA VELOCIDAD MENOR A 60KM POR HORA DIFERENTES DIMENSIONES (VER PLANO DE SEÑALAMIENTOS) COLOR BLANCO, REFLEJANTE CON MICRO ESFERA DE VIDRIO EN PROPORCIÓN SEGÚN NORMA SCT DE (VER DETALLES EN PLANOS) INCLUYE: MATERIALES Y ESPECIFICACIONES QUE CUMPLAN CON LA NORMATIVA N-CMT-5-01-001/05, N-PRY-CAR-10-01-002/13 APLICADAS AL DIA DE HOY, MATERIAL, TRAZO, ENMASCARILLADO, MANO DE OBRA, LIMPIEZA PREVIA DE SUPERFICIE, EQUIPO NECESARIO PARA SU EJECUCIÓN, Y TODO LO NECESARIO PARA SU CORRECTA EJECUCIÓN, TRABAJO TERMINADO.	PZA	3	$1,152.37	$3,457.11

Obra: **OBRA COMPLEMENTARIA Y SEÑALIZACIÓN AV. CONVENCIÓN 1914 SUR (CALZADA SUR)**

Ubicación: **TRAMO: ENTRE AV. JOSÉ MA. CHÁVEZ Y AV. HÉROE DE NACOZARI, AGUASCALIENTES Mpio.**

Contratista: **JLJ CONSTRUCCIONES, S.A. DE C.V. (627)**

No.	Concepto	Unidad	Cantidad	Precio Unitario	Importe Total
	GRUPO: **OBRA COMPLEMENTARIA Y SEÑALIZACION**				
	PARTIDA: **SEÑALIZACION HORIZONTAL**				
35	SUMINISTRO Y APLICACIÓN DE PINTURA BASE SOLVENTE " EN LETRAS Y NUMEROS CLASIFICACIÓN M - 11.4 "L INVERTIDA" PARA ESTABLECER LUGAR DE PARADA CUYO LADO MAYOR EN UNA LÍNEA DE 20 CM DE ANCHO POR 20 MTS DE LARGO Y SU LADO MENOR EN UNA LÍNEA DE 50 CM DE ANCHO POR EL ANCHO DEL CARRIL, SOBRE PAVIMENTO EN VIALIDADES PARA VELOCIDAD MENOR A 60KM POR HORA DIFERENTES DIMENSIONES (VER PLANO DE SEÑALAMIENTOS) COLOR BLANCO, REFLEJANTE CON MICRO ESFERA DE VIDRIO EN PROPORCIÓN SEGÚN NORMA SCT DE (VER DETALLES EN PLANOS) INCLUYE: MATERIALES Y ESPECIFICACIONES QUE CUMPLAN CON LA NORMATIVA N-CMT-5-01-001/05, N-PRY-CAR-10-01-002/13 APLICADAS AL DIA DE HOY, MATERIAL, TRAZO, ENMASCARILLADO, MANO DE OBRA, LIMPIEZA PREVIA DE SUPERFICIE, EQUIPO NECESARIO PARA SU EJECUCIÓN, Y TODO LO NECESARIO PARA SU CORRECTA EJECUCIÓN, TRABAJO TERMINADO.	PZA	3	$271.78	$815.34
36	SUMINISTRO Y COLOCACIÓN DE VIALETA STANDARD (S-200) DE 10X10CM. COLOR: CUERPO AMARILLO Y/O BLANCO Y REFLEJANTE AMARILLO 1 CARA MARCA SEA O SIMILAR EN CALIDAD Y ESPECIFICACIONES DE FICHA TÉCNICA, FIJADO EN PAVIMENTO CON SISTEMA DE SUJECIÓN DE ALTO AGARRE PEGAMENTO EPOXICO 100 A/B (RESINA EPÓXICA/RESINA POLIAMIDA MODIFICADA), RESISTENTE A ALTA TEMPERATURA (VER PLANO DE DETALLES DE SEÑALAMIENTOS HORIZONTAL), INCLUYE: LIMPIEZA PREVIA Y FINAL DE LA SUPERFICIE, PREPARACIÓN DE LA SUPERFICIE, TRAZO, ALINEACIÓN, Y TODO LO NECESARIO PARA SU CORRECTA EJECUCIÓN, TRABAJO TERMINADO.	PZA	821	$92.95	$76,311.95
37	SUMINISTRO Y COLOCACION DE VIALETA SOLAR DE 10X10CM. COLOR: CUERPO ALUMINIO 3 LED DOS CARAS REFLEJANTES MARCA CREATIVAL VT-29 O SIMILAR EN CALIDAD Y ESPECIFICACIONES DE FICHA TÉCNICA, FIJADO EN PAVIMENTO CON SISTEMA DE SUJECIÓN DE ALTO AGARRE PEGAMENTO EPOXICO 100 A/B (RESINA EPÓXICA/RESINA POLIAMIDA MODIFICADA), RESISTENTE A ALTA TEMPERATURA (VER PLANO DE DETALLES DE SEÑALAMIENTOS HORIZONTAL), INCLUYE: LIMPIEZA PREVIA Y FINAL DE LA SUPERFICIE+C92, PREPARACIÓN DE LA SUPERFICIE, TRAZO, ALINEACIÓN, Y TODO LO NECESARIO PARA SU CORRECTA EJECUCIÓN, TRABAJO TERMINADO.	PZA	210	$840.09	$176,418.90
38	SUMINISTRO Y COLOCACIÓN DE BOYA DE PLÁSTICO OJO DE GATO (VT-38). MARCA CREATIVIAL O SIMILAR EN CALIDAD, CON REFLEJANTE COLOR BLANCO GRADO ALTA INTENSIDAD. FIJACIÓN A SUPERFICIE asfaltica CON CLAVOS DE ACERO DE ALTA RESISTENCIA. INCLUYE: MATERIAL, MANO DE OBRA, HERRAMIENTA, ELEMENTOS DE FIJACIÓN, ALINEADO, LIMPIEZAS Y TODO LO NECESARIO PARA SU CORRECTA EJECUCIÓN. TRABAJO TERMINADO.	PZA	52	$340.59	$17,710.68
				Totales por Partida	**$568,851.07**

Obra: **OBRA COMPLEMENTARIA Y SEÑALIZACIÓN AV. CONVENCIÓN 1914 SUR (CALZADA SUR)**

Ubicación: **TRAMO: ENTRE AV. JOSÉ MA. CHÁVEZ Y AV. HÉROE DE NACOZARI, AGUASCALIENTES Mpio.**

Contratista: **JLJ CONSTRUCCIONES, S.A. DE C.V. (627)**

No.	Concepto	Unidad	Cantidad	Precio Unitario	Importe Total
	GRUPO: **OBRA COMPLEMENTARIA Y SEÑALIZACION**				
	PARTIDA: **SEÑALIZACION VERTICAL**				
39	SUMINISTRO Y COLOCACIÓN DE SEÑALAMIENTO VERTICAL DE RESTRICCIÓN SR-9 "VELOCIDAD PERMITIDA 50KM /HR" DISEÑO NORMATIVO SCT, HECHO A BASE DE LAMINA GALVANIZADA (CON CEJA) 72 cm x 72 cm CALIBRE 16 CON TERMINADO GRADO DE INGENIERÍA EN SU TOTALIDAD, EL COLOR SERA REFLEJANTE GRADO INGENIERÍA Y SÍMBOLO EN COLOR REFLEJANTE , TODOS LOS COLORES RESISTENTES A LA INTEMPERIE, FIJADA MEDIANTE BARRENADO Y TORNILLOS DE 2 1/2" x 5/16" A UN POSTE DE PTR O DE 2"x2" CALIBRE 14 EN ACABADO GALVANIZADO Y CON ALTURA DE 2.50 m AL NIVEL DE LA BANQUETA A LA PARTE INFERIOR DE LA LAMINA MAS EL EXCEDENTE REQUERIDO PARA FIJAR LAS LAMINAS Y ANCLADO DE 50 cm DE PROFUNDIDAD CON ANGULO TRANSVERSAL DE 1" x 1" DE 25 cm EN DADO DE CONCRETO F'C=150kg/cm2 DE 30 cm POR LADO (VER PLANO DE DETALLES CRITERIOS DE ANCLAJE DE SEÑALAMIENTO VERTICAL DETALLE SEÑ-02 Y SEÑ-03). MCA. SEA O SIMILAR EN CALIDAD Y ESPECIFICACIONES, INCLUYE: MATERIALES Y ESPECIFICACIONES QUE CUMPLAN CON LA NORMATIVA N-CMT-5-02-002/05 Y N-PRY-CAR-10-01-008/13 APLICADAS AL DIA DE HOY MANO DE OBRA, EXCAVACIONES, Y/O DEMOLICIONES, PREPARACIONES, ANCLADO, NIVELADO, COLADO, FLETES, MANIOBRAS LIMPIEZA Y CARGA Y ACARREOS, RETIRO DE SOBRANTES FUERA DE LA OBRA HASTA TIRADERO OFICIAL, LIMPIEZAS, TRABAJO TERMINADO.	PZA	2	$3,648.84	$7,297.68
				Totales por Partida	**$7,297.68**
				Totales por Grupo	**$774,105.35**

Obra: **OBRA COMPLEMENTARIA Y SEÑALIZACIÓN AV. CONVENCIÓN 1914 SUR (CALZADA SUR)**

Ubicación: **TRAMO: ENTRE AV. JOSÉ MA. CHÁVEZ Y AV. HÉROE DE NACOZARI, AGUASCALIENTES Mpio.**

Contratista: **JLJ CONSTRUCCIONES, S.A. DE C.V. (627)**

No.	Concepto	Unidad	Cantidad	Precio Unitario	Importe Total
	GRUPO: **EXTRAORDINARIO**				
	PARTIDA: **EXTRAORDINARIO**				
46	REHABILITACION DE CAIMAN (PARTES SUPERIOR) SECCION DE 6.00 X 0.70 MTS, INCLUYE: COLOCACION DE VIGAS IPS FALTANTES, HABILITACION DE PASO HOMBRE, TIRAS DE SOLERA SUFICIENTE PARA MEJOR SUJECION ENTRE TODAS LAS VIGAS SOLDADAS TRANSVERSALMENTE, TRABAJOS DE TALLER PAR AAJUSTES, PLOMEADO, NIVELADO, CARGAS Y ACARREOS DENTRO DE LA OBRA, LIMPIEZA PREVIA FINAL Y TODO LO NECESARIOS PARA SU CORRECTA EJECUCION DEL CONCEPTO.	PZA	1	$14,619.94	$14,619.94
47	REHABILITACION DE CAIMAN (PARTE SUPERIOR) SECCION DE 3.7 X 1.7 MTS, INCLUYE: COLOCACION DE VIGAS IPS FALTANTES, TRABAJOS DE TALLER PARA AJUSTES, PLOMEADO, NIVELADO, CARGAS Y ACARREOS DENTRO DE LA OBRA, LIMPIEZA PREVIA, FINAL Y TODO LO NECESARIOS PARA SU CORRECTA EJECUCION DEL CONCEPTO.	PZA	1	$8,480.68	$8,480.68
48	DEDUCTIVA POR CONCEPTO DE INDIRECTOS NO COMPROBADOS	LOTE	-4.71954	$1,000.00	-$4,719.54

Totales por Partida		**$18,381.08**
Totales por Grupo		**$18,381.08**
Totales Presup.		**$792,486.43**
Anticipo	**+**	**$237,745.93**
Amortizac. Ant.	**-**	**$237,745.93**
SubTotal. Ant.	**=**	**$792,486.43**
IVA	**+**	**$126,797.83**
Total	**=**	**$919,284.26**

H. AYUNTAMIENTO CONSTITUCIONAL DEL MUNICIPIO DE AGUASCALIENTES 2021-2024

PRESUPUESTO MODIFICADO

Aguascalientes

Obra: **OBRA COMPLEMENTARIA Y SEÑALIZACIÓN AV. CONVENCIÓN 1914 SUR (CALZADA SUR)**

Ubicación: **TRAMO: ENTRE AV. JOSÉ MA. CHÁVEZ Y AV. HÉROE DE NACOZARI, AGUASCALIENTES Mpio.**

Contratista: **JLJ CONSTRUCCIONES, S.A. DE C.V. (627)**

Grupo	Partida		Importe
OBRA COMPLEMENTARIA Y SEÑALIZACION			
	PRELIMINARES		$4,086.14
	OBRA COMPLEMENTARIA		$193,348.79
	LIMPIEZAS		$521.67
	SEÑALIZACION HORIZONTAL		$568,851.07
	SEÑALIZACION VERTICAL		$7,297.68
		Subtotal por Grupo	**$774,105.35**
EXTRAORDINARIO			
	EXTRAORDINARIO		$18,381.08
		Subtotal por Grupo	**$18,381.08**
		Totales Presup.	**$792,486.43**
		Anticipo +	**$237,745.93**
		Amortizac. Ant. -	**$237,745.93**
		SubTotal. Ant. =	**$792,486.43**
		IVA +	**$126,797.83**
		Total =	**$919,284.26**

MUNICIPIO DE AGUASCALIENTES

SECRETARIA DE OBRA PUBLICAS MUNICIPALES

DIRECCION DE COSTOS Y LICITACION DE OBRA

CONTRATO: DM-0054-2022

OBRA: OBRA COMPLEMENTARIA Y SEÑALIZACIÓN AV. CONVENCIÓN 1914 SUR (CALZADA SUR), TRAMO: ENTRE AV. JOSÉ MA. CHÁVEZ Y AV. HÉROE DE NACOZARI, AGUASCALIENTES Mpio.

MONTO MODIFICADO FINAL: $919,284.26

VOLUMEN	UNIDAD	COMPONENTE DE OBRA	MONTO	PU
6.19	M3	LIMPIA, CORTE CON DISCO, DEMOLICION, CARGA Y ACARREO	$ 4,086.14	$ 660.12
11.00	PZAS	RENIVELACIONES DE TAPAS DE INFRAESTRUCTURA EXISTENTE (POZOS, CAJAS DE VALVULAS, REGISTROS DE VOZ	$ 211,729.87	$ 19,248.17
28.29	M2	LIMPIEZAS GENERAL DE OBRA A DETALLE Y DESASOLVE DE POZOS DE VISITA EN LINEAS DE ALCANTARILLADO	$ 521.67	$ 18.44
5342.69	ML	SEÑALIZACION HORIZONTAL Y VERTICAL SEGÚN NORMA SCT	$ 576,148.75	$ 107.84
			$ 792,486.43	


H. AYUNTAMIENTO DE AGUASCALIENTES
SECRETARÍA DE OBRAS PÚBLICAS
DIRECCIÓN DE SUPERVISIÓN DE OBRA


Aguascalientes
LA CIUDAD DE TU VIDA


MEMORIA FOTOGRAFICA

OBRA:	DM-0054-2022 - OBRA COMPLEMENTARIA Y SEÑALIZACIÓN AV. CONVENCIÓN 1914 SUR (CALZADA SUR)					
NO. DE CONTRATO:	DM-0054-2022		CONTRATISTA:	JLJ CONSTRUCCIONES, S.A. DE C.V.		

INICIO.

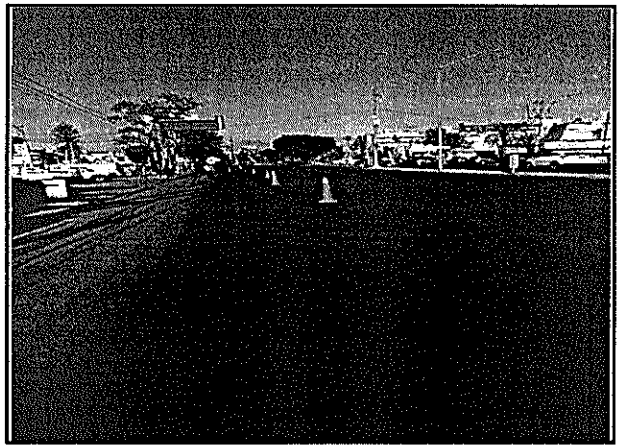

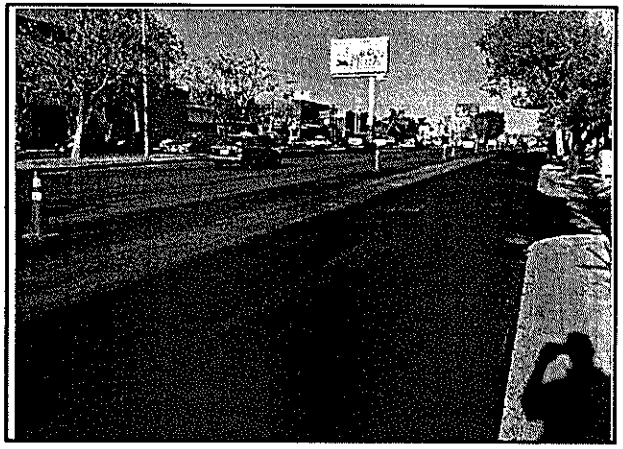

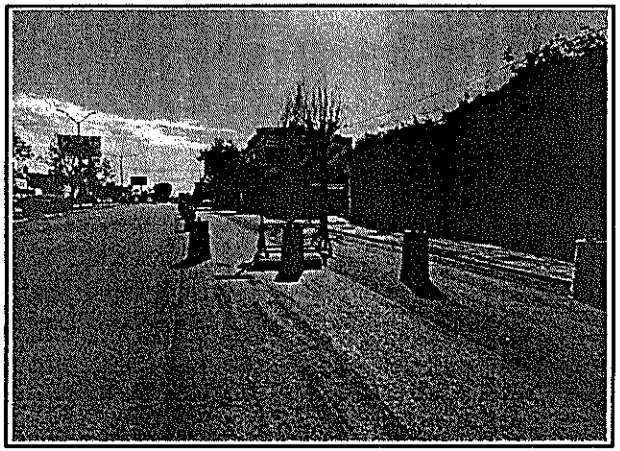



ING. RICARDO MACÍAS MERCADO
SUPERVISOR DE OBRA.


SECRETARÍA DE OBRAS PÚBLICAS
DIRECCIÓN DE SUPERVISIÓN DE OBRA

Aguascalientes
LA CIUDAD DE TU VIDA

MEMORIA FOTOGRAFICA

OBRA:	DM-0054-2022 - OBRA COMPLEMENTAR.A Y SEÑALIZACIÓN AV. CONVENCIÓN 1914 SUR (CALZADA SUR)					
NO. DE CONTRATO:	DM-0054-2022		CONTRATISTA:	JLJ CONSTRUCCIONES, S.A. DE C.V.		

PROCESO

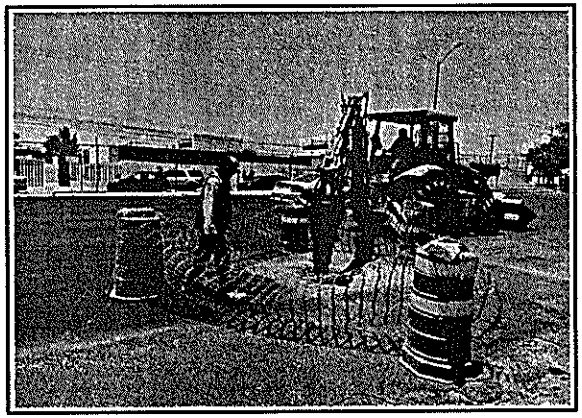







ING. RICARDO MACÍAS MERCADO
SUPERVISOR DE OBRA.

H. AYUNTAMIENTO DE AGUASCALIENTES

SECRETARÍA DE OBRAS PÚBLICAS


DIRECCIÓN DE SUPERVISIÓN DE OBRA

Aguascalientes
LA CIUDAD DE TU VIDA


MEMORIA FOTOGRAFICA


OBRA:	DM-0054-2022 - OBRA COMPLEMENTARIA Y SEÑALIZACIÓN AV. CONVENCIÓN 1914 SUR (CALZADA SUR)					
NO. DE CONTRATO:	DM-0054-2022		CONTRATISTA:	JLJ CONSTRUCCIONES, S.A. DE C.V.		

TERMINO

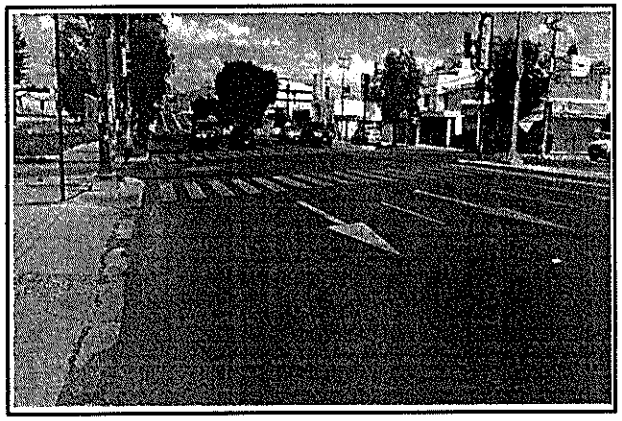




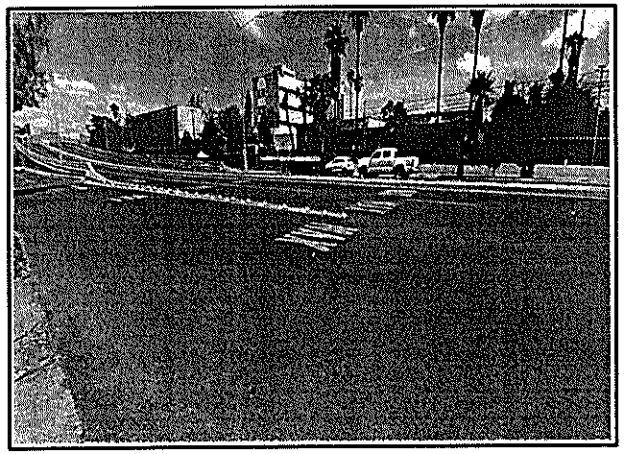


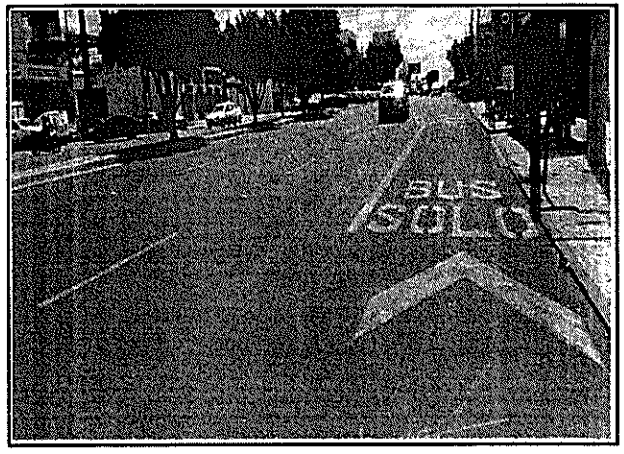

ING. RICARDO MACÍAS MERCADO
SUPERVISOR DE OBRA.

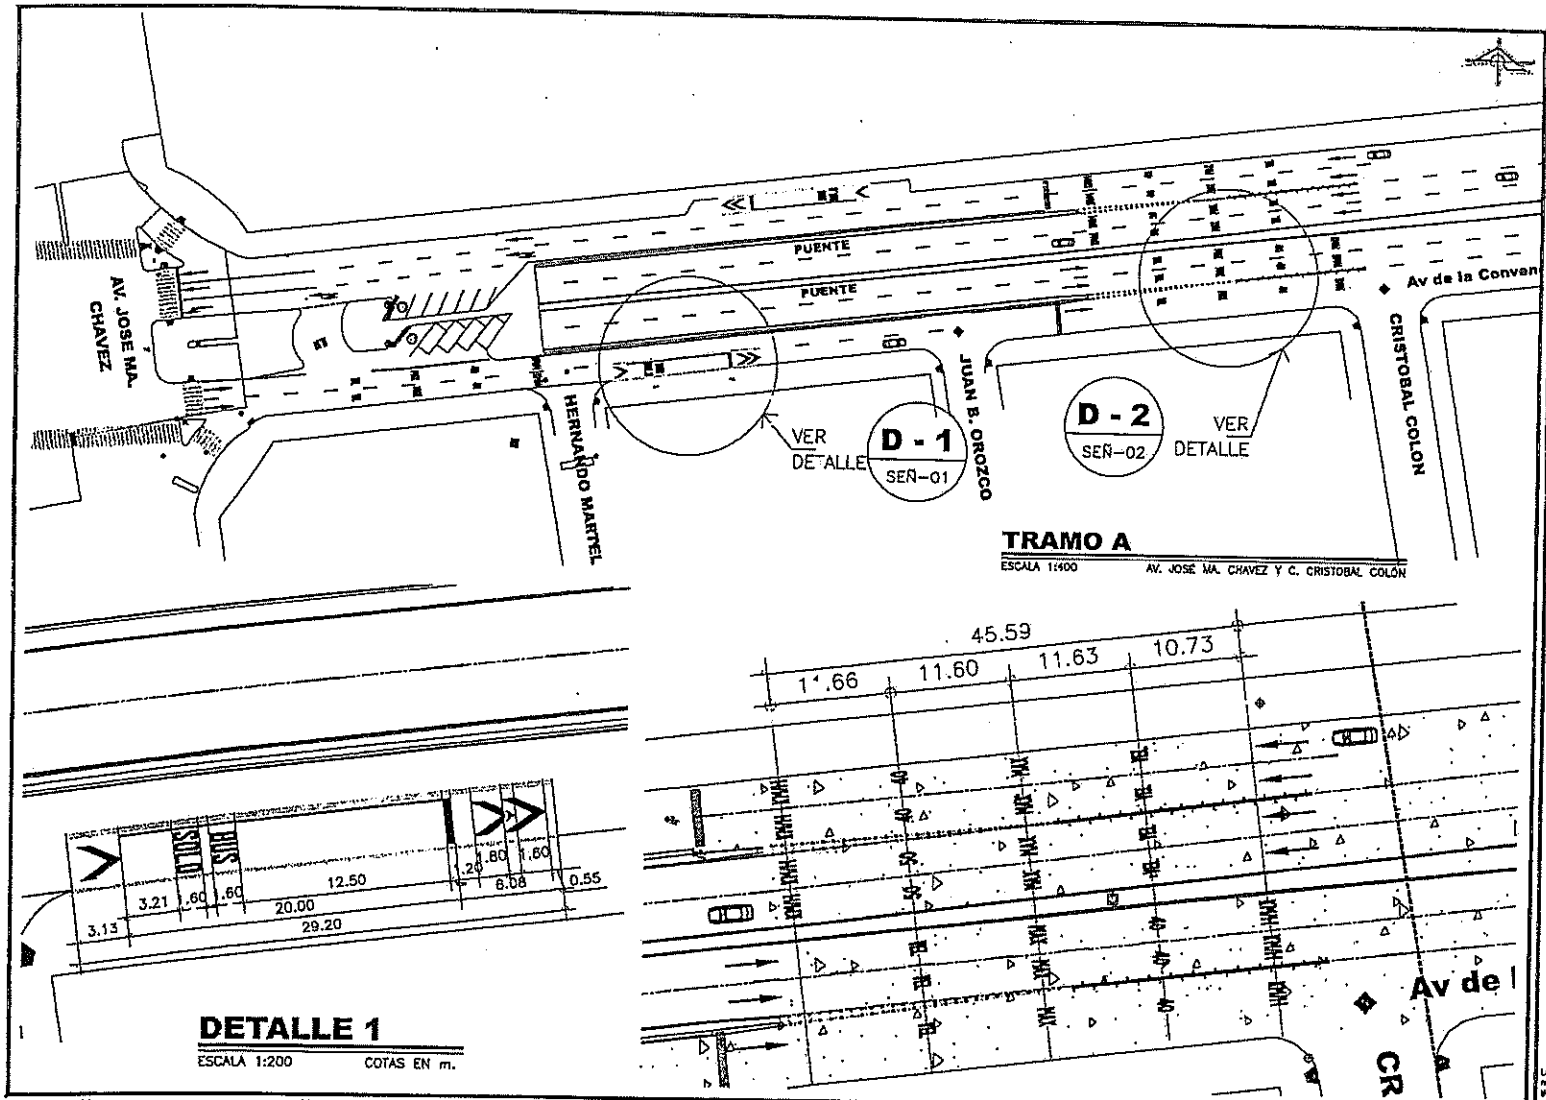

LOCALIZACIÓN:

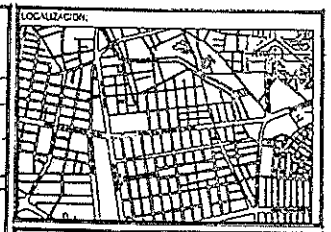

SIMBOLOGÍA

Nota1:

Se aplicará en todos los señalamientos horizontales pintura para tráfico base solvente tipo alquidal de secado rápido, que cumpla con las especificaciones n-cmt-5-01-001/05, n-pry-car-10-01-002/13 de la SCT aplicadas al día de hoy.

Nota 2:

Dosificación de micro esfera

La cantidad de esferas de vidrio en la película de pintura en húmedo, según su tipo, será la que se indica en la Tabla.

La Dirección de Planeación y Proyectos solo autoriza el proyecto ejecutivo, no se responsabiliza de la correcta ejecución de la obra. Este documento no tiene validez si no presenta las firmas de los responsables para su autorización, así como los sellos respectivos.

PRESIDENTE MUNICIPAL
M.P.P. Leonardo Montañez Castro
ENCARGADA DE DESPACHO DE LA SOPMA
Arq. Gloria Guadalupe Castillo González

REV	FECHA	OBSERVACIONES

RESP. DE PROY. EXTERNO		LOGO EXTERNO
CED. PROFESIONAL		
PROYECTÓ	REVISO	AUTORIZÓ

Dirección de Planeación y Proyectos de Obra | Secretaría de Obras Públicas

PROYECTISTA	COORDINADOR
ARQ. LAURA ALEJANDRA AGUAYO PÉREZ	ARQ. ALEJANDRO JAIME LEÓN
ARQ. LAURA ALEJANDRA GONZÁLEZ	DIRECTOR: M.en ARQ. JOSÉ LUIS IBÁÑEZ GARCÍA


PROYECTO
OBRA COMPLEMENTARIA Y SEÑALIZACIÓN AVENIDA DE LA CONVENCIÓN DE 1914 SUR

UBICACIÓN
AV. CONVENCIÓN DE 1914, AMBAS CALZADAS DE ENTRE AV. JOSÉ MARÍA CHÁVEZ Y CALLE CRISTÓBAL COLÓN

CONTENIDO
PLANO DE SEÑALIZACIÓN TRAMO 1 DETALLES 1, 2


CLAVE	No. PLANO
SEÑ 02	03
FECHA MARZO 2022	ESCALA INDICADA
ACOTACIÓN METROS	No. EXP. E-000-22

Aguascalientes
LA RIQUEZA DE TU VIDA

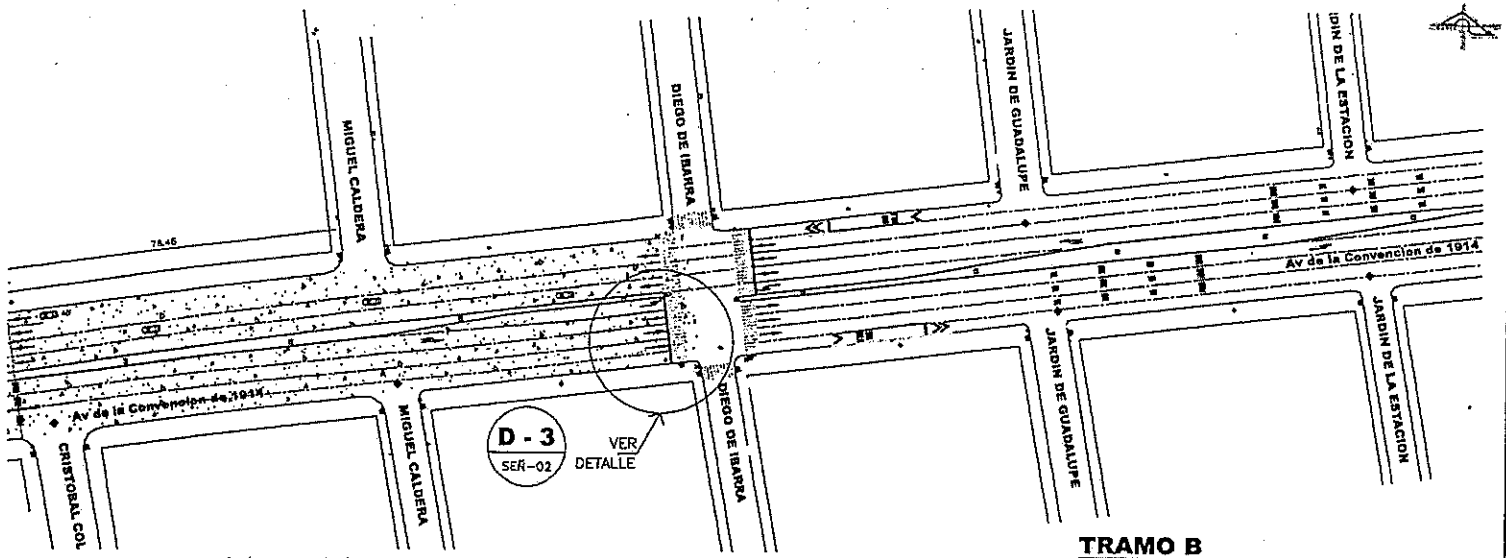

TRAMO B


ESCALA 1:500 C. CRISTOBAL COLÓN Y C. JARDÍN DE LA ESTACIÓN

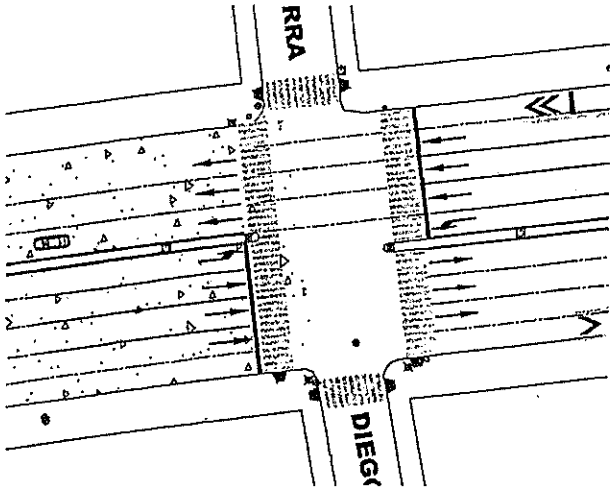

DETALLE 3

ESCALA 1:200 COTAS EN m.

LOCALIZACIÓN:

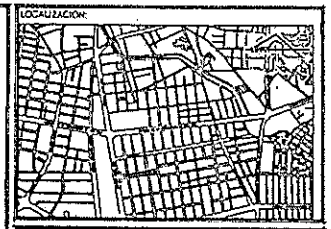

SIMBOLOGÍA

Nota1:

Se aplicará en todos los señalamientos horizontales pintura para trafico base solvente tipo alquidal de secado rápido, que cumpla con las especificaciones n-cmt-5-01-001/05, n-pry-car-10-01-002/13 de la SCT aplicadas al día de hoy.

Nota 2:

Dosificación de micro esfera

La cantidad de esferas de vidrio en la película de pintura en húmedo, según su tipo, será la que se indica en la Tabla

La Dirección de Planeación y Proyectos solo autoriza el proyecto ejecutivo, no es responsable de la correcta ejecución de la obra. Este documento no tiene validez si no presenta las firmas de los responsables para su autorización, así como los sellos respectivos.

PRESIDENTE MUNICIPAL
M.P.P. Leonardo Montañez Castro
ENCARGADA DE DESPACHO DE LA SOPMA
Arq. Gloria Guadalupe Castillo González

REV	FECHA	OBSERVACIONES

V. Bo. DE LA DEPENDENCIA

RESP. DE PROY. EXTERNO		LOGO EXTERNO
CED. PROFESIONAL		
PROYECTO	REVISO	AUTORIZÓ

Dirección de Planeación y Proyectos de Obra — Secretaría de Obras Públicas

PROYECTISTA	COORDINADOR
BLANCA ESTHER OURO PÉREZ	ARQ. ALEJANDRO JAIME LEAL
JEFE DE DEP.	DIRECTOR
ARQ. J. JESÚS PADILLA GONZÁLEZ	M. en ARQ. JOSÉ LUIS JIMÉNEZ GARCÍA


PROYECTO
OBRA COMPLEMENTARIA Y SEÑALIZACIÓN AV. DE LA CONVENCIÓN DE 1914 SUR

UBICACIÓN
AV. CONVENCIÓN DE 1914, AMBAS CALZADAS DE ENTRE CALLE CRISTOBAL COLÓN Y CALLE JARDÍN DE LA ESTACIÓN


CONTENIDO
PLANO DE SEÑALIZACIÓN TRAMO 2
DETALLE 3

CLAVE	No. PLANO
SEÑ 03	04
FECHA	ESCALA
MARZO 2022	INDICADA
ACOTACIÓN	No. EXP.
METROS	5.000.22

Aguascalientes
LA CIUDAD DE TU VIDA

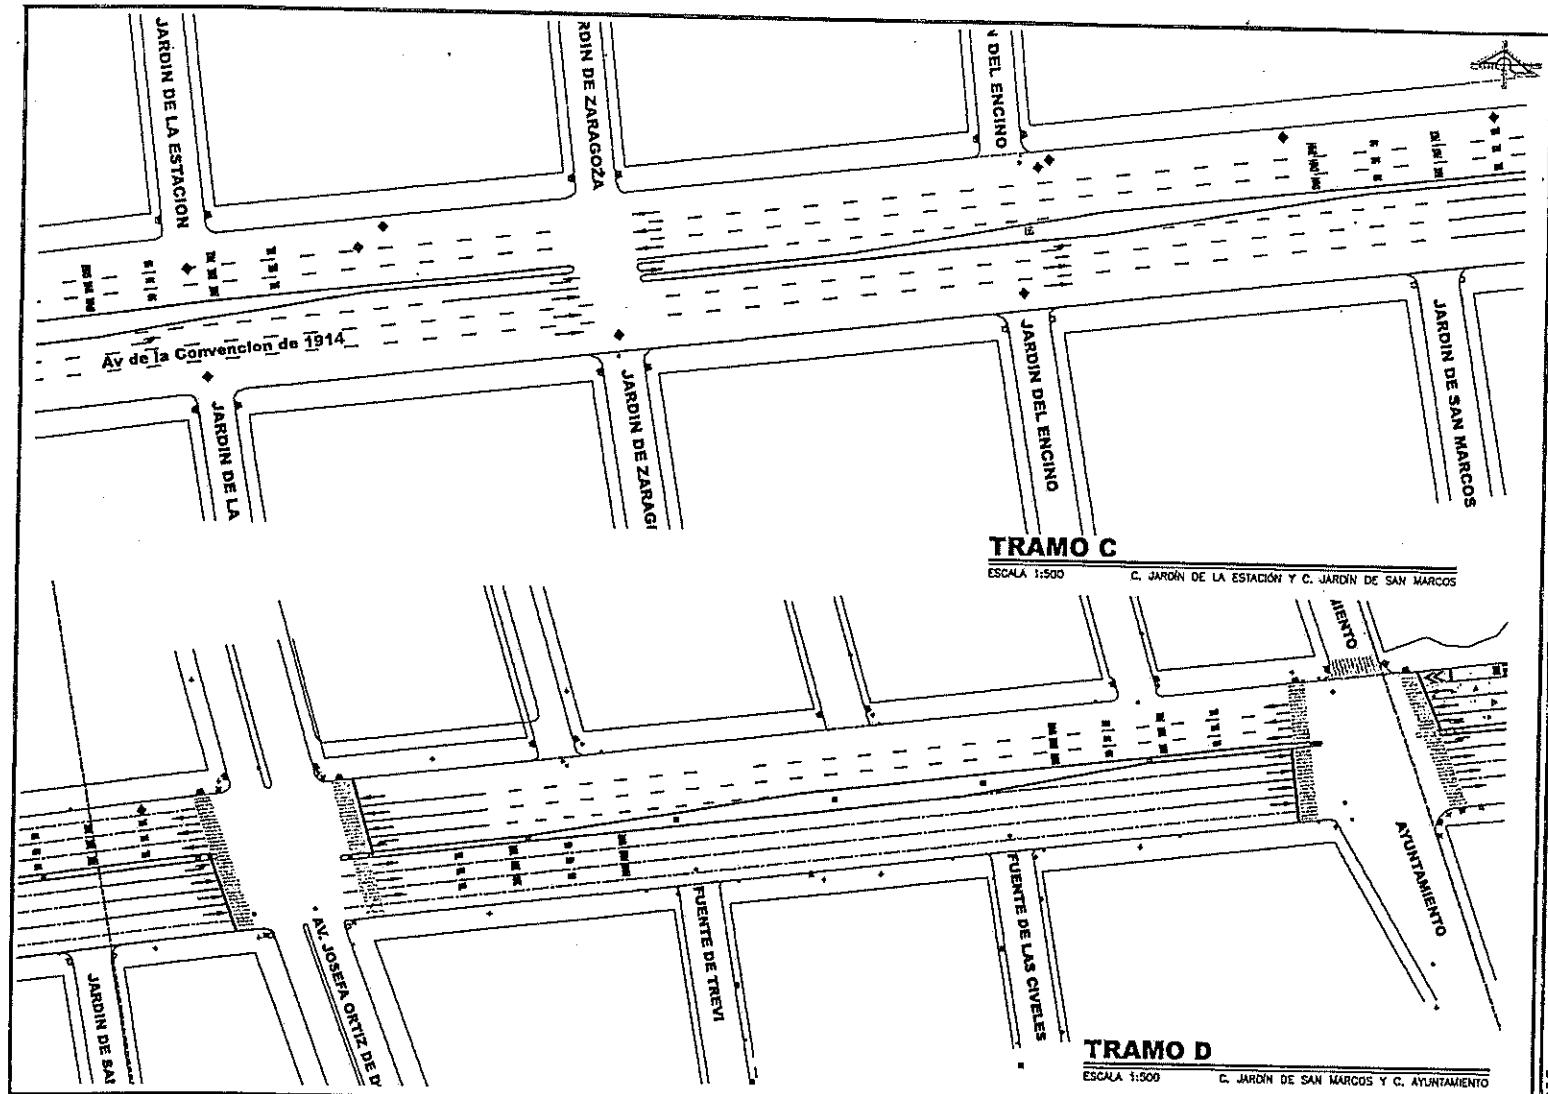

LOCALIZACION:

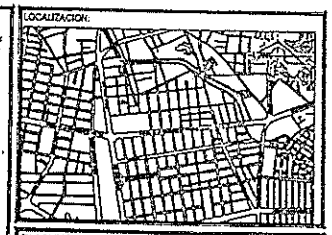

SIMBOLOGÍA

Nota1:

Se aplicará en todos los señalamientos horizontales pintura para trafico base solvente tipo alquidal de secado rápido, que cumpla con las especificaciones n-cmt-5-0*-001/05, n-pry-car-10-01-002/13 de la SCT aplicadas al día de hoy.

Nota 2:

Dosificación de micro esfera

La cantidad de esferas de vidrio en la película de pintura en húmedo, según su tipo, será la que se indica en la Tabla

La Dirección de Planeación y Proyectos solo autoriza el proyecto ejecutivo, no es responsable de la correcta ejecución de la obra. Este documento no tiene validez si no presenta las firmas de los responsables para su autorización, así como los sellos respectivos.

PRESIDENTE MUNICIPAL
M.P.P. Leonardo Montañez Castro
ENCARGADA DE DESPACHO DE LA SOPSMA
Arq. Gloria Guadalupe Castillo González

REV	FECHA	OBSERVACIONES

V°B° DE LA DEPENDENCIA

RESP. DE PROY. EXTERNO		LOGO EXTERNO
CED. PROFESIONAL		
PROYECTO	REVISO	AUTORIZO


Dirección de Planeación y Proyectos de Obra
Secretaría de Obras Públicas

PROYECTISTA	COORDINACIÓN
ARQ. LESSLIE ALBERTO PÉREZ	ARQ. ALEJANDRO JAIME LEAL
JEFE DE DEPTO.	DIRECTOR
ARQ. J. JESÚS PALAFOX GONZÁLEZ	M. en ARQ. JOSÉ LUIS JUÁREZ GARCÍA

PROYECTO	OBRA COMPLEMENTARIA Y SEÑALIZACIÓN AVENIDA DE LA CONVENCIÓN DE 1914 SUR
UBICACIÓN	AV. CONVENCIÓN DE 1914, AMBAS CALZADAS DE ENTRE CALLE JARDÍN DE LA ESTACIÓN Y CALLE AYUNTAMIENTO
CONTENIDO	PLANO DE SEÑALIZACIÓN TRAMO C/ PLANO DE SEÑALIZACIÓN TRAMO D

CLAVE	No. PLANO
SEÑ 04	05
FECHA MARZO 2022	ESCALA INDICADA
ACOTACIÓN METROS	No. EXP. IS-000-22

Aguascalientes
LA CIUDAD DE TU VIDA

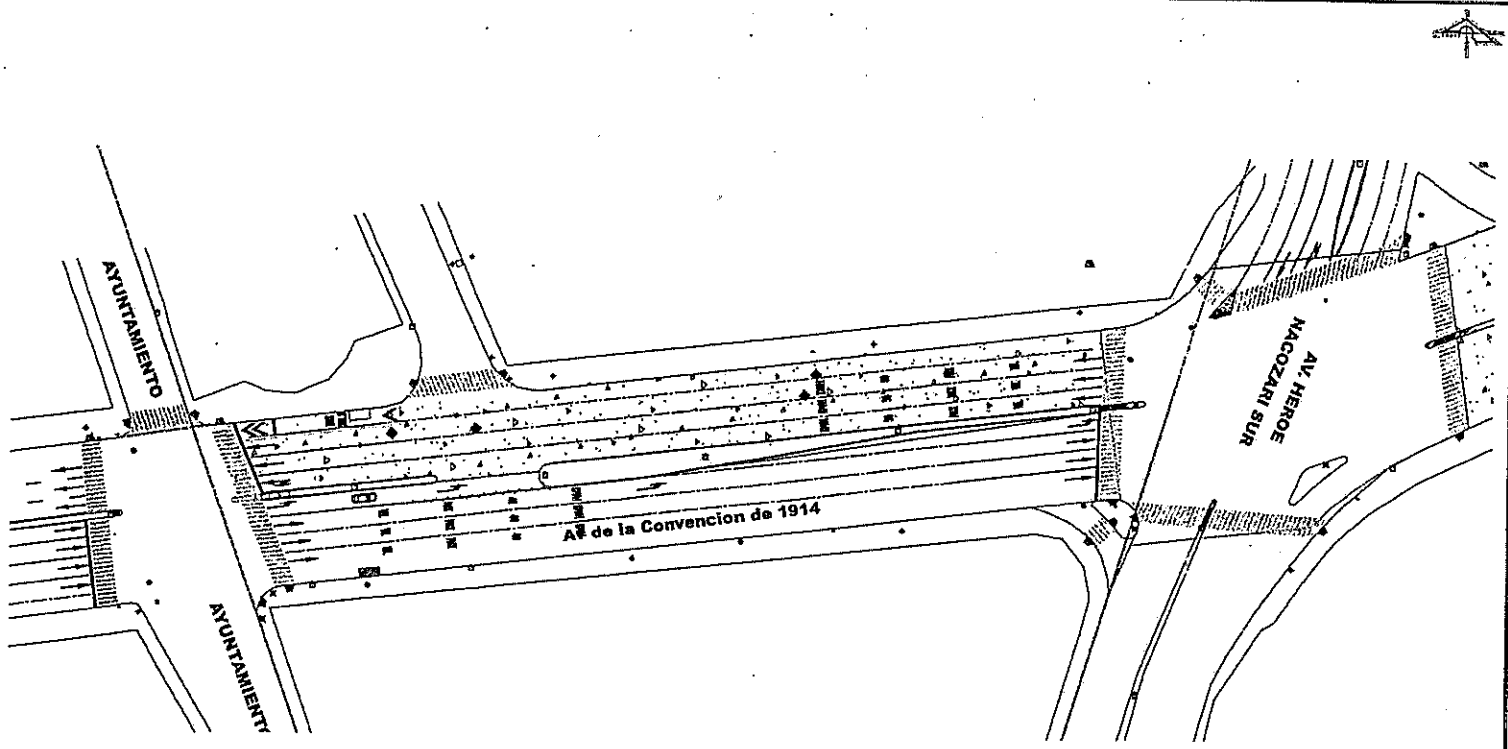

TRAMO E

ESCALA 1:500 C. AYUNTAMIENTO Y AV. HEROE DE NACOZARI

LOCALIZACIÓN



SIMBOLOGÍA

Nota1:

Se aplicará en todos los señalamientos horizontales pintura para trafico base solvente tipo alquidal de secado rápido, que cumpla con las especificaciones n-cmt-5-01-001/05, n-pry-car-10-01-002/13 de la SCT aplicadas al día de hoy.

Nota 2:

Dosificación de micro esfera

La cantidad de esferas de vidrio en la película de pintura en húmedo, según su tipo, será la que se indica en la Tabla

La Dirección de Planeación y Proyectos solo autoriza el proyecto ejecutivo, no se responsable de la correcta ejecución de la obra, Este documento no tiene validez si no presenta las firmas de los responsables para su autorización, así como los sellos respectivos.

PRESIDENTE MUNICIPAL
M.P.P. Leonardo Montañez Castro
ENCARGADA DE DESPACHO DE LA SOPMA
Arq. Gloria Guadalupe Castillo González

REV	FECHA	OBSERVACIONES

V°B° DE LA DEPENDENCIA

RESP. DE PROY. EXTERNO		LOGO EXTERNO
CED. PROFESIONAL		
PROYECTO	REVISO	AUTORIZO

Dirección de Planeación y Proyectos de Obra — Secretaría de Obras Públicas

PROYECTISTA	COORDINACIÓN
ARQ. ALEJANDRO JAIME LEÓN	
JEFE DE DEP.	DIRECTOR
ARQ. J. JESÚS FRANCISCO GONZÁLEZ	M. en ARQ. JOSÉ LUIS JIMÉNEZ GARCÍA

PROYECTO
OBRA COMPLEMENTARIA Y SEÑALIZACIÓN AVENIDA DE LA CONVENCIÓN DE 1914 SUR

UBICACIÓN
AV. CONVENCIÓN DE 1914, AMBAS CALZADAS DE ENTRE CALLE AYUNTAMIENTO Y AV. HEROE DE NACOZARI

CONTENIDO
PLANO DE SEÑALIZACIÓN TRAMO E

CLAVE	No. PLANO
SEÑ 05	06
FECHA: MARZO 2022	ESCALA: S/ESCALA
ACOTACIÓN: METROS	No. EXP.: E-000-22

Aguascalientes
LA CIUDAD DE TU VIDA