Aguascalientes
LA CIUDAD DE TU VIDA

Dirección de Programación Presupuestal
Núm. Oficio AMPP/0672/22
Aguascalientes, Ags. 29 de Diciembre del 2022
Asunto: Validación de Expediente Técnico

C.P. SERGIO ARTURO LOZANO GONZÁLEZ
SECRETARIO DE FINANZAS MUNICIPALES
P R E S E N T E

Con fundamento en los artículos 17 fracción XV, 60 fracción XVI y 76 fracción VI del Reglamento del Sistema Integral de Desarrollo Municipal y del Instituto Municipal de Planeación y Evaluación de Aguascalientes, hago referencia al oficio SOPMA/3080/2022 recibido por este Instituto el día 29 de Diciembre del 2022 por parte de la Secretaría de Obras Públicas Municipales, mediante el cual remiten el expediente técnico original de la siguiente obra para su análisis, registro y priorización, conforme al Programa Anual de Obra Pública y Programas Sociales para el ejercicio presupuestal 2022:

DEPENDENCIA EJECUTORA:	SOPMA
NOMBRE DE LA OBRA O PROYECTO:	SEÑALIZACIÓN AMBAS CALZADAS
UBICACIÓN:	BLVD. JOSÉ MARÍA CHÁVEZ, TRAMO: ENTRE AV. AGUASCALIENTES SUR Y AV. SIGLO XXI, VARIAS COLONIAS, AGUASCALIENTES, AGS.
FONDO DE INVERSIÓN:	FONDO DE INFRAESTRUCTURA SOCIAL MUNICIPAL Y DE LAS DEMARCACIONES TERRITORIALES DEL DISTRITO FEDERAL
IMPORTE:	$1,100,000.00 (ET FINAL)
No. DE OBRA:	2022-FISMDF-0140-11-0109
MODALIDAD DE EJECUCIÓN:	CONTRATO
EJE:	MUNICIPIO SOBRESALIENTE
ESTRATEGIA:	OBRA PÚBLICA INTELIGENTE
POLITICA:	5.8.1.REHABILITACIÓN Y MANTENIMIENTO VIALIDADES, CAMINOS, CALLES, ÁREAS DE TERRACERÍA Y CAUCES (C

Al respecto, hago de su conocimiento que dicho expediente ha sido analizado en su integración técnica y documental, con base en el artículo 168 fracción I del Reglamento de la Ley de Obras Públicas y Servicios Relacionados para el Estado de Aguascalientes y sus Municipios.

Asimismo, le comento que este Instituto valida dicha obra acorde a lo establecido en los artículos 14, 22 párrafo segundo y 23 de la Ley de Obras Públicas y Servicios Relacionados para el Estado de Aguascalientes y sus Municipios, la cual se encuentra alineada al Plan de Desarrollo Municipal vigente, para dar cumplimiento a las metas establecidas en el mismo, y a los Lineamientos Generales para la Operación de este Fondo de Inversión, toda vez que la misma cuente con la autorización del CODEMUN. De igual manera, se hace de su conocimiento que deberá cumplir con lo establecido en los ordenamientos aplicables en lo que respecta al ejercicio, control e información de los recursos de este Fondo. Cabe hacer mención que los recursos solicitados para este proyecto de inversión, estarán sujetos a la disponibilidad presupuestal para el presente ejercicio fiscal que determine la Secretaría a su digno cargo. Sin otro particular por el momento, le envío un cordial saludo.

A T E N T A M E N T E

ARQ. AUSTRIA GABRIELA DÁVILA DE LA LLAVE
DIRECTORA GENERAL DEL IMPLAN

SEDR/ GAAR / JDBC
C.c.p. I.C. ING. MIGUEL ÁNGEL HUIZAR BOTELLO .- Secretaría de Obras Públicas Municipales .Para su conocimiento.
C.c.p. Archivo.

Instituto Municipal de Planeación y Evaluación de Aguascalientes

Antonio Acevedo Escobedo 103 A. Col. Centro
Aguascalientes, Ags. C.P. 20000

(449) 9101010 Ext. 3117

www.implanags.gob.mx

GOBIERNO MUNICIPAL DE AGUASCALIENTES

INSTITUTO MUNICIPAL DE PLANEACION

IMPLAN

ANÁLISIS INTEGRAL DE EXPEDIENTE TÉCNICO

No. DE OBRA (PAOP 2020):	2022-FISMDF-0140-11-0109	REGISTRO No.	306
OFICIO DE VALIDACIÓN:	AMPP/0672/22	FECHA RECIBIDO PARA REVISIÓN:	29 de Diciembre del 2022
PROGRAMA:	URBANIZACION MUNICIPAL	LOCALIDAD O COLONIA:	VARIAS COLONIAS
SUB-PROGRAMA:	0411- Calles y Caminos	DELEGACIÓN:	Aguascalientes
DEPENDENCIA:	Secretaría de Obras Públicas Municipales	MOD. DE EJECUCIÓN:	CONTRATO
NOMBRE DE LA OBRA:	SEÑALIZACIÓN AMBAS CALZADAS, BLVD. JOSÉ MARÍA CHÁVEZ, TRAMO: ENTRE AV. AGUASCALIENTES SUR Y AV. SIGLO XXI		
FUENTE DE FINANCIAMIENTO:	FONDO DE INFRAESTRUCTURA SOCIAL MUNICIPAL Y DE LAS DEMARCACIONES TERRITORIALES DEL DISTRITO FEDERAL, FISMDF		
INVERSIÓN:	$1,100,000.00	CLASIFICACIÓN DE OBRA:	BIENES DE DOMINIO PUBLICA

TOTAL	FEDERAL	ESTATAL	MUNICIPAL	BENEFICIARIOS	OTROS	DIFERENCIA ENTRE MOD.
$1,100,000.00	$1,100,000.00	0.00	0.00	0.00	0.00	*$15.999,99*

TIPO DE EXPENDIENTE:	ET FINAL	AÑO: 2023	AÑO:	AÑO:
AVANCES:	Financiero: 100 %	Físico: 100 %		
FECHA DE INICIO:	10 de Diciembre del 2022	FECHA DE TÉRMINO:	19 de Diciembre del 2022	REGISTRO SIMA: 140

CHEK LIST DE LOS ANEXOS DEL EXPEDIENTE TÉCNICO

CÉDULA DE REGISTRO DE OBRA	✓
DICTAMEN DE FACTIBILIDAD	✓
MEMORIA DESCRIPTIVA	✓
PRESUPUESTO BASE	✓
FACTIBILIDAD VERIFICADA EN CAMPO	✓
CROQUIS DE UBICACIÓN (MACRO)	✓
CROQUIS DE UBICACIÓN (MACRO)	✓
PROGRAMA DE OBRA Y MONTOS MENSUALES	✓
PLANOS O ESTUDIOS TÉCNICOS	✓
PADRÓN DE BENEFICIARIOS	N/A
ACTA DE ACEPTACIÓN DEL PROYECTO	N/A
DICTAMEN DE IMPACTO AMBIENTAL	N/A
CONVENIO DE CONCERTACIÓN	N/A
ACTA CONSTITUTIVA	N/A

METAS		BENEFICIARIOS		PERIODO DE EJECUCION		OBRA PROPUESTA		CLAVE SISCO
UNIDAD DE MEDIDA	CANT	TIPO DE BENEFICIARIOS	CANTIDAD	FECHA DE INICIO	FECHA DE TERMINO	CONCEPTO	JORNALES A GENERAR	
OBRA	1	Personas	160	2022-12-10	2022-12-19	Obra Complementaria y/o Señalización	2860	2398

INCLUIDO EN PLAN DE DESARROLLO MUNICIPAL Y EL PROGRAMA ANUAL DE OBRA PÚBLICA

OBSERVACIONES:

SIN OBSERVACIONES

RECIBIO: ING. JOSÉ DAVID BARQUETE CLAUSTRO
Analista de Programación e Inversión de Obra Pública

29 de Diciembre del 2022
Fecha de validación

29 de Diciembre del 2022
Fecha de validación Expediente

PROCEDE Si ✓ No

H. AYUNTAMIENTO CONSTITUCIONAL DEL MUNICIPIO DE AGUASCALIENTES 2021-2024

AYUNTAMIENTO DE AGUASCALIENTES

CEDULA DE REGISTRO POR OBRA

Aguascalientes
LA CIUDAD DE TU VIDA

050400-001E00E05-05-2-2-1-00-1-E-0510-0-17-0140-21-2502-6144

2022-FISMDF-0140-0411109-076	Obra **SEÑALIZACIÓN AV. JOSÉ MARÍA CHÁVEZ, AMBAS CALZADAS**
Tipo DEFINITIVO 1 2022 Folio SISCO **2398**	Ubic. TRAMO: ENTRE AV. AGUASCALIENTES SUR Y AV. SIGLO XXI, AGUASCALIENTES Mpio.

Ent. Ejecutora : **050400001E00E05**

Eje: **05**	MUNICIPIO SOBRESALIENTE
Finalidad: **2**	DESARROLLO SOCIAL
Función: **2**	VIVIENDA Y SERVICIOS A LA COMUNIDAD
Subfunción: **1**	URBANIZACIÓN
Tema: **00**	SIN TEMA
Cuenta del Gasto **1**	GASTO PROGRAMABLE
Clasif. Programatica: **E**	PRESTACIÓN DE SERVICIOS PÚBLICOS
Programa: **0510**	Movilidad Urbana
SubPrograma: **0**	SUBPROGRAMA GENÉRICO
Proyecto: **17**	
Tipo de Gasto: **21**	GASTO INVERSIÓN / OBRA PÚBLICA

I N V E R S I O N 2022

Municipal	2502	FONDO PARA LA INFRAESTRUCTURA SOCIAL MUNICIPAL Y DE LAS DEMARCACIONES TERRITORIALES DEL DISTRITO FEDERAL 2022	$1,100,000.00

Folio SIMA 140 Total $1,100,000.00

M E T A S

Unidad de Medida	Cantidad	Descripción
OBRA	1	OBRA SEÑALIZACIÓN AV. JOSÉ MARÍA CHÁVEZ, AMBAS CALZADAS

Inversión Ejercida Total al 31 de Diciembre de 2021 $0.00

Avance Fisico Acumulado al 31 de Diciembre de 2021

Avance Fisico Acumulado Programado al 31 de Diciembre de 2022 100 %

Fecha de Inicio 10 Dic 2022 Fecha de Terminación 19 Dic 2022

Jornales a Generar en 2022 2860

Modalidad de ejecución CONTRATO

Clasificación de la Obra Bienes de Dominio Público

Registro del Patrimonio: Obras del dominio público

OBRAS PÚBLICAS

Av. Aguascalientes Sur No. 2615
Fracc. Jardines de las Fuentes,
Aguascalientes, Ags. C.P. 20278

(449) 9 78 92 01, 06, 09

www.ags.gob.mx

GENERALES

Nombre del Proyecto : SEÑALIZACIÓN AV. JOSÉ MARÍA CHÁVEZ, AMBAS CALZADAS

TRAMO: ENTRE AV. AGUASCALIENTES SUR Y AV. SIGLO XXI, AGUASCALIENTES Mpio.

Programa : 04 URBANIZACION MUNICIPAL

Subprograma : 11 Calles y caminos (428.- Rehabilitación: 0411208- Señalización)

Clave del Municipio : AGUASCALIENTES

Localidad :

Barrio, Colonia o Ejido : AGUASCALIENTES Mpio.

Tipo de Obra : NUEVA

DESCRIPCIÓN DEL PROYECTO:

SUMINISTRO Y APLICACIÓN DE PINTURA BASE SOLVENTE PARA MARCAS EN GUARNICIONES CLASIFICACION M-12.1 5891.30 ML

SUMINISTRO Y APLICACIÓN DE PINTURA TERMOPLASTICA ALQUIDALICA DE 120 MILESIMAS DE " (in) EN RAYA SEPA 210.00 ML

SUMINISTRO Y APLICACIÓN DE PINTURA TERMOPLASTICA ALQUIDALICA DE 120 MILESIMAS DE " (in) EN RAYA SEPA 5684.65 ML

SUMINISTRO Y APLICACIÓN DE PINTURA TERMOPLASTICA ALQUIDALICA DE 120 MILESIMAS DE " (in) EN RAYA EN L 3055.80 ML

SUMINISTRO Y APLICACIÓN DE PINTURA TERMOPLASTICA ALQUIDALICA DE 120 MILESIMAS DE " (in) EN RAYA GUIA 92.70 ML

SUMINISTRO Y APLICACIÓN DE PINTURA TERMOPLASTICA ALQUIDALICA DE 120 MILESIMAS DE " (in) EN RAYA DE A 43.40 ML

SUMINISTRO Y APLICACIÓN DE PINTURA TERMOPLASTICA ALQUIDALICA DE 120 MILESIMAS DE " (in) EN RAYA PARA 176.23 M2

SUMINISTRO Y APLICACIÓN DE PINTURA TERMOPLASTICA ALQUIDALICA DE 120 MILESIMAS DE " (in) EN FLECHAS 30.00 PIEZA

SUMINISTRO Y APLICACIÓN DE PINTURA TERMOPLASTICA ALQUIDALICA DE 120 MILESIMAS DE " (in) EN FLECHAS C 3.00 PIEZA

DESMONTAJE Y RETIRO MANUAL DE VIALETA EXISTENTE (SOLAR O ESTANDAR) CON RECUPERACION Y TRASLADO A PAR 602.12 PIEZA

SUMINISTRO Y COLOCACION DE VIALETA STANDARD (S-200) DE 10X10CM. COLOR: CUERPO AMARILLO Y REFLEJANTE 408.00 PIEZA

SUMINISTRO Y COLOCACION DE VIALETA SOLAR DE 10X10CM. COLOR: CUERPO ALUMINIO 3 LED DOS CARAS REFLEJAN 194.00 PIEZA

SUMINISTRO Y APLICACIÓN DE PINTURA TERMOPLASTICA ALQUIDALICA DE 120 MILESIMAS DE " EN LETRAS Y NUME 3.00 PIEZA

SUMINISTRO Y APLICACIÓN DE PINTURA TERMOPLASTICA ALQUIDALICA DE 120 MILESIMAS DE " EN LETRAS Y NUME 1.00 PIEZA

SUMINISTRO Y APLICACIÓN DE PINTURA TERMOPLASTICA ALQUIDALICA DE 120 MILESIMAS DE " EN LETRAS Y NUME 1.00 PIEZA

Beneficiarios (No. y Tipo) :

160 PERSONAS

Mujeres: 85

Av. Aguascalientes Sur No. 2615
Fracc. Hornos 76 Fuentes,
Aguascalientes, Ags. C.P. 20278

(449) 9 78 92 01, 06, 09

www.ags.gob.mx

Los abajo firmantes, hacen constar que el presente proyecto :

SEÑALIZACIÓN AV. JOSÉ MARÍA CHÁVEZ, AMBAS CALZADAS

TRAMO: ENTRE AV. AGUASCALIENTES SUR Y AV. SIGLO XXI, AGUASCALIENTES Mpio.

cumple con los Requisitos y Normas Técnicas establecidas por la Dependencia Normativa, por lo que es viable su ejecución. Comprometiéndose la misma a proporcionar la supervisión y asistencia técnica necesaria durante el proceso administrativo.

Por la Dependencia Ejecutora

Ing. Miguel Angel Huizar Botello
Secretario de Obras Públicas

Lic. Jaime Gallo Camacho
Secretario de Desarrollo Urbano

LUGAR :AGUASCALIENTES, AGS.

MUNICIPIO: AGUASCALIENTES

LOCALIZACION: TRAMO: ENTRE AV. AGUASCALIENTES SUR Y AV. SIGLO XXI, AGUASCALIENTES Mpio.

PROGRAMA: URBANIZACION MUNICIPAL

SUBPROGRAMA: Calles y caminos (428.- Rehabilitación: 0411208- Señalización)

OBRA A REALIZAR: SEÑALIZACIÓN AV. JOSÉ MARÍA CHÁVEZ, AMBAS CALZADAS

DEPENDENCIA EJECUTORA: SECRETARÍA DE OBRAS PUBLICAS DEL MUNICIPIO DE AGUASCALIENTES

FORMA DE EJECUCION: CONTRATO

TIPO DE OBRA PROPUESTA: NUEVA

CONDICIONES ACTUALES DE LA OBRA:

SEÑALIZACIÓN AV. JOSÉ MARÍA CHÁVEZ, AMBAS CALZADAS

CARACTERISTICAS DE LA OBRA: Pesimo

FACTIBILIDAD DE LA OBRA:

ESTA OBRA SE REQUIERE PARA EL BENEFICIO DE LA CIUDADANÍA

PROCEDE: SI [X] NO [ ]

REVISÓ: Jefa del Departamento de Expedientes Tecnicos y Costos

NOMBRE: Arq. Blanca Margarita Martinez Amador

FIRMA:

FECHA: 29 Dic 2022

SECRETARÍA DE OBRAS PÚBLICAS

Av. Aguascalientes Sur No. 2615
Fracc. Jardines de las Fuentes,
Aguascalientes, Ags. C.P. 20278

(449) 9 78 92 01, 06, 09

www.ags.gob.mx


No. Folio SISCO 2398

H. AYUNTAMIENTO DE AGUASCALIENTES
SECRETARÍA DE OBRAS PÚBLICAS
DIRECCIÓN DE SUPERVISIÓN DE OBRA
LOCALIZACION

H. AYUNTAMIENTO CONSTITUCIONAL DEL MUNICIPIO DE AGUASCALIENTES 2021-2024

Aguascalientes LA CIUDAD DE TU VIDA

OBRA:	SEÑALIZACION AV. JOSÉ MARIA CHAVEZ, AMBAS CALZADAS, TRAMO: ENTRE AV. AGUASCALEINTES SUR Y AV. SIGLO XXI, AGUASCALEINTES Mpio.					
NO. DE CONTR	FISMDF-0140-2022	CONTRATISTA:	CONSTRUCTORA INTEGRAL DE AGUASCALIENTES, S.A. DE			

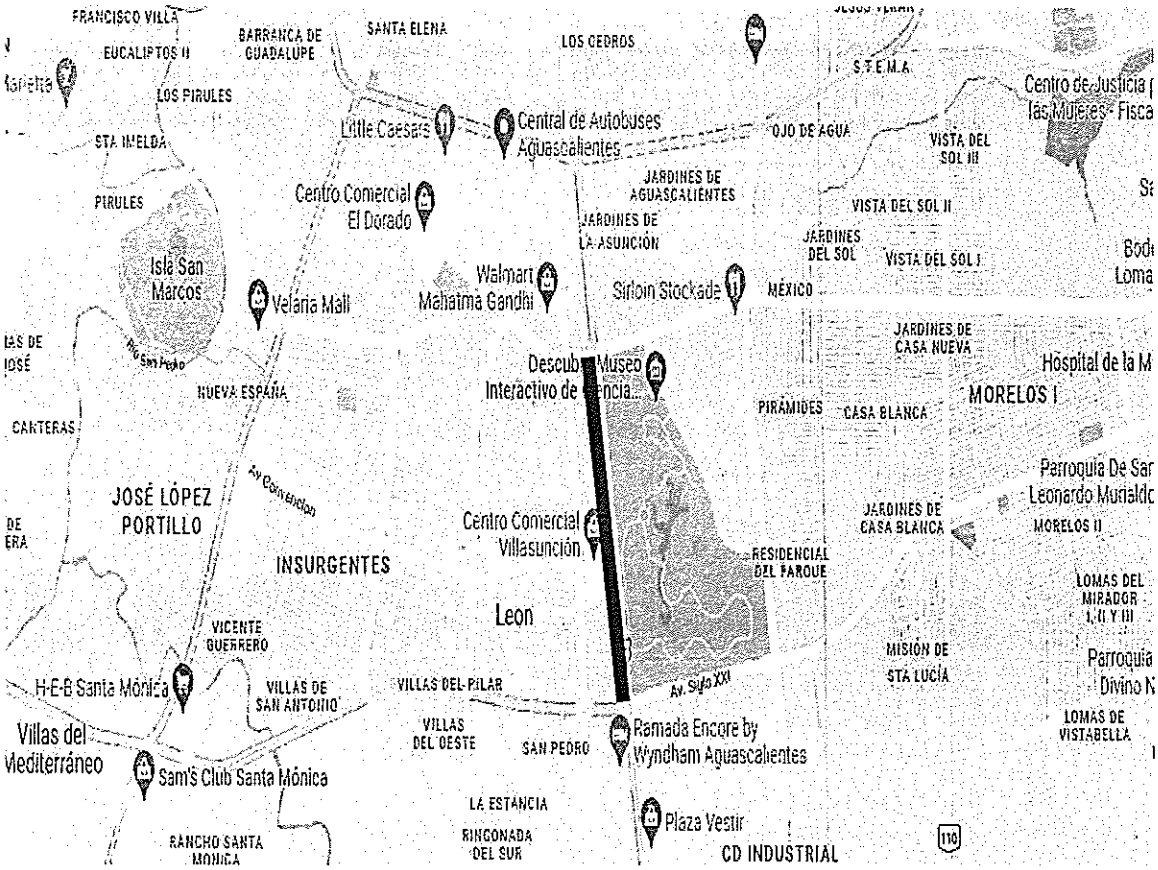

ING. DAVID ALONSO MONTOYA
SUPERVISOR DE OBRA.

H. AYUNTAMIENTO CONSTITUCIONAL DEL MUNICIPIO DE AGUASCALIENTES 2021-2024

H. AYUNTAMIENTO DE AGUASCALIENTES
SECRETARÍA DE OBRAS PÚBLICAS
DIRECCIÓN DE SUPERVISIÓN DE OBRA
LOCALIZACION

Aguascalientes
LA CIUDAD DE TU VIDA

OBRA:	SEÑALIZACION AV. JOSÉ MARIA CHAVEZ, AMBAS CALZADAS, TRAMO: ENTRE AV. AGUASCALEINTES SUR Y AV. SIGLO XXI, AGUASCALEINTES Mpio.					
NO. DE CONTR	FISMDF-0140-2022		CONTRATISTA:	CONSTRUCTORA INTEGRAL DE AGUASCALIENTES, S.A. DE		



ING. DAVID ALONSO MONTOYA
SUPERVISOR DE OBRA.

R03-POS-SOS-7.5.1-04	
REVISION:	00
FECHA DE REVISION:	
RESPONSABLE:	SUPERVISOR DE OBRA
TIEMPO DE RET:	02 AÑOS

PROGRAMA DE OBRA DEFINITIVO

Aguascalientes
LA CIUDAD DE TU VIDA

No. DE CONTRATO : FISMDF-0140-2022

PROGRAMA: 04 URBANIZACION MUNICIPAL

No. OBRA Y NOMBRE DE LA OBRA: SEÑALIZACION AV. JOSÉ MARIA CHAVEZ, AMBAS CALZADAS, TRAMO: ENTRE AV. AGUASCALEINTES SUR Y AV. SIGLO XXI, AGUASCALEINTES Mplo.

INICIO VIGENTE: 10-diciembre-22

TERMINO REAL: 19-diciembre-22

RECURSO 2022

CONCEPTO			1	2	3	4	5	6	7	8	9	10	11	12	13	14	15	16	PONDERACIÓN %	
			2022																	
			OCTUBRE	NOVIEMBRE	DICIEMBRE	ENERO	FEBRERO	MARZO	ABRIL	MAYO	JUNIO	JULIO	AGOSTO	SEPTIEMBRE	OCTUBRE	NOVIEMBRE	DICIEMBRE	ENERO	FINANCIERO	FÍSICO
DESCRIPCION	INVERSION																20 8			
SEÑALIZACION AV. JOSÉ MARIA CHAVEZ, AMBAS CALZADAS, TRAMO: ENTRE AV. AGUASCALEINTES SUR Y AV. SIGLO XXI, AGUASCALEINTES Mplo.																				
TRAMO: ENTRE AV. AGUASCALEINTES SUR Y AV. SIGLO XXI, AGUASCALEINTES, MPO.																				
SEÑALIZACION HORIZONTAL	$ 948,275.86	100			43 57														100.00	100.00
																			0.00	0.00
SUBTOTAL SIN IVA	$ 948,275.85		0 0 0 0	0 0 0 0	0 1 1 1	0 0 0 0	0 0 0 0	0 0 0 0	0 0 0 0	0 0 0 0	0 0 0 0	0 0 0 0	0 0 0 0	0 0 0 0	0 0 0 0	0 0 0 0	0 0 0 0	0 0 0 0		
AVANCE SEMANAL %			0% 0% 0% 0%	0% 0% 0% 0%	33% 33% 33% 100%	0% 0% 0% 0%	0% 0% 0% 0%	0% 0% 0% 0%	0% 0% 0% 0%	0% 0% 0% 0%	0% 0% 0% 0%	0% 0% 0% 0%	0% 0% 0% 0%	0% 0% 0% 0%	0% 0% 0% 0%	0% 0% 0% 0%	0% 0% 0% 0%	0% 0% 0% 0%		
AVANCE SEMANAL ACUMULADO %			0% 0% 0% 0%	0% 0% 0% 0%	33% 67% 100% 100%	100% 100% 100% 100%	100% 100% 100% 100%	100% 100% 100% 100%	100% 100% 100% 100%	100% 100% 100% 100%	100% 100% 100% 100%	100% 100% 100% 100%	100% 100% 100% 100%	100% 100% 100% 100%	100% 100% 100% 100%	100% 100% 100% 100%	100% 100% 100% 100%	100% 100% 100% 100%	100.00	100.00
EJERCIDO SEMANAL $			- - - -	- - - -	428,724.14 331,896.55 189,655.17	- - - -	- - - -	- - - -	- - - -	- - - -	- - - -	- - - -	- - - -	- - - -	- - - -	- - - -	- - - -	- - - -	$ 948,275.86	
EJERCIDO MENSUAL $			$0.00	$0.00	$948,275.86	$0.00	$0.00	$0.00	$0.00	$0.00	$0.00	$0.00	$0.00	$0.00	$0.00	$0.00	$0.00	$0.00	$ 151,724.14	IVA 16%
EJERCIDO MENSUAL ACUMULADO $			0.00	0.00	948,275.86	948,275.86	948,275.86	948,275.86	948,275.86	948,275.86	948,275.86	948,275.86	948,275.86	948,275.86	948,275.86	948,275.86	948,275.86	948,275.86		
EJERCIDO SEMANAL %			0% 0% 0% 0%	0% 0% 0% 0%	45% 35% 20%	0% 0% 0% 0%	0% 0% 0% 0%	0% 0% 0% 0%	0% 0% 0% 0%	0% 0% 0% 0%	0% 0% 0% 0%	0% 0% 0% 0%	0% 0% 0% 0%	0% 0% 0% 0%	0% 0% 0% 0%	0% 0% 0% 0%	0% 0% 0% 0%	0% 0% 0% 0%		
EJERCIDO MENSUAL %			0%	0%	100%	0%	0%	0%	0%	0%	0%	0%	0%	0%	0%	0%	0%	0%	GRAN TOTAL EJERCIDO	
EJERCIDO MENSUAL ACUMULADO %			0%	0%	100%	100%	100%	100%	100%	100%	100%	100%	100%	100%	100%	100%	100%	100%	$ 1,100,000.00	

PRE

ING. DAVID ALONSO MONTOYA
SUPERVISOR

PRESIDENCIA MUNICIPAL DE AGUASCALIENTES

FACTIBILIDAD VERIFICADA EN CAMPO

GENERALES

EJERCICIO: 2022 APROBACION No: 2022-FISMDF-0140-0411109-076
LOCALIDAD: TRAMO: ENTRE AV. AGUASCALIENTES SUR Y AV. SIGLO XXI, AGUASCALIENTES, MPO.
MUNICIPIO: AGUASCALIENTES, Mpio.
TIPO DE INVERSION: FONDO PARA LA INFRAESTRUCTURA SOCIAL MUNICIPAL Y DE LAS DEMARCACIONES TERRITORIALES DEL DISTRITO FEDERAL (100%) (MUNICIPAL)
PROGRAMA: 04 URBANIZACION MUNICIPAL
SUB-PROGRAMA: 11 Calles y caminos

OBRA A REALIZARSE: SEÑALIZACION AV. JOSÉ MARIA CHAVEZ, AMBAS CALZADAS, TRAMO: ENTRE AV. AGUASCALEINTES SUR Y AV. SIGLO XXI, AGUASCALEINTES Mpio.

DEPENDENCIA EJECUTORA: SECRETARÍA DE OBRAS PÚBLICAS MUNICIPALES (S.O.P.M.A)
FORMACIÓN DE EJECUCION: CONTRATO NO. DE CONTRATO: FISMDF-0140-2022
NOMBRE CONTRATISTA: CONSTRUCTORA INTEGRAL DE AGUASCALIENTES, S.A. DE C.V.
REPRESENTANTE: JOSÉ OJEDA GOMEZ
MONTO CONT. ORIGEN $ 1,100,000.00 ANTICIPO: $ - PLAZO 10 DIAS
1A AMPLIACION $: $ - 1 AMPL DIAS
2A AMPLIACION $: 2 AMPL DIAS
FIRMA CONTRATO: 09/12/2022
INICIO CONT: dd/mm/aa 10/12/2022 TERMINO CONT: 19/12/2022
INICIO REAL: dd/mm/aa 10/12/2022 TERMINO REAL: 19/12/2022

TIPO DE OBRA PROPUESTA

NUEVA CREACIÓN		CONSOLIDACIÓN	
COMPLEMENTARIA	X	AMPLIACIÓN	
REHABILITACIÓN		EQUIPAMIENTO	

CARACTERÍSTICAS DE LA OBRA:

SEÑALIZACION ZONAS PEATONALES Y GUARNICIONES
SUMINISTRO Y APLICACIÓN DE PINTURA TERMOPASTICA ALQUILADICA
FLECHAS CABEZA DOBLE
LINEA SEPARADORA DE CARRILES

CONDICIONES ACTUALES DE LA OBRA: (SELECCIONAR UNO OBLIGATORIO)

BUEN ESTADO X REGULAR PESIMO ESTADO

FACTIBILIDAD DE LA OBRA: (CONDICIONES ACTUALES DE LA OBRA)

ESTA OBRA SE ENCUENTRA EN CONDICIONES PARA OPERARSE

PROCEDE: SI: X NO:
MARQUE SOLO UNA

ING. DAVID ALONSO MONTOYA
SUPERVISOR

PRESIDENCIA MUNICIPAL DE AGUASCALIENTES

FACTIBILIDAD VERIFICADA EN CAMPO

GENERALES

LOCALIDAD: TRAMO: ENTRE AV. AGUASCALIENTES SUR Y AV. SIGLO XXI, AGUASCALIENTES, MPO.
MUNICIPIO: AGUASCALIENTES, Mpio.
PROGRAMA: 04 URBANIZACION MUNICIPAL
SUB-PROGRAMA: 11 Calles y caminos
OBRA A REALIZARSE: SEÑALIZACION AV. JOSÉ MARIA CHAVEZ, AMBAS CALZADAS, TRAMO: ENTRE AV. AGUASCALEINTES SUR Y AV. SIGLO XXI, AGUASCALEINTES Mpio.

DEPENDENCIA EJECUTORA: SECRETARÍA DE OBRAS PÚBLICAS MUNICIPALES (S.O.P.M.A)
FORMACIÓN DE EJECUCION: CONTRATO

TIPO DE OBRA PROPUESTA

NUEVA CREACIÓN		CONSOLIDACIÓN	
COMPLEMENTARIA	X	AMPLIACIÓN	
REHABILITACIÓN		EQUIPAMIENTO	

CARACTERÍSTICAS DE LA OBRA:

SEÑALIZACION ZONAS PEATONALES Y GUARNICIONES
SUMINISTRO Y APLICACIÓN DE PINTURA TERMOPASTICA ALQUILADICA
FLECHAS CABEZA DOBLE
LINEA SEPARADORA DE CARRILES

CONDICIONES ACTUALES DE LA OBRA:

BUEN ESTADO: X REGULAR: PESIMO ESTADO:

FACTIBILIDAD DE LA OBRA:

ESTA OBRA SE ENCUENTRA EN CONDICIONES PARA OPERARSE

PROCEDE **SI:** X **NO:**

ING. DAVID ALONSO MONTOYA
SUPERVISOR

H. AYUNTAMIENTO CONSTITUCIONAL DEL MUNICIPIO DE AGUASCALIENTES 2021-2024

PRESUPUESTO MODIFICADO

Aguascalientes
LA CIUDAD DE TU VIDA

Obra: **SEÑALIZACIÓN AV. JOSÉ MARÍA CHÁVEZ, AMBAS CALZADAS**

Ubicación: **TRAMO: ENTRE AV. AGUASCALIENTES SUR Y AV. SIGLO XXI, AGUASCALIENTES Mpio.**

Contratista: **CONSTRUCTORA INTEGRAL DE AGUASCALIENTES, S.A. DE C.V. (471)**

No.	Concepto	Unidad	Cantidad	Precio Unitario	Importe Total
	GRUPO: **SEÑALIZACION**				
	PARTIDA: **SEÑALIZACION HORIZONTAL**				
1	SUMINISTRO Y APLICACIÓN DE PINTURA BASE SOLVENTE PARA MARCAS EN GUARNICIONES CLASIFICACION M-12.1, M12.2 APLICADA SOBRE GUARNICIONES Y DENTELLONES DE CUALQUIER COLOR, SEGÚN SE REQUIERA Y SEGÚN NORMA S.C.T. SECADO AL TACTO EN 5 MIN Y AL DURO EN 30 MIN CON MICRO ESFERA , DESARROLLO DE 35 CM. INCLUYE: MATERIALES Y ESPECIFICACIONES QUE CUMPLAN CON LA NORMATIVA N-CMT-5-01-001/05, N-PRY-CAR-10-01-002/13 APLICADAS AL DIA DE HOY, TRAZO, MANO DE OBRA, LIMPIEZA PREVIA DE SUPERFICIE, EQUIPO NECESARIO PARA SU EJECUCIÓN, Y TODO LO NECESARIO PARA SU CORRECTA EJECUCIÓN, TRABAJO TERMINADO.	ML	5891.3	$50.27	$296,155.65
2	SUMINISTRO Y APLICACIÓN DE PINTURA TERMOPLASTICA ALQUIDALICA DE 120 MILESIMAS DE " (in) EN RAYA SEPARADORA DE SENTIDOS DE CIRCULACION CLASIFICACIÓN M - 1.1, LÍNEA CONTINUA SENCILLA DE DIVISIÓN DE CARRILES DE FRENTE EN PISO, DE 10 CM DE ANCHO, COLOR BLANCO Y/O AMARILLO CON MICRO ESFERA SEGÚN MANUAL DE SEÑALIZACIÓN VIAL Y DISPOSITIVOS DE SEGURIDAD SICT, SECADO AL TACTO EN 5 MIN Y AL DURO EN 30 MIN. INCLUYE: MATERIALES Y ESPECIFICACIONES QUE CUMPLAN CON LA NORMATIVA N-CMT-5-01-001/13, N-PRY-CAR-10-01-002/13 APLICADAS AL DIA DE HOY, MATERIAL APLICADO EN SU ESTADO DE FUSION A UNA TEMPERATURA MINIMA DE 204 C, LA SUPERFICIE DE CONCRETO O ASFALTO NO DEBE PRESENTAR UNA TEMPERATURA MENOR A LOS 10 C, ;TIEMPO DE SECADO EN RANGOS DE TEMPERATURA DE 10 C DEL SUSTRATO 2 MINUTOS, Y NO MAS DE 10 MINUTOS CUANDO EL SUSTRATO OSCILA ALREDEDOR DE 54C, TRAZO, ENMASCARILLADO, MANO DE OBRA, LIMPIEZA PREVIA Y FINAL DE SUPERFICIE, EQUIPO NECESARIO PARA SU EJECUCIÓN, Y TODO LO NECESARIO PARA SU CORRECTA EJECUCIÓN, TRABAJO TERMINADO.	ML	210	$41.59	$8,733.90
3	SUMINISTRO Y APLICACIÓN DE PINTURA TERMOPLASTICA ALQUIDALICA DE 120 MILESIMAS DE " (in) EN RAYA SEPARADORA DE SENTIDOS DE CIRCULACION CLASIFICACIÓN M - 1.2, RAYA DISCONTINUA SENCILLA, DE DIVISIÓN DE CARRILES PARA VELOCIDADES MENORES A 60 KM/HR DE FRENTE EN PISO, DESARROLLO DE 2.50 ML X 0.10 MTS DE ANCHO, CON UNA SEPARACIÓN DE 5.00 MTS ENTRE SI PROMEDIO, A BASE DE PINTURA PARA TRAFICO COLOR BLANCO CON MICRO ESFERA SEGÚN MANUAL DE SEÑALIZACIÓN VIAL Y DISPOSITIVOS DE SEGURIDAD SICT (S.C.T). INCLUYE: MATERIALES Y ESPECIFICACIONES QUE CUMPLAN CON LA NORMATIVA N-CMT-5-01-001/13, N-PRY-CAR-10-01-002/13 APLICADAS AL DIA DE HOY, MATERIAL APLICADO EN SU ESTADO DE FUSION A UNA TEMPERATURA MINIMA DE 204 C, LA SUPERFICIE DE CONCRETO O ASFALTO NO DEBE PRESENTAR UNA TEMPERATURA MENOR A LOS 10 C, ;TIEMPO DE SECADO EN RANGOS DE TEMPERATURA DE 10 C DEL SUSTRATO 2 MINUTOS, Y NO MAS DE 10 MINUTOS CUANDO EL SUSTRATO OSCILA ALREDEDOR DE 54C, TRAZO, ENMASCARILLADO, MANO DE OBRA, LIMPIEZA PREVIA Y FINAL DE SUPERFICIE, EQUIPO NECESARIO PARA SU EJECUCIÓN, Y TODO LO NECESARIO PARA SU CORRECTA EJECUCIÓN, TRABAJO TERMINADO.	ML	5684.65	$41.59	$236,424.59

Obra: **SEÑALIZACIÓN AV. JOSÉ MARÍA CHÁVEZ, AMBAS CALZADAS**

Ubicación: **TRAMO: ENTRE AV. AGUASCALIENTES SUR Y AV. SIGLO XXI, AGUASCALIENTES Mpio.**

Contratista: **CONSTRUCTORA INTEGRAL DE AGUASCALIENTES, S.A. DE C.V. (471)**

No.	Concepto	Unidad	Cantidad	Precio Unitario	Importe Total
	GRUPO: **SEÑALIZACION**				
	PARTIDA: **SEÑALIZACION HORIZONTAL**				
4	SUMINISTRO Y APLICACIÓN DE PINTURA TERMOPLASTICA ALQUIDALICA DE 120 MILESIMAS DE " (in) EN RAYA EN LA ORILLA DEL ARROYO VIAL CLASIFICACIÓN M - 3.3, CONTINUA IZQUIERDA, PARA VIALIDADES URBANAS DE FRENTE EN PISO, DE 10 CM DE ANCHO Y SEPARADA 15 CM. DE LA GUARNICION, A BASE DE PINTURA PARA TRAFICO COLOR BLANCO CON MICRO ESFERA SEGÚN MANUAL DE SEÑALIZACIÓN VIAL Y DISPOSITIVOS DE SEGURIDAD SICT (S.C.T)., INCLUYE: MATERIALES Y ESPECIFICACIONES QUE CUMPLAN CON LA NORMATIVA N-CMT-5-01-001/13, N-PRY-CAR-10-01-002/13 APLICADAS AL DIA DE HOY, MATERIAL APLICADO EN SU ESTADO DE FUSION A UNA TEMPERATURA MINIMA DE 204 C, LA SUPERFICIE DE CONCRETO O ASFALTO NO DEBE PRESENTAR UNA TEMPERATURA MENOR A LOS 10 C, ;TIEMPO DE SECADO EN RANGOS DE TEMPERATURA DE 10 C DEL SUSTRATO 2 MINUTOS, Y NO MAS DE 10 MINUTOS CUANDO EL SUSTRATO OSCILA ALREDEDOR DE 54C, TRAZO, ENMASCARILLADO, MANO DE OBRA, LIMPIEZA PREVIA Y FINAL DE SUPERFICIE, EQUIPO NECESARIO PARA SU EJECUCIÓN, Y TODO LO NECESARIO PARA SU CORRECTA EJECUCIÓN, TRABAJO TERMINADO.	ML	3055.8	$41.59	$127,090.72
5	SUMINISTRO Y APLICACIÓN DE PINTURA TERMOPLASTICA ALQUIDALICA DE 120 MILESIMAS DE " (in) EN RAYA GUIA EN ZONAS DE TRANSICION CLASIFICACIÓN M - 4, PARA INDICAR LÍNEA GUÍA EN ZONA DE TRANSICIÓN DE FRENTE EN PISO, DESARROLLO DE 2.00 X 0.10 MTS, CON UNA SEPARACIÓN DE 4.00 MTS ENTRE SI PROMEDIO, A BASE DE PINTURA PARA TRAFICO COLOR BLANCO CON MICRO ESFERA SEGÚN MANUAL DE SEÑALIZACIÓN VIAL Y DISPOSITIVOS DE SEGURIDAD SICT (S.C.T)., MCA. COMEX O SIMILAR, SECADO AL TACTO EN 5 MIN Y AL DURO EN 30 MIN.INCLUYE: MATERIALES Y ESPECIFICACIONES QUE CUMPLAN CON LA NORMATIVA N-CMT-5-01-001/13, N-PRY-CAR-10-01-002/13 APLICADAS AL DIA DE HOY, MATERIAL APLICADO EN SU ESTADO DE FUSION A UNA TEMPERATURA MINIMA DE 204 C, LA SUPERFICIE DE CONCRETO O ASFALTO NO DEBE PRESENTAR UNA TEMPERATURA MENOR A LOS 10 C, ;TIEMPO DE SECADO EN RANGOS DE TEMPERATURA DE 10 C DEL SUSTRATO 2 MINUTOS, Y NO MAS DE 10 MINUTOS CUANDO EL SUSTRATO OSCILA ALREDEDOR DE 54C, TRAZO, ENMASCARILLADO, MANO DE OBRA, LIMPIEZA PREVIA Y FINAL DE SUPERFICIE, EQUIPO NECESARIO PARA SU EJECUCIÓN, Y TODO LO NECESARIO PARA SU CORRECTA EJECUCIÓN, TRABAJO TERMINADO.	ML	92.7	$41.59	$3,855.39
6	SUMINISTRO Y APLICACIÓN DE PINTURA TERMOPLASTICA ALQUIDALICA DE 120 MILESIMAS DE " (in) EN RAYA DE ALTO CLASIFICACIÓN M - 6, PARA INDICAR ALTO EN CRUCEROS, COLOR BLANCO, REFLEJANTE CON MICRO ESFERA DE VIDRIO EN PROPORCIÓN SEGÚN MANUAL DE SEÑALIZACIÓN VIAL Y DISPOSITIVOS DE SEGURIDAD SICT (S.C.T). DE 0.60 MTS DE ANCHO DE LONGITUD VARIABLE, INCLUYE: MATERIALES Y ESPECIFICACIONES QUE CUMPLAN CON LA NORMATIVA N-CMT-5-01-001/13, N-PRY-CAR-10-01-002/13 APLICADAS AL DIA DE HOY, MATERIAL APLICADO EN SU ESTADO DE FUSION A UNA TEMPERATURA MINIMA DE 204 C, LA SUPERFICIE DE CONCRETO O ASFALTO NO DEBE PRESENTAR UNA TEMPERATURA MENOR A LOS 10 C, ;TIEMPO DE SECADO EN RANGOS DE TEMPERATURA DE 10 C DEL SUSTRATO 2 MINUTOS, Y NO MAS DE 10 MINUTOS CUANDO EL SUSTRATO OSCILA ALREDEDOR DE 54C, TRAZO, ENMASCARILLADO, MANO DE OBRA, LIMPIEZA PREVIA Y FINAL DE SUPERFICIE, EQUIPO NECESARIO PARA SU EJECUCIÓN, Y TODO LO NECESARIO PARA SU CORRECTA EJECUCIÓN, TRABAJO TERMINADO.	ML	43.4	$209.24	$9,081.02

Obra: **SEÑALIZACIÓN AV. JOSÉ MARÍA CHÁVEZ, AMBAS CALZADAS**

Ubicación: **TRAMO: ENTRE AV. AGUASCALIENTES SUR Y AV. SIGLO XXI, AGUASCALIENTES Mpio.**

Contratista: **CONSTRUCTORA INTEGRAL DE AGUASCALIENTES, S.A. DE C.V. (471)**

No.	Concepto	Unidad	Cantidad	Precio Unitario	Importe Total
	GRUPO: **SEÑALIZACION**				
	PARTIDA: **SEÑALIZACION HORIZONTAL**				
7	SUMINISTRO Y APLICACIÓN DE PINTURA TERMOPLASTICA ALQUIDALICA DE 120 MILESIMAS DE " (in) EN RAYA PARA CRUCE PEATONAL CLASIFICACIÓN M - 7.1, PARA INDICAR " CRUCE PEATONAL EN VIAS PRIMARIAS", COLOR AMARILLO, REFLEJANTE CON MICRO ESFERA DE VIDRIO EN PROPORCIÓN SEGÚN MANUAL DE SEÑALIZACIÓN VIAL Y DISPOSITIVOS DE SEGURIDAD SICT (S.C.T). DE 0.40 MTS DE ANCHO Y 3.5 MTS. DE LONGITUD POR EL ANCHO DE LA VIALIDAD, CON UNA SEPARACIÓN DE 0.40 MTS. ENTRE ELLAS, INCLUYE: MATERIALES Y ESPECIFICACIONES QUE CUMPLAN CON LA NORMATIVA N-CMT-5-01-001/13, N-PRY-CAR-10-01-002/13 APLICADAS AL DIA DE HOY, MATERIAL APLICADO EN SU ESTADO DE FUSION A UNA TEMPERATURA MINIMA DE 204 C, LA SUPERFICIE DE CONCRETO O ASFALTO NO DEBE PRESENTAR UNA TEMPERATURA MENOR A LOS 10 C, ;TIEMPO DE SECADO EN RANGOS DE TEMPERATURA DE 10 C DEL SUSTRATO 2 MINUTOS, Y NO MAS DE 10 MINUTOS CUANDO EL SUSTRATO OSCILA ALREDEDOR DE 54C, TRAZO, ENMASCARILLADO, MANO DE OBRA, LIMPIEZA PREVIA Y FINAL DE SUPERFICIE, EQUIPO NECESARIO PARA SU EJECUCIÓN, Y TODO LO NECESARIO PARA SU CORRECTA EJECUCIÓN, TRABAJO TERMINADO.	M2	176.23	$451.03	$79,485.02
8	SUMINISTRO Y APLICACIÓN DE PINTURA TERMOPLASTICA ALQUIDALICA DE 120 MILESIMAS DE " (in) EN FLECHAS CLASIFICACIÓN M - 11.1, "FLECHA SENCILLA" PARA INDICAR SENTIDO DE CIRCULACIÓN , EN VIALIDADES PARA VELOCIDAD MENOR A 60KM POR HORA DIMENSION NORMATIVA SEGUN MANUAL DE SEÑALIZACIÓN VIAL Y DISPOSITIVOS DE SEGURIDAD SICT (SCT) Y/O (VER PLANO DE SEÑALAMIENTOS), COLOR BLANCO, REFLEJANTE CON MICRO ESFERA DE VIDRIO EN PROPORCIÓN SEGÚN NORMA SCT, INCLUYE: MATERIALES Y ESPECIFICACIONES QUE CUMPLAN CON LA NORMATIVA N-CMT-5-01-001/13, N-PRY-CAR-10-01-002/13 APLICADAS AL DIA DE HOY, MATERIAL APLICADO EN SU ESTADO DE FUSION A UNA TEMPERATURA MINIMA DE 204 C, LA SUPERFICIE DE CONCRETO O ASFALTO NO DEBE PRESENTAR UNA TEMPERATURA MENOR A LOS 10 C, ;TIEMPO DE SECADO EN RANGOS DE TEMPERATURA DE 10 C DEL SUSTRATO 2 MINUTOS, Y NO MAS DE 10 MINUTOS CUANDO EL SUSTRATO OSCILA ALREDEDOR DE 54C, TRAZO, ENMASCARILLADO, MANO DE OBRA, LIMPIEZA PREVIA Y FINAL DE SUPERFICIE, EQUIPO NECESARIO PARA SU EJECUCIÓN, Y TODO LO NECESARIO PARA SU CORRECTA EJECUCIÓN, TRABAJO TERMINADO.	PZA	30	$636.75	$19,102.50
9	SUMINISTRO Y APLICACIÓN DE PINTURA TERMOPLASTICA ALQUIDALICA DE 120 MILESIMAS DE " (in) EN FLECHAS CLASIFICACIÓN M - 11.1, " FLECHA CABEZA DOBLE" PARA INDICAR SENTIDO DE CIRCULACIÓN (VUELTA IZQUIERDA O DERECHA), EN VIALIDADES PARA VELOCIDAD MENOR A 60KM POR HORA SEGUN MANUAL DE SEÑALIZACIÓN VIAL Y DISPOSITIVOS DE SEGURIDAD SICT (SCT), (VER PLANO DE SEÑALAMIENTOS), EN COLOR BLANCO, REFLEJANTE CON MICRO ESFERA DE VIDRIO EN PROPORCIÓN SEGÚN NORMA SCT, INCLUYE: MATERIALES Y ESPECIFICACIONES QUE CUMPLAN CON LA NORMATIVA N-CMT-5-01-001/13, N-PRY-CAR-10-01-002/13 APLICADAS AL DIA DE HOY, MATERIAL APLICADO EN SU ESTADO DE FUSION A UNA TEMPERATURA MINIMA DE 204 C, LA SUPERFICIE DE CONCRETO O ASFALTO NO DEBE PRESENTAR UNA TEMPERATURA MENOR A LOS 10 C, ;TIEMPO DE SECADO EN RANGOS DE TEMPERATURA DE 10 C DEL SUSTRATO 2 MINUTOS, Y NO MAS DE 10 MINUTOS CUANDO EL SUSTRATO OSCILA ALREDEDOR DE 54C, TRAZO, ENMASCARILLADO, MANO DE OBRA, LIMPIEZA PREVIA Y FINAL DE SUPERFICIE, EQUIPO NECESARIO PARA SU EJECUCIÓN, Y TODO LO NECESARIO PARA SU CORRECTA EJECUCIÓN, TRABAJO TERMINADO.	PZA	3	$766.77	$2,300.31

Obra: **SEÑALIZACIÓN AV. JOSÉ MARÍA CHÁVEZ, AMBAS CALZADAS**

Ubicación: **TRAMO: ENTRE AV. AGUASCALIENTES SUR Y AV. SIGLO XXI, AGUASCALIENTES Mpio.**

Contratista: **CONSTRUCTORA INTEGRAL DE AGUASCALIENTES, S.A. DE C.V. (471)**

No.	Concepto	Unidad	Cantidad	Precio Unitario	Importe Total
	GRUPO: **SEÑALIZACION**				
	PARTIDA: **SEÑALIZACION HORIZONTAL**				
10	DESMONTAJE Y RETIRO MANUAL DE VIALETA EXISTENTE (SOLAR O ESTANDAR) CON RECUPERACION Y TRASLADO A PARQUE Y MAQUINARIA DE SOPMA, INCLUYE: IDENTIFICACIÓN, MANO DE OBRA, CARGAS Y ACARREOS, LOCALES Y A KILOMETROS SUBSECUENTES, LIMPIEZA DE SUPERFICIE CON CEPILLO DE ALAMBRE Y HOJA LAMINADA, PARA RECIBIR VIALETA NUEVA, EQUIPO NECESARIO PARA SU EJECUCIÓN, TRABAJO TERMINADO.	PZA	602.12	$24.56	$14,788.07
11	SUMINISTRO Y COLOCACION DE VIALETA STANDARD (S-200) DE 10X10CM. COLOR: CUERPO AMARILLO Y REFLEJANTE AMARILLO 1 CARA MARCA SEA O SIMILAR EN CALIDAD Y ESPECIFICACIONES DE FICHA TECNICA, ANCLADO EN PAVIMENTO SISTEMA DE SUJECION DE ALTO AGARRE BASE CUÑAS CON AB PEGAMENTO EPOXICO 50/50 RESISTENTE A ALTA TEMPERATURA (VER PLANO DE DETALLES DE SEÑALAMIENTOS HORIZONTAL Y VERTICAL). INCLUYE: TRAZO, ALINEACION, ELEVACION CUALQUIER ALTURA, TRABAJO TERMINADO, LIMPIEZAS.	PZA	408	$54.04	$22,048.32
12	SUMINISTRO Y COLOCACION DE VIALETA SOLAR DE 10X10CM. COLOR: CUERPO ALUMINIO 3 LED DOS CARAS REFLEJANTES MARCA CREATIVAL VT-29 O SIMILAR EN CALIDAD Y ESPECIFICACIONES DE FICHA TÉCNICA, FIJADO EN PAVIMENTO CON SISTEMA DE SUJECIÓN DE ALTO AGARRE PEGAMENTO EPOXICO 100 A/B (RESINA EPÓXICA/RESINA POLIAMIDA MODIFICADA), RESISTENTE A ALTA TEMPERATURA (VER PLANO DE DETALLES DE SEÑALAMIENTOS HORIZONTAL), INCLUYE: LIMPIEZA PREVIA DE LA SUPERFICIE+C92, PREPARACIÓN DE LA SUPERFICIE, TRAZO, ALINEACIÓN, Y TODO LO NECESARIO PARA SU CORRECTA EJECUCIÓN, TRABAJO TERMINADO.	PZA	194	$633.26	$122,852.44
13	SUMINISTRO Y APLICACIÓN DE PINTURA TERMOPLASTICA ALQUIDALICA DE 120 MILESIMAS DE " EN LETRAS Y NUMEROS CLASIFICACIÓN M - 11.2 "FLECHA SIN CUERPO" PARA ESTABLECER LUGARES DE PARADA, (VER PLANO DE SEÑALAMIENTOS) COLOR BLANCO, REFLEJANTE CON MICRO ESFERA DE VIDRIO EN PROPORCIÓN SEGÚN NORMA SCT DE (VER DETALLES EN PLANOS) INCLUYE: MATERIALES Y ESPECIFICACIONES QUE CUMPLAN CON LA NORMATIVA N-CMT-5-01-001/05, N-PRY-CAR-10-01-002/13 APLICADAS AL DIA DE HOY, MATERIAL APLICADO EN SU ESTADO DE FUSION A UNA TEMPERATURA MINIMA DE 204 C, LA SUPERFICIE DE CONCRETO O ASFALTO NO DEBE PRESENTAR UNA TEMPERATURA MENOR A LOS 10 C, ;TIEMPO DE SECADO EN RANGOS DE TEMPERATURA DE 10 C DEL SUSTRATO 2 MINUTOS, Y NO MAS DE 10 MINUTOS CUANDO EL SUSTRATO OSCILA ALREDEDOR DE 54C, TRAZO, ENMASCARILLADO, MANO DE OBRA, LIMPIEZA PREVIA Y FINAL DE SUPERFICIE, EQUIPO NECESARIO PARA SU EJECUCIÓN, Y TODO LO NECESARIO PARA SU CORRECTA EJECUCIÓN, TRABAJO TERMINADO.	PZA	3	$717.98	$2,153.94
14	SUMINISTRO Y APLICACIÓN DE PINTURA TERMOPLASTICA ALQUIDALICA DE 120 MILESIMAS DE " EN LETRAS Y NUMEROS CLASIFICACIÓN M - 11.2 "LEYENDA SOLO BUS" PARA VELOCIDAD MENOR A 60KM POR HORA DIFERENTES DIMENSIONES (VER PLANO DE SEÑALAMIENTOS) COLOR BLANCO, REFLEJANTE CON MICRO ESFERA DE VIDRIO EN PROPORCIÓN SEGÚN NORMA SCT DE (VER DETALLES EN PLANOS) INCLUYE: MATERIALES Y ESPECIFICACIONES QUE CUMPLAN CON LA NORMATIVA N-CMT-5-01-001/05, N-PRY-CAR-10-01-002/13 APLICADAS AL DIA DE HOY, MATERIAL APLICADO EN SU ESTADO DE FUSION A UNA TEMPERATURA MINIMA DE 204 C, LA SUPERFICIE DE CONCRETO O ASFALTO NO DEBE PRESENTAR UNA TEMPERATURA MENOR A LOS 10 C, ;TIEMPO DE SECADO EN RANGOS DE TEMPERATURA DE 10 C DEL SUSTRATO 2 MINUTOS, Y NO MAS DE 10 MINUTOS CUANDO EL SUSTRATO OSCILA ALREDEDOR DE 54C, TRAZO, ENMASCARILLADO, MANO DE OBRA, LIMPIEZA PREVIA Y FINAL DE SUPERFICIE, EQUIPO NECESARIO PARA SU EJECUCIÓN, Y TODO LO NECESARIO PARA SU CORRECTA EJECUCIÓN, TRABAJO TERMINADO.	PZA	1	$2,547.16	$2,547.16

Obra: SEÑALIZACIÓN AV. JOSÉ MARÍA CHÁVEZ, AMBAS CALZADAS

Ubicación: TRAMO: ENTRE AV. AGUASCALIENTES SUR Y AV. SIGLO XXI, AGUASCALIENTES Mpio.

Contratista: CONSTRUCTORA INTEGRAL DE AGUASCALIENTES, S.A. DE C.V. (471)

No.	Concepto	Unidad	Cantidad	Precio Unitario	Importe Total
	GRUPO: SEÑALIZACION				
	PARTIDA: SEÑALIZACION HORIZONTAL				
15	SUMINISTRO Y APLICACIÓN DE PINTURA TERMOPLASTICA ALQUIDALICA DE 120 MILESIMAS DE " EN LETRAS Y NUMEROS CLASIFICACIÓN M - 11.4 "L INVERTIDA" PARA ESTABLECER LUGAR DE PARADA CUYO LADO MAYOR EN UNA LÍNEA DE 20 CM DE ANCHO POR 20 MTS DE LARGO Y SU LADO MENOR EN UNA LÍNEA DE 50 CM DE ANCHO POR EL ANCHO DEL CARRIL, SOBRE PAVIMENTO EN VIALIDADES PARA VELOCIDAD MENOR A 60KM POR HORA DIFERENTES DIMENSIONES (VER PLANO DE SEÑALAMIENTOS) COLOR BLANCO, REFLEJANTE CON MICRO ESFERA DE VIDRIO EN PROPORCIÓN SEGÚN NORMA SCT DE (VER DETALLES EN PLANOS) INCLUYE: MATERIALES Y ESPECIFICACIONES QUE CUMPLAN CON LA NORMATIVA N-CMT-5-01-001/05, N-PRY-CAR-10-01-002/13 APLICADAS AL DIA DE HOY, MATERIAL APLICADO EN SU ESTADO DE FUSION A UNA TEMPERATURA MINIMA DE 204 C, LA SUPERFICIE DE CONCRETO O ASFALTO NO DEBE PRESENTAR UNA TEMPERATURA MENOR A LOS 10 C, ;TIEMPO DE SECADO EN RANGOS DE TEMPERATURA DE 10 C DEL SUSTRATO 2 MINUTOS, Y NO MAS DE 10 MINUTOS CUANDO EL SUSTRATO OSCILA ALREDEDOR DE 54C, TRAZO, ENMASCARILLADO, MANO DE OBRA, LIMPIEZA PREVIA Y FINAL DE SUPERFICIE, EQUIPO NECESARIO PARA SU EJECUCIÓN, Y TODO LO NECESARIO PARA SU CORRECTA EJECUCIÓN, TRABAJO TERMINADO.	PZA	1	$1,656.83	$1,656.83

Totales por Partida		**$948,275.86**
Totales por Grupo		**$948,275.86**
Totales Presup.		**$948,275.86**
Anticipo	**+**	**$0.00**
Amortizac. Ant.	**-**	**$0.00**
SubTotal. Ant.	**=**	**$948,275.86**
IVA	**+**	**$151,724.14**
Total	**=**	**$1,100,000.00**

H. AYUNTAMIENTO CONSTITUCIONAL DEL MUNICIPIO DE AGUASCALIENTES 2021-2024

PRESUPUESTO MODIFICADO

Aguascalientes
LA CIUDAD DE SU VIDA

Obra: SEÑALIZACIÓN AV. JOSÉ MARÍA CHÁVEZ, AMBAS CALZADAS

Ubicación: TRAMO: ENTRE AV. AGUASCALIENTES SUR Y AV. SIGLO XXI, AGUASCALIENTES Mpio.

Contratista: CONSTRUCTORA INTEGRAL DE AGUASCALIENTES, S.A. DE C.V. (471)

Grupo	Partida	Importe
SEÑALIZACION		
	SEÑALIZACION HORIZONTAL	$948,275.86
	Subtotal por Grupo	**$948,275.86**

Totales Presup.		$948,275.86
Anticipo	+	$0.00
Amortizac. Ant.	-	$0.00
SubTotal. Ant.	=	$948,275.86
IVA	+	$151,724.14
Total	=	$1,100,000.00

H. AYUNTAMIENTO CONSTITUCIONAL DEL MUNICIPIO DE AGUASCALIENTES 2021-2024

H. AYUNTAMIENTO DE AGUASCALIENTES

SECRETARÍA DE OBRAS PÚBLICAS

DIRECCIÓN DE SUPERVISIÓN DE OBRA

Aguascalientes
LA CIUDAD DE TU VIDA


MEMORIA FOTOGRAFICA

OBRA:	SEÑALIZACION AV. JOSÉ MARIA CHAVEZ, AMBAS CALZADAS, TRAMO: ENTRE AV. AGUASCALEINTES SUR Y AV. SIGLO XXI, AGUASCALEINTES Mpio.					
NO. DE CONTRATO:	FISMDF-0140-2022		CONTRATISTA:	CONSTRUCTORA INTEGRAL DE AGUASCALIENTES, S.A. DE C.V.		

INICIO.





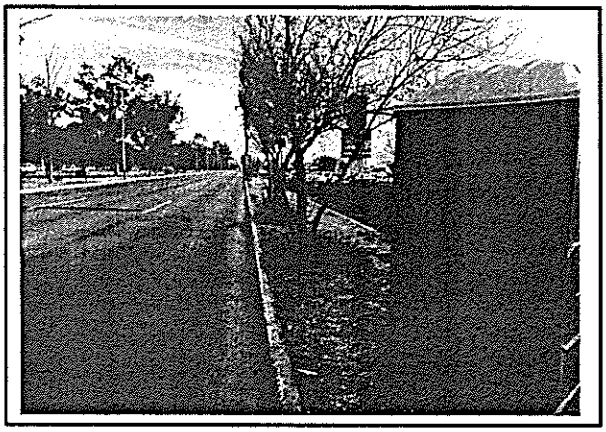



ING. DAVID ALONSO MONTOYA
SUPERVISOR DE OBRA.

H. AYUNTAMIENTO CONSTITUCIONAL DEL MUNICIPIO DE AGUASCALIENTES 2021-2024

H. AYUNTAMIENTO DE AGUASCALIENTES

SECRETARÍA DE OBRAS PÚBLICAS

DIRECCIÓN DE SUPERVISIÓN DE OBRA

Aguascalientes
LA CIUDAD DE TU VIDA

MEMORIA FOTOGRAFICA


OBRA:	SEÑALIZACION AV. JOSÉ MARIA CHAVEZ, AMBAS CALZADAS, TRAMO: ENTRE AV. AGUASCALEINTES SUR Y AV. SIGLO XXI, AGUASCALEINTES Mpio.					
NO. DE CONTRATO:	FISMDF-0140-2022		CONTRATISTA:	CONSTRUCTORA INTEGRAL DE AGUASCALIENTES, S.A. DE C.V.		

PROCESO







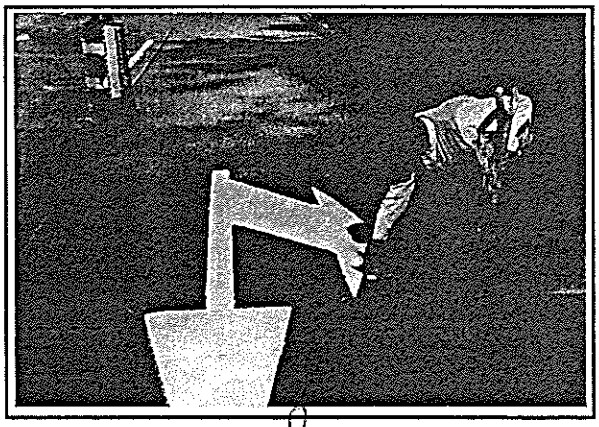

ING. DAVID ALONSO MONTOYA
SUPERVISOR DE OBRA.

H. AYUNTAMIENTO CONSTITUCIONAL DEL MUNICIPIO DE AGUASCALIENTES 2021-2024

H. AYUNTAMIENTO DE AGUASCALIENTES

SECRETARÍA DE OBRAS PÚBLICAS


DIRECCIÓN DE SUPERVISIÓN DE OBRA


Aguascalientes
LA CIUDAD DE TU VIDA


MEMORIA FOTOGRAFICA

OBRA:	SEÑALIZACION AV. JOSÉ MARIA CHAVEZ, AMBAS CALZADAS, TRAMO: ENTRE AV. AGUASCALEINTES SUR Y AV. SIGLO XXI, AGUASCALEINTES Mpio.					
NO. DE CONTRATO:	FISMDF-0140-2022		CONTRATISTA:	CONSTRUCTORA INTEGRAL DE AGUASCALIENTES, S.A. DE C.V.		

TERMINO

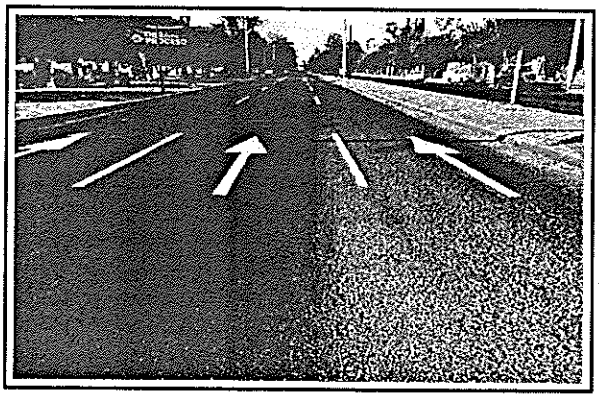

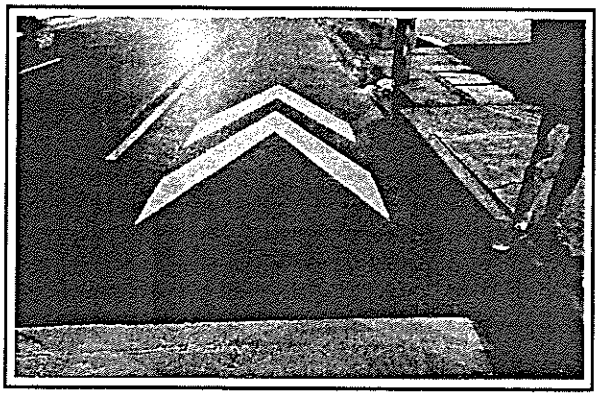

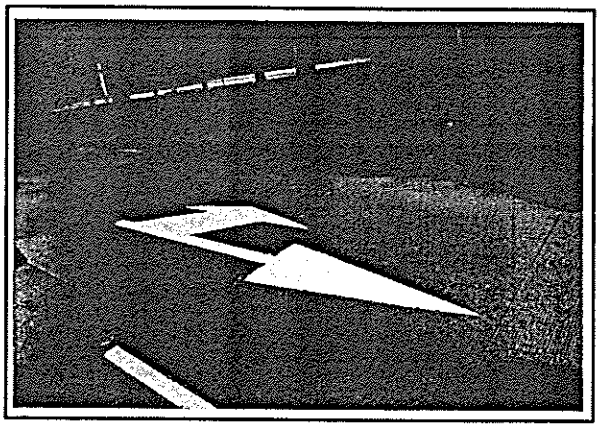



ING. DAVID ALONSO MONTOYA
SUPERVISOR DE OBRA.

SECRETARÍA DE OBRAS PÚBLICAS

DIRECCIÓN DE SUPERVISIÓN DE OBRA

EJERCICIO 2022

N° DE CONTRATO: FISMDF-0140-2022


NOMBRE DE LA OBRA: SEÑALIZACION AV. JOSÉ MARIA CHAVEZ, AMBAS CALZADAS, TRAMO: ENTRE AV. AGUASCALEINTES SUR Y AV. SIGLO XXI, AGUASCALEINTES Mpio.


MONTO MODIFICADO FINAL: $ 1,100,000.00

VOLUMEN	UNIDAD	COMPONENTE DE LA OBRA	MONTO
5891.30	ML	SUMINISTRO Y APLICACIÓN DE PINTURA BASE SOLVENTE PARA MARCAS EN GUARNICIONES CLASIFICACION M-12.1, M12.2 APLICADA SOBRE GUARNICIONES Y DENTELLONES DE CUALQUIER COLOR, SEGÚN SE REQUIERA Y SEGÚN NORMA S.C.T. SECADO AL TACTO EN 5 MIN Y AL DURO EN 30 MIN CON MICRO ESFERA, DESARROLLO DE	$ 948,275.86
			$ -
			$ -

TOTAL PRESUP.	$	948,275.86
IVA	$	151,724.14
TOTAL	$	1,100,000.00

NOMBRE DEL SUPERVISOR: ING. DAVID ALONSO MONTOYA

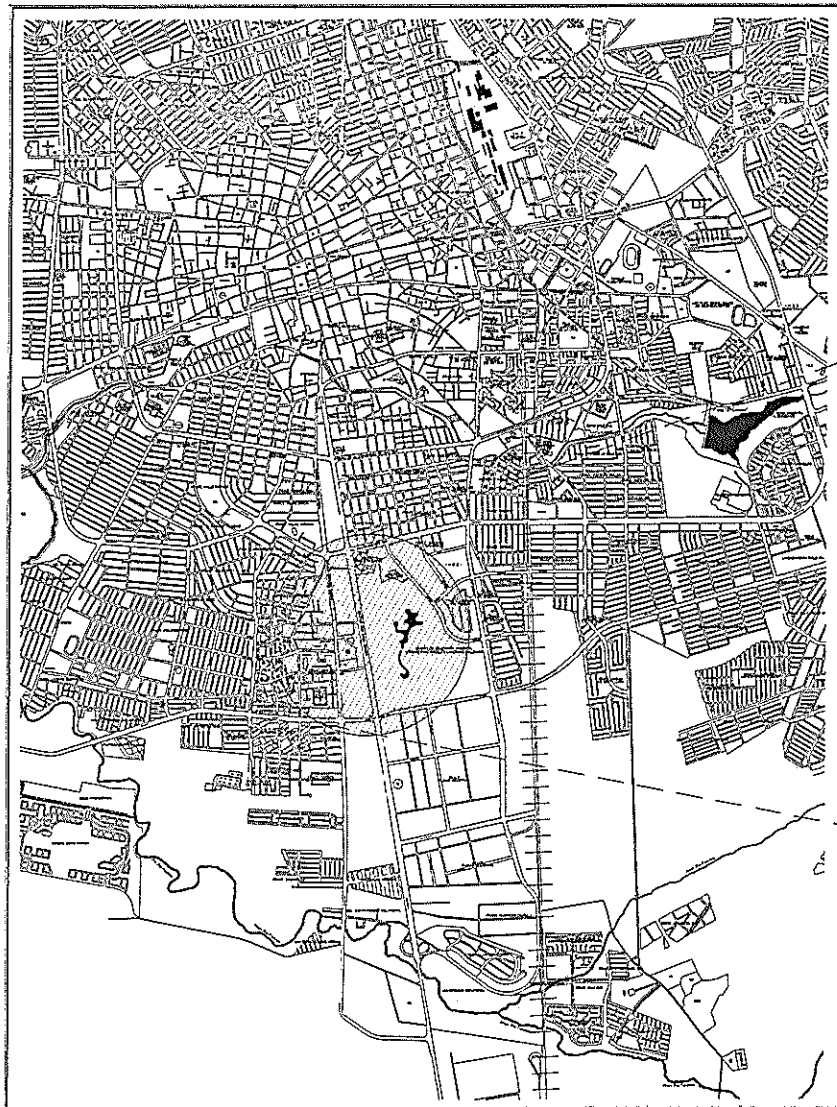


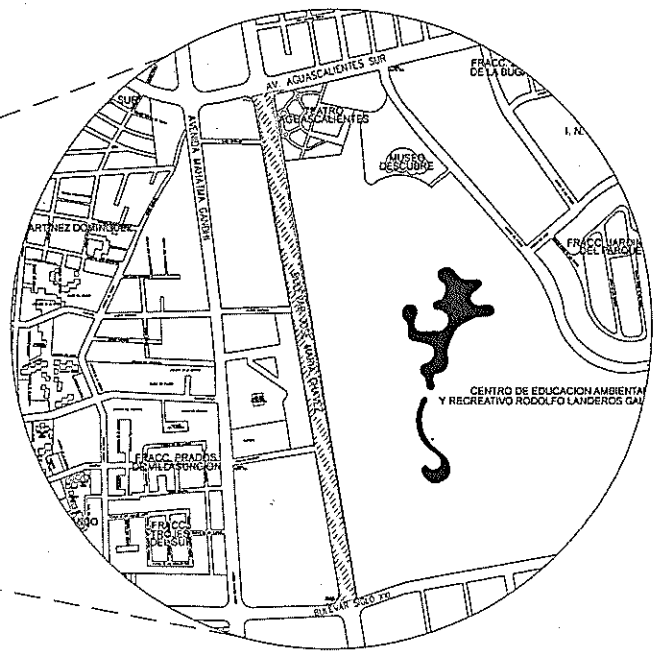

CROQUIS DE LOCALIZACIÓN

SIN ESCALA


AV. JOSÉ MARÍA CHÁVEZ

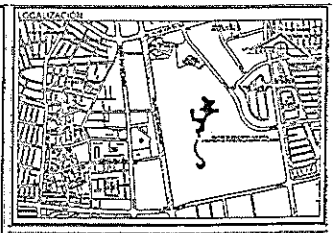

SIMBOLOGÍA

La Dirección de Planeación y Proyectos solo autoriza el proyectoejecutivo, no es responsable de la correcta ejecución de la obra. Este documento no tiene validez si no presenta las firmas de los responsables parasu autorización, así como los sellos respectivos.

PRESIDENTE MUNICIPAL M.P.P. Leonardo Montañez Castro SECRETARIO DE OBRAS PÚBLICAS Ing. Miguel Ángel Huizar Botello	REV. FECHA OBSERVACIONES	Vo. Bo. DE LA DEPENDENCIA	RESP. DE PROY. EXTERNO CED. PROFESIONAL PROYECTO / REVISO / AUTORIZÓ	LOGO EXTERNO	Dirección de Planeación y Proyectos de Obra / Secretaría de Obras Públicas PROYECTISTA / COORDINADOR ARQ. ALEJANDRO JAIME LEAL DIRECTOR	PROYECTO SEÑALÉTICA HORIZONTAL AV. JOSÉ MARÍA CHÁVEZ AMBAS CALZADAS UBICACIÓN TRAMO DE AV. AGUASCALIENTES CALZADA SUR A AV. SIGLO XXI CALZADA NORTE CONTENIDO CROQUIS DE LOCALIZACIÓN	CLAVE LOC 01 FECHA NOV 2022 ACOTACIÓN METROS	No. PLANO 01 ESCALA INDICADA No. EXP. E-000-22	Aguascalientes LA CIUDAD DE TU VIDA

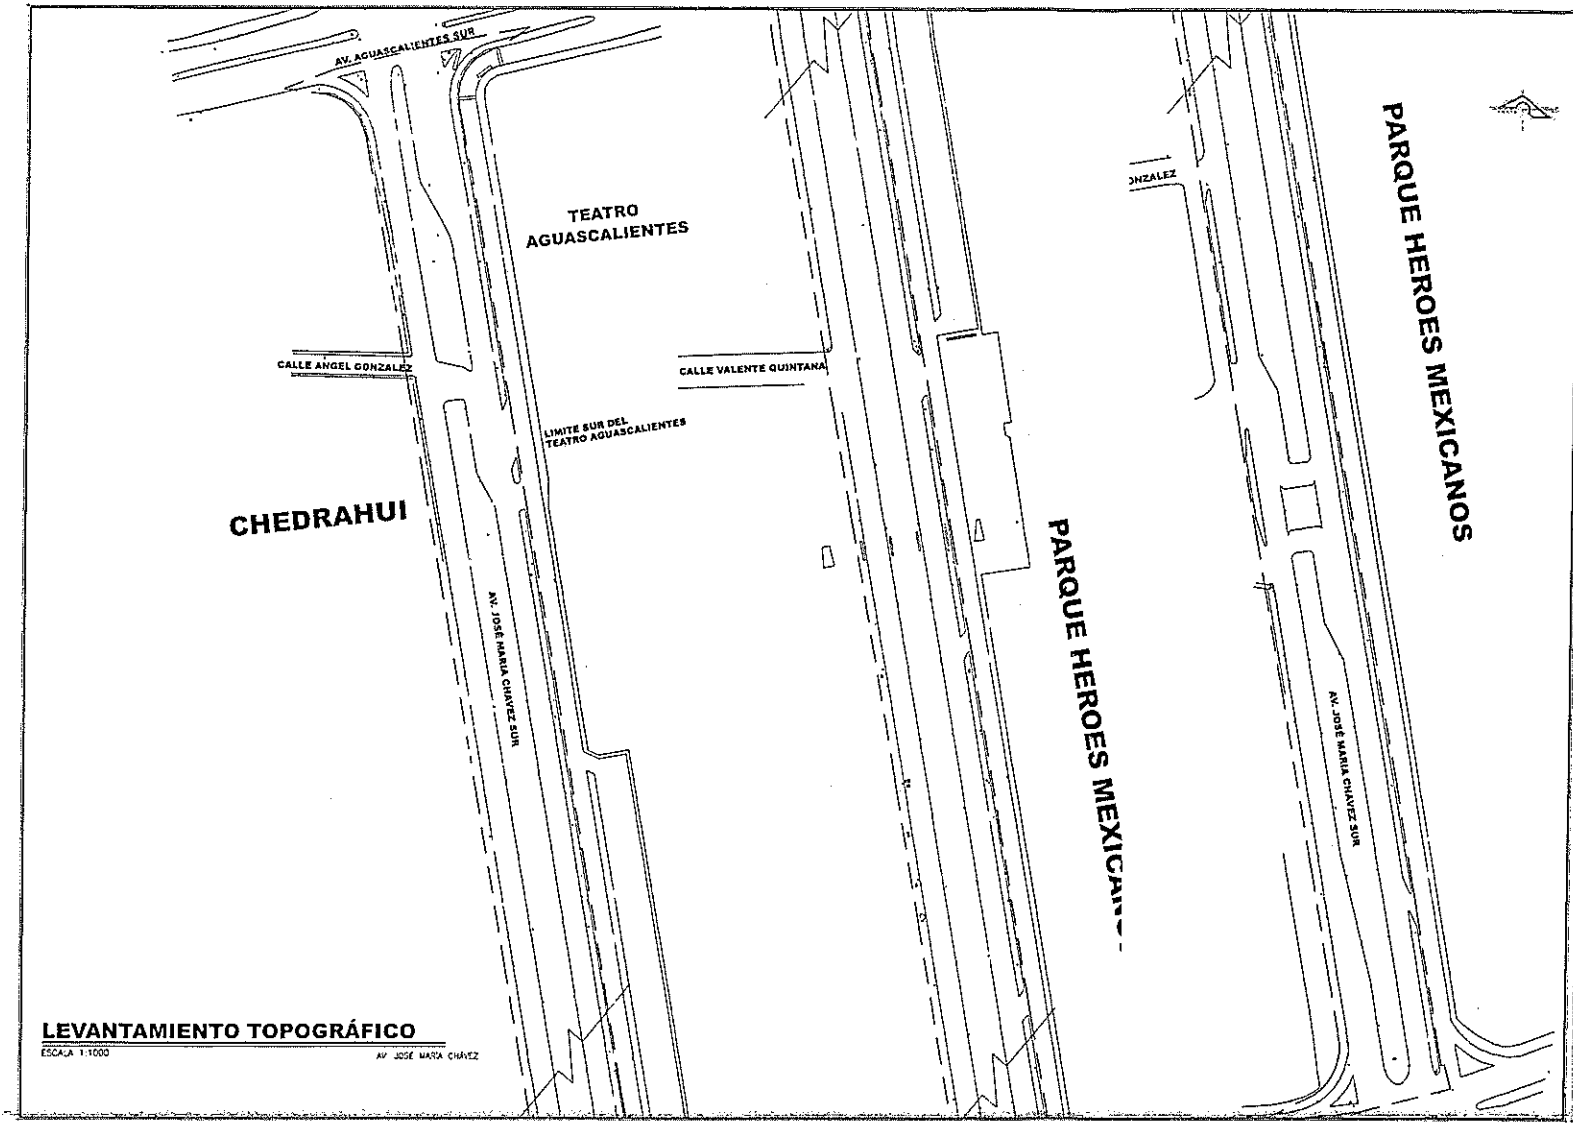


LEVANTAMIENTO TOPOGRÁFICO

ESCALA 1:1000

AV. JOSÉ MARIA CHAVEZ

LOCALIZACIÓN

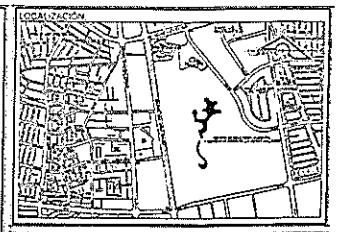

SIMBOLOGÍA

SIMBOLOGIA

- LIMITE DE PROYECTO
- LUM — POSTE LUMINARIA
- CFE — POSTE DE CFE
- TEL — POSTE DE TELMEX
- REG — REGISTRO
- POST — POSTE
- REGISTROS CFE
- REGISTRO SEMAFORO
- REGISTROS TELMEX
- TELEFONO — TELEFONO
- POZO DE VISITA
- CAJA DE VALVULAS
- SEMAFOROS
- CAIMAN — CAIMANES
- ANUNCIO — ANUNCIO
- RETENIDA POS — RETENIDA POSTE

La Dirección de Planeación y Proyectos solo autoriza el proyectoejecutivo, no es responsable de la correcta ejecución de la obra. Este documento no tiene validez si no presenta las firmas de los responsables para su autorización, así como los sellos respectivos.

PRESIDENTE MUNICIPAL
M.P.P. Leonardo Montañez Castro
SECRETARIO DE OBRAS PÚBLICAS
Ing. Miguel Ángel Huizar Botello

REV	FECHA	OBSERVACIONES

Vo. Bo. DE LA DEPENDENCIA

RESP. DE PROY. EXTERNO		LOGO EXTERNO
CED. PROFESIONAL		
PROYECTÓ	REVISÓ	AUTORIZÓ

Dirección de Planeación y Proyectos de Obra — Secretaría de Obras Públicas

PROYECTISTA	COORDINADOR
APO ALVA ORTEGA CONTRERAS	ARQ. ALEJANDRO JAIME LEAL
JEFE DE DEP.	DIRECTOR
LIC. OSCAR ALEJANDRO LUNA GARCIA	ARQ. ALEJANDRO JAIME LEAL


PROYECTO
SEÑALETICA HORIZONTAL AV. JOSÉ MARIA CHAVEZ AMBAS CALZADAS

UBICACIÓN
TRAMO DE AV. AGUASCALIENTES CALZADA SUR A AV. SIGLO XXI CALZADA NORTE

CONTENIDO
LEVANTAMIENTO TOPOGRAFICO

CLAVE	No. PLANO
LEV 01	02
FECHA NOV 2022	ESCALA INDICADA
ACOTACIÓN METROS	No EXP E-000-22


Aguascalientes
LA CIUDAD DE TU VIDA

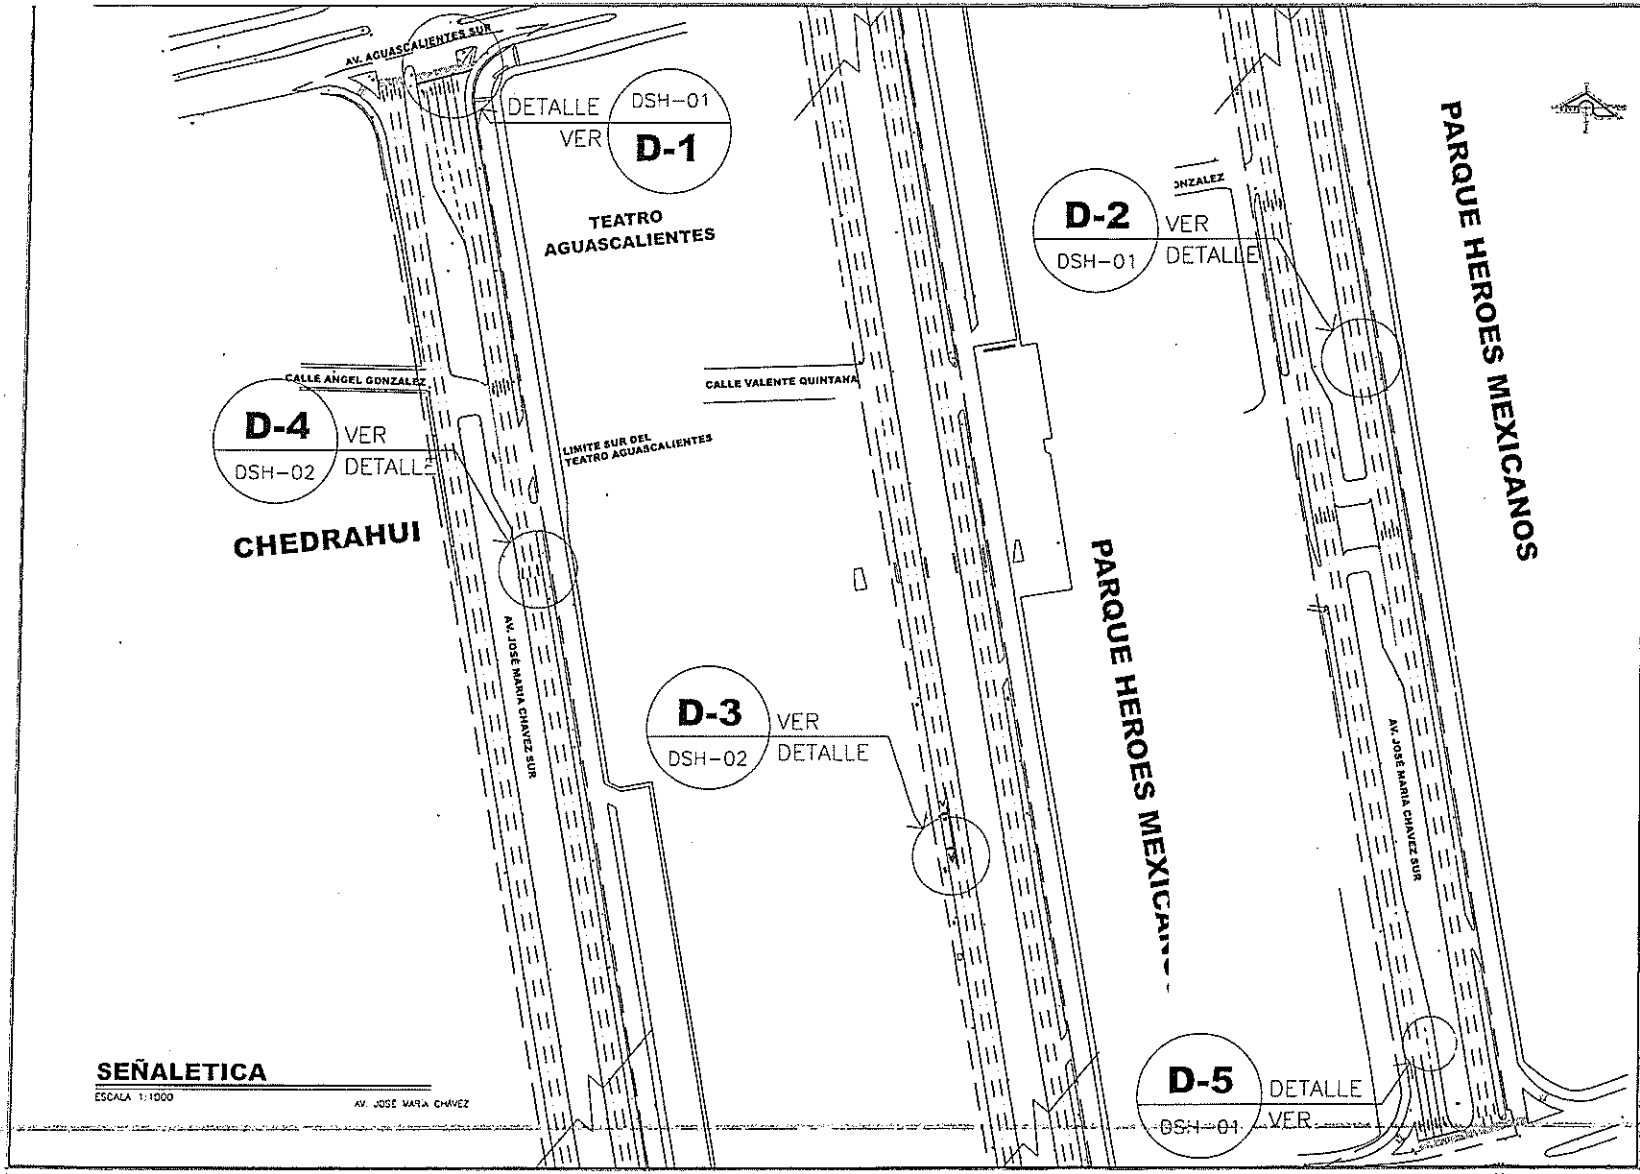

SEÑALETICA

ESCALA 1:1000

LOCALIZACIÓN:

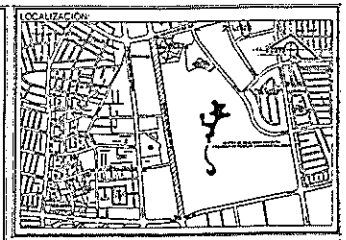

SIMBOLOGÍA

NOTA:
Se aplicará en todos los señalamientos horizontales pintura para trafico base solvente tipo alquidal de secado rápido, que cumpla con las especificaciones n-cmt-5-01-001/05, n-pry-cer-10-01-002/13 de la SCT aplicadas al día de hoy.

M-12.1, M12.2 APLICADA SOBRE GUARNICIONES Y DENTELLONES DE CUALQUIER COLOR

Se aplicará en todos los señalamientos horizontales pintura para trafico Termoplastica tipo alquidal de secado rápido, que cumpla con las especificaciones n-cmt-5-01-001/05, n-pry-cer-10-01-002/13 de la SCT aplicadas al día de hoy.

M - 1.2, LÍNEA DISCONTINUA SENCILLA DE DIVISIÓN DE CARRILES DE FRENTE EN PISO, DE 10 CM DE ANCHO
M - 3.3, CONTINUA IZQUIERDA, PARA VIALIDADES URBANAS DE FRENTE EN PISO, SEPARADA 15 CM. DE LA GUARNICION, COLOR AMARILLO
M - 4, PARA INDICAR LÍNEA GUÍA EN ZONA DE TRANSICION DE FRENTE EN PISO, DESARROLLO DE 2.00 X 0.10 MTS, CON UNA SEPARACIÓN DE 4.00 MTS ENTRE SI PROMEDIO
M - 5, PARA INDICAR ENTRADA Y SALIDA EN BIFURCACIONES
M - 6, PARA INDICAR ALTO EN CRUCEROS, COLOR BLANCO
M - 7.1, PARA INDICAR " CRUCE PEATONAL EN VIAS PRIMARIAS" COLOR AMARILLO
M - 11.1 "FLECHA SENCILLA" PARA INDICAR SENTIDO DE CIRCULACIÓN
M - 11.1 "FLECHA CABEZA DOBLE" PARA INDICAR SENTIDO DE CIRCULACIÓN (VUELTA IZQUIERDA O DERECHA)

Nota2: Dosificación de micro esfera
La cantidad de esferas de vidrio en la película de pintura en húmedo, según su tipo, será la que se indica en la Tabla.


TABLA 8. Cantidad de esferas de vidrio en la película de pintura en humedo.

TIPO DE PINTURA	ESPESOR DE LA PELÍCULA DE PINTURA EN HÚMEDO MM	CANTIDAD DE ESFERAS KG/M2		TIPO DE GRANULOMETRIA
		INTEGRADAS	SEMBRADAS, MÍNIMO	
BASE SOLVENTE	0.38 A 0.50	---	0.350	I
BASE AGUA	0.38 A 0.50	---	0.350	I o II
TERMOPLASTICA	1.50 A 2.50	0.12 A 0.18	0.350	II

La Dirección de Planeación y Proyectos solo autoriza el proyecto ejecutivo, no es responsable de la correcta ejecución de la obra. Este documento no tiene validez si no presenta las firmas de los responsables para su autorización, así como los sellos respectivos.


PRESIDENTE MUNICIPAL M.P.P. Leonardo Montañez Castro SECRETARIO DE OBRAS PUBLICAS Ing. Miguel Ángel Ruizar Botello	REV. FECHA OBSERVACIONES	No. DE LA REVISIÓN	RESP. DE PROY. EXTERNO	LOGO EXTERNO	Dirección de Planeación y Proyectos de Obra / Secretaría de Obras Públicas	PROYECTO SEÑALETICA HORIZONTAL AV. JOSÉ MARÍA CHÁVEZ AMBAS CALZADAS	CLAVE SEÑ 01	No. PLANO 03
			CED. PROFESIONAL		PROYECTISTA / COORDINACIÓN	UBICACIÓN TRAMO DE AV. AGUASCALIENTES CALZADA SUR A AV. SIGLO XXI CALZADA NORTE	FECHA NOV 2022	ESCALA INDICADA
			PROYECTO / REVISO / AUTORIZO		JEFE DE DEP. / DIRECTOR	CONTENIDO SEÑALETICA.	ACOTACIÓN METROS	No. EXP. E-000-22

Aguascalientes
LA CIUDAD DE TU VIDA

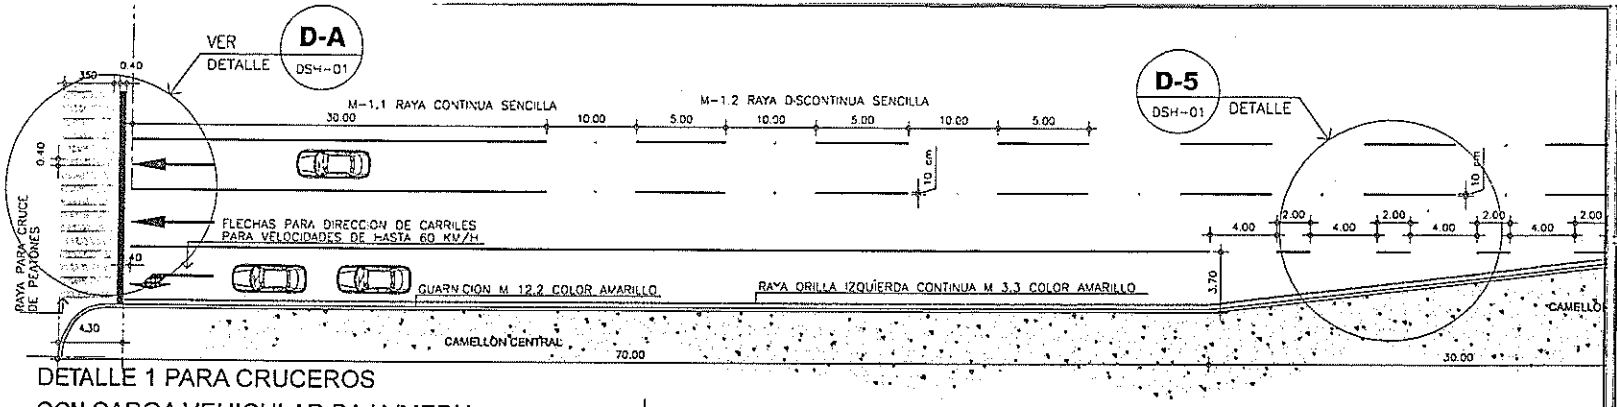


DETALLE 1 PARA CRUCEROS CON CARGA VEHICULAR BAJA/MEDIA

COTAS: cm.

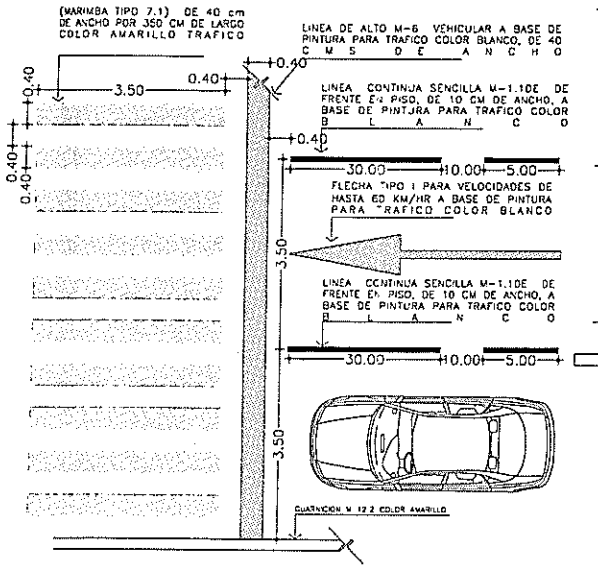

DETALLE A

TRAZO PINTURA EN CRUCEROS SIN ESCALA

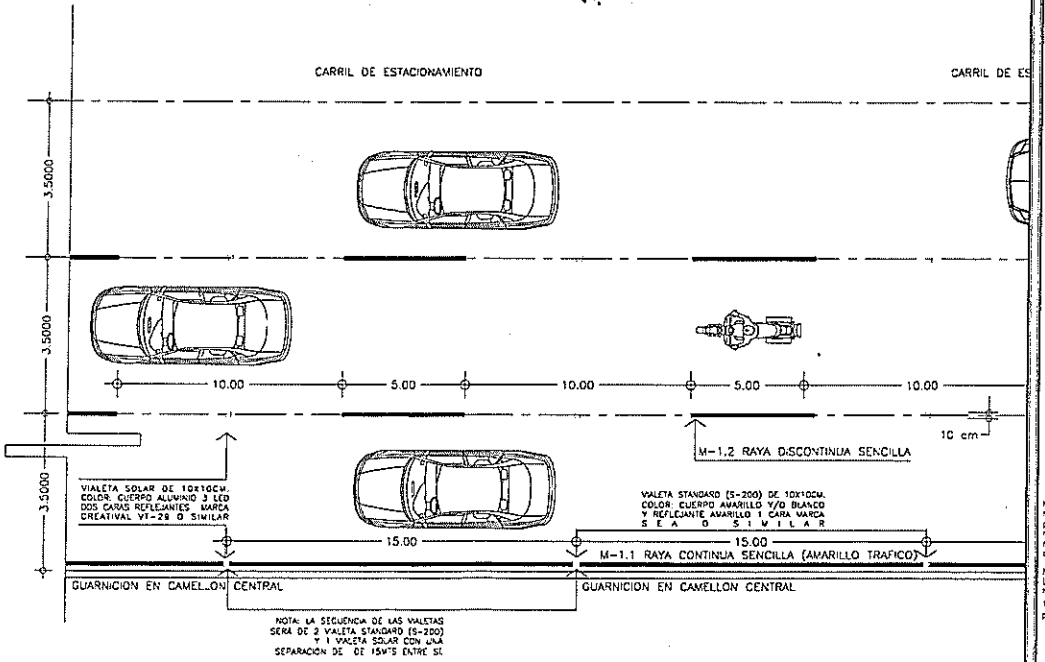


DETALLE 2

PARA VELOCIDADES MENOR A 60 KM/HR S/E

LINEA DISCONTINUA DE 2.50 MTS ESPACIO 5 MTS ESPESOR 10CM

LOCALIZACIÓN

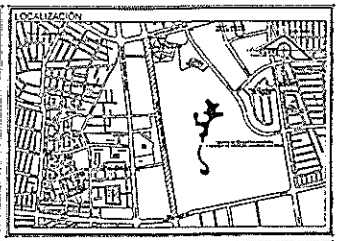

SIMBOLOGÍA

NOTA:
Se aplicará en todos los señalamientos horizontales pintura para trafico base solvente tipo alquidal de secado rápido, que cumpla con las especificaciones n-cmt-5-01-001/05, n-pry-car-10-01-002/13 de la SCT aplicadas al día de hoy.

M-12.1, M12.2 APLICADA SOBRE GUARNICIONES Y DENTELLONES DE CUALQUIER COLOR

Se aplicará en todos los señalamientos horizontales pintura para trafico Termoplastica tipo alquidal de secado rápido, que cumpla con las especificaciones n-cmt-5-01-001/05, n-pry-car-10-01-002/13 de la SCT aplicadas al día de hoy.

M - 1.2, LÍNEA DISCONTINUA SENCILLA DE DIVISIÓN DE CARRILES DE FRENTE EN PISO, DE 10 CM DE ANCHO

M - 3.3, CONTINUA IZQUIERDA, PARA VIALIDADES URBANAS DE FRENTE EN PISO, SEPARADA 15 CM. DE LA GUARNICION, COLOR AMARILLO

M - 4, PARA INDICAR LÍNEA GUÍA EN ZONA DE TRANSICIÓN DE FRENTE EN PISO, DESARROLLO DE 2.00 X 0.10 MTS, CON UNA SEPARACIÓN DE 4.00 MTS ENTRE SI PROMEDIO

M - 5, PARA INDICAR ENTRADA Y SALIDA EN BIFURCACIONES

M - 6, PARA INDICAR ALTO EN CRUCEROS, COLOR BLANCO

M - 7.1, PARA INDICAR " CRUCE PEATONAL EN VIAS PRIMARIAS" COLOR AMARILLO

M - 11.1, "FLECHA SENCILLA" PARA INDICAR SENTIDO DE CIRCULACIÓN

M - 11.1, "FLECHA CABEZA DOBLE" PARA INDICAR SENTIDO DE CIRCULACIÓN (VUELTA IZQUIERDA O DERECHA)

NOTA:
Nota1: Se aplicará en todos los señalamientos horizontales pintura para trafico base solvente tipo alquidal de secado rápido, que cumpla con las especificaciones n-cmt-5-01-001/05, n-pry-car-10-01-002/13 de la SCT aplicadas al día de hoy.

Nota2: Dosificación de micro esfera
La cantidad de esferas de vidrio en la película de pintura en húmedo, según su tipo, será la que se indica en la Tabla.

TABLA 8. Cantidad de esferas de vidrio en la película de pintura en humedo.

TIPO DE PINTURA	ESPESOR DE LA PELICULA DE PINTURA EN HUMEDO mm	CANTIDAD DE ESFERAS kg/m2		TIPO DE GRANULOMETRIA
		INTEGRADAS	SEMBRADAS, MINIMO	
BASE SOLVENTE	0.38 A 0.50	----	0.350	I
BASE AGUA	0.38 A 0.50	----	0.320	IAB
TERMOPLASTICA	1.50 A 0.19	0.57 A 0.69	0.350	II

La Dirección de Planeación y Proyectos, solo autoriza el proyecto ejecutivo, no es responsable de la correcta ejecución de la obra. Este documento no tiene validez si no presenta las firmas de los responsables para su autorización, así como los sellos respectivos.

PRESIDENTE MUNICIPAL
M.P.P. Leonardo Montañez Castro
SECRETARIO DE OBRAS PÚBLICAS
Ing. Miguel Ángel Huizar Botello

REV.	FECHA	OBSERVACIONES

No. De OBRA / DEPENDENCIA


RESP. DE PROY. EXTERNO	LOGO EXTERNO
CED PROFESIONAL	
PROYECTO / REVISÓ / AUTORIZÓ	

Dirección de Planeación y Proyectos de Obra — Secretaría de Obras Públicas

PROYECTO	COORDINACIÓN
ARQ. ALEJANDRO JAIME LEAL	ARQ. ALEJANDRO JAIME LEAL
JEFE DE DEP.	DIRECTOR
LIC. CARLOS ALBERTO OLLIVIER GARCÍA	ARQ. ALEJANDRO PONCE RODRÍGUEZ


PROYECTO	CLAVE	No. PLANO
SEÑALETICA HORIZONTAL AV. JOSE MARÍA CHÁVEZ AMBAS CALZADAS	DSH 01	04
UBICACION: TRAMO DE AV. AGUASCALIENTES CALZADA SUR A AV. SIGLO XXI CALZADA NORTE	FECHA NOV 2022	ESCALA INDICADA
CONTENIDO: DETALLES SEÑALETICA HORIZONTAL	ACOTACIÓN METROS	No. EXP E-000-22

Aguascalientes
LA CIUDAD DE TU VIDA

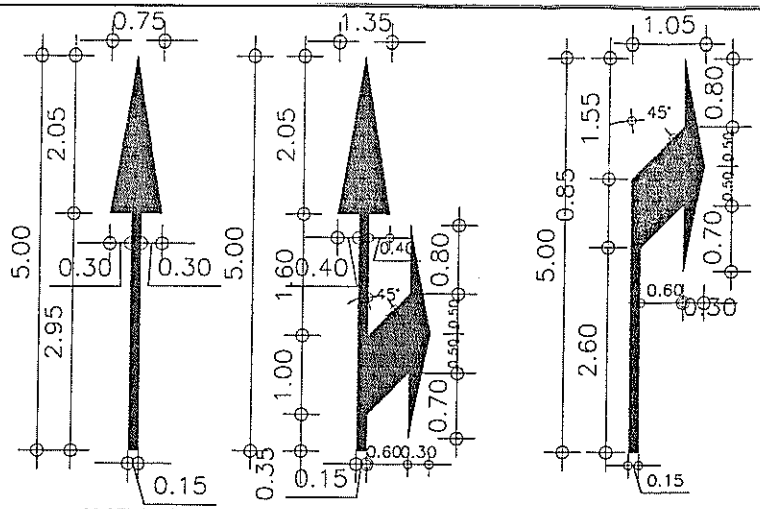

DETALLE 4 FLECHAS EN PAVIMENTO PARA VELOCIDADES HASTA DE 60KM/H

COTAS EN M

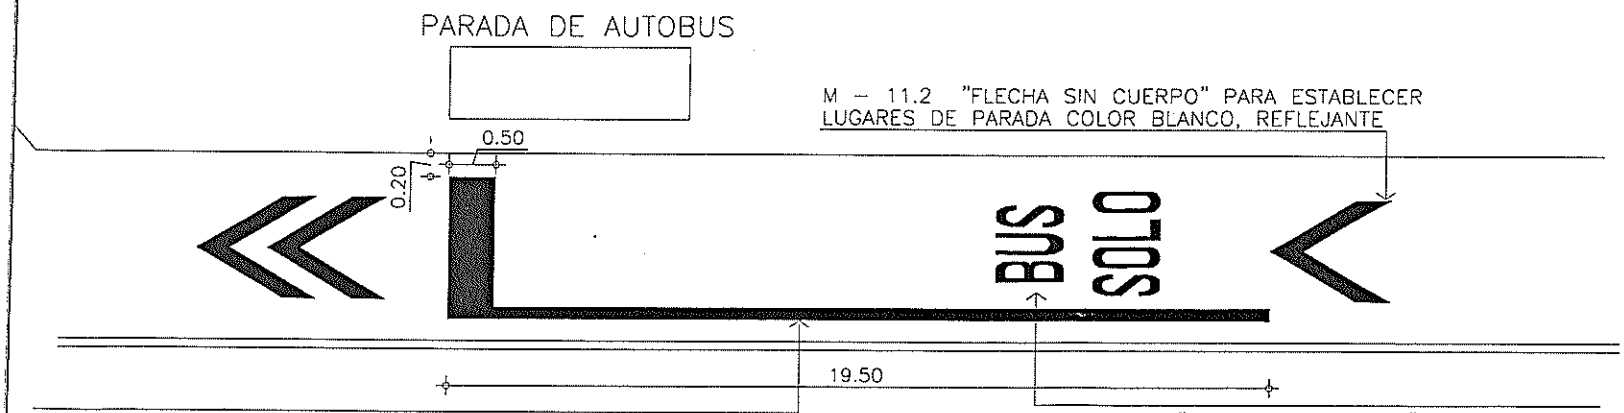


DETALLE 3 SEÑALIZACION HORIZONTAL SOLO BUS

SIN ESCALA

COTAS: M.

LOCALIZACIÓN:

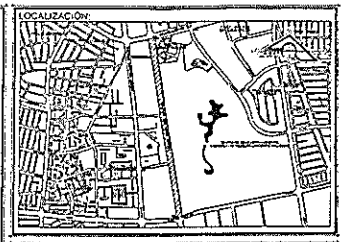

SIMBOLOGÍA

NOTA:
Se aplicará en todos los señalamientos horizontales pintura para trafico base solvente tipo alquidal de secado rápido, que cumpla con las especificaciones n-cmt-5-01-001/05, n-pry-car-10-01-002/13 de la SCT aplicadas al día de hoy.

M-12.1, M-2.2 APLICADA SOBRE GUARNICIONES Y DENTELLONES DE CUALQUIER COLOR

Se aplicará en todos los señalamientos horizontales pintura para trafico Termoplastico tipo alquidal de secado rápido, que cumpla con las especificaciones n-cmt-5-01-001/05, n-pry-car-10-01-002/13 de la SCT aplicadas al día de hoy.

M - 1.2, LÍNEA DISCONTINUA SENCILLA DE DIVISIÓN DE CARRILES DE FRENTE EN PISO, DE 10 CM DE ANCHO
M - 3.3, CONTINUA IZQUIERDA, PARA VIALIDADES URBANAS DE FRENTE EN PISO, SEPARADA 15 CM. DE LA GUARNICION, COLOR AMARILLO
M - 4, PARA INDICAR LÍNEA GUÍA EN ZONA DE TRANSICIÓN DE FRENTE EN PISO, DESARROLLO DE 2.00 X 0.10 MTS, CON UNA SEPARACIÓN DE 4.00 MTS ENTRE SI PROMEDIO
M - 5, PARA INDICAR ENTRADA Y SALIDA EN BIFURCACIONES
M - 6, PARA INDICAR ALTO EN CRUCEROS, COLOR BLANCO
M - 7.1 PARA INDICAR " CRUCE PEATONAL EN VIAS PRIMARIAS" COLOR AMARILLO
M - 11.1, "FLECHA SENCILLA" PARA INDICAR SENTIDO DE CIRCULACIÓN
M - 11.1, "FLECHA CABEZA DOBLE" PARA INDICAR SENTIDO DE CIRCULACIÓN (VUELTA IZQUIERDA O DERECHA)

NOTA:
Nota1: Se aplicará en todos los señalamientos horizontales pintura para trafico base solvente tipo alquidal de secado rápido, que cumpla con las especificaciones n-cmt-5-01-001/05, n-pry-car-10-01-002/13 de la SCT aplicadas al día de hoy.


Nota2: Dosificación de micro esfera
La cantidad de esferas de vidrio en la película de pintura en húmedo, según su tipo, será la que se indica en la Tabla.

TABLA 8: Cantidad de esferas de vidrio en la película de pintura en humedo.

TIPO DE PINTURA	ESPESOR DE LA PELICULA DE PINTURA EN HUMEDO mm	CANTIDAD DE ESFERAS kg/m2		TIPO DE GRANULOMETRIA
		INTEGRADAS	SEMBRADAS, MINIMO	
BASE SOLVENTE	0.38 A 0.50	---	0.330	1
BASE AGUA	0.38 A 0.50	---	0.330	1AB
TERMOPLASTICA	1.50 A 0.69	0.57 A 0.89	0.330	B

La Dirección de Planeación y Proyectos solo asesora el proyecto ejecutivo, no es responsable de la correcta ejecución de la obra. Este documento no tiene validez si no presenta las firmas de los responsables para su autorización, así como los sellos respectivos.

PRESIDENTE MUNICIPAL M.P.P. Leonardo Montañez Castro SECRETARIO DE OBRAS PÚBLICAS Ing. Miguel Ángel Huizar Botello	REV / FECHA / OBSERVACIONES	V°B° DE LA SECRETARÍA	RESP. DE PROY. EXTERNO / CED. PROFESIONAL / PROYECTO / REVISO / AUTORIZO	LOGO EXTERNO	Dirección de Planeación y Proyectos de Obra / Secretaría de Obras Públicas PROYECTO / COORDINADOR ARQ. ALEJANDRO JARAMILLO LEAL JEFE DE DEP. / DIRECTOR LIC. ARQ. JUAN GARCÍA / ARQ. ALEJANDRO JARAMILLO LEAL	PROYECTO SEÑALETICA HORIZONTAL AV. JOSÉ MARÍA CHÁVEZ AMBAS CALZADAS UBICACIÓN TRAMO DE AV. AGUASCALIENTES CALZADA SUR A AV. SIGLO XXI CALZADA NORTE CONTENIDO DETALLES SEÑALETICA HORIZONTAL	CLAVE DSH 02 / No. PLANO 05 FECHA NOV 2022 / ESCALA INDICADA ACOTACIÓN METROS / No EXP E-000-22	Aguascalientes LA CIUDAD DE TU VIDA

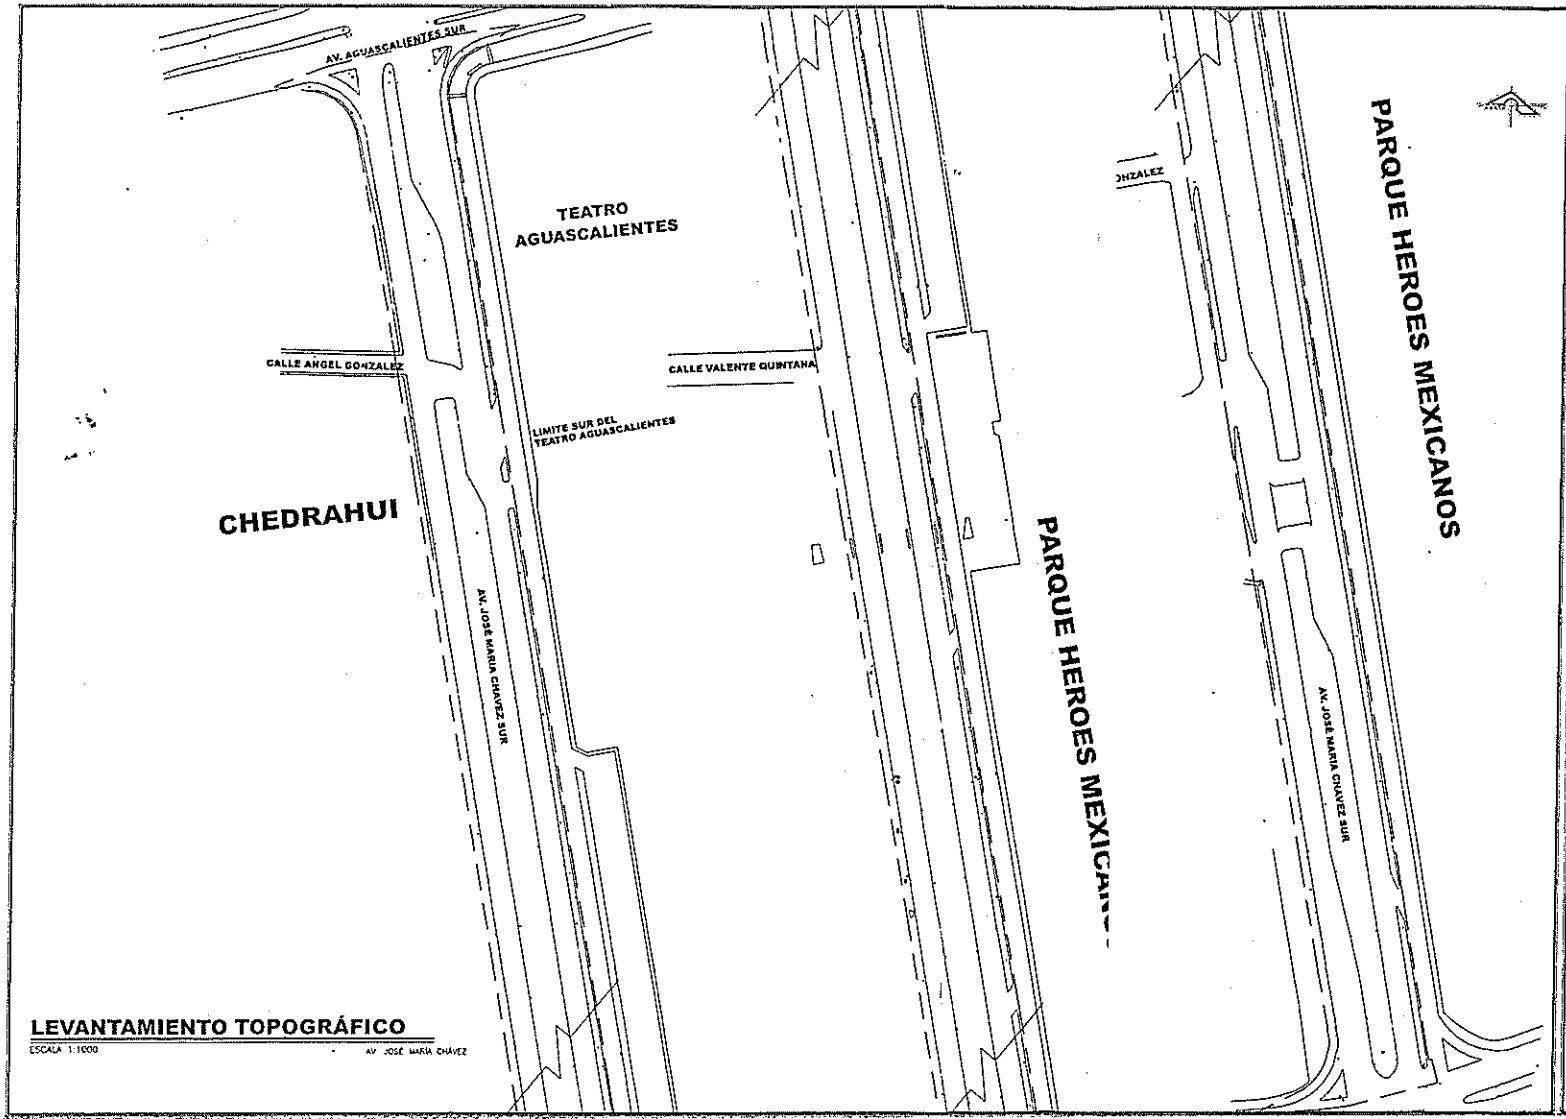

LEVANTAMIENTO TOPOGRÁFICO

ESCALA 1:1000

LOCALIZACIÓN

SIMBOLOGÍA

SIMBOLOGIA

- LIMITE DE PROYECTO
- LUM — POSTE LUMINARIA
- CFE — POSTE DE CFE
- TEL — POSTE DE TELMEX
- REG — REGISTRO
- POSTE — POSTE
- REGISTROS CFE
- REGISTRO SEMAFORO
- REGISTROS TELMEX
- TELEFONO — TELEFONO
- POZO DE VISITA
- CAJA DE VALVULAS
- SEMAFOROS
- CAIMAN — CAIMANES
- ANUNCIO — ANUNCIO
- RETENIDA POS — RETENIDA POSTE

La Dirección de Planeación y Proyectos solo autoriza el proyecto ejecutivo, no es responsable de la correcta ejecución de la obra. Este documento no tiene validez si no presenta las firmas de los responsables para su autorización, así como los sellos respectivos.

PRESIDENTE MUNICIPAL
M.P.P. Leonardo Montañez Castro
SECRETARIO DE OBRAS PÚBLICAS
Ing. Miguel Ángel Huizar Botello

REV	FECHA	OBSERVACIONES

Vo. Bo. DE LA DIRECCIÓN

RESP. DE PROY. EXTERNO		LOGO EXTERNO
CED. PROFESIONAL		
PROYECTO	REVISO	AUTORIZO

Dirección de Planeación y Proyectos de Obra — Secretaría de Obras Públicas

PROYECTISTA	COORDINADOR
ARQ. ALEJANDRO MEZA CONTRERAS	ARQ. ALEJANDRO JAIME LEAL
JEFE DE DEP.	DIRECTOR
LIC. OMAR ALFREDO MACIAS GARCIA	ARQ. RENATO GONZALEZ ESTRADA

PROYECTO	SEÑALETICA HORIZONTAL AV. JOSÉ MARÍA CHÁVEZ AMBAS CALZADAS
UBICACIÓN	TRAMO DE AV. AGUASCALIENTES CALZADA SUR A AV. SIGLO XXI CALZADA NORTE
CONTENIDO	LEVANTAMIENTO TOPOGRAFICO

CLAVE	No. PLANO
LEV 01	02
FECHA NOV 2022	ESCALA INDICADA
ACOTACIÓN METROS	No. EXP. E-000-22

Aguascalientes
LA CIUDAD DE TU VIDA