Aguascalientes
LA CIUDAD DE TU VIDA

Dirección de Programación Presupuestal
Núm. Oficio AMPP/0631/22
Aguascalientes, Ags. 29 de Diciembre del 2022
Asunto: Validación de Expediente Técnico

C.P. SERGIO ARTURO LOZANO GONZÁLEZ
SECRETARIO DE FINANZAS MUNICIPALES
P R E S E N T E

Con fundamento en los artículos 17 fracción XV, 60 fracción XVI y 76 fracción VI del Reglamento del Sistema Integral de Desarrollo Municipal y del Instituto Municipal de Planeación y Evaluación de Aguascalientes, hago referencia al oficio SOPMA/2887/2022 recibido por este Instituto el día 29 de Diciembre del 2022 por parte de la Secretaría de Obras Públicas Municipales, mediante el cual remiten el expediente técnico original de la siguiente obra para su análisis, registro y priorización, conforme al Programa Anual de Obra Pública y Programas Sociales para el ejercicio presupuestal 2022:

DEPENDENCIA EJECUTORA:	SOPMA
NOMBRE DE LA OBRA O PROYECTO:	SOBRECARPETA ASFÁLTICA Y PAVIMENTO HIDRÁULICO
UBICACIÓN:	AV. DE LOS MAESTROS (CALZADA PONIENTE), TRAMO: ENTRE CALLE PROF. JOSÉ GUADALUPE PERALTA Y AV. SIGLO XXI, VARIAS COLONIAS, AGUASCALIENTES, AGS.
FONDO DE INVERSIÓN:	FONDO DE INFRAESTRUCTURA SOCIAL MUNICIPAL Y DE LAS DEMARCACIONES TERRITORIALES DEL DISTRITO FEDERAL
IMPORTE:	$7,520,297.16 (ET FINAL)
No. DE OBRA:	2022-FISMDF-0086-04-1101
MODALIDAD DE EJECUCIÓN:	CONTRATO
EJE:	MUNICIPIO SOBRESALIENTE
ESTRATEGIA:	OBRA PÚBLICA INTELIGENTE
POLITICA:	5.8.1.REHABILITACIÓN Y MANTENIMIENTO VIALIDADES, CAMINOS, CALLES, ÁREAS DE TERRACERÍA Y CAUCES (C

Al respecto, hago de su conocimiento que dicho expediente ha sido analizado en su integración técnica y documental, con base en el artículo 168 fracción I del Reglamento de la Ley de Obras Públicas y Servicios Relacionados para el Estado de Aguascalientes y sus Municipios.

Asimismo, le comento que este Instituto valida dicha obra acorde a lo establecido en los artículos 14, 22 párrafo segundo y 23 de la Ley de Obras Públicas y Servicios Relacionados para el Estado de Aguascalientes y sus Municipios, la cual se encuentra alineada al Plan de Desarrollo Municipal vigente, para dar cumplimiento a las metas establecidas en el mismo, y a los Lineamientos Generales para la Operación de este Fondo de Inversión, toda vez que la misma cuente con la autorización del CODEMUN. De igual manera, se hace de su conocimiento que deberá cumplir con lo establecido en los ordenamientos aplicables en lo que respecta al ejercicio, control e información de los recursos de este Fondo. Cabe hacer mención que los recursos solicitados para este proyecto de inversión, estarán sujetos a la disponibilidad presupuestal para el presente ejercicio fiscal que determine la Secretaría a su digno cargo. Sin otro particular por el momento, le envío un cordial saludo.

A T E N T A M E N T E

ARQ. AUSTRIA GABRIELA DÁVILA DE LA LLAVE
DIRECTORA GENERAL DEL IMPLAN

SEDR/ CAAR / JDBC
C.c.p. I.C. ING. MIGUEL ÁNGEL HUIZAR BOTELLO .- Secretaría de Obras Públicas Municipales .Para su conocimiento.
C.c.p. Archivo.

Instituto Municipal de Planeación y Evaluación de Aguascalientes

Antonio Acevedo Escobedo 103 A, Col. Centro
Aguascalientes, Ags. C.P. 20000

(449) 9101010 Ext. 3117

www.implanags.gob.mx

GOBIERNO MUNICIPAL DE AGUASCALIENTES

INSTITUTO MUNICIPAL DE PLANEACION

IMPLAN

ANÁLISIS INTEGRAL DE EXPEDIENTE TÉCNICO

No. DE OBRA (PAOP 2020):	2022-FISMDF-0086-04-1101	REGISTRO No.	250
OFICIO DE VALIDACIÓN:	AMPP/0631/22	FECHA RECIBIDO PARA REVISIÓN:	29 de Diciembre del 2022
PROGRAMA:	URBANIZACION MUNICIPAL	LOCALIDAD O COLONIA:	VARIAS COLONIAS
SUB-PROGRAMA:	0411- Calles y Caminos	DELEGACIÓN:	Aguascalientes
DEPENDENCIA:	Secretaría de Obras Públicas Municipales	MOD. DE EJECUCIÓN:	CONTRATO
NOMBRE DE LA OBRA:	SOBRECARPETA ASFÁLTICA Y PAVIMENTO HIDRÁULICO, AV. DE LOS MAESTROS (CALZADA PONIENTE), TRAMO: ENTRE CALLE PROF. JOSÉ GUADALUPE PERALTA Y AV. SIGLO XXI		
FUENTE DE FINANCIAMIENTO:	FONDO DE INFRAESTRUCTURA SOCIAL MUNICIPAL Y DE LAS DEMARCACIONES TERRITORIALES DEL DISTRITO FEDERAL, FISMDF		
INVERSIÓN:	$7,520,297.16	CLASIFICACIÓN DE OBRA:	BIENES DE DOMINIO PUBLICA

TOTAL	FEDERAL	ESTATAL	MUNICIPAL	BENEFICIARIOS	OTROS	DIFERENCIA ENTRE MOD.
$7,520,297.16	$7,520,297.16	0.00	0.00	0.00	0.00	*$0.00*

TIPO DE EXPENDIENTE:	ET FINAL	AÑO: 2022	AÑO:	AÑO:
AVANCES:	Financiero: 29 %	Físico: 42 %		
FECHA DE INICIO:	7 de Septiembre del 2022	FECHA DE TÉRMINO:	5 de Diciembre del 2022	REGISTRO SIMA: 86

CHEK LIST DE LOS ANEXOS DEL EXPEDIENTE TÉCNICO

CÉDULA DE REGISTRO DE OBRA	✓
DICTAMEN DE FACTIBILIDAD	✓
MEMORIA DESCRIPTIVA	✓
PRESUPUESTO BASE	✓
FACTIBILIDAD VERIFICADA EN CAMPO	✓
CROQUIS DE UBICACIÓN (MACRO)	✓
CROQUIS DE UBICACIÓN (MACRO)	✓
PROGRAMA DE OBRA Y MONTOS MENSUALES	✓
PLANOS O ESTUDIOS TÉCNICOS	✓
PADRÓN DE BENEFICIARIOS	N/A
ACTA DE ACEPTACIÓN DEL PROYECTO	N/A
DICTAMEN DE IMPACTO AMBIENTAL	N/A
CONVENIO DE CONCERTACIÓN	N/A
ACTA CONSTITUTIVA	N/A

METAS		BENEFICIARIOS		PERIODO DE EJECUCION		OBRA PROPUESTA		CLAVE SISCO
UNIDAD DE MEDIDA	CANT	TIPO DE BENEFICIARIOS	CANTIDAD	FECHA DE INICIO	FECHA DE TERMINO	CONCEPTO	JORNALES A GENERAR	
M2	3008.85	Personas	550	2022-09-07	2022-12-05	Sobrecarpeta Asfáltica	19552	2356

INCLUIDO EN PLAN DE DESARROLLO MUNICIPAL Y EL PROGRAMA ANUAL DE OBRA PÚBLICA

OBSERVACIONES:

SIN OBSERVACIONES

RECIBIO: ING. JOSÉ DAVID BURGUETE CLAUSTRO
Analista de Programación e Inversión de Obra Pública

29 de Diciembre del 2022
Fecha de validación

29 de Diciembre del 2022
Fecha de validación Expediente

PROCEDE Si ✓ No

H. AYUNTAMIENTO CONSTITUCIONAL DEL MUNICIPIO DE AGUASCALIENTES 2021-2024

AYUNTAMIENTO DE AGUASCALIENTES

CEDULA DE REGISTRO POR OBRA

Aguascalientes

050400-001E00E05-05-2-2-1-00-1-E-0510-0-17-0086-21-2502-6144

2022-FISMDF-0086-0411101-040	Obra **SOBRECARPETA ASFÁLTICA Y PAVIMENTO HIDRÁULICO AV. DE LOS MAESTROS (CALZADA PONIENTE)**
Tipo DEFINITIVO 1 2022 Folio SISCO **2356**	Ubic. TRAMOS: ENTRE CALLE PROF. JOSÉ GUADALUPE PERALTA GÁMEZ Y BLVD. SIGLO XXI, AGUASCALIENTES Mpio.

Ent. Ejecutora : **050400001E00E05**

Eje: **05**	MUNICIPIO SOBRESALIENTE
Finalidad: **2**	DESARROLLO SOCIAL
Función: **2**	VIVIENDA Y SERVICIOS A LA COMUNIDAD
Subfunción: **1**	URBANIZACIÓN
Tema: **00**	SIN TEMA
Cuenta del Gasto **1**	GASTO PROGRAMABLE
Clasif. Programatica: **E**	PRESTACIÓN DE SERVICIOS PÚBLICOS
Programa: **0510**	Movilidad Urbana
SubPrograma: **0**	SUBPROGRAMA GENÉRICO
Proyecto: **17**	
Tipo de Gasto: **21**	GASTO INVERSIÓN / OBRA PÚBLICA

I N V E R S I O N 2022

Municipal	2502	FONDO PARA LA INFRAESTRUCTURA SOCIAL MUNICIPAL Y DE LAS DEMARCACIONES TERRITORIALES DEL DISTRITO FEDERAL 2022	$7,520,297.16

Folio SIMA 86 Total $7,520,297.16

M E T A S

Unidad de Medida	Cantidad	Descripción
M2	3008.85	SOBRECARPETA ASFÁLTICA SOBRECARPETA ASFÁLTICA Y PAVIMENTO HIDRÁULICO AV. DE LOS MAESTROS (CALZADA PONIENTE)

Inversión Ejercida Total al	31 de Diciembre de 2021	$0.00
Avance Fisico Acumulado al	31 de Diciembre de 2021	
Avance Fisico Acumulado Programado al	31 de Diciembre de 2022	100 %

Fecha de Inicio 07 Sep 2022 Fecha de Terminación 05 Dic 2022

Jornales a Generar en 2022 19552

Modalidad de ejecución CONTRATO

Clasificación de la Obra Bienes de Dominio Público

Registro del Patrimonio: Obras del dominio público

OBRAS PÚBLICAS

Av. Aguascalientes Sur No. 2615
Fracc. Jardines de las Fuentes,
Aguascalientes, Ags. C.P. 20278

(449) 9 78 92 01, 06, 09

www.ags.gob.mx

GENERALES

Nombre del Proyecto : SOBRECARPETA ASFÁLTICA Y PAVIMENTO HIDRÁULICO AV. DE LOS MAESTROS (CALZADA PONIENTE)

TRAMOS: ENTRE CALLE PROF. JOSÉ GUADALUPE PERALTA GÁMEZ Y BLVD. SIGLO XXI, AGUASCALIENTES Mpio.

Programa : 04 URBANIZACION MUNICIPAL

Subprograma : 11 Calles y caminos (422.- Rehabilitación: 0411202- Concreto Asfáltico)

Clave del Municipio : AGUASCALIENTES

Localidad :

Barrio, Colonia o Ejido : AGUASCALIENTES Mpio.

Tipo de Obra : NUEVA

DESCRIPCIÓN DEL PROYECTO:

SOBRECARPETA ASFÁLTICA Y PAVIMENTO HIDRÁULICO AV. DE LOS MAESTROS (CALZADA PONIENTE)

PRELIMINARES 5,450.77 M2
SOBRECARPETA ASFÁLTICA 3,008.85 M2
CONCRETO HIDRÁULICO 2,441.92 M2
OBRA COMPLEMENTARIA 1.00 OBRA
HIDRÁULICO SANITARIO 48 HR
EXTRAORDINARIOS 1.00 OBRA

Beneficiarios (No. y Tipo) :

550	PERSONAS

Hombres: 247 Mujeres: 303

OBRAS PÚBLICAS

No. Folio SISCO 2356

Los abajo firmantes, hacen constar que el presente proyecto :

SOBRECARPETA ASFÁLTICA Y PAVIMENTO HIDRÁULICO AV. DE LOS MAESTROS (CALZADA PONIENTE)

TRAMOS: ENTRE CALLE PROF. JOSÉ GUADALUPE PERALTA GÁMEZ Y BLVD. SIGLO XXI, AGUASCALIENTES Mpio.

cumple con los Requisitos y Normas Técnicas establecidas por la Dependencia Normativa, por lo que es viable su ejecución. Comprometiéndose la misma a proporcionar la supervisión y asistencia técnica necesaria durante el proceso administrativo.

Por la Dependencia Ejecutora

Ing. Miguel Angel Huizar Botello
Secretario de Obras Públicas

Lic. Jaime Gallo Camacho
Secretario de Desarrollo Urbano

LUGAR :AGUASCALIENTES, AGS.

Av. Aguascalientes Sur No. 2615
Fracc. Jardines de las Fuentes,
Aguascalientes, Ags. C.P. 20278

(449) 9 78 92 01, 06, 09

www.ags.gob.mx

MUNICIPIO: AGUASCALIENTES

LOCALIZACION: TRAMOS: ENTRE CALLE PROF. JOSÉ GUADALUPE PERALTA GÁMEZ Y BLVD. SIGLO XXI, AGUASCALIENTES Mpio.

PROGRAMA: URBANIZACION MUNICIPAL

SUBPROGRAMA: Calles y caminos (422.- Rehabilitación: 0411202- Concreto Asfáltico)

OBRA A REALIZAR: SOBRECARPETA ASFÁLTICA Y PAVIMENTO HIDRÁULICO AV. DE LOS MAESTROS (CALZADA PONIENTE)

DEPENDENCIA EJECUTORA: SECRETARÍA DE OBRAS PUBLICAS DEL MUNICIPIO DE AGUASCALIENTES

FORMA DE EJECUCION: CONTRATO

TIPO DE OBRA PROPUESTA: NUEVA

CONDICIONES ACTUALES DE LA OBRA:

SOBRECARPETA ASFÁLTICA Y PAVIMENTO HIDRÁULICO AV. DE LOS MAESTROS (CALZADA PONIENTE)

CARACTERISTICAS DE LA OBRA: Bueno

FACTIBILIDAD DE LA OBRA:

ESTA OBRA SE REQUIERE PARA EL BENEFICIO DE LA CIUDADANÍA

PROCEDE: SI [X] NO [ ]

REVISÓ: Jefa del Departamento de Expedientes Tecnicos y Costos

NOMBRE: Arq. Blanca Margarita Martinez Amador

FIRMA:


FECHA: 09 Dic 2022

SECRETARÍA DE OBRAS PÚBLICAS

No. Folio SISCO 2356

H. AYUNTAMIENTO DE AGUASCALIENTES
SECRETARÍA DE OBRAS PÚBLICAS
DIRECCIÓN DE SUPERVISIÓN DE OBRA
LOCALIZACION


OBRA:	FISMDF-0086-2022 SOBRECARPETA ASFÁLTICA Y PAVIMENTO HIDRÁULICO AV. DE LOS MAESTROS (CALZADA PONIENTE)					
NO. DE CONTR	FISMDF-0086-2022	CONTRATISTA:	GRUPO CONSTRUCTOR URBANO AVANTE, S.A. DE C.V.			

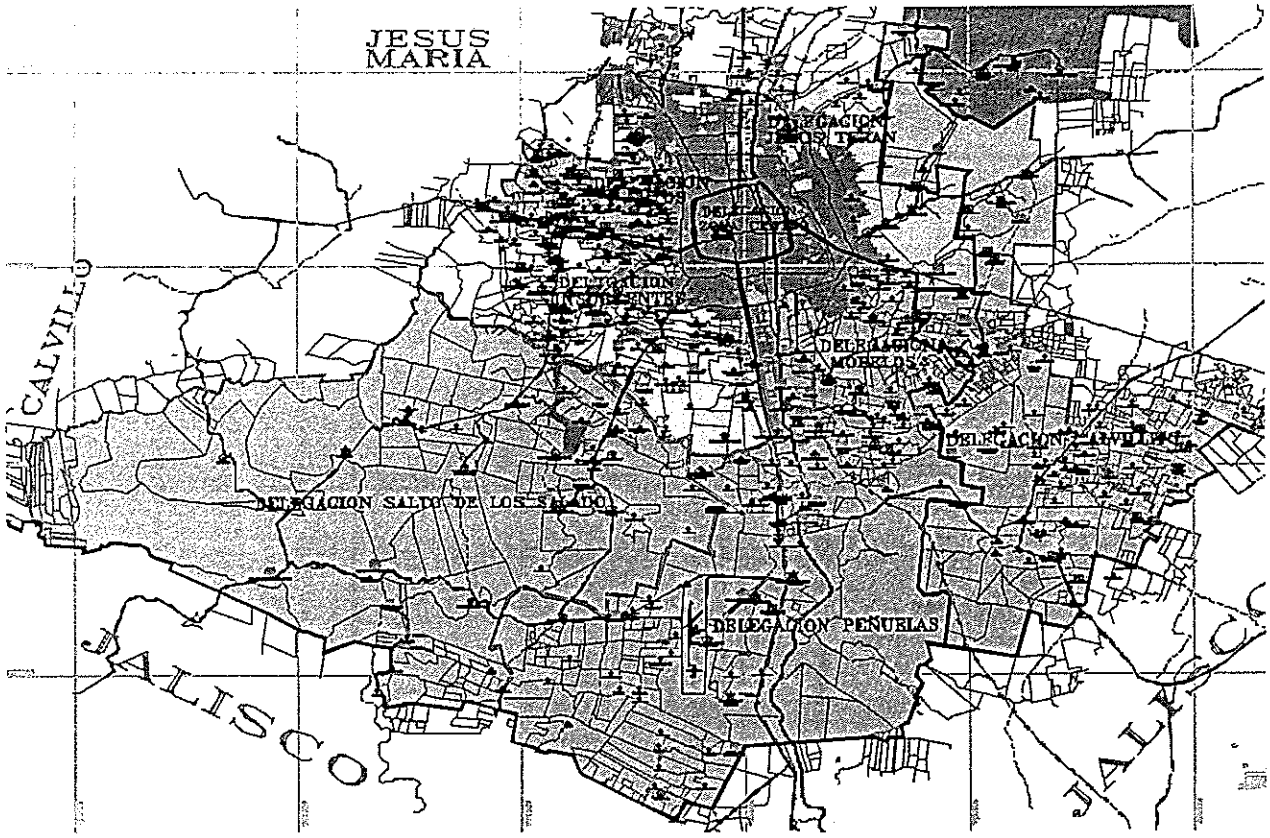

ARQ ARIADNA MEDINA
SUPERVISOR DE OBRA.

H. AYUNTAMIENTO DE AGUASCALIENTES
SECRETARÍA DE OBRAS PÚBLICAS
DIRECCIÓN DE SUPERVISIÓN DE OBRA
LOCALIZACION

OBRA:	FISMDF-0086-2022 SOBRECARPETA ASFÁLTICA Y PAVIMENTO HIDRÁULICO AV. DE LOS MAESTROS (CALZADA PONIENTE)					
NO. DE CONTR	FISMDF-0086-2022	CONTRATISTA:	GRUPO CONSTRUCTOR URBANO AVANTE, S.A. DE C.V.			

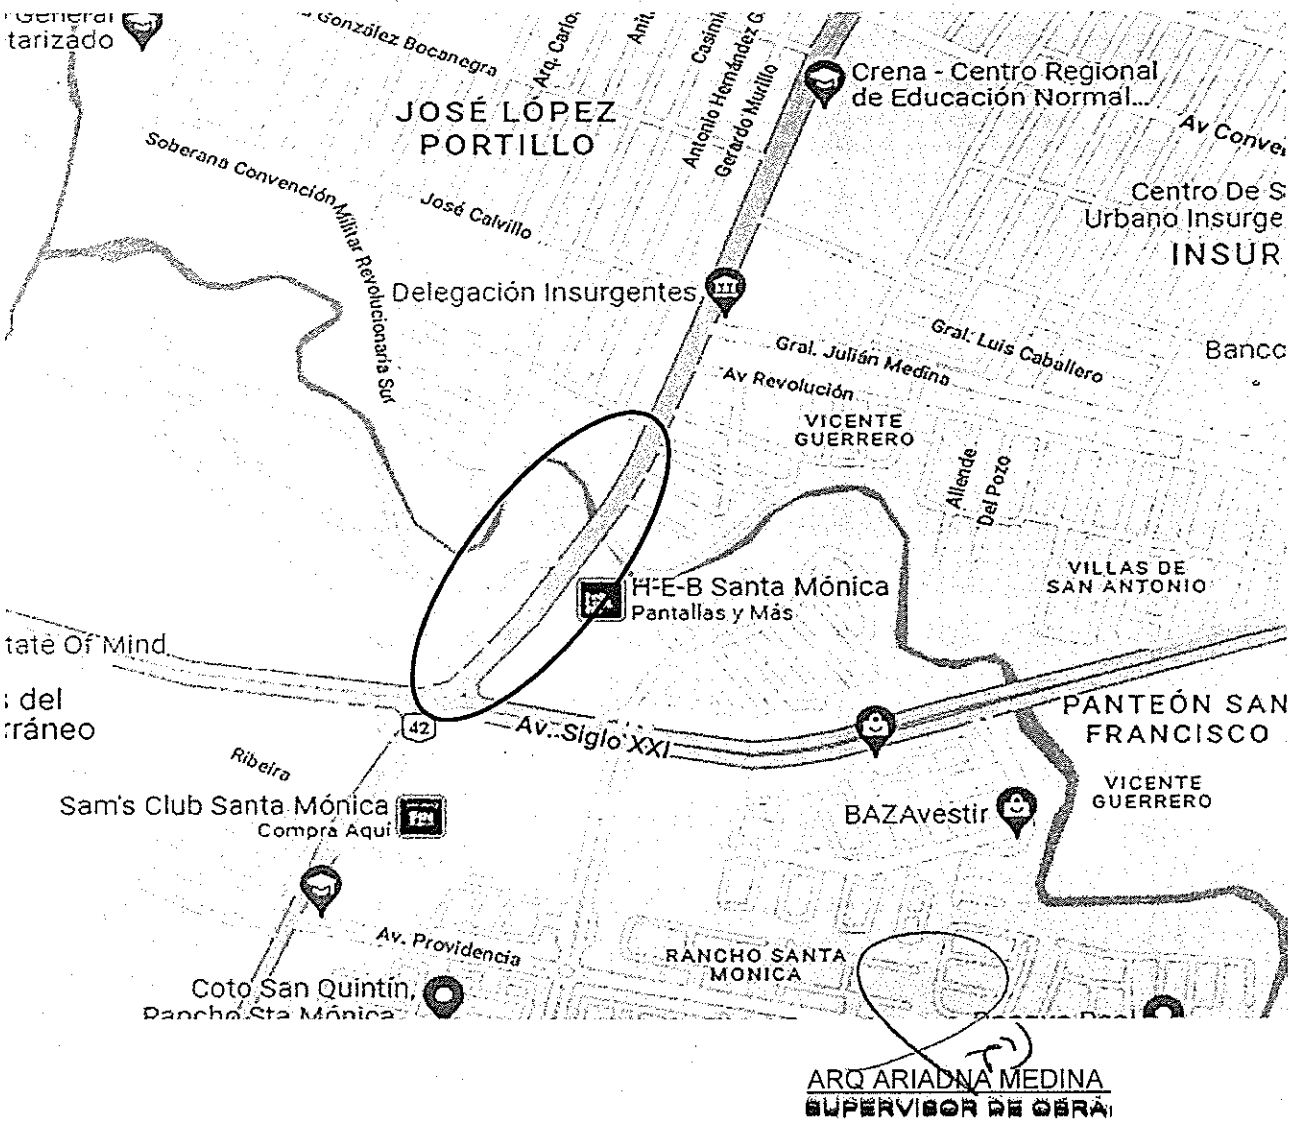

R03-POS-SOS-7.5.1-04	
REVISIÓN:	00
FECHA DE EDICIÓN:	
RESPONSABLE:	SUPERVISOR DE OBRA
TIEMPO DE RET:	02 AÑOS

Aguascalientes
LA CIUDAD DE TU VIDA

PROGRAMA DE OBRA DEFINITIVO

No. DE CONTRATO : FISMDF-0086-2022

PROGRAMA: UR-URBANIZACION

OBRA Y NOMBRE DE LA OBRA: FISMDF-0086-2022 SOBRECARPETA ASFÁLTICA Y PAVIMENTO HIDRÁULICO AV. DE LOS MAESTROS (CALZADA PONIENTE)

INICIO VIGENTE: 07-septiembre-22

TERMINO REAL: 05-diciembre-22

RECURSO 2022

CONCEPTO			1	2	3	4	5	6	7	8	9	10	11	12	13	14	15	16	PONDERACIÓN %	
			2022																FINANCIERO	FÍSICO
			SEPTIEMBRE	OCTUBRE	NOVIEMBRE	DICIEMBRE	ENERO	FEBRERO	MARZO	ABRIL	MAYO	JUNIO	JULIO	AGOSTO	SEPTIEMBRE	OCTUBRE	NOVIEMBRE	DICIEMBRE	%	%
DESCRIPCIÓN	INVERSION																			
FISMDF-0086-2022 SOBRECARPETA ASFÁLTICA Y PAVIMENTO HIDRÁULICO AV. DE LOS MAESTROS (CALZADA PONIENTE)																				
TRAMO: ENTRE AV. PROF. JOSÉ GUADALUPE PERALTA GÁMEZ Y BLVD. SIGLO XXI, AGUASCALIENTES.																				
FISMDF-0086-2022 SOBRECARPETA ASFÁLTICA Y PAVIMENTO HIDRÁULICO AV. DE LOS MAESTROS (CALZADA PONIENTE)																				
PRELIMINARES																				
PRELIMINARES Y DEMOLICIONES	$ 393,287.79	3													33%	33%	33%		6.07	5.36
SOBRECARPETA ASFÁLTICA																				
BACHEO PROFUNDO	$ 428,150.35	3														33%	33%	33%	6.60	5.36
SOBRECARPETA ASFÁLTICA	$ 1,528,743.64	5														20%	20%	20%	23.58	8.93
CONCRETO HIDRÁULICO																				
EXCAVACIONES, ACARREOS Y TERRACERÍAS	$ 1,255,469.94	5													20%	20%	20%	20%	19.37	8.93
PAVIMENTO	$ 556,264.44	8														13%	13%	13%	8.58	14.29
DENTELLÓN DE CONCRETO	$ 37,171.23	3														33%	33%	33%	0.57	5.36
GUARNICIONES	$ 107,484.52	3														33%	33%	33%	1.66	5.36
BANQUETA RAMPA	$ 62,403.44	3															33%	33%	0.96	5.36
OBRA COMPLEMENTARIA																				
OBRA COMPLEMENTARIA	$ 43,121.10	3																33%	0.67	5.36
LIMPIEZA	$ 48,581.52	3																33%	0.75	5.36
SEÑALIZACIÓN HORIZONTAL	$ 214,714.77	2																50%	3.31	3.57
SEÑALAMIENTO VERTICA	$ 8,763.42	3																33%	0.14	5.36
HIDRÁULICO SANITARIO																				
LINEA POTABLE	$ 8,482.08	4														25%	25%	25%	0.13	7.14
EXTRAORDINARIO																				
EXTRAORDINARIOS	$ 1,790,367.56	8														13%	13%	13%	27.62	14.29
SUBTOTAL IVA	$ 6,483,014.80	56.00	0	0	0	0	0	0	0	0	0	0	0	0	1	2	3	4	7	8	5	5	3	3	3	3	4	3	0	0		
AVANCE SEMANAL %			0%	0%	0%	0%	0%	0%	0%	0%	0%	0%	0%	0%	0%	0%	0%	0%	13%	14%	9%	9%	5%	5%	5%	5%	7%	6%	0%	0%		
AVANCE SEMANAL ACUMULADO %			0%	0%	0%	0%	0%	0%	0%	0%	0%	0%	0%	0%	0%	0%	0%	0%	13%	27%	36%	45%	50%	55%	60%	65%	72%	78%	78%	78%	100.00	100.00
EJERCIDO SEMANAL $			$0.00	$0.00	$0.00	$0.00	$0.00	$0.00	$0.00	$0.00	$0.00	$0.00	$0.00	$0.00	131,049.92	302,185.92	418,018.69	442,022.35	731,481.87	1,026,203.64	621,969.29	599,077.73	599,077.73	307,702.72	306,811.66	140,441.07	176,472.37		$ 6,483,014.80	
EJERCIDO MENSUAL $			$0.00			$0.00			$0.00			$0.00			$1,373,336.29			$3,009,664.24			$1,632,875.84			$287,316.43				$ 1,037,282.37	IVA 16%
EJERCIDO MENSUAL ACUMULADO $			0.00			0.00			0.00			0.00			1,373,336.29			4,383,000.53			6,215,890.37			6,483,014.80					
EJERCIDO SEMANAL %			0%	0%	0%	0%	0%	0%	0%	0%	0%	0%	0%	0%	2%	5%	6%	7%	11%	15%	10%	9%	9%	5%	5%	2%	3%	0%	0%	0%		
EJERCIDO MENSUAL %			0%			0%			0%			0%			21%			46%			25%			4%				GRAN TOTAL EJERCIDO	
EJERCIDO MENSUAL ACUMULADO %			0%			0%			0%			0%			21%			68%			96%			100%				$ 7,520,297.16	

ARQ. [illegible] MEDINA
SUPERVISOR

PRESIDENCIA MUNICIPAL DE AGUASCALIENTES

FACTIBILIDAD VERIFICADA EN CAMPO

GENERALES

EJERCICIO: 2022 APROBACION No: 2022-FISMDF-0086-0411101-040

LOCALIDAD : TRAMOS: ENTRE CALLE PROF. JOSÉ GUADALUPE PERALTA GÁMEZ Y BLVD. SIGLO XXI, AGUASCALIENTI

MUNICIPIO: AGUASCALIENTES, AGS

TIPO DE INVERCION: FONDO PARA LA INFRAESTRUCTURA SOCIAL MUNICIPAL Y DE LAS DEMARCACIONES TERRITORIALES DEL DISTRITO FEDERAL

PROGRAMA : UR-URBANIZACION

SUB-PROGRAMA: 01- PAVIMENTACIÓN (CONST., AMPLIACIÓN Y REHABILITACIÓN) D) SOBRECARPETA

OBRA A REALIZARSE: FISMDF-0086-2022 SOBRECARPETA ASFÁLTICA Y PAVIMENTO HIDRÁULICO AV. DE LOS MAESTROS (CALZADA PONIENTE)

DEPENDENCIA EJECUTOI SECRETARÍA DE OBRAS PÚBLICAS MUNICIPALES (S.O.P.M.A)

FORMACIÓN DE EJECUCI CONTRATO NO. DE CONTRATO: FISMDF-0086-2022

NOMBRE CONTRATISTA: GRUPO CONSTRUCTOR URBANO AVANTE, S.A. DE C.V.

REPRESENTANTE:	I.C. LUIS FERNANDO LÓPEZ MARTÍNEZ			RESIDENTE	I.C. LUIS FERNANDO LÓPEZ MARTÍNEZ	
MONTO CONT. ORIGEN	$7,255,451.63	ANTICIPO:	$ 2,176,635.49	PLAZO	90	TERMINO:
1A AMPLIACION $:	264,845.53	3.65%	1 AMPL DIAS	0.00%	0	05/12/2022
2A AMPLIACION $:	-	0.00%	2 AMPL DIAS	0%	0	05/12/2022
3A AMPLIACION $:		0%	3 AMPL DIAS	0%	0	05/12/2022
4A AMPLIACION $:		0%	4 AMPL DIAS	0%	0	05/12/2022
MONTO TOTAL:	**$ 7,520,297.16**	**104%**		0.00%	0	05/12/2022

FIRMA CONTRATO: 31 de agosto de 2022

INICIO Carta: dd/mm/aa 1 de septiembre de 2022 TERMINO Carta: 29 de noviembre de 2022

INICIO REAL: dd/mm/aa 7 de septiembre de 2022 TERMINO REAL: 5 de diciembre de 2022

TIPO DE OBRA PROPUESTA

NUEVA CREACIÓN	X	CONSOLIDACIÓN	
COMPLEMENTARIA		AMPLIACIÓN	
REHABILITACIÓN		EQUIPAMIENTO	

CARACTERÍSTICAS DE LA OBRA:

REHABILITACION DE PAVIMENTO ASFÁLTICO Y CONTRUCCIÓN DE CONCRETO HIDRÁULICO AV DE LOS MAESTROS MAESTROS CALZADA PONIENTE, FRESADO DE CARPETA, SOBRECARPETA SOBRE CALZADA PRINCIPAL CONCRETO HIDRAULICO SOBRE CARPETA PRINCIPAL

CONDICIONES ACTUALES DE LA OBRA: (SELECCIONAR UNO OBLIGATORIO)

BUEN ESTADO X REGULAR PESIMO ESTADO

FACTIBILIDAD DE LA OBRA: (CONDICIONES ACTUALES DE LA OBRA)

ESTA OBRA SE ENCUENTRA EN BUEN ESTADO

PROCEDE: SI: X NO:

MARQUE SOLO UNA

ARQ ARIADNA MEDINA
SUPERVISOR

PRESIDENCIA MUNICIPAL DE AGUASCALIENTES

FACTIBILIDAD VERIFICADA EN CAMPO

GENERALES

LOCALIDAD: TRAMOS: ENTRE CALLE PROF. JOSÉ GUADALUPE PERALTA GÁMEZ Y BLVD. SIGLO XXI, AGUASC
MUNICIPIO: AGUASCALIENTES, AGS
PROGRAMA: UR-URBANIZACION
SUB-PROGRAMA: 01- PAVIMENTACIÓN (CONST., AMPLIACIÓN Y REHABILITACIÓN) D) SOBRECARPETA
OBRA A REALIZARSE: FISMDF-0086-2022 SOBRECARPETA ASFÁLTICA Y PAVIMENTO HIDRÁULICO AV. DE LOS MAESTROS (CALZADA PONIENTE)

DEPENDENCIA EJECUTORA: SECRETARÍA DE OBRAS PÚBLICAS MUNICIPALES (S.O.P.M.A)
FORMACIÓN DE EJECUCION: CONTRATO

TIPO DE OBRA PROPUESTA

NUEVA CREACIÓN	X	CONSOLIDACIÓN	
COMPLEMENTARIA		AMPLIACIÓN	
REHABILITACIÓN		EQUIPAMIENTO	

CARACTERÍSTICAS DE LA OBRA:

REHABILITACION DE PAVIMENTO ASFÁLTICO Y CONTRUCCIÓN DE CONCRETO HIDRÁULICO AV DE LOS MAESTROS MAESTROS CALZADA PONIENTE, FRESADO DE CARPETA, SOBRECARPETA SOBRE CALZADA PRINCIPAL CONCRETO CONCRETO HIDRÁULICO SOBRE CARPETA PRINCIPAL

CONDICIONES ACTUALES DE LA OBRA:

BUEN ESTADO: X REGULAR: PESIMO ESTADO:

FACTIBILIDAD DE LA OBRA:

ESTA OBRA SE ENCUENTRA EN BUEN ESTADO

PROCEDE SI: X NO:

ARQ ARIADNA MEDINA
SUPERVISOR

PRESUPUESTO MODIFICADO

Obra: SOBRECARPETA ASFÁLTICA Y PAVIMENTO HIDRÁULICO AV. DE LOS MAESTROS (CALZADA PONIENTE)

Ubicación: TRAMOS: ENTRE CALLE PROF. JOSÉ GUADALUPE PERALTA GÁMEZ Y BLVD. SIGLO XXI, AGUASCALIENTES Mpio.

Contratista: GRUPO CONSTRUCTOR URBANO AVANTE, S.A. DE C.V. (727)

No.	Concepto	Unidad	Cantidad	Precio Unitario	Importe Total
	GRUPO: PRELIMINARES				
	PARTIDA: PRELIMINARES Y DEMOLICIONES				
1	LIMPIA, TRAZO Y NIVELACION EN PAVIMENTOS, CALLES Y VIALIDADES CON EQUIPO TOPOGRAFICO, INCLUYE: EJES, BANCO DE NIVEL, RENIVELACIONES LAS VECES NECESARIAS, CORRECCION DE RASANTE A PUNTOS OBLIGADOS (AUTORIZADOS POR LA SUPERVISION), ESTACAS, VARILLAS, MANO DE OBRA CALIFICADA, HERRAMIENTA NECESARIA, EQUIPO DE PRECISION CALIBRADO, TRABAJO TERMINADO.P.U.O.T.	M2	5450.77	$13.33	$72,658.76
3	SONDEO A MANO O A MAQUINA PARA LOCALIZACION DE TUBERIAS CUALQUIER PROFUNDIDAD Y MATERIAL PARA VERIFICAR LA CALIDAD DE LAS INSTALACIONES HIDRAULICO SANITARIAS CUIDANDO NO DAÑARLAS PARA NO INTERFERIR EN LOS SERVICIOS, INCLUYE: EXCAVACION, EQUIPO, MANO DE OBRA, REPORTE A LA SUPERVISION, RELLENOS, COMPACTACIONES, TRABAJO TERMINADO.	SONDE	4	$1,090.28	$4,361.12
5	DEMOLICION PARCIAL DE PAVIMENTO HIDRAULICO Y/O ASFALTICO DE HASTA 15 CM. DE ESPESOR PROMEDIO EN PAVIMENTOS Y (BANQUETAS, LOSAS DIAMANTE Y CAJAS DE VALVULAS, TOPES) CON O SIN ARMADO DE ACERO, SIN RECUPERACION, MUROS, MOJONERAS, ANCLAJES, ETC, DE FORMA MANUAL Y MECANICA, INCLUYE ACARREO DE MATERIAL AL LUGAR DE ACOPIO, HERRAMIENTA NECESARIA Y TODO LO NECESARIO PARA SU CORRECTA EJECUCION, LIMPIEZA, TRABAJO TERMINADO	M3	170.93	$248.02	$42,394.06
6	FRESADO UNIFORME DE LA SUPERFICIE DE RODADURA EN PAVIMENTO DE CONCRETO ASFALTICO 3-7 CM (5 cm de espesor promedio) MEDIANTE FRESADORA EN FRIO COMPACTA, EQUIPADA CON BANDA TRANSPORTADORA PARA CARGA DIRECTA SOBRE CAMION DE VOLTEO, INCLUYE: TRAMO DE PRUEBA AL INICIO DEL FRESADO PARA AUTORIZACION DE SUPERVISION (SUPERFICIE FRESADA UNIFORME Y SIN PROTUBERANCIAS NI ONDEOS), ACARREOS LOCALES, CARGA Y ACARREO A KM SUBSECUENTES (11 A 15 KM APROX) DE MATERIAL PRODUCTO DEL FRESADO DE CARPETA ASFALTICA EL TRASLADO SERA A PARQUE DE MAQUINARIA DE LA SOPMA, PIEZAS DE DESGASTE, COMBUSTIBLES, CONSUMIBLES, MANO DE OBRA, CUALQUIER VOLUMEN Y AREA,EQUIPO NECESARIO, LIMPIEZA FINA Y GRUESA, TRABAJO TERMINADO.	M3	138.63	$1,625.44	$225,334.75
7	REMOCIÓN DE CARPETA ASFÁLTICA SOBRE CONCRETO HIDRÁULICO EXISTENTE POR MEDIOS MECÁNICOS (MOTO CONFORMADORA), DE HASTA 5 CM DE ESPESOR, INCLUYE: ACAMELLONAMIENTO, EQUIPO, ACARREO DE MATERIAL PRODUCTO DE REMOCIÓN DE CARPETA ASFÁLTICA A LUGAR DE ACOPIO, PIEZAS DE DESGASTE, COMBUSTIBLES, MANO DE OBRA, EQUIPO, DESPERDICIOS, LIMPIEZAS, TRABAJO TERMINADO, ACARREOS LOCALES, CARGA Y ACARREO A KM SUBSECUENTES (11 A 15 KM APROX) DE MATERIAL PRODUCTO DE REMOCIÓN DE CARPETA ASFÁLTICA, EL TRASLADO SERA A PARQUE DE MAQUINARIA DE LA SOPMA	M3	11.82	$393.54	$4,651.64
8	DEMOLICION CONTROLADA DE CONCRETO HIDRAULICO EN DENTELLONES Y GUARNICIONES DE 15 x 20 x 40 CM. DE FORMA MANUAL Y MECÁNICA, INCLUYE: CORTES CON DISCO, ACARREO DEL MATERIAL AL LUGAR DE ACOPIO PARA SU CARGA Y ACARREO FUERA DE LA OBRA.	ML	228.8	$50.32	$11,513.22
9	CARGA MECANICA Y ACARREO DE MATERIAL PRODUCTO DE EXCAVACION Y DEMOLICION EN CAMION DE VOLTEO AL 1er. KM, VOLUMEN MEDIDO COMPACTO.	M3	186.95	$33.94	$6,345.08
10	ACARREO DE MATERIAL PRODUCTO DE EXCAVACION Y/O DEMOLICION EN CAMION DE VOLTEO A KILOMETROS SUBSECUENTES, AL TIRADERO OFICIAL AUTORIZADO MAS CERCANO AUTORIZADO POR LA SUPERVISION, VOLUMEN MEDIDO COMPACTO.	M3-KM	2430.86	$10.71	$26,029.16
				Totales por Partida	**$393,287.79**
				Totales por Grupo	**$393,287.79**

Obra: SOBRECARPETA ASFÁLTICA Y PAVIMENTO HIDRÁULICO AV. DE LOS MAESTROS (CALZADA PONIENTE)

Ubicación: TRAMOS: ENTRE CALLE PROF. JOSÉ GUADALUPE PERALTA GÁMEZ Y BLVD. SIGLO XXI, AGUASCALIENTES Mpio. .

Contratista: GRUPO CONSTRUCTOR URBANO AVANTE, S.A. DE C.V. (727)

No.	Concepto	Unidad	Cantidad	Precio Unitario	Importe Total
	GRUPO: SOBRECARPETA ASFALTICA				
	PARTIDA: BACHEO PROFUNDO				
12	BACHEO PROFUNDO AISLADO UTILIZANDO MATERIAL CALIDAD BASE HIDRAULICA PARA MAS DE UN MILLON DE EJES EQUIVALENTES DEL BANCO QUE ELIJA EL CONTRATISTA, INCISO N.CSV.CAR-1.02.004/03 DE LAS NORMAS DE CONSTRUCCION DE CARR. DE LA SCT, BASE HIDRAULICA MEJORADA CON CEMENTO EN PROPORCION DE 40 KILOS DE CEMENTO POR CADA M3, INCLUYE: PREPARACION, PERFILADO, MATERIALES, MANO DE OBRA, HERRAMIENTA MENOR Y EQUIPO NECESARIO QUE SE REQUIERA PARA LOGRAR LA COMPACTACION DE 100 %, PVSM, ACARREOS DENTRO Y FUERA DE LA OBRA, PREPARACION DE MATERIAL, HUMEDECIDO, NIVELADO, TRASLADO DE UN PUNTO A OTRO DENTRO DE LA OBRA EN CUALQUIER VOLUMEN, MOVIMIENTO DE MAQUINARIA P.U.O.T	M3	554.51	$772.14	$428,159.35
			Totales por Partida		$428,159.35
	PARTIDA: SOBRE CARPETA ASFALTICA				
14	PREPARACIÓN DE LA SUPERFICIE DE CONTACTO EN LOS EXTREMOS DONDE LA PERFILADORA NO ALCANCE POR LÍMITES CON LA GUARNICIÓN, CON UN RASPADO SUPERFICIAL CON RETROEXCAVADORA, ELIMINANDO TECATAS QUE HAYAN QUEDADO PARA RENIVELADO, BARRIDOS ENTRE PASADA DE MOTOCONFORMADORA Y EN REMATES DE EMPATES A DETALLE A MANO, INCLUYE: RETIRO DE MATERIAL FUERA DE LA OBRA A TIRADERO OFICIAL INDICADO.	M2	335.2	$32.75	$10,977.80
18	RIEGO DE IMPREGNACION CON EMULSION DE ROMPIMIENTO LENTO (ECL-60 %), INCLUYE BARRIDO DE LA SUPERFICIE, LIMPIEZA A DETALLE, SUMINISTRO, ALMACENAMIENTO, CALENTAMIENTO, Y APLICACION DE LA EMULSION CON EQUIPO ESPECIAL PARA ESA ACTIVIDAD, ESPREAS LIMPIAS Y ALINEADAS, EN CASO DE RECOMENDARLO EL LABORATORIO DE CALIDAD DEL CONTRATISTA SE DEBERÁ DAR UN RIEGO MATAPOLVO ANTES DE COLOCAR LA CAPA DE IMPREGNACION, A RAZON DE 1.5 LT DE EMULSION POR M2, O LO QUE INDIQUE EL LABORATORIO DE CALIDAD DEL CONTRATISTA, NO SE ACEPTAN LEVANTAMIENTO DEL RIEGO, TRABAJO TERMINADO, P.U.O.T.	M2	2772.54	$31.80	$88,166.77
19	RIEGO DE LIGA CON EMULSION DE ROMPIMIENTO RAPIDO (ECR-65 %), INCLUYE, SUMINISTRO, ALMACENAMIENTO, CALENTAMIENTO, Y APLICACION DE LA EMULSION CON EQUIPO ESPECIAL PARA ESA ACTIVIDAD, ESPREAS O BACHADOR LIMPIAS Y ALINEADAS, CONTROL DE CALIDAD A CADA DOS REMESAS EN OBRA (INDEPENDIENTEMENTE DE LA CANTIDAD A UTILIZAR) EN LA PETROLIZADORA, A RAZON DE 0.8 LT DE EMULSION POR M2, O LO QUE INDIQUE EL LABORATORIO DE CALIDAD DEL CONTRATISTA, NO SE ACEPTAN "IMPREGNALIGA", TRABAJO TERMINADO, P.U.O.T.	M2	3008.85	$20.80	$62,584.08
20	SUMINISTRO Y COLOCACION DE CONCRETO ASFALTICO EN CALIENTE DE GRANULOMETRIA DENSA ELABORADA CON ASFALTO MODIFICADO TIPO I, AGREGADO 3/4" A FINOS, DE 5 CM DE ESPESOR, FORMADA Y COMPACTADO AL 95%, INCLUYE MATERIALES, QUE CUMPLAN LA NORMATIVA SCT-N-CMT-04-04, SCT-CMT-4-05-002, SCT-CMT-4-05-003, SCT-CMT-4-05-004, SCT-CTR-CAR-1-04-006-14 APLICADAS AL DIA DE HOY, DISEÑO MARSHALL (DEVERÁ SER AUTORIZADO POR EL LABORATORIO DE CALIDAD DE SOPMA AL MENOS 3 DIAS ANTES DE INICIO DE TENDIDO DE LA MEZCLA ASFALTICA), INCUYE: TRAMO DE PRUEBA AL INICIO PARA REVISION Y AUTORIZACION DEL ESPESOR POR PARTE DEL SUPERVISOR, EL CONTRATISTA DEBERÁ PREVEER EL SUMINISTRO Y TIEMPOS MUERTOS POR MOVIMIENTOS DEL TREN DE MAQUINAS DE TRABAJO EN TRAMOS AISLADOS. TRABAJO TERMINADO P.U.O.T. Y LIMPIEZAS DE GRANZON Y HUESO LATERAL.	M2	3008.85	$307.70	$925,823.15

Obra: SOBRECARPETA ASFÁLTICA Y PAVIMENTO HIDRÁULICO AV. DE LOS MAESTROS (CALZADA PONIENTE)

Ubicación: TRAMOS: ENTRE CALLE PROF. JOSÉ GUADALUPE PERALTA GÁMEZ Y BLVD. SIGLO XXI, AGUASCALIENTES Mpio.

Contratista: GRUPO CONSTRUCTOR URBANO AVANTE, S.A. DE C.V. (727)

No.	Concepto	Unidad	Cantidad	Precio Unitario	Importe Total
	GRUPO: SOBRECARPETA ASFALTICA				
	PARTIDA: SOBRE CARPETA ASFALTICA				
21	COMPACTACION SOBRE MORTERO ASFALTICO TENDIDO EN APROCHES CON GUARNICIONES CON EQUIPO LIGERO (PLANCHITA), INCLUYE: MANO DE OBRA Y EQUIPO, TRABAJO TERMINADO.	M2	335.2	$17.88	$5,993.38
22	SUMINISTRO Y COLOCACION DE JUNTA WABO ESL 400 ELASTOFLEX BRIDGE DUREZA SHORE TIPO A, JUNTA DE EXPANSION PARA PUENTES CONDICIONES DE LOSA A LOSA, INCLUYE: PREPARACION Y TERMINADO DE LOSA, SEGUN ESPECIFICACION DEL FABRICANTE, ELEMENTOS DE FIJACION QUIMICOS Y MECANICOS, CARGAS Y ACARREOS, DEMOLICIONES, CONCRETO MR=42 KG/CM2, ARMADO DE LOSAS DE RODAMIENTO, CURADO Y COLADO DE LOSAS (LOSAS DE 50 CM DE ANCHO ARMADAS CON 8 VRS No. 4 y estribos No. 3 @ 15 cm,), PREPARACION DE LOSA A BASE DE APUNTALAMIENTO INFERIOR SUFICIENTE SEGUN LA SUPERVISION, DEMOLICION DEL AREA NECESARIA PARA LA NUEVA LOSA (3 CM ABAJO DEL ACERO POR TEMPERATURA) PARA AMARRAR EL NUEVO ARMADO, ELEMENTOS QUIMICOS PARA UNIR CONCRETO NUEVO CON CONCRETO VIEJO, LIMPIEZA CON AIRE DEL ELEMENTO ANTES DE COLAR, COLADO, CURADO CON MEMBRANA QUIMICA Y RAYADO SEGUN LAS LOSAS EXISTENTES, COLOCACION DE JUNTA Y HERRAJES, CORTE CON DISCO, TRAZO, CORTES Y DESPERDICIOS, TRABAJO TERMINADO, LIMPIEZAS DE LOS ELEMENTOS Y LIMPIEZA FINA DEL AREA, P.U.O.T	ML	19.1	$22,785.26	$435,198.47
				Totales por Partida	$1,528,743.64
				Totales por Grupo	$1,956,902.99

Obra: SOBRECARPETA ASFÁLTICA Y PAVIMENTO HIDRÁULICO AV. DE LOS MAESTROS (CALZADA PONIENTE)

Ubicación: TRAMOS: ENTRE CALLE PROF. JOSÉ GUADALUPE PERALTA GÁMEZ Y BLVD. SIGLO XXI, AGUASCALIENTES Mpio.

Contratista: GRUPO CONSTRUCTOR URBANO AVANTE, S.A. DE C.V. (727)

No.	Concepto	Unidad	Cantidad	Precio Unitario	Importe Total
	GRUPO: CONCRETO HIDRAULICO				
	PARTIDA: EXCAVACIONES, ACARREOS Y TERRACERIAS				
23	EXCAVACION EN CORTE CON MAQUINA HASTA UNA PROFUNDIDAD DE 80 CM, EN MATERIAL TIPO II, INCLUYE: AFLOJE Y EXTRACCION DE MATERIAL, ACARREOS AL LUGAR DE ACOPIO PARA SU CARGA Y ACARREO FUERA DE LA OBRA, VOLUMEN MEDIDO COMPACTO.	M3	2825.49	$20.50	$57,922.54
24	COMPACTACION DE TERRENO NATURAL AL 90% DE SU P.V.S.M EN SU COMPACTACION., INCLUYE ESCARIFICADO, TENDIDO, HOMOGENIZADO, HUMEDECIDO OPTIMO NIVELADO Y COMPACTADO EN CAPAS DE 20 CM, CALIDAD Limite liquido máximo 50%, Valor de Soporte California (CBR) mínimo 15%, Expansión máxima 5%, Grado de Compactación minimo 90% ± 2, Y TODO LO NECESARIO PARA SU CORRECTA EJECUCION,	M2	5214.46	$15.22	$79,364.08
25	MEJORAMIENTO DE TERRENO NATURAL ADICIONANDO CAL AL MATERIAL DEL LUGAR, EXCARIFICADO, ADICIONADO DEL CAL AL 3% PVSS, MEZCLADO, HUMEDECIDO, TENDIDO Y COMPACTADO AL 90 %, EN CAPAS DE 20 CM DE ESPESOR MAXIMO, TRABAJO TERMINADO	M2	2441.92	$43.36	$105,881.65
26	FORMACION Y COMPACTACION DE SUB-RRASANTE, CON EL USO DE EQUIPO MAYOR, HASTA ALCANZAR EL 100% AASHTO MODIFICADA. EN CAPAS DE 20 CM MAXIMO, INCLUYE: SUMINISTRO DE MATERIAL DE BANCO QUE CUMPLA CON LA NORMA, HUMEDAD OPTIMA Y TODO LO NECESARIO PARA SU CORRECTA COLOCACION, EL MATERIAL DEBERA CUMPLIR CON UN C.B.R. DEL 60% PARA LO CUAL EL CONTRATISTA DEBERA PROPONER UN BANCO DE MATERIAL Y UN FRENTE, DEBERA PRESENTAR EL ESTUDIO DE CALIDAD QUE AVALE EL CUMPLIMIENTO AL 100 % DE LA NORMA Y DEMAS CARACTERISTICAS SOLICITADAS, P.U.O.T.	M3	488.38	$249.59	$121,894.76
27	FORMACION Y COMPACTACION DE SUB-BASE PARA MENOS DE UN MILLON DE EJES EQUIVALENTES, CON EL USO DE EQUIPO MAYOR, HASTA ALCANZAR EL 100% AASHTO MODIFICADA. EN CAPAS DE 20 CM MAXIMO, INCLUYE: SUMINISTRO DE MATERIAL DE BANCO QUE CUMPLA CON LA NORMA, HUMEDAD OPTIMA Y TODO LO NECESARIO PARA SU CORRECTA COLOCACION, EL MATERIAL DEBERA CUMPLIR CON UN C.B.R. DEL 50% PARA LO CUAL EL CONTRATISTA DEBERA PROPONER UN BANCO DE MATERIAL Y UN FRENTE, DEBERA PRESENTAR EL ESTUDIO DE CALIDAD QUE AVALE EL CUMPLIMIENTO AL 100 % . Y DEMAS CARACTERISTICAS SOLICITADAS, P.U.O.T.	M3	488.38	$249.59	$121,894.76
28	FORMACION Y COMPACTACION DE BASE HIDRAULICA PARA MENOS DE UN MILLON DE EJES EQUIVALENTES DE 20 CMS. DE ESPESOR, PARA SUPERFICIE DE RODAMIENTO DE CONCRETO HIDRAULICO, CON MATERIAL 100% TRITURADO O MEZCLA DE 1 1/2" A FINOS QUE CUMPLA CON LA NORMA, COMPACTADA AL 100 % DE PRUEBA AASHTO. COMBINANDO COMPACTADOR DE RODILLO EN BAJA Y MUERTO Y LLANTEO CON EQUIPO PESADO (CAMION DE VOLTEO CARGADO AL MAXIMO), INCLUYE HOMOGENEIZADO, TENDIDO, COMPACTADO, E INCORPORACION DE AGUA HASTA ALCANZAR LA HUMEDAD OPTIMA Y NIVELACIONES.	M3	488.38	$571.73	$279,221.50
29	CARGA MECANICA Y ACARREO DE MATERIAL PRODUCTO DE EXCAVACION Y DEMOLICION EN CAMION DE VOLTEO AL 1er. KM, VOLUMEN MEDIDO COMPACTO.	M3	2825.49	$33.94	$95,897.13
30	ACARREO DE MATERIAL PRODUCTO DE EXCAVACION Y/O DEMOLICION EN CAMION DE VOLTEO A KILOMETROS SUBSECUENTES, AL TIRADERO OFICIAL AUTORIZADO MAS CERCANO AUTORIZADO POR LA SUPERVISION, VOLUMEN MEDIDO COMPACTO.	M3-KM	36731.42	$10.71	$393,393.51
				Totales por Partida	$1,255,469.94

Obra: SOBRECARPETA ASFÁLTICA Y PAVIMENTO HIDRÁULICO AV. DE LOS MAESTROS (CALZADA PONIENTE)

Ubicación: TRAMOS: ENTRE CALLE PROF. JOSÉ GUADALUPE PERALTA GÁMEZ Y BLVD. SIGLO XXI, AGUASCALIENTES Mpio.

Contratista: GRUPO CONSTRUCTOR URBANO AVANTE, S.A. DE C.V. (727)

No.	Concepto	Unidad	Cantidad	Precio Unitario	Importe Total
	GRUPO: CONCRETO HIDRAULICO				
	PARTIDA: PAVIMENTO				
32	SUMINISTRO Y COLOCACION DE CANASTILLAS O PASAJUNTAS TIPO PESADO DE SECCION NOMINAL DE BARRA PRINCIPAL DE 46 CMS, CON REDONDO LISO DE 1 1/4" SOLDADO EN EXTREMOS ALTERNOS @ 30 CMS. SEPARADORES, ATIESADORES, BASES Y SOPORTES DE ACERO F´y= 4,200 DE DIAMETRO 5/16", DE ACUERDO A DISEÑO ANEXO EN PLANOS, INCLUYE: MATERIAL, MANO DE OBRA, CORTES, PULIDO EN CORTES, ANCLAJES, FUNDAS DE PLASTICO EN LOS EXTREMOS NO SOLDADOS, AJUSTES, DESPERDICIOS, ACARREOS, FLETES DENTRO Y FUERA DE LA OBRA.	ML	753.4	$671.72	$506,073.85
33	SUMINISTRO Y COLOCACION DE RELLENO PARA JUNTAS DE EXPANSION A BASE DE ESPUMA DE POLIETILENO DE CELDAS CERRADAS (FOAMTECH) DE 1/2" DE ESPESOR Y 20 CM DE ALTURA DE ACUERDO AL DISEÑO ANEXO EN PLANOS, INCLUYE: MATERIAL, SELLADOR AUTONIVELANTE,MANO DE OBRA, CORTES, AJUSTES, DESPERDICIOS, ACARREO, FLETES DENTRO Y FUERA DE LA OBRA DE ACUERDO A ESPECIFICACIONES DE CONTROL DE CALIDAD (LA FICHA TECNICA DEL FABRICANTE DEBERA CUMPLIR CON LAS ESPECIFICACIONES DE LA NORMA)	ML	537.43	$93.39	$50,190.59
				Totales por Partida	$556,264.44
	PARTIDA: DENTELLONES DE CONCRETO				
34	EXCAVACION A MANO EN MATERIAL TIPO B DE 0.00 A 2.00 M DE PROFUNDIDAD, INCLUYE: TRASPALEO VERTICAL, AFINE DE TALUDES CONSERVACION DE LA EXCAVACION Y ACARREO DE MATERIAL AL LUGAR DE ACOPIO PARA SU POSTERIOR CARGA Y ACARREO FUERA DE LA OBRA.	M3	6.97	$154.85	$1,079.30
35	COMPACTACION DE TERRENO NATURAL AL 90% DE SU P.V.S.M EN SU COMPACTACION., INCLUYE ESCARIFICADO, TENDIDO, HOMOGENIZADO, HUMEDECIDO OPTIMO NIVELADO Y COMPACTADO EN CAPAS DE 20 CM, CALIDAD Limite liquido máximo 50%, Valor de Soporte California (CBR) mínimo 15%, Expansión máxima 5%, Grado de Compactación minimo 90% ± 2, Y TODO LO NECESARIO PARA SU CORRECTA EJECUCION.	M2	0	$15.22	$0.00
36	RELLENO COMPACTADO AL 90% CON MATERIAL DE BANCO EN CAPAS DE 20 CM UTILIZANDO BAILARINA. INCLUYE: SUMINISTRO DE TEPETATE (MATERIAL DE BANCO) EN LA OBRA, ABUNDAMIENTO, ACARREOS DENTRO DE LA OBRA, CRIBADO, RETIRO DE MATERIAL, MANO DE OBRA Y EQUIPO, LIMPIEZAS, TRABAJO TERMINADO.	M3	3.48	$377.90	$1,315.09
37	CARGA MECANICA Y ACARREO DE MATERIAL PRODUCTO DE EXCAVACION Y DEMOLICION EN CAMION DE VOLTEO AL 1er. KM, VOLUMEN MEDIDO COMPACTO.	M3	6.97	$33.94	$236.56
38	ACARREO DE MATERIAL PRODUCTO DE EXCAVACION Y/O DEMOLICION EN CAMION DE VOLTEO A KILOMETROS SUBSECUENTES, AL TIRADERO OFICIAL AUTORIZADO MAS CERCANO AUTORIZADO POR LA SUPERVISION, VOLUMEN MEDIDO COMPACTO.	M3-KM	90.6	$10.71	$970.33
39	CONSTRUCCION DE DENTELLON RECTO Y/O CURVO 20-20X40 CM DE SECCION, CON CONCRETO PREMEZCLADO MR=42 KGF/CM2, TMA 1 1/2", R.R 3 DIAS. REVENIMIENTO NORMAL DE 10+-2 CM, GRAVA TRITURADA, ACABADO CON DOBLADOR Y PULIDO. INCLUYE: TRAZO, NIVELACION, CIMBRADO, COLADO, VIBRADO, DESCIMBRADO, , Y CURADO CON MEMBRANA QUIMICA APLICADA CON ASPERSOR Y LIMPIEZA, REMATE CON PAVIMENTO EXISTENTE DEL MISMO MATERIAL Y TIPO, TRABAJO TERMINADO P.U.O.T.	ML	87.12	$385.33	$33,569.95
				Totales por Partida	$37,171.23

Obra: SOBRECARPETA ASFÁLTICA Y PAVIMENTO HIDRÁULICO AV. DE LOS MAESTROS (CALZADA PONIENTE)

Ubicación: TRAMOS: ENTRE CALLE PROF. JOSÉ GUADALUPE PERALTA GÁMEZ Y BLVD. SIGLO XXI, AGUASCALIENTES Mpio.

Contratista: GRUPO CONSTRUCTOR URBANO AVANTE, S.A. DE C.V. (727)

No.	Concepto	Unidad	Cantidad	Precio Unitario	Importe Total
	GRUPO: **CONCRETO HIDRAULICO**				
	PARTIDA: **GUARNICIONES**				
40	EXCAVACION A MAQUINA Y/O A MANO EN MATERIAL TIPO II, EN SECO O PRESENCIA DE AGUA, INCLUYE. CORTE DE RAIZ DE CUALQUIER TAMAÑO Y GROSOR, HASTA UNA PROFUNDIDAD DE 40 CM DESPUES DE DESMONTE, DESPALME Y/O DEMOLICION DE SUPERFICIE O ELEMENTO ESTRUCTURAL O DE ACABADO, PROTECCION DE AREAS ADYACENTES, SIN DAÑAR AREAS ALEDAÑAS, CARGA Y ACARREO A TIRADERO OFICIAL, CONSERVACION DE LA MISMA, TRABAJO TERMINADO, LIMPIEZAS.	M3	50.34	$73.45	$3,697.47
41	COMPACTACION DE TERRENO NATURAL AL 90% DE SU P.V.S.M EN SU COMPACTACION., INCLUYE ESCARIFICADO, TENDIDO, HOMOGENIZADO, HUMEDECIDO OPTIMO NIVELADO Y COMPACTADO EN CAPAS DE 20 CM, CALIDAD Limite liquido máximo 50%, Valor de Soporte California (CBR) mínimo 15%, Expansión máxima 5%, Grado de Compactación minimo 90% ± 2, Y TODO LO NECESARIO PARA SU CORRECTA EJECUCION,	M2	137.28	$15.22	$2,089.40
42	CONSTRUCCION DE GUARNICION RECTA Y/O CURVA TRAPEZOIDAL 15-20X40 CM DE SECCION CON CONCRETO PREMEZCLADO MR=38 KGF/CM2, R.N.REVENIMIENTO DE 8 A 10 CM, T.M.A. 3/4", GRAVA TRITURADA, ACABADO PULIDO EN PARTE DE SUPERIOR Y DOBLADOR EN ARISTAS, INCLUYE: COMPACTADO DE PLANTILLA, CIMBRADO, COLADO, VIBRADO, ACABADO, DESCIMBRADO, ALINEADO, NIVELADO, Y CURADO EN SU PARTE SUPERIOR CON MEMBRANA BASE AGUA A RAZON DE 1 LTO/M2, JUNTA DE AISLAMIENTO LONGITUDINAL AL COMBINAR CON OTRO ELEMENTO Y TRANSVERSAL @ 30 MT MAXIMO, SELLADO CON SELLADOR AUTONIVELANTE LONGITUDINAL, TRABAJO TERMINADO, .P.U.O.T.	ML	228.8	$323.24	$73,957.31
43	RELLENO COMPACTADO AL 90% CON MATERIAL DE BANCO EN CAPAS DE 20 CM UTILIZANDO BAILARINA. INCLUYE: SUMINISTRO DE TEPETATE (MATERIAL DE BANCO) EN LA OBRA, ABUNDAMIENTO, ACARREOS DENTRO DE LA OBRA, CRIBADO, RETIRO DE MATERIAL, MANO DE OBRA Y EQUIPO, LIMPIEZAS, TRABAJO TERMINADO.	M3	50.34	$377.90	$19,023.49
44	CARGA MECANICA Y ACARREO DE MATERIAL PRODUCTO DE EXCAVACION Y DEMOLICION EN CAMION DE VOLTEO AL 1er. KM, VOLUMEN MEDIDO COMPACTO.	M3	50.34	$33.94	$1,708.54
45	ACARREO DE MATERIAL PRODUCTO DE EXCAVACION Y/O DEMOLICION EN CAMION DE VOLTEO A KILOMETROS SUBSECUENTES, AL TIRADERO OFICIAL AUTORIZADO MAS CERCANO AUTORIZADO POR LA SUPERVISION, VOLUMEN MEDIDO COMPACTO.	M3-KM	654.37	$10.71	$7,008.30
				Totales por Partida	**$107,484.52**
	PARTIDA: **BANQUETA Y RAMPA**				
47	EXCAVACION A MAQUINA Y/O A MANO EN MATERIAL TIPO II, EN SECO O PRESENCIA DE AGUA, INCLUYE. CORTE DE RAIZ DE CUALQUIER TAMAÑO Y GROSOR, HASTA UNA PROFUNDIDAD DE 40 CM DESPUES DE DESMONTE, DESPALME Y/O DEMOLICION DE SUPERFICIE O ELEMENTO ESTRUCTURAL O DE ACABADO, PROTECCION DE AREAS ADYACENTES, SIN DAÑAR AREAS ALEDAÑAS, CARGA Y ACARREO A TIRADERO OFICIAL, CONSERVACION DE LA MISMA, TRABAJO TERMINADO, LIMPIEZAS.	M3	32.98	$73.45	$2,422.38
48	CARGA MECANICA Y ACARREO DE MATERIAL PRODUCTO DE EXCAVACION Y DEMOLICION EN CAMION DE VOLTEO AL 1er. KM, VOLUMEN MEDIDO COMPACTO.	M3	32.88	$33.94	$1,115.95
49	ACARREO DE MATERIAL PRODUCTO DE EXCAVACION Y/O DEMOLICION EN CAMION DE VOLTEO A KILOMETROS SUBSECUENTES, AL TIRADERO OFICIAL AUTORIZADO MAS CERCANO AUTORIZADO POR LA SUPERVISION, VOLUMEN MEDIDO COMPACTO.	M3-KM	427.71	$10.71	$4,580.77

Obra: SOBRECARPETA ASFÁLTICA Y PAVIMENTO HIDRÁULICO AV. DE LOS MAESTROS (CALZADA PONIENTE)

Ubicación: TRAMOS: ENTRE CALLE PROF. JOSÉ GUADALUPE PERALTA GÁMEZ Y BLVD. SIGLO XXI, AGUASCALIENTES Mpio.

Contratista: GRUPO CONSTRUCTOR URBANO AVANTE, S.A. DE C.V. (727)

No.	Concepto	Unidad	Cantidad	Precio Unitario	Importe Total
	GRUPO: **CONCRETO HIDRAULICO**				
	PARTIDA: **BANQUETA Y RAMPA**				
50	COMPACTACION POR MEDIOS MECANICOS DEL TERRENO NATURAL AL 95% DE SU PVSM EN UN ESPESOR DE 20 cm. INCLUYE: ESCARIFICACION, MANIOBRAS, HUMEDECIDO, SELECCION DE MATERIAL, ACARREOS DENTRO DE LA OBRA, MEDIDO COMPACTO, LIMPIEZAS, Y TODO LO NECESARIO PARA SU CORRECTA APLICACION, TRABAJO TERMINADO.	M2	118.93	$17.83	$2,120.52
51	RELLENO COMPACTADO AL 90% CON MATERIAL DE BANCO EN CAPAS DE 20 CM UTILIZANDO BAILARINA. INCLUYE: SUMINISTRO DE TEPETATE (MATERIAL DE BANCO) EN LA OBRA, ABUNDAMIENTO, ACARREOS DENTRO DE LA OBRA, CRIBADO, RETIRO DE MATERIAL, MANO DE OBRA Y EQUIPO, LIMPIEZAS, TRABAJO TERMINADO.	M3	36.7866	$377.90	$13,901.66
53	CONSTRUCCION DE BANQUETA DE 10 CM DE ESPESOR A BASE DE CONCRETO PREMEZCLADO F'C=150 KG/CM2, T.M.A. 3/4", R.N. GRAVA TRITURADA, REVENIMIENTI DE 10+-2 CM, ACABADO RAYADO FINO CON BROCHA DE PELO, JUNTAS FRIAS CON DOBLADOR DE 2" SECCION DE LOSAS COMO INDIQUE PROYECTO, INCLUYE: JUNTA A BASE DE ESPUMA DE POLIETILENO DE CELDAS CERRADAS DE 1/2" EN JUNTAS FRIAS LONGITUDINALES CON MUROS Y TRANSVERSALES DEL ELEMENTO, ASI COMO SU UNION CON ELEMENTOS VIEJOS O CAMBIO DE ELEMENTO, CIMBRADO, COLADO, DESCIMBRADO, CORTES CON CORTADORA DE DISCO, SELLADO DE CORTES CON SELLADOR AUTONIVELANTE Y TIRA DE RELLENO PREFORMADA NO ADHERENTE DE 1/8" (EN TODAS LAS JUNTAS DE CONTRACCCION Y CONSTRUCCION TRANSVERSALES), CURADO CON MEMBRANA QUIMICA APLICADA CON ASPERSOR, TRABAJO TERMINADO	M2	118.93	$321.72	$38,262.16
				Totales por Partida	**$62,403.44**
				Totales por Grupo	**$2,018,793.57**

Obra: SOBRECARPETA ASFÁLTICA Y PAVIMENTO HIDRÁULICO AV. DE LOS MAESTROS (CALZADA PONIENTE)

Ubicación: TRAMOS: ENTRE CALLE PROF. JOSÉ GUADALUPE PERALTA GÁMEZ Y BLVD. SIGLO XXI, AGUASCALIENTES Mpio.

Contratista: GRUPO CONSTRUCTOR URBANO AVANTE, S.A. DE C.V. (727)

No.	Concepto	Unidad	Cantidad	Precio Unitario	Importe Total
	GRUPO: OBRA COMPLEMENTARIA				
	PARTIDA: OBRA COMPLEMENTARIA				
56	RENIVELACIÓN DE RASANTE (PARTE SUPERIOR) DE CAJA DE VÁLVULAS TIPO 3 DE HASTA 1.96 X 1. 75 MTS, NIVELADO HASTA UNA ALTURA MAXIMA DE 10 CM, Y MINIMA DE 5 CM. MEDIDAS INTERIORES INCLUYE: TRAZO, EXCAVACIÓN, NIVELACIÓN, PREPARACIONES , Y DEMOLICIONES, RETIRO SIN RECUPERACIÓN DE TAPA DE FOFO EXISTENTE, MURO DE TABIQUE ROJO RECOCIDO COMÚN 7X14X28 CM DE 14 CM DE ESPESOR, JUNTEADO CON MORTERO CEMENTO-ARENA 1:3 APLANADO INTERIOR CON MORTERO CEMENTO ARENA 1:3 DE 2.00 CM DE ESPESOR ACABADO PULIDO, LOSA DE CONCRETO F´C= 250 KG/CM2 T.M.A. 19 MM DE 15 CM DE ESPESOR ARMADA CON VRS No. 3 @15 cm EN AMBOS SENTIDOS, CONTRAMARCO SENCILLO DE CANAL FoFo DE 100 mm, CONTRAMARCO CON TAPA DE FOFO, TIPO PESADO DE 50X50 CM, DEMOLICIÓN Y RECONSTRUCCIÓN DE APROCHES, CARGA Y ACARREOS DENTRO DE LA OBRA, CIMBRADO, DESCIMBRADO, COLADO, VIBRADO, LIMPIEZA PREVIA, FINAL, Y TODO LO NECESARIO PARA LA CORRECTA EJECUCIÓN DEL CONCEPTO. PZA 2.00	PZA	2	$13,259.14	$26,518.28
57	RENIVELACION DE RASANTE (PARTE SUPERIOR) DE REGISTRO ELECTRICO DE C.F.E. DE 1.50 X 1.50 MTS DE SECCION NIVELADO HASTA UNA ALTURA MAXIMA DE 10 CM, Y MINIMA DE 5 CM, INCLUYE: TRAZO, EXCAVACION, NIVELACIÓN, PREPARACIONES, Y DEMOLICIONES, RETIRO SIN RECUPERACION DE TAPA DE FOFO EXISTENTE, LOSA DE CONCRETO F´c= 250 KG/CM2 T.M.A. 19 MM DE 15 CM DE ESPESOR ARMADA CON VRS No. 3 @ 15 CM EN AMBOS SENTIDOS, ESPUMA DE POLIURETANO DE ALTA DENSIDAD EN TODO EL PERÍMETRO EXTERIOR DE 1/2", TAPA DE CONCRETO POLIMERICO 84-A, ESPECIFICACION C.F.E. TORNILLERIA, DEMOLICIÓN Y RECONSTRUCCIÓN DE APROCHES CARGAS Y ACAREOS DENTRO Y FUERA DE LA OBRA A DONDE SUPERVISION LO INDIQUE, CIMBRADO, DESCIMBRADO, COLADO, VIBRADO, CURADO CON MEMBRANA QUÍMICA BASE AGUA, LIMPIEZAS Y TODO LO NECESARIO PARA SU CORRECTA EJECUCIÓN DEL CONCEPTO.	PZA	2	$8,301.41	$16,602.82
			Totales por Partida		**$43,121.10**
	PARTIDA: LIMPIEZAS				
59	LIMPIEZA GENERAL DE LA OBRA, INCLUYE: BARRIDO, CARGA, ACARREOS Y RETIRO DE ESCOMBROS FUERA DE LA OBRA, TRABAJO TERMINADO.	M2	5584.083	$8.70	$48,581.52
			Totales por Partida		**$48,581.52**
	PARTIDA: SEÑALIZACION HORIZONTAL				
60	SUMINISTRO Y APLICACIÓN DE PINTURA EPOXICA BASE SOLVENTE COLOR AZUL (PANTONE 294) EN RAMPAS PARA PERSONAS CON DISCAPACIDAD CUALQUIER SECCIÓN SEGÚN PLANOS. INCLUYE: TRAZO, MANO DE OBRA, LIMPIEZA PREVIA DE SUPERFICIE, EQUIPO NECESARIO PARA SU EJECUCIÓN, Y TODO LO NECESARIO PARA SU CORRECTA EJECUCIÓN, TRABAJO TERMINADO.	M2	5.6	$166.24	$930.94
61	SUMINISTRO Y APLICACIÓN DE LOGOTIPO A (SILLA DE RUEDAS) EN PINTURA EPOXICA BASE SOLVENTE COLOR BLANCO EN RAMPAS PARA PERSONAS CON DISCAPACIDAD TAMAÑO Y DISEÑO SEGÚN PLANOS. INCLUYE: TRAZO, ENMASCARILLADO, PLANTILLA, MANO DE OBRA, LIMPIEZA PREVIA DE SUPERFICIE, EQUIPO NECESARIO PARA SU EJECUCIÓN, Y TODO LO NECESARIO PARA SU CORRECTA EJECUCIÓN, TRABAJO TERMINADO.	PZA	4	$94.06	$376.24

Obra: SOBRECARPETA ASFÁLTICA Y PAVIMENTO HIDRÁULICO AV. DE LOS MAESTROS (CALZADA PONIENTE)

Ubicación: TRAMOS: ENTRE CALLE PROF. JOSÉ GUADALUPE PERALTA GÁMEZ Y BLVD. SIGLO XXI, AGUASCALIENTES Mpio.

Contratista: GRUPO CONSTRUCTOR URBANO AVANTE, S.A. DE C.V. (727)

No.	Concepto	Unidad	Cantidad	Precio Unitario	Importe Total
	GRUPO: OBRA COMPLEMENTARIA				
	PARTIDA: SEÑALIZACION HORIZONTAL				
62	SUMINISTRO Y APLICACIÓN DE PINTURA BASE SOLVENTE PARA MARCAS EN GUARNICIONES CLASIFICACION M-12.1, M12.2 APLICADA SOBRE GUARNICIONES Y DENTELLONES DE CUALQUIER COLOR, SEGÚN SE REQUIERA Y SEGÚN NORMA S.C.T. SECADO AL TACTO EN 5 MIN Y AL DURO EN 30 MIN CON MICRO ESFERA , DESARROLLO DE 35 CM. INCLUYE: MATERIALES Y ESPECIFICACIONES QUE CUMPLAN CON LA NORMATIVA N-CMT-5-01-001/05, N-PRY-CAR-10-01-002/13 APLICADAS AL DIA DE HOY, TRAZO, MANO DE OBRA, LIMPIEZA PREVIA DE SUPERFICIE, EQUIPO NECESARIO PARA SU EJECUCIÓN, Y TODO LO NECESARIO PARA SU CORRECTA EJECUCIÓN, TRABAJO TERMINADO.	ML	1157	$30.42	$35,195.94
63	SUMINISTRO Y APLICACIÓN DE PINTURA TERMOPLASTICA ALQUIDALICA DE 120 MILESIMAS DE " (in) EN RAYA SEPARADORA DE SENTIDOS DE CIRCULACION CLASIFICACIÓN M - 1.1, LÍNEA CONTINUA SENCILLA DE DIVISIÓN DE CARRILES DE FRENTE EN PISO, DE 10 CM DE ANCHO, COLOR BLANCO Y/O AMARILLO CON MICRO ESFERA SEGÚN MANUAL DE SEÑALIZACIÓN VIAL Y DISPOSITIVOS DE SEGURIDAD SICT, SECADO AL TACTO EN 5 MIN Y AL DURO EN 30 MIN. INCLUYE: MATERIALES Y ESPECIFICACIONES QUE CUMPLAN CON LA NORMATIVA N-CMT-5-01-001/13, N-PRY-CAR-10-01-002/13 APLICADAS AL DIA DE HOY, MATERIAL APLICADO EN SU ESTADO DE FUSION A UNA TEMPERATURA MINIMA DE 204 C, LA SUPERFICIE DE CONCRETO O ASFALTO NO DEBE PRESENTAR UNA TEMPERATURA MENOR A LOS 10 C, ;TIEMPO DE SECADO EN RANGOS DE TEMPERATURA DE 10 C DEL SUSTRATO 2 MINUTOS, Y NO MAS DE 10 MINUTOS CUANDO EL SUSTRATO OSCILA ALREDEDOR DE 54C, TRAZO, ENMASCARILLADO, MANO DE OBRA, LIMPIEZA PREVIA Y FINAL DE SUPERFICIE, EQUIPO NECESARIO PARA SU EJECUCIÓN, Y TODO LO NECESARIO PARA SU CORRECTA EJECUCIÓN, TRABAJO TERMINADO.	ML	90	$47.50	$4,275.00
64	SUMINISTRO Y APLICACIÓN DE PINTURA TERMOPLASTICA ALQUIDALICA DE 120 MILESIMAS DE " (in) EN RAYA SEPARADORA DE SENTIDOS DE CIRCULACION CLASIFICACIÓN M - 1.2, RAYA DISCONTINUA SENCILLA, DE DIVISIÓN DE CARRILES PARA VELOCIDADES MENORES A 60 KM/HR DE FRENTE EN PISO, DESARROLLO DE 2.50 ML X 0.10 MTS DE ANCHO, CON UNA SEPARACIÓN DE 5.00 MTS ENTRE SI PROMEDIO, A BASE DE PINTURA PARA TRAFICO COLOR BLANCO CON MICRO ESFERA SEGÚN MANUAL DE SEÑALIZACIÓN VIAL Y DISPOSITIVOS DE SEGURIDAD SICT (S.C.T). INCLUYE: MATERIALES Y ESPECIFICACIONES QUE CUMPLAN CON LA NORMATIVA N-CMT-5-01-001/13, N-PRY-CAR-10-01-002/13 APLICADAS AL DIA DE HOY, MATERIAL APLICADO EN SU ESTADO DE FUSION A UNA TEMPERATURA MINIMA DE 204 C, LA SUPERFICIE DE CONCRETO O ASFALTO NO DEBE PRESENTAR UNA TEMPERATURA MENOR A LOS 10 C, ;TIEMPO DE SECADO EN RANGOS DE TEMPERATURA DE 10 C DEL SUSTRATO 2 MINUTOS, Y NO MAS DE 10 MINUTOS CUANDO EL SUSTRATO OSCILA ALREDEDOR DE 54C, TRAZO, ENMASCARILLADO, MANO DE OBRA, LIMPIEZA PREVIA Y FINAL DE SUPERFICIE, EQUIPO NECESARIO PARA SU EJECUCIÓN, Y TODO LO NECESARIO PARA SU CORRECTA EJECUCIÓN, TRABAJO TERMINADO.	ML	1203.5	$47.50	$57,166.25

Obra: SOBRECARPETA ASFÁLTICA Y PAVIMENTO HIDRÁULICO AV. DE LOS MAESTROS (CALZADA PONIENTE)

Ubicación: TRAMOS: ENTRE CALLE PROF. JOSÉ GUADALUPE PERALTA GÁMEZ Y BLVD. SIGLO XXI, AGUASCALIENTES Mpio.

Contratista: GRUPO CONSTRUCTOR URBANO AVANTE, S.A. DE C.V. (727)

No.	Concepto	Unidad	Cantidad	Precio Unitario	Importe Total
	GRUPO: OBRA COMPLEMENTARIA				
	PARTIDA: SEÑALIZACION HORIZONTAL				
65	SUMINISTRO Y APLICACIÓN DE PINTURA TERMOPLASTICA ALQUIDALICA DE 120 MILESIMAS DE " (in) EN RAYA EN LA ORILLA DEL ARROYO VIAL CLASIFICACIÓN M - 3.3, CONTINUA IZQUIERDA, PARA VIALIDADES URBANAS DE FRENTE EN PISO, DE 10 CM DE ANCHO Y SEPARADA 15 CM. DE LA GUARNICION, A BASE DE PINTURA PARA TRAFICO COLOR BLANCO CON MICRO ESFERA SEGÚN MANUAL DE SEÑALIZACIÓN VIAL Y DISPOSITIVOS DE SEGURIDAD SICT (S.C.T)., INCLUYE: MATERIALES Y ESPECIFICACIONES QUE CUMPLAN CON LA NORMATIVA N-CMT-5-01-001/13, N-PRY-CAR-10-01-002/13 APLICADAS AL DIA DE HOY, MATERIAL APLICADO EN SU ESTADO DE FUSION A UNA TEMPERATURA MINIMA DE 204 C, LA SUPERFICIE DE CONCRETO O ASFALTO NO DEBE PRESENTAR UNA TEMPERATURA MENOR A LOS 10 C, ;TIEMPO DE SECADO EN RANGOS DE TEMPERATURA DE 10 C DEL SUSTRATO 2 MINUTOS, Y NO MAS DE 10 MINUTOS CUANDO EL SUSTRATO OSCILA ALREDEDOR DE 54C, TRAZO, ENMASCARILLADO, MANO DE OBRA, LIMPIEZA PREVIA Y FINAL DE SUPERFICIE, EQUIPO NECESARIO PARA SU EJECUCIÓN, Y TODO LO NECESARIO PARA SU CORRECTA EJECUCIÓN, TRABAJO TERMINADO.	ML	553	$47.50	$26,267.50
66	SUMINISTRO Y APLICACIÓN DE PINTURA TERMOPLASTICA ALQUIDALICA DE 120 MILESIMAS DE " (in) EN RAYA GUIA EN ZONAS DE TRANSICION CLASIFICACIÓN M - 4, PARA INDICAR LÍNEA GUÍA EN ZONA DE TRANSICIÓN DE FRENTE EN PISO, DESARROLLO DE 2.00 X 0.10 MTS, CON UNA SEPARACIÓN DE 4.00 MTS ENTRE SI PROMEDIO, A BASE DE PINTURA PARA TRAFICO COLOR BLANCO CON MICRO ESFERA SEGÚN MANUAL DE SEÑALIZACIÓN VIAL Y DISPOSITIVOS DE SEGURIDAD SICT (S.C.T)., MCA. COMEX O SIMILAR, SECADO AL TACTO EN 5 MIN Y AL DURO EN 30 MIN.INCLUYE: MATERIALES Y ESPECIFICACIONES QUE CUMPLAN CON LA NORMATIVA N-CMT-5-01-001/13, N-PRY-CAR-10-01-002/13 APLICADAS AL DIA DE HOY, MATERIAL APLICADO EN SU ESTADO DE FUSION A UNA TEMPERATURA MINIMA DE 204 C, LA SUPERFICIE DE CONCRETO O ASFALTO NO DEBE PRESENTAR UNA TEMPERATURA MENOR A LOS 10 C, ;TIEMPO DE SECADO EN RANGOS DE TEMPERATURA DE 10 C DEL SUSTRATO 2 MINUTOS, Y NO MAS DE 10 MINUTOS CUANDO EL SUSTRATO OSCILA ALREDEDOR DE 54C, TRAZO, ENMASCARILLADO, MANO DE OBRA, LIMPIEZA PREVIA Y FINAL DE SUPERFICIE, EQUIPO NECESARIO PARA SU EJECUCIÓN, Y TODO LO NECESARIO PARA SU CORRECTA EJECUCIÓN, TRABAJO TERMINADO.	ML	100	$47.50	$4,750.00
67	SUMINISTRO Y APLICACIÓN DE PINTURA TERMOPLASTICA ALQUIDALICA DE 120 MILESIMAS DE " (in) EN RAYA CANALIZADORA CLASIFICACIÓN M - 5, PARA INDICAR ENTRADA Y SALIDA EN BIFURCACIONES, COLOR BLANCO O AMARILLO, REFLEJANTE CON MICRO ESFERA DE VIDRIO EN PROPORCIÓN SEGÚN MANUAL DE SEÑALIZACIÓN VIAL Y DISPOSITIVOS DE SEGURIDAD SICT (S.C.T). DE 0.20 MTS DE ANCHO DE LONGITUD Y TRAZO VARIABLE (SEGUN PROYECTO), INCLUYE: MATERIALES Y ESPECIFICACIONES QUE CUMPLAN CON LA NORMATIVA N-CMT-5-01-001/13, N-PRY-CAR-10-01-002/13 APLICADAS AL DIA DE HOY, MATERIAL APLICADO EN SU ESTADO DE FUSION A UNA TEMPERATURA MINIMA DE 204 C, LA SUPERFICIE DE CONCRETO O ASFALTO NO DEBE PRESENTAR UNA TEMPERATURA MENOR A LOS 10 C, ;TIEMPO DE SECADO EN RANGOS DE TEMPERATURA DE 10 C DEL SUSTRATO 2 MINUTOS, Y NO MAS DE 10 MINUTOS CUANDO EL SUSTRATO OSCILA ALREDEDOR DE 54C, TRAZO, ENMASCARILLADO, MANO DE OBRA, LIMPIEZA PREVIA Y FINAL DE SUPERFICIE, EQUIPO NECESARIO PARA SU EJECUCIÓN, Y TODO LO NECESARIO PARA SU CORRECTA EJECUCIÓN, TRABAJO TERMINADO.	ML	20	$95.43	$1,908.60

Obra: SOBRECARPETA ASFÁLTICA Y PAVIMENTO HIDRÁULICO AV. DE LOS MAESTROS (CALZADA PONIENTE)

Ubicación: TRAMOS: ENTRE CALLE PROF. JOSÉ GUADALUPE PERALTA GÁMEZ Y BLVD. SIGLO XXI, AGUASCALIENTES Mpio.

Contratista: GRUPO CONSTRUCTOR URBANO AVANTE, S.A. DE C.V. (727)

No.	Concepto	Unidad	Cantidad	Precio Unitario	Importe Total
	GRUPO: OBRA COMPLEMENTARIA				
	PARTIDA: SEÑALIZACION HORIZONTAL				
68	SUMINISTRO Y APLICACIÓN DE PINTURA TERMOPLASTICA ALQUIDALICA DE 120 MILESIMAS DE " (in) EN RAYA DE ALTO CLASIFICACIÓN M - 6, PARA INDICAR ALTO EN CRUCEROS, COLOR BLANCO, REFLEJANTE CON MICRO ESFERA DE VIDRIO EN PROPORCIÓN SEGÚN MANUAL DE SEÑALIZACIÓN VIAL Y DISPOSITIVOS DE SEGURIDAD SICT (S.C.T). DE 0.60 MTS DE ANCHO DE LONGITUD VARIABLE, INCLUYE: MATERIALES Y ESPECIFICACIONES QUE CUMPLAN CON LA NORMATIVA N-CMT-5-01-001/13, N-PRY-CAR-10-01-002/13 APLICADAS AL DIA DE HOY, MATERIAL APLICADO EN SU ESTADO DE FUSION A UNA TEMPERATURA MINIMA DE 204 C, LA SUPERFICIE DE CONCRETO O ASFALTO NO DEBE PRESENTAR UNA TEMPERATURA MENOR A LOS 10 C, ;TIEMPO DE SECADO EN RANGOS DE TEMPERATURA DE 10 C DEL SUSTRATO 2 MINUTOS, Y NO MAS DE 10 MINUTOS CUANDO EL SUSTRATO OSCILA ALREDEDOR DE 54C, TRAZO, ENMASCARILLADO, MANO DE OBRA, LIMPIEZA PREVIA Y FINAL DE SUPERFICIE, EQUIPO NECESARIO PARA SU EJECUCIÓN, Y TODO LO NECESARIO PARA SU CORRECTA EJECUCIÓN, TRABAJO TERMINADO.	ML	15	$339.67	$5,095.05
69	SUMINISTRO Y APLICACIÓN DE PINTURA TERMOPLASTICA ALQUIDALICA DE 120 MILESIMAS DE " (in) EN RAYA PARA CRUCE PEATONAL CLASIFICACIÓN M - 7.1, PARA INDICAR " CRUCE PEATONAL EN VIAS PRIMARIAS", COLOR AMARILLO, REFLEJANTE CON MICRO ESFERA DE VIDRIO EN PROPORCIÓN SEGÚN MANUAL DE SEÑALIZACIÓN VIAL Y DISPOSITIVOS DE SEGURIDAD SICT (S.C.T). DE 0.40 MTS DE ANCHO Y 3.5 MTS. DE LONGITUD POR EL ANCHO DE LA VIALIDAD, CON UNA SEPARACIÓN DE 0.40 MTS. ENTRE ELLAS, INCLUYE: MATERIALES Y ESPECIFICACIONES QUE CUMPLAN CON LA NORMATIVA N-CMT-5-01-001/13, N-PRY-CAR-10-01-002/13 APLICADAS AL DIA DE HOY, MATERIAL APLICADO EN SU ESTADO DE FUSION A UNA TEMPERATURA MINIMA DE 204 C, LA SUPERFICIE DE CONCRETO O ASFALTO NO DEBE PRESENTAR UNA TEMPERATURA MENOR A LOS 10 C, ;TIEMPO DE SECADO EN RANGOS DE TEMPERATURA DE 10 C DEL SUSTRATO 2 MINUTOS, Y NO MAS DE 10 MINUTOS CUANDO EL SUSTRATO OSCILA ALREDEDOR DE 54C, TRAZO, ENMASCARILLADO, MANO DE OBRA, LIMPIEZA PREVIA Y FINAL DE SUPERFICIE, EQUIPO NECESARIO PARA SU EJECUCIÓN, Y TODO LO NECESARIO PARA SU CORRECTA EJECUCIÓN, TRABAJO TERMINADO.	M2	51	$470.98	$24,019.98
70	SUMINISTRO Y APLICACIÓN DE PINTURA TERMOPLASTICA ALQUIDALICA DE 120 MILESIMAS DE " (in) EN FLECHAS CLASIFICACIÓN M - 11.1, "FLECHA SENCILLA" PARA INDICAR SENTIDO DE CIRCULACIÓN , EN VIALIDADES PARA VELOCIDAD MENOR A 60KM POR HORA DIMENSION NORMATIVA SEGUN MANUAL DE SEÑALIZACIÓN VIAL Y DISPOSITIVOS DE SEGURIDAD SICT (SCT) Y/O (VER PLANO DE SEÑALAMIENTOS), COLOR BLANCO, REFLEJANTE CON MICRO ESFERA DE VIDRIO EN PROPORCIÓN SEGÚN NORMA SCT, INCLUYE: MATERIALES Y ESPECIFICACIONES QUE CUMPLAN CON LA NORMATIVA N-CMT-5-01-001/13, N-PRY-CAR-10-01-002/13 APLICADAS AL DIA DE HOY, MATERIAL APLICADO EN SU ESTADO DE FUSION A UNA TEMPERATURA MINIMA DE 204 C, LA SUPERFICIE DE CONCRETO O ASFALTO NO DEBE PRESENTAR UNA TEMPERATURA MENOR A LOS 10 C, ;TIEMPO DE SECADO EN RANGOS DE TEMPERATURA DE 10 C DEL SUSTRATO 2 MINUTOS, Y NO MAS DE 10 MINUTOS CUANDO EL SUSTRATO OSCILA ALREDEDOR DE 54C, TRAZO, ENMASCARILLADO, MANO DE OBRA, LIMPIEZA PREVIA Y FINAL DE SUPERFICIE, EQUIPO NECESARIO PARA SU EJECUCIÓN, Y TODO LO NECESARIO PARA SU CORRECTA EJECUCIÓN, TRABAJO TERMINADO.	PZA	6	$965.94	$5,795.64

Obra: SOBRECARPETA ASFÁLTICA Y PAVIMENTO HIDRÁULICO AV. DE LOS MAESTROS (CALZADA PONIENTE)

Ubicación: TRAMOS: ENTRE CALLE PROF. JOSÉ GUADALUPE PERALTA GÁMEZ Y BLVD. SIGLO XXI, AGUASCALIENTES Mpio.

Contratista: GRUPO CONSTRUCTOR URBANO AVANTE, S.A. DE C.V. (727)

No.	Concepto	Unidad	Cantidad	Precio Unitario	Importe Total
	GRUPO: OBRA COMPLEMENTARIA				
	PARTIDA: SEÑALIZACION HORIZONTAL				
71	SUMINISTRO Y APLICACIÓN DE PINTURA TERMOPLASTICA ALQUIDALICA DE 120 MILESIMAS DE " (in) EN FLECHAS CLASIFICACIÓN M - 11.1, " FLECHA CABEZA DOBLE" PARA INDICAR SENTIDO DE CIRCULACIÓN (VUELTA IZQUIERDA O DERECHA), EN VIALIDADES PARA VELOCIDAD MENOR A 60KM POR HORA SEGUN MANUAL DE SEÑALIZACIÓN VIAL Y DISPOSITIVOS DE SEGURIDAD SICT (SCT), (VER PLANO DE SEÑALAMIENTOS), EN COLOR BLANCO, REFLEJANTE CON MICRO ESFERA DE VIDRIO EN PROPORCIÓN SEGÚN NORMA SCT, INCLUYE: MATERIALES Y ESPECIFICACIONES QUE CUMPLAN CON LA NORMATIVA N-CMT-5-01-001/13, N-PRY-CAR-10-01-002/13 APLICADAS AL DIA DE HOY, MATERIAL APLICADO EN SU ESTADO DE FUSION A UNA TEMPERATURA MINIMA DE 204 C, LA SUPERFICIE DE CONCRETO O ASFALTO NO DEBE PRESENTAR UNA TEMPERATURA MENOR A LOS 10 C, ;TIEMPO DE SECADO EN RANGOS DE TEMPERATURA DE 10 C DEL SUSTRATO 2 MINUTOS, Y NO MAS DE 10 MINUTOS CUANDO EL SUSTRATO OSCILA ALREDEDOR DE 54C, TRAZO, ENMASCARILLADO, MANO DE OBRA, LIMPIEZA PREVIA Y FINAL DE SUPERFICIE, EQUIPO NECESARIO PARA SU EJECUCIÓN, Y TODO LO NECESARIO PARA SU CORRECTA EJECUCIÓN, TRABAJO TERMINADO.	PZA	1	$1,288.13	$1,288.13
72	SUMINISTRO Y COLOCACION DE VIALETA STANDARD (S-200) DE 10X10CM. COLOR: CUERPO AMARILLO Y REFLEJANTE AMARILLO 1 CARA MARCA SEA O SIMILAR EN CALIDAD Y ESPECIFICACIONES DE FICHA TECNICA, ANCLADO EN PAVIMENTO SISTEMA DE SUJECION DE ALTO AGARRE BASE CUÑAS CON AB PEGAMENTO EPOXICO 50/50 RESISTENTE A ALTA TEMPERATURA (VER PLANO DE DETALLES DE SEÑALAMIENTOS HORIZONTAL Y VERTICAL). INCLUYE: TRAZO, ALINEACION, ELEVACION CUALQUIER ALTURA, TRABAJO TERMINADO, LIMPIEZAS.	PZA	160	$47.73	$7,636.80
73	SUMINISTRO Y COLOCACION DE VIALETA SOLAR DE 10X10CM. COLOR: CUERPO ALUMINIO 3 LED DOS CARAS REFLEJANTES MARCA CREATIVAL VT-29 O SIMILAR EN CALIDAD Y ESPECIFICACIONES DE FICHA TÉCNICA, FIJADO EN PAVIMENTO CON SISTEMA DE SUJECIÓN DE ALTO AGARRE PEGAMENTO EPOXICO 100 A/B (RESINA EPÓXICA/RESINA POLIAMIDA MODIFICADA), RESISTENTE A ALTA TEMPERATURA (VER PLANO DE DETALLES DE SEÑALAMIENTOS HORIZONTAL), INCLUYE: LIMPIEZA PREVIA DE LA SUPERFICIE+C92, PREPARACIÓN DE LA SUPERFICIE, TRAZO, ALINEACIÓN, Y TODO LO NECESARIO PARA SU CORRECTA EJECUCIÓN, TRABAJO TERMINADO.	PZA	50	$512.67	$25,633.50
74	SUMINISTRO Y APLICACION DE PINTURA DE ESMALTE APLICADA CON BROCHA DE AIRE EN PASAMANOS METALICO (PARAPETO EXISTENTE) FABRICADO A BASE DE TUBO NEGRO DE 3" (2 PZS LONGITUDINALES) , POSTES DE 90 CM DE ALTO A BASE DE TUBO NEGRO DE 4" SEPARADOS @ 1.80 MTS INCLUYE: PREPARACION DE LA SUPERFICIES, RETIRO DE OXIDO, GRASAS, SUCIEDAD, ETC, DEJANDO SUPERFICIE LIMPIA Y TRATADA PARA RECIBIR ACABADO INICIAL PRIMER ANTICORROSIVO COLOR ROJO ÓXIDO Y TERMINADO CON PINTURA DE ESMALTE CALIDAD COMEX COLOR BLANCO O SIMILAR EN PRECIO Y CALIDAD, MANOS DE PINTURA SUFICIENTES PARA CUBRIR TOTAL Y SATISFACTORIAMENTE LA SUPERFICIE, MATERIALES, MANO DE OBRA, ACARREOS, FLETES, DESPERDICIOS, LIMPIEZAS, TRABAJO TERMINADO.	ML	20	$108.12	$2,162.40

Obra: SOBRECARPETA ASFÁLTICA Y PAVIMENTO HIDRÁULICO AV. DE LOS MAESTROS (CALZADA PONIENTE)

Ubicación: TRAMOS: ENTRE CALLE PROF. JOSÉ GUADALUPE PERALTA GÁMEZ Y BLVD. SIGLO XXI, AGUASCALIENTES Mpio.

Contratista: GRUPO CONSTRUCTOR URBANO AVANTE, S.A. DE C.V. (727)

No.	Concepto	Unidad	Cantidad	Precio Unitario	Importe Total
	GRUPO: OBRA COMPLEMENTARIA				
	PARTIDA: SEÑALIZACION HORIZONTAL				
75	SUMINISTRO Y APLICACION DE PINTURA VINILICA APLICADA CON BROCHA Y RODILLO EN PARAPETO DE CONCRETO INCLUYE: PREPARACION DE LA SUPERFICIES, RETIRO DE CAPAS DE PINTURA SUELTA, GRASAS, SUCIEDAD, ETC, DEJANDO SUPERFICIE LIMPIA Y TRATADA PARA RECIBIR, UNA MANO DE SELLADOR Y PINTURA VINILICA PARA EXTERIORES CALIDAD COMEX COLOR BLANCO O SIMILAR EN PRECIO Y CALIDAD, MANOS DE PINTURA SUFICIENTES PARA CUBRIR TOTAL Y SATISFACTORIAMENTE LA SUPERFICIE, MATERIALES, MANO DE OBRA, ACARREOS, FLETES, DESPERDICIOS, LIMPIEZAS, TRABAJO TERMINADO.	M2	160	$76.33	$12,212.80
			Totales por Partida		$214,714.77
	PARTIDA: SEÑALAMIENTO VERTICAL				
76	SUMINISTRO Y COLOCACION DE SEÑALAMIENTO VERTICAL DE PREVENCION SP-19 (SALIDA), DISEÑO NORMATIVO SCT, HECHO A ABASE DE LAMINA GALVANIZADA CON CEJA DE 72 X 72 CM CALIBRE 16, CON TERMINADO GRADO INGENIERIA EN SU TOTALIDAD, EL COLOR SERA REFLEJANTE GRADO INGENIERIA Y SIMBOLOS EN COLOR REFLEJANTE, TODOS LOS COLORES RESISTENTES A LA INTEMPERIE, FIJADA MEDIANTE BARRENADO Y TORNILLOS DE 2 1/2" X 5/16" A UN POSTE DE PTR DE 2 X 2" CALIBRE 14 EN ACABADO GALVANIZADO Y CON UNA ALTURA DE 2.5 MTS AL NIVEL DE BANQUETA A LA PARTE INFERIOR DE LA LAMINA MAS EL EXCEDENTE REQUERIDO PARA FIJAR LAS LAMINAS Y ANCLADO DE 50 CM DE PROFUNDIDAD CON ANGULO TRANSVERSAL DE 1 X 1" DE 25 CM, EN DADO DE CONCRETO F´c=150 KG/CM2 DE 30 CM DE LADO (VER PLANO DE DETALLES CRITERIOS DE ANCLAJE DE SEÑALAMIENTO VERTICAL, DETALLE SEÑ-02 Y SEÑ 03), MCA ASEA O SIMILAR EN CALIDAD Y ESPECIFICACIONES, INCLUYE: MANO DE OBRA, FLETES, MANIOBRAS LIMPIEZAS Y RETIRO DEL SOBRANTE FUERA DE LA OBRA HASTA TIRADERO OFICIAL, TRABAJO TERMINADO.	PZA	1	$2,471.26	$2,471.26
77	SUMINISTRO Y COLOCACION DE SEÑALAMIENTO VERTICAL DE INDICACION OD-6 (INDICADOR DE BANQUETA, BORDE U OBJETO), DISEÑO NORMATIVO SCT, HECHO A ABASE DE LAMINA GALVANIZADA CON CEJA DE 30 X 122 CM CALIBRE 16, CON TERMINADO GRADO INGENIERIA EN SU TOTALIDAD, EL COLOR SERA REFLEJANTE GRADO INGENIERIA Y SIMBOLOS EN COLOR REFLEJANTE, TODOS LOS COLORES RESISTENTES A LA INTEMPERIE, FIJADA MEDIANTE BARRENADO Y TORNILLOS DE 2 1/2" X 5/16" A UN POSTE DE PTR DE 2 X 2" CALIBRE 14 EN ACABADO GALVANIZADO Y CON UNA ALTURA DE 20 CM AL NIVEL DE BANQUETA A LA PARTE INFERIOR DE LA LAMINA MAS EL EXCEDENTE REQUERIDO PARA FIJAR LAS LAMINAS Y ANCLADO DE 50 CM DE PROFUNDIDAD CON ANGULO TRANSVERSAL DE 1 X 1" DE 25 CM, EN DADO DE CONCRETO F´c=150 KG/CM2 DE 30 CM DE LADO (VER PLANO DE DETALLES CRITERIOS DE ANCLAJE DE SEÑALAMIENTO VERTICAL, DETALLE SEÑ-02 Y SEÑ 03), MCA ASEA O SIMILAR EN CALIDAD Y ESPECIFICACIONES, INCLUYE: MANO DE OBRA, FLETES, MANIOBRAS LIMPIEZAS Y RETIRO DEL SOBRANTE FUERA DE LA OBRA HASTA TIRADERO OFICIAL, TRABAJO TERMINADO.	PZA	1	$1,275.16	$1,275.16

Obra: SOBRECARPETA ASFÁLTICA Y PAVIMENTO HIDRÁULICO AV. DE LOS MAESTROS (CALZADA PONIENTE)

Ubicación: TRAMOS: ENTRE CALLE PROF. JOSÉ GUADALUPE PERALTA GÁMEZ Y BLVD. SIGLO XXI, AGUASCALIENTES Mpio.

Contratista: GRUPO CONSTRUCTOR URBANO AVANTE, S.A. DE C.V. (727)

No.	Concepto	Unidad	Cantidad	Precio Unitario	Importe Total
	GRUPO: OBRA COMPLEMENTARIA				
	PARTIDA: SEÑALAMIENTO VERTICAL				
78	SUMINISTRO Y COLOCACION DE SEÑALAMIENTO VERTICAL DE RESTRICCION SR-9 (VELOCIDAD MAXIMA), DISEÑO NORMATIVO SCT, HECHO A ABASE DE LAMINA GALVANIZADA CON CEJA DE 72 X 72 CM CALIBRE 16, CON TERMINADO GRADO INGENIERIA EN SU TOTALIDAD, EL COLOR SERA REFLEJANTE GRADO INGENIERIA Y SIMBOLOS EN COLOR REFLEJANTE, TODOS LOS COLORES RESISTENTES A LA INTEMPERIE, FIJADA MEDIANTE BARRENADO Y TORNILLOS DE 2 1/2" X 5/16" A UN POSTE DE PTR DE 2 X 2" CALIBRE 14 EN ACABADO GALVANIZADO Y CON UNA ALTURA DE 2.5 MTS AL NIVEL DE BANQUETA A LA PARTE INFERIOR DE LA LAMINA MAS EL EXCEDENTE REQUERIDO PARA FIJAR LAS LAMINAS Y ANCLADO DE 50 CM DE PROFUNDIDAD CON ANGULO TRANSVERSAL DE 1 X 1" DE 25 CM, EN DADO DE CONCRETO F´c=150 KG/CM2 DE 30 CM DE LADO (VER PLANO DE DETALLES CRITERIOS DE ANCLAJE DE SEÑALAMIENTO VERTICAL, DETALLE SEÑ-02 Y SEÑ 03), MCA ASEA O SIMILAR EN CALIDAD Y ESPECIFICACIONES, INCLUYE: MANO DE OBRA, FLETES, MANIOBRAS LIMPIEZAS Y RETIRO DEL SOBRANTE FUERA DE LA OBRA HASTA TIRADERO OFICIAL, TRABAJO TERMINADO.	PZA	2	$2,508.50	$5,017.00
				Totales por Partida	$8,763.42
				Totales por Grupo	$315,180.82

Obra: SOBRECARPETA ASFÁLTICA Y PAVIMENTO HIDRÁULICO AV. DE LOS MAESTROS (CALZADA PONIENTE)

Ubicación: TRAMOS: ENTRE CALLE PROF. JOSÉ GUADALUPE PERALTA GÁMEZ Y BLVD. SIGLO XXI, AGUASCALIENTES Mpio.

Contratista: GRUPO CONSTRUCTOR URBANO AVANTE, S.A. DE C.V. (727)

No.	Concepto	Unidad	Cantidad	Precio Unitario	Importe Total
GRUPO: HIDRAULICO SANITARIO					
PARTIDA: LINEA DE AGUA POTABLE					
103	BOMBEO DE ACHIQUE CON BOMBA DE 3" Y 8 H.P., OPERACION BOMBA Y EQUIPO COMPLEMENTARIO CON MANGUERA Y PICHANCHA.	HR	48	$176.71	$8,482.08
			Totales por Partida		$8,482.08
			Totales por Grupo		$8,482.08

Obra: SOBRECARPETA ASFÁLTICA Y PAVIMENTO HIDRÁULICO AV. DE LOS MAESTROS (CALZADA PONIENTE)

Ubicación: TRAMOS: ENTRE CALLE PROF. JOSÉ GUADALUPE PERALTA GÁMEZ Y BLVD. SIGLO XXI, AGUASCALIENTES Mpio.

Contratista: GRUPO CONSTRUCTOR URBANO AVANTE, S.A. DE C.V. (727)

No.	Concepto	Unidad	Cantidad	Precio Unitario	Importe Total
GRUPO: EXTRAORDINARIO					
PARTIDA: EXTRAORDINARIOS					
125	CONSTRUCCION DE PAVIMENTO HIDRAULICO A BASE DE CONCRETO PREMEZCLADO MR=42 KG/CM2 TMA 1 1/2" GRAVA TRITURADA, REVENIMIENTO DE 6 A 8 CM RESISTENCIA RAPIDA 7 DIAS DE 20 CM DE ESPESOR MODULADO EN LOSAS DE 3.5 MTS. (ANCHO) X 3.5 MTS (LARGO) COMO MAXIMO, CON CORTES EN LAS LOSAS DE 1/3 DEL ESPESOR DE LA LOSA (7 CM) Y SELLADO CON MATERIAL ELASTOMERICO Y TIRA PREFORMADA EN JUNTAS Y CORTES LONGITUDINALES Y TRANSVERSALES COLA DE RATA DE 1/8", ASI COMO EL APROCHE CON GUARNICION Y DENTELLON. INCLUYE: CIMBRADO, COLADO, VIBRADO CON INMERSION Y REGLA VIBRATORIA, DESCIMBRADO, REGLEADO FINAL, ACABADO CEPILLO DE ALUMINIO Y CON DOBLADOR, CALAFATEO, CURADO CON MEMBRANA BASE AGUA Y TODO LO NECESARIO PARA SU CORRECTA COLOCACION, P.U.O.T.	M2	2441.92	$729.46	$1,781,282.96
126	SUMINISTRO Y COLOCACION DE TUBERIA PAD DE 2" DE DIAMETRO PARA CRUCE ELECTRICO, INCLUYE: MATERIAL. ACARREO DE LA OBRA, MNAO DE OBRA, EXCAVACIONES, COMPACTACION CON BAILARINA Y TODO LOO NECESARIO PARA L ACORRECTA EJECUCION	ML	90	$100.94	$9,084.60

Totales por Partida		$1,790,367.56
Totales por Grupo		$1,790,367.56
Totales Presup.		$6,483,014.80
Anticipo	+	$1,876,409.91
Amortizac. Ant.	-	$1,876,409.91
SubTotal. Ant.	=	$6,483,014.80
IVA	+	$1,037,282.36
Total	=	$7,520,297.16

H. AYUNTAMIENTO CONSTITUCIONAL DEL MUNICIPIO DE AGUASCALIENTES 2014-2016


H. AYUNTAMIENTO DE AGUASCALIENTES
SECRETARÍA DE OBRAS PÚBLICAS
DIRECCIÓN DE SUPERVISIÓN DE OBRA


Aguascalientes
LA CIUDAD DE TU VIDA


MEMORIA FOTOGRAFICA


OBRA:	FISMDF-0086-2022 SOBRECARPETA ASFÁLTICA Y PAVIMENTO HIDRÁULICO AV. DE LOS MAESTROS (CALZADA PONIENTE)					
NO. DE CONTRATO:	FISMDF-0086-2022		CONTRATISTA:	GRUPO CONSTRUCTOR URBANO AVANTE, S.A. DE C.V.		

INICIO.

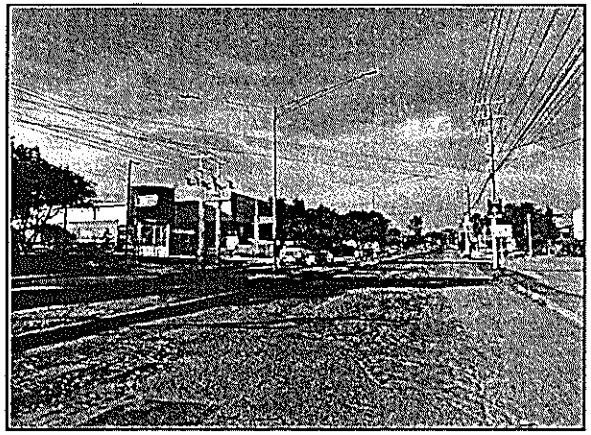

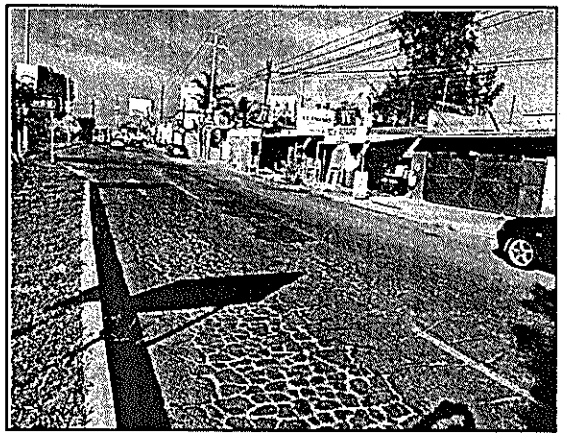

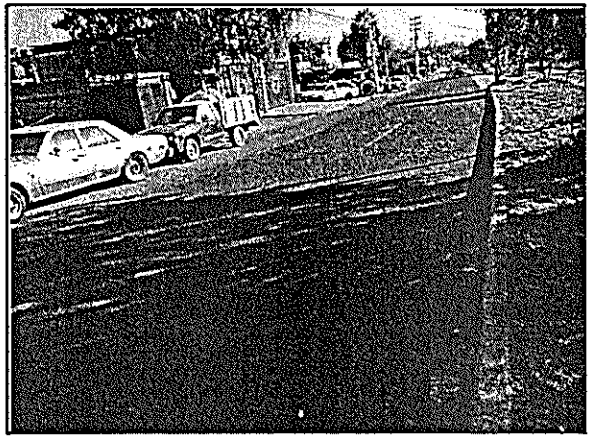

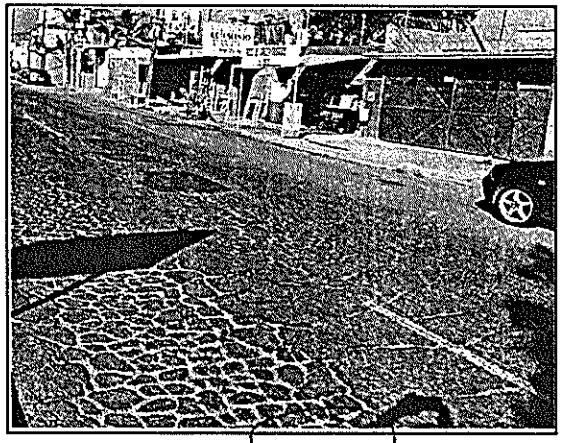

ARQ ARIADNA MEDINA
SUPERVISOR DE OBRA.

H. AYUNTAMIENTO DE AGUASCALIENTES
SECRETARÍA DE OBRAS PÚBLICAS
DIRECCIÓN DE SUPERVISIÓN DE OBRA


H. AYUNTAMIENTO CONSTITUCIONAL DEL MUNICIPIO DE AGUASCALIENTES 2014-2016


Aguascalientes
LA CIUDAD DE TU VIDA

MEMORIA FOTOGRAFICA


OBRA:	FISMDF-0086-2022 SOBRECARPETA ASFÁLTICA Y PAVIMENTO HIDRÁULICO AV. DE LOS MAESTROS (CALZADA PONIENTE)					
NO. DE CONTRATO:	FISMDF-0086-2022		CONTRATISTA:	GRUPO CONSTRUCTOR URBANO AVANTE, S.A. DE C.V.		

PROCESO

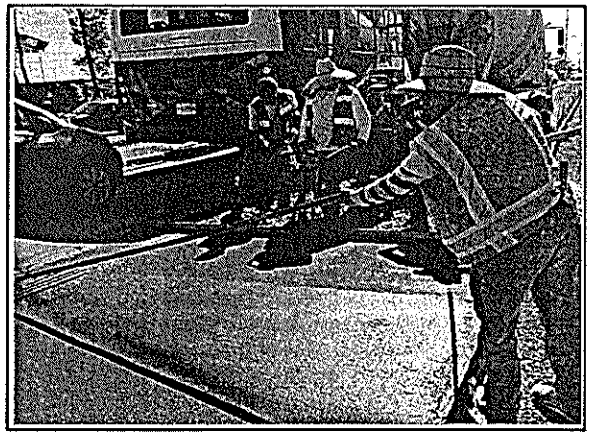

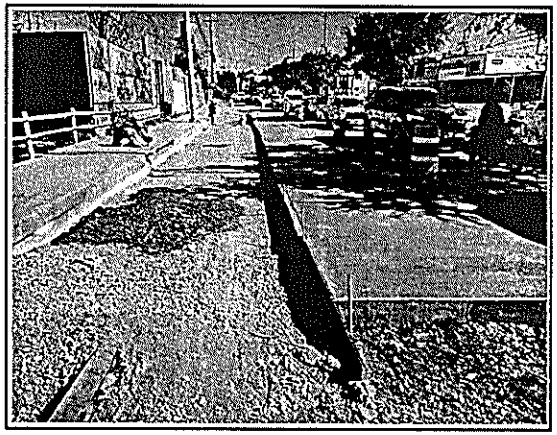



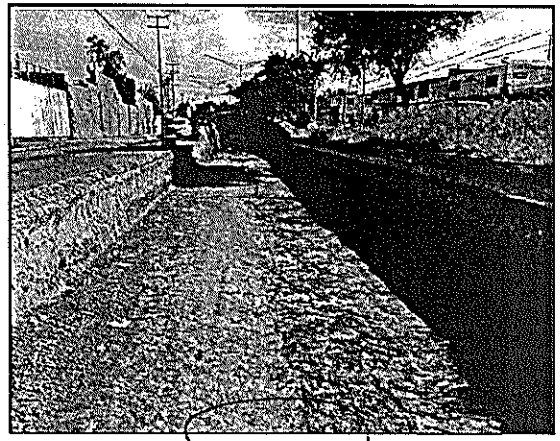

ARQ ARIADNA MEDINA
SUPERVISOR DE OBRA.

H. AYUNTAMIENTO CONSTITUCIONAL DEL MUNICIPIO DE AGUASCALIENTES 2014-2016

H. AYUNTAMIENTO DE AGUASCALIENTES
SECRETARÍA DE OBRAS PÚBLICAS
DIRECCIÓN DE SUPERVISIÓN DE OBRA

Aguascalientes
LA CIUDAD DE TU VIDA

MEMORIA FOTOGRAFICA

OBRA:	FISMDF-0086-2022 SOBRECARPETA ASFÁLTICA Y PAVIMENTO HIDRÁULICO AV. DE LOS MAESTROS (CALZADA PONIENTE)					
NO. DE CONTRATO:	FISMDF-0086-2022		CONTRATISTA:	GRUPO CONSTRUCTOR URBANO AVANTE, S.A. DE C.V.		

TERMINO

ARQ ARIADNA MEDINA
SUPERVISOR DE OBRA.

MODIFICADO

SECRETARÍA DE OBRAS PÚBLICAS

DIRECCIÓN DE SUPERVISIÓN DE OBRA

EJERCICIO 2022

N° DE CONTRATO: **FISMDF-0086-2022**

NOMBRE DE LA OBRA: **FISMDF-0086-2022 SOBRECARPETA ASFÁLTICA Y PAVIMENTO HIDRÁULICO AV. DE LOS MAESTROS (CALZADA PONIENTE)**

MONTO MODIFICADO FINAL: **$ 7,520,297.16**


VOLUMEN	UNIDAD	COMPONENTE DE LA OBRA	MONTO
138.63	M3	FRESADO UNIFORME DE LA SUPERFICIE DE RODADURA EN PAVIMENTO DE CONCRETO ASFALTICO 3-7 CM (5 cm de espesor promedio) MEDIANTE FRESADORA EN FRIO COMPACTA, EQUIPADA CON BANDA TRANSPORTADORA PARA CARGA DIRECTA SOBRE CAMION DE VOLTEO, INCLUYE: TRAMO DE PRUEBA AL INICIO DEL FRESADO PARA AUTORIZACION DE SUPERVISION (SUPERFICIE FRESADA UNIFORME Y SIN PROTUBERANCIAS NI ONDEOS), ACARREOS LOCALES, CARGA Y ACARREO A KM SUBSECUENTES (11 A 15 KM APROX) DE MATERIAL PRODUCTO DEL FRESADO DE CARPETA ASFALTICA EL TRASLADO SERA A PARQUE DE MAQUINARIA DE LA SOPMA, PIEZAS DE DESGASTE, COMBUSTIBLES, CONSUMIBLES, MANO DE OBRA, CUALQUIER VOLUMEN Y AREA,EQUIPO NECESARIO, LIMPIEZA FINA Y GRUESA, TRABAJO TERMINADO	$ 393,287.79
554.51	M3	BACHEO PROFUNDO AISLADO UTILIZANDO MATERIAL CALIDAD BASE HIDRAULICA PARA MAS DE UN MILLON DE EJES EQUIVALENTES DEL BANCO QUE ELIJA EL CONTRATISTA, INCISO N.CSV.CAR-1.02.004/03 DE LAS NORMAS DE CONSTRUCCION DE CARR. DE LA SCT, BASE HIDRAULICA MEJORADA CON CEMENTO EN PROPORCION DE 40 KILOS DE CEMENTO POR CADA M3, INCLUYE: PREPARACION, PERFILADO, MATERIALES, MANO DE OBRA, HERRAMIENTA MENOR Y EQUIPO NECESARIO QUE SE REQUIERA PARA LOGRAR LA COMPACTACION DE 100 %, PVSM, ACARREOS DENTRO Y FUERA DE LA OBRA, PREPARACION DE MATERIAL, HUMEDECIDO, NIVELADO, TRASLADO DE UN PUNTO A OTRO DENTRO DE LA OBRA EN CUALQUIER VOLUMEN, MOVIMIENTO DE MAQUINARIA P.U.O.T	$ 428,159.35
3008.85	M2	SUMINISTRO Y COLOCACION DE CONCRETO ASFALTICO EN CALIENTE DE GRANULOMETRIA DENSA ELABORADA CON ASFALTO MODIFICADO TIPO I, AGREGADO 3/4" A FINOS, DE 5 CM DE ESPESOR, FORMADA Y COMPACTADO AL 95%, INCLUYE MATERIALES, QUE CUMPLAN LA NORMATIVA SCT-N-CMT-04-04, SCT-CMT-4-05-002, SCT-CMT-4-05-003, SCT-CMT-4-05-004, SCT-CTR-CAR-1-04-006-14 APLICADAS AL DIA DE HOY, DISEÑO MARSHALL (DEVERÁ SER AUTORIZADO POR EL LABORATORIO DE CALIDAD DE SOPMA AL MENOS 3 DIAS ANTES DE INICIO DE TENDIDO DE LA MEZCLA ASFALTICA), INCUYE: TRAMO DE PRUEBA AL INICIO PARA REVISION Y AUTORIZACION DEL ESPESOR POR PARTE DEL SUPERVISOR, EL CONTRATISTA DEBERÁ PREVEER EL SUMINISTRO Y TIEMPOS MUERTOS POR MOVIMIENTOS DEL TREN DE MAQUINAS DE TRABAJO EN TRAMOS AISLADOS. TRABAJO TERMINADO P.U.O.T. Y LIMPIEZAS DE GRANZON Y HUESO LATERAL.	$ 1,528,743.64


36731.42	M3-KM	ACARREO DE MATERIAL PRODUCTO DE EXCAVACION Y/O DEMOLICION EN CAMION DE VOLTEO A KILOMETROS SUBSECUENTES, AL TIRADERO OFICIAL AUTORIZADO MAS CERCANO AUTORIZADO POR LA SUPERVISION, VOLUMEN MEDIDO COMPACTO.	$	1,255,469.94
753.40	ML	SUMINISTRO Y COLOCACION DE CANASTILLAS O PASAJUNTAS TIPO PESADO DE SECCION NOMINAL DE BARRA PRINCIPAL DE 46 CMS, CON REDONDO LISO DE 1 1/4" SOLDADO EN EXTREMOS ALTERNOS @ 30 CMS.SEPARADORES, ATIESADORES, BASES Y SOPORTES DE ACERO F´y=4,200 DE DIAMETRO 5/16", DE ACUERDO A DISEÑO ANEXO EN PLANOS, INCLUYE: MATERIAL, MANO DE OBRA, CORTES, PULIDO EN CORTES, ANCLAJES, FUNDAS DE PLASTICO EN LOS EXTREMOS NO SOLDADOS, AJUSTES, DESPERDICIOS, ACARREOS, FLETES DENTRO Y FUERA DE LA OBRA.	$	556,264.44
87.12	ML	CONSTRUCCION DE DENTELLON RECTO Y/O CURVO 20-20X40 CM DE SECCION, CON CONCRETO PREMEZCLADO MR=42 KGF/CM2, TMA 1 1/2", R.R 3 DIAS. REVENIMIENTO NORMAL DE 10+-2 CM, GRAVA TRITURADA, ACABADO CON DOBLADOR Y PULIDO. INCLUYE: TRAZO, NIVELACION, CIMBRADO, COLADO, VIBRADO, DESCIMBRADO, , Y CURADO CON MEMBRANA QUIMICA APLICADA CON ASPERSOR Y LIMPIEZA, REMATE CON PAVIMENTO EXISTENTE DEL MISMO MATERIAL Y TIPO, TRABAJO TERMINADO P.U.O.T.	$	37,171.23
228.80	ML	CONSTRUCCION DE GUARNICION RECTA Y/O CURVA TRAPEZOIDAL 15-20X40 CM DE SECCION CON CONCRETO PREMEZCLADO MR=38 KGF/CM2, R.N.REVENIMIENTO DE 8 A 10 CM, T.M.A. 3/4", GRAVA TRITURADA, ACABADO PULIDO EN PARTE DE SUPERIOR Y DOBLADOR EN ARISTAS, INCLUYE: COMPACTADO DE PLANTILLA, CIMBRADO, COLADO, VIBRADO, ACABADO, DESCIMBRADO, ALINEADO, NIVELADO, Y CURADO EN SU PARTE SUPERIOR CON MEMBRANA BASE AGUA A RAZON DE 1 LTO/M2, JUNTA DE AISLAMIENTO LONGITUDINAL AL COMBINAR CON OTRO ELEMENTO Y TRANSVERSAL @ 30 MT MAXIMO, SELLADO CON SELLADOR AUTONIVELANTE LONGITUDINAL, TRABAJO TERMINADO, .P.U.O.T.	$	107,484.52
118.93	M2	CONSTRUCCION DE BANQUETA DE 10 CM DE ESPESOR A BASE DE CONCRETO PREMEZCLADO F'C=150 KG/CM2, T.M.A. 3/4", R.N. GRAVA TRITURADA, REVENIMIENTI DE 10+-2 CM, ACABADO RAYADO FINO CON BROCHA DE PELO, JUNTAS FRIAS CON DOBLADOR DE 2" SECCION DE LOSAS COMO INDIQUE PROYECTO, INCLUYE: JUNTA A BASE DE ESPUMA DE POLIETILENO DE CELDAS CERRADAS DE 1/2" EN JUNTAS FRIAS LONGITUDINALES CON MUROS Y TRANSVERSALES DEL ELEMENTO, ASI COMO SU UNION CON ELEMENTOS VIEJOS O CAMBIO DE ELEMENTO, CIMBRADO, COLADO, DESCIMBRADO, CORTES CON CORTADORA DE DISCO, SELLADO DE CORTES CON SELLADOR AUTONIVELANTE Y TIRA DE RELLENO PREFORMADA NO ADHERENTE DE 1/8" (EN TODAS LAS JUNTAS DE CONTRACCCION Y CONSTRUCCION TRANSVERSALES), CURADO CON MEMBRANA QUIMICA APLICADA CON ASPERSOR, TRABAJO TERMINADO	$	62,403.44
2.00	PZA	RENIVELACIÓN DE RASANTE (PARTE SUPERIOR) DE CAJA DE VÁLVULAS TIPO 3 DE HASTA 1.96 X 1. 75 MTS, NIVELADO HASTA UNA ALTURA MAXIMA DE 10 CM, Y MINIMA DE 5 CM. MEDIDAS INTERIORES INCLUYE: TRAZO, EXCAVACIÓN, NIVELACIÓN, PREPARACIONES , Y DEMOLICIONES, RETIRO SIN RECUPERACIÓN DE TAPA DE FOFO EXISTENTE, MURO DE TABIQUE ROJO RECOCIDO COMÚN 7X14X28 CM DE 14 CM DE ESPESOR, JUNTEADO CON MORTERO CEMENTO-ARENA 1:3 APLANADO INTERIOR CON MORTERO CEMENTO ARENA 1:3 DE 2.00 CM DE ESPESOR ACABADO PULIDO, LOSA DE CONCRETO F´C= 250 KG/CM2 T.M.A. 19 MM DE 15 CM DE ESPESOR ARMADA CON VRS No. 3 @15 cm EN AMBOS SENTIDOS, CONTRAMARCO SENCILLO DE CANAL FoFo DE 100 mm, CONTRAMARCO CON TAPA DE FOFO, TIPO PESADO DE 50X50 CM, DEMOLICIÓN Y RECONSTRUCCIÓN DE APROCHES, CARGA Y ACARREOS DENTRO DE LA OBRA, CIMBRADO, DESCIMBRADO, COLADO, VIBRADO, LIMPIEZA PREVIA, FINAL, Y TODO LO NECESARIO PARA LA CORRECTA EJECUCIÓN DEL CONCEPTO. PZA 2.00	$	43,121.10
5584.08	M2	LIMPIEZA GENERAL DE LA OBRA, INCLUYE: BARRIDO, CARGA, ACARREOS Y RETIRO DE ESCOMBROS FUERA DE LA OBRA, TRABAJO TERMINADO.	$	48,581.52

1157.00	ML	SUMINISTRO Y APLICACIÓN DE PINTURA BASE SOLVENTE PARA MARCAS EN GUARNICIONES CLASIFICACION M-12.1, M12.2 APLICADA SOBRE GUARNICIONES Y DENTELLONES DE CUALQUIER COLOR, SEGÚN SE REQUIERA Y SEGÚN NORMA S.C.T. SECADO AL TACTO EN 5 MIN Y AL DURO EN 30 MIN CON MICRO ESFERA , DESARROLLO DE 35 CM. INCLUYE: MATERIALES Y ESPECIFICACIONES QUE CUMPLAN CON LA NORMATIVA N-CMT-5-01-001/05, N-PRY-CAR-10-01-002/13 APLICADAS AL DIA DE HOY, TRAZO, MANO DE OBRA, LIMPIEZA PREVIA DE SUPERFICIE, EQUIPO NECESARIO PARA SU EJECUCIÓN, Y TODO LO NECESARIO PARA SU CORRECTA EJECUCIÓN, TRABAJO TERMINADO.	$	214,714.77
2.00	PZA	SUMINISTRO Y COLOCACION DE SEÑALAMIENTO VERTICAL DE RESTRICCION SR-9 (VELOCIDAD MAXIMA), DISEÑO NORMATIVO SCT, HECHO A ABASE DE LAMINA GALVANIZADA CON CEJA DE 72 X 72 CMCALIBRE 16, CON TERMINADO GRADO INGENIERIA EN SU TOTALIDAD, ELCOLOR SERA REFLEJANTE GRADO INGENIERIA Y SIMBOLOS EN COLOR REFLEJANTE, TODOS LOS COLORES RESISTENTES A LA INTEMPERIE, FIJADA MEDIANTE BARRENADO Y TORNILLOS DE 2 1/2" X 5/16" A UN POSTE DE PTR DE 2 X 2" CALIBRE 14 EN ACABADO GALVANIZADO Y CON UNA ALTURA DE 2.5 MTS AL NIVEL DE BANQUETA A LA PARTE INFERIOR DE LA LAMINA MAS EL EXCEDENTE REQUERIDO PARA FIJAR LAS LAMINASY ANCLADO DE 50 CM DE PROFUNDIDAD CON ANGULO TRANSVERSAL DE 1 X 1" DE 25 CM, EN DADO DE CONCRETO F´c=150 KG/CM2 DE 30 CM DE LADO (VER PLANO DE DETALLES CRITERIOS DE ANCLAJE DE SEÑALAMIENTO VERTICAL, DETALLE SEÑ-02 Y SEÑ 03), MCA ASEA O SIMILAR EN CALIDAD Y ESPECIFICACIONES, INCLUYE: MANO DE OBRA, FLETES, MANIOBRAS LIMPIEZAS Y RETIRO DEL SOBRANTE FUERA DE LA OBRA HASTA TIRADERO OFICIAL, TRABAJO TERMINADO.	$	8,763.42
48.00	HR	BOMBEO DE ACHIQUE CON BOMBA DE 3" Y 8 H.P., OPERACION BOMBA Y EQUIPO COMPLEMENTARIO CON MANGUERA Y PICHANCHA.	$	8,482.08
2441.92	M2	CONSTRUCCION DE PAVIMENTO HIDRAULICO A BASE DE CONCRETO PREMEZCLADO MR=42 KG/CM2 TMA 1 1/2" GRAVA TRITURADA, REVENIMIENTO DE 6 A 8 CM RESISTENCIA RAPIDA 7 DIAS DE 20 CM DE ESPESOR MODULADO EN LOSAS DE 3.5 MTS. (ANCHO) X 3.5 MTS (LARGO)COMO MAXIMO, CON CORTES EN LAS LOSAS DE 1/3 DEL ESPESOR DE LA LOSA (7 CM) Y SELLADO CON MATERIAL ELASTOMERICO Y TIRA PREFORMADA EN JUNTAS Y CORTES LONGITUDINALES Y TRANSVERSALES COLA DE RATA DE 1/8", ASI COMO EL APROCHE CON GUARNICION Y DENTELLON. INCLUYE: CIMBRADO, COLADO, VIBRADOCON INMERSION Y REGLA VIBRATORIA, DESCIMBRADO, REGLEADO FINAL, ACABADO CEPILLO DE ALUMINIO Y CON DOBLADOR, CALAFATEO, CURADO CON MEMBRANA BASE AGUA Y TODO LO NECESARIO PARA SU CORRECTA COLOCACION, P.U.O.T.	$	1,790,367.56

TOTAL PRESUP.	$	6,483,014.80
IVA	$	1,037,282.36
TOTAL	$	7,520,297.16

NOMBRE DEL SUPERVISOR: ARQ. ARIADNA MEDINA DOMINGUEZ

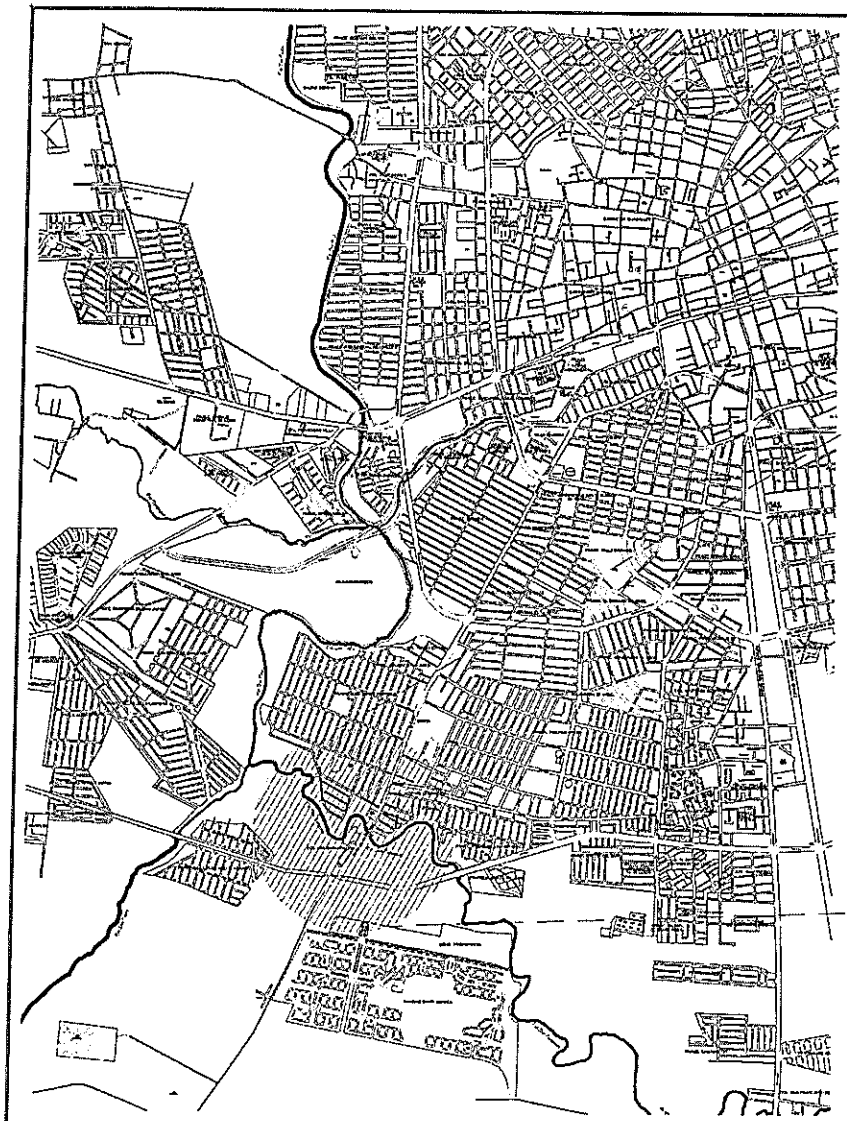

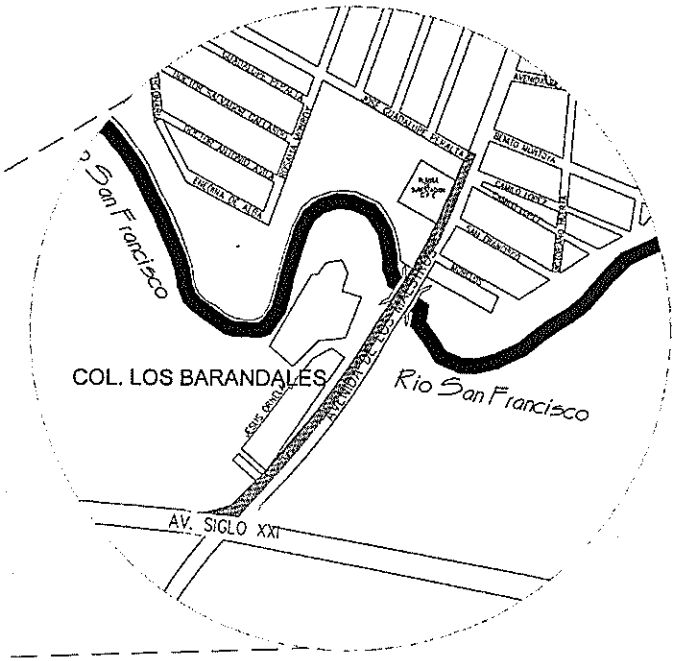


CROQUIS DE LOCALIZACIÓN

SIN ESCALA

AV. LOS MAESTROS

LOCALIZACION

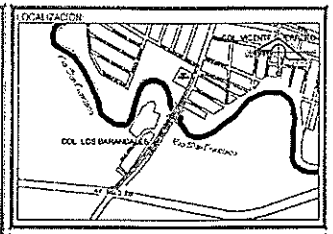

SIMBOLOGIA

La Dirección de Planeación y Proyectos solo autoriza el proyecto ejecutivo, no es responsable de la correcta ejecución de la obra. Este documento no tiene validez si no presenta las firmas de los responsables para su autorización, así como los sellos respectivos.

PRESIDENTE MUNICIPAL
M.P.P. Leonardo Montañez Castro
ENCARGADA DE DESPACHO DE LA SOPMA
Arq. Gloria Guadalupe Castillo González

REV	FECHA	OBSERVACIONES

No. No. DE LA DEPENDENCIA

REGP DE PROY EXTERNO		LOGO EXTERNO
CED. PROFESIONAL		
PROYECTO	REVISO	AUTORIZO


Dirección de Planeación y Proyectos de Obra
Secretaría de Obras Públicas

PROYECTISTA	COORDINADOR
ARQ. ALVARO DAVID MEZA CONTRERAS	ARQ. ALEJANDRO JAIME LEAL
JEFE DE DEP.	DIRECTOR
ARQ. J. JESÚS PALAFOX GONZÁLEZ	M. en ARQ. JOSE LUIS JIMÉNEZ GARCÍA

PROYECTO
SOBRECARPETA ASFALTICA Y CONCRETO HIDRAULICO "AV DE LOS MAESTROS" CALZADA PONIENTE
UBICACION
CALZADA PONIENTE DE ENTRE AV. SIGLO XXI A CALLE GUADALUPE PERALTA
CONTENIDO
CROQUIS DE LOCALIZACION

CLAVE	No. PLANO
LOC 01	01
FECHA: JULIO 2022	ESCALA: INDICADA
ACOTACION: METROS	No. EXP.: E-000-22

Aguascalientes
LA CIUDAD DE TU VIDA

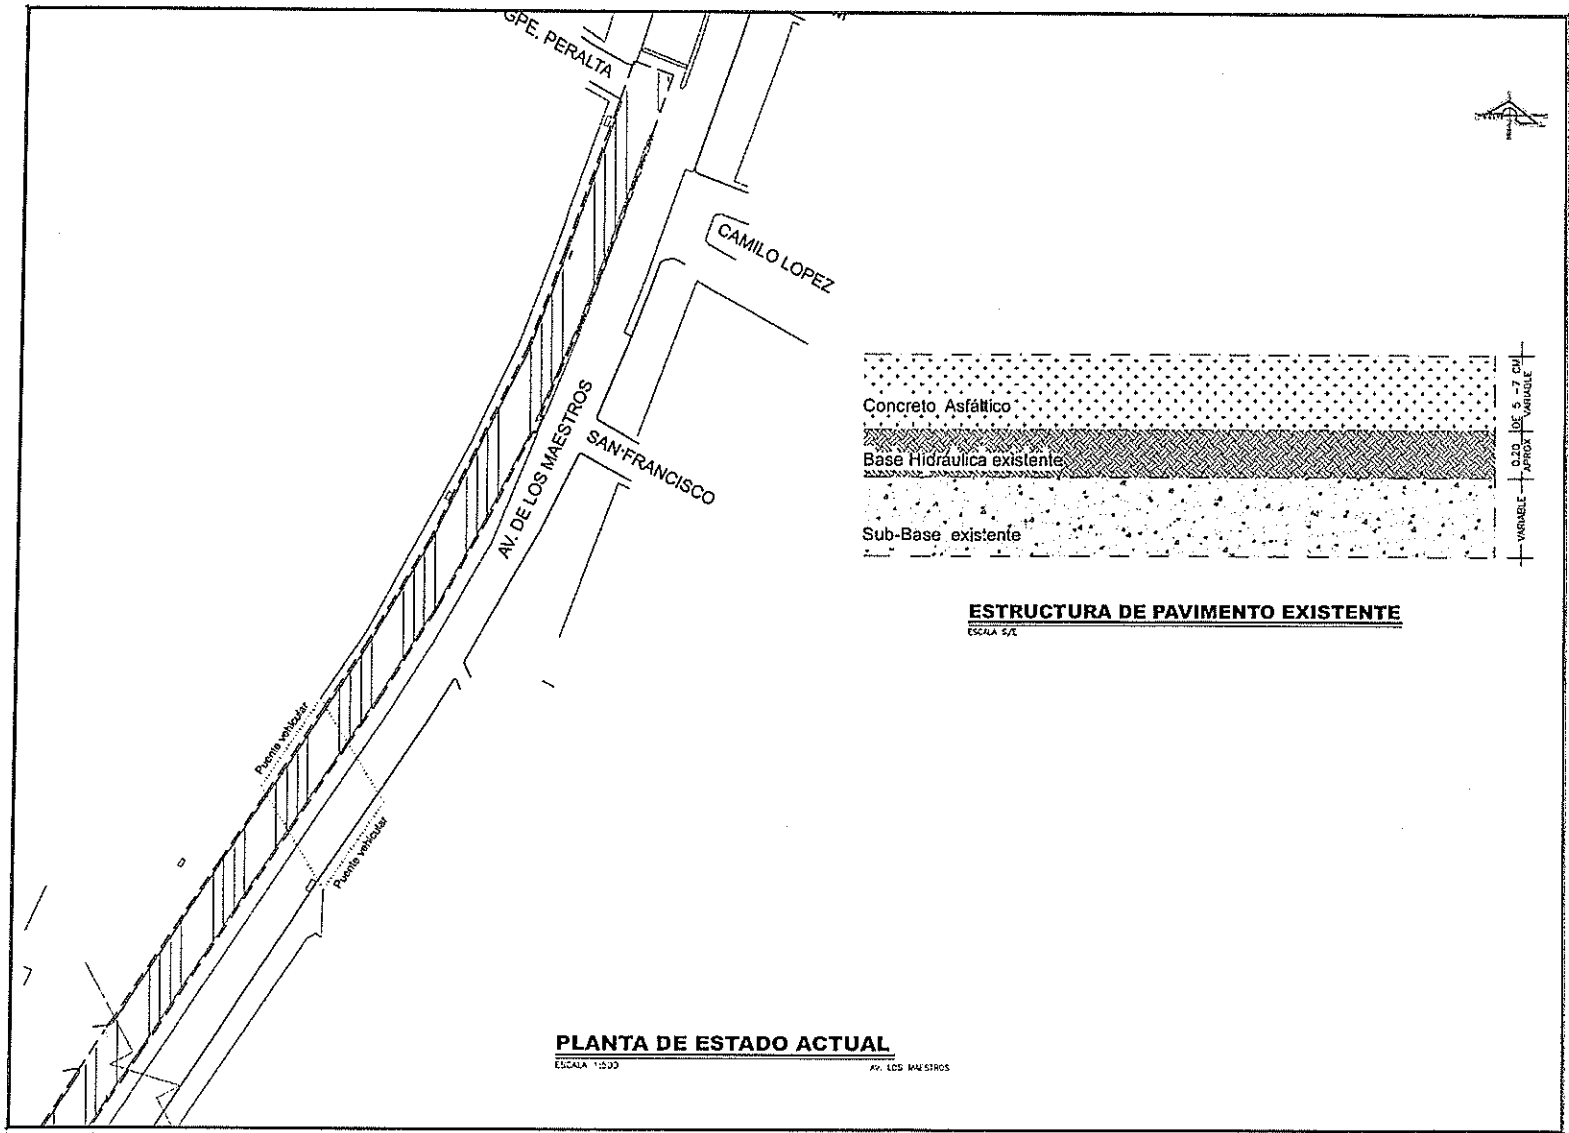

PLANTA DE ESTADO ACTUAL


ESCALA 1:500

AV. LOS MAESTROS

ESTRUCTURA DE PAVIMENTO EXISTENTE

ESCALA S/E

LOCALIZACIÓN

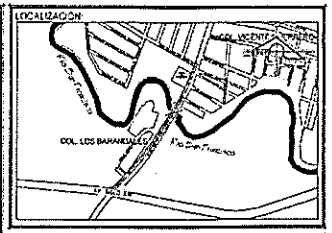

SIMBOLOGÍA

- LIMITE DE PROYECTO
- BANQUETAS EXISTENTES
- PARAMENTO EXISTENTE
- CARPETA ASFALTICA EXISTENTE
- PUENTE VEHICULAR EXISTENTE CON CARPETA ASFALTICA
- REGISTRO CFE (REG-CFE)
- ALUMBRADO
- POSTES CFE
- POSTES TELMEX
- POZO DE VISITA EXISTENTE

La Dirección de Planeación y Proyectos solo autoriza el proyecto ejecutivo, no es responsable de la correcta ejecución de la obra. Este documento no tiene validez si no presenta las firmas de los responsables para su autorización, así como los sellos respectivos.

PRESIDENTE MUNICIPAL
M.P.P. Leonardo Montañez Castro
ENCARGADA DE DESPACHO DE LA SOPMA
Arq. Gloria Guadalupe Castillo González

REV	FECHA	OBSERVACIONES

No. Mts. de la DEPENDENCIA

RESP. DE PROY. EXTERNO	LOGO EXTERNO
CED. PROFESIONAL	
PROYECTO / REVISO / AUTORIZO	

Dirección de Planeación y Proyectos de Obra — Secretaría de Obras Públicas

PROYECTISTA	COORDINADOR
ARQ. ARNOLD DAVID MEZA CONTRERAS	ARQ. ALEJANDRO JAIME LEAL
JEFE DE DEP.	DIRECTOR
ARQ. J. JESÚS PALAFOX GONZÁLEZ	M. en ARQ. JOSÉ LUIS JIMÉNEZ GARCÍA

PROYECTO
SOBRECARPETA ASFALTICA Y CONCRETO HIDRAULICO "AV. DE LOS MAESTROS" CALZADA PONIENTE

UBICACIÓN
CALZADA PONIENTE DE ENTRE AV. SIGLO XXI A CALLE GUADALUPE PERALTA


CONTENIDO
ESTADO ACTUAL Y LEVANTAMIENTO TOPOGRAFICO

CLAVE	NO. PLANO
EA 01	02
FECHA: JULIO 2022	ESCALA: INDICADA
ACOTACIÓN: METROS	NO. EXP.: E-000-22

Aguascalientes
LA CIUDAD DE TU VIDA

ESTRUCTURA DE PAVIMENTO EXISTENTE

ESCALA S/E

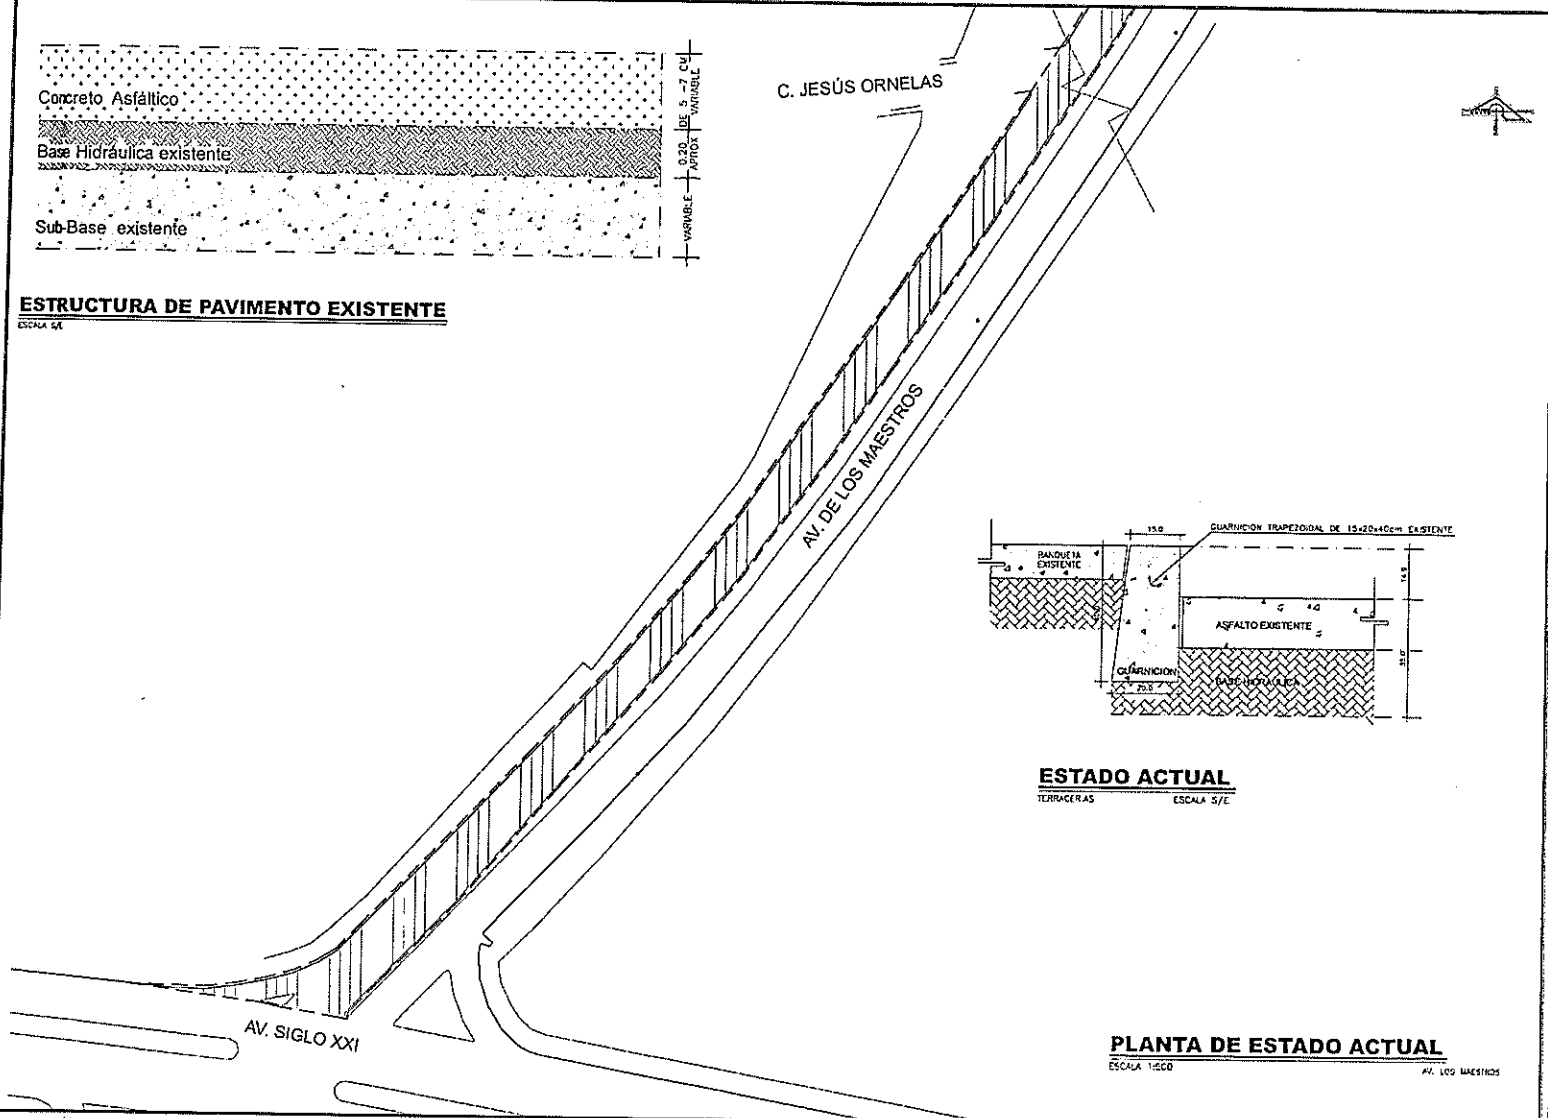

ESTADO ACTUAL


TERRACERIAS ESCALA S/E

PLANTA DE ESTADO ACTUAL

ESCALA 1:500

AV. LOS MAESTROS

LOCALIZACIÓN

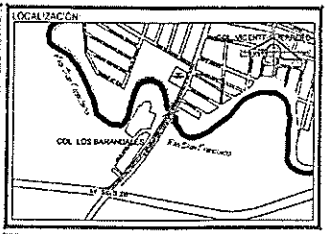

SIMBOLOGÍA

- LIMITE DE PROYECTO
- BANQUETAS EXISTENTES
- PARAMENTO EXISTENTE
- CARPETA ASFALTICA EXISTENTE
- PUENTE VEHICULAR EXISTENTE CON CARPETA ASFALTICA
- REGISTRO CFE — REG-CFE
- ALUMBRADO
- POSTES CFE
- POSTES TELMEX
- POZO DE VISITA EXISTENTE

La Dirección de Planeación y Proyectos solo autoriza el proyecto ejecutivo, no es responsable de la correcta ejecución de la obra. Este documento no tiene validez si no presenta las firmas de los responsables para su autorización según los sellos respectivos.

PRESIDENTE MUNICIPAL
M.P.P. Leonardo Montañez Castro
ENCARGADA DE DESPACHO DE LA SOPMA
Arq. Gloria Guadalupe Castillo González

REV.	FECHA	OBSERVACIONES

No. DE LA DEPENDENCIA

RESP. DE PROY. EXTERNO		LOGO EXTERNO
CED. PROFESIONAL		
PROYECTO	REVISO	AUTORIZO

Dirección de Planeación y Proyectos de Obra — Secretaría de Obras Públicas

PROYECTISTA	COORDINADOR
ARQ. ALVARO DAVID MEZA CONTRERAS	ARQ. ALEJANDRO JAIME LEAL
JEFE DE DEP.	DIRECTOR
ARQ. J. JESÚS PALAFOX GONZÁLEZ	M. en ARQ. JOSÉ LUIS ANDRADE GARCÍA


PROYECTO
SOBRECARPETA ASFALTICA Y CONCRETO HIDRAULICO, "AV. DE LOS MAESTROS" CALZADA PONIENTE

UBICACIÓN
CALZADA PONIENTE DE ENTRE AV. SIGLO XXI A CALLE GUADALUPE PERALTA

CONTENIDO
ESTADO ACTUAL Y LEVANTAMIENTO TOPOGRAFICO

CLAVE	No. PLANO
EA 02	03
FECHA: JULIO 2022	ESCALA: INDICADA
ACOTACION: METROS	No. EXP: E-000-22


Aguascalientes
LA CIUDAD DE TU VIDA

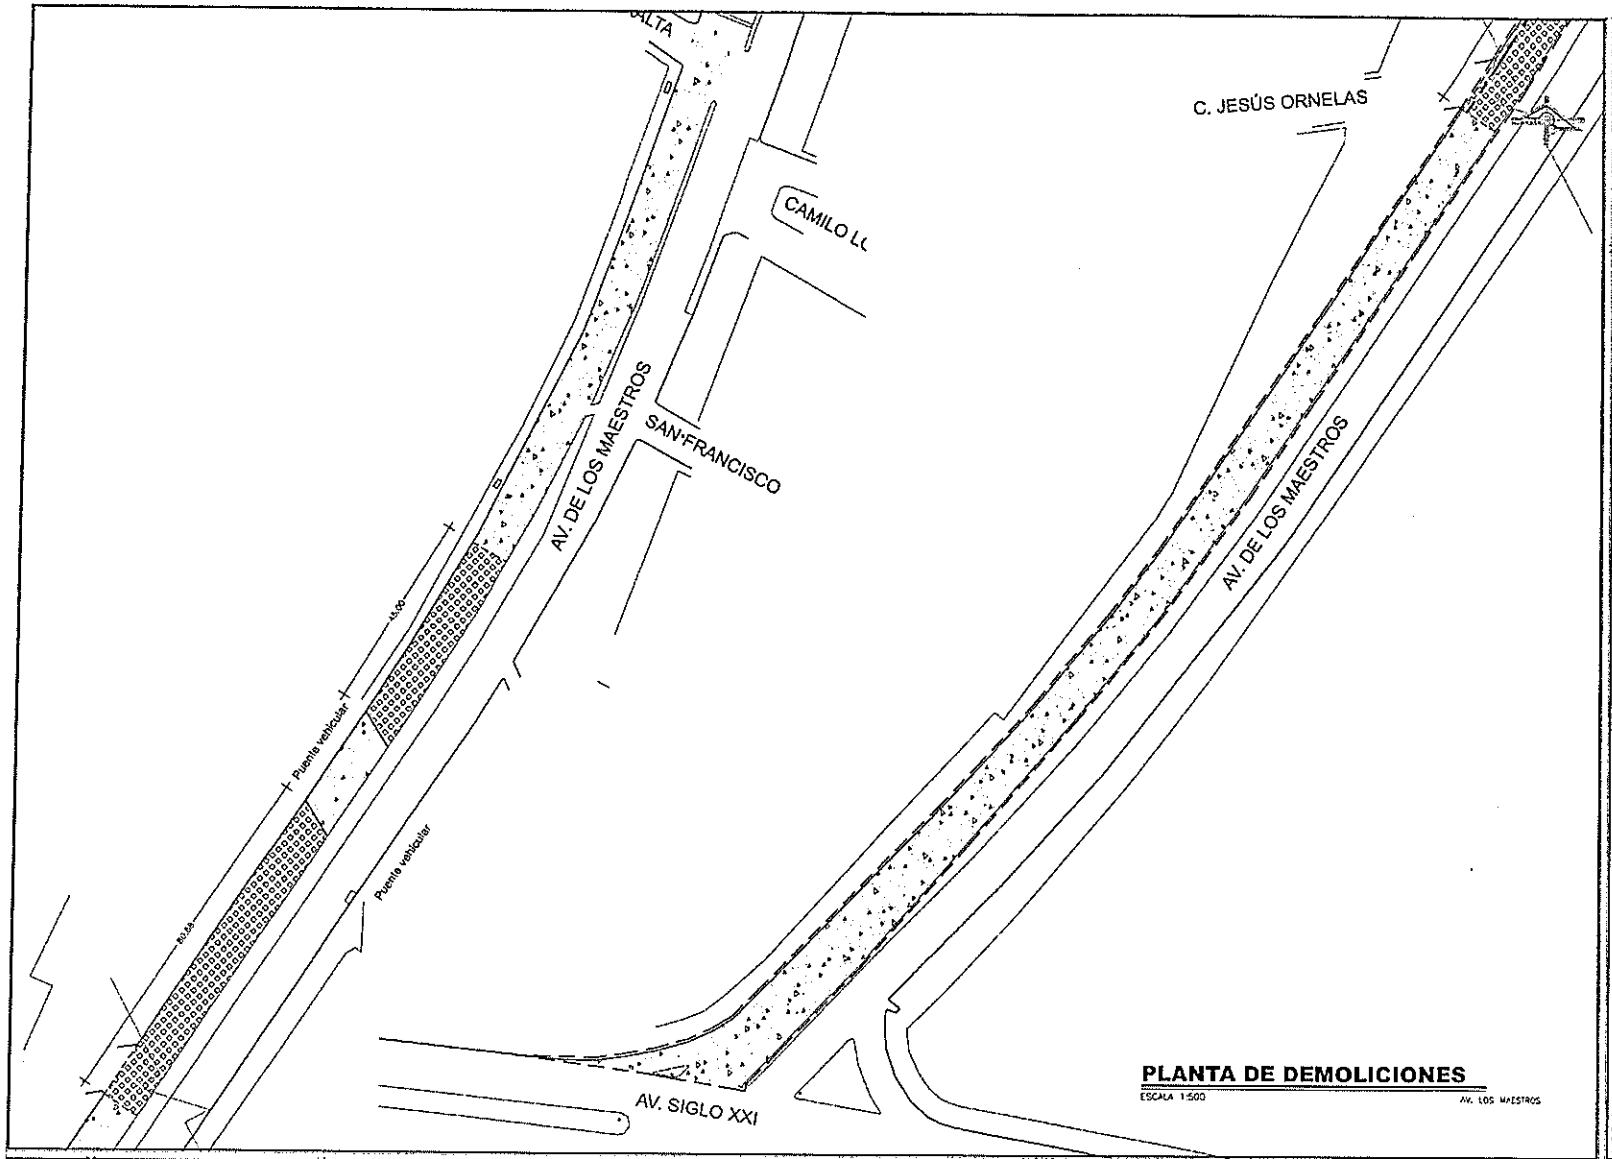

PLANTA DE DEMOLICIONES

ESCALA 1:500

LOCALIZACION

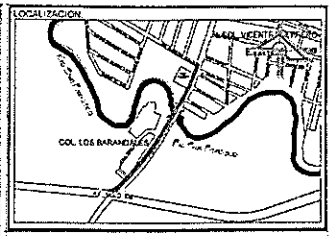

SIMBOLOGÍA

- LIMITE DE PROYECTO
- BANQUETAS
- PARAMENTO
- CORTE CON DISCO
- FRESADO UNIFORME DE LA SUPERFICIE DE RODADURA EN PAVIMENTO DE CONCRETO ASFALTICO 3-7 CM (5 CM DE ESPESOR PROMEDIO) MEDIANTE FRESADORA EN FRIO COMPACTA, EQUIPADA CON BANDA TRANSPORTADORA PARA CARGA DIRECTA SOBRE CAMION DE VOLTEO
- DEMOLICION DE PAVIMENTO HIDRAULICO Y/O ASFALTICO DE HASTA 15 CM. DE ESPESOR PROMEDIO EN PAVIMENTO (BANQUETAS, LOSA DIAMANTE Y CAJAS DE VALVULAS, TEPES) CON O SIN ARMADO DE ACERO, SIN RECUPERACIÓN. NUROS, MOJONERAS, ANCLAJES, ETC. DE FORMA MANUAL O MECANICA.

NOTA:
LAS DEMOLICIONES DE GUARNICIONES Y/O DENTELLONES SE DETERMINAN EN SITIO, UBICANDO O DANDO PRIORIDAD A LAS ÁREAS MAS DAÑADA, DANDO LA AUTORIZACIÓN AL EJECUTOR POR PARTE DEL SUPERVISOR DE OBRA DE SOPMA.

La Dirección de Planeación y Proyectos solo autoriza el proyecto ejecutivo, no es responsable de la correcta ejecución de la obra. Este documento no tiene validez si no presenta las firmas de los responsables para su autorización, así como los sellos respectivos.

PRESIDENTE MUNICIPAL
M.P.P. Leonardo Montañez Castro
ENCARGADA DE DESPACHO DE LA SOPMA
Arq. Gloria Guadalupe Castillo González

REV	FECHA	OBSERVACIONES

V0. Bo. DE LA DEPENDENCIA

RESP. DE PROY EXTERNO		LOGO EXTERNO
CED. PROFESIONAL		
PROYECTO	REVISO	AUTORIZÓ

Dirección de Planeación y Proyectos de Obra — Secretaría de Obras Públicas

PROYECTISTA	COORDINADOR
ARQ. ALVARO DAVID MEZA CONTRERAS	ARQ. ALEJANDRO JULIAN LEAL
JEFE DE DEP.	DIRECTOR
ARQ. JESÚS PALAFOX GONZÁLEZ	M. en ARQ. JOSE LUIS JIMÉNEZ GARCÍA

PROYECTO	SOBRECARPETA ASFALTICA Y CONCRETO HIDRAULICO "AV. DE LOS MAESTROS" CALZADA PONIENTE
UBICACION	CALZADA PONIENTE DE ENTRE AV. SIGLO XXI A CALLE GUADALUPE PERALTA
CONTENIDO	PLANTA DE DEMOLICIONES

CLAVE	No PLANO
DEM 01	04
FECHA JULIO 2022	ESCALA INDICADA
ACOTACION METROS	No EXP E-000-22

Aguascalientes
LA CIUDAD DE TU VIDA

SIMBOLOGIA


a) BACHEO PROFUNDO AISLADO UTILIZANDO MATERIAL CALIDAD BASE HIDRAULICA PARA MAS DE UN MILLON DE EJES EQUIVALENTES DEL BANCO QUE ELIJA EL CONTRATISTA, INCISO N·CSV.CAR.1.02.004/03 DE LAS NORMAS DE CONSTRUCCION DE CARR. DE LA SCT.

b) RENIVELACIONES CON CONCRETO ASFALTICO MEZCLA EN PLANTA EN CALIENTE ASFALTO MODIFICADO CON POLIMERO TIPO I, CUMPLIENDO CON LAS NORMAS SCT RELEVANTES DE CONSTRUCCION Y CONSERVACION, GRANULOMETRIA DENSA 3/4"A FINOS, MEDIDO COMPACTO AL NOVENTA Y CINCO PORCIENTO (95%)


c) RIEGO DE IMPREGNACION CON EMULSION DE ROMPIMIENTO LENTO (ECL-60 %), INCLUYE BARRIDO DE LA SUPERFICIE, LIMPIEZA A DETALLE, SUMINISTRO, ALMACENAMIENTO, CALENTAMIENTO, Y APLICACION DE LA EMULSION CON EQUIPO ESPECIAL PARA ESA ACTIVIDAD, ESPREAS LIMPIAS Y ALINEADAS, EN CASO DE RECOVENDARLO EL LABORATORIO DE CALIDAD DEL CONTRATISTA SE DEBERÁ DAR UN RIEGO MATAPOLVO ANTES DE COLOCAR LA CAPA DE IMPREGNACION, A RAZON DE 1.5 LT DE EMULSION POR M2, O LO QUE INDIQUE EL LABORATORIO DE CALIDAD DEL CONTRATISTA

d) RIEGO DE LIGA CON EMULSION DE ROMPIMIENTO RAPIDO (ECR-65 %), INCLUYE, SUMINISTRO, ALMACENAMIENTO, CALENTAMIENTO, Y APLICACION DE LA EMULSION CON EQUIPO ESPECIAL PARA ESA ACTIVIDAD, ESPREAS O BACHADOR LIMPIAS Y ALINEADAS, EN LA PETROLIZADORA, A RAZON DE 0.8 LT DE EMULSION POR M2, O LO QUE INDIQUE EL LABORATORIO DE CALIDAD DEL CONTRATISTA, NO SE ACEPTAN "IMPREGNALIGA"


e) CONCRETO ASFALTICO EN CALIENTE DE GRANULOMETRIA DENSA ELABORADA CON ASFALTO MODIFICADO TIPO I, AGREGADO 3/4" A FINOS, DE 5 CM DE ESPESOR TOTAL, FORMADA Y COMPACTADO AL 95%, INCLUYE MATERIALES, QUE CUMPLAN LA NORMATIVA SCT-N-CMT-04-04, SCT-CMT-4-05-002, SCT-CMT-4-05-003, SCT-CMT-4-05-004, SCT-CTR-CAR-1-04-006-14 APLICADAS AL DIA DE HOY, DISEÑO MARSHALL (DEBERA SER AUTORIZADO POR EL LABORATORIO DE CALIDAD DE SOPMA AL MENOS 3 DIAS ANTES DE INICIO DE TENDIDO DE LA MEZCLA ASFALTICA)

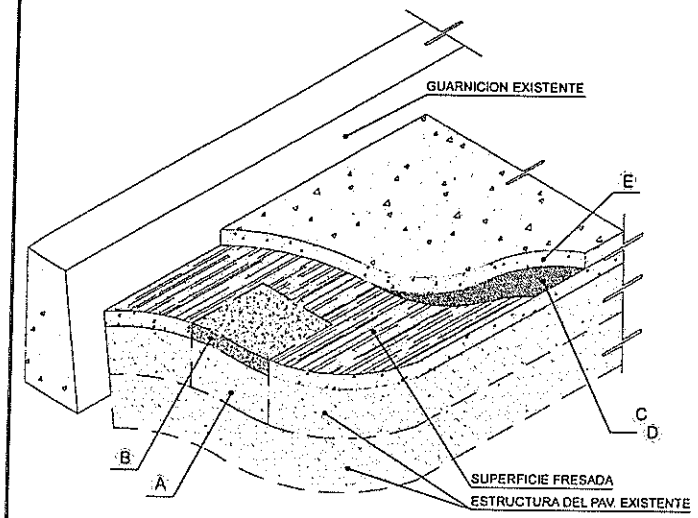

ESTRUCTURA DE PAVIMENTO
ESCALA S/E

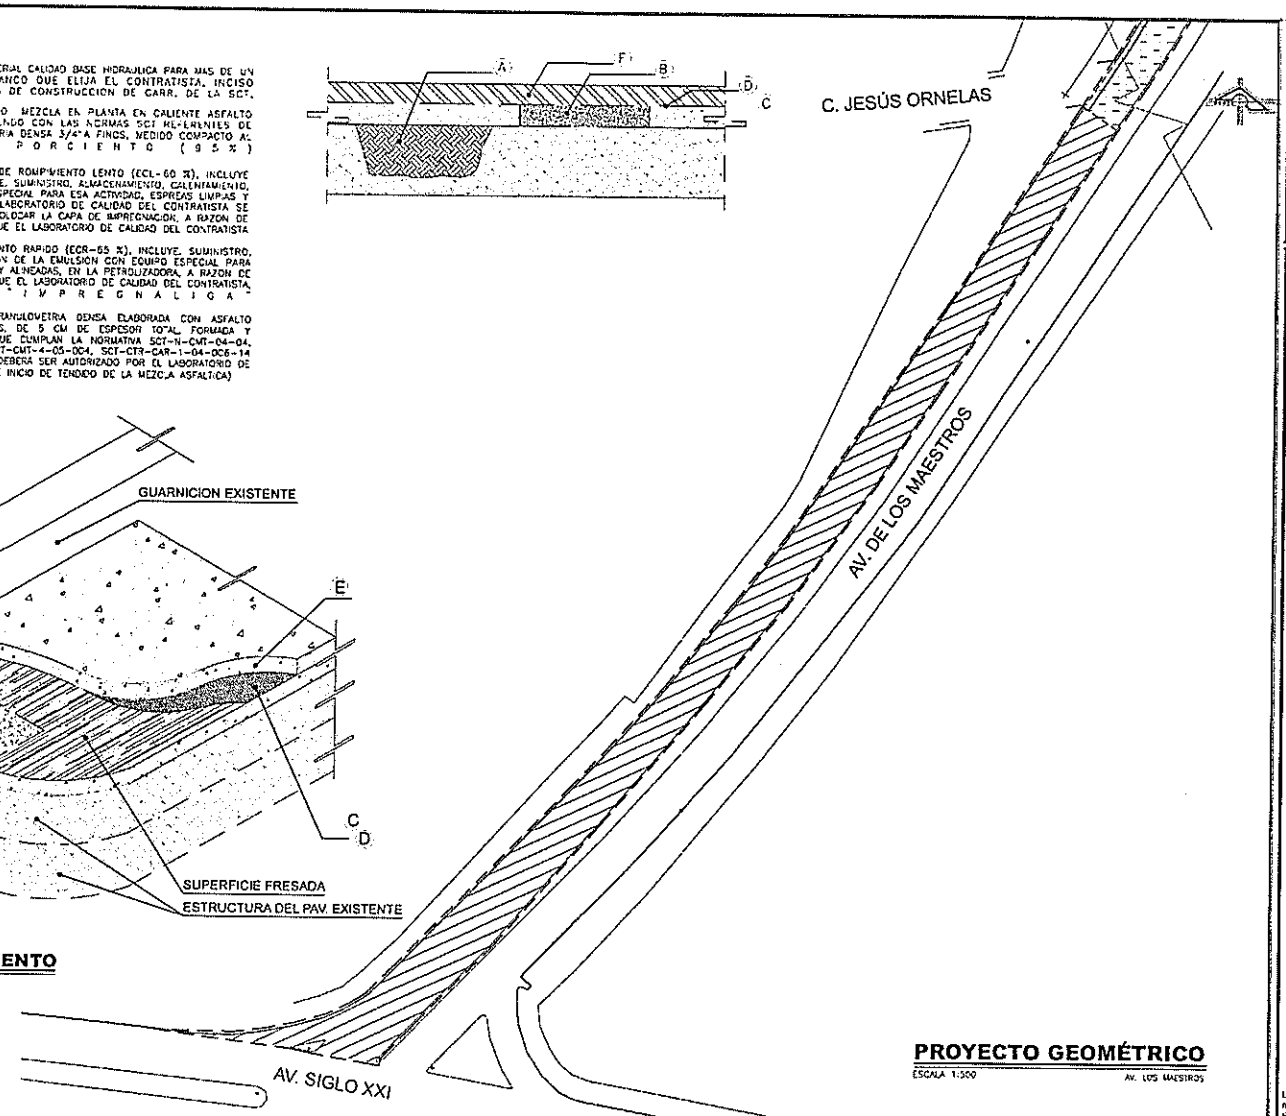

PROYECTO GEOMÉTRICO
ESCALA 1:500
AV. LOS MAESTROS

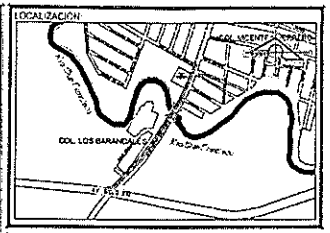

SIMBOLOGÍA

- LIMITE DE PROYECTO
- BANQUETAS
- PAVIMENTO
- CANAN
- CAJA VALVULAS
- BOTA HIDRAULICA
- POZO DE VISITA EXISTENTE
- CONSTRUCCION DE DENTELLON RECTO Y/O CURVO 20-20x40 CM DE SECCION, CON CONCRETO PREMEZCLADO MR=42 KG/CM2 T.M.A. 1 1" GRAVA TRITURADA, R.R. 3 DIAS, REVENIMIENTO NORMAL DE 10±2 CM, GRAVA TRITURADA, ACABADO CON DOBLADOR Y PULIDO.
- CONSTRUCCION DE PAVIMENTO HIDRAULICO A BASE DE CONCRETO PREMEZCLADO MR=42 KG/CM2 T.M.A. 1 1" GRAVA TRITURADA, REVENIMIENTO DE 6 A 8 CM FRAGUADO NORMAL DE 20 CM DE ESPESOR MODULADO EN LOSAS DE 3.5 MTS. (ANCHO) X 3.5 MTS. (LARGO) COMO MINIMO, CON CORTES EN LAS LOSAS DE 1/3 DEL ESPESOR DE LA LOSA (7 CM), Y SELLADO CON MATERIAL ELASTOMERICO Y TIRA PREFORMADA EN JUNTAS Y CORTES LONGITUDINALES Y TRANSVERSALES CON CUÑA DE MAYA DE 2", ASI COMO EL APROCHE CON GUARNICION Y DENTELLON.
- SUMINISTRO Y COLOCACION DE CONCRETO ALFALTICO EN CALIENTE DE GRANULOMETRIA DENSA ELABORADA CON CM DE ESPESOR, FORMADA Y COMPACTADO AL 95% INCLUYE MATERIALES QUE CUMPLAN LA NORMATIVA SCT-N-CMT-04-04, SCT-CMT-4-05-002, SCT-CMT-4-05-003, SCT-CMT-4-05-004, SCT-CTR-CAR-1-04-006-14, APLICADAS AL DIA DE HOY, DISEÑO MARSHALL (DEBERA SER AUTORIZADO POR EL LABORATORIO DE CALIDAD DE SOPMA AL MENOS 3 DIAS ANTES DE INICIO DE TENDIDO DE LA MEZCLA ASFALTICA).
- SUMINISTRO Y COLOCACION DE JUNTA WABO EFL 400 ELASTOFLEX BRIDGE DUNTZA SHORE TIPO A, JUNTA DE EXPANSION PARA PUENTES CONEXIONES DE LOSA A LOSA.

La Dirección de Planeación y Proyectos solo autoriza el proyecto ejecutivo, no es responsable de la correcta ejecución de la obra. Este documento no tiene validez si no presenta las firmas de los responsables para su autorización, así como los sellos respectivos.

PRESIDENTE MUNICIPAL
M.P.P. Leonardo Montañez Castro
ENCARGADA DE DESPACHO DE LA SOPMA
Arq. Gloria Guadalupe Castillo González

REV.	FECHA	OBSERVACIONES

NO HAY USO DE LA DEPENDENCIA

RESP. DE PROY. EXTERNO		LOGO EXTERNO
CED. PROFESIONAL		
PROYECTO	REVISO	AUTORIZO


Dirección de Planeación y Proyectos de Obra — Secretaría de Obras Públicas

PROYECTISTA	COORDINADOR
ARQ. ALVARO DAVID MEZA CONTRERAS	ARQ. ALEJANDRO JAIME LEAL
JEFE DE DEP.	DIRECTOR
ARQ. J. JESÚS PALAFOX GONZÁLEZ	M. en ARQ. JOSÉ LUIS JIMÉNEZ GARCÍA

PROYECTO: SOBRECARPETA ASFALTICA Y CONCRETO HIDRAULICO "AV. DE LOS MAESTROS" CALZADA PONIENTE
UBICACION: CALZADA PONIENTE DE ENTRE AV. SIGLO XXI A CALLE GUADALUPE PERALTA
CONTENIDO: PROYECTO GEOMETRICO DETALLES DE ESTRUCTURA DE CARPETA ASFALTICA

CLAVE	NO. PLANO
GEO 01	05
FECHA: JULIO 2022	ESCALA: INDICADA
ACOTACION: METROS	No. EXP.: E-000-22

Aguascalientes
LA CIUDAD DE TU VIDA

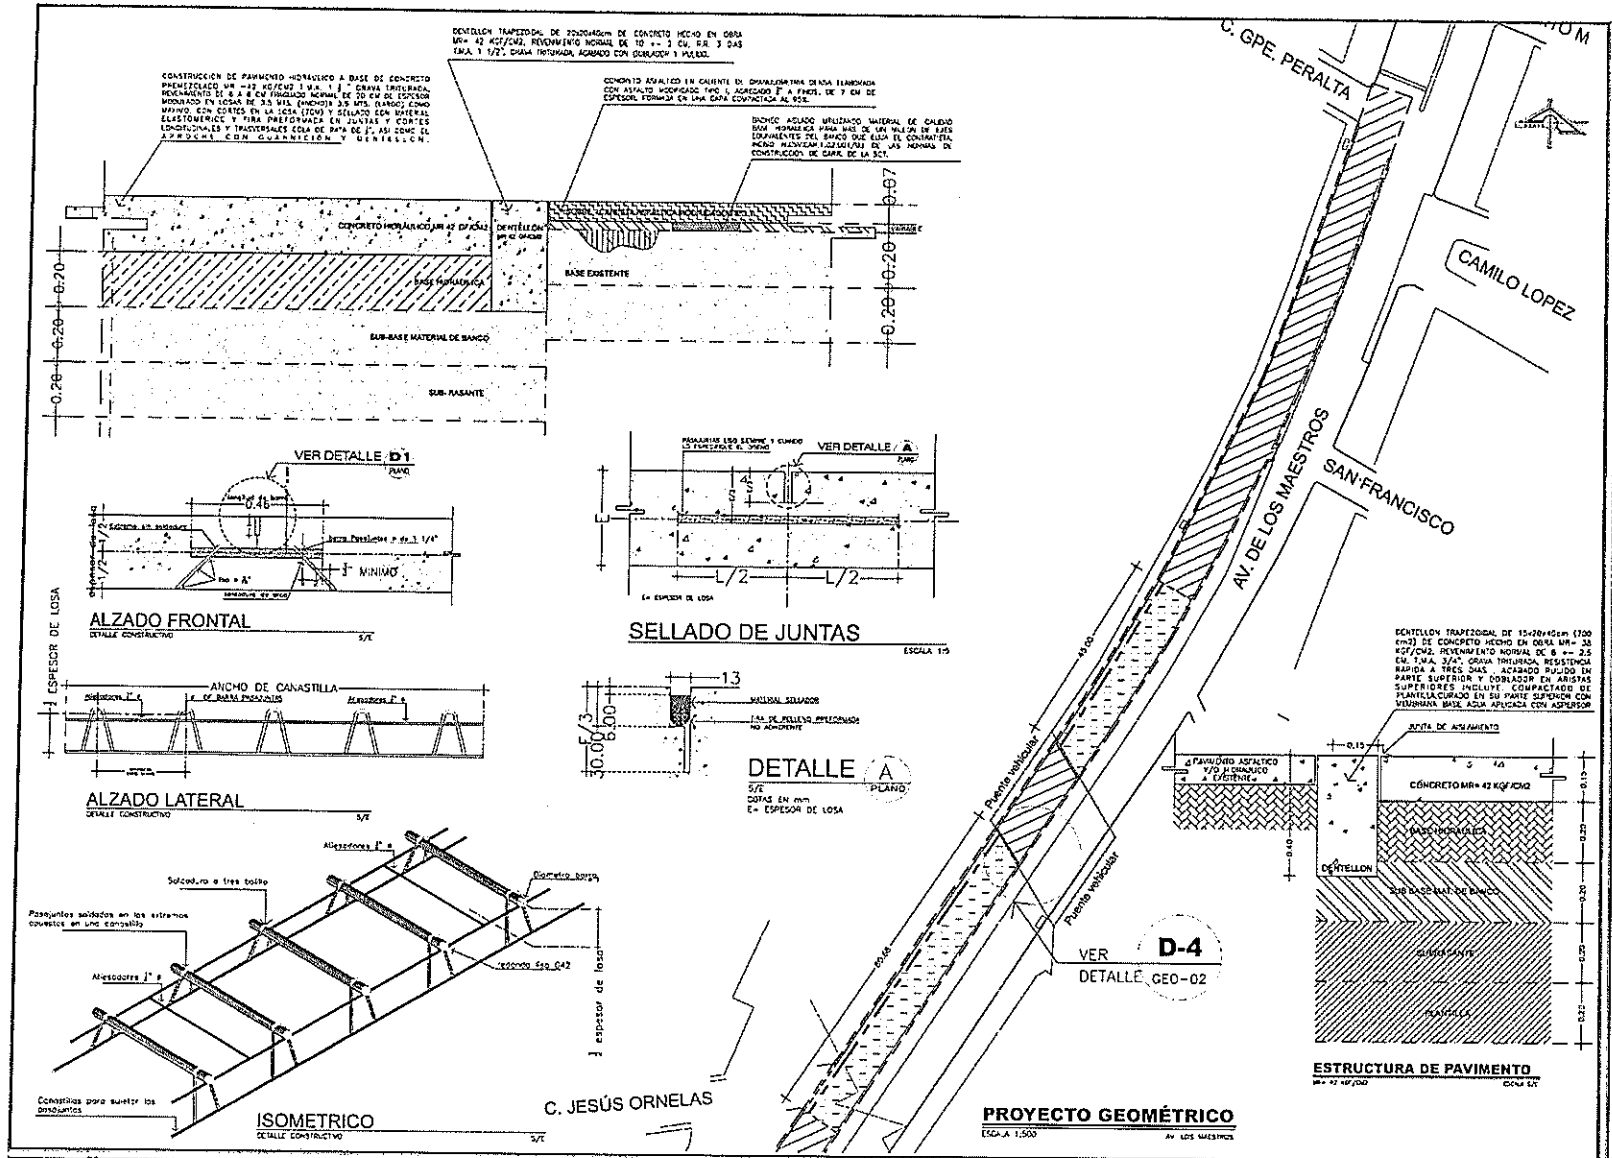

PRESIDENTE MUNICIPAL
M.P.P. Leonardo Montañez Castro
ENCARGADA DE DESPACHO DE LA SOPMA
Arq. Gloria Guadalupe Castillo González

REV	FECHA	OBSERVACIONES

V.o.B. DE LA DEPENDENCIA

RESP. DE PROY. EXTERNO		LOGO EXTERNO
CED. PROFESIONAL		
PROYECTO	REVISÓ	AUTORIZÓ


Dirección de Planeación y Proyectos de Obra — Secretaría de Obras Públicas

PROYECTISTA	COORDINADOR
ARQ. ALFONSO DAVID MEZA CORREDERAS	ARQ. ALEJANDRO JAIME LEAL
JEFE DE DEP	DIRECTOR
ARQ. JESÚS FAUSTO GONZÁLEZ	M. en ARQ. JOSÉ LUIS JIMÉNEZ CAPETILLO

PROYECTO: SOBRECARPETA ASFALTICA Y CONCRETO HIDRAULICO "AV. DE LOS MAESTROS" CALZADA PONIENTE
UBICACIÓN: CALZADA PONIENTE DE ENTRE AV. SIGLO XXI A CALLE GUADALUPE PERALTA
CONTENIDO: PROYECTO GEOMETRICO DETALLES DE ESTRUCTURA DE CONCRETO HIDRAULICO
ACOTACION: METROS


CLAVE	No. PLANO
GEO 02	06
FECHA: JULIO 2022	ESCALA: INDICADA
No. EXP: E-000-22	

Aguascalientes
LA CIUDAD DE TU VIDA

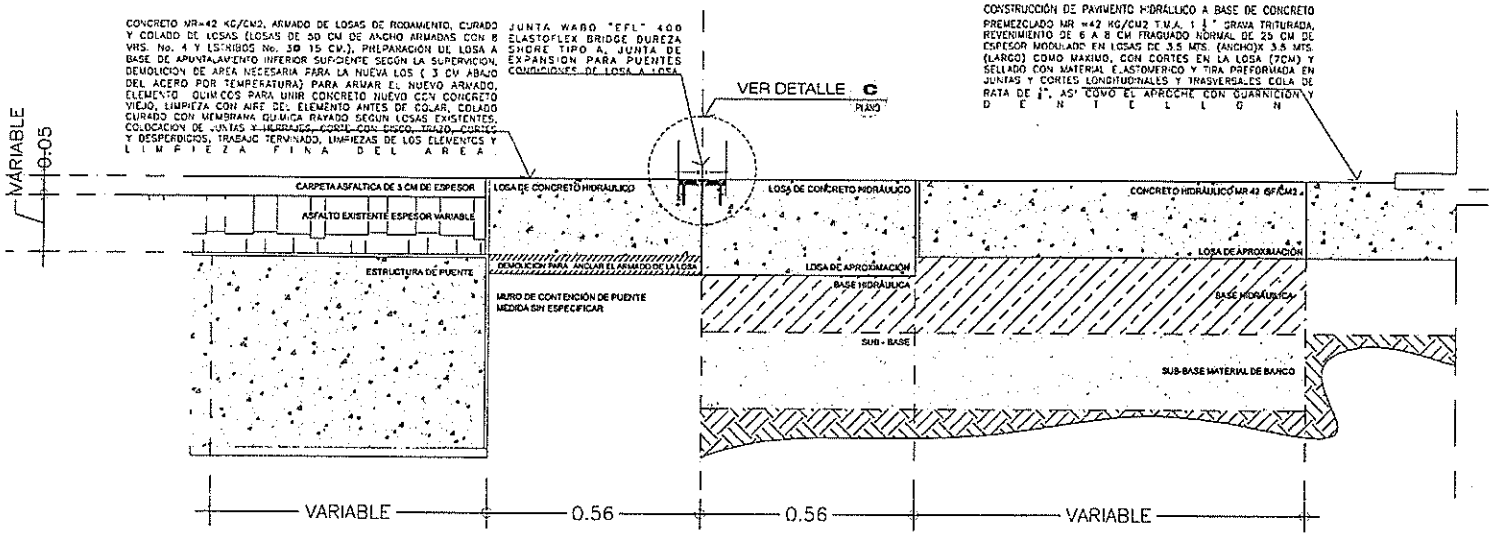

DETALLE 3 JUNTA WABO EFL 400 DE PAVIMENTO EN PUENTE VEHICULAR

ESCALA S/E

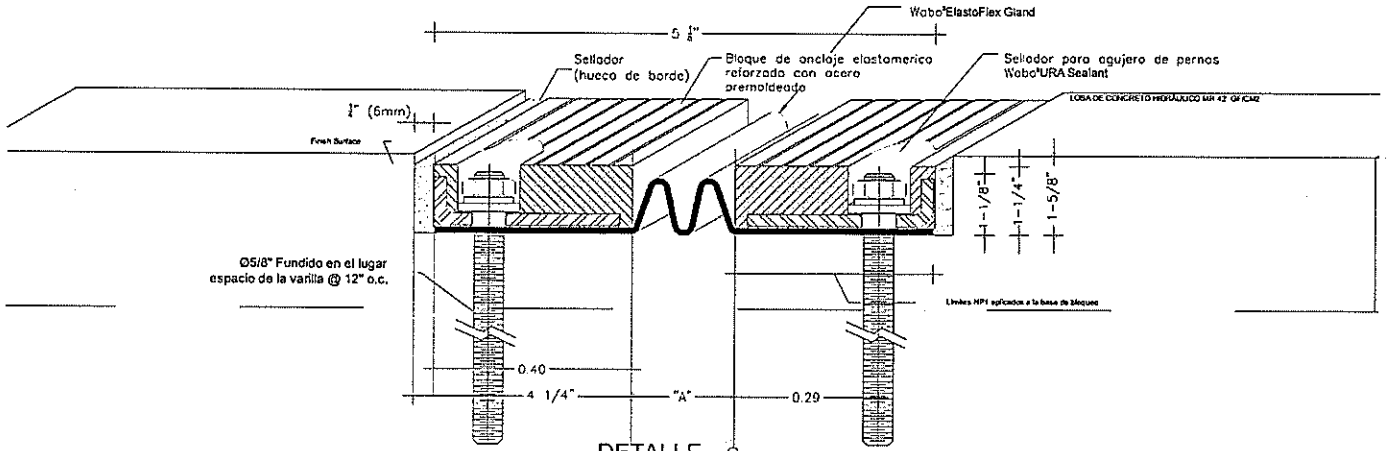


DETALLE C

S/E — PLANO

COTAS EN mm

LOCALIZACIÓN:

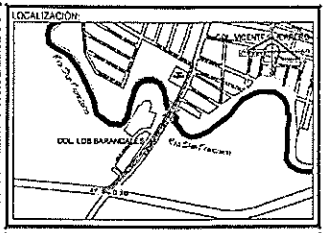

SIMBOLOGÍA

La Dirección de Planeación y Proyectos solo autoriza el proyecto ejecutivo, no es responsable de la correcta ejecución de la obra. Este documento no tiene validez si no presenta las firmas de los responsables para su autorización, así como los sellos respectivos.

PRESIDENTE MUNICIPAL
M.P.P. Leonardo Montañez Castro
ENCARGADA DE DESPACHO DE LA SOFMA
Arq. Gloria Guadalupe Castillo González

REV.	FECHA	OBSERVACIONES

V° Bo. DE LA DEPENDENCIA


RESP. DE PROY. EXTERNO		LOGO EXTERNO
CED. PROFESIONAL		
PROYECTO	REVISO	AUTORIZO

Dirección de Planeación y Proyectos de Obra	Secretaría de Obras Públicas
PROYECTISTA	COORDINADOR
ARQ. ÁLVARO DAVID MEZA CONTRERAS	ARQ. ALEJANDRO JAIME LEAL
JEFE DE DEP.	DIRECTOR
ARQ. J. JESÚS PALAFOX GONZÁLEZ	M. en ARQ. JOSÉ LUIS JIMÉNEZ GARCÍA

PROYECTO
SOBRECARPETA ASFALTICA Y CONCRETO HIDRAULICO "AV. DE LOS MAESTROS" CALZADA PONIENTE
UBICACIÓN
CALZADA PONIENTE DE ENTRE AV. SIGLO XXI A CALLE GUADALUPE PERALTA
CONTENIDO
JUNTA CONSTRUCTIVA
DETALLES DE ESTRUCTURA DE CONCRETO HIDRAULICO

CLAVE	No. PLANO
GEO 03	07
FECHA	ESCALA
JULIO 2022	INDICADA
ACOTACION	No. EXP.
METROS	E-000-22


Aguascalientes
LA CIUDAD DE TU VIDA

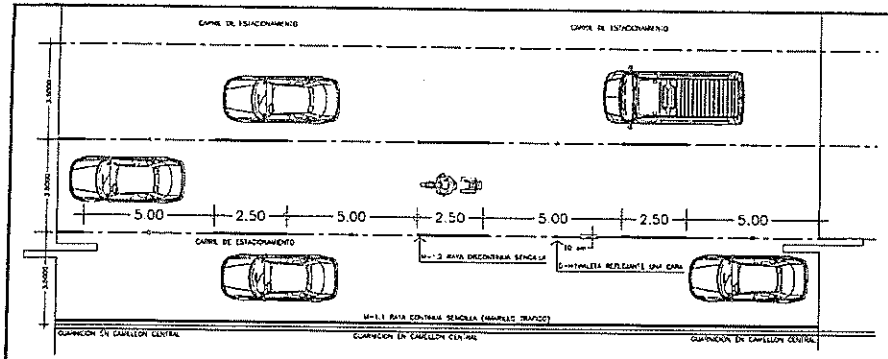

DETALLE TIPO 1

PARA VELOCIDADES MENOR A 60 KM/HR
LINEA DISCONTINUA DE 3.50 MTS ESPACIO 5 MTS
ESPESOR 10CM


S/E

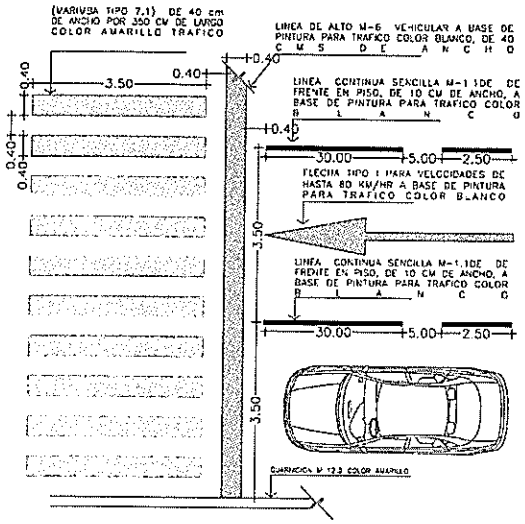

DETALLE 2

TRAZO PINTURA EN CRUCEROS


SIN ESCALA

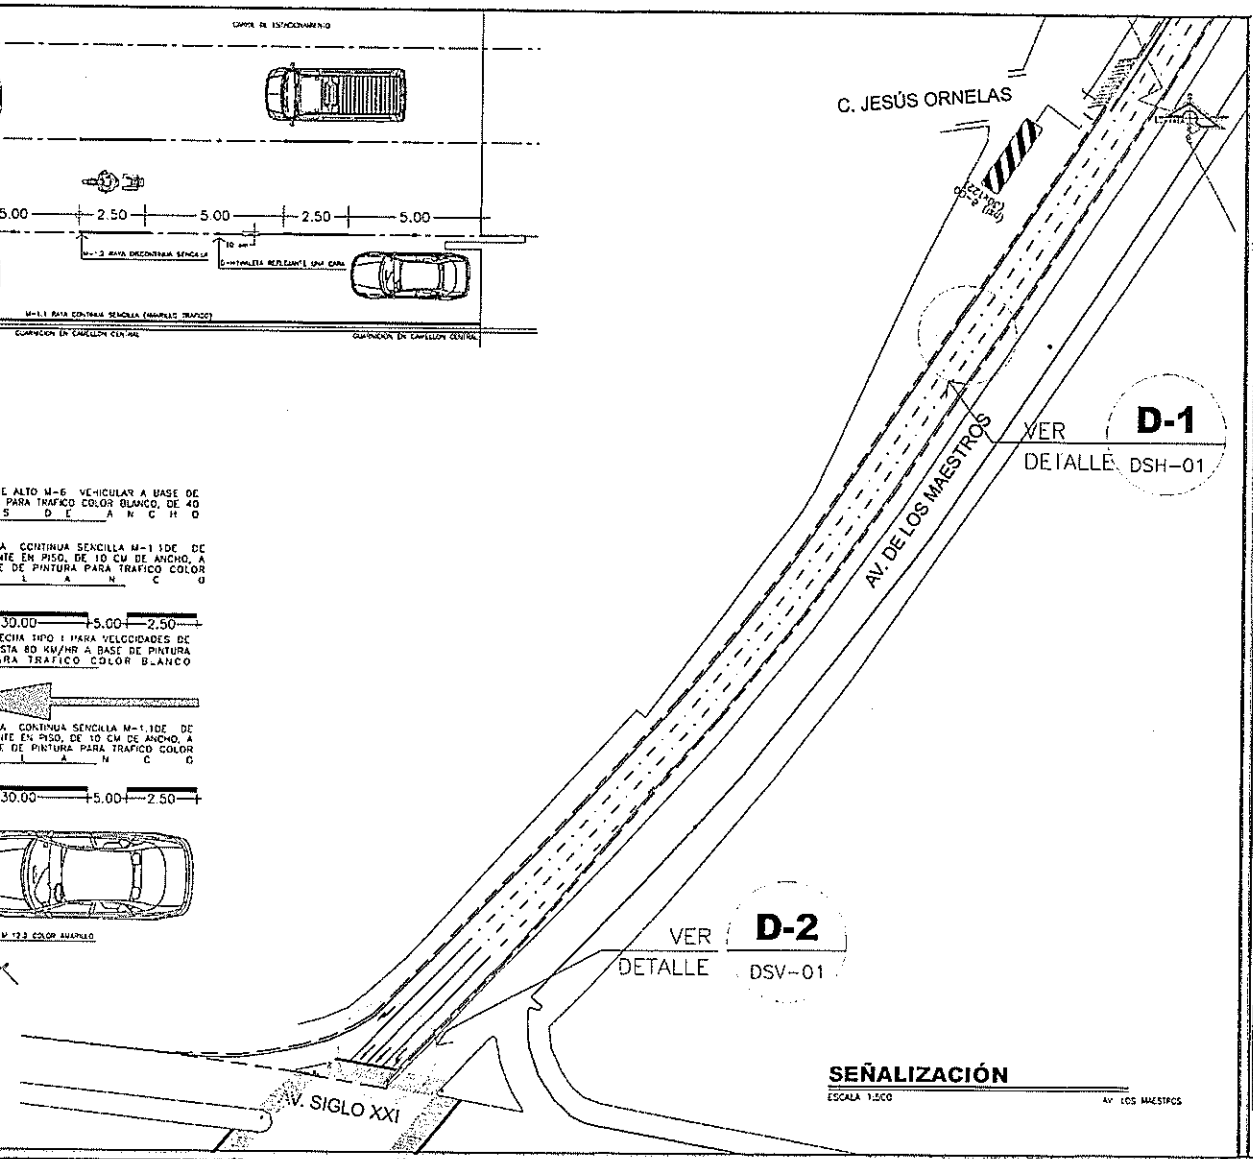

SEÑALIZACIÓN

ESCALA 1:500

AV. LOS MAESTROS

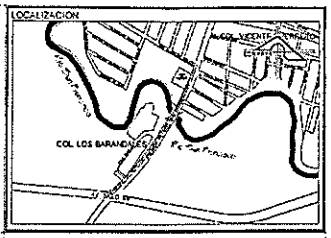

SIMBOLOGÍA

NOTA:
Se aplicará en todos los señalamientos horizontales pintura para trafico base solvente tipo alquidal de secado rápido, que cumpla con los especificaciones n-cmt-5-01-001/05, n-pry-car-10-01-002/13 de la SCT aplicados al dia de hoy.

Se aplicará en todos los señalamientos horizontales pintura para trafico Termoplastico tipo alquidal de secado rápido, que cumpla con los especificaciones n-cmt-5-01-001/05, n-pry-car-10-01-002/13 de la SCT aplicados al dia de hoy.

M – 1.2, Linea discontinua sencilla de división de carriles de frente en piso, de 10 cm de ancho.
M – 3.3, Continua izquierda, para vialidades urbanas de frente en piso, separada 15 cm de la guarnición, color amarillo.
M – 4, Para indicar linea guia en zona de transición de frejte en piso, desarrolo de 2.00 x 0.10 mts entre si promedio.
M – 5, Para indicar entrada y salida en bifurcaciones.
M – 6, Para indicar alto en cruceros, color blanco.
M – 7.1, Para indicar "cruce peatonal en primarias" color amarillo.
M – 11.1 "Flecha sencilla" para indicar sentido de circulación.
M – 11.1, "Flecha doble cabeza" para indicar sentido de circulación (vuelta izquierda o derecha).

NOTA:
Nota1: Se aplicará en todos los señalamientos horizontales pintura para trafico base solvente y/o termoplastico tipo alquidal de secado rápido, que cumpla con los especificaciones n-cmt-5-01-001/05, n-pry-car-10-01-002/13 de la SCT aplicados al dia de hoy.

Nota2: Dosificación de micro esfera
La cantidad de esferas de vidrio en la película de pintura en húmedo, según su tipo, será la que se indica en la Tabla.

TABLA 8: Cantidad de esferas de vidrio en la película de pintura en humedo.

CANTIDAD DE ESFERAS DE VIDRIO EN LA PELICULA DE PINTURA EN HÚMEDO				
TIPO DE PINTURA	ESPESOR DE LA PELÍCULA DE PINTURA EN HÚMEDO mm	CANTIDAD DE ESFERAS EQMO INTEGRADAS	LEVANTADAS, MÍNIMO	TIPO DE GRANULOMETRÍA
BASE SOLVENTE	0.30 A 0.50	-	0.150	II
BASE AGUA	0.30 A 0.50	-	0.230	I o II
TERMOPLÁSTICA	1.50 A 3.00	-	0.330	II

La Dirección de Planeación y Proyectos solo autoriza el proyecto ejecutivo, no es responsable de la correcta ejecución de la obra. Este documento no tiene validez si no presenta las firmas de los responsables para su autorización, así como los sellos respectivos.

PRESIDENTE MUNICIPAL
M.P.P. Leonardo Montañez Castro
ENCARGADA DE DESPACHO DE LA SOPIMA
Arq. Gloria Guadalupe Castillo González

REV	FECHA	OBSERVACIONES

VOLADO DE LA DEPENDENCIA

RESP DE PROY. EXTERNO		LOGO EXTERNO
CED PROFESIONAL		
PROYECTÓ	REVISÓ	AUTORIZÓ

Dirección de Planeación y Proyectos de Obra — Secretaría de Obras Públicas

PROYECTISTA	COORDINADOR
ARQ. IVONNE DAVID MEZA CONTRERAS	ARQ. ALEJANDRO JAIME LEAL
JEFE DE DEP.	DIRECTOR
ARQ. J. JESÚS PALAFOX GONZÁLEZ	M. en ARQ. JOSE LUIS JIMÉNEZ GARCÍA


PROYECTO
SOBRECARPETA ASFALTICA Y CONCRETO HIDRAULICO "AV. DE LOS MAESTROS" CALZADA PONIENTE

UBICACIÓN
CALZADA PONIENTE DE ENTRE AV. SIGLO XXI A CALLE GUADALUPE PERALTA

CONTENIDO
PROYECTO SEÑALIZACIÓN HORIZONTAL

CLAVE	No PLANO
SEÑ 01	08
FECHA	ESCALA
JULIO 2022	INDICADA
ACOTACIÓN METROS	No EXP. E-000-22

Aguascalientes
LA CIUDAD DE TU VIDA

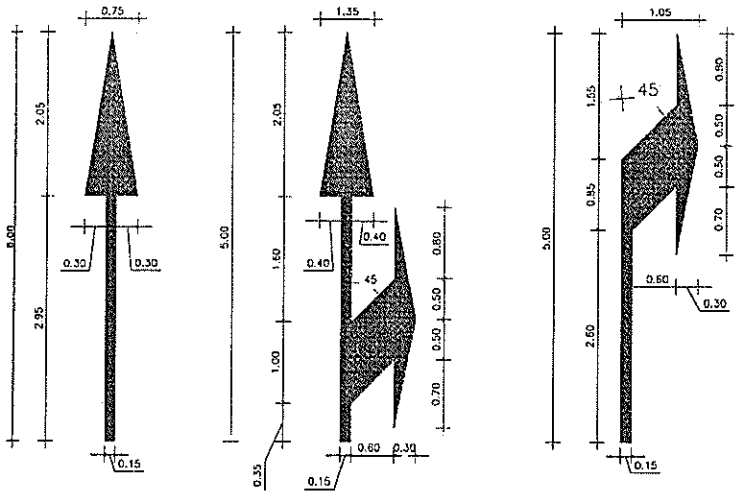

DETALLE DE FLECHAS EN PAVIMENTO
PARA VELOCIDADES HASTA DE 60KM/H
COTAS EN M


SEÑALES PREVENTIVAS						
SIMBOLO	CLAVE	DESCRIPCIÓN	DIMENSIÓN (cm)	UNIDAD	COLOR	CANTIDAD
	SP-19	SALIDA A LA DERECHA	71 X 71	PZA	AMARILLO REFLEJANTE	1

OBRAS Y DISPOSITIVOS DIVERSOS						
SIMBOLO	CLAVE	DESCRIPCIÓN	DIMENSIÓN (cm)	UNIDAD	COLOR	CANTIDAD
	OD-5I	ZONA PEATONAL	30 X 122	PZA	AMARILLO REFLEJANTE	1

EN CORTE

1.50 MAXIMA

0.50 MINIMA

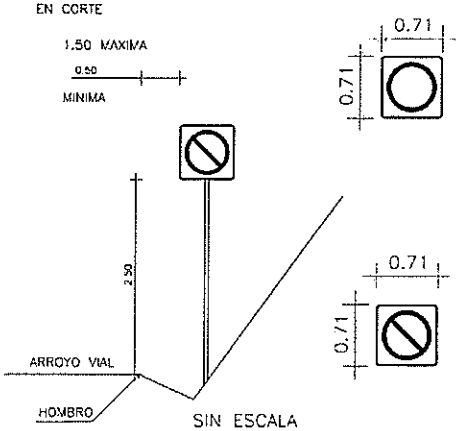


SIN ESCALA

EN TERRAPLEN


1.50 MAXIMA

0.50 MINIMA

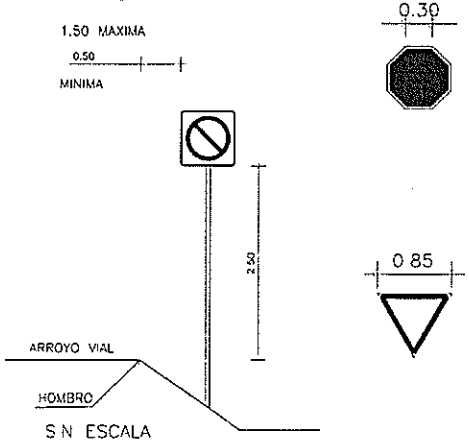

S N ESCALA


ZONA URBANA

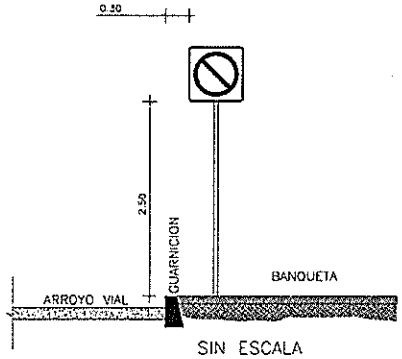

SIN ESCALA

NOTA: LAS SECCIONES ESTRUCTURALES SE ENCUENTRAN EL APARTADO II.7.3. ESTRUCTURA DE SOPORTE DE SEÑALES BAJAS. DEL MANUAL DE SEÑALAMIENTO VIAL DE LA SCT

LOCALIZACIÓN:

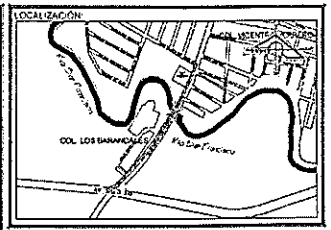

SIMBOLOGÍA

NOTA:
Se aplicará en todos los señalamientos horizontales pintura para trafico base solvente tipo alquidal de secado rápido, que cumpla con las especificaciones n-cmt-5-01-001/05, n-pry-car-10-01-002/13 de la SCT aplicados al día de hoy.

M-12.1, M12.2 APLICADA SOBRE GUARNICIONES Y DENTELLONES DE CUALQUIER COLOR

Se aplicará en todos los señalamientos horizontales pintura para trafico Termoplastica tipo alquidal de secado rápido, que cumpla con las especificaciones n-cmt-5-01-001/05, n-pry-car-10-01-002/13 de la SCT aplicados al día de hoy.

M - 1.2, LÍNEA DISCONTINUA SENCILLA DE DIVISIÓN DE CARRILES DE FRENTE EN PISO, DE 10 CM DE ANCHO

M - 3.3, CONTINUA IZQUIERDA, PARA VIALIDADES URBANAS DE FRENTE EN PISO, SEPARADA 15 CM. DE LA GUARNICION, COLOR AMARILLO

M - 4, PARA INDICAR LÍNEA GUÍA EN ZONA DE TRANSICIÓN DE FRENTE EN PISO, DESARROLLO DE 2.00 X 0.10 MTS, CON UNA SEPARACIÓN DE 4.00 MTS ENTRE SI PROMEDIO

M - 5, PARA INDICAR ENTRADA Y SALIDA EN BIFURCACIONES

M - 6, PARA INDICAR ALTO EN CRUCEROS, COLOR BLANCO

M - 7.1, PARA INDICAR " CRUCE PEATONAL EN VIAS PRIMARIAS" COLOR AMARILLO

M - 11.1, "FLECHA SENCILLA" PARA INDICAR SENTIDO DE CIRCULACIÓN

M - 11.1, "FLECHA CABEZA DOBLE" PARA INDICAR SENTIDO DE CIRCULACIÓN (VUELTA IZQUIERDA O DERECHA)

NOTA:
Nota1: Se aplicará en todos los señalamientos horizontales pintura para trafico base solvente y/o termoplastica los plazos de secado rápido que cumplo con las especificaciones n-cmt-5-01-001/05 n-pry-car-10-01-002/13 de la SCT aplicados al día de hoy.

Nota2. Dosificación de micro esfera
La cantidad de esferas de vidrio en la película de pintura en húmedo según su tipo, será la que se indica en la Tabla.

TABLA 8: Cantidad de esferas de vidrio en la película de pintura en humedo.

CANTIDAD DE ESFERAS DE VIDRIO EN LA PELÍCULA DE PINTURA EN HÚMEDO				
TIPO DE PINTURA	ESPESOR DE LA PELÍCULA DE PINTURA EN HÚMEDO mm	CANTIDAD ESFERAS KG/M2 INTEGRADAS	CANTIDAD ESFERAS KG/M2 SUPERFICIAL MÍNIMO	TIPO DE GUARNICIONETA
BASE SOLVENTE	0.30 A 0.50	-	0.350	I
BASE AGUA	0.30 A 0.50	-	0.350	III A
TERMOPLÁSTICA	3.00 A 3.00	-	0.350	II

La Dirección de Planeación y Proyectos solo autoriza el proyecto ejecutivo, no es responsable de la correcta ejecución de la obra. Este documento no tiene validez si no presenta las firmas de los responsables para su autorización así como los sellos respectivos.

PRESIDENTE MUNICIPAL: M.P.P. Leonardo Montañez Castro. ENCARGADA DE DESPACHO DE LA SCPMA: Arq. Gloria Guadalupe Castillo González	REV.	FECHA	OBSERVACIONES	V°B° DE LA DEPENDENCIA	RESP. DE PROY. EXTERNO / CED. PROFESIONAL	LOGO EXTERNO	Dirección de Planeación y Proyectos de Obra / Secretaría de Obras Públicas	PROYECTO: SOBRECARPETA ASFALTICA Y CONCRETO HIDRAULICO "AV. DE LOS MAESTROS" CALZADA PONIENTE. UBICACIÓN: CALZADA PONIENTE DE ENTRE AV. SIGLO XXI A CALLE GUADALUPE PERALTA. CONTENIDO: DETALLES SEÑALETICA VERTICAL	CLAVE: DSV 01	No. PLANO: 10
					PROYECTO / REVISO / AUTORIZÓ		PROYECTISTA: ARQ. ALFREDO DAVID MEZA CONTRERAS. COORDINADOR: ARQ. ALEJANDRO JAIME LEAL. JEFE DE DEP.: ARQ. J. JESÚS PALAFOX GONZÁLEZ. DIRECTOR: M. en ARQ. JOSÉ LUIS JIMÉNEZ GARCÍA		FECHA: JULIO 2022	ESCALA INDICADA
									ACOTACIÓN: METROS	NO. EXP.: E-000-22

Aguascalientes. LA CIUDAD DE TU VIDA