Aguascalientes
LA CIUDAD DE TU VIDA

Dirección de Programación Presupuestal
Núm. Oficio AMPP/0561/22
Aguascalientes, Ags. 6 de Diciembre del 2022
Asunto: Validación de Expediente Técnico

C.P. SERGIO ARTURO LOZANO GONZÁLEZ
SECRETARIO DE FINANZAS MUNICIPALES
P R E S E N T E

Con fundamento en los artículos 17 fracción XV, 60 fracción XVI y 76 fracción VI del Reglamento del Sistema Integral de Desarrollo Municipal y del Instituto Municipal de Planeación y Evaluación de Aguascalientes, hago referencia al oficio SOPMA/2690/2022 recibido por este Instituto el día 5 de Diciembre del 2022 por parte de la Secretaría de Obras Públicas Municipales, mediante el cual remiten el expediente técnico original de la siguiente obra para su análisis, registro y priorización, conforme al Programa Anual de Obra Pública y Programas Sociales para el ejercicio presupuestal 2022:

DEPENDENCIA EJECUTORA:	SOPMA
NOMBRE DE LA OBRA O PROYECTO:	REHABILITACIÓN Y CONSTRUCCIÓN DE TROTAPISTA Y MARCADOR ELECTRÓNICO
UBICACIÓN:	PARQUE EX-PENSIÓN MUNICIPAL, AV. OJOCALIENTE Y AV. SAN GABRIEL, OJOCALIENTE III, AGUASCALIENTES, AGS.
FONDO DE INVERSIÓN:	FONDO DE INFRAESTRUCTURA SOCIAL MUNICIPAL Y DE LAS DEMARCACIONES TERRITORIALES DEL DISTRITO FEDERAL
IMPORTE:	$392,910.18 (ET FINAL)
No. DE OBRA:	2022-FISMDF-0071-13-4000
MODALIDAD DE EJECUCIÓN:	CONTRATO
EJE:	MUNICIPIO SOBRESALIENTE
ESTRATEGIA:	OBRA PÚBLICA INTELIGENTE
POLITICA:	5.8.2.REHABILITACIÓN Y MANTENIMIENTO ESPACIOS PÚBLICOS E INFRAESTRUCTURA URBANA.

Al respecto, hago de su conocimiento que dicho expediente ha sido analizado en su integración técnica y documental, con base en el artículo 168 fracción I del Reglamento de la Ley de Obras Públicas y Servicios Relacionados para el Estado de Aguascalientes y sus Municipios.

Asimismo, le comento que este Instituto valida dicha obra acorde a lo establecido en los artículos 14, 22 párrafo segundo y 23 de la Ley de Obras Públicas y Servicios Relacionados para el Estado de Aguascalientes y sus Municipios, la cual se encuentra alineada al Plan de Desarrollo Municipal vigente, para dar cumplimiento a las metas establecidas en el mismo, y a los Lineamientos Generales para la Operación de este Fondo de Inversión, toda vez que la misma cuente con la autorización del CODEMUN. De igual manera, se hace de su conocimiento que deberá cumplir con lo establecido en los ordenamientos aplicables en lo que respecta al ejercicio, control e información de los recursos de este Fondo. Cabe hacer mención que los recursos solicitados para este proyecto de inversión, estarán sujetos a la disponibilidad presupuestal para el presente ejercicio fiscal que determine la Secretaría a su digno cargo. Sin otro particular por el momento, le envío un cordial saludo.

A T E N T A M E N T E

ARQ. AUSTRIA GABRIELA DÁVILA DE LA LLAVE
DIRECTORA GENERAL DEL IMPLAN

CAAR / JDBG
C.c.p. I.C. ING. MIGUEL ÁNGEL HUIZAR BOTELLO .- Secretaría de Obras Públicas Municipales .Para su conocimiento.
C.c.p. Archivo.

Instituto Municipal de Planeación y Evaluación de Aguascalientes
Antonio Acevedo Escobedo 103 A. Col. Centro
Aguascalientes. Ags. C.P. 20000
(449) 9101010 Ext. 3117
www.implanags.gob.mx

GOBIERNO MUNICIPAL DE AGUASCALIENTES

INSTITUTO MUNICIPAL DE PLANEACION

IMPLAN

ANÁLISIS INTEGRAL DE EXPEDIENTE TÉCNICO

No. DE OBRA (PAOP 2020):	2022-FISMDF-0071-13-4000	REGISTRO No.	233
OFICIO DE VALIDACIÓN:	AMPP/0561/22	FECHA RECIBIDO PARA REVISIÓN:	6 de Diciembre del 2022
PROGRAMA:	INFRAESTRUCTURA DEPORTIVA	LOCALIDAD O COLONIA:	OJOCALIENTE III
SUB-PROGRAMA:	Construcción	DELEGACIÓN:	Guadalupe Peralta
DEPENDENCIA:	Secretaría de Obras Públicas Municipales	MOD. DE EJECUCIÓN:	CONTRATO
NOMBRE DE LA OBRA:	REHABILITACIÓN Y CONSTRUCCIÓN DE TROTAPISTA Y MARCADOR ELECTRÓNICO, PARQUE EX-PENSIÓN MUNICIPAL, AV. OJOCALIENTE Y AV. SAN GABRIEL		
FUENTE DE FINANCIAMIENTO:	FONDO DE INFRAESTRUCTURA SOCIAL MUNICIPAL Y DE LAS DEMARCACIONES TERRITORIALES DEL DISTRITO FEDERAL, FISMDF		
INVERSIÓN:	$392,910.18	CLASIFICACIÓN DE OBRA:	BIENES DE DOMINIO PUBLICA

TOTAL	FEDERAL	ESTATAL	MUNICIPAL	BENEFICIARIOS	OTROS	DIFERENCIA ENTRE MOD.
$392,910.18	$392,910.18	0.00	0.00	0.00	0.00	*$20.331,70*

TIPO DE EXPENDIENTE:	ET FINAL	AÑO: 2022	AÑO:	AÑO:		
AVANCES:	Financiero: 93 %	Físico: 100 %				
FECHA DE INICIO:	23 de Julio del 2022	FECHA DE TÉRMINO:	28 de Agosto del 2022	REGISTRO SIMA:	71	

CHEK LIST DE LOS ANEXOS DEL EXPEDIENTE TÉCNICO

CÉDULA DE REGISTRO DE OBRA	✓
DICTAMEN DE FACTIBILIDAD	✓
MEMORIA DESCRIPTIVA	✓
PRESUPUESTO BASE	✓
FACTIBILIDAD VERIFICADA EN CAMPO	✓
CROQUIS DE UBICACIÓN (MACRO)	✓
CROQUIS DE UBICACIÓN (MACRO)	✓
PROGRAMA DE OBRA Y MONTOS MENSUALES	✓
PLANOS O ESTUDIOS TÉCNICOS	✓
PADRÓN DE BENEFICIARIOS	N/A
ACTA DE ACEPTACIÓN DEL PROYECTO	N/A
DICTAMEN DE IMPACTO AMBIENTAL	N/A
CONVENIO DE CONCERTACIÓN	N/A
ACTA CONSTITUTIVA	N/A

METAS		BENEFICIARIOS		PERIODO DE EJECUCION		OBRA PROPUESTA		CLAVE SISCO
UNIDAD DE MEDIDA	CANT	TIPO DE BENEFICIARIOS	CANTIDAD	FECHA DE INICIO	FECHA DE TERMINO	CONCEPTO	JORNALES A GENERAR	
OBRA	1	Personas	160	2022-07-23	2022-08-28	Trotapista	1021	2344

INCLUIDO EN PLAN DE DESARROLLO MUNICIPAL Y EL PROGRAMA ANUAL DE OBRA PÚBLICA

OBSERVACIONES:

SIN OBSERVACIONES

RECIBIO: ING. JOSÉ DAVID BURGUETE CLAUSTRO
Analista de Programación e Inversión de Obra Pública

6 de Diciembre del 2022
Fecha de validación

6 de Diciembre del 2022
Fecha de validación Expediente

PROCEDE Si ✓ No

H. AYUNTAMIENTO CONSTITUCIONAL DEL MUNICIPIO DE AGUASCALIENTES 2021-2024

AYUNTAMIENTO DE AGUASCALIENTES

CEDULA DE REGISTRO POR OBRA

Aguascalientes

050400-001E00E05-05-2-2-2-00-1-E-0509-0-17-0071-21-2502-6122

2022-FISMDF-0071-1340-029	Obra **REHABILITACIÓN Y CONSTRUCCIÓN DE TROTAPISTA Y MARCADOR ELECTRÓNICO, PARQUE EX-PENSIÓN MUNICIPAL**
Tipo DEFINITIVO 1 2022 Folio SISCO **2344**	Ubic. AV. OJOCALIENTE Y AV. SAN GABRIEL, FRACC. OJOCALIENTE II, AGUASCALIENTES Mpio.

Ent. Ejecutora : **050400001E00E05**

Eje: **05**	MUNICIPIO SOBRESALIENTE
Finalidad: **2**	DESARROLLO SOCIAL
Función: **2**	VIVIENDA Y SERVICIOS A LA COMUNIDAD
Subfunción: **2**	DESARROLLO COMUNITARIO
Tema: **00**	SIN TEMA
Cuenta del Gasto **1**	GASTO PROGRAMABLE
Clasif. Programatica: **E**	PRESTACIÓN DE SERVICIOS PÚBLICOS
Programa: **0509**	Infraestructura Inteligente
SubPrograma: **0**	SUBPROGRAMA GENÉRICO
Proyecto: **17**	
Tipo de Gasto: **21**	GASTO INVERSIÓN / OBRA PÚBLICA

I N V E R S I O N 2022

Municipal	2502	FONDO PARA LA INFRAESTRUCTURA SOCIAL MUNICIPAL Y DE LAS DEMARCACIONES TERRITORIALES DEL DISTRITO FEDERAL 2022	$392,910.18

Folio SIMA 71 Total $392,910.18

M E T A S

Unidad de Medida	Cantidad	Descripción
OBRA	1	OBRA REHABILITACIÓN Y CONSTRUCCIÓN DE TROTAPISTA Y MARCADOR ELECTRÓNICO, PARQUE EX-PENSIÓN MUNICIPAL

Inversión Ejercida Total al 31 de Diciembre de 2021 $0.00

Avance Fisico Acumulado al 31 de Diciembre de 2021

Avance Fisico Acumulado Programado al 31 de Diciembre de 2022 100 %

Fecha de Inicio 23 Jul 2022 Fecha de Terminación 28 Ago 2022

Jornales a Generar en 2022 1021

Modalidad de ejecución CONTRATO

Clasificación de la Obra Bienes de Dominio Público

Registro del Patrimonio: Infraestructura

OBRAS PÚBLICAS

Av. Aguascalientes Sur No. 2615
Fracc. Jardines de las Fuentes,
Aguascalientes, Ags. C.P. 20278

(449) 9 78 92 01, 06, 09

www.ags.gob.mx

GENERALES

Nombre del Proyecto : REHABILITACIÓN Y CONSTRUCCIÓN DE TROTAPISTA Y MARCADOR ELECTRÓNICO, PARQUE EX-PENSIÓN MUNICIPAL

AV. OJOCALIENTE Y AV. SAN GABRIEL, FRACC. OJOCALIENTE II, AGUASCALIENTES Mpio.

Programa : 13 INFRAESTRUCTURA DEPORTIVA

Subprograma :

Clave del Municipio : AGUASCALIENTES

Localidad :

Barrio, Colonia o Ejido : AGUASCALIENTES Mpio.

Tipo de Obra : NUEVA

DESCRIPCIÓN DEL PROYECTO:

REHABILITACIÓN Y CONSTRUCCIÓN DE TROTAPISTA Y MARCADOR ELECTRÓNICO, PARQUE EX-PENSIÓN MUNICIPAL 1.00 obra

Beneficiarios (No. y Tipo) :

160	PERSONAS

OBRAS PÚBLICAS

Av. Aguascalientes Sur No. 2615
Fracc. Jardines de las Fuentes,
Aguascalientes, Ags. C.P. 20278

(449) 9 78 92 01, 06, 09

www.ags.gob.mx

Los abajo firmantes, hacen constar que el presente proyecto :

REHABILITACIÓN Y CONSTRUCCIÓN DE TROTAPISTA Y MARCADOR ELECTRÓNICO, PARQUE EX-PENSIÓN MUNICIPAL

AV. OJOCALIENTE Y AV. SAN GABRIEL, FRACC. OJOCALIENTE II, AGUASCALIENTES Mpio.

cumple con los Requisitos y Normas Técnicas establecidas por la Dependencia Normativa, por lo que es viable su ejecución. Comprometiéndose la misma a proporcionar la supervisión y asistencia técnica necesaria durante el proceso administrativo.

Por la Dependencia Ejecutora

Ing. Miguel Angel Huizar Botello
Secretario de Obras Públicas

Mtro. Edson Rubén Camarillo Rodríguez
Secretario de Desarrollo Social

LUGAR :AGUASCALIENTES, AGS.

Av. Aguascalientes Sur No. 2615
Fracc. Jardines de las Fuentes,
Aguascalientes, Ags. C.P. 20278

(449) 9 78 92 01, 06, 09

www.ags.gob.mx

H. AYUNTAMIENTO CONSTITUCIONAL DEL MUNICIPIO DE AGUASCALIENTES 2021-2024

AYUNTAMIENTO DE AGUASCALIENTES

FACTIBILIDAD VERIFICADA EN CAMPO

Aguascalientes
LA CIUDAD DE TU VIDA

MUNICIPIO: AGUASCALIENTES

LOCALIZACION: AV. OJOCALIENTE Y AV. SAN GABRIEL, FRACC. OJOCALIENTE II, AGUASCALIENTES Mpio.

PROGRAMA: INFRAESTRUCTURA DEPORTIVA

SUBPROGRAMA:

OBRA A REALIZAR: REHABILITACIÓN Y CONSTRUCCIÓN DE TROTAPISTA Y MARCADOR ELECTRÓNICO, PARQUE EX-PENSIÓN MUNICIPAL

DEPENDENCIA EJECUTORA: SECRETARÍA DE OBRAS PUBLICAS DEL MUNICIPIO DE AGUASCALIENTES

FORMA DE EJECUCION: CONTRATO

TIPO DE OBRA PROPUESTA: NUEVA

CONDICIONES ACTUALES DE LA OBRA:

REHABILITACIÓN Y CONSTRUCCIÓN DE TROTAPISTA Y MARCADOR ELECTRÓNICO, PARQUE EX-PENSIÓN MUNICIPAL

CARACTERISTICAS DE LA OBRA: Bueno

FACTIBILIDAD DE LA OBRA:

ESTA OBRA SE REQUIERE PARA EL BENEFICIO DE LA CIUDADANÍA

PROCEDE: SI [X] NO [ ]

REVISÓ: Jefa del Departamento de Expedientes Tecnicos y Costos

NOMBRE: Arq. Blanca Margarita Martinez Amador

FIRMA:

FECHA: 11 Nov 2022

SECRETARÍA DE OBRAS PÚBLICAS

Av. Aguascalientes Sur No. 2615
Fracc. Jardines de las Fuentes,
Aguascalientes, Ags. C.P. 20278

(449) 9 78 92 01, 06, 09


www.ags.gob.mx

No. Folio SISCO 2344

SECRETARIA DE OBRAS PUBLICAS MUNICIPALES

DIRECCION DE SUPERVISION

REHABILITACIÓN Y CONSTRUCCIÓN DE TROTAPISTA Y MARCADOR ELECTRÓNICO, PARQUE EX-PENSIÓN MUNICIPAL, AV. OJOCALIENTE Y AV. SAN GABRIEL, FRACC. OJOCALIENTE II, AGUASCALIENTES Mpio.

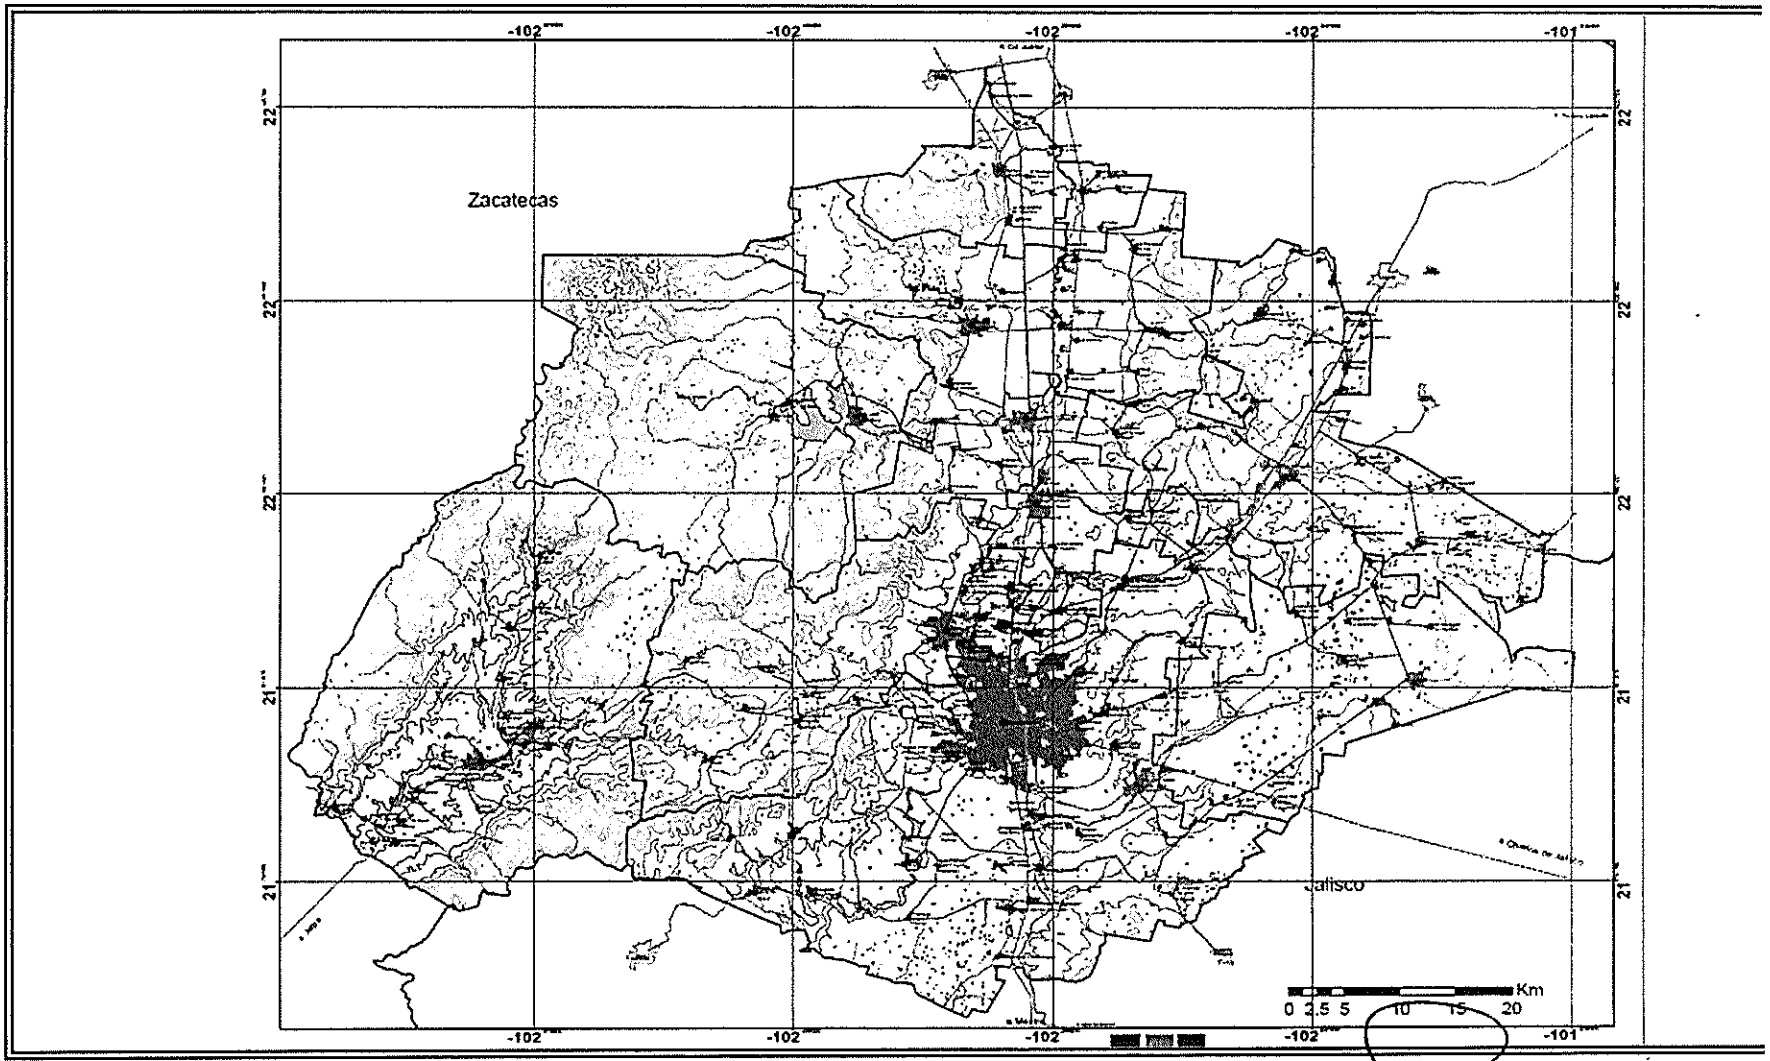

LOCALIZACION A NIVEL MACRO

SECRETARIA DE OBRAS PUBLICAS MUNICIPALES

DIRECCION DE SUPERVISION

REHABILITACIÓN Y CONSTRUCCIÓN DE TROTAPISTA Y MARCADOR ELECTRÓNICO, PARQUE EX-PENSIÓN MUNICIPAL, AV. OJOCALIENTE Y AV. SAN GABRIEL, FRACC. OJOCALIENTE II, AGUASCALIENTES Mpio.



LOCALIZACION A NIVEL MICRO

RO3-POS-SOS-7.5.1-04	
REVISION:	00
FECHA DE REVISION:	
RESPONSABLE:	SUPERVISOR DE OBRA
TIEMPO DE RET:	02 AÑOS

Aguascalientes
LA CIUDAD DE TU VIDA

PROGRAMA DE OBRA DEFINITIVO

No. DE CONTRATO : FISMDF-0071-2022

PROGRAMA: 13- INFRAESTRUCTURA DEPORTIVA

INICIO VIGENTE: 23-Julio-22

No. OBRA Y NOMBRE DE LA OBRA: REHABILITACIOÓN Y CONSTRUCCIÓN DE TROTAPISTA Y MARCADOR ELECTRÓNICO, PARQUE EX PENSIÓN MUNICIPAL

TERMINO REAL: 28-agosto-22

RECURSO 2022

| CONCEPTO | | | 2022 | | |

PRESIDENCIA MUNICIPAL DE AGUASCALIENTES

FACTIBILIDAD VERIFICADA EN CAMPO

GENERALES

EJERCICIO: 2022 APROBACION No: 2022-FISMDF-0071-1340-029
LOCALIDAD: A. OJOCALIENTE Y AV. SAN GABRIEL, FRACC. OJOCALIENTE II, AGUASCALIENTES Mpio.
MUNICIPIO: AGUASCALIENTES
TIPO DE INVERSION: FONDO PARA LA INFRAESTRUCTURA SOCIAL MUNICIPAL Y DE LAS DEMARCACIONES TERRITORIALES DEL DISTRITO FEDERAL
PROGRAMA: 13- INFRAESTRUCTURA DEPORTIVA
SUB-PROGRAMA:

OBRA A REALIZARSE: REHABILITACIOÓN Y CONSTRUCCIÓN DE TROTAPISTA Y MARCADOR ELECTRÓNICO, PARQUE EX PENSIÓN MUNICIPAL

DEPENDENCIA EJECUTORA: SECRETARÍA DE OBRAS PÚBLICAS MUNICIPALES (S.O.P.M.A)
FORMACIÓN DE EJECUCION: CONTRATO NO. DE CONTRATO: FISMDF-0071-2022
NOMBRE CONTRATISTA: EDIFICACIONES E INSTALACIONES DAP, S. DE R.L. DE C.V.
REPRESENTANTE: ILEANA PAULINA OLVERA GALLEGOS
MONTO CONT. ORIGEN $399,950.69 ANTICIPO: PLAZO 30
1A AMPLIACION $: 1 AMPL DIAS 7
2A AMPLIACION $: 2 AMPL DIAS
FIRMA CONTRATO: 18/07/2022
INICIO CONT: dd/mm/aa 19/07/2022 RMINO CONT: 24 de agosto de 2022
INICIO REAL: dd/mm/aa 23/07/2022 ERMINO REAL: 28 de agosto de 2022

TIPO DE OBRA PROPUESTA

NUEVA CREACIÓN	X	CONSOLIDACIÓN	
COMPLEMENTARIA		AMPLIACIÓN	
REHABILITACIÓN		EQUIPAMIENTO	

CARACTERÍSTICAS DE LA OBRA:

REHABILITACIOÓN Y CONSTRUCCIÓN DE TROTAPISTA Y MARCADOR ELECTRÓNICO, PARQUE EX PENSIÓN MUNICIPAL

CONDICIONES ACTUALES DE LA OBRA: (SELECCIONAR UNO OBLIGATORIO)

BUEN ESTADO X REGULAR PESIMO ESTADO

FACTIBILIDAD DE LA OBRA: (CONDICIONES ACTUALES DE LA OBRA)

ESTA OBRA SE ENCUENTRA EN CONDICIONES PARA OPERARSE

PROCEDE: SI: X NO:
MARQUE SOLO UNA

ARQ. ARIADNA MEDINA DOMINGUEZ
SUPERVISOR

PRESIDENCIA MUNICIPAL DE AGUASCALIENTES

FACTIBILIDAD VERIFICADA EN CAMPO

GENERALES

LOCALIDAD: A. OJOCALIENTE Y AV. SAN GABRIEL, FRACC. OJOCALIENTE II, AGUASCALIENTES Mpio.
MUNICIPIO: AGUASCALIENTES
PROGRAMA: 13- INFRAESTRUCTURA DEPORTIVA
SUB-PROGRAMA: 0
OBRA A REALIZARSE: REHABILITACIOÓN Y CONSTRUCCIÓN DE TROTAPISTA Y MARCADOR ELECTRÓNICO, PARQUE EX PENSIÓN MUNICIPAL

DEPENDENCIA EJECUTORA: SECRETARÍA DE OBRAS PÚBLICAS MUNICIPALES (S.O.P.M.A)
FORMACIÓN DE EJECUCION: CONTRATO

TIPO DE OBRA PROPUESTA

NUEVA CREACIÓN	X	CONSOLIDACIÓN	
COMPLEMENTARIA		AMPLIACIÓN	
REHABILITACIÓN		EQUIPAMIENTO	

CARACTERÍSTICAS DE LA OBRA:

REHABILITACIOÓN Y CONSTRUCCIÓN DE TROTAPISTA Y MARCADOR ELECTRÓNICO, PARQUE EX PENSIÓN MUNICIPAL

CONDICIONES ACTUALES DE LA OBRA:

BUEN ESTADO:	X	REGULAR:		PESIMO ESTADO:	

FACTIBILIDAD DE LA OBRA:

ESTA OBRA SE ENCUENTRA EN CONDICIONES PARA OPERARSE

PROCEDE	**SI:**	X	**NO:**	

ARQ. ARIADNA MEDINA DOMINGUEZ
SUPERVISOR

PRESUPUESTO MODIFICADO

Obra: REHABILITACIÓN Y CONSTRUCCIÓN DE TROTAPISTA Y MARCADOR ELECTRÓNICO, PARQUE EX-PENSIÓN MUNICIPAL

Ubicación: AV. OJOCALIENTE Y AV. SAN GABRIEL, FRACC. OJOCALIENTE II, AGUASCALIENTES Mpio.

Contratista: EDIFICACIONES E INSTALACIONES DAP, S. DE R.L. DE C.V. (276)

GRUPO: **REHABILITACIÓN Y CONSTRUCCIÓN DE TROTAPISTA Y MARCADOR ELECTRONICO PARQUE EX-PEN**

PARTIDA: **DEMOLICIONES Y DESMONTAJES**

No.	Concepto	Unidad	Cantidad	Precio Unitario	Importe Total
1	EXTRACCIÓN CON RECUPERACIÓN DE ARBOL (CUALQUIER ESPECIE) CON UNA ALTURA DE HASTA 5 MTS. DE ALTO Y TRONCON DE ENTRE 20cm Y 60cm, INCLUYE PODA, EXTRACCION DESDE EL TOCON,Y TRASPLANTE, LAS ACTIVIDADES DEBERAN CONTAR CON LAS SIGUIENTES ESPECIFICACIONES: BANQUEO (EL DIÁMETRO DE LA BOLA DEBE SER 9 VECES EL DIÁMETRO DEL TRONCO, MEDIDO 30 CM ARRIBA DEL CUELLO DE LA RAÍZ) ARPILLADO (CON ARPILLA O TELA DE COSTAL Y AMARRE EN FORMA DE TAMBOR CON CUERDAS DE HENEQUEN), CORTE DE LA BOLA CON CABLE DE ACERO DE 1/2", PROTECCIÓN DE FOLLAJE, REMOCIÓN POR MEDIOS FÍSICOS O MECÁNICOS, SIEMBRA, ABONO DE TIERRA LAMA, 1KG DE RAIZAL POR CADA ARBOL Y MANTENIMIENTO DURANTE 30 DIAS, INCLUYE: CARGO DIRECTO POR EL COSTO DE MANO DE OBRA Y MATERIALES REQUERIDOS, TRASLADO, ACARREOS DENTRO Y FUERA DE LA OBRA A EXCAVACIÓN DONDE LO INDIQUE LA SUPERVISIÓN, A UNA DISTANCIA NO MAYOR A 2km. FLETES, ALMACENAJE, EQUIPO DE SEGURIDAD, INSTALACIONES ESPECÍFICAS, DEPRECIACIÓN, ELEVACIONES, CUALQUIER ALTURA, HERRAMIENTA Y EQUIPO NECESARIO PARA LA CORRECTA EJECUCIÓN, LIMPIEZAS, TRABAJO TERMINADO. P.U.O.T.	PZA	2	$1,337.90	$2,675.80
2	CORTE CON DISCO EN PAVIMENTO DE CONCRETO (8cm DE PROFUNDIDAD). INCLUYE: EQUIPO Y OPERACION, AGUA NECESARIA, ACARREOS DENTRO DE LA OBRA, FLETES, PROTECCION DE AREAS ADYACENTES, EQUIPO Y HERRAMIENTA, LIMPIEZAS, TRABAJO TERMINADO. P.U.O.T.	ML	21.54	$45.71	$984.59
3	RETIRO DE MATERIAL PORFIDO IRREGULAR CUALQUIER SECCION, CON RECUPERACION DE PIEZAS, CON LIMPIEZA DE PIEZAS QUITANDO REBABA DE MORTERO, INCLUYE: CARGAS, ACARREOS DENTRO Y FUERA DE LA OBRA AL SITIO DONDE INDIQUE LA SUPERVISION DE LA SOPMA, DESCARGAS, RETIRO DEL MATERIAL SOBRANTE FUERA DE LA OBRA, MANO DE OBA, MATERIAL, HERRAMIENTA Y EQUIPO NECESARIO PARA SU CORRECTA EJECUCION, PROTECCION DE AREAS ADYACENTES TENIENDO CUIDADO DE NO ROMPER O DAÑAR LAS PIEZAS, EL RETIRO DE LA BASE QUE CONTENGA EL PORFIDO (CAMA DE ARENA Y/O MORTERO DESDE 2cm HASTA 5cm DE ESPESOR,) LIMPIEZAS, Y TODO LO NECESARIO PARA LA CORRECTA EJECUCION DEL CONCEPTO, TRABAJO TERMINADO, NOTA EL MATERIAL RECUPERADO SE DEBERA ENLISTAR EN HOJA MEMBRETADA PARA SU ENTREGA-RECEPCION.	M2	12.39	$74.65	$924.91
4	DEMOLICION MANUAL CON EQUIPO MECANICO (MARTILLO DEMOLEDOR) DE GUARNICION DE CONCRETO SIMPLE DE DIMENSIONES 15X20X40CM O CUALQUIER OTRA SECCION, CON ARMAR O SIN ARMAR, INCLUYE: MANO DE OBRA, HERRAMIENTA NECESARIA PARA SU CORRECTA EJECUCION, EQUIPO DE SEGURIDAD, ACARREOS EN CARRETILLA HACIA LUGAR DE ACOPIO DENTRO DE LA OBRA, LIMPIEZAS, TRABAJO TERMINADO.	M3	5.2	$132.87	$690.92
5	DEMOLICION MANUAL CON EQUIPO MECANICO (MARTILLO DEMOLEDOR) DE TROTAPISTA EXISTENTE HECHA DE PAVIMENTO ASFALTICO, ESPESOR DESDE 5cm HASTA 10cm, INCLUYE: CARGAS Y ACARREO, DENTRO Y FUERA DE LA OBRA DE MATERIAL PRODUCTO DE DEMOLICION, EQUIPO Y HERRAMIENTA, TODO LO NECESARIO PARA LA CORRECTA EJECUCION, LIMPIEZAS, TRABAJO TERMINADO.	M3	6.34	$132.87	$842.40
6	CARGA Y ACARREO EN CAMION DE MATERIAL MIXTO AL PRIMER KILOMETRO, ZONA URBANA, SUBURBANA, TERRACERIAS, ETC. (CARGA MECANICA) MEDIDO COMPACTO, LIMPIEZAS, TRABAJO TERMINADO.	M3	11.53	$36.64	$422.46
7	ACARREO EN CAMION DE MATERIAL MIXTO A KMS. SUBSECUENTES, ZONA SUB-URBANA. ENTREGAR COMPROBANTE DE TIRADERO OFICIAL	M3/KM	345.98	$8.93	$3,089.60
				Totales por Partida	**$9,630.69**

Obra: **REHABILITACIÓN Y CONSTRUCCIÓN DE TROTAPISTA Y MARCADOR ELECTRÓNICO, PARQUE EX-PENSIÓN MUNICIPAL**

Ubicación: **AV. OJOCALIENTE Y AV. SAN GABRIEL, FRACC. OJOCALIENTE II, AGUASCALIENTES Mpio.**

Contratista: **EDIFICACIONES E INSTALACIONES DAP, S. DE R.L. DE C.V. (276)**

No.	Concepto	Unidad	Cantidad	Precio Unitario	Importe Total
	GRUPO: **REHABILITACIÓN Y CONSTRUCCIÓN DE TROTAPISTA Y MARCADOR ELECTRONICO PARQUE EX-PEN**				
	PARTIDA: **PRELIMINARES**				
8	LIMPIA, TRAZO Y NIVELACION DEL TERRENO CON EQUIPO TOPOGRAFICO. INCLUYE: CARGO DIRECTO POR EL COSTO DE MANO DE OBRA Y MATERIALES REQUERIDOS, ACARREOS DENTRO DE LA OBRA (PRIMERA ESTACION), PUENTEO, SEÑALIZACION DEL BANCO Y PUNTOS QUE SE REQUIERAN EN LA NIVELACION CON PINTURA, RENIVELACIONES NECESARIAS, EQUIPO DE SEGURIDAD, HERRAMIENTA Y EQUIPO NECESARIO PARA LA CORRECTA EJECUCION, LIMPIEZAS, TRABAJO TERMINADO. P.U.O.T.	M2	344.21	$12.27	$4,223.46
9	DESPALME DE TERRENO A MAQUINA SECCION MAXIMA DE 15cm EN MATERIAL TIPO I Y II TODAS LAS ZONAS. INCLUYE: CARGO DIRECTO POR EL COSTO DE MANO DE OBRA Y MATERIALES REQUERIDOS, ACARREOS DENTRO DE LA OBRA (PRIMERA ESTACION), AFINE CON MAQUINA, (SE DEBER TENER ESPECIAL CUIDADO DE NO AFECTAR LAS RAICES DE LOS ARBOLES EXISTENTES), PROTECCION PERIMETRAL DE ARBOLES EXISTENTES, EQUIPO DE SEGURIDAD, INSTALACIONES ESPECIFICAS, DEPRECIACION, , HERRAMIENTA Y EQUIPO NECESARIO PARA LA CORRECTA EJECUCION, LIMPIEZAS, TRABAJO TERMINADO. P.U.O.T.	M3	6.92	$23.15	$160.20
10	CORTE POR MEDIOS MECANICOS EN MATERIAL TIPO II EN CAJONES A CIELO ABIERTO DEPOSITANDO EL MATERIAL DONDE LO INDIQUE LA SUPERVISION CON ACARREO LIBRE DE 60 m, MEDIDO EN TERRENO NATURAL (COMPACTO). INCLUYE: CARGO DIRECTO POR EL COSTO DE MANO DE OBRA Y MATERIALES REQUERIDOS, ACARREOS DENTRO DE LA OBRA (PRIMERA ESTACION), AFINE CON MAQUINA, EQUIPO DE SEGURIDAD, INSTALACIONES ESPECIFICAS, DEPRECIACION, ANDAMIOS CONVENCIONALES, HERRAMIENTA Y EQUIPO NECESARIO PARA LA CORRECTA EJECUCION, LIMPIEZAS, TRABAJO TERMINADO. P.U.O.T.	M3	37.51	$40.13	$1,505.28
12	PLATAFORMA CONFORMADA CON MATERIAL DE BANCO (TEPETATE) EN CAPAS DE 20cm. HASTA LLEGAR AL NIVEL DE PLATAFORMA, COMPACTADA CON BAILARINA AL 95% DE SU PVSM,, INCLUYE: CARGO DIRECTO POR EL COSTO DE MANO DE OBRA Y MATERIALES REQUERIDOS, ACARREOS DENTRO DE LA OBRA, MANIOBRAS, AGUA NECESARIA, RIEGOS DE CONSERVACION, EXTENDIDO DE MATERIAL, CONFORMACION, NIVELADO, COMPACTACION DE TEPETATE, EQUIPO DE SEGURIDAD, INSTALACIONES ESPECIFICAS, DEPRECIACION, HERRAMIENTA Y EQUIPO NECESARIO PARA LA CORRECTA EJECUCION, LIMPIEZAS, TRABAJO TERMINADO. P.U.O.T.	M3	12.8	$284.29	$3,638.91
13	CARGA MECANICA Y ACARREO DE MATERIAL PRODUCTO DE LA EXCAVACION Y/O DEMOLICION EN CAMION DE VOLTEO AL 1ER KM, VOLUMEN MEDIDO COMPACTO. INCLUYE: PERMISOS, MAQUINARIA Y EQUIPO, COMBUSTIBLES, OPERADORES, MATERIALES DE CONSUMO, MANO DE OBRA, LIMPIEZAS. TRABAJO TERMINADO.	M3	44.42	$36.64	$1,627.55
14	ACARREO EN CAMION DE MATERIAL MIXTO A KMS. SUBSECUENTES, ZONA SUB-URBANA. ENTREGAR COMPROBANTE DE TIRADERO OFICIAL	M3/KM	1332.71	$8.93	$11,901.10
				Totales por Partida	**$23,056.49**
	PARTIDA: **GUARNICIONES**				
15	LIMPIEZA, TRAZO Y NIVELACION DEL TERRENO CON EQUIPO TOPOGRAFICO, PARA LINEAS ELECTRICAS, HIDRAULICAS, SANITARIAS Y GUARNICIONES, ESTABLECIENDO EJES, REFERENCIAS Y NIVELES, INCLUYE: MATERIALES, MANO DE OBRA, HERRAMIENTA Y EQUIPO NECESARIO. POR UNIDAD DE CONCEPTO TERMINADO.	ML	153.51	$12.27	$1,883.57
16	EXCAVACION A MANO EN CEPA EN TERRENO TIPO "II", DE 0.00 A 1.00 m. DE PROFUNDIDAD, INCLUYE: AFINE DE TALUDES Y FONDO, HERRAMIENTA, MANO DE OBRA Y EQUIPO NECESARIO. POR UNIDAD DE CONCEPTO TERMINADO	M3	15.35	$266.62	$4,092.62

Obra: REHABILITACIÓN Y CONSTRUCCIÓN DE TROTAPISTA Y MARCADOR ELECTRÓNICO, PARQUE EX-PENSIÓN MUNICIPAL

Ubicación: AV. OJOCALIENTE Y AV. SAN GABRIEL, FRACC. OJOCALIENTE II, AGUASCALIENTES Mpio.

Contratista: EDIFICACIONES E INSTALACIONES DAP, S. DE R.L. DE C.V. (276)

No.	Concepto	Unidad	Cantidad	Precio Unitario	Importe Total
GRUPO:	**REHABILITACIÓN Y CONSTRUCCIÓN DE TROTAPISTA Y MARCADOR ELECTRONICO PARQUE EX-PEN**				
PARTIDA:	**GUARNICIONES**				
18	CONSTRUCCION DE GUARNICION TRAPEZOIDAL DE 15x20x40 cm DE CONCRETO HECHO EN OBRA F'c=150 Kg/cm2 TMA 19 mm. ACABADO PULIDO CON DOBLADOR EN FILOS, CURADO CON MEMBRANA BASE AGUA (CURACRETO) APLICADO CON ASPERSOR A RAZON DE 1 lt/m2 CON ESPESOR DE 1 mm, INCLUYE: JUNTA DE PVC 1" @4 m, INCLUYE:MATERIAL, MANO DE OBRA, HERRAMIENTA, EQUIPO, ACARREOS LOCALES, ELEVACIONES A CUALQUIER ALTURA, CIMBRA, DESMOLDANTE, CIMBRADO, COLADO, VIBRADO, DESCIMBRADO, CURADO, ALINEADO, NIVELADO, DESPERDICIOS, LIMPIEZAS Y TODO LO NECESARIO PARA SU CORRECTA EJECUCION. TRABAJO TERMINADO.	ML	153.51	$332.02	$50,968.39
19	RELLENO CON MATERIAL PRODUCTO DE BANCO (TEPETATE) COMPACTADO AL 95% DE SU PVSM CON COMPACTADOR DE IMPACTO (BAILARINA) EN CAPAS DE HASTA 20 cm. DE ESPESOR. INCLUYE: AGUA LA NECESARIA, MEDIDO COMPACTO, SELECCION DEL MATERIAL, TENDIDO, PAPEADO DE MATERIAL, ACARREOS DENTRO DE LA OBRA, LIMPIEZAS.	M3	7.68	$84.52	$649.11
20	CARGA Y ACARREO EN CAMION DE MATERIAL MIXTO AL PRIMER KILOMETRO, ZONA URBANA, SUBURBANA, TERRACERIAS, ETC. (CARGA MECANICA) MEDIDO COMPACTO, LIMPIEZAS, TRABAJO TERMINADO.	M3	15.35	$36.64	$562.42
21	ACARREO EN CAMION DE MATERIAL MIXTO A KMS. SUBSECUENTES, ZONA SUB-URBANA. (ENTREGAR COMPROBANTE DE TIRADERO OFICIAL)	M3/KM	460.53	$8.93	$4,112.53
				Totales por Partida	**$62,268.65**
PARTIDA:	**ACABADOS**				
22	RIEGO DE LIGA CON EMULSION DE ROMPIMIENTO RAPIDO (ECR-65%), INCLUYE: SUMINISTRO, ALMACENAMIENTO, CALENTAMIENTO Y APLICACION DE LA EMULSION CON EQUIPO ESPECIAL PARA ESA ACTIVIDAD, ESPREAS O BACHADOR LIMPIAS Y ALINEADAS, CONTROL DE CALIDAD A CADA DOS REMESAS EN OBRA (INDEPENDIENTEMENTE DE LA CANTIDAD A UTILIZAR) EN LA PETROLIZADORA, A RAZON DE 0.8 lt DE EMULSION POR m2, O LO QUE INDIQUE EL LABORATORIO DE CALIDAD DEL CONTRATISTA, NO SE ACEPTAN ""IMPREGNALIGA"", TRABAJO TERMINADO, P.U.O.T.	M2	189.31	$14.90	$2,820.72
24	CARPETA DE CONCRETO ASFALTICO DE 5 cm DE ESPESOR COMPACTO (NO INCLUYE RIEGO), APLICADA SEGUN ESPECIFICACIONES TECNICAS DEL LABORATORIO DE CONTROL DE CALIDAD DE SOPMA, INCLUYE. TENDIDO, COMPACTADO, DESPERDICIOS, ACARREOS DENTRO DE LA OBRA, LIMPIEZAS.	M2	189.31	$254.95	$48,264.58
25	SUMINISTRO DE TIERRA VEGETAL O DE BARRANCO, UNA CAPA DE 10 cm DE ESPESOR, INCLUYE: MANO DE OBRA Y EQUIPO, CARGA Y ACARREO DENTRO Y FUERA DE LA OBRA, TENDIDO, NIVELADO, EXTENDIDO LIMPIEZAS, Y TODO LO NECESARIO PARA LA CORRECTA EJECUCION DEL CONCEPTO, TRABAJO TERMINADO.	M3	36.86	$313.45	$11,553.77
				Totales por Partida	**$62,639.07**
PARTIDA:	**LIMPIEZA FINAL**				
26	LIMPIEZA GENERAL DE LA OBRA. INCLUYE: ACARREOS DE ESCOMBROS, RETIRO FUERA DE LA OBRA DE LOS MISMOS.	M2	313.79	$19.69	$6,178.52
				Totales por Partida	**$6,178.52**
				Totales por Grupo	**$163,773.42**

Obra: REHABILITACIÓN Y CONSTRUCCIÓN DE TROTAPISTA Y MARCADOR ELECTRÓNICO, PARQUE EX-PENSIÓN MUNICIPAL

Ubicación: AV. OJOCALIENTE Y AV. SAN GABRIEL, FRACC. OJOCALIENTE II, AGUASCALIENTES Mpio.

Contratista: EDIFICACIONES E INSTALACIONES DAP, S. DE R.L. DE C.V. (276)

No.	Concepto	Unidad	Cantidad	Precio Unitario	Importe Total
	GRUPO: **MARCADOR ELECTRONICO CANCHA EX-PENSION MUNICIPAL**				
	PARTIDA: **REGISTROS Y POSTES**				
27	SUMINISTRO Y COLOCACION DE REGISTRO PARA ALUMBRADO MCA. CENTRIFUGADOS MEXICANOS O SIMILAR EN CALIDAD, DE CONCRETO POLIMERICO DE 0.37 x 0.40 MTS, CON TAPA Y CONTRAMARCO DE CONCRETO POLIMERICO, TORNILLOS DE SUJECION GALVANIZADOS, CUERPO DE PVC HIDRAULICO, INCLUYE: TRAZO, CORTE CON DISCO, DEMOLICION DE PAVIMENTO Y/O BANQUETA, EXCAVACION, RELLENO, RETIRO DEL MATERIAL PRODUCTO DE EXCAVACION Y DEMOLICION, MANIOBRA DE MONTAJE, NIVELACION, CORTES DEL REGISTRO CON SACABOCADOS, REPOSICION DE BANQUETAS, PISO Y/O PAVIMENTOS (ACABADO IGUAL AL EXISTENTE)., LIMPIEZA DEL AREA DE TRABAJO, MATERIAL Y MANO DE OBRA, TRABAJO TERMINADO.	PZA	9	$2,269.51	$20,425.59
			Totales por Partida		**$20,425.59**
	PARTIDA: **CONDUCTORES ELECTRICOS**				
28	SUMINISTRO Y COLOCACION DE CABLE UNIPOLAR TIPO XLP DRS, PARA 600 V, DE ALUMINIO, MONOCONDUCTOR CALIBRE 6 AWG MARCA VIAKON, CONDUMEX O SIMILAR EN CALIDAD. INCLUYE: COCAS, PUNTAS, CORTES, DESPERDICIOS, ELEVACIONES A CUALQUIER ALTURA, MATERIALES MISCELANEOS, MEDIDO DE CENTRO DE REGISTRO A CENTRO DE REGISTRO. MATERIAL Y MANO DE OBRA, TRABAJO TERMINADO.	ML	399.84	$111.72	$44,670.13
			Totales por Partida		**$44,670.13**
	PARTIDA: **INTERRUPTORES Y GABINETES**				
35	SUMINISTRO Y COLOCACIÓN DE GABINETE METÁLICO MARCA HIMEL DE 0.60X0.40X0.20 MTS, CAT. CRN-6040200-M, PARA ALOJAR CIRCUITOS DE CONTROL, INCLUYE: 1 METRO DE RIEL DIN, CINTILLOS, BORNES DE CONEXIÓN VIKING 3 PARA CONEXIÓN DE TIERRA Y EMPATES DE CABLES, MONTADA EN EL RIEL DIN CATALOGO 393 96 Y 393 72 MARCA LEGRAND, CINTA DE AISLAR, PEINADO DE CABLES, FIJACIÓNES A POSTE DE ALUMBRADO EXISTENTE, SOPORTERIAS, PIJAS, PRUEBAS, ELEVACIONES A CUALQUIER ALTURA, TODO LO NECESARIO PARA SU CORRECTA COLOCACIÓN, MANO DE OBRA, TRABAJO TERMINADO.	PZA	1	$4,351.47	$4,351.47
38	SUMINISTRO Y COLOCACION DE INTERRUPTOR TERMOMAGNETICO ENCHUFABLE DE 1 POLO, DE 20 AMP, No. DE CATALOGO QO120, PARA TABLERO DE DISTRIBUCION O CENTRO DE CARGA, MCA. SQUARE'D O SIMILAR EN CALIDAD, INCLUYE: CONEXIONES, ACARREOS DENTRO DE LA OBRA, PRUEBAS, ELEVACIONES, CUALQUIER ALTURA Y TODO LO NECESARIO PARA SU CORRECTA COLOCACION, MANO DE OBRA, TRABAJO TERMINADO.	PZA	2	$450.36	$900.72
39	SUMINISTRO Y COLOCACION DE CENTRO DE CARGAS, 2 FASES, 3 HILOS, 20 ESPACIOS, No. DE CATALOGO QO320L125G-S, MARCA SQUARE D, O SIMILAR EN CALIDAD, INCLUYE: FIJACIÓN, NIVELACION, CONEXIONES, ACARREOS DENTRO DE LA OBRA, PRUEBAS, ELEVACIONES, CUALQUIER ALTURA Y TODO LO NECESARIO PARA SU CORRECTA COLOCACION, MANO DE OBRA, TRABAJO TERMINADO.	PZA	1	$2,119.28	$2,119.28
			Totales por Partida		**$7,371.47**

Obra: **REHABILITACIÓN Y CONSTRUCCIÓN DE TROTAPISTA Y MARCADOR ELECTRÓNICO, PARQUE EX-PENSIÓN MUNICIPAL**

Ubicación: **AV. OJOCALIENTE Y AV. SAN GABRIEL, FRACC. OJOCALIENTE II, AGUASCALIENTES Mpio.**

Contratista: **EDIFICACIONES E INSTALACIONES DAP, S. DE R.L. DE C.V. (276)**

No.	Concepto	Unidad	Cantidad	Precio Unitario	Importe Total
	GRUPO: **MARCADOR ELECTRONICO CANCHA EX-PENSION MUNICIPAL**				
	PARTIDA: **CANALIZACION**				
40	SUMINISTRO Y COLOCACION DE TUBO PAD CONDUIT (ROJO) DE 53 MM, (2") DE DIAMETRO EN BANQUETA Y/O EN ARROYO, INCLUYE: COLOCACION Y TENDIDO DE TUBO PAD DE 53 MM (2") CONDUIT (ROJO), GUIADO CON ALAMBRE GALVANIZADO CAL. 16, SEPARADORES PARA TUBERIA PAD A CADA 3 METROS CATALOGO 4W10-1, MANO DE OBRA, LIMPIEZA DE AREA DE TRABAJO, TRABAJO TERMINADO. VER NORMA CFE.	ML	121.08	$70.43	$8,527.66
41	SUMINISTRO Y COLOCACIÓN DE CANALIZACIÓN DE TUBO CONDUIT PARED GRUESA GALVANIZADO DE 25 MM DE DIÁMETRO, INCLUYE: ROSCAS, CURVAS, CONTRAS, MONITORES, COPLES, ABRAZADERAS TIPO OMEGA, FIJACIONES, SOPORTERIAS, ELEVACIONES A CUALQUIER ALTURA, FLETES, ACARREOS, MANO DE OBRA, LIMPIEZA DE ÁREA DE TRABAJO, TRABAJO. TERMINADO.	ML	7.5	$174.46	$1,308.45
42	SUMINISTRO Y COLOCACIÓN DE CAJA REGISTRO (CONDULET) TIPO "LB, LL ó LR" DE 25 MM DE DIÁMETRO, SERIE OVALADA, MARCA CROUSE HINDS DOMEX, PARA ÁREAS NO PELIGROSAS. INCLUYE: TAPA, ELEVACIONES A CUALQUIER ALTURA, FLETES, ACARREOS, MANO DE OBRA, LIMPIEZA DE ÁREA DE TRABAJÓ, TRABAJO TERMINADO.	PZA	1	$265.80	$265.80
43	SUMINISTRO Y COLOCACIÓN DE TUBO CONDUIT TIPO LIQUATITE DE 25 MM, INC: GUÍA DE ALAMBRE GALVANIZADO CAL, 14, FIJACIÓN, TRAZO, CORTES, DESPERDICIOS, PUNTAS, FLETES Y ACARREOS, PINTURA, MIMETIZADO DEL TUBO AL COLOR EXISTENTE, MATERIAL Y MANO DE OBRA, TRABAJO TERMINADO.	ML	1.8	$135.21	$243.38
44	SUMINISTRO Y COLOCACIÓN DE CONECTOR RECTO PARA TUBO LIQUATITE DE 25mm DE DIÁMETRO, INCLUYE: FIJACIÓN, NIVELACIÓN, ACCESORIOS, MATERIALES MISCELÁNEOS, ELEVACIONES CUALQUIER ALTURA, MANO DE OBRA, LIMPIEZA DEL ÁREA DE TRABAJÓ, TRABAJO TERMINADO. VER NORMA CFE.	PZA	6	$97.13	$582.78
			Totales por Partida		**$10,928.07**
	PARTIDA: **SISTEMA DE TIERRA**				
46	SUMINISTRO Y COLOCACION DE TIERRA FISICA FIN DE CIRCUITO, INCLUYE: 1 VARILLA TIPO COPPERWELD O SIMILAR EN CALIDAD DE 16 mm x 3 MTS, 1 CONECTOR PARA VARILLA A CABLE GX2626 MARCA BURNDY O SIMILAR EN CALIDAD, 1.5 MTS DE CABLE DE Cu. CAL. 8 AWG, ACCESORIOS, MATERIALES DE CONSUMO, FIJACIÓN Y HINCADO EN CUALQUIER TIPO DE SUELO, MATERIAL Y MANO DE OBRA, TRABAJO TERMINADO.	LOTE	1	$820.48	$820.48
47	SUMINISTRO Y COLOCACION DE TIERRA FISICA PARA MEDICION, INCLUYE: 1 VARILLA TIPO COPPERWELD O SIMILAR EN CALIDAD DE 16 mm x 3 MTS, 1 CONECTOR PARA VARILLA A CABLE GKP635 MARCA BURNDY O SIMILAR EN CALIDAD, 2 MTS DE CABLE DE Cu. CAL. 8 AWG, 1.5 M DE TUBO CONDUIT PDG DE 16 MM, 1 CONECTOR CONDUIT PDG TIPO AMERICANO, ACCESORIOS, MATERIALES DE CONSUMO, FIJACIÓN Y HINCADO EN CUALQUIER TIPO DE SUELO, MATERIAL Y MANO DE OBRA, TRABAJO TERMINADO.	PZA	1	$904.55	$904.55
			Totales por Partida		**$1,725.03**

Obra: REHABILITACIÓN Y CONSTRUCCIÓN DE TROTAPISTA Y MARCADOR ELECTRÓNICO, PARQUE EX-PENSIÓN MUNICIPAL

Ubicación: AV. OJOCALIENTE Y AV. SAN GABRIEL, FRACC. OJOCALIENTE II, AGUASCALIENTES Mpio.

Contratista: EDIFICACIONES E INSTALACIONES DAP, S. DE R.L. DE C.V. (276)

No.	Concepto	Unidad	Cantidad	Precio Unitario	Importe Total
	GRUPO: **MARCADOR ELECTRONICO CANCHA EX-PENSION MUNICIPAL**				
	PARTIDA: **OBRA CIVIL ALUMBRADO**				
48	EXCAVACION A MANO EN ZANJAS EN MATERIAL TIPO 1, INCLUYE: AFLOJE Y EXTRACCION DEL MATERIAL, AFINE, PARA SU EXTRACCION, CONSERVACION DE LA EXCAVACION, SEÑALAMIENTOS, COLOCACION DE PASOS PEATONALES Y PROTECCION DE LA ZANJA, HERRAMIENTA NECESARIA, Y TODO LO NECESARIO PARA SU CORRECTA EJECUCION, LIMPIEZA, TRABAJO TERMINADO.	M3	9.14	$169.67	$1,550.78
49	EXCAVACION A MAQUINA EN ZANJAS EN MATERIAL TIPO 2 , INCLUYE: AFLOJE Y EXTRACCION DEL MATERIAL, AFINE, TRASPALEO VERTICAL PARA SU EXTRACCION, CONSERVACION DE LA EXCAVACION, SEÑALAMIENTOS, COLOCACION DE PASOS PEATONALES Y PROTECCION DE LA ZANJA, HERRAMIENTA NECESARIA, Y TODO LO NECESARIO PARA SU CORRECTA EJECUCION, LIMPIEZA, TRABAJO TERMINADO.	M3	20.73	$266.62	$5,527.03
51	CARGA Y ACARREO DE MATERIAL PRODUCTO DE EXCAVACION POR MEDIOS MECANICOS EN CAMION DE VOLTEO AL 1 ER KM	M3	29.88	$36.64	$1,094.80
52	ACARREO DE MATERIAL PRODUCTO DE EXCAVACION . KM SUBSECUENTES (20 KM)	M3-KM	896.26	$8.93	$8,003.60
53	ACOSTILLADO CON ARENA Y PISON DE MANO, AL 85% DE SU P.V.S.M. ALREDEDOR DE LA TUBERIA INCLUYE: SUMINISTRO DE MATERIAL EN LA OBRA, ACARREO DESCARGA EN LA ZANJA, EXTENDIDO, NIVELADO Y APISONADO, APOYO SEMICIRCULAR PARA LA TUBERIA , SE CONSTRUIRA INMEDIATAMENTE ANTES DE TENDER LA TUBERIA, DEBIENDO COLOCAR HILOS LONGITUDINALMENTE PARA VERIFICAR LA INIFORMIDAD DE LA PLANTILLA, HERRAMINETA NECESARIA Y TODO LO NECESARIO PARA SU CORRECTA EJECUCION, LIMPIEZA, TRABAJO TERMINADO.	M3	2.18	$800.82	$1,745.79
54	PLANTILLA CON ARENA Y PISON DE MANO, INCLUYE: SUMINISTRO DE MATERIAL DE OBRA, ACARREO DESCARGA EN LA ZANJA, EXTENDIDO, NIVELADO Y APISONADO, APOYO SEMICIRCULAR PARA LA TUBERIA, SE CONSTRUIRA INMEDIATAMENTE ANTES DE TENDER LA TUBERIA, DEBIENDO COLOCAR HILOS LONGITUDINALMENTE PARA VERIFICAR LA UNIFORMIDAD DE LA PLANTILLA, HERRAMIENTA NECESARIA Y TODO LO NECESARIO PARA SU CORRECTA EJECUCION, LIMPIEZA TRABAJO TERMINADO. VER FICHA TECNICA SOPMA	M3	4.98	$800.82	$3,988.08
55	RELLENO Y COMPACTACION CON MATERIAL DE BANCO AL 90% DE SU P.V.S.M., EN CAPAS DE 20 CM DE ESPESOR, CON EQUIPO MECANICO (BAILARINA), INCLUYE: SUMINISTRO, TENDIDO, HOMOGENIZADO, COMPACTADO, VOLUMEN COMPACTO, ACARREOS DENTRO Y FUERA DE LA OBRA, HERRAMIENTA NECESARIA Y TODO LO NECESARIO PARA SU CORRECTA EJECUCION , TRABAJO TERMINADO.	M3	9.96	$305.57	$3,043.48
56	RELLENO Y COMPACTACION CON MATERIAL DE BANCO AL 95% DE SU P.V.S.M., EN CAPAS DE 20 CM DE ESPESOR, CON EQUIPO MECANICO (BAILARINA), INCLUYE: SUMINISTRO, TENDIDO, HOMOGENIZADO, COMPACTADO, VOLUMEN COMPACTO, ACARREOS DENTRO Y FUERA DE LA OBRA, HERRAMIENTA NECESARIA Y TODO LO NECESARIO PARA SU CORRECTA EJECUCION , TRABAJO TERMINADO.	M3	9.96	$314.39	$3,131.32
				Totales por Partida	**$28,084.90**

Obra: REHABILITACIÓN Y CONSTRUCCIÓN DE TROTAPISTA Y MARCADOR ELECTRÓNICO, PARQUE EX-PENSIÓN MUNICIPAL

Ubicación: AV. OJOCALIENTE Y AV. SAN GABRIEL, FRACC. OJOCALIENTE II, AGUASCALIENTES Mpio.

Contratista: EDIFICACIONES E INSTALACIONES DAP, S. DE R.L. DE C.V. (276)

No.	Concepto	Unidad	Cantidad	Precio Unitario	Importe Total
	GRUPO: **MARCADOR ELECTRONICO CANCHA EX-PENSION MUNICIPAL**				
	PARTIDA: **EQUIPOS, MEDICION Y ACCESORIOS**				
57	SUMINISTRO E INSTALACION DE MARCADOR ELECTRONICO PARA CANCHA DE FUTBOL 7, MARCA RG MARCADORES DEPORTIVOS O SIMILAR EN CALIDAD, MEDIDAS DE 120X100CMS, CONEXIÓN ELECTRICA 110 VCA, DIGITOS DE 20CMS. DE ALTURA Y LEGIBILIDAD A 90MTS. CONTEO REGRESIVO Y EN AUMENTO CON DESIMAS DE SEGUNDO EN ULTIMO MINUTO (MODELO DE MANDO INALAMBRICO), INCLUYE: 2 CONTROLES, ROTULOS PINTADOS (NO VINIL NI CALCAS) PARA LARGA DURACION, SEÑAL AUDIBLE DE FINAL DE TIEMPO, PARA USO EN EXTERIORES, CON CARCASA DE ALUMINIO Y FRENTE ACRILICO, INCLUYE FLETES, TRASLADOS, ELEVACIONES A CUALQUIER ALTURA, SOPORTERIAS, ELEMENTOS DE FIJACION, NIVELACION, PROGRAMACIONES, MANO DE OBRA, MATERIALES NECESARIOS PARA SU CORRECTA INSTALACION Y OPERACION, MANO DE OBRA, MANIOBRAS, TRABAJO TERMINADO.	PZA	1	$53,437.73	$53,437.73
58	SUMINISTRO E INSTALACION DE REGULADOR MARCA SOLA BASIC O SIMILAR EN CALIDAD, MEDIDAS DE 17X24X12CMS, CONEXIÓN ELECTRICA 127 VCA, +10%-37%, 60HZ, 2 HILOS + TIERRA FISICA, CORRIENTE MAXIMA 19.50 AMP..CAPACIDAD 2 HP, 1500W, INCLUYE: FLETES, TRASLADOS, ELEVACIONES A CUALQUIER ALTURA, CONEXIONES, RECEPTACULOS, CONECTORES GLANDULA, MANO DE OBRA, MATERIALES NECESARIOS PARA SU CORRECTA INSTALACION Y OPERACION, MANO DE OBRA, MANIOBRAS, TRABAJO TERMINADO.	PZA	1	$3,119.15	$3,119.15
59	SUMINISTRO Y COLOCACION DE BASE DE MEDICION 1 FASE, 2 HILOS, 100 amp, MODELO MS1004J, MARCA SQUARE D. INCLUYE: FIJACION Y NIVELACION DE LA CAJA DE CONEXIONES, ACCESORIOS, MANO DE OBRA, ACARREOS , TRABAJO A CUALQUIER ALTURA, MATERIALES MISCELANEOS, LIMPIEZA DEL AREA DE TRABAJO, TRABAJO TERMINADO.	PZA	1	$1,837.86	$1,837.86
60	REUBICACION DE MEDIDOR DE CFE EXISTENTE A NUEVA PREPARACION, INCLUYE: SISTEMA DE TIERRA FISICA CON VARILLA CPW DE 16MM X 3 MTS, CONECTOR MECANICO REFORZADO, TUBO CONDUIT PDG DE ½", ELEMENTOS DE SOPORTERIA Y FIJACIÒN, CABLE THW COLOR VERDE DE COBRE CALIBRE 8 AWG, DESCONEXION Y RECONEXION DE LA RED DE CFE, CONECTORES, ENCINTADOS, ELEVACIONES A CUALQUIER ALTURA, MANO DE OBRA, TRABAJO TERMINADO.	PZA	1	$3,342.33	$3,342.33

Totales por Partida		**$61,737.07**
Totales por Grupo		**$174,942.25**
Totales Presup.		**$338,715.67**
Anticipo	**+**	**$103,435.53**
Amortizac. Ant.	**-**	**$103,435.53**
SubTotal. Ant.	**=**	**$338,715.68**
IVA	**+**	**$54,194.50**
Total	**=**	**$392,910.18**

H. AYUNTAMIENTO CONSTITUCIONAL DEL MUNICIPIO DE AGUASCALIENTES 2021-2024

PRESUPUESTO MODIFICADO

Aguascalientes


Obra: REHABILITACIÓN Y CONSTRUCCIÓN DE TROTAPISTA Y MARCADOR ELECTRÓNICO, PARQUE EX-PENSIÓN MUNICIPAL

Ubicación: AV. OJOCALIENTE Y AV. SAN GABRIEL, FRACC. OJOCALIENTE II, AGUASCALIENTES Mpio.

Contratista: EDIFICACIONES E INSTALACIONES DAP, S. DE R.L. DE C.V. (276)

Grupo	Partida	Importe
REHABILITACIÓN Y CONSTRUCCIÓN DE TROTAPISTA Y MARCADOR ELECTRONICO PARQUE EX-PEN		
	DEMOLICIONES Y DESMONTAJES	$9,630.69
	PRELIMINARES	$23,056.49
	GUARNICIONES	$62,268.65
	ACABADOS	$62,639.07
	LIMPIEZA FINAL	$6,178.52
	Subtotal por Grupo	**$163,773.42**
MARCADOR ELECTRONICO CANCHA EX-PENSION MUNICIPAL		
	REGISTROS Y POSTES	$20,425.59
	CONDUCTORES ELECTRICOS	$44,670.13
	INTERRUPTORES Y GABINETES	$7,371.47
	CANALIZACION	$10,928.07
	SISTEMA DE TIERRA	$1,725.03
	OBRA CIVIL ALUMBRADO	$28,084.90
	EQUIPOS, MEDICION Y ACCESORIOS	$61,737.07
	Subtotal por Grupo	**$174,942.25**

Totales Presup.		$338,715.67
Anticipo	+	$103,435.53
Amortizac. Ant.	-	$103,435.53
SubTotal. Ant.	=	$338,715.68
IVA	+	$54,194.50
Total	=	$392,910.18

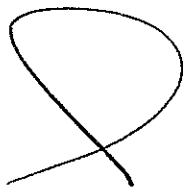


H. AYUNTAMIENTO DE AGUASCALIENTES
SECRETARÍA DE OBRAS PÚBLICAS
DIRECCIÓN DE SUPERVISIÓN DE OBRA


Aguascalientes
LA CIUDAD DE TU VIDA

MEMORIA FOTOGRAFICA


OBRA: REHABILITACIÓN Y CONSTRUCCIÓN DE TROTAPISTA Y MARCADOR ELECTRÓNICO, PARQUE EX-PENSIÓN MUNICIPAL
NO. DE CONTRATO: FISMDF-0071-2022
UBICACIÓN: AV. OJOCALIENTE Y AV. SAN GABRIEL, FRACC. OJOCALIENTE II, AGUASCALIENTES Mpio.
LOCALIDAD: AGS
CONTRATISTA: EDIFICACIONES E INSTALACIONES DAP, S. DE R.L. DE C.V.

INICIO

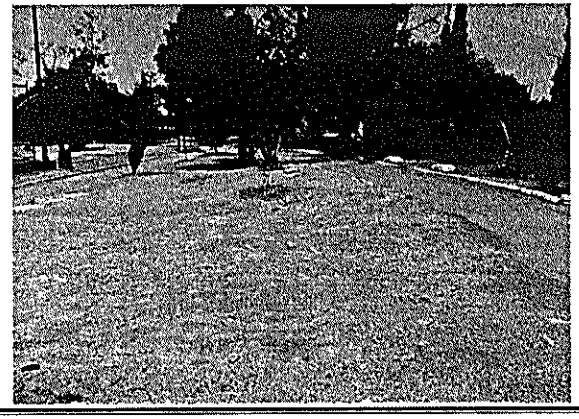

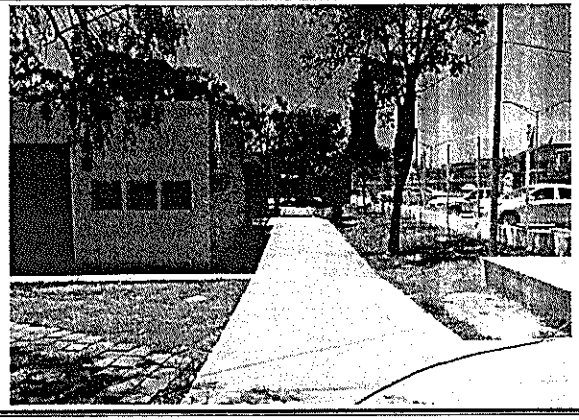



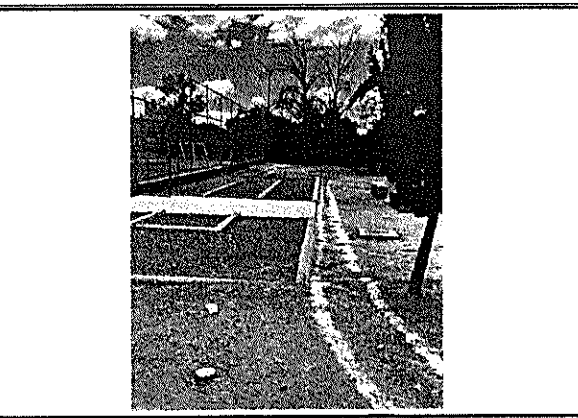

ARQ. ARIADNA MEDINA DOMINGUEZ

H. AYUNTAMIENTO DE AGUASCALIENTES
SECRETARÍA DE OBRAS PÚBLICAS
DIRECCIÓN DE SUPERVISIÓN DE OBRA


Aguascalientes
LA CIUDAD DE TU VIDA


MEMORIA FOTOGRAFICA

OBRA: REHABILITACIÓN Y CONSTRUCCIÓN DE TROTAPISTA Y MARCADOR ELECTRÓNICO, PARQUE EX-PENSIÓN MUNICIPAL
UBICACIÓN: AV. OJOCALIENTE Y AV. SAN GABRIEL, FRACC. OJOCALIENTE II, AGUASCALIENTES Mpio.
CONTRATISTA: EDIFICACIONES E INSTALACIONES DAP, S. DE R.L. DE C.V.

NO. DE CONTRATO: FISMDF-0071-2022
LOCALIDAD: AGS

PROCESO

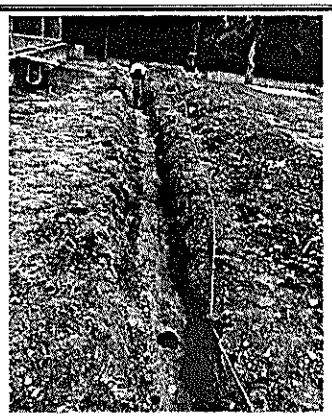

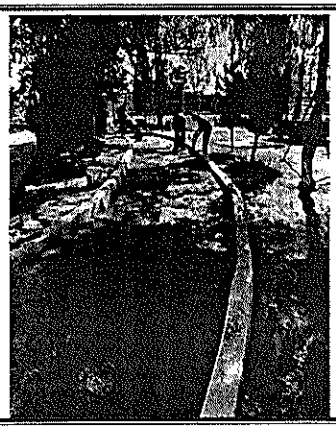





ARQ. ARIADNA MEDINA DOMINGUEZ

H. AYUNTAMIENTO DE AGUASCALIENTES
SECRETARÍA DE OBRAS PÚBLICAS
DIRECCIÓN DE SUPERVISIÓN DE OBRA


Aguascalientes
LA CIUDAD DE TU VIDA


MEMORIA FOTOGRAFICA

OBRA: REHABILITACIÓN Y CONSTRUCCIÓN DE TROTAPISTA Y MARCADOR ELECTRÓNICO, PARQUE EX-PENSIÓN MUNICIPAL
UBICACIÓN: AV. OJOCALIENTE Y AV. SAN GABRIEL, FRACC. OJOCALIENTE II, AGUASCALIENTES Mpio.
CONTRATISTA: EDIFICACIONES E INSTALACIONES DAP, S. DE R.L. DE C.V.


NO. DE CONTRATO: FISMDF-0071-2022
LOCALIDAD: AGS

TERMINO

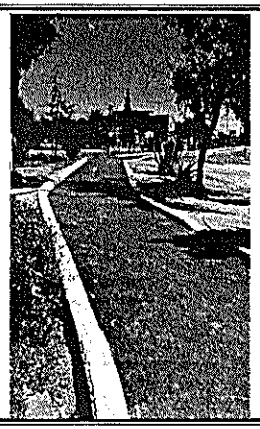

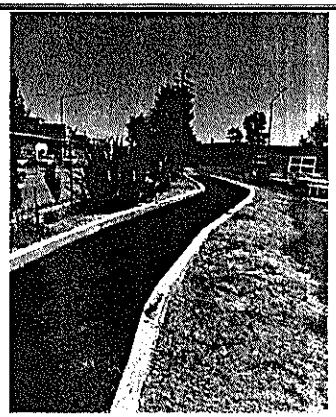



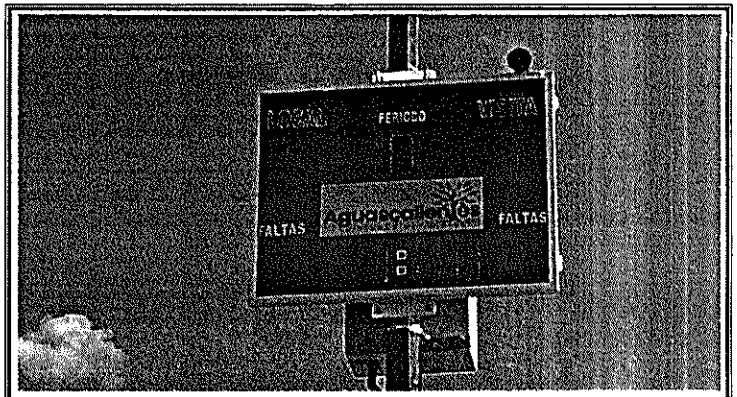

ARQ. ARIADNA MEDINA DOMINGUEZ

MODIFICADO 1

SECRETARÍA DE OBRAS PÚBLICAS

DIRECCIÓN DE SUPERVISIÓN DE OBRA

EJERCICIO 2022

Nº DE CONTRATO: FISMDF-0071-2022


NOMBRE DE LA OBRA: REHABILITACIÓN Y CONSTRUCCIÓN DE TROTAPISTA Y MARCADOR ELECTRÓNICO, PARQUE EX-PENSIÓN MUNICIPAL

MONTO MODIFICADO FINAL: $ 2,699,890.64

VOLUMEN	UNIDAD	COMPONENTE DE LA OBRA	MONTO
2.00	PZA	EXTRACCIÓN CON RECUPERACIÓN DE ARBOL (CUALQUIER ESPECIE) CON UNA ALTURA DE HASTA 5 MTS. DE ALTO Y TRONCON DE ENTRE 30cm. Y 60cm. INCLUYE PODA, EXTRACCION DESDE EL	$ 9,630.69
12.80	M3	PLATAFORMA CONFORMADA CON MATERIAL DE BANCO (TEPETATE) EN CAPAS DE 20cm. HASTA LLEGAR AL NIVEL DE PLATAFORMA, COMPACTADA CON BAILARINA AL 95% DE SU PVSM., INCLUYE	$ 23,056.49
153.51	ML	CONSTRUCCION DE GUARNICION TRAPEZOIDAL DE 15x20x40 cm DE CONCRETO HECHO EN OBRA F'c=150 Kg/cm2 TMA 19 mm. ACABADO RUDO CON DOBLADOR EN FILOS, CURADO CON MEMBRANA BASE	$ 62,268.65
189.31	M2	CARPETA DE CONCRETO ASFALTICO DE 5 cm DE ESPESOR COMPACTO (NO INCLUYE RIEGO), APLICADA SEGUN ESPECIFICACIONES TECNICAS DEL LABORATORIO DE CONTROL DE	$ 62,639.07
313.79	M2	LIMPIEZA GENERAL DE LA OBRA. INCLUYE: ACARREOS DE ESCOMBROS, RETIRO FUERA DE LA OBRA DE LOS MISMOS.	$ 6,178.52
9.00	PZA	SUMINISTRO Y COLOCACION DE REGISTRO PARA ALUMBRADO MCA. CENTRIFUGADOS MEXICANOS O SIMILAR EN CALIDAD, DE CONCRETO POLIMERICO DE 0.37m. 0.40 MTS. CON TAPA Y	$ 20,425.59
399.84	ML	SUMINISTRO Y COLOCACION DE CABLE UNIPOLAR TIPO XLP DRS, PARA 600 V, DE ALUMINIO, MONOCONDUCTOR CALIBRE 6 AWG MARCA VIAKON, CONDUMEX O SIMILAR EN CALIDAD, INCLUYE	$ 44,670.13
1.00	PZA	SUMINISTRO Y COLOCACIÓN DE GABINETE METÁLICO MARCA HIMEL DE 0.60X0.40X0.20 MTS, CAT. CRN 6040200 M, PARA ALOJAR CIRCUITOS DE CONTROL, INCLUYE: 1 METRO DE RIEL DIN, CINTILLOS	$ 7,371.47
121.08	ML	SUMINISTRO Y COLOCACION DE TUBO PAD CONDUIT (ROJO) DE 53 MM, (2") DE DIAMETRO EN BANQUETA Y/O EN ARROYO, INCLUYE: COLOCACION Y TENDIDO DE TUBO, PAD DE 53 MM (2") CONDUIT	$ 10,928.07
1.00	PZA	SUMINISTRO Y COLOCACION DE TIERRA FISICA PARA MEDICION, INCLUYE: 1 VARILLA TIPO COPPERWELD O SIMILAR EN CALIDAD DE 16mm x 2.4 MTS, 1 CONECTOR PARA VARILLA A CABLE CV8C2F MARCA	$ 1,725.03
20.73	M3	EXCAVACION A MAQUINA EN ZANJAS EN MATERIAL TIPO 2 , INCLUYE: AFLOJE Y EXTRACCION DEL MATERIAL, AFINE, TRASPALEO VERTICAL PARA SU EXTRACCION, CONSERVACION DE LA	$ 28,084.90
1.00	PZA	SUMINISTRO E INSTALACION DE MARCADOR ELECTRONICO PARA CANCHA DE FUTBOL 7, MARCA RG MARCADORES DEPORTIVOS O SIMILAR EN CALIDAD, MEDIDAS DE 420X200CMS, CONEXIÓN	$ 61,737.07

TOTAL PRESUP.	$	338,715.67
IVA	$	54,194.51
TOTAL	$	392,910.18

NOMBRE DEL SUPERVISOR: ARQ. ARIADNA MEDINA DOMINGUEZ

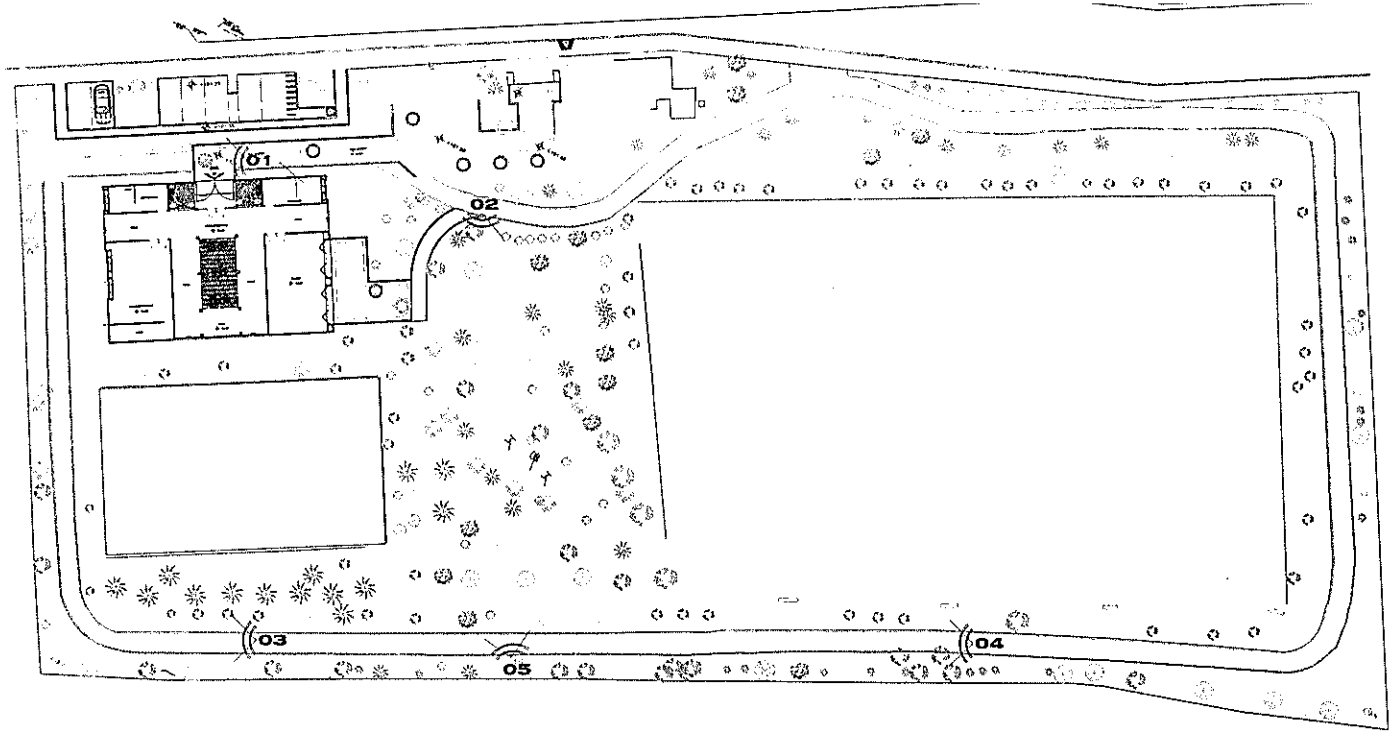

PLANTA ARQUITECTÓNICA DE CONJUNTO ESTADO ACTUAL

 


IMAGEN ESTADO ACTUAL 01



 


IMAGEN ESTADO ACTUAL 02

 

I. EDO. ACTUAL 03

 

I. EDO. ACTUAL 04


 


IMAGEN ESTADO ACTUAL 05

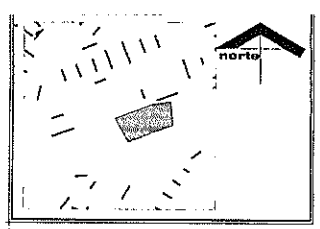

SIMBOLOGIA:

PLANO DEFINITIVO

EDIFICACIONES E INSTALACIONES DAP, S. DE R.L. DE C.V.

Aguascalientes
LA CIUDAD DE TU VIDA

PRESIDENTE MUNICIPAL
Lic. Leonardo Montañez Castro.
SECRETARIO DE OBRAS PUBLICAS
ARQ. GLORIA GUADALUPE CASTILLO GONZALEZ

REV.	FECHA:	OBSERVACIONES:

DIRECCION GENERAL DE PROYECTOS

TITULO: No. PROYECTO 01.2021
REHABILITACIÓN TROTAPISTA CEVIDA PARQUE EX-PENSIÓN MUNICIPAL

CONTENIDO:
ESTADO ACTUAL LEVANTAMIENTO FOTOGRÁFICO

UBICACION:
AV. SAN GABRIEL S/N FRACC. OJOCALIENTE II


CLAVE:
EA-01

ACOTACIONES: CM
ESCALA: 1:200
FECHA: AGOSTO-2022



PLANTA ARQUITECTÓNICA DE ACABADOS

LOCALIZACION:

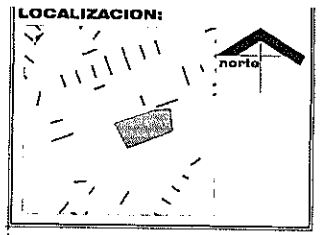

SIMBOLOGIA:

ACABADOS EN PISO

DESPALME DE TERRENO CON MAQUINA, EN CAPAS DE 30 CMS INCLUYE: UN METRO PERIMETRAL PARA PATIO, AFLOJE Y EXTRACCION DEL MATERIAL POR MEDIOS MECANICOS, EQUIPO, TODO LO NECESARIO PARA SU CORRECTA EJECUCION, TRABAJO TERMINADO.

EXCAVACION POR MEDIOS MECANICOS EN MATERIAL TIPO I Y II EN CAJONES A CIELO ABIERTO DEPOSITANDO EL MATERIAL DONDE LO INDIQUE LA SUPERVISION, CON ACARREO LIBRE DE 40 M MEDIDO EN TERRENO NATURAL (COMPACTO) INCLUYE: AFINE CON MAQUINA.

COMPACTACION POR MEDIOS MECANICOS DEL TERRENO NATURAL AL 85% DE SU PVSM EN UN ESPESOR DE 15 cm PARA CAR.NIVEL DE SUBRASANTE INCLUYE: ESCARIFICACION, HUMEDECIDO, NIVELACION, SELECCION DE MATERIAL, ACARREOS DENTRO DE LA OBRA, MEDIDO COMPACTADO, LIMPIEZAS

RELLENO DE TEPETATE COMPACTADO AL 85% DE SU PVSM CON COMPACTADOR DE IMPACTO (BAILARINA) EN CAPAS DE HASTA 20 cm. DE ESPESOR. INCLUYE: SUMINISTRO DE TEPETATE, AGUA LA NECESARIA, MEDIO COMPACTO, SELECCION DEL MATERIAL, TENDIDO, PAPALEO DE MATERIAL, ACARREOS DENTRO DE LA OBRA, LIMPIEZAS

SUMINISTRO Y COLOCACION DE CARPETA ASFÁLTICA EN ESTACIONAMIENTOS Y PATIO DE MANIOBRAS, DE 10 CM DE ESPESOR, APLICADA SEGÚN ESPECIFICACIONES TECNICAS DEL LABORATORIO DE CONTROL DE CALIDAD DE SOPSA.

GUARNICION DE CONCRETO HECHO EN OBRA (REVOLVEDORA DE 1 SACO) f'c= 150 kg/cm2 T.M.A.=3/4" DE 15X 20 X 40 cm, ACABADO PULIDO CON DOBLADOR EN FILOS, CURADO CON MEMBRANA BASE AGUA (EMACRETO) APLICADO CON ASPERSOR A RAZON DE 1LT/m2 CON ESPESOR DE 3mm, INCLUYE: JUNTA DE PVC 1" Ø 1m., MATERIAL BANCO DE OBRA, HERRAMIENTA, EQUIPO, ACARREOS LOCALES, ELEVACIONES A CUALQUIER ALTURA, CIMBRA, DESCIMBRADO, CINCHADO, COLADO, PICADO, DESCIMBRADO, CURADO, DESPERDICIOS, LIMPIEZAS Y TODO LO NECESARIO PARA SU CORRECTA EJECUCION, TRABAJO TERMINADO.

PLANO DEFINITIVO

EDIFICACIONES E INSTALACIONES DAP, S. DE R.L. DE C.V.

DAP

Aguascalientes
LA CIUDAD DE TU VIDA

PRESIDENTE MUNICIPAL
Lic. Leonardo Montañez Castro.
SECRETARIO DE OBRAS PUBLICAS:
ARQ. GLORIA GUADALUPE CASTILLO GONZALEZ

REV	FECHA	OBSERVACIONES:

DIRECCION GENERAL DE PROYECTOS

PROYECTO	REVISO
ARQ. JORGE DIAZ READOS PROYECTISTA	ARQ. FERNANDO J. SOTO G COORDINADOR
ARQ. J. JESUS PRADO G JEFE DE PROYECTOS	ARQ. JOSE LUIS SANCHEZ G DIRECTOR GRAL. DE PROYECTOS

TITULO: No. PROYECTO 01-2007
REHABILITACIÓN TROTAPISTA CEVIDA PARQUE EX-PENSIÓN MUNICIPAL

CONTENIDO:
ACABADOS
PLANTA ARQ. DE ACABADOS

UBICACION:
AV. SAN GABRIEL S/N FRACC. OJOCALIENTE II

No.	FECHA
0	AGOSTO 2007

CLAVE:
ACA-01

FECHA	ESCALA
AGOSTO 2007	1:200
CONTENIDO	CLAVE
PPA	ACA-01



PLANTA ARQUITECTÓNICA DE ACABADOS

SIMBOLOGIA:

ACABADOS EN PISO

PLANO DEFINITIVO

EDIFICACIONES E INSTALACIONES DAP, S. DE R.L. DE C.V.

PRESIDENTE MUNICIPAL:
Lic. Leonardo Montañez Castro.
SECRETARIO DE OBRAS PUBLICAS:
ARQ. GLORIA GUADALUPE CASTILLO GONZALEZ

REV.	FECHA:	OBSERVACIONES:

DIRECCION GENERAL DE PROYECTOS

ARQ. JORGE DIAZ RENDEC PROYECTISTA
ARQ. FERNANDA I. SOTO G. COORDINADOR
ARQ. J. JESUS PALACIOS G. JEFE DE PROYECTOS
ARQ. JOSE LUIS JIMENEZ G. DIRECTOR DE PROYECTOS

TITULO: REHABILITACIÓN TROTAPISTA CEVIDA PARQUE EX-PENSIÓN MUNICIPAL
CONTENIDO: ACABADOS PLANTA ARQ. DE ACABADOS
UBICACION: AV. SAN GABRIEL S/N FRACC. OJOCALIENTE II

AGOSTO 2021
0

CLAVE: ACA-02
AGOSTO 2021
1:200
ACABADOS