Aguascalientes
LA CIUDAD DE TU VIDA

Dirección de Programación Presupuestal
Núm. Oficio AMPP/0451/22
Aguascalientes, Ags. 19 de Octubre del 2022
Asunto: Validación de Expediente Técnico

C.P. SERGIO ARTURO LOZANO GONZÁLEZ
SECRETARIO DE FINANZAS MUNICIPALES
P R E S E N T E

Con fundamento en los artículos 17 fracción XV, 60 fracción XVI y 76 fracción VI del Reglamento del Sistema Integral de Desarrollo Municipal y del Instituto Municipal de Planeación y Evaluación de Aguascalientes, hago referencia al oficio **SOPMA/2260/2022** recibido por este Instituto el día 19 de Octubre del 2022 por parte de la **Secretaría de Obras Públicas**, mediante el cual remiten el expediente técnico original de la siguiente obra para su análisis, registro y priorización, conforme al Programa Anual de Obra Pública y Programas Sociales para el ejercicio presupuestal 2022:

DEPENDENCIA EJECUTORA:	SOPMA
NOMBRE DE LA OBRA O PROYECTO:	SOBRECARPETA ASFÁLTICA
UBICACIÓN:	CALLE ALVARO OBREGÓN, ENTRE CALLE IGNACIO ZARAGOZA Y CALLE GENERAL MIGUEL BARRAGÁN, ZONA CENTRO, AGUASCALIENTES, AGS.
FONDO DE INVERSIÓN:	FONDO DE INFRAESTRUCTURA SOCIAL MUNICIPAL Y DE LAS DEMARCACIONES TERRITORIALES DEL DISTRITO FEDERAL
IMPORTE:	$3,363,306.92 (ET FINAL)
No. DE OBRA:	2022-FISMDF-0049-04-1101
MODALIDAD DE EJECUCIÓN:	CONTRATO
EJE:	MUNICIPIO SOBRESALIENTE
ESTRATEGIA:	OBRA PÚBLICA INTELIGENTE
POLITICA:	5.8.1.REHABILITACIÓN Y MANTENIMIENTO VIALIDADES, CAMINOS, CALLES, ÁREAS DE TERRACERÍA Y CAUCES (COM.

Al respecto, hago de su conocimiento que dicho expediente ha sido analizado en su integración técnica y documental, con base en el artículo 168 fracción I del Reglamento de la Ley de Obras Públicas y Servicios Relacionados para el Estado de Aguascalientes y sus Municipios.

Asimismo, le comento que este Instituto valida dicha obra acorde a lo establecido en los artículos 14, 22 párrafo segundo y 23 de la Ley de Obras Públicas y Servicios Relacionados para el Estado de Aguascalientes y sus Municipios, la cual se encuentra alineada al Plan de Desarrollo Municipal vigente, para dar cumplimiento a las metas establecidas en el mismo, y a los Lineamientos Generales para la Operación de este Fondo de Inversión, toda vez que la misma cuente con la autorización del CODEMUN. De igual manera, se hace de su conocimiento que deberá cumplir con lo establecido en los ordenamientos aplicables en lo que respecta al ejercicio, control e información de los recursos de este Fondo. Cabe hacer mención que los recursos solicitados para este proyecto de inversión, estarán sujetos a la disponibilidad presupuestal para el presente ejercicio fiscal que determine la Secretaría a su digno cargo. Sin otro particular por el momento, le envío un cordial saludo.

A T E N T A M E N T E

DR. RAMÓN RODRIGO RODRÍGUEZ CAMACHO
ENCARGADO DE DESPACHO DE LA DIRECCIÓN GENERAL DEL IMPLAN

CAAR / JDBC
C.c.p. I.C. Arq. Gloria Guadalupe Castillo González .- Secretaría de Obras Públicas .Para su conocimiento.
C.c.p. Archivo.

Instituto Municipal de Planeación y Evaluación de Aguascalientes

Antonio Acevedo Escobedo 103 A. Col. Centro
Aguascalientes. Ags. C.P. 20000

(449) 9101010 Ext. 3117

www.implanags.gob.mx

GOBIERNO MUNICIPAL DE AGUASCALIENTES

INSTITUTO MUNICIPAL DE PLANEACION

IMPLAN

ANÁLISIS INTEGRAL DE EXPEDIENTE TÉCNICO

No. DE OBRA (PAOP 2020):	2022-FISMDF-0049-04-1101	REGISTRO No.	210
OFICIO DE VALIDACIÓN:	AMPP/0451/22	FECHA RECIBIDO PARA REVISIÓN:	19 de Octubre del 2022
PROGRAMA:	URBANIZACION MUNICIPAL	LOCALIDAD O COLONIA:	ZONA CENTRO
SUB-PROGRAMA:	0411- Calles y Caminos	DELEGACIÓN:	Centro Oriente
DEPENDENCIA:	Secretaría de Obras Públicas	MOD. DE EJECUCIÓN:	CONTRATO
NOMBRE DE LA OBRA:	SOBRECARPETA ASFÁLTICA, CALLE ALVARO OBREGÓN, ENTRE CALLE IGNACIO ZARAGOZA Y CALLE GENERAL MIGUEL BARRAGÁN		
FUENTE DE FINANCIAMIENTO:	FONDO DE INFRAESTRUCTURA SOCIAL MUNICIPAL Y DE LAS DEMARCACIONES TERRITORIALES DEL DISTRITO FEDERAL, FISMDF		
INVERSIÓN:	$3,363,306.92	CLASIFICACIÓN DE OBRA:	BIENES DE DOMINIO PUBLICA

TOTAL	FEDERAL	ESTATAL	MUNICIPAL	BENEFICIARIOS	OTROS	DIFERENCIA ENTRE MOD.
$3,363,306.92	$3,363,306.92	0.00	0.00	0.00	0.00	*$136.198,40*

TIPO DE EXPENDIENTE:	ET FINAL	AÑO: 2022	AÑO:	AÑO:		
AVANCES:	Financiero: 5 %	Físico: 5 %				
FECHA DE INICIO:	12 de Julio del 2022	FECHA DE TÉRMINO:	25 de Agosto del 2022	REGISTRO SIMA:	49	

CHEK LIST DE LOS ANEXOS DEL EXPEDIENTE TÉCNICO

CÉDULA DE REGISTRO DE OBRA	✓
DICTAMEN DE FACTIBILIDAD	✓
MEMORIA DESCRIPTIVA	✓
PRESUPUESTO BASE	✓
FACTIBILIDAD VERIFICADA EN CAMPO	✓
CROQUIS DE UBICACIÓN (MACRO)	✓
CROQUIS DE UBICACIÓN (MACRO)	✓
PROGRAMA DE OBRA Y MONTOS MENSUALES	✓
PLANOS O ESTUDIOS TÉCNICOS	✓
PADRÓN DE BENEFICIARIOS	N/A
ACTA DE ACEPTACIÓN DEL PROYECTO	N/A
DICTAMEN DE IMPACTO AMBIENTAL	N/A
CONVENIO DE CONCERTACIÓN	N/A
ACTA CONSTITUTIVA	N/A

METAS		BENEFICIARIOS		PERIODO DE EJECUCION		OBRA PROPUESTA		CLAVE SISCO
UNIDAD DE MEDIDA	CANT	TIPO DE BENEFICIARIOS	CANTIDAD	FECHA DE INICIO	FECHA DE TERMINO	CONCEPTO	JORNALES A GENERAR	
M2	5361.21	Personas	350	2022-07-12	2022-08-25	Sobrecarpeta Asfáltica	8744	2323

INCLUIDO EN PLAN DE DESARROLLO MUNICIPAL Y EL PROGRAMA ANUAL DE OBRA PÚBLICA

OBSERVACIONES:

SIN OBSERVACIONES

RECIBIO: ING. JOSE DAVID BURGUETE CLAUSTRO
Analista de Programación e Inversión de Obra Pública

19 de Octubre del 2022
Fecha de validación

19 de Octubre del 2022
Fecha de validación Expediente

PROCEDE Si ✓ No

H. AYUNTAMIENTO CONSTITUCIONAL DEL MUNICIPIO DE AGUASCALIENTES 2021-2024

AYUNTAMIENTO DE AGUASCALIENTES

CEDULA DE REGISTRO POR OBRA

Aguascalientes

050400-001E00E05-05-2-2-1-00-1-E-0510-0-17-0049-21-2502-6144

2022-FISMDF-0049-0411102-020	Obra **SOBRECARPETA ASFÁLTICA CALLE ALVARO OBREGÓN**
Tipo DEFINITIVO 2 2022 Folio SISCO **2323**	Ubic. TRAMO: ENTRE CALLE IGNACIO ZARAGOZA Y CALLE GRAL. MIGUEL BARRAGÁN, CENTRO Zona , Deleg. Zona Centro

Ent. Ejecutora : **050400001E00E05**

Eje: **05**	MUNICIPIO SOBRESALIENTE
Finalidad: **2**	DESARROLLO SOCIAL
Función: **2**	VIVIENDA Y SERVICIOS A LA COMUNIDAD
Subfunción: **1**	URBANIZACIÓN
Tema: **00**	SIN TEMA
Cuenta del Gasto **1**	GASTO PROGRAMABLE
Clasif. Programatica: **E**	PRESTACIÓN DE SERVICIOS PÚBLICOS
Programa: **0510**	Movilidad Urbana
SubPrograma: **0**	SUBPROGRAMA GENÉRICO
Proyecto: **17**	
Tipo de Gasto: **21**	GASTO INVERSIÓN / OBRA PÚBLICA

I N V E R S I O N 2022

Municipal	2502	FONDO PARA LA INFRAESTRUCTURA SOCIAL MUNICIPAL Y DE LAS DEMARCACIONES TERRITORIALES DEL DISTRITO FEDERAL 2022	$3,363,306.92

Folio SIMA 49 Total $3,363,306.92

M E T A S

Unidad de Medida	Cantidad	Descripción
M2	5361.21	SOBRECARPETA ASFÁLTICA SOBRECARPETA ASFÁLTICA CALLE ALVARO OBREGÓN

Inversión Ejercida Total al 31 de Diciembre de 2021 $0.00

Avance Fisico Acumulado al 31 de Diciembre de 2021

Avance Fisico Acumulado Programado al 31 de Diciembre de 2022 100 %

Fecha de Inicio 12 Jul 2022 Fecha de Terminación 25 Ago 2022

Jornales a Generar en 2022 8744

Modalidad de ejecución CONTRATO

Clasificación de la Obra Bienes de Dominio Público

Registro del Patrimonio: Obras del dominio público

OBRAS PÚBLICAS

Av. Aguascalientes Sur No. 2615
Fracc. Jardines de las Fuentes,
Aguascalientes, Ags. C.P. 20278

(449) 9 78 92 01, 06, 09

www.ags.gob.mx

GENERALES

Nombre del Proyecto : SOBRECARPETA ASFÁLTICA CALLE ALVARO OBREGÓN

TRAMO: ENTRE CALLE IGNACIO ZARAGOZA Y CALLE GRAL. MIGUEL BARRAGÁN, CENTRO Zona , Deleg. Zona Centro

Programa : 04 URBANIZACION MUNICIPAL

Subprograma : 11 Calles y caminos (422.- Rehabilitación: 0411202- Concreto Asfáltico)

Clave del Municipio : AGUASCALIENTES

Localidad :

Barrio, Colonia o Ejido : CENTRO Zona

Tipo de Obra : NUEVA

DESCRIPCIÓN DEL PROYECTO:

SOBRECARPETA ASFÁLTICA CALLE ALVARO OBREGÓN

PRELIMINARES Y DEMOLICIONES 256 M3
SOBRECARPETA ASFÁLTICA 5,361.21 M2
OBRA COMPLEMENTARIA 1.00 OBRA
LIMPIEZAS 5,434.14 M2
GUARNICIONES Y/O DENTELLONES DE CONCRETO 124.15 ML
SEÑALIZACIÓN HORIZONTAL 1.00 OBRA
EXTRAORDINARIO 1.00 OBRA

Beneficiarios (No. y Tipo) :

350	PERSONAS

OBRAS PÚBLICAS

No. Folio SISCO 2323

Los abajo firmantes, hacen constar que el presente proyecto :

SOBRECARPETA ASFÁLTICA CALLE ALVARO OBREGÓN

TRAMO: ENTRE CALLE IGNACIO ZARAGOZA Y CALLE GRAL. MIGUEL BARRAGÁN, CENTRO Zona , Deleg. Zona Centro

cumple con los Requisitos y Normas Técnicas establecidas por la Dependencia Normativa, por lo que es viable su ejecución. Comprometiéndose la misma a proporcionar la supervisión y asistencia técnica necesaria durante el proceso administrativo.

Por la Dependencia Ejecutora

Arq. Gloria Guadalupe Castillo González
Encargada de Despacho de la Secretaría de Obras Públicas

Lic. Jaime Gallo Camacho
Secretario de Desarrollo Urbano

LUGAR :AGUASCALIENTES, AGS.

Av. Aguascalientes Sur No. 2615
Fracc. Jardines de las Fuentes,
Aguascalientes, Ags. C.P. 20278

(449) 9 78 92 01, 06, 09

www.ags.gob.mx

No. Folio SISCO 2323

H. AYUNTAMIENTO CONSTITUCIONAL DEL MUNICIPIO DE AGUASCALIENTES 2021-2024

AYUNTAMIENTO DE AGUASCALIENTES

FACTIBILIDAD VERIFICADA EN CAMPO

Aguascalientes
LA CIUDAD DE TU VIDA

MUNICIPIO: AGUASCALIENTES

LOCALIZACION: TRAMO: ENTRE CALLE IGNACIO ZARAGOZA Y CALLE GRAL. MIGUEL BARRAGÁN, CENTRO Zona , Deleg. Zona Centro

PROGRAMA: URBANIZACION MUNICIPAL

SUBPROGRAMA: Calles y caminos (422.- Rehabilitación: 0411202- Concreto Asfáltico)

OBRA A REALIZAR: SOBRECARPETA ASFÁLTICA CALLE ALVARO OBREGÓN

DEPENDENCIA EJECUTORA: SECRETARÍA DE OBRAS PUBLICAS DEL MUNICIPIO DE AGUASCALIENTES

FORMA DE EJECUCION: CONTRATO

TIPO DE OBRA PROPUESTA: NUEVA

CONDICIONES ACTUALES DE LA OBRA:

SOBRECARPETA ASFÁLTICA CALLE ALVARO OBREGÓN

CARACTERISTICAS DE LA OBRA: Bueno

FACTIBILIDAD DE LA OBRA:

ESTA OBRA SE REQUIERE PARA EL BENEFICIO DE LA CIUDADANÍA

PROCEDE: SI [X] NO [ ]

REVISÓ: Jefa del Departamento de Expedientes Tecnicos y Costos

NOMBRE: Arq. Blanca Margarita Martinez Amador

FIRMA:

FECHA: 03 Oct 2022

SECRETARÍA DE OBRAS PÚBLICAS

Av. Aguascalientes Sur No. 2615
Fracc. Jardines de las Fuentes,
Aguascalientes, Ags. C.P. 20278


(449) 9 78 92 01, 06, 09

www.ags.gob.mx

No. Folio SISCO 2323

H. AYUNTAMIENTO DE AGUASCALIENTES
SECRETARÍA DE OBRAS PÚBLICAS
DIRECCIÓN DE SUPERVISIÓN DE OBRA
LOCALIZACION


OBRA:	SOBRECARPETA ASFÁLTICA CALLE ALVARO OBREGÓN,TRAMO: ENTRE CALLE IGNACIO ZARAGOZA Y CALLE GRAL. MIGUEL BARRAGÁN, CENTRO Zona					
NO. DE CONT	FISMDF-0049-2022		CONTRATISTA:	MAQUINARIA Y CONSTRUCCIONES CAFA S.A. DE C.V.		

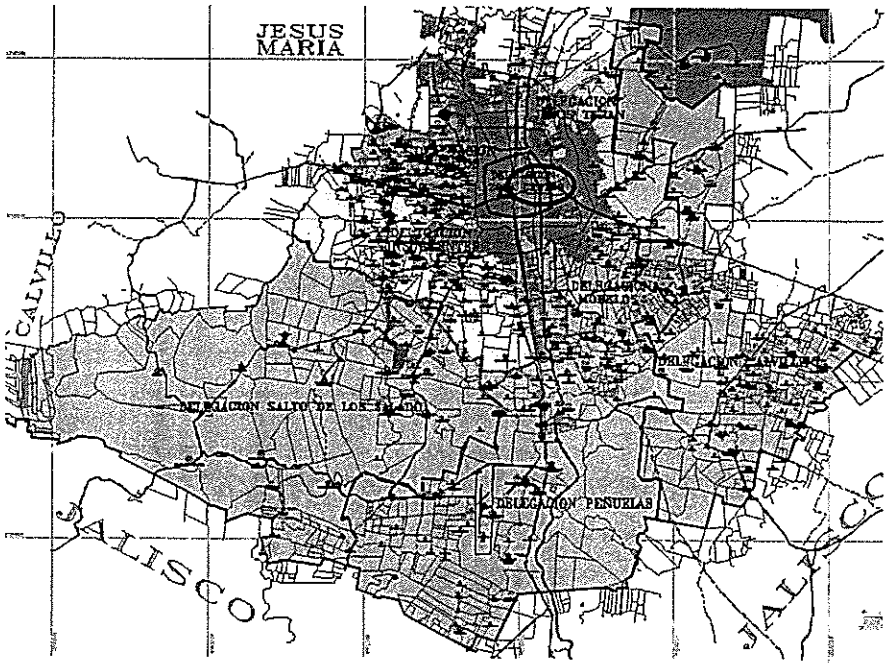

ING. IRENE DUEÑAS FLORES
SUPERVISOR DE OBRA.

H. AYUNTAMIENTO DE AGUASCALIENTES
SECRETARÍA DE OBRAS PÚBLICAS
DIRECCIÓN DE SUPERVISIÓN DE OBRA
LOCALIZACION

OBRA:	SOBRECARPETA ASFÁLTICA CALLE ALVARO OBREGÓN,TRAMO: ENTRE CALLE IGNACIO ZARAGOZA Y CALLE GRAL. MIGUEL BARRAGÁN, CENTRO Zona				
NO. DE CONT	FISMDF-0049-2022		CONTRATISTA:	MAQUINARIA Y CONSTRUCCIONES CA	

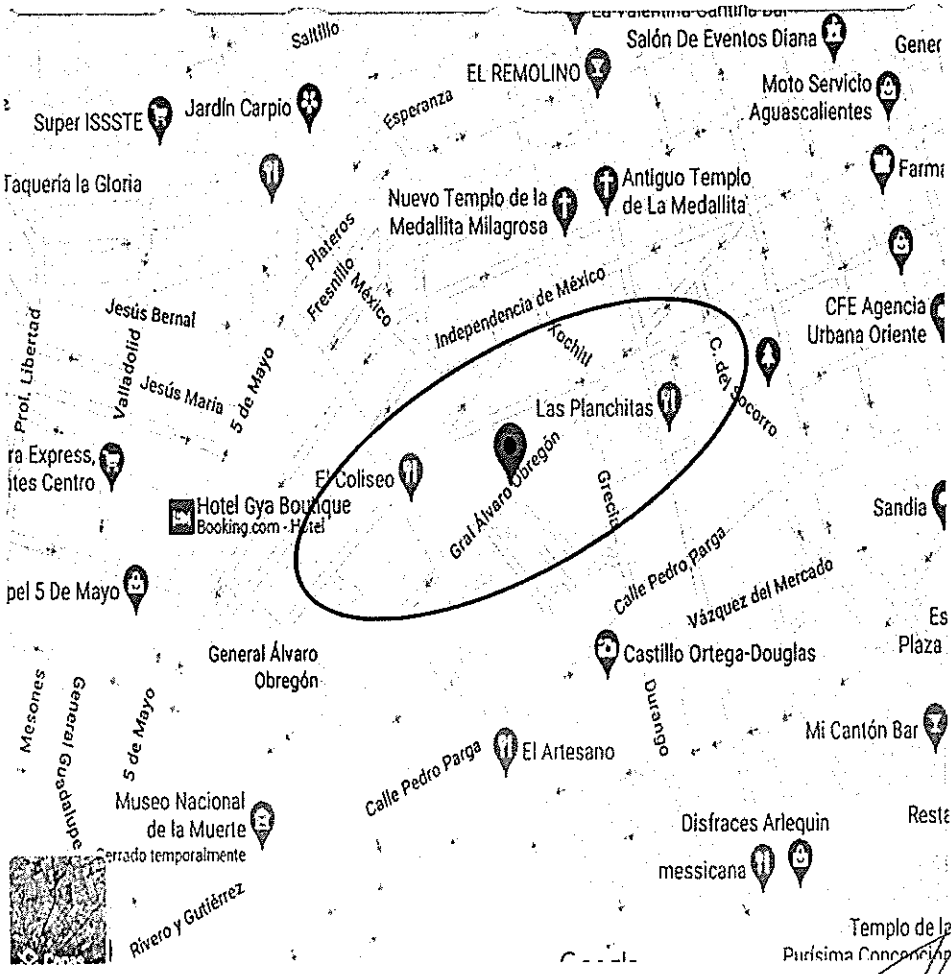

ING. IRENE DUEÑAS FLORES
SUPERVISOR DE OBRA.

RO3-POG-SOS-7.5.1-04	
REVISION:	00
FECHA DE REVISION:	
RESPONSABLE:	SUPERVISOR DE OBRA
TIEMPO DE RET:	02 AÑOS

Aguascalientes
LA CIUDAD DE TU VIDA

PROGRAMA DE OBRA DEFINITIVO

No. DE CONTRATO : FISMDF-0049-2022

PROGRAMA: URBANIZACION MUNICIPAL

INICIO VIC 12 DE JULIO 2022

No. OBRA Y NOMBRE DE LA OBRA: 2022-FISMDF-0049-0411102-020 SOBRECARPETA ASFÁLTICA CALLE ALVARO OBREGÓN,TRAMO; ENTRE CALLE IGNACIO ZARAGOZA Y CALLE GRAL. MIGUEL BARRAGÁN, CENTRO Zona

TERMINO 25 DE AGOSTO 2022

RECURSO 2022

CONCEPTO			1	2	3	4	5	6	7	8	9	10	11	12	13	14	15	16	PONDERACION %	
			2022-2023																	
			ENERO	FEBRERO	MARZO	ABRIL	MAYO	JUNIO	JULIO	AGOSTO	SEPTIEMBRE	OCTUBRE	NOVIEMBRE	DICIEMBRE	ENERO	FEBRERO	MARZO	ABRIL	FINANCIERO	FÍSICO
DESCRIPCION	INVERSION																			
2022-FISMDF-0049-0411102-020 SOBRECARPETA ASFALTICA CALLE ALVARO OBREGON,TRAMO; ENTRE CALLE IGNACIO ZARAGOZA Y CALLE GRAL. MIGUEL BARRAGÁN, CENTRO Zona																				
SOBRECARPETA ASFÁLTICA CALLE ALVARO OBREGÓN																				
PAVIMENTO ASFALTICO																				
PRELIMINARES Y DEMOLICIONES	$	264,117.33							50	50									9.11	20.00
SOBRECARPETA ASFALTICA	$	2,157,942.07								50	50								74.43	13.33
OBRA COMPLEMENTARIA	$	120,827.53								50	50								4.17	13.33
LIMPIEZA	$	37,223.86									50	50							1.28	13.33
GUARNICIONES O DENTELLONES	$	34,506.25								50	50								1.19	13.33
SENALIZACION HORIZONTAL	$	138,075.76									50	50							4.76	13.33
EXTRAODINARIO																				
EXTRAODINARIOS	$	146,709.12								50	50								5.06	13.33
SUBTOTAL SIN IVA	$	2,899,402.52	$ 15.00	1	0	0	0	0	0	0	0	0	0	0	0	0	0	0		
AVANCE SEMANAL %																				
AVANCE SEMANAL ACUMULADO %																			100.00	100.00
EJERCIDO SEMANAL $																			$ 2,899,402.52	
EJERCIDO MENSUAL $			#¡REF!	#¡REF!	#¡REF!	#¡REF!	#¡REF!	#¡REF!	#¡REF!	#¡REF!	#¡REF!	#¡REF!	#¡REF!	#¡REF!	#¡REF!	#¡REF!	#¡REF!	#¡REF!	$ 463,904.40	IVA 16%
EJERCIDO MENSUAL ACUMULADO $			#¡REF!	#¡REF!	#¡REF!	#¡REF!	#¡REF!	#¡REF!	#¡REF!	#¡REF!	#¡REF!	#¡REF!	#¡REF!	#¡REF!	#¡REF!	#¡REF!	#¡REF!	#¡REF!		
EJERCIDO SEMANAL %																			$ 3,363,306.92	
EJERCIDO MENSUAL %			#¡REF!	#¡REF!	#¡REF!	#¡REF!	#¡REF!	#¡REF!	#¡REF!	#¡REF!	#¡REF!	#¡REF!	#¡REF!	#¡REF!	#¡REF!	#¡REF!	#¡REF!	#¡REF!	GRAN TOTRAL EJERCIDO	
EJERCIDO MENSUAL ACUMULADO %			#¡REF!	#¡REF!	#¡REF!	#¡REF!	#¡REF!	#¡REF!	#¡REF!	#¡REF!	#¡REF!	#¡REF!	#¡REF!	#¡REF!	#¡REF!	#¡REF!	#¡REF!	#¡REF!		

$ 15.00

ING. CONSTRUCTOR
SUPERVISOR

PRESIDENCIA MUNICIPAL DE AGUASCALIENTES

FACTIBILIDAD VERIFICADA EN CAMPO

GENERALES

EJERCICIO: 2022 APROBACION No: 2022-FISMDF-0049-0411102-020
LOCALIDAD: SOBRECARPETA ASFÁLTICA CALLE ALVARO OBREGÓN
MUNICIPIO: AGUASCALIENTES, AGS
TIPO DE INVERCION: FONDO PARA LA INFRAESTRUCTURA SOCIAL MUNICIPAL Y DE LAS DEMARCACIONES TERRITORIALES DEL DISTRITO FEDERAL
PROGRAMA: URBANIZACION MUNICIPAL
SUB-PROGRAMA: CALLES Y CAMINOS
OBRA A REALIZARSE: SOBRECARPETA ASFÁLTICA CALLE ALVARO OBREGÓN,TRAMO: ENTRE CALLE IGNACIO ZARAGOZA Y CALLE GRAL. MIGUEL BARRAGÁN, CENTRO Zona

DEPENDENCIA EJECUTORA: SECRETARÍA DE OBRAS PÚBLICAS MUNICIPALES (S.O.P.M.A)
FORMACIÓN DE EJECUCION: CONTRATO NO. DE CONTRATO: FISMDF-0049-2022
NOMBRE CONTRATISTA: MAQUINARIA Y CONSTRUCCIONES CAFA S.A. DE C.V.
REPRESENTANTE:
MONTO CONT. ORIGEN $3,799,506.00 PLAZO 45 DIAS CALENDARIO
MONTO EJERCIDO EN OBRA $3,363,306.92 1 AMPL DIAS
MONTO SOBRANTE EN OBRA 2 AMPL DIAS
FIRMA CONTRATO: 04/07/2022
INICIO CONT: dd/mm/aa 05 DE JULIO 2022 TERMINO CON 18 DE AGOSTO 2022
INICIO REAL: dd/mm/aa 12 DE JULIO 2022 TERMINO REAL 25 DE AGOSTO 2022

TIPO DE OBRA PROPUESTA

NUEVA CREACIÓN	X	CONSOLIDACIÓN	
COMPLEMENTARIA		AMPLIACIÓN	
REHABILITACIÓN		EQUIPAMIENTO	

CARACTERÍSTICAS DE LA OBRA:

SOBRECARPETA ASFÁLTICA CALLE ALVARO OBREGÓN,TRAMO: ENTRE CALLE IGNACIO ZARAGOZA Y CALLE GRAL. MIGUEL BARRAGÁN, CENTRO Zona

CONDICIONES ACTUALES DE LA OBRA: (SELECCIONAR UNO OBLIGATORIO)

BUEN ESTADO X REGULAR PESIMO ESTADO

FACTIBILIDAD DE LA OBRA: (CONDICIONES ACTUALES DE LA OBRA)

LA OBRA SE ENCUENTRA EN BUEN ESTADO PARA USO.

PROCEDE: SI: X NO:
MARQUE SOLO UNA

ING. IRENE DUEÑAS FLORES
SUPERVISOR

PRESIDENCIA MUNICIPAL DE AGUASCALIENTES

FACTIBILIDAD VERIFICADA EN CAMPO

GENERALES

LOCALIDAD: SOBRECARPETA ASFÁLTICA CALLE ALVARO OBREGÓN
MUNICIPIO: AGUASCALIENTES, AGS
PROGRAMA: URBANIZACION MUNICIPAL
SUB-PROGRAMA: CALLES Y CAMINOS
OBRA A REALIZARSE: 2022-FISMDF-0049-0411102-020 SOBRECARPETA ASFÁLTICA CALLE ALVARO OBREGÓN,TRAMO: ENTRE CALLE IGNACIO ZARAGOZA Y CALLE GRAL. MIGUEL BARRAGÁN, CENTRO Zona

DEPENDENCIA EJECUTORA: SECRETARÍA DE OBRAS PÚBLICAS MUNICIPALES (S.O.P.M.A)
FORMACIÓN DE EJECUCION: CONTRATO

TIPO DE OBRA PROPUESTA

NUEVA CREACIÓN	X	CONSOLIDACIÓN	
COMPLEMENTARIA		AMPLIACIÓN	
REHABILITACIÓN		EQUIPAMIENTO	

CARACTERÍSTICAS DE LA OBRA:

SOBRECARPETA ASFÁLTICA CALLE ALVARO OBREGÓN,TRAMO: ENTRE CALLE IGNACIO ZARAGOZA Y CALLE GRAL. MIGUEL BARRAGÁN, CENTRO Zona

CONDICIONES ACTUALES DE LA OBRA:

BUEN ESTADO:	X	REGULAR:		PESIMO ESTADO:	

FACTIBILIDAD DE LA OBRA:

LA OBRA SE ENCUENTRA EN BUEN ESTADO PARA USO.

PROCEDE	**SI:**	X	**NO:**	

ING. IRENE DUEÑAS FLORES
SUPERVISOR

PRESUPUESTO MODIFICADO

Obra: SOBRECARPETA ASFÁLTICA CALLE ALVARO OBREGÓN

Ubicación: TRAMO: ENTRE CALLE IGNACIO ZARAGOZA Y CALLE GRAL. MIGUEL BARRAGÁN, CENTRO Zona

Contratista: MAQUINARIA Y CONSTRUCCIONES CAFA S.A. DE C.V. (014)

Grupo	Partida	Importe
PAVIMENTO ASFALTICO		
	PRELIMINARES Y DEMOLICIONES	$264,117.33
	SOBRE CARPETA ASFALTICA	$2,157,942.67
	OBRA COMPLEMENTARIA	$120,827.53
	LIMPIEZAS	$37,223.86
	GUARNICIONES Y/O DENTELLONES DE CONCRETO	$34,506.25
	SEÑALIZACION HORIZONTAL	$138,075.76
	Subtotal por Grupo	$2,752,693.40
EXTRAORDINARIO		
	EXTRAORDINARIO	-$23,080.86
	EXTRAORDINARIOS	$169,789.98
	Subtotal por Grupo	$146,709.12

Totales Presup.		$2,899,402.52
Anticipo	+	$982,630.86
Amortizac. Ant.	-	$982,630.86
SubTotal. Ant.	=	$2,899,402.52
IVA	+	$463,904.40
Total	=	$3,363,306.92

PRESUPUESTO MODIFICADO

Obra: SOBRECARPETA ASFÁLTICA CALLE ALVARO OBREGÓN

Ubicación: TRAMO: ENTRE CALLE IGNACIO ZARAGOZA Y CALLE GRAL. MIGUEL BARRAGÁN, CENTRO Zona

Contratista: MAQUINARIA Y CONSTRUCCIONES CAFA S.A. DE C.V. (014)

No.	Concepto	Unidad	Cantidad	Precio Unitario	Importe Total
	GRUPO: PAVIMENTO ASFALTICO				
	PARTIDA: PRELIMINARES Y DEMOLICIONES				
	LIMPIA, TRAZO Y NIVELACION EN PAVIMENTOS, CALLES Y VIALIDADES CON EQUIPO TOPOGRAFICO, INCLUYE: EJES, BANCO DE NIVEL, RENIVELACIONES LAS VECES NECESARIAS, CORRECCION DE RASANTE A PUNTOS OBLIGADOS (AUTORIZADOS POR LA SUPERVISION), ESTACAS, VARILLAS, MANO DE OBRA CALIFICADA, HERRAMIENTA NECESARIA, EQUIPO DE PRECISION CALIBRADO, TRABAJO TERMINADO.P.U.O.T.	M2	5434.14	$4.66	$25,323.09
	FRESADO UNIFORME DE LA SUPERFICIE DE RODADURA EN PAVIMENTO DE CONCRETO ASFALTICO 3-7 CM (5 cm de espesor promedio) MEDIANTE FRESADORA EN FRIO COMPACTA, EQUIPADA CON BANDA TRANSPORTADORA PARA CARGA DIRECTA SOBRE CAMION DE VOLTEO, INCLUYE: TRAMO DE PRUEBA AL INICIO DEL FRESADO PARA AUTORIZACION DE SUPERVISION (SUPERFICIE FRESADA UNIFORME Y SIN PROTUBERANCIAS NI ONDEOS), ACARREOS LOCALES, CARGA Y ACARREO A KM SUBSECUENTES (11 A 15 KM APROX) DE MATERIAL PRODUCTO DEL FRESADO DE CARPETA ASFALTICA EL TRASLADO SERA A PARQUE DE MAQUINARIA DE LA SOPMA, PIEZAS DE DESGASTE, COMBUSTIBLES, CONSUMIBLES, MANO DE OBRA, CUALQUIER VOLUMEN Y AREA,EQUIPO NECESARIO, LIMPIEZA FINA Y GRUESA, TRABAJO TERMINADO.	M3	256	$932.79	$238,794.24
				Totales por Partida	**$264,117.33**
	PARTIDA: SOBRE CARPETA ASFALTICA				
2	PREPARACIÓN DE LA SUPERFICIE DE CONTACTO EN LOS EXTREMOS DONDE LA PERFILADORA NO ALCANCE POR LÍMITES CON LA GUARNICIÓN, CON UN RASPADO SUPERFICIAL CON RETROEXCAVADORA, ELIMINANDO TECATAS QUE HAYAN QUEDADO PARA RENIVELADO, BARRIDOS ENTRE PASADA DE MOTOCONFORMADORA Y EN REMATES DE EMPATES A DETALLE A MANO, INCLUYE: RETIRO DE MATERIAL FUERA DE LA OBRA A TIRADERO OFICIAL INDICADO.	M2	174	$30.05	$5,228.70
3	RENIVELACIONES CON CONCRETO ASFALTICO MEZCLA EN PLANTA EN CALIENTE ASFALTO MODIFICADO CON POLIMERO TIPO I, CUMPLIENDO LAS NORMAS SCT REFERENTES DE CONSTRUCCCION Y CONSERVACION, GRANULOMETRIA DENSA 3/4" A FINOS, MEDIDO COMPACTO AL NOVENTA Y CINCO PORCIENTO (95%), INCLUYE CARGA Y ACARREO EN TRAMOS AISLADOS, MATERIALES, MANO DE OBRA, ACARREO DE MATERIALES, Y MAQUINARIA Y EQUIPO AL SIGUIENTE PUNTO EN CUALQUIER VOLUEN, PERFILADO, LIMPIEZA DE HUESO Y GRAVA SUELTA, TRABAJO TERMINADO P.U.O.T	M3	77.36	$6,152.30	$475,941.93
6	RIEGO DE LIGA CON EMULSION DE ROMPIMIENTO RAPIDO (ECR-65 %), INCLUYE, SUMINISTRO, ALMACENAMIENTO, CALENTAMIENTO, Y APLICACION DE LA EMULSION CON EQUIPO ESPECIAL PARA ESA ACTIVIDAD, ESPREAS O BACHADOR LIMPIAS Y ALINEADAS, CONTROL DE CALIDAD A CADA DOS REMESAS EN OBRA (INDEPENDIENTEMENTE DE LA CANTIDAD A UTILIZAR) EN LA PETROLIZADORA, A RAZON DE 0.8 LT DE EMULSION POR M2, O LO QUE INDIQUE EL LABORATORIO DE CALIDAD DEL CONTRATISTA, NO SE ACEPTAN "IMPREGNALIGA", TRABAJO TERMINADO, P.U.O.T.	M2	5361.21	$13.78	$73,877.47

Obra: SOBRECARPETA ASFÁLTICA CALLE ALVARO OBREGÓN

Ubicación: TRAMO: ENTRE CALLE IGNACIO ZARAGOZA Y CALLE GRAL. MIGUEL BARRAGÁN, CENTRO Zona

Contratista: MAQUINARIA Y CONSTRUCCIONES CAFA S.A. DE C.V. (014)

No.	Concepto	Unidad	Cantidad	Precio Unitario	Importe Total
	GRUPO: PAVIMENTO ASFALTICO				
	PARTIDA: SOBRE CARPETA ASFALTICA				
17	SUMINISTRO Y COLOCACION DE CONCRETO ASFALTICO EN CALIENTE DE GRANULOMETRIA DENSA ELABORADA CON ASFALTO MODIFICADO TIPO I, AGREGADO 3/4" A FINOS, DE 5 CM DE ESPESOR, FORMADA Y COMPACTADO AL 95%, INCLUYE MATERIALES, QUE CUMPLAN LA NORMATIVA SCT-N-CMT-04-04, SCT-CMT-4-05-002, SCT-CMT-4-05-003, SCT-CMT-4-05-004, SCT-CTR-CAR-1-04-006-14 APLICADAS AL DIA DE HOY, DISEÑO MARSHALL (DEVERÁ SER AUTORIZADO POR EL LABORATORIO DE CALIDAD DE SOPMA AL MENOS 3 DIAS ANTES DE INICIO DE TENDIDO DE LA MEZCLA ASFALTICA), INCUYE: TRAMO DE PRUEBA AL INICIO PARA REVISION Y AUTORIZACION DEL ESPESOR POR PARTE DEL SUPERVISOR, EL CONTRATISTA DEBERÁ PREVEER EL SUMINISTRO Y TIEMPOS MUERTOS POR MOVIMIENTOS DEL TREN DE MAQUINAS DE TRABAJO EN TRAMOS AISLADOS. TRABAJO TERMINADO P.U.O.T. Y LIMPIEZAS DE GRANZON Y HUESO LATERAL.	M2	5361.21	$298.98	$1,602,894.57
			Totales por Partida		$2,157,942.67
	PARTIDA: OBRA COMPLEMENTARIA				
19	RE NIVELACIÓN DE POZO DE VISITA HASTA 30 cm DE ALTURA. INCLUYE: RETIRO SIN RECUPERACIÓN DE BROCAL EXISTENTE, DEMOLICIONES, NIVELADO CON TABIQUE ROJO RECOCIDO 7X14X28, ASENTADO CON MORTERO CEMENTO-ARENA 1:3 DE 28 cm DE ESPESOR, APLANADO CON MORTERO CEMENTO-ARENA 1:3 , PLOMEADO, NIVELADO, DEMOLICIONES, CARGAS Y ACARREOS DENTRO DE LA OBRA, LIMPIEZAS Y TODO LO NECESARIO PARA SU CORRECTA EJECUCIÓN DEL CONCEPTO.	PZA	7	$2,733.49	$19,134.43
22	RENIVELACIÓN DE RASANTE (PARTE SUPERIOR) DE CAJA DE VÁLVULAS TIPO 2, ó DE HASTA 1.20 X 1. 30 MTS, NIVELADO HASTA UNA ALTURA MAXIMA DE 10 CM, Y MINIMA DE 5 CM. MEDIDAS INTERIORES INCLUYE: TRAZO, EXCAVACIÓN, NIVELACIÓN, PREPARACIONES , Y DEMOLICIONES, RETIRO SIN RECUPERACIÓN DE TAPA DE FOFO EXISTENTE, MURO DE TABIQUE ROJO RECOCIDO COMÚN 7X14X28 CM DE 14 CM DE ESPESOR, JUNTEADO CON MORTERO CEMENTO-ARENA 1:3 APLANADO INTERIOR CON MORTERO CEMENTO ARENA 1:3 DE 2.00 CM DE ESPESOR ACABADO PULIDO, LOSA DE CONCRETO F´C= 250 KG/CM2 T.M.A. 19 MM DE 15 CM DE ESPESOR ARMADA CON VRS No. 3 @15 cm EN AMBOS SENTIDOS, CONTRAMARCO SENCILLO DE CANAL FoFo DE 100 mm, CONTRAMARCO CON TAPA DE FOFO, TIPO PESADO DE 50X50 CM, DEMOLICIÓN Y RECONSTRUCCIÓN DE APROCHES, CARGA Y ACARREOS DENTRO DE LA OBRA, CIMBRADO, DESCIMBRADO, COLADO, VIBRADO, LIMPIEZA PREVIA, FINAL, Y TODO LO NECESARIO PARA LA CORRECTA EJECUCIÓN DEL CONCEPTO.	PZA	2	$15,088.77	$30,177.54
23	RENIVELACIÓN DE RASANTE (PARTE SUPERIOR) DE CAJA DE VÁLVULAS TIPO 3 DE HASTA 1.96 X 1. 75 MTS, NIVELADO HASTA UNA ALTURA MAXIMA DE 10 CM, Y MINIMA DE 5 CM. MEDIDAS INTERIORES INCLUYE: TRAZO, EXCAVACIÓN, NIVELACIÓN, PREPARACIONES , Y DEMOLICIONES, RETIRO SIN RECUPERACIÓN DE TAPA DE FOFO EXISTENTE, MURO DE TABIQUE ROJO RECOCIDO COMÚN 7X14X28 CM DE 14 CM DE ESPESOR, JUNTEADO CON MORTERO CEMENTO-ARENA 1:3 APLANADO INTERIOR CON MORTERO CEMENTO ARENA 1:3 DE 2.00 CM DE ESPESOR ACABADO PULIDO, LOSA DE CONCRETO F´C= 250 KG/CM2 T.M.A. 19 MM DE 15 CM DE ESPESOR ARMADA CON VRS No. 3 @15 cm EN AMBOS SENTIDOS, CONTRAMARCO SENCILLO DE CANAL FoFo DE 100 mm, CONTRAMARCO CON TAPA DE FOFO, TIPO PESADO DE 50X50 CM, DEMOLICIÓN Y RECONSTRUCCIÓN DE APROCHES, CARGA Y ACARREOS DENTRO DE LA OBRA, CIMBRADO, DESCIMBRADO, COLADO, VIBRADO, LIMPIEZA PREVIA, FINAL, Y TODO LO NECESARIO PARA LA CORRECTA EJECUCIÓN DEL CONCEPTO. PZA 2.00	PZA	4	$17,878.89	$71,515.56
			Totales por Partida		$120,827.53

Obra: SOBRECARPETA ASFÁLTICA CALLE ALVARO OBREGÓN

Ubicación: TRAMO: ENTRE CALLE IGNACIO ZARAGOZA Y CALLE GRAL. MIGUEL BARRAGÁN, CENTRO Zona

Contratista: MAQUINARIA Y CONSTRUCCIONES CAFA S.A. DE C.V. (014)

No.	Concepto	Unidad	Cantidad	Precio Unitario	Importe Total
	GRUPO: PAVIMENTO ASFALTICO				
	PARTIDA: LIMPIEZAS				
25	LIMPIEZA GENERAL DE LA OBRA, INCLUYE: BARRIDO, CARGA, ACARREOS Y RETIRO DE ESCOMBROS FUERA DE LA OBRA, TRABAJO TERMINADO.	M2	5434.14	$6.85	$37,223.86
			Totales por Partida		$37,223.86
	PARTIDA: GUARNICIONES Y/O DENTELLONES DE CONCRETO				
28	CONSTRUCCION DE GUARNICION Y/O DENTELLON, RECTA Y/O CURVA TRAPEZOIDAL 15-20X40 CM DE SECCION CON CONCRETO PREMEZCLADO MR=38 KGF/CM2, R.N.REVENIMIENTO DE 8 A 10 CM, T.M.A. 3/4" (19 MM), GRAVA TRITURADA, ACABADO PULIDO EN PARTE DE SUPERIOR Y DOBLADOR EN ARISTAS, INCLUYE: COMPACTADO DE PLANTILLA, CIMBRADO, COLADO, VIBRADO, ACABADO, DESCIMBRADO, ALINEADO, NIVELADO, Y CURADO EN SU PARTE SUPERIOR CON MEMBRANA BASE AGUA A RAZON DE 1 LTO/M2, SEGUN FICHA TECNICA 204	ML	124.15	$277.94	$34,506.25
			Totales por Partida		$34,506.25
	PARTIDA: SEÑALIZACION HORIZONTAL				
32	SUMINISTRO Y APLICACIÓN DE PINTURA EPOXICA BASE SOLVENTE COLOR AZUL (PANTONE 294) EN RAMPAS PARA PERSONAS CON DISCAPACIDAD CUALQUIER SECCIÓN SEGÚN PLANOS. INCLUYE: TRAZO, MANO DE OBRA, LIMPIEZA PREVIA DE SUPERFICIE, EQUIPO NECESARIO PARA SU EJECUCIÓN, Y TODO LO NECESARIO PARA SU CORRECTA EJECUCIÓN, TRABAJO TERMINADO.	M2	20.25	$234.65	$4,751.66
33	SUMINISTRO Y APLICACIÓN DE LOGOTIPO A (SILLA DE RUEDAS) EN PINTURA EPOXICA BASE SOLVENTE COLOR BLANCO EN RAMPAS PARA PERSONAS CON DISCAPACIDAD TAMAÑO Y DISEÑO SEGÚN PLANOS. INCLUYE: TRAZO, ENMASCARILLADO, PLANTILLA, MANO DE OBRA, LIMPIEZA PREVIA DE SUPERFICIE, EQUIPO NECESARIO PARA SU EJECUCIÓN, Y TODO LO NECESARIO PARA SU CORRECTA EJECUCIÓN, TRABAJO TERMINADO.	PZA	9	$322.55	$2,902.95
34	SUMINISTRO Y APLICACIÓN DE PINTURA BASE SOLVENTE PARA MARCAS EN GUARNICIONES CLASIFICACION M-12.1, M12.2 APLICADA SOBRE GUARNICIONES Y DENTELLONES DE CUALQUIER COLOR, SEGÚN SE REQUIERA Y SEGÚN NORMA S.C.T. SECADO AL TACTO EN 5 MIN Y AL DURO EN 30 MIN CON MICRO ESFERA , DESARROLLO DE 35 CM. INCLUYE: MATERIALES Y ESPECIFICACIONES QUE CUMPLAN CON LA NORMATIVA N-CMT-5-01-001/05, N-PRY-CAR-10-01-002/13 APLICADAS AL DIA DE HOY, TRAZO, MANO DE OBRA, LIMPIEZA PREVIA DE SUPERFICIE, EQUIPO NECESARIO PARA SU EJECUCIÓN, Y TODO LO NECESARIO PARA SU CORRECTA EJECUCIÓN, TRABAJO TERMINADO.	ML	938	$68.42	$64,177.96
39	SUMINISTRO Y COLOCACION DE VIALETA STANDARD (S-200) DE 10X10CM. COLOR: CUERPO AMARILLO Y REFLEJANTE AMARILLO 1 CARA MARCA SEA O SIMILAR EN CALIDAD Y ESPECIFICACIONES DE FICHA TECNICA, ANCLADO EN PAVIMENTO SISTEMA DE SUJECION DE ALTO AGARRE BASE CUÑAS CON AB PEGAMENTO EPOXICO 50/50 RESISTENTE A ALTA TEMPERATURA (VER PLANO DE DETALLES DE SEÑALAMIENTOS HORIZONTAL Y VERTICAL). INCLUYE: TRAZO, ALINEACION, ELEVACION CUALQUIER ALTURA, TRABAJO TERMINADO, LIMPIEZAS.	PZA	64	$49.48	$3,166.72

Obra: SOBRECARPETA ASFÁLTICA CALLE ALVARO OBREGÓN

Ubicación: TRAMO: ENTRE CALLE IGNACIO ZARAGOZA Y CALLE GRAL. MIGUEL BARRAGÁN, CENTRO Zona

Contratista: MAQUINARIA Y CONSTRUCCIONES CAFA S.A. DE C.V. (014)

No.	Concepto	Unidad	Cantidad	Precio Unitario	Importe Total
GRUPO: PAVIMENTO ASFALTICO					
PARTIDA: SEÑALIZACION HORIZONTAL					
41	SUMINISTRO Y APLICACIÓN DE PINTURA BASE SOLVENTE PARA AMPLIACIÓN DE BANQUETAS EN ESQUINA CON PINTURA COLOR BLANCO REFLEJANTE CON MICROESFERA SEGÚN NORMA SCT, SEGÚN PROYECTO, DE 40 CM DE ANCHO CON UNA SEPARACIÓN DE 40 CMS. ENTRE ELLAS, SECADO AL TACTO EN 5 MIN Y AL DURO EN 30 MIN. INCLUYE: MATERIAL, Y ESPECIFICACIONES QUE CUMPLAN CON LA NORMATIVA N-CMT-5-01-001/05,N-PRY-CAR-10-01-002/13 APLICADAS AL DIA DE HOY MANO DE OBRA, TRAZO, ENMASCARILLADO, LIMPIEZAS PREVIAS Y POSTERIORES DE LA SUPERFICIE, Y TODO LO NECESARIO PARA SU CORRECTA EJECUCION, TRABAJO TERMINADO.	M2	162.7	$147.33	$23,970.59
44	SUMINISTRO Y COLOCACION DE VIALETA SOLAR DE 10X10CM. COLOR: CUERPO ALUMINIO 3 LED DOS CARAS REFLEJANTES MARCA CREATIVAL VT-29 O SIMILAR EN CALIDAD Y ESPECIFICACIONES DE FICHA TÉCNICA, FIJADO EN PAVIMENTO CON SISTEMA DE SUJECIÓN DE ALTO AGARRE PEGAMENTO EPOXICO 100 A/B (RESINA EPÓXICA/RESINA POLIAMIDA MODIFICADA), RESISTENTE A ALTA TEMPERATURA (VER PLANO DE DETALLES DE SEÑALAMIENTOS HORIZONTAL), INCLUYE: LIMPIEZA PREVIA DE LA SUPERFICIE+C92, PREPARACIÓN DE LA SUPERFICIE, TRAZO, ALINEACIÓN, Y TODO LO NECESARIO PARA SU CORRECTA EJECUCIÓN, TRABAJO TERMINADO.	PZA	62	$630.74	$39,105.88
				Totales por Partida	$138,075.76
				Totales por Grupo	$2,752,693.40

Obra: SOBRECARPETA ASFÁLTICA CALLE ALVARO OBREGÓN

Ubicación: TRAMO: ENTRE CALLE IGNACIO ZARAGOZA Y CALLE GRAL. MIGUEL BARRAGÁN, CENTRO Zona

Contratista: MAQUINARIA Y CONSTRUCCIONES CAFA S.A. DE C.V. (014)

No.	Concepto	Unidad	Cantidad	Precio Unitario	Importe Total
	GRUPO: EXTRAORDINARIO				
	PARTIDA: EXTRAORDINARIO				
49	DEDUCTIVA POR CONCEPTO DE INDIRECTOS NO COMPROBADOS	LOTE	-23.08086	$1,000.00	-$23,080.86
			Totales por Partida		-$23,080.86
	PARTIDA: EXTRAORDINARIOS				
50	SUMINISTRO Y APLICACIÓN DE PINTURA TERMOPLASTICA PARA PARADA DE AUTOBUS COLOR BLANCO, INCLUYE: 3 FLECHAS SIN CUERPO, TEXTO "SOLO BUS", "L" INVERTIDA, ADEMAS DE LINEA DOBLE CON PINTURA ERMOPLASTICA EN COLOR AMARILLO, SEGUN NORMA SICT VIGENTE, TERMINADO REFLEJANTE CON MICROESFERA, LIMPIEZA, TRAZO, MANO DE OBRA, MAQUINARIA Y HERRAMIENTA NECESARIA, TODO LO NECESARIO PARA SU CORRECTA APLICACION.	PZA	1	$9,897.88	$9,897.88
52	SUMINISTRO Y APLICACIÓN DE PINTURA TERMOPLASTICA PARA LINEA DE ALTO DE 60 CM COLOR BLANCO, SEGUN NORMA SICT VIGENTE, TERMINADO REFLEJANTE CON MICROESFERA, LIMPIEZA, TRAZO, MANO DE OBRA, MAQUINARIA Y HERRAMIENTA NECESARIA, TODO LO NECESARIO PARA SU CORRECTA APLICACION.	ML	15.2	$420.45	$6,390.84
53	SUMINISTRO Y APLICACIÓN DE PINTURA TERMOPLASTICA PARA FLECHA DIRECCIONAL DE FRENTE SENCILLA DE 5 M DE LARGO COLOR BLANCO, SEGUN NORMA SICT VIGENTE, TERMINADO REFLEJANTE CON MICROESFERA, LIMPIEZA, TRAZO, MANO DE OBRA, MAQUINARIA Y HERRAMIENTA NECESARIA, TODO LO NECESARIO PARA SU CORRECTA APLICACION.	PZA	7	$889.35	$6,225.45
54	SUMINISTRO Y APLICACIÓN DE PINTURA TERMOPLASTICA PARA FLECHA DIRECCIONAL DOBLE DE 5 M DE LARGO COLOR BLANCO, SEGUN NORMA SICT VIGENTE, TERMINADO REFLEJANTE CON MICROESFERA, LIMPIEZA, TRAZO, MANO DE OBRA, MAQUINARIA Y HERRAMIENTA NECESARIA, TODO LO NECESARIO PARA SU CORRECTA APLICACION.	PZA	3	$1,534.53	$4,603.59
55	CONSTRUCCION DE LOSA DE DIAMANTE DE CONCRETO MR= 45 , T.M.A. DE 3/4" (19MM), GRAVA TRITURADA, REVENIMIENTO DE 8+-2.5CM CM, FRAGUADO RAPIDOA A 3 DIAS, DE 25 CM DE ESPESOR, EN POZO DE VISITA, Y 1.50 M POR LADO, INCLUYE: SUMINISTRO DE MATERIALES, JUNTAS DIAGONALES PARA FORMAR 4 PARTES, BROCAL Y TAPA DE Fo. Fo. TIPO PESADO, (165 KG), CIMBRADO, COLADO, VIBRADO, DESCIMBRADO, CURADO CON MEMBRANA QUIMICA BASE AGUA, APLANADO FINO EN RECEPCION DE BROCAL, CORTES CON CORTADORA DE DISCO DE 5 CM ENTRE JUNTAS DIAGONALES FORMADO 8 PIEZAS Y SELLADO DE JUNTAS Y CORTES CON MATERIAL PREFORMADO Y SELLADOR AUTONIVELANTE, MANO DE OBRA, ACARREOS DE MATERIAL DENTRO Y FUERA DE LA OBRA, TRABAJO TERMINADO. P.U.O.T.	PZA	7	$7,004.83	$49,033.81
56	SUMINISTRO Y APLICACIÓN DE PINTURA TERMOPLASTICA PARA LINEA DOBLE CONTINUA DE 10 CM COLOR BLANCO Y/O AMARILLO, SEGUN NORMA SICT VIGENTE, TERMINADO REFLEJANTE CON MICROESFERA, LIMPIEZA, TRAZO, MANO DE OBRA, MAQUINARIA Y HERRAMIENTA NECESARIA, TODO LO NECESARIO PARA SU CORRECTA APLICACION.	ML	432	$130.49	$56,371.68
57	SUMINISTRO Y APLICACIÓN DE PINTURA TERMOPLASTICA COLOR AMARILLO PARA INDICAR CRUCE PEATONAL DE 40 CM DE ANCHO Y LONGITUD VARIABLE CON UNA SEPARACION DE 0.4 MTS ENTRE ELLAS, SEGUN NORMA SICT VIGENTE, TERMINADO REFLEJANTE CON MICROESFERA, LIMPIEZA, TRAZO, ENMASCARILLADO, MANO DE OBRA, MAQUINARIA Y HERRAMIENTA NECESARIA, TODO LO NECESARIO PARA SU CORRECTA APLICACION.	M2	125.3	$297.42	$37,266.73
			Totales por Partida		$169,789.98
			Totales por Grupo		$146,709.12

PRESUPUESTO MODIFICADO

Obra: SOBRECARPETA ASFÁLTICA CALLE ALVARO OBREGÓN

Ubicación: TRAMO: ENTRE CALLE IGNACIO ZARAGOZA Y CALLE GRAL. MIGUEL BARRAGÁN, CENTRO Zona

Contratista: MAQUINARIA Y CONSTRUCCIONES CAFA S.A. DE C.V. (014)

No.	Concepto	Unidad	Cantidad	Precio Unitario	Importe Total

Totales Presup.		$2,899,402.52
Anticipo	+	$982,630.86
Amortizac. Ant.	-	$982,630.86
SubTotal. Ant.	=	$2,899,402.52
IVA	+	$463,904.40
Total	=	$3,363,306.92

MODIFICADO FINAL

SECRETARÍA DE OBRAS PÚBLICAS

DIRECCIÓN DE SUPERVISIÓN DE OBRAS

EJERCICIO 2022

N° DE **FISMDF-0049-2022**

NOMBRE DE LA **SOBRECARPETA ASFÁLTICA CALLE ALVARO OBREGÓN,TRAMO: ENTRE CALLE IGNACIO ZARAGOZA Y CALLE GRAL. MIGUEL BARRAGÁN, CENTRO**
Zona

MONTO MODIFICADO **$** **3,363,306.92**

VOLUM	UNIDAD	COMPONENTE DE LA OBRA	MONTO
256	M3	FRESADO UNIFORME DE LA SUPERFICIE DE RODADURA EN PAVIMENTO DE CONCRETO ASFALTICO 3-7 CM (5 cm de espesor promedio) MEDIANTE FRESADORA EN FRIO COMPACTA, EQUIPADA CON BANDA TRANSPORTADORA PARA CARGA DIRECTA SOBRE CAMION DE VOLTEO, INCLUYE: TRAMO DE PRUEBA AL INICIO DEL FRESADO PARA AUTORIZACION DE SUPERVISION (SUPERFICIE FRESADA UNIFORME Y SIN PROTUBERANCIAS NI ONDEOS), ACARREOS LOCALES, CARGA Y ACARREO A KM SUBSECUENTES (11 A 15 KM APROX) DE MATERIAL PRODUCTO DEL FRESADO DE CARPETA ASFALTICA	$ 264,117.33
7350.49	M2	SUMINISTRO Y COLOCACION DE CONCRETO ASFALTICO EN CALIENTE DE GRANULOMETRIA DENSA ELABORADA CON ASFALTO MODIFICADO TIPO I, AGREGADO 3/4" A FINOS, DE 5 CM DE ESPESOR, FORMADA Y COMPACTADO AL 95%, INCLUYE MATERIALES, QUE CUMPLAN LA NORMATIVA SCT-N-CMT-04-04, SCT-CMT-4-05-002, SCT-CMT-4-05-003, SCT-CMT-4-05-004, SCT-	$ 2,635,285.19
		TOTAL PRESUP.	$ 2,899,402.52
		IVA	$ 463,904.40
		TOTAL	$ 3,363,306.92

ING. IRENE DUEÑAS FLORES
SUPERVISOR DE OBRA.


H. AYUNTAMIENTO DE AGUASCALIENTES
SECRETARÍA DE OBRAS PÚBLICAS
DIRECCIÓN DE SUPERVISIÓN DE OBRA


Aguascalientes
LA CIUDAD DE TU VIDA

MEMORIA FOTOGRAFICA


OBRA:	2022-FISMDF-0049-0411102-020 SOBRECARPETA ASFÁLTICA CALLE ALVARO OBREGÓN,TRAMO: ENTRE CALLE IGNACIO ZARAGOZA Y CALLE GRAL. MIGUEL BARRAGÁN, CENTRO Zona					
NO. DE CONTRATO:	FISMDF-0049-2022		CONTRATISTA:	MAQUINARIA Y CONSTRUCCIONES CAFA S.A. DE C.V.		

ALBUM INICIO

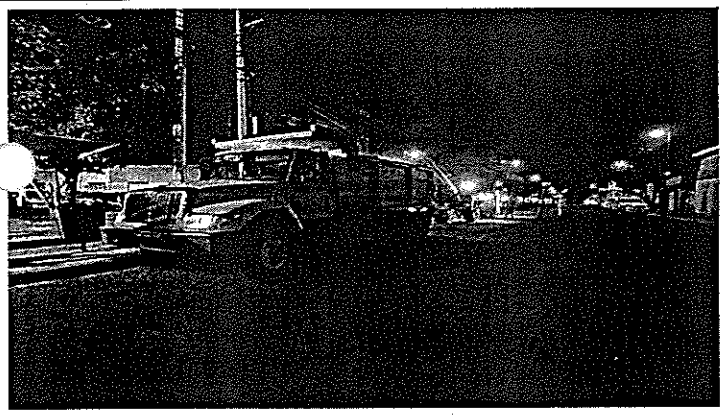

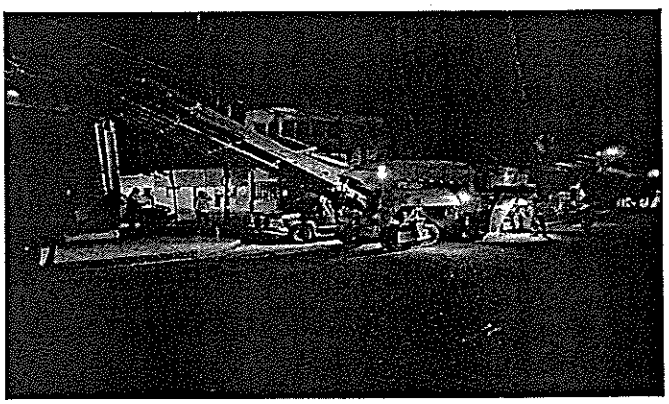



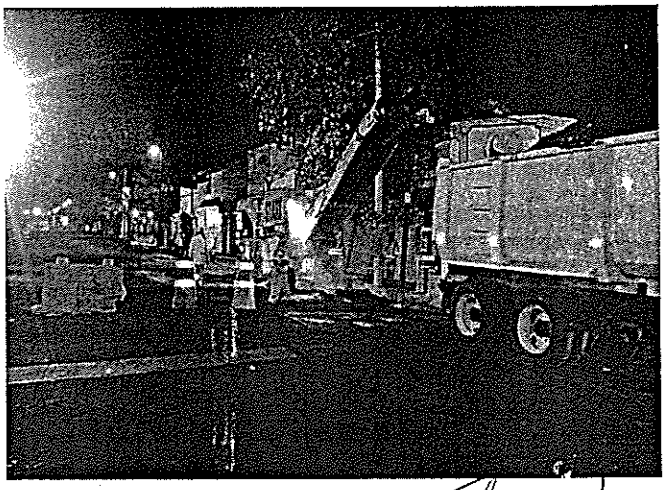

ING. IRENE DUEÑAS FLORES
SUPERVISOR DE OBRA.

H. AYUNTAMIENTO DE AGUASCALIENTES
SECRETARÍA DE OBRAS PÚBLICAS
DIRECCIÓN DE SUPERVISIÓN DE OBRA

Aguascalientes
LA CIUDAD DE TU VIDA


MEMORIA FOTOGRAFICA


OBRA:	2022-FISMDF-0049-0411102-020 SOBRECARPETA ASFÁLTICA CALLE ALVARO OBREGÓN,TRAMO: ENTRE CALLE IGNACIO ZARAGOZA Y CALLE GRAL. MIGUEL BARRAGÁN, CENTRO Zona					
NO. DE CONTRATO:	FISMDF-0049-2022		CONTRATISTA:	MAQUINARIA Y CONSTRUCCIONES CAFA S.A. DE C.V.		

ALBUM PROCESO





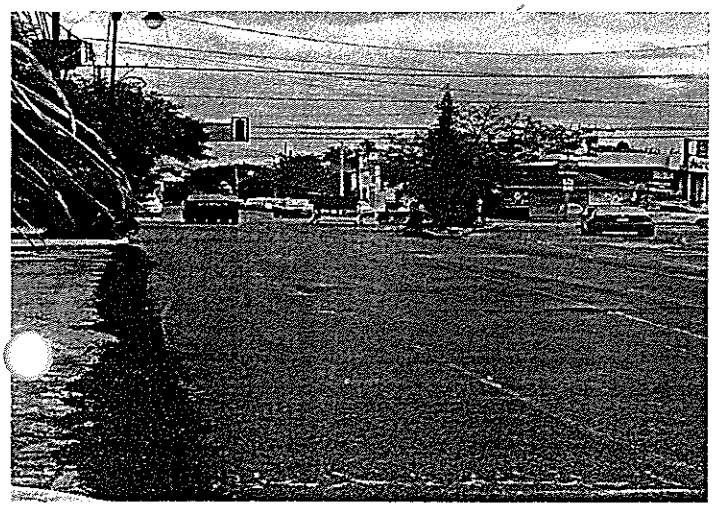

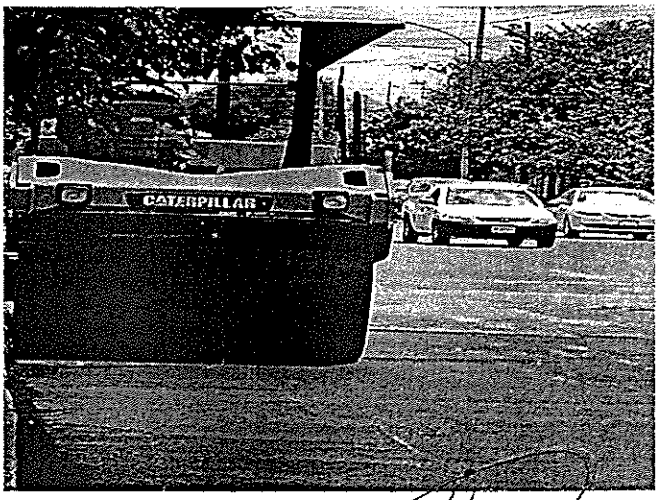

ING. IRENE DUEÑAS FLORES
SUPERVISOR DE OBRA.

H. AYUNTAMIENTO DE AGUASCALIENTES

SECRETARÍA DE OBRAS PÚBLICAS


DIRECCIÓN DE SUPERVISIÓN DE OBRA


Aguascalientes
LA CIUDAD DE TU VIDA

MEMORIA FOTOGRAFICA


OBRA:	2022-FISMDF-0049-0411102-020 SOBRECARPETA ASFÁLTICA CALLE ALVARO OBREGÓN,TRAMO: ENTRE CALLE IGNACIO ZARAGOZA Y CALLE GRAL. MIGUEL BARRAGÁN, CENTRO Zona					
NO. DE CONTRATO:	FISMDF-0049-2022		CONTRATISTA:	MAQUINARIA Y CONSTRUCCIONES CAFA S.A. DE C.V.		

ALBUM TERMINO

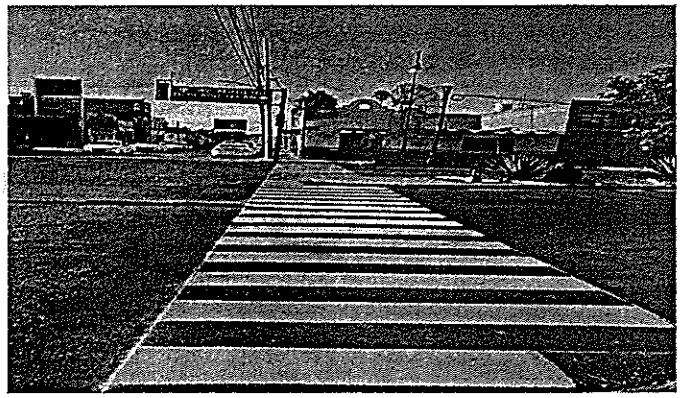

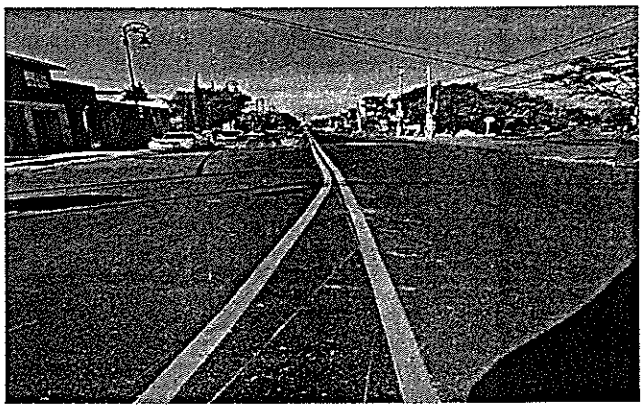




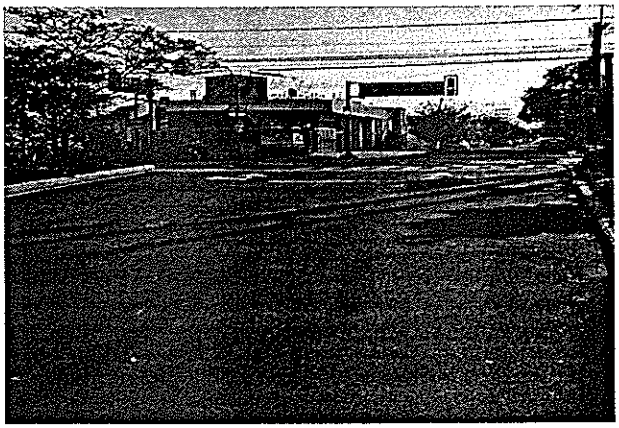

ING. IRENE DUEÑAS FLORES
SUPERVISOR DE OBRA

CONSTRUCCION DE SOBRECARPETA ASFÁLTICA CALLE ALVARO OBREGON , TRAMO ENTRE CALLE IGNACIO ZARAGOZA Y CALLE GRAL. MIGUEL BARRAGAN, CENTRO DELEGACION, ZONA CENTRO.


LOCALIZACION

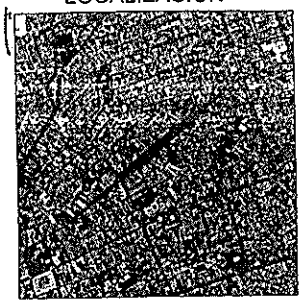

SUMINISTRO Y COLOCACION DE CONCRETO ASFALTICO EN CALIENTE DE GRANULOMETRIA DENSA ELABORADA CON ASFALTO MODIFICADO TIPO I, AGREGADO 3/4" A FINOS, DE 5 CM DE ESPESOR, FORMADA Y COMPACTADO AL 95%, INCLUYE MATERIALES, QUE CUMPLAN LA NORMATIVA SCT-N-CMT-04-04, SCT-CMT-4-05-002, SCT-CMT-4-05-003, SCT-CMT-4-05-004, SCT-CTR-CAR-1-04-006-14 APLICADAS AL DIA DE HOY, DISEÑO MARSHALL (DEVERÁ SER AUTORIZADO POR EL LABORATORIO DE CALIDAD DE SOPMA AL MENOS 3 DIAS ANTES DE INICIO DE TENDIDO DE LA MEZCLA ASFALTICA), INCUYE: TRAMO DE PRUEBA AL INICIO PARA REVISION Y AUTORIZACION DEL ESPESOR POR PARTE DEL SUPERVISOR, EL CONTRATISTA DEBERÁ PREVEER EL SUMINISTRO Y TIEMPOS MUERTOS POR MOVIMIENTOS DEL TREN DE MAQUINAS DE TRABAJO EN TRAMOS AISLADOS. TRABAJO TERMINADO P.U.O.T. Y LIMPIEZAS DE GRANZON Y HUESO LATERAL.

C. ZARAGOZA

C. GENERAL BARRAGAN

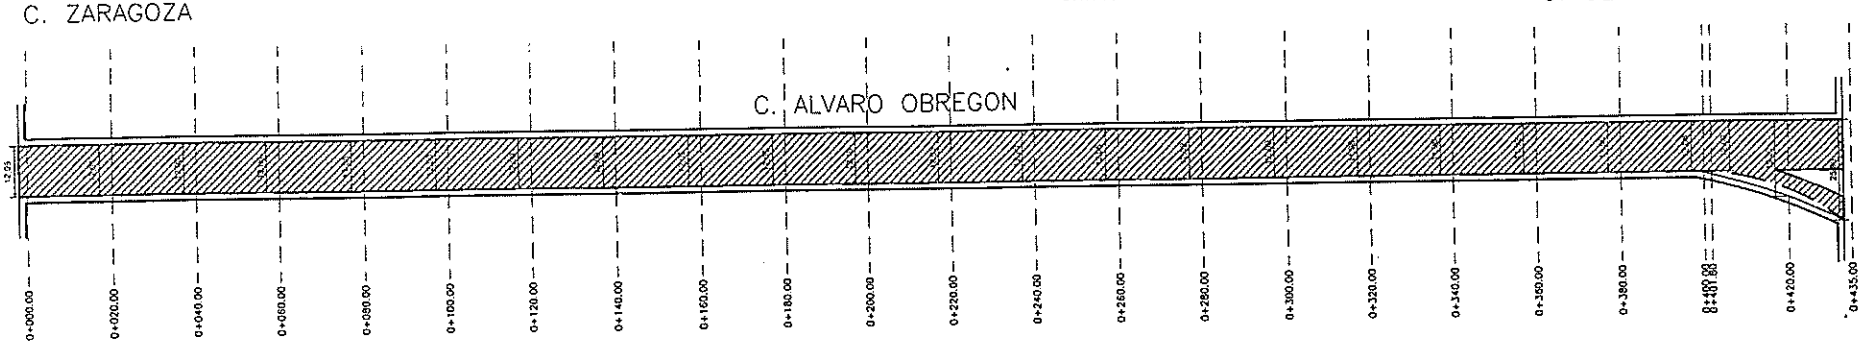

PLANO DEFINITIVO

ESCALA 1:500.

Aguascalientes
LA CIUDAD DE TU VIDA

PROYECTO / OBRA: CONSTRUCCION DE SOBRECARPETA ASFALTICA CALLE ALVARO OBREGON , TRAMO ENTRE CALLE IGNACIO ZARAGOZA Y CALLE GRAL. MIGUEL BARRAGAN, CENTRO DELEGACION, ZONA CENTRO.	Contratista: MAQUINARIA Y CONSTRUCCIONES CAFA S.A. DE C.V.	proyecto: CONSTRUCCION DE SOBRECARPETA ASFÁLTICA CALLE ALVARO OBREGON , TRAMO ENTRE CALLE IGNACIO ZARAGOZA Y CALLE GRAL. MIGUEL BARRAGAN, CENTRO DELEGACION, ZONA CENTRO.	Ubicación: CALLE ALVARO OBREGON , TRAMO ENTRE CALLE IGNACIO ZARAGOZA Y CALLE GENERAL MIGUEL BARRAGAN, CENTRO DELEGACION, ZONA CENTRO
Subrubro de Obra: Ing. IRENE DUEÑAS FLORES.	Contrato No.: FISMDF-0049-2022.	contenido: SUMINISTRO Y COLOCACION DE CONCRETO ASFALTICO EN CALIENTE DE GRANULOMETRIA DENSA ELABORADA CON ASFALTO MODIFICADO TIPO I, AGREGADO 3/4" A FINOS, DE 5 CM DE ESPESOR, FORMADA Y COMPACTADO AL 95%	Constructora: CAFA S.A. de C.V.
Responsable Constructora: Ing. SALVADOR TREJO. / CAFA S.A. DE C.V.	diseño / revisó / autorizó		Grupo CAFA, Blvd. Aeropuerto Km. 9, Col. Trojes 2da Sección, C.P. 20349, Aguascalientes, Ags. Tel. (449) 9229222, Fax (449) 922 92 29 www.cafa.com.mx

CLAVE: **GEN-A03**

fecha: JULIO / 2022.	escala: INDICADA
coordenadas: MTS.	cotas: MTS.

CONSTRUCCION DE SOBRECARPETA ASFÁLTICA CALLE ALVARO OBREGON , TRAMO ENTRE CALLE IGNACIO ZARAGOZA Y CALLE GRAL. MIGUEL BARRAGAN, CENTRO DELEGACION, ZONA CENTRO.


LOCALIZACION



RIEGO DE LIGA CON EMULSION DE ROMPIMIENTO RAPIDO ECR-65 %), INCLUYE, SUMINISTRO, ALMACENAMIENTO, CALENTAMIENTO, Y APLICACION DE LA EMULSION CON EQUIPO ESPECIAL PARA ESA ACTIVIDAD, ESPREAS O BACHADOR LIMPIAS Y ALINEADAS, CONTROL DE CALIDAD A CADA DOS REMESAS EN OBRA(INDEPENDIENTEMENTE DE LA CANTIDAD A UTILIZAR) EN LA PETROLIZADORA, A RAZON DE 0.8 LT DE EMULSION POR M2, O LO QUE INDIQUE EL LABORATORIO DE CALIDAD DEL CONTRATISTA, NO SEACEPTAN "IMPREGNALIGA", TRABAJO TERMINADO, P . U . O . T .

C. ZARAGOZA

C. GENERAL BARRAGAN

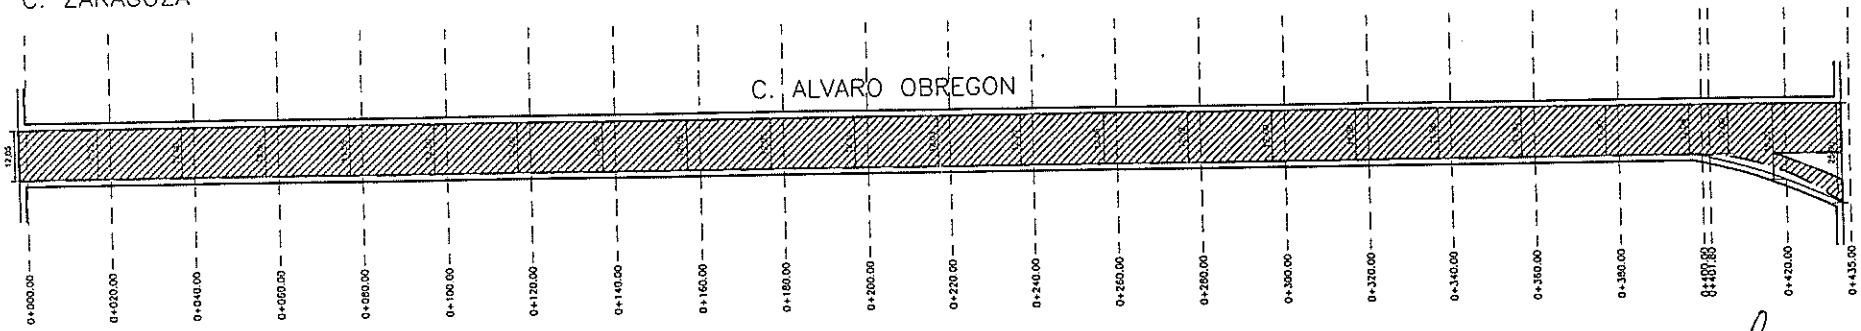

PLANO DEFINITIVO

ESCALA 1:500.

Aguascalientes
LA CIUDAD DE TU VIDA

PROYECTO / OBRA: CONSTRUCCION DE SOBRECARPETA ASFALTICA CALLE ALVARO OBREGON , TRAMO ENTRE CALLE IGNACIO ZARAGOZA Y CALLE GRAL. MIGUEL BARRAGAN, CENTRO DELEGACION, ZONA CENTRO.	Contratista: MAQUINARIA Y CONSTRUCCIONES CAFA S.A. DE C.V.	Proyecto: CONSTRUCCION DE SOBRECARPETA ASFALTICA CALLE ALVARO OBREGON , TRAMO ENTRE CALLE IGNACIO ZARAGOZA Y CALLE GRAL. MIGUEL BARRAGAN, CENTRO DELEGACION, ZONA CENTRO.
Ubicación: CALLE ALVARO OBREGON , TRAMO ENTRE CALLE IGNACIO ZARAGOZA Y CALLE GENERAL MIGUEL BARRAGAN, CENTRO DELEGACION, ZONA CENTRO.	Convenio: FISMDF-0049-2022.	Contenido: RIEGO DE LIGA CON EMULSION DE ROMPIMIENTO RAPIDO ECR-65 %).
Supervisor de Obra: Ing. IRENE DUEÑAS FLORES.	ANEXO / REVISO / AUTORIZO	Revisión No. / Anexo:
Responsable Constructor: Ing. SALVADOR TREJO. / CAFA S.A. DE C.V.		

Elaboró: Maquinaria y Construcciones CAFA S.A. de C.V.


Dependencia: Grupo CAFA, Blvd. Aguascalientes Sur, Km. 9, Col. Trojes de Alonso, C.P. 20116, Aguascalientes, Ags., Tel. (449) 922 50 29, 9229222, Fax. (449) 922 50 29, www.cafa.com.mx

CLAVE: GEN-A02

Fecha: JULIO / 2022.	Escala: INDICADA.
Dimensiones: MTS.	Origen: NEM.

CONSTRUCCION DE SOBRECARPETA ASFÁLTICA CA[illegible] ALVARO OBREGON , TRAMO ENTRE CALLE IGNACIO ZARAGOZA Y CALLE GRAL. MIGUEL BARRAGAN, CENTRO DELEGACION, ZONA CENTRO.


LOCALIZACION

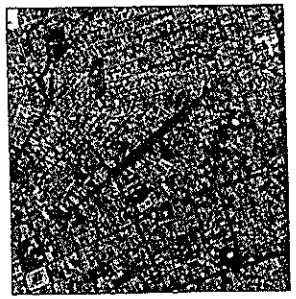

LIMPIA, TRAZO Y NIVELACION EN PAVIMENTOS, CALLES Y VIALIDADES CON EQUIPO TOPOGRAFICO, INCLUYE: EJES, BANCO DE NIVEL, RENIVELACIONES LAS VECES NECESARIAS, CORRECCION DE RASANTE A PUNTOS OBLIGADOS (AUTORIZADOS POR LA SUPERVISION), ESTACAS, VARILLAS, MANO DE OBRA CALIFICADA, HERRAMIENTA NECESARIA, EQUIPO DE PRECISION CALIBRADO, TRABAJO TERMINADO.P.U.O.T.

C. ZARAGOZA

C. GENERAL BARRAGAN

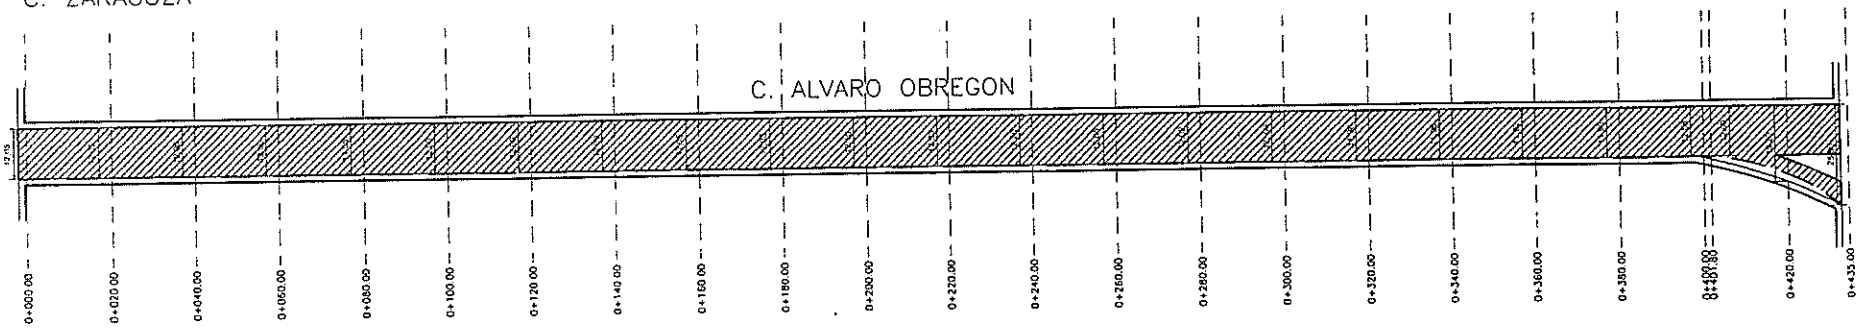

PLANO DEFINITIVO

ESCALA 1:500.

Aguascalientes
LA CIUDAD DE TU VIDA

• PROYECTO • OBRA: CONSTRUCCION DE SOBRECARPETA ASFÁLTICA CALLE ALVARO OBREGON , TRAMO ENTRE CALLE IGNACIO ZARAGOZA Y CALLE GRAL. MIGUEL BARRAGAN, CENTRO DELEGACION, ZONA CENTRO.	• Contratista: MAQUINARIA Y CONSTRUCCIONES CAFA S.A. DE C.V.	• proyecto: CONSTRUCCION DE SOBRECARPETA ASFALTICA CALLE ALVARO OBREGON , TRAMO ENTRE CALLE IGNACIO ZARAGOZA Y CALLE GRAL. MIGUEL BARRAGAN, CENTRO DELEGACION, ZONA CENTRO.	• Elaboró: CAFA Maquinaria y Construcciones CAFA S.A. de C.V.
• Ubicación: CALLE ALVARO OBREGON , TRAMO ENTRE CALLE IGNACIO ZARAGOZA Y CALLE GENERAL MIGUEL BARRAGAN, CENTRO DELEGACION, ZONA CENTRO.	• Contrato: FISMDF-0049-2022.	• contenido: • LIMPIA, TRAZO Y NIVELACION EN PAVIMENTOS, CALLES Y VIALIDADES CON EQUIPO TOPOGRAFICO.	• Organización: Grupo CAFA, Blvd. Ags - Zac. km. 9, Col. Tres de Alonso, C.P. 20116, Aguascalientes, Ags., Tel. (449) 922 02 22, Fax. (449) 922 92 29 www.cafa.com.mx
• Supervisor de Obra: Ing. IRENE DUEÑAS FLORES.	• Localidad: • MUNICIPIO: • ESTADO:	• Revisión No.: • Fecha:	CLAVE: GEN-A01
• Responsable Complementario: Ing. SALVADOR TREJO. / CAFA S.A. DE C.V.			• fecha: JULIO / 2022. • escala: INDICADA
			• acotaciones: MTS. • cliente: NEM.