Aguascalientes
LA CIUDAD DE TU VIDA

Dirección de Programación Presupuestal
Núm. Oficio AMPP/0575/22
Aguascalientes, Ags. 8 de Diciembre del 2022
Asunto: Validación de Expediente Técnico

C.P. SERGIO ARTURO LOZANO GONZÁLEZ
SECRETARIO DE FINANZAS MUNICIPALES
P R E S E N T E

Con fundamento en los artículos 17 fracción XV, 60 fracción XVI y 76 fracción VI del Reglamento del Sistema Integral de Desarrollo Municipal y del Instituto Municipal de Planeación y Evaluación de Aguascalientes, hago referencia al oficio SOPMA/2732/2022 recibido por este Instituto el día 8 de Diciembre del 2022 por parte de la Secretaría de Obras Públicas Municipales, mediante el cual remiten el expediente técnico original de la siguiente obra para su análisis, registro y priorización, conforme al Programa Anual de Obra Pública y Programas Sociales para el ejercicio presupuestal 2022:

DEPENDENCIA EJECUTORA:	SOPMA
NOMBRE DE LA OBRA O PROYECTO:	OBRA COMPLEMENTARIA Y SEÑALIZACIÓN
UBICACIÓN:	AV. AGUASCALIENTES SUR, ENTRE AV. MAHATMA GANDHI Y BLVD. JOSÉ MARÁ CHÁVEZ, VARIAS COLONIAS, AGUASCALIENTES, AGS.
FONDO DE INVERSIÓN:	FONDO DE INFRAESTRUCTURA SOCIAL MUNICIPAL Y DE LAS DEMARCACIONES TERRITORIALES DEL DISTRITO FEDERAL
IMPORTE:	$431,358.09 (ET FINAL)
No. DE OBRA:	2022-FISMDF-0078-04-1101
MODALIDAD DE EJECUCIÓN:	CONTRATO
EJE:	MUNICIPIO SOBRESALIENTE
ESTRATEGIA:	OBRA PÚBLICA INTELIGENTE
POLITICA:	5.8.1.REHABILITACIÓN Y MANTENIMIENTO VIALIDADES, CAMINOS, CALLES, ÁREAS DE TERRACERÍA Y CAUCES (C

Al respecto, hago de su conocimiento que dicho expediente ha sido analizado en su integración técnica y documental, con base en el artículo 168 fracción I del Reglamento de la Ley de Obras Públicas y Servicios Relacionados para el Estado de Aguascalientes y sus Municipios.

Asimismo, le comento que este Instituto valida dicha obra acorde a lo establecido en los artículos 14, 22 párrafo segundo y 23 de la Ley de Obras Públicas y Servicios Relacionados para el Estado de Aguascalientes y sus Municipios, la cual se encuentra alineada al Plan de Desarrollo Municipal vigente, para dar cumplimiento a las metas establecidas en el mismo, y a los Lineamientos Generales para la Operación de este Fondo de Inversión, toda vez que la misma cuente con la autorización del CODEMUN. De igual manera, se hace de su conocimiento que deberá cumplir con lo establecido en los ordenamientos aplicables en lo que respecta al ejercicio, control e información de los recursos de este Fondo. Cabe hacer mención que los recursos solicitados para este proyecto de inversión, estarán sujetos a la disponibilidad presupuestal para el presente ejercicio fiscal que determine la Secretaría a su digno cargo. Sin otro particular por el momento, le envío un cordial saludo.

A T E N T A M E N T E

ARQ. AUSTRIA GABRIELA DÁVILA DE LA LLAVE
DIRECTORA GENERAL DEL IMPLAN

SEDR/ CAAR / JDBC
C.c.p. I.C. ING. MIGUEL ÁNGEL HUIZAR BOTELLO .- Secretaría de Obras Públicas Municipales .Para su conocimiento.
C.c.p. Archivo.

Instituto Municipal de Planeación y Evaluación de Aguascalientes

Antonio Acevedo Escobedo 103 A. Col. Centro
Aguascalientes. Ags. C.P. 20000

(449) 9101010 Ext. 3117

www.implanags.gob.mx

GOBIERNO MUNICIPAL DE AGUASCALIENTES

INSTITUTO MUNICIPAL DE PLANEACION

IMPLAN

ANÁLISIS INTEGRAL DE EXPEDIENTE TÉCNICO

No. DE OBRA (PAOP 2020):	2022-FISMDF-0078-04-1101	REGISTRO No.	251
OFICIO DE VALIDACIÓN:	AMPP/0575/22	FECHA RECIBIDO PARA REVISIÓN:	8 de Diciembre del 2022
PROGRAMA:	URBANIZACION MUNICIPAL	LOCALIDAD O COLONIA:	VARIAS COLONIAS
SUB-PROGRAMA:	0411- Calles y Caminos	DELEGACIÓN:	Aguascalientes
DEPENDENCIA:	Secretaría de Obras Públicas Municipales	MOD. DE EJECUCIÓN:	CONTRATO
NOMBRE DE LA OBRA:	OBRA COMPLEMENTARIA Y SEÑALIZACIÓN, AV. AGUASCALIENTES SUR, ENTRE AV. MAHATMA GANDHI Y BLVD. JOSÉ MARÁ CHÁVEZ		
FUENTE DE FINANCIAMIENTO:	FONDO DE INFRAESTRUCTURA SOCIAL MUNICIPAL Y DE LAS DEMARCACIONES TERRITORIALES DEL DISTRITO FEDERAL, FISMDF		
INVERSIÓN:	$431,358.09	CLASIFICACIÓN DE OBRA:	BIENES DE DOMINIO PUBLICA

TOTAL	FEDERAL	ESTATAL	MUNICIPAL	BENEFICIARIOS	OTROS	DIFERENCIA ENTRE MOD.
$431,358.09	$431,358.09	0.00	0.00	0.00	0.00	*$335.329,84*

TIPO DE EXPENDIENTE:	ET FINAL	AÑO: 2022	AÑO:	AÑO:		
AVANCES:	Financiero: 29 %	Físico: 1 %				
FECHA DE INICIO:	29 de Octubre del 2022	FECHA DE TÉRMINO:	27 de Noviembre del 2022	REGISTRO SIMA:	78	

CHEK LIST DE LOS ANEXOS DEL EXPEDIENTE TÉCNICO

CÉDULA DE REGISTRO DE OBRA	✓
DICTAMEN DE FACTIBILIDAD	✓
MEMORIA DESCRIPTIVA	✓
PRESUPUESTO BASE	✓
FACTIBILIDAD VERIFICADA EN CAMPO	✓
CROQUIS DE UBICACIÓN (MACRO)	✓
CROQUIS DE UBICACIÓN (MACRO)	✓
PROGRAMA DE OBRA Y MONTOS MENSUALES	✓
PLANOS O ESTUDIOS TÉCNICOS	✓
PADRÓN DE BENEFICIARIOS	N/A
ACTA DE ACEPTACIÓN DEL PROYECTO	N/A
DICTAMEN DE IMPACTO AMBIENTAL	N/A
CONVENIO DE CONCERTACIÓN	N/A
ACTA CONSTITUTIVA	N/A

METAS		BENEFICIARIOS		PERIODO DE EJECUCION		OBRA PROPUESTA		CLAVE SISCO
UNIDAD DE MEDIDA	CANT	TIPO DE BENEFICIARIOS	CANTIDAD	FECHA DE INICIO	FECHA DE TERMINO	CONCEPTO	JORNALES A GENERAR	
OBRA	1.00	Personas	150	2022-10-29	2022-11-27	Obra Complementaria y/o Señalización	1121	2349

INCLUIDO EN PLAN DE DESARROLLO MUNICIPAL Y EL PROGRAMA ANUAL DE OBRA PÚBLICA

OBSERVACIONES:

SIN OBSERVACIONES

RECIBIO: ING. JOSÉ DAVID BURGUETE CLAUSTRO
Analista de Programación e Inversión de Obra Pública

8 de Diciembre del 2022
Fecha de validación

8 de Diciembre del 2022
Fecha de validación Expediente

PROCEDE Si ✓ No

H. AYUNTAMIENTO CONSTITUCIONAL DEL MUNICIPIO DE AGUASCALIENTES 2021-2024

AYUNTAMIENTO DE AGUASCALIENTES

CEDULA DE REGISTRO POR OBRA

Aguascalientes LA CIUDAD DE TU VIDA

050400-001E00E05-05-2-2-1-00-1-E-0510-0-17-0078-21-2502-6144

2022-FISMDF-0078-0411109-033	Obra **OBRA COMPLEMENTARIA Y SEÑALIZACIÓN AV. AGUASCALIENTES SUR**
Tipo DEFINITIVO 1 2022 Folio SISCO **2349**	Ubic. TRAMO: ENTRE AV. MAHATMA GANDHI Y AV. JOSÉ MARÍA CHÁVEZ, AGUASCALIENTES Mpio.

Ent. Ejecutora : **050400001E00E05**

Eje: **05**	MUNICIPIO SOBRESALIENTE
Finalidad: **2**	DESARROLLO SOCIAL
Función: **2**	VIVIENDA Y SERVICIOS A LA COMUNIDAD
Subfunción: **1**	URBANIZACIÓN
Tema: **00**	SIN TEMA
Cuenta del Gasto **1**	GASTO PROGRAMABLE
Clasif. Programatica: **E**	PRESTACIÓN DE SERVICIOS PÚBLICOS
Programa: **0510**	Movilidad Urbana
SubPrograma: **0**	SUBPROGRAMA GENÉRICO
Proyecto: **17**	
Tipo de Gasto: **21**	GASTO INVERSIÓN / OBRA PÚBLICA

I N V E R S I O N 2022

Municipal	2502	FONDO PARA LA INFRAESTRUCTURA SOCIAL MUNICIPAL Y DE LAS DEMARCACIONES TERRITORIALES DEL DISTRITO FEDERAL 2022	$431,358.09

Folio SIMA 78 Total $431,358.09

M E T A S

Unidad de Medida	Cantidad	Descripción
OBRA	1	OBRA OBRA COMPLEMENTARIA Y SEÑALIZACIÓN AV. AGUASCALIENTES SUR

Inversión Ejercida Total al	31 de Diciembre de 2021	$0.00
Avance Fisico Acumulado al	31 de Diciembre de 2021	
Avance Fisico Acumulado Programado al	31 de Diciembre de 2022	100 %

Fecha de Inicio 29 Oct 2022 Fecha de Terminación 27 Nov 2022

Jornales a Generar en 2022 1121

Modalidad de ejecución CONTRATO

Clasificación de la Obra Bienes de Dominio Público

Registro del Patrimonio: Obras del dominio público

OBRAS PÚBLICAS

Av. Aguascalientes Sur No. 2615
Fracc. Jardines de las Fuentes,
Aguascalientes, Ags. C.P. 20278

(449) 9 78 92 01, 06, 09

www.ags.gob.mx

GENERALES

Nombre del Proyecto : OBRA COMPLEMENTARIA Y SEÑALIZACIÓN AV. AGUASCALIENTES SUR

TRAMO: ENTRE AV. MAHATMA GANDHI Y AV. JOSÉ MARÍA CHÁVEZ, AGUASCALIENTES Mpio.

Programa : 04 URBANIZACION MUNICIPAL

Subprograma : 11 Calles y caminos (428.- Rehabilitación: 0411208- Señalización)

Clave del Municipio : AGUASCALIENTES

Localidad :

Barrio, Colonia o Ejido : AGUASCALIENTES Mpio.

Tipo de Obra : NUEVA

DESCRIPCIÓN DEL PROYECTO:

OBRA COMPLEMENTARIA Y SEÑALIZACIÓN AV. AGUASCALIENTES SUR 1.00 obra

PRELIMINARES 5.9 M3
OBRA COMPLEMENTARIA 1.00 OBRA
LIMPIEZAS 22.63 M2
SEÑALIZACIÓN HORIZONTAL 1.00 OBRA
SEÑALIZACIÓN VERTICAL 1.00 OBRA
GUARNICIONES 31.7 ML

Beneficiarios (No. y Tipo) :

150	PERSONAS

Hombres: 120 Mujeres: 130

OBRAS PÚBLICAS

No. Folio SISCO 2349

Los abajo firmantes, hacen constar que el presente proyecto :

OBRA COMPLEMENTARIA Y SEÑALIZACIÓN AV. AGUASCALIENTES SUR

TRAMO: ENTRE AV. MAHATMA GANDHI Y AV. JOSÉ MARÍA CHÁVEZ, AGUASCALIENTES Mpio.

cumple con los Requisitos y Normas Técnicas establecidas por la Dependencia Normativa, por lo que es viable su ejecución. Comprometiéndose la misma a proporcionar la supervisión y asistencia técnica necesaria durante el proceso administrativo.

Por la Dependencia Ejecutora

Ing. Miguel Angel Huizar Botello
Secretario de Obras Públicas

Lic. Jaime Gallo Camacho
Secretario de Desarrollo Urbano

LUGAR :AGUASCALIENTES, AGS.

SECRETARIA DE OBRAS PÚBLICAS

Av. Aguascalientes Sur No. 2615
Fracc. Jardines de las Fuentes,
Aguascalientes, Ags. C.P. 20278

(449) 9 78 92 01, 06, 09

www.ags.gob.mx

H. AYUNTAMIENTO CONSTITUCIONAL DEL MUNICIPIO DE AGUASCALIENTES 2021-2024

AYUNTAMIENTO DE AGUASCALIENTES

FACTIBILIDAD VERIFICADA EN CAMPO

Aguascalientes
LA CIUDAD DE TU VIDA

MUNICIPIO: AGUASCALIENTES

LOCALIZACION: TRAMO: ENTRE AV. MAHATMA GANDHI Y AV. JOSÉ MARÍA CHÁVEZ, AGUASCALIENTES Mpio.

PROGRAMA: URBANIZACION MUNICIPAL

SUBPROGRAMA: Calles y caminos (428.- Rehabilitación: 0411208- Señalización)

OBRA A REALIZAR: OBRA COMPLEMENTARIA Y SEÑALIZACIÓN AV. AGUASCALIENTES SUR

DEPENDENCIA EJECUTORA: SECRETARÍA DE OBRAS PUBLICAS DEL MUNICIPIO DE AGUASCALIENTES

FORMA DE EJECUCION: CONTRATO

TIPO DE OBRA PROPUESTA: NUEVA

CONDICIONES ACTUALES DE LA OBRA:

OBRA COMPLEMENTARIA Y SEÑALIZACIÓN AV. AGUASCALIENTES SUR

CARACTERISTICAS DE LA OBRA: Bueno

FACTIBILIDAD DE LA OBRA:

ESTA OBRA SE REQUIERE PARA EL BENEFICIO DE LA CIUDADANÍA

PROCEDE: SI [X] NO [ ]

REVISÓ: Jefa del Departamento de Expedientes Tecnicos y Costos

NOMBRE: Arq. Blanca Margarita Martinez Amador

FIRMA:

FECHA: 29 Nov 2022

SECRETARÍA DE OBRAS PÚBLICAS

Av. Aguascalientes Sur No. 2615
Fracc. Jardines de las Fuentes,
Aguascalientes, Ags. C.P. 20278

(449) 9 78 92 01, 06, 09

www.ags.gob.mx


No. Folio SISCO 2349

H. AYUNTAMIENTO CONSTITUCIONAL DEL MUNICIPIO DE AGUASCALIENTES 2021-2024

H. AYUNTAMIENTO DE AGUASCALIENTES
SECRETARÍA DE OBRAS PÚBLICAS
DIRECCIÓN DE SUPERVISIÓN DE OBRA
LOCALIZACION

Aguascalientes
LA CIUDAD DE TU VIDA

OBRA:	OBRA COMPLEMENTARIA Y SEÑALIZACIÓN AV. AGUASCALIENTES SUR TRAMO :ENTRE AV MAHATMA GANDHI Y JOSÉ MÁRIA CHÁVEZ., AGUASCALIENTES Mpio.					
NO. DE CONTR	FISMDF-0078-2022		CONTRATISTA:	CODEFRAZA S.A DE C.V		

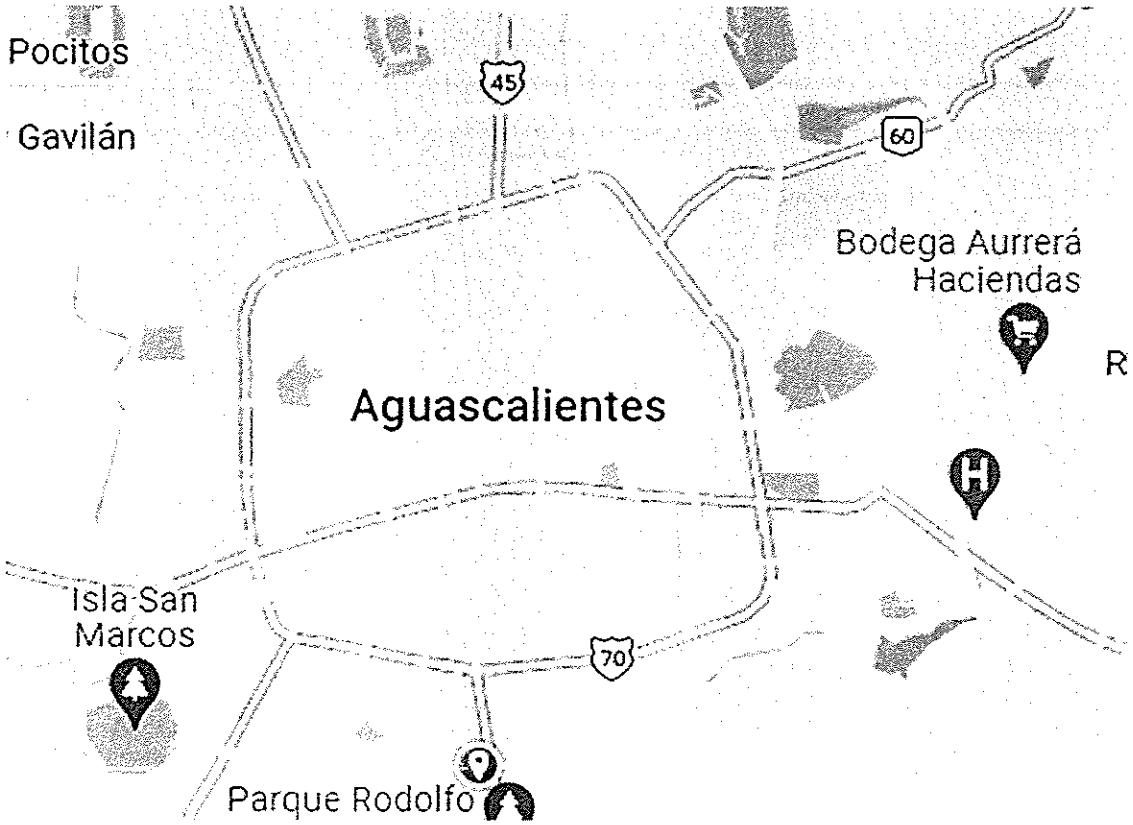

ING.DAVID ALONSO MONTOYA
SUPERVISOR DE OBRA.

H. AYUNTAMIENTO CONSTITUCIONAL DEL MUNICIPIO DE AGUASCALIENTES 2021-2024

H. AYUNTAMIENTO DE AGUASCALIENTES
SECRETARÍA DE OBRAS PÚBLICAS
DIRECCIÓN DE SUPERVISIÓN DE OBRA
LOCALIZACION

Aguascalientes
LA CIUDAD DE TU VIDA

OBRA:	OBRA COMPLEMENTARIA Y SEÑALIZACIÓN AV. AGUASCALIENTES SUR TRAMO :ENTRE AV MAHATMA GANDHI Y JOSÉ MÁRIA CHÁVEZ., AGUASCALIENTES Mpio.					
NO. DE CONTR	FISMDF-0078-2022		CONTRATISTA:	CODEFRAZA S.A DE C.V		



ING.DAVID ALONSO MONTOYA
SUPERVISOR DE OBRA.

ROJ-POS-SOS-7.5.1-04	
REVISIÓN:	00
FECHA DE REVISIÓN:	
RESPONSABLE:	SUPERVISOR DE OBRA
TIEMPO DE RET.	02 AÑOS

PROGRAMA DE OBRA DEFINITIVO

No. DE CONTRATO : FISMDF-0078-2022

PROGRAMA: 04 URBANIZACION MUNICIPAL

No. OBRA Y NOMBRE DE LA OBRA: OBRA COMPLEMENTARIA Y SEÑALIZACIÓN AV. AGUASCALIENTES SUR TRAMO :ENTRE AV MAHATMA GANDHI Y JOSÉ MÁRIA CHÁVEZ., AGUASCALIENTES Mpio.

INICIO VIGENTE: 29-octubre-22

TERMINO REAL: 27-noviembre-22

RECURSO 2022

CONCEPTO				1	2	3	4	5	6	7	8	9	10	11	12	13	14	15	16	PONDERACIÓN %	
				2022																	
				OCTUBRE	NOVIEMBRE	DICIEMBRE	ENERO	FEBRERO	MARZO	ABRIL	MAYO	JUNIO	JULIO	AGOSTO	SEPTIEMBRE	OCTUBRE	NOVIEMBRE	DICIEMBRE	ENERO	FINANCIERO %	FISICO %
DESCRIPCION	INVERSION																				
OBRA COMPLEMENTARIA Y SEÑALIZACIÓN AV. AGUASCALIENTES SUR TRAMO :ENTRE AV MAHATMA GANDHI Y JOSÉ MÁRIA CHÁVEZ., AGUASCALIENTES Mpio.																					
OBRA COMPLEMENTARIA Y SEÑALIZACION AV AGUASCALIENTES SUR , TRAMO: ENTRE AV MAHATMA GANDHI Y AV JOSÉ MARÍA																					
PRELIMINARES	$	9,715.94	100													50			50	2.61	12.50
OBRA COMPLEMENTARIA	$	95,092.32	100													50	30	10		25.57	25.00
LIMPIEZAS	$	317.27	100														50	50		0.09	12.50
SEÑALIZACION HORIZONTAL	$	241,961.82	100														50	25	25	65.07	18.75
SEÑALIZACION VERTICAL	$	12,227.12	100														50	25	25	3.29	18.75
GUARNICIONES	$	12,545.96	100														50	50		3.37	12.50
			-																	0.00	0.00
			-																		
			-																		
			-																		
			-																		
			-																		
			-																		
SUBTOTAL SIN IVA	$	371,860.43		0 0 0 0	0 0 0 0	0 0 0 0	0 0 0 0	0 0 0 0	0 0 0 0	0 0 0 0	0 0 0 0	0 0 0 0	0 0 0 0	0 0 0 0	0 0 0 0	0 0 0 0	2 1 5 1	0 0 0 0	0 0 0 0		
AVANCE SEMANAL %				0% 0% 0% 0%	0% 0% 0% 0%	0% 0% 0% 0%	0% 0% 0% 0%	0% 0% 0% 0%	0% 0% 0% 0%	0% 0% 0% 0%	0% 0% 0% 0%	0% 0% 0% 0%	0% 0% 0% 0%	0% 0% 0% 0%	0% 0% 0% 0%	0% 0% 0% 0%	13% 2% 31% 10%	0% 0% 0% 0%	0% 0% 0% 0%		
AVANCE SEMANAL ACUMULADO %				0% 0% 0% 0%	0% 0% 0% 0%	0% 0% 0% 0%	0% 0% 0% 0%	0% 0% 0% 0%	0% 0% 0% 0%	0% 0% 0% 0%	0% 0% 0% 0%	0% 0% 0% 0%	0% 0% 0% 0%	0% 0% 0% 0%	0% 0% 0% 0%	0% 0% 0% 0%	13% 15% 50% 31% 10%	100% 100% 100% 100%	100% 100% 100% 100%	100.00	100.00
EJERCIDO SEMANAL $				- - - -	- - - -	- - - -	- - - -	- - - -	- - - -	- - - -	- - - -	- - - -	- - - -	- - - -	- - - -	33,385.67	28,527.70 182,053.78 79,488.08 68,405.21	- - - -	- - - -	$ 371,860.43	
EJERCIDO MENSUAL $				$0.00	$0.00	$0.00	$0.00	$0.00	$0.00	$0.00	$0.00	$0.00	$0.00	$0.00	$0.00	$33,385.67	$358,474.76	$0.00	$0.00	$ 59,497.67	IVA 16%
EJERCIDO MENSUAL ACUMULADO $				0.00	0.00	0.00	0.00	0.00	0.00	0.00	0.00	0.00	0.00	0.00	0.00	33,385.67	371,860.43	371,860.43	371,860.43		
EJERCIDO SEMANAL %				0% 0% 0% 0%	0% 0% 0% 0%	0% 0% 0% 0%	0% 0% 0% 0%	0% 0% 0% 0%	0% 0% 0% 0%	0% 0% 0% 0%	0% 0% 0% 0%	0% 0% 0% 0%	0% 0% 0% 0%	0% 0% 0% 0%	0% 0% 0% 0%	0% 0% 0% 0%	9% 5% 21% 18%	0% 0% 0% 0%	0% 0% 0% 0%		
EJERCIDO MENSUAL %				0%	0%	0%	0%	0%	0%	0%	0%	0%	0%	0%	0%	9%	91%	0%	0%	GRAN TOTAL EJERCIDO	
EJERCIDO MENSUAL ACUMULADO %				0%	0%	0%	0%	0%	0%	0%	0%	0%	0%	0%	0%	9%	100%	100%	100%	$	431,358.10

PRE

ING DAVID ALONSO MONTOYA
SUPERVISOR

PRESIDENCIA MUNICIPAL DE AGUASCALIENTES

FACTIBILIDAD VERIFICADA EN CAMPO

GENERALES

EJERCICIO: 2022 APROBACION No: 2022-FISMDF-0078-0411109-33
LOCALIDAD: OBRA.COMPLEMENTARIA Y SEÑALIZACIÓN AV AGUASCALIENTES SUR , TRAMO: ENTRE:AV
MUNICIPIO: AGUASCALIENTES, Mpio.
TIPO DE INVERSION: FONDO PARA LA INFRAESTRUCTURA SOCIAL MUNICIPAL Y DE LAS DEMARCACIONES TERRITORIALES DEL DISTRITO FEDERAL (100%) (MUNICIPAL)
PROGRAMA: 04 URBANIZACION MUNICIPAL
SUB-PROGRAMA: 11 Calles y caminos

OBRA A REALIZARSE: OBRA COMPLEMENTARIA Y SEÑALIZACIÓN AV. AGUASCALIENTES SUR TRAMO :ENTRE AV MAHATMA GANDHI Y JOSÉ MÁRIA CHÁVEZ., AGUASCALIENTES Mpio.

DEPENDENCIA EJECUTORA: SECRETARÍA DE OBRAS PÚBLICAS MUNICIPALES (S.O.P.M.A)
FORMACIÓN DE EJECUCION: CONTRATO NO. DE CONTRATO: FISMDF-0078-2022
NOMBRE CONTRATISTA: CODEFRAZA S.A DE C.V
REPRESENTANTE: CODEFRAZA S.A DE C.V
MONTO CONT. ORIGEN $ 729,942.42 ANTICIPO: $ 218,982.73 PLAZO 30 DIAS
1A AMPLIACION $: $ -
2A AMPLIACION $:
FIRMA CONTRATO: 17/10/2022
INICIO CONT: dd/mm/aa 18/10/2022 TERMINO CONT: 16/11/2022
INICIO REAL: dd/mm/aa 29/10/2022 TERMINO REAL: 27/11/2022

TIPO DE OBRA PROPUESTA

NUEVA CREACIÓN		CONSOLIDACIÓN	
COMPLEMENTARIA	X	AMPLIACIÓN	
REHABILITACIÓN		EQUIPAMIENTO	

CARACTERÍSTICAS DE LA OBRA:

RENIVELACION DE POZOS DE VISITA, REGISTROS, CAJAS DE VALVULAS
PINTURA EN GUARNICION
VIALETAS SOLARES, SEÑALIZACION VERTICAL

CONDICIONES ACTUALES DE LA OBRA: (SELECCIONAR UNO OBLIGATORIO)

BUEN ESTADO X REGULAR PESIMO ESTADO

FACTIBILIDAD DE LA OBRA: (CONDICIONES ACTUALES DE LA OBRA)

ESTA OBRA SE ENCUENTRA EN CONDICIONES PARA OPERARSE

PROCEDE: SI: X NO:
MARQUE SOLO UNA

ING.DAVID ALONSO MONTOYA
SUPERVISOR

PRESIDENCIA MUNICIPAL DE AGUASCALIENTES

FACTIBILIDAD VERIFICADA EN CAMPO

GENERALES

LOCALIDAD: OBRA.COMPLEMENTARIA Y SEÑALIZACIÓN AV AGUASCALIENTES SUR , TRAMO: ENTRE.AV MAHATMA GANDHI Y A
MUNICIPIO: AGUASCALIENTES, Mpio.
PROGRAMA: 04 URBANIZACION MUNICIPAL
SUB-PROGRAMA: 11 Calles y caminos
OBRA A REALIZARSE: OBRA COMPLEMENTARIA Y SEÑALIZACIÓN AV. AGUASCALIENTES SUR TRAMO :ENTRE AV MAHATMA GANDHI Y JOSÉ MÁRIA CHÁVEZ., AGUASCALIENTES Mpio.

DEPENDENCIA EJECUTORA: SECRETARÍA DE OBRAS PÚBLICAS MUNICIPALES (S.O.P.M.A)
FORMACIÓN DE EJECUCION: CONTRATO

TIPO DE OBRA PROPUESTA

NUEVA CREACIÓN		CONSOLIDACIÓN	
COMPLEMENTARIA	X	AMPLIACIÓN	
REHABILITACIÓN		EQUIPAMIENTO	

CARACTERÍSTICAS DE LA OBRA:

RENIVELACION DE POZOS DE VISITA, REGISTROS, CAJAS DE VALVULAS
PINTURA EN GUARNICION

VIALETAS SOLARES, SEÑALIZACION VERTICAL

CONDICIONES ACTUALES DE LA OBRA:

BUEN ESTADO: X REGULAR: PESIMO ESTADO:

FACTIBILIDAD DE LA OBRA:

ESTA OBRA SE ENCUENTRA EN CONDICIONES PARA OPERARSE

PROCEDE **SI:** X **NO:**

ING.DAVID ALONSO MONTOYA
SUPERVISOR

PRESUPUESTO MODIFICADO

Obra: OBRA COMPLEMENTARIA Y SEÑALIZACIÓN AV. AGUASCALIENTES SUR

Ubicación: TRAMO: ENTRE AV. MAHATMA GANDHI Y AV. JOSÉ MARÍA CHÁVEZ, AGUASCALIENTES Mpio.

Contratista: CODEFRAZA, S.A. DE C.V. (758)

No.	Concepto	Unidad	Cantidad	Precio Unitario	Importe Total
	GRUPO: **OBRA COMPLEMENTARIA Y SEÑALIZACION**				
	PARTIDA: **PRELIMINARES**				
1	CORTE CON DISCO DIAMANTADO DE 14" EN PISOS DE CONCRETO ASFÁLTICO DE HASTA (HASTA 8.00 cm. DE PROFUNDIDAD). INCLUYE: TRAZO, EQUIPO Y OPERACIÓN, LIMPIEZAS.	ML	44.84	$59.50	$2,667.98
2	DEMOLICIÓN A MANO Y MECÁNICA DE PAVIMENTO HIDRÁULICO Y/O ASFÁLTICO EN CUALQUIER ESPESOR, EN PAVIMENTOS, LOSAS DIAMANTE, LOSAS DE CAJAS DE VÁLVULAS, LOSAS DE LLAVE HIDRAULICA, CAIMANES, ETC., CON O SIN ARMADO DE ACERO SIN RECUPERACIÓN., INCLUYE: CARGA Y ACARREO LOCAL DE MATERIAL AL LUGAR DE ACOPIO, HERRAMIENTA NECESARIA, CORTES CON DISCO Y TODO LO NECESARIO PARA SU CORRECTA EJECUCIÓN, LIMPIEZA, TRABAJO TERMINADO.	M3	3.68	$760.14	$2,797.32
3	DEMOLICION CONTROLADA DE GUARNICION/DENTELLON DE CONCRETO DE 15X20X40 CM DE SECCION, EN FORMA MECANICA CON EQUIPO MAYOR, INCLUYE: ACARREO LIBRE A ESTACIONES NECESARIAS PARA SU POSTERIOR RETIRO FUERA DE LA OBRA	ML	31.7	$86.51	$2,742.37
4	CARGA MECANICA Y ACARREO DE MATERIAL PRODUCTO DE EXCAVACION Y DEMOLICION EN CAMION DE VOLTEO AL 1er. KM, VOLUMEN MEDIDO COMPACTO.	M3	5.9	$37.45	$220.96
5	ACARREO DE MATERIAL PRODUCTO DE EXCAVACION Y/O DEMOLICION EN CAMION DE VOLTEO A KILOMETROS SUBSECUENTES, AL TIRADERO OFICIAL AUTORIZADO MAS CERCANO AUTORIZADO POR LA SUPERVISION, VOLUMEN MEDIDO COMPACTO.	M3-KM	123.9	$10.39	$1,287.32
				Totales por Partida	**$9,715.94**
	PARTIDA: **OBRA COMPLEMENTARIA**				
6	RE NIVELACIÓN DE POZO DE VISITA HASTA 30 cm DE ALTURA. INCLUYE: RETIRO SIN RECUPERACIÓN DE BROCAL EXISTENTE, DEMOLICIONES, NIVELADO CON TABIQUE ROJO RECOCIDO 7X14X28, ASENTADO CON MORTERO CEMENTO-ARENA 1:3 DE 28 cm DE ESPESOR, APLANADO CON MORTERO CEMENTO-ARENA 1:3 , PLOMEADO, NIVELADO, DEMOLICIONES, CARGAS Y ACARREOS DENTRO DE LA OBRA, LIMPIEZA PREVIA Y FINAL.	PZA	6	$2,643.36	$15,860.16
7	CONSTRUCCIÓN DE LOSA DIAMANTE A BASE DE CONCRETO PREMEZCLADO MR= 45 KG/CM2, T.M.A. 3/4" (19 mm), GRAVA TRITURADA, REVENIMIENTO DE 8+-2.5 cm, RESISTENCIA RÁPIDA A 3 DÍAS, DE 25 CM DE ESPESOR, EN POZO DE VISITA, SECCIÓN DE 1.50 M X 1.50 M , INCLUYE: TRAZO, NIVELACIÓN, LIMPIEZA PREVIA Y PREPARACIÓN DE LA SUPERFICIE, COMPACTACIÓN DE TERRENO AL 95% DE SU PVSM, ESCARIFICADO, SUMINISTRO DE MATERIALES, DEMOLICIÓN Y RECONSTRUCCIÓN DE APROCHES, ESPUMA DE POLIURETANO DE ALTA DENSIDAD EN TODO EL PERÍMETRO EXTERIOR DE 1/2", ASÍ COMO EN LAS JUNTAS DIAGONALES PARA FORMAR 4 PARTES, BROCAL Y TAPA DE Fo. Fo. TIPO PESADO (165 KG), CIMBRADO, COLADO, VIBRADO, DESCIMBRADO, CURADO CON MEMBRANA QUÍMICA BASE AGUA, APLANADO FINO EN RECEPCIÓN DE BROCAL, CORTES CON CORTADORA DE DISCO DE 5 CM ENTRE JUNTAS DIAGONALES FORMANDO 8 PIEZAS Y SELLADO DE JUNTAS, CORTES RELLENOS CON MATERIAL PREFORMADO Y SELLADOR AUTONIVELANTE, MANO DE OBRA, CARGA Y ACARREOS DE MATERIAL DENTRO Y FUERA DE LA OBRA, LIMPIEZA FINAL, TRABAJO TERMINADO P.U.O.T.	PZA	6	$10,406.53	$62,439.18

PRESUPUESTO MODIFICADO

Obra: OBRA COMPLEMENTARIA Y SEÑALIZACIÓN AV. AGUASCALIENTES SUR

Ubicación: TRAMO: ENTRE AV. MAHATMA GANDHI Y AV. JOSÉ MARÍA CHÁVEZ, AGUASCALIENTES Mpio.

Contratista: CODEFRAZA, S.A. DE C.V. (758)

No.	Concepto	Unidad	Cantidad	Precio Unitario	Importe Total
	GRUPO: OBRA COMPLEMENTARIA Y SEÑALIZACION				
	PARTIDA: OBRA COMPLEMENTARIA				
8	RENIVELACIÓN DE RASANTE (PARTE SUPERIOR) DE CAJA DE VÁLVULAS TIPO 4 DE HASTA 2.30 X 2.30 MTS, NIVELADO HASTA UNA ALTURA MAXIMA DE 10 CM, Y MINIMA DE 5 CM. MEDIDAS INTERIORES INCLUYE: TRAZO, EXCAVACIÓN, NIVELACIÓN, PREPARACIONES , Y DEMOLICIONES, RETIRO SIN RECUPERACIÓN DE TAPA DE FOFO EXISTENTE, MURO DE TABIQUE ROJO RECOCIDO COMÚN 7X14X28 CM DE 14 CM DE ESPESOR, JUNTEADO CON MORTERO CEMENTO-ARENA 1:3 APLANADO INTERIOR CON MORTERO CEMENTO ARENA 1:3 DE 2.00 CM DE ESPESOR ACABADO PULIDO, LOSA DE CONCRETO F´C= 250 KG/CM2 T.M.A. 19 MM DE 15 CM DE ESPESOR ARMADA CON VRS No. 3 @15 cm EN AMBOS SENTIDOS, CONTRAMARCO SENCILLO DE CANAL FoFo DE 150 mm, CONTRAMARCO CON TAPA DE FOFO, TIPO PESADO DE 50X50 CM, DEMOLICIÓN Y RECONSTRUCCIÓN DE APROCHES, CARGA Y ACARREOS DENTRO DE LA OBRA, CIMBRADO, DESCIMBRADO, COLADO, VIBRADO, LIMPIEZA PREVIA, FINAL, Y TODO LO NECESARIO PARA LA CORRECTA EJECUCIÓN DEL CONCEPTO.	PZA	1	$16,792.98	$16,792.98
			Totales por Partida		$95,092.32
	PARTIDA: LIMPIEZAS				
12	LIMPIEZA FINAL DE LA OBRA, INCLUYE: BARRIDO, CARGA, ACARREOS Y RETIRO DE ESCOMBROS FUERA DE LA OBRA, TRABAJO TERMINADO.	M2	22.63	$14.02	$317.27
			Totales por Partida		$317.27
	PARTIDA: SEÑALIZACION HORIZONTAL				
13	SUMINISTRO Y APLICACIÓN DE PINTURA BASE SOLVENTE COLOR AZUL (PANTONE 294) EN RAMPAS PARA PERSONAS CON DISCAPACIDAD CUALQUIER SECCIÓN SEGÚN PLANOS. INCLUYE: TRAZO, MANO DE OBRA, LIMPIEZA PREVIA Y FINAL DE SUPERFICIE, EQUIPO NECESARIO PARA SU EJECUCIÓN, Y TODO LO NECESARIO PARA SU CORRECTA EJECUCIÓN, TRABAJO TERMINADO.	M2	24	$251.34	$6,032.16
14	SUMINISTRO Y APLICACIÓN DE LOGOTIPO A (SILLA DE RUEDAS) EN PINTURA BASE SOLVENTE COLOR BLANCO EN RAMPAS PARA PERSONAS CON DISCAPACIDAD TAMAÑO Y DISEÑO SEGÚN PLANOS Y PROYECTO. INCLUYE: TRAZO, ENMASCARILLADO, PLANTILLA, MANO DE OBRA, LIMPIEZA PREVIA Y FINAL DE SUPERFICIE, EQUIPO NECESARIO PARA SU EJECUCIÓN, Y TODO LO NECESARIO PARA SU CORRECTA EJECUCIÓN, TRABAJO TERMINADO.	PZA	20	$174.59	$3,491.80
15	SUMINISTRO Y APLICACIÓN DE PINTURA BASE SOLVENTE (ESMALTE) PARA MARCAS EN GUARNICIONES CLASIFICACION M-12.1, M12.2 APLICADA SOBRE GUARNICIONES Y DENTELLONES COLOR BLANCA Y/O AMARILLA, SEGÚN SE REQUIERA Y SEGÚN MANUAL DE SEÑALIZACIÓN VIAL Y DISPOSITIVOS DE SEGURIDAD SICT (S.C.T). SECADO AL TACTO EN 5 MIN Y AL DURO EN 30 MIN CON MICRO ESFERA , DESARROLLO DE 35 CM. INCLUYE: MATERIALES Y ESPECIFICACIONES QUE CUMPLAN CON LA NORMATIVA N-CMT-5-01-001/13, N-PRY-CAR-10-01-002/13 APLICADAS AL DIA DE HOY, TRAZO, MANO DE OBRA, LIMPIEZA PREVIA Y FINAL DE SUPERFICIE, EQUIPO NECESARIO PARA SU EJECUCIÓN, Y TODO LO NECESARIO PARA SU CORRECTA EJECUCIÓN, TRABAJO TERMINADO.	ML	899.82	$32.35	$29,109.18

Obra: OBRA COMPLEMENTARIA Y SEÑALIZACIÓN AV. AGUASCALIENTES SUR

Ubicación: TRAMO: ENTRE AV. MAHATMA GANDHI Y AV. JOSÉ MARÍA CHÁVEZ, AGUASCALIENTES Mpio.

Contratista: CODEFRAZA, S.A. DE C.V. (758)

No.	Concepto	Unidad	Cantidad	Precio Unitario	Importe Total
	GRUPO: OBRA COMPLEMENTARIA Y SEÑALIZACION				
	PARTIDA: SEÑALIZACION HORIZONTAL				
16	SUMINISTRO Y APLICACIÓN DE PINTURA TERMOPLASTICA ALQUIDALICA DE 120 MILESIMAS DE " (in) EN RAYA SEPARADORA DE SENTIDOS DE CIRCULACION CLASIFICACIÓN M - 1.1, LÍNEA CONTINUA SENCILLA DE DIVISIÓN DE CARRILES DE FRENTE EN PISO, DE 10 CM DE ANCHO, COLOR BLANCO Y/O AMARILLO CON MICRO ESFERA SEGÚN MANUAL DE SEÑALIZACIÓN VIAL Y DISPOSITIVOS DE SEGURIDAD SICT, SECADO AL TACTO EN 5 MIN Y AL DURO EN 30 MIN. INCLUYE: MATERIALES Y ESPECIFICACIONES QUE CUMPLAN CON LA NORMATIVA N-CMT-5-01-001/13, N-PRY-CAR-10-01-002/13 APLICADAS AL DIA DE HOY, MATERIAL APLICADO EN SU ESTADO DE FUSION A UNA TEMPERATURA MINIMA DE 204 C, LA SUPERFICIE DE CONCRETO O ASFALTO NO DEBE PRESENTAR UNA TEMPERATURA MENOR A LOS 10 C, ;TIEMPO DE SECADO EN RANGOS DE TEMPERATURA DE 10 C DEL SUSTRATO 2 MINUTOS, Y NO MAS DE 10 MINUTOS CUANDO EL SUSTRATO OSCILA ALREDEDOR DE 54C, TRAZO, ENMASCARILLADO, MANO DE OBRA, LIMPIEZA PREVIA Y FINAL DE SUPERFICIE, EQUIPO NECESARIO PARA SU EJECUCIÓN, Y TODO LO NECESARIO PARA SU CORRECTA EJECUCIÓN, TRABAJO TERMINADO.	ML	120	$57.27	$6,872.40
17	SUMINISTRO Y APLICACIÓN DE PINTURA TERMOPLASTICA ALQUIDALICA DE 120 MILESIMAS DE " (in) EN RAYA SEPARADORA DE SENTIDOS DE CIRCULACION CLASIFICACIÓN M - 1.2, RAYA DISCONTINUA SENCILLA, DE DIVISIÓN DE CARRILES PARA VELOCIDADES MENORES A 60 KM/HR DE FRENTE EN PISO, DESARROLLO DE 2.50 ML X 0.10 MTS DE ANCHO, CON UNA SEPARACIÓN DE 5.00 MTS ENTRE SI PROMEDIO, A BASE DE PINTURA PARA TRAFICO COLOR BLANCO CON MICRO ESFERA SEGÚN MANUAL DE SEÑALIZACIÓN VIAL Y DISPOSITIVOS DE SEGURIDAD SICT (S.C.T). INCLUYE: MATERIALES Y ESPECIFICACIONES QUE CUMPLAN CON LA NORMATIVA N-CMT-5-01-001/13, N-PRY-CAR-10-01-002/13 APLICADAS AL DIA DE HOY, MATERIAL APLICADO EN SU ESTADO DE FUSION A UNA TEMPERATURA MINIMA DE 204 C, LA SUPERFICIE DE CONCRETO O ASFALTO NO DEBE PRESENTAR UNA TEMPERATURA MENOR A LOS 10 C, ;TIEMPO DE SECADO EN RANGOS DE TEMPERATURA DE 10 C DEL SUSTRATO 2 MINUTOS, Y NO MAS DE 10 MINUTOS CUANDO EL SUSTRATO OSCILA ALREDEDOR DE 54C, TRAZO, ENMASCARILLADO, MANO DE OBRA, LIMPIEZA PREVIA Y FINAL DE SUPERFICIE, EQUIPO NECESARIO PARA SU EJECUCIÓN, Y TODO LO NECESARIO PARA SU CORRECTA EJECUCIÓN, TRABAJO TERMINADO.	ML	90	$57.27	$5,154.30
18	SUMINISTRO Y APLICACIÓN DE PINTURA TERMOPLASTICA ALQUIDALICA DE 120 MILESIMAS DE " (in) EN RAYA EN LA ORILLA DEL ARROYO VIAL CLASIFICACIÓN M - 3.3, CONTINUA IZQUIERDA, PARA VIALIDADES URBANAS DE FRENTE EN PISO, DE 10 CM DE ANCHO Y SEPARADA 15 CM. DE LA GUARNICION, A BASE DE PINTURA PARA TRAFICO COLOR BLANCO CON MICRO ESFERA SEGÚN MANUAL DE SEÑALIZACIÓN VIAL Y DISPOSITIVOS DE SEGURIDAD SICT (S.C.T)., INCLUYE: MATERIALES Y ESPECIFICACIONES QUE CUMPLAN CON LA NORMATIVA N-CMT-5-01-001/13, N-PRY-CAR-10-01-002/13 APLICADAS AL DIA DE HOY, MATERIAL APLICADO EN SU ESTADO DE FUSION A UNA TEMPERATURA MINIMA DE 204 C, LA SUPERFICIE DE CONCRETO O ASFALTO NO DEBE PRESENTAR UNA TEMPERATURA MENOR A LOS 10 C, ;TIEMPO DE SECADO EN RANGOS DE TEMPERATURA DE 10 C DEL SUSTRATO 2 MINUTOS, Y NO MAS DE 10 MINUTOS CUANDO EL SUSTRATO OSCILA ALREDEDOR DE 54C, TRAZO, ENMASCARILLADO, MANO DE OBRA, LIMPIEZA PREVIA Y FINAL DE SUPERFICIE, EQUIPO NECESARIO PARA SU EJECUCIÓN, Y TODO LO NECESARIO PARA SU CORRECTA EJECUCIÓN, TRABAJO TERMINADO.	ML	927.7	$57.27	$53,129.38

Obra: OBRA COMPLEMENTARIA Y SEÑALIZACIÓN AV. AGUASCALIENTES SUR

Ubicación: TRAMO: ENTRE AV. MAHATMA GANDHI Y AV. JOSÉ MARÍA CHÁVEZ, AGUASCALIENTES Mpio.

Contratista: CODEFRAZA, S.A. DE C.V. (758)

No.	Concepto	Unidad	Cantidad	Precio Unitario	Importe Total
	GRUPO: OBRA COMPLEMENTARIA Y SEÑALIZACION				
	PARTIDA: SEÑALIZACION HORIZONTAL				
19	SUMINISTRO Y APLICACIÓN DE PINTURA TERMOPLASTICA ALQUIDALICA DE 120 MILESIMAS DE " (in) EN RAYA DE ALTO CLASIFICACIÓN M - 6, PARA INDICAR ALTO EN CRUCEROS, COLOR BLANCO, REFLEJANTE CON MICRO ESFERA DE VIDRIO EN PROPORCIÓN SEGÚN MANUAL DE SEÑALIZACIÓN VIAL Y DISPOSITIVOS DE SEGURIDAD SICT (S.C.T). DE 0.60 MTS DE ANCHO DE LONGITUD VARIABLE, INCLUYE: MATERIALES Y ESPECIFICACIONES QUE CUMPLAN CON LA NORMATIVA N-CMT-5-01-001/13, N-PRY-CAR-10-01-002/13 APLICADAS AL DIA DE HOY, MATERIAL APLICADO EN SU ESTADO DE FUSION A UNA TEMPERATURA MINIMA DE 204 C, LA SUPERFICIE DE CONCRETO O ASFALTO NO DEBE PRESENTAR UNA TEMPERATURA MENOR A LOS 10 C, ;TIEMPO DE SECADO EN RANGOS DE TEMPERATURA DE 10 C DEL SUSTRATO 2 MINUTOS, Y NO MAS DE 10 MINUTOS CUANDO EL SUSTRATO OSCILA ALREDEDOR DE 54C, TRAZO, ENMASCARILLADO, MANO DE OBRA, LIMPIEZA PREVIA Y FINAL DE SUPERFICIE, EQUIPO NECESARIO PARA SU EJECUCIÓN, Y TODO LO NECESARIO PARA SU CORRECTA EJECUCIÓN, TRABAJO TERMINADO.	ML	85.6	$344.88	$29,521.73
20	SUMINISTRO Y APLICACIÓN DE PINTURA TERMOPLASTICA ALQUIDALICA DE 120 MILESIMAS DE " (in) EN RAYA PARA CRUCE PEATONAL CLASIFICACIÓN M - 7.1, PARA INDICAR " CRUCE PEATONAL EN VIAS PRIMARIAS", COLOR AMARILLO, REFLEJANTE CON MICRO ESFERA DE VIDRIO EN PROPORCIÓN SEGÚN MANUAL DE SEÑALIZACIÓN VIAL Y DISPOSITIVOS DE SEGURIDAD SICT (S.C.T). DE 0.40 MTS DE ANCHO Y 3.5 MTS. DE LONGITUD POR EL ANCHO DE LA VIALIDAD, CON UNA SEPARACIÓN DE 0.40 MTS. ENTRE ELLAS, INCLUYE: MATERIALES Y ESPECIFICACIONES QUE CUMPLAN CON LA NORMATIVA N-CMT-5-01-001/13, N-PRY-CAR-10-01-002/13 APLICADAS AL DIA DE HOY, MATERIAL APLICADO EN SU ESTADO DE FUSION A UNA TEMPERATURA MINIMA DE 204 C, LA SUPERFICIE DE CONCRETO O ASFALTO NO DEBE PRESENTAR UNA TEMPERATURA MENOR A LOS 10 C, ;TIEMPO DE SECADO EN RANGOS DE TEMPERATURA DE 10 C DEL SUSTRATO 2 MINUTOS, Y NO MAS DE 10 MINUTOS CUANDO EL SUSTRATO OSCILA ALREDEDOR DE 54C, TRAZO, ENMASCARILLADO, MANO DE OBRA, LIMPIEZA PREVIA Y FINAL DE SUPERFICIE, EQUIPO NECESARIO PARA SU EJECUCIÓN, Y TODO LO NECESARIO PARA SU CORRECTA EJECUCIÓN, TRABAJO TERMINADO.	M2	112.2	$595.76	$66,844.27
21	SUMINISTRO Y APLICACIÓN DE PINTURA TERMOPLASTICA ALQUIDALICA DE 120 MILESIMAS DE " (in) EN FLECHAS CLASIFICACIÓN M - 11.1, "FLECHA SENCILLA" PARA INDICAR SENTIDO DE CIRCULACIÓN , EN VIALIDADES PARA VELOCIDAD MENOR A 60KM POR HORA DIMENSION NORMATIVA SEGUN MANUAL DE SEÑALIZACIÓN VIAL Y DISPOSITIVOS DE SEGURIDAD SICT (SCT) Y/O (VER PLANO DE SEÑALAMIENTOS), COLOR BLANCO, REFLEJANTE CON MICRO ESFERA DE VIDRIO EN PROPORCIÓN SEGÚN NORMA SCT, INCLUYE: MATERIALES Y ESPECIFICACIONES QUE CUMPLAN CON LA NORMATIVA N-CMT-5-01-001/13, N-PRY-CAR-10-01-002/13 APLICADAS AL DIA DE HOY, MATERIAL APLICADO EN SU ESTADO DE FUSION A UNA TEMPERATURA MINIMA DE 204 C, LA SUPERFICIE DE CONCRETO O ASFALTO NO DEBE PRESENTAR UNA TEMPERATURA MENOR A LOS 10 C, ;TIEMPO DE SECADO EN RANGOS DE TEMPERATURA DE 10 C DEL SUSTRATO 2 MINUTOS, Y NO MAS DE 10 MINUTOS CUANDO EL SUSTRATO OSCILA ALREDEDOR DE 54C, TRAZO, ENMASCARILLADO, MANO DE OBRA, LIMPIEZA PREVIA Y FINAL DE SUPERFICIE, EQUIPO NECESARIO PARA SU EJECUCIÓN, Y TODO LO NECESARIO PARA SU CORRECTA EJECUCIÓN, TRABAJO TERMINADO.	PZA	6	$789.91	$4,739.46

Obra: OBRA COMPLEMENTARIA Y SEÑALIZACIÓN AV. AGUASCALIENTES SUR

Ubicación: TRAMO: ENTRE AV. MAHATMA GANDHI Y AV. JOSÉ MARÍA CHÁVEZ, AGUASCALIENTES Mpio.

Contratista: CODEFRAZA, S.A. DE C.V. (758)

No.	Concepto	Unidad	Cantidad	Precio Unitario	Importe Total
	GRUPO: OBRA COMPLEMENTARIA Y SEÑALIZACION				
	PARTIDA: SEÑALIZACION HORIZONTAL				
22	SUMINISTRO Y APLICACIÓN DE PINTURA TERMOPLASTICA ALQUIDALICA DE 120 MILESIMAS DE " (in) EN FLECHAS CLASIFICACIÓN M - 11.1, " FLECHA CABEZA DOBLE" PARA INDICAR SENTIDO DE CIRCULACIÓN (VUELTA IZQUIERDA O DERECHA), EN VIALIDADES PARA VELOCIDAD MENOR A 60KM POR HORA SEGUN MANUAL DE SEÑALIZACIÓN VIAL Y DISPOSITIVOS DE SEGURIDAD SICT (SCT), (VER PLANO DE SEÑALAMIENTOS), EN COLOR BLANCO, REFLEJANTE CON MICRO ESFERA DE VIDRIO EN PROPORCIÓN SEGÚN NORMA SCT, INCLUYE: MATERIALES Y ESPECIFICACIONES QUE CUMPLAN CON LA NORMATIVA N-CMT-5-01-001/13, N-PRY-CAR-10-01-002/13 APLICADAS AL DIA DE HOY, MATERIAL APLICADO EN SU ESTADO DE FUSION A UNA TEMPERATURA MINIMA DE 204 C, LA SUPERFICIE DE CONCRETO O ASFALTO NO DEBE PRESENTAR UNA TEMPERATURA MENOR A LOS 10 C, ;TIEMPO DE SECADO EN RANGOS DE TEMPERATURA DE 10 C DEL SUSTRATO 2 MINUTOS, Y NO MAS DE 10 MINUTOS CUANDO EL SUSTRATO OSCILA ALREDEDOR DE 54C, TRAZO, ENMASCARILLADO, MANO DE OBRA, LIMPIEZA PREVIA Y FINAL DE SUPERFICIE, EQUIPO NECESARIO PARA SU EJECUCIÓN, Y TODO LO NECESARIO PARA SU CORRECTA EJECUCIÓN, TRABAJO TERMINADO.	PZA	2	$991.08	$1,982.16
23	SUMINISTRO Y APLICACIÓN DE PINTURA TERMOPLASTICA ALQUIDALICA DE 120 MILESIMAS DE " (in) EN LETRAS Y NUMEROS CLASIFICACIÓN M - 11.1 "LETRAS Y NUMEROS" EN VIALIDADES PARA VELOCIDAD MENOR A 60KM POR HORA SEGUN MANUAL DE SEÑALIZACIÓN VIAL Y DISPOSITIVOS DE SEGURIDAD SICT (SCT), (VER PLANO DE SEÑALAMIENTOS) EN COLOR BLANCO, REFLEJANTE CON MICRO ESFERA DE VIDRIO EN PROPORCIÓN SEGÚN NORMA SCT DE (VER DETALLES EN PLANOS) INCLUYE: MATERIALES Y ESPECIFICACIONES QUE CUMPLAN CON LA NORMATIVA N-CMT-5-01-001/13, N-PRY-CAR-10-01-002/13 APLICADAS AL DIA DE HOY, MATERIAL APLICADO EN SU ESTADO DE FUSION A UNA TEMPERATURA MINIMA DE 204 C, LA SUPERFICIE DE CONCRETO O ASFALTO NO DEBE PRESENTAR UNA TEMPERATURA MENOR A LOS 10 C, ;TIEMPO DE SECADO EN RANGOS DE TEMPERATURA DE 10 C DEL SUSTRATO 2 MINUTOS, Y NO MAS DE 10 MINUTOS CUANDO EL SUSTRATO OSCILA ALREDEDOR DE 54C, TRAZO, ENMASCARILLADO, MANO DE OBRA, LIMPIEZA PREVIA Y FINAL DE SUPERFICIE, EQUIPO NECESARIO PARA SU EJECUCIÓN, Y TODO LO NECESARIO PARA SU CORRECTA EJECUCIÓN, TRABAJO TERMINADO.	PZA	32	$918.69	$29,398.08
25	SUMINISTRO Y COLOCACIÓN DE VIALETA STANDARD (S-200) DE 10X10CM. COLOR: CUERPO AMARILLO Y/O BLANCO Y REFLEJANTE AMARILLO 1 CARA MARCA SEA O SIMILAR EN CALIDAD Y ESPECIFICACIONES DE FICHA TÉCNICA, FIJADO EN PAVIMENTO CON SISTEMA DE SUJECIÓN DE ALTO AGARRE PEGAMENTO EPOXICO 100 A/B (RESINA EPÓXICA/RESINA POLIAMIDA MODIFICADA), RESISTENTE A ALTA TEMPERATURA (VER PLANO DE DETALLES DE SEÑALAMIENTOS HORIZONTAL), INCLUYE: LIMPIEZA PREVIA Y FINAL DE LA SUPERFICIE, PREPARACIÓN DE LA SUPERFICIE, TRAZO, ALINEACIÓN, Y TODO LO NECESARIO PARA SU CORRECTA EJECUCIÓN, TRABAJO TERMINADO.	PZA	74	$76.85	$5,686.90
				Totales por Partida	$241,961.82

Obra: OBRA COMPLEMENTARIA Y SEÑALIZACIÓN AV. AGUASCALIENTES SUR

Ubicación: TRAMO: ENTRE AV. MAHATMA GANDHI Y AV. JOSÉ MARÍA CHÁVEZ, AGUASCALIENTES Mpio.

Contratista: CODEFRAZA, S.A. DE C.V. (758)

No.	Concepto	Unidad	Cantidad	Precio Unitario	Importe Total
	GRUPO: OBRA COMPLEMENTARIA Y SEÑALIZACION				
	PARTIDA: SEÑALIZACION VERTICAL				
26	SUMINISTRO Y COLOCACION DE SEÑALAMIENTO VERTICAL DE RESTRICCION SP-32 (CRUCE DE PEATONES), DISEÑO NORMATIVO SCT, HECHO A ABASE DE LAMINA GALVANIZADA CON CEJA DE 86 X 86 CM CALIBRE 16, CON TERMINADO GRADO INGENIERIA EN SU TOTALIDAD, EL COLOR SERA REFLEJANTE GRADO INGENIERIA Y SIMBOLOS EN COLOR REFLEJANTE, TODOS LOS COLORES RESISTENTES A LA INTEMPERIE, FIJADA MEDIANTE BARRENADO Y TORNILLOS DE 2 1/2" X 5/16" A UN POSTE DE PTR DE 2 X 2" CALIBRE 14 EN ACABADO GALVANIZADO Y CON UNA ALTURA DE 2.5 MTS AL NIVEL DE BANQUETA A LA PARTE INFERIOR DE LA LAMINA MAS EL EXCEDENTE REQUERIDO PARA FIJAR LAS LAMINAS Y ANCLADO DE 50 CM DE PROFUNDIDAD CON ANGULO TRANSVERSAL DE 1 X 1" DE 25 CM, EN DADO DE CONCRETO F´c=150 KG/CM2 DE 30 CM DE LADO (VER PLANO DE DETALLES CRITERIOS DE ANCLAJE DE SEÑALAMIENTO VERTICAL, DETALLE SEÑ-02 Y SEÑ 03), MCA ASEA O SIMILAR EN CALIDAD Y ESPECIFICACIONES, INCLUYE: MANO DE OBRA, FLETES, MANIOBRAS LIMPIEZAS Y RETIRO DEL SOBRANTE FUERA DE LA OBRA HASTA TIRADERO OFICIAL, TRABAJO TERMINADO.	PZA	4	$3,056.78	$12,227.12
				Totales por Partida	$12,227.12
	PARTIDA: GUARNICIONES				
27	EXCAVACION A MAQUINA Y/O A MANO EN MATERIAL TIPO II, EN SECO O PRESENCIA DE AGUA, INCLUYE. CORTE DE RAIZ DE CUALQUIER TAMAÑO Y GROSOR, HASTA UNA PROFUNDIDAD DE 40 CM DESPUES DE DESMONTE, DESPALME Y/O DEMOLICION DE SUPERFICIE O ELEMENTO ESTRUCTURAL O DE ACABADO, PROTECCION DE AREAS ADYACENTES, SIN DAÑAR AREAS ALEDAÑAS, CARGA Y ACARREO A TIRADERO OFICIAL, CONSERVACION DE LA MISMA, TRABAJO TERMINADO, LIMPIEZAS.	M3	2.22	$538.26	$1,194.94
29	CONSTRUCCION DE GUARNICION Y/O DENTELLON, RECTA Y/O CURVA TRAPEZOIDAL 15-20X40 CM DE SECCION CON CONCRETO PREMEZCLADO MR=38 KGF/CM2, R.N.REVENIMIENTO DE 8 A 10 CM, T.M.A. 3/4", GRAVA TRITURADA, ACABADO PULIDO EN PARTE DE SUPERIOR Y DOBLADOR EN ARISTAS, INCLUYE:TRAZO, DEMOLICIÓN Y RECONSTRUCCIÓN DE APROCHES, COMPACTADO DE PLANTILLA, CIMBRADO, COLADO, VIBRADO, ACABADO, DESCIMBRADO, ALINEADO, NIVELADO, Y CURADO EN SU PARTE SUPERIOR CON MEMBRANA BASE AGUA A RAZON DE 1 LTO/M2, JUNTA DE AISLAMIENTO LONGITUDINAL AL COMBINAR CON OTRO ELEMENTO Y TRANSVERSAL @ 30 MT MAXIMO, SELLADO CON SELLADOR AUTONIVELANTE LONGITUDINAL, LIMPIEZAS, CARGAS Y ACARREOS LOCALES, TRABAJO TERMINADO, .P.U.O.T.	ML	31.7	$340.18	$10,783.71
31	CARGA MECANICA Y ACARREO DE MATERIAL PRODUCTO DE EXCAVACION Y DEMOLICION EN CAMION DE VOLTEO AL 1er. KM, VOLUMEN MEDIDO COMPACTO.	M3	2.22	$37.45	$83.14
32	ACARREO DE MATERIAL PRODUCTO DE EXCAVACION Y/O DEMOLICION EN CAMION DE VOLTEO A KILOMETROS SUBSECUENTES, AL TIRADERO OFICIAL AUTORIZADO MAS CERCANO AUTORIZADO POR LA SUPERVISION, VOLUMEN MEDIDO COMPACTO.	M3-KM	46.6	$10.39	$484.17
				Totales por Partida	$12,545.96
				Totales por Grupo	$371,860.42

PRESUPUESTO MODIFICADO

Obra: OBRA COMPLEMENTARIA Y SEÑALIZACIÓN AV. AGUASCALIENTES SUR

Ubicación: TRAMO: ENTRE AV. MAHATMA GANDHI Y AV. JOSÉ MARÍA CHÁVEZ, AGUASCALIENTES Mpio.

Contratista: CODEFRAZA, S.A. DE C.V. (758)

No	Concepto	Unidad	Cantidad	Precio Unitario	Importe Total

Totales Presup.		$371,860.42
Anticipo	+	$188,778.22
Amortizac. Ant.	-	$188,778.22
SubTotal. Ant.	=	$371,860.43
IVA	+	$59,497.66
Total	=	$431,358.09

PRESUPUESTO MODIFICADO

Obra: OBRA COMPLEMENTARIA Y SEÑALIZACIÓN AV. AGUASCALIENTES SUR

Ubicación: TRAMO: ENTRE AV. MAHATMA GANDHI Y AV. JOSÉ MARÍA CHÁVEZ, AGUASCALIENTES Mpio.

Contratista: CODEFRAZA, S.A. DE C.V. (758)

Grupo	Partida	Importe
OBRA COMPLEMENTARIA Y SEÑALIZACION		
	PRELIMINARES	$9,715.94
	OBRA COMPLEMENTARIA	$95,092.32
	LIMPIEZAS	$317.27
	SEÑALIZACION HORIZONTAL	$241,961.82
	SEÑALIZACION VERTICAL	$12,227.12
	GUARNICIONES	$12,545.96
	Subtotal por Grupo	$371,860.42

Totales Presup.		$371,860.42
Anticipo	+	$188,778.22
Amortizac. Ant.	-	$188,778.22
SubTotal. Ant.	=	$371,860.43
IVA	+	$59,497.66
Total	=	$431,358.09

H. AYUNTAMIENTO CONSTITUCIONAL DEL MUNICIPIO DE AGUASCALIENTES 2021-2024

H. AYUNTAMIENTO DE AGUASCALIENTES

SECRETARÍA DE OBRAS PÚBLICAS


DIRECCIÓN DE SUPERVISIÓN DE OBRA


Aguascalientes
LA CIUDAD DE TU VIDA


MEMORIA FOTOGRAFICA

OBRA:	OBRA COMPLEMENTARIA Y SEÑALIZACIÓN AV. AGUASCALIENTES SUR TRAMO :ENTRE AV MAHATMA GANDHI Y JOSÉ MÁRIA CHÁVEZ., AGUASCALIENTES Mpio.					
NO. DE CONTRATO:	FISMDF-0078-2022		CONTRATISTA:	CODEFRAZA S.A DE C.V		

INICIO.

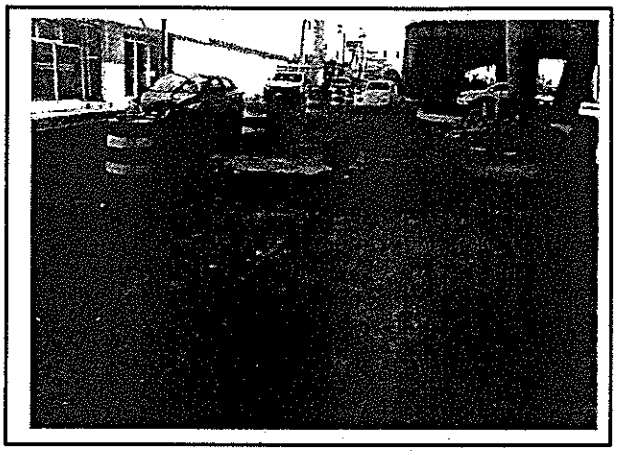

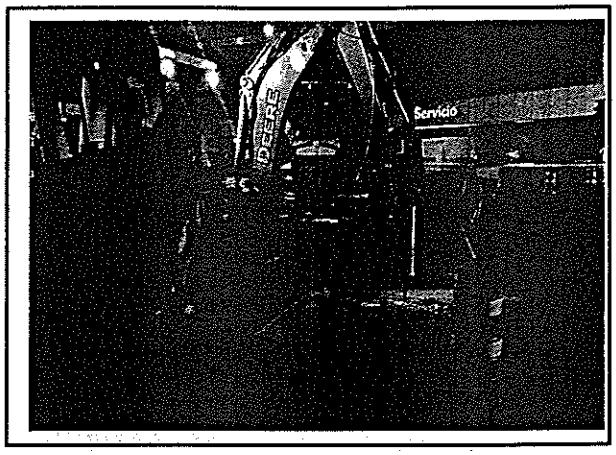

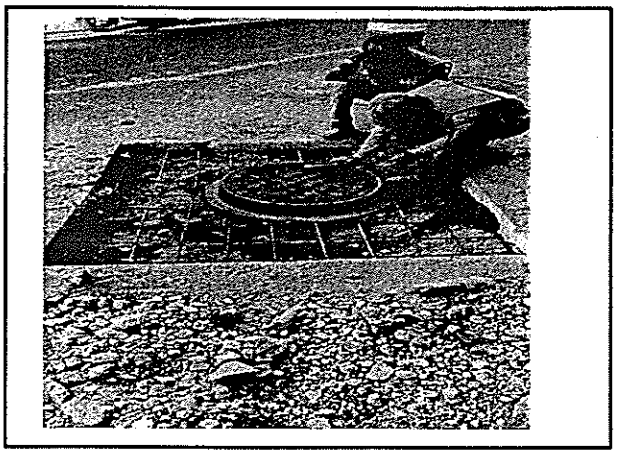



ING.DAVID ALONSO MONTOYA
SUPERVISOR DE OBRA.

H. AYUNTAMIENTO DE AGUASCALIENTES
SECRETARÍA DE OBRAS PÚBLICAS
DIRECCIÓN DE SUPERVISIÓN DE OBRA


H. AYUNTAMIENTO CONSTITUCIONAL DEL MUNICIPIO DE AGUASCALIENTES 2021-2024


Aguascalientes
LA CIUDAD DE TU VIDA


MEMORIA FOTOGRAFICA

OBRA:	OBRA COMPLEMENTARIA Y SEÑALIZACIÓN AV. AGUASCALIENTES SUR TRAMO :ENTRE AV MAHATMA GANDHI Y JOSÉ MÁRIA CHÁVEZ., AGUASCALIENTES Mpio.					
NO. DE CONTRATO:	FISMDF-0078-2022		CONTRATISTA:	CODEFRAZA S.A DE C.V		

PROCESO

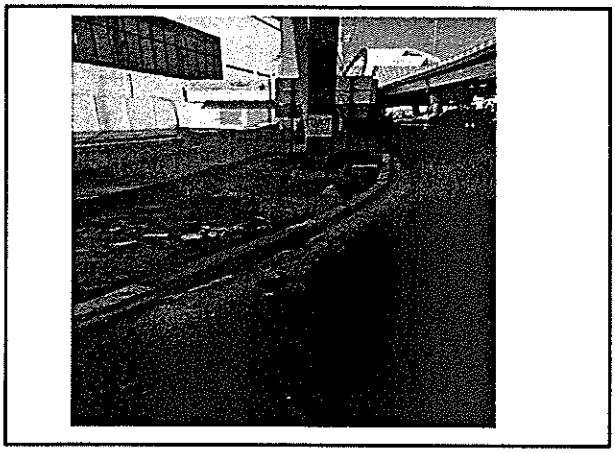

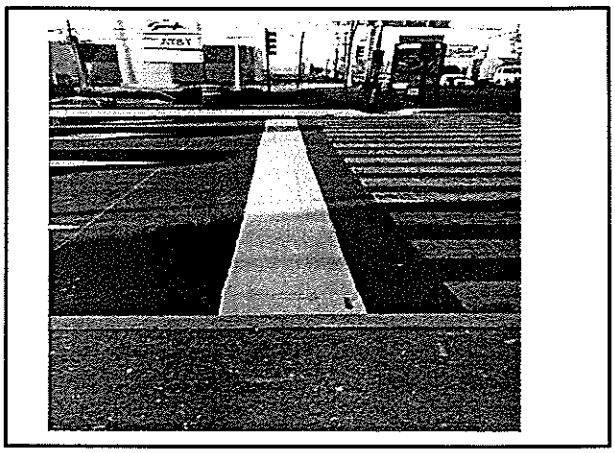

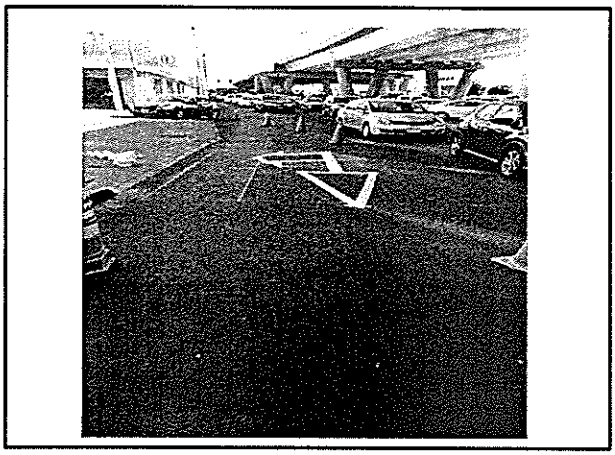



ING.DAVID ALONSO MONTOYA
SUPERVISOR DE OBRA.

H. AYUNTAMIENTO CONSTITUCIONAL
DEL MUNICIPIO DE AGUASCALIENTES
2021-2024

H. AYUNTAMIENTO DE AGUASCALIENTES

SECRETARÍA DE OBRAS PÚBLICAS

DIRECCIÓN DE SUPERVISIÓN DE OBRA


Aguascalientes
LA CIUDAD DE TU VIDA

MEMORIA FOTOGRAFICA


OBRA:	OBRA COMPLEMENTARIA Y SEÑALIZACIÓN AV. AGUASCALIENTES SUR TRAMO :ENTRE AV MAHATMA GANDHI Y JOSÉ MÁRIA CHÁVEZ., AGUASCALIENTES Mpio.					
NO. DE CONTRATO:	FISMDF-0078-2022		CONTRATISTA:	CODEFRAZA S.A DE C.V		

TERMINO



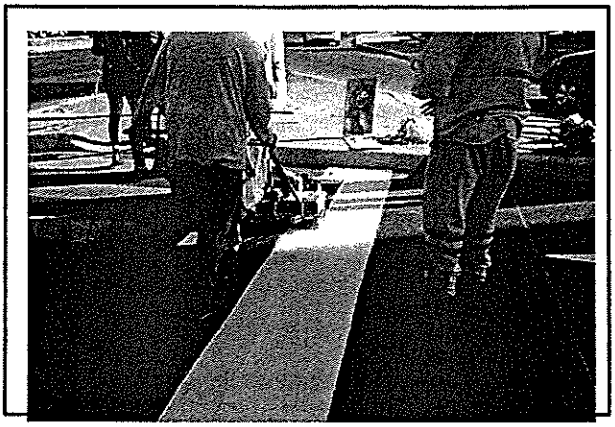



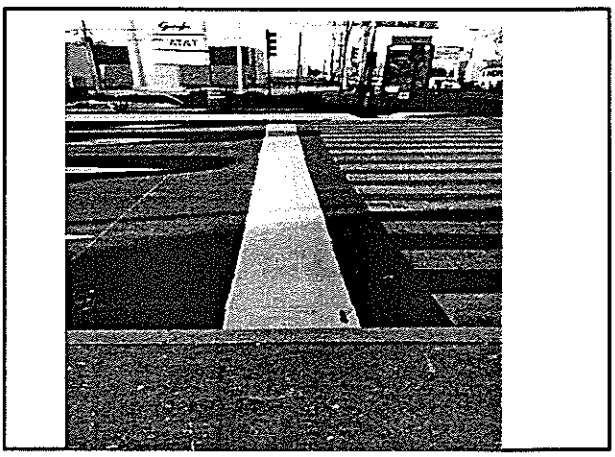

ING.DAVID ALONSO MONTOYA
SUPERVISOR DE OBRA.

MODIFICADO

SECRETARÍA DE OBRAS PÚBLICAS

DIRECCIÓN DE SUPERVISIÓN DE OBRA

EJERCICIO 2022

N° DE CONTRATO: FISMDF-0078-2022


NOMBRE DE LA OBRA: OBRA COMPLEMENTARIA Y SEÑALIZACIÓN AV. AGUASCALIENTES SUR TRAMO :ENTRE AV MAHATMA GANDHI Y JOSÉ MÁRIA CHÁVEZ., AGUASCALIENTES Mpio.

MONTO MODIFICADO FINAL: $ 431,358.10

VOLUMEN	UNIDAD	COMPONENTE DE LA OBRA	MONTO
8.91	M3	DEMOLICION CONTROLADA DE GUARNICION/DENTELLON DE CONCRETO DE 15X20X40 CM DE SECCION, EN FORMA MECANICA CON EQUIPO MAYOR, INCLUYE: ACARREO LIBRE A ESTACIONES NECESARIAS PARA SU POSTERIOR RETIRO FUERA DE LA OBRA	$ 9,715.94
11.00	PZA	LIMPIEZA Y DESAZOLVE DE POZOS DE VISITA Y LÍNEAS DE ALCANTARILLADO EXISTENTE CON CAMIÓN TIPO VACTOR. INCLUYE: RESANE INTERIOR DEL POZO Y REMATE DE POZO CON TUBO SELLADOR FESTER Y MORTERO 1:3, MANO DE OBRA, SUMINISTRO DE AGUA EN PIPA, HERRAMIENTAS Y EQUIPO PARA SU CORRECTA	$ 95,092.32
74.00	M2	LIMPIEZA FINAL DE LA OBRA, INCLUYE: BARRIDO, CARGA, ACARREOS Y RETIRO DE ESCOMBROS FUERA DE LA OBRA, TRABAJO TERMINADO.	$ 317.27
1619.75	ML	SUMINISTRO Y APLICACIÓN DE PINTURA TERMOPLASTICA ALQUIDALICA DE 120 MILESIMAS DE " (in) EN LETRAS Y NUMEROS CLASIFICACIÓN M - 11.1 "LETRAS Y NUMEROS" EN VIALIDADES PARA VELOCIDAD MENOR A 60KM POR HORA SEGUN MANUAL DE SEÑALIZACIÓN VIAL Y DISPOSITIVOS DE SEGURIDAD SICT (SCT), (VER	$ 241,961.82
1.00	PZA	SUMINISTRO Y COLOCACIÓN DE SEÑALAMIENTO VERTICAL INFORMATIVA DE SERVICIOS SIS-19 "PARADA DE AUTOBUS" DISEÑO NORMATIVO SCT , HECHO A BASE DE LAMINA GALVANIZADA (CON CEJA) 71 cm x 71 cm CALIBRE 16 CON TERMINADO GRADO DE INGENIERÍA EN SU TOTALIDAD, EL COLOR SERA REFLEJANTE GRADO	$ 12,227.12
31.70	ML	CONSTRUCCION DE GUARNICION Y/O DENTELLON, RECTA Y/O CURVA TRAPEZOIDAL 15-20X40 CM DE SECCION CON CONCRETO PREMEZCLADO MR=38 KGF/CM2, R.N.REVENIMIENTO DE 8 A 10 CM, T.M.A. 3/4", GRAVA TRITURADA, ACABADO PULIDO EN PARTE DE SUPERIOR Y DOBLADOR EN ARISTAS, INCLUYE:TRAZO, DEMOLICIÓN	$ 12,545.96
		TOTAL PRESUP.	$ 371,860.43
		IVA	$ 59,497.67
		TOTAL	$ 431,358.10

NOMBRE DEL SUPERVISOR: ING.DAVID ALONSO MONTOYA




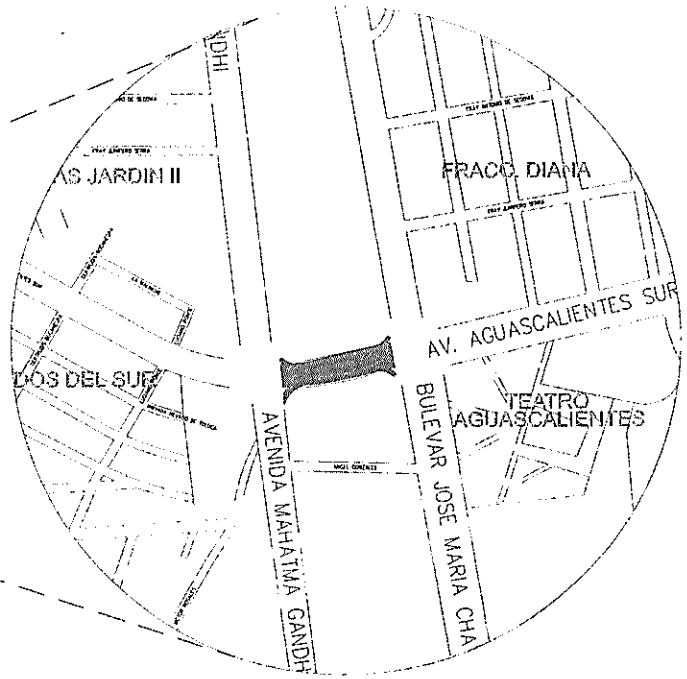

CROQUIS DE LOCALIZACIÓN

SIN ESCALA

AV. AGUASCALIENTES SUR

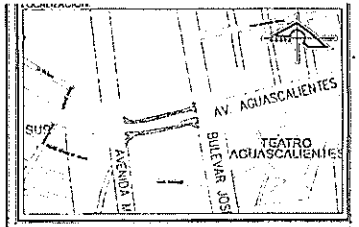

SIMBOLOGÍA

La Dirección de Planeación y Proyectos solo autoriza el proyecto ejecutivo, no se responsable de la correcta ejecución de la obra. Este documento no tiene validez si no presenta las firmas de los responsables para su autorización, así como los sellos respectivos.

PRESIDENTE MUNICIPAL
M.P.P. Leonardo Montañez Castro
ENCARGADA DE DESPACHO DE LA SOPMA
Arq. Gloria Guadalupe Castillo González

REV.	FECHA	OBSERVACIONES

V°B° DE LA DEPENDENCIA

RESP. DE PROY. EXTERNO		LOGO EXTERNO
CED. PROFESIONAL		
PROYECTÓ	REVISÓ	AUTORIZÓ

Dirección de Planeación y Proyectos de Obra — Secretaría de Obras Públicas

PROYECTISTA	COORDINADOR
ARQ. ALVARO DAVID MEZA CONTRERAS	ARQ. ALEJANDRO JAIME LEAL
JEFE DE DEP.	DIRECTOR
ARQ. J. JESÚS PALAFOX GONZÁLEZ	M. en ARQ. JOSÉ LUIS JIMÉNEZ GARCÍA


PROYECTO
OBRA COMPLEMENTARIA Y SEÑALETICA AV. AGUASCALIENTES SUR.

UBICACIÓN
AMBAS CALZADAS DE ENTRE AV. MAHATMA GANDHI Y AV. JOSÉ MARÍA CHAVEZ.

CONTENIDO
CROQUIS DE LOCALIZACIÓN

CLAVE	No. PLANO
LOC 01	01
FECHA MAR 2022	ESCALA INDICADA
ACOTACIÓN METROS	No. EXP. E-000-22

Aguascalientes
LA CIUDAD DE TU VIDA

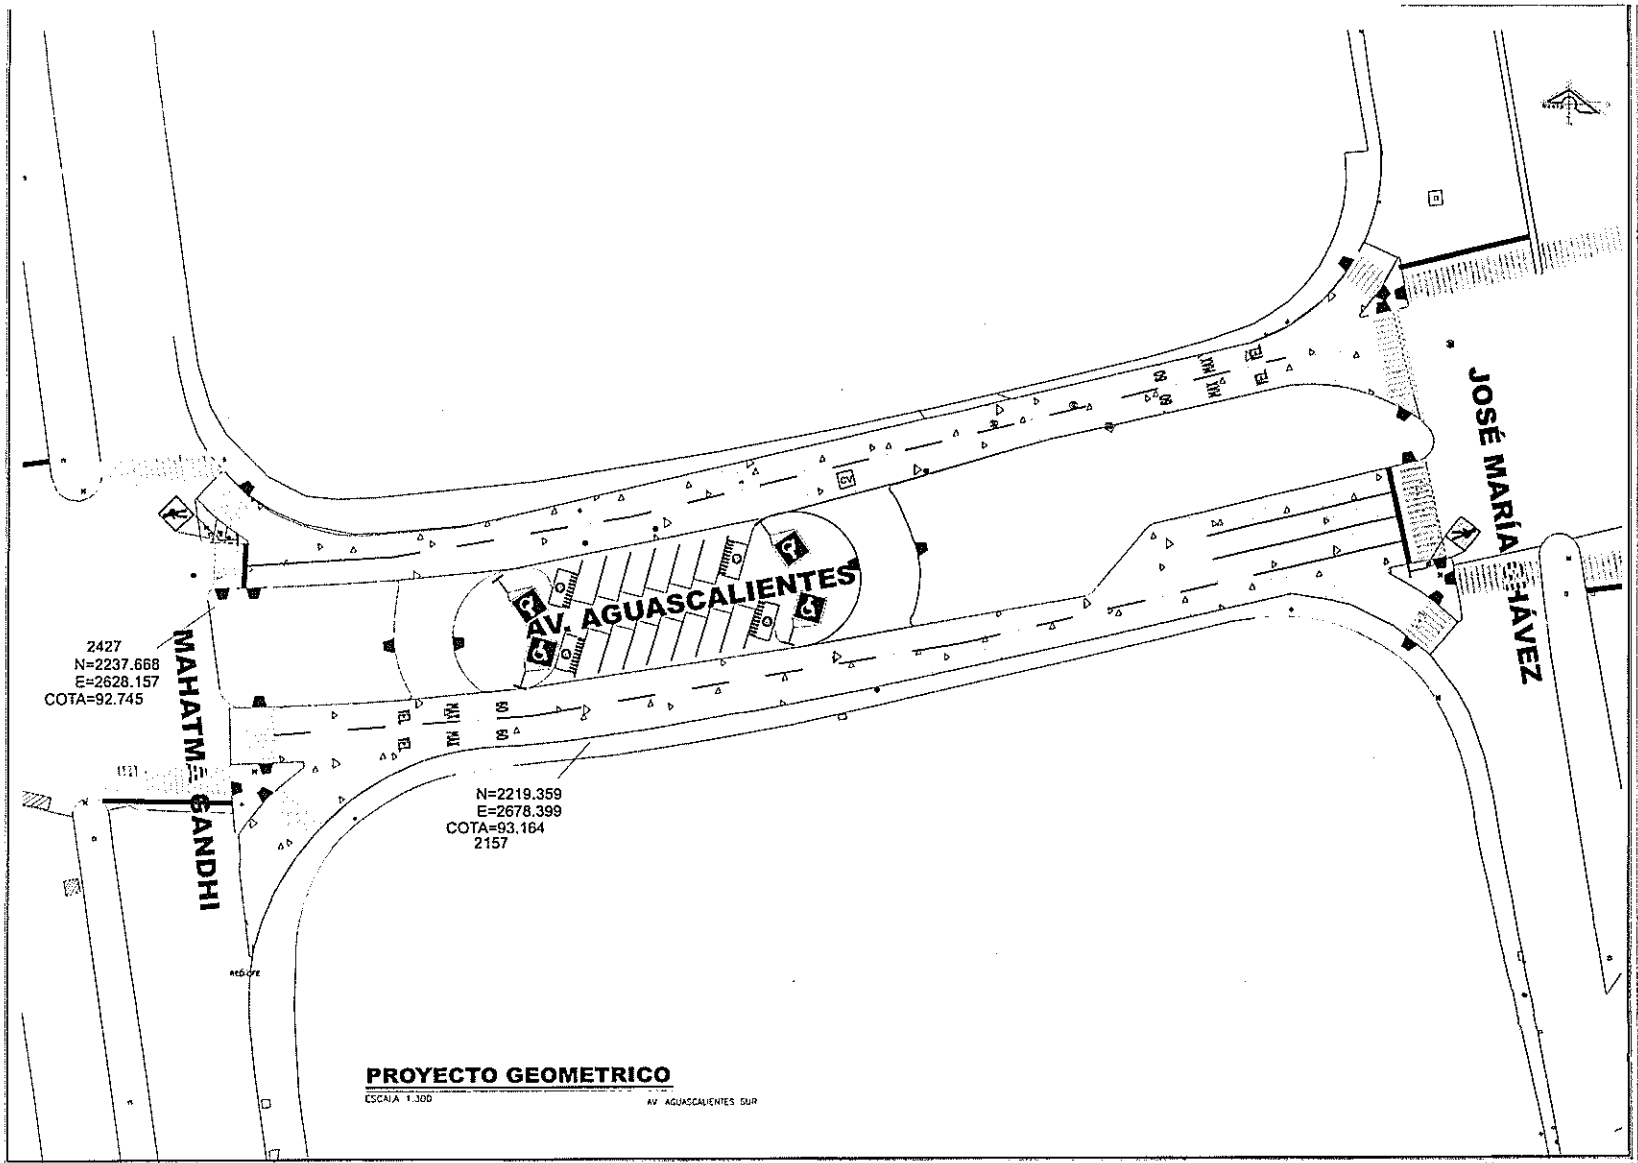


PROYECTO GEOMETRICO

ESCALA 1:300

AV. AGUASCALIENTES SUR

LOCALIZACIÓN

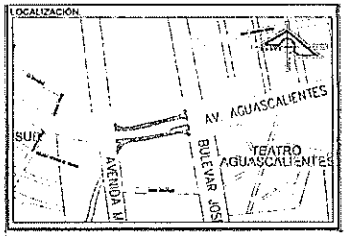

SIMBOLOGÍA

- M - 1.1 RAYA PARA CARRILES, CONTINUA SENCILLA
- M - 1.2 RAYA SEPARADORA DE CARRILES, DISCONTINUA.
- M - 3.3 RAYA PARA PROHIBICIÓN DE ESTACIONAMIENTO EN GUARNICIÓN.
- M - 11.1 FLECHA DE DIRECCIÓN DE CARRIL DE FRENTE EN PISO DE 5.0 MTS DE LARGO POR 0.75 MTS DE ANCHO.
- M - 11.1 FLECHA DE DIRECCIÓN DE CARRIL VUELTA A LA IZQUIERDA Y/O DERECHA EN PISO DE 3.45 MTS DE LARGO POR 1.30 MTS DE ANCHO.
- M - 11.1 FLECHA DE DIRECCIÓN DE CARRIL DE DOBLE CABEZA DE FRENTE EN PISO DE 5.0 MTS DE LARGO POR 0.75 MTS DE ANCHO.
- M - 11.2 FLECHA SIN CUERPO EN PISO DE 2.53 MTS DE LARGO POR 2.00 MTS DE ANCHO.
- M - 11.2 SIMBOLO PARA INDICAR LA PARADA DE AUTOBUS. LEYENDA SOLO BUS EN PISO.
- MARIMBAS PARA PASO PEATONAL: M - 7.1 RAYA PARA CRUCE DE PEATONES.

BUS SOLO

NOTA: VER LOS DETALLES DE CADA SEÑALAMIENTO EN PLANOS: "DSH-01" "DSH-02" "DSH-03" "DSV-01"

La Dirección de Planeación y Proyectos solo autoriza el proyecto ejecutivo, no es responsable de la correcta ejecución de la obra. Este documento no tiene validez si no presenta las firmas de los responsables para su autorización, así como los sellos respectivos.

PRESIDENTE MUNICIPAL
M.P.P. Leonardo Montañez Castro
ENCARGADA DE DESPACHO DE LA SOPMA
Arq. Gloria Guadalupe Castillo González

REV	FECHA	OBSERVACIONES

V°B° DE LA DEPENDENCIA

RESP. DE PROY EXTERNO		LOGO EXTERNO
CED. PROFESIONAL		
PROYECTÓ	REVISÓ	AUTORIZÓ


Dirección de Planeación y Proyectos de Obra — Secretaría de Obras Públicas

PROYECTISTA	COORDINADOR
ARQ. ALVARO DAVID MEZA CONTRERAS	ARQ. ALEJANDRO JAIME LEAL
JEFE DE DEP.	DIRECTOR
ARQ. J. JESÚS PALAFOX GONZÁLEZ	M. en ARQ. JOSÉ LUIS JIMÉNEZ GARCÍA

PROYECTO
OBRA COMPLEMENTARIA Y SEÑALETICA AV. AGUASCALIENTES SUR.
UBICACIÓN
AMBAS CALZADAS DE ENTRE AV. MAHATMA GANDHI Y AV. JOSÉ MARÍA CHÁVEZ.
CONTENIDO
PROYECTO SEÑALAMIENTO HORIZONTAL


CLAVE	No. PLANO
GEO 01	03
FECHA MAR 2022	ESCALA INDICADA
ACOTACIÓN METROS	No. EXP. E-000-22

Aguascalientes
LA CIUDAD DE TU VIDA

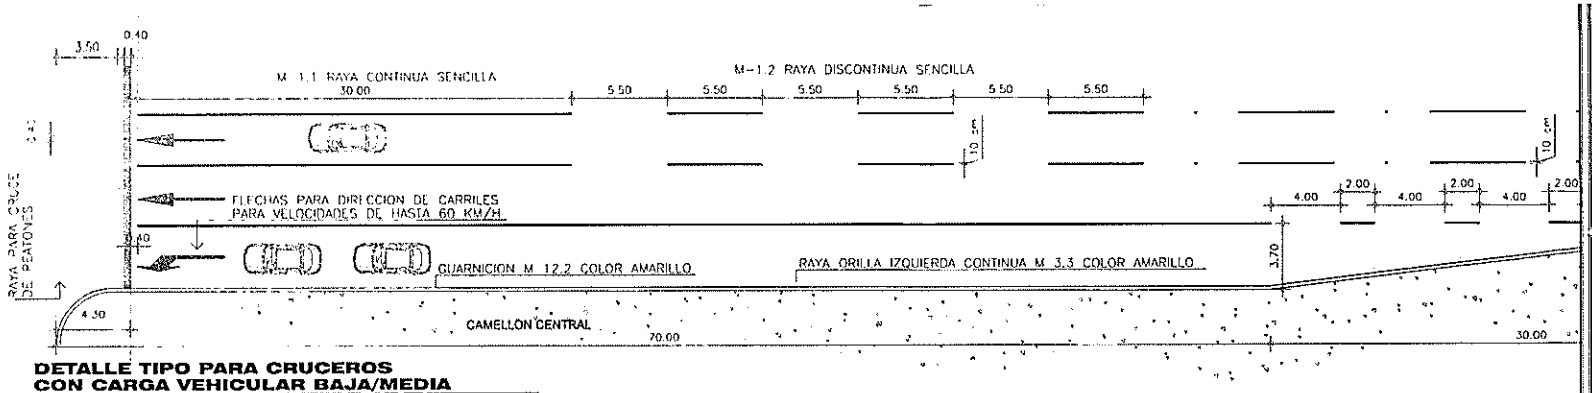


DETALLE TIPO PARA CRUCEROS CON CARGA VEHICULAR BAJA/MEDIA

COTAS: cm.

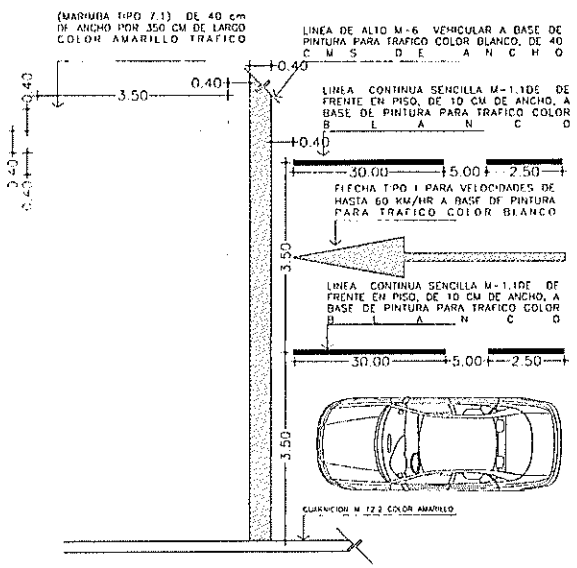

DETALLE TIPO 2


TRAZO PINTURA EN CRUCEROS SIN ESCALA

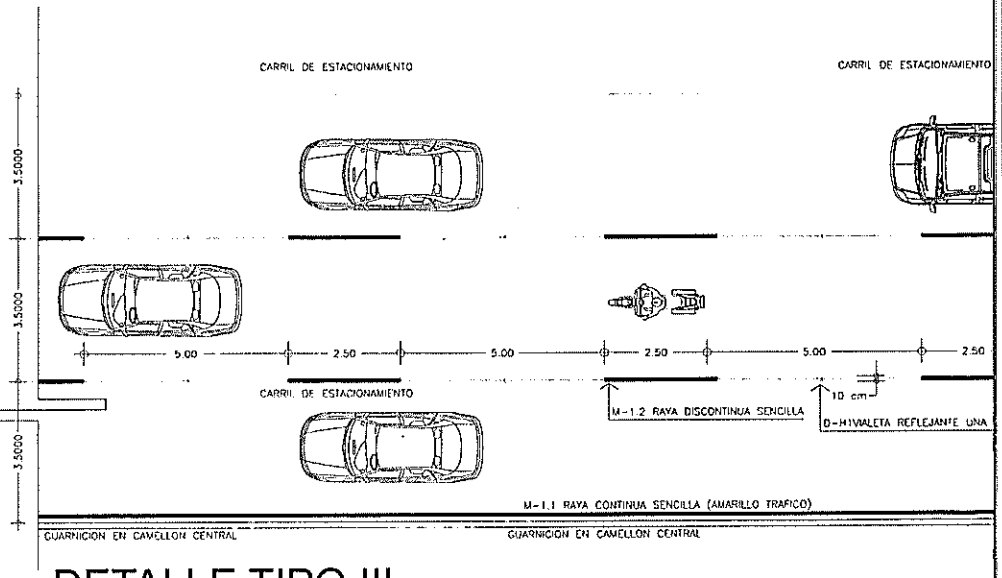

DETALLE TIPO III

PARA VELOCIDADES MENOR A 60 KM/HR S/E
LINEA DISCONTINUA DE 2.50 MTS ESPACIO 5 MTS
ESPESOR 10CM

LOCALIZACIÓN

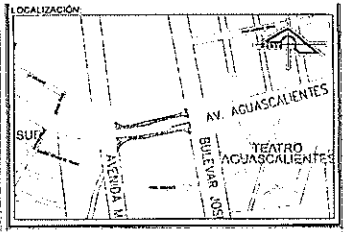

SIMBOLOGÍA

NOTA 1: En señalización horizontal suministro y aplicación de pintura termoplastica alquidalica de 120 milesimas, color amarilla o blanco, reflejante con micro esfera de vidrio en proporción según norma sct (ver detalles en planos), mca comex o similar en precio y calidad, especificaciones que cumplan con la normativa de la sct: n-cmt-5-01-001/05, n-pry-cor-10-01-002/13 aplicadas al dia de hoy, material aplicado en su estado de fusion a una temperatura minima de 204 c, la superficie de concreto o asfalto no debe presentar una temperatura menor a los 10 c, tiempo de secado en rangos de temperatura de 10 c del sustrato 2 minutos, y no mas de 10 minutos cuando el sustrato esche alrededor de 54c.

NOTA 2: Se aplicara pintura base solvente en guarniciones, en rampas para discapacitados, lineas divisorias para cajones de estacionamiento, cualquier color según se requiera y según norma s.c.t secado al tacto en 5 min y al duro en 30 min con micro esfera, marca comex o similar en precio y calidad especificaciones incluye materiales y especificaciones que cumplan con la normativa n-cmt-5-01-001/05, n-pry-cor-10-01-002/13 aplicadas al dia de hoy.

NOTA 3: Dosificación de micro esfera.
La cantidad de esferas de vidrio en la película de pintura en húmedo, según su tipo, será la que se indica en la Tabla.
TABLA 8. Cantidad de esferas de vidrio en la película de pintura en humedo.

TIPO DE PINTURA	ESPESOR DE LA PELÍCULA DE PINTURA EN HÚMEDO MM	CANTIDAD DE ESFERAS kg/m2		TIPO DE GRANULOMETRÍA
		INTEGRADAS	SEMBRADAS, MÍNIMO	
BASE SOLVENTE	0.38 ± 0.50	—	0.330	I
BASE AGUA	0.38 ± 0.50	—	0.330	I ó II
TERMOPLÁSTICA	1.5 ± 0.65	0.57 ± 0.69	0.330	II

La Dirección de Planeación y Proyectos solo autoriza el proyecto ejecutivo, no es responsable de la correcta ejecución de la obra. Este documento no tiene validez si no presenta las firmas de los responsables para su autorización, así como los sellos respectivos.

PRESIDENTE MUNICIPAL
M.P.P. Leonardo Montañez Castro
ENCARGADA DE DESPACHO DE LA SOPMA
Arq. Gloria Guadalupe Castillo González

REV	FECHA	OBSERVACIONES

Vo. Bo. DE LA DEPENDENCIA

RESP. DE PROY. EXTERNO		LOGO EXTERNO
CED. PROFESIONAL		
PROYECTO	REVISÓ	AUTORIZÓ


Dirección de Planeación y Proyectos de Obra — Secretaría de Obras Públicas


PROYECTISTA	COORDINADOR
ARQ. ALVARO DAVID MEZA CONTRERAS	ARQ. ALEJANDRO JAIME LEAL
JEFE DE DEP.	DIRECTOR
ARQ. J. JESÚS PALAFOX GONZÁLEZ	M. en ARQ. JOSÉ LUIS JIMÉNEZ GARCÍA


PROYECTO
OBRA COMPLEMENTARIA Y SEÑALETICA AV. AGUASCALIENTES SUR.
UBICACIÓN
AMBAS CALZADAS DE ENTRE AV. MAHATMA GANDHI Y AV. JOSE MARÍA CHAVEZ.
CONTENIDO
DETALLES SEÑALETICA HORIZONTAL

CLAVE	No. PLANO
DSH 01	04
FECHA: MAR 2022	ESCALA: INDICADA
ACOTACIÓN: METROS	No. EXP.: E-000-22


Aguascalientes
LA CIUDAD DE TU VIDA

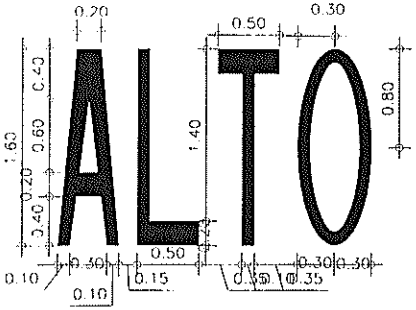

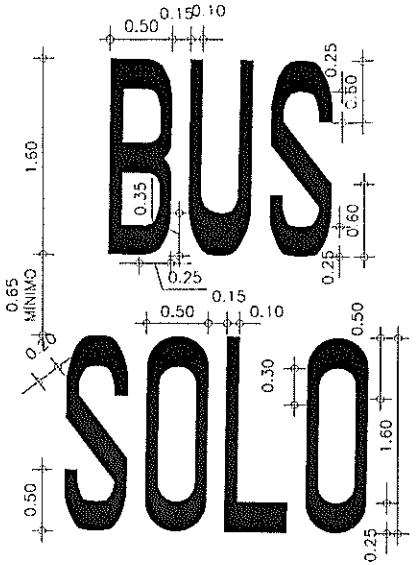

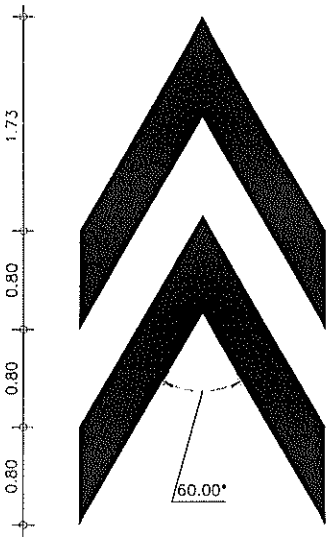

PARADA DE AUTOBUS

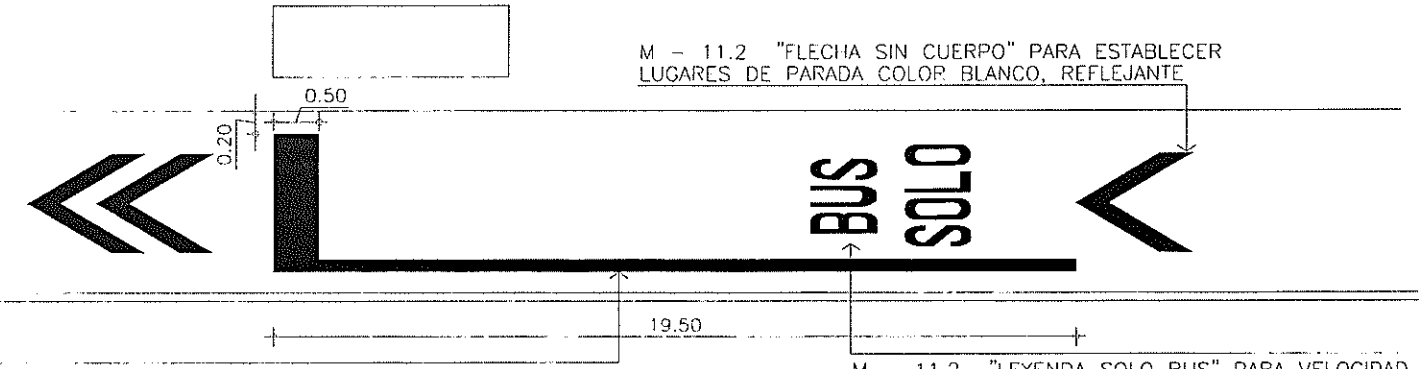

M – 11.2 "FLECHA SIN CUERPO" PARA ESTABLECER LUGARES DE PARADA COLOR BLANCO, REFLEJANTE

M – 11.4 "L INVERTIDA" PARA ESTABLECER LUGAR DE PARADA SOBRE PAVIMENTO EN VIALIDADES PARA VELOCIDAD MENOR A 60KM POR HORA


M – 11.2 "LEYENDA SOLO BUS" PARA VELOCIDAD MENOR A 60KM POR HORA DIFERENTES DIMENSIONES, COLOR BLANCO REFLEJANTE

SEÑALIZACION HORIZONTAL SOLO BUS

SIN ESCALA

COTAS: M.

LOCALIZACION

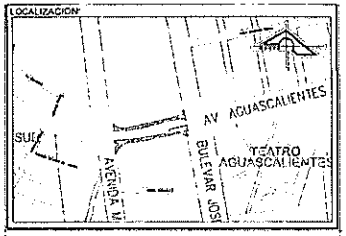

SIMBOLOGÍA

NOTA 1: En señalización horizontal suministro y aplicación de pintura termoplastica alquidalica de 120 milesimas, color amarillo y blanco, reflejante con micro esfera de vidrio en proporción según norma sct (ver detalles en planos), mca. comex o similar en precio y calidad, especificaciones que cumplan con la normativa de la sct: n-cmt-5-01-001/05, n-pry-car-10-01-002/13 aplicadas al dia de hoy, material aplicado en su estado de fusion a una temperatura minima de 204 c, la superficie de concreto o asfalto no debe presentar una temperatura menor a los 10 c, tiempo de secado en rangos de temperatura de 10 c del sustrato 2 minutos, y no mas de 10 minutos cuando el sustrato oscile alrededor de 54c

NOTA 2: Se aplicara pintura base solvente en guarniciones, en rampas para discapacitados, lineas divisorias para cajones de estacionamiento, cualquier color según se requiera y según norma s.c.t. secado al tacto en 5 min y al duro en 30 min con micro esfera, marca comex o similar en precio y calidad especificaciones. Incluye: materiales y especificaciones que cumplan con la normativa n-cmt-5-01-001/05, n-pry-car-10-01-002/13 aplicadas al dia de hoy.

NOTA 3: Dosificación de micro esfera.
La cantidad de esferas de vidrio en la película de pintura en húmedo, según su tipo, será la que se indica en la Tabla.

TABLA 8. Cantidad de esferas de vidrio en la película de pintura en humedo.

TIPO DE PINTURA	ESPESOR DE LA PELÍCULA DE PINTURA EN HÚMEDO mm	CANTIDAD DE ESFERAS kg/m2		TIPO DE GRANULOMETRÍA
		INTEGRADAS	SEMBRADAS, MÍNIMO	
BASE SOLVENTE	0.38 ± 0.50	—	0.330	2
BASE AGUA	0.38 ± 0.50	—	0.330	I ó II
TERMOPLASTICA	1.5 ± 0.89	0.57 ± 0.09	0.230	II

La Dirección de Planeación y Proyectos solo autoriza el proyecto ejecutivo, no es responsable de la correcta ejecución de la obra. Este documento no tiene validez si no presenta las firmas de los responsables para su autorización, así como los sellos respectivos.

PRESIDENTE MUNICIPAL
M.P.P. Leonardo Montañez Castro
ENCARGADA DE DESPACHO DE LA SOPMA
Arq. Gloria Guadalupe Castillo González

REV	FECHA	OBSERVACIONES

Vo. Bo. DE LA DEPENDENCIA

RESP. DE PROY EXTERNO		LOGO EXTERNO
CED. PROFESIONAL		
PROYECTO	REVISÓ	AUTORIZÓ


Dirección de Planeación y Proyectos de Obra — Secretaría de Obras Públicas

PROYECTISTA	COORDINADOR
ARQ. ALVARO DAVID MEZA CONTRERAS	ARQ. ALEJANDRO JAIME LEAL
JEFE DE DEP.	DIRECTOR
ARQ. J. JESÚS PALAFOX GONZÁLEZ	M. en ARQ. JOSÉ LUIS JIMÉNEZ GARCÍA


PROYECTO: OBRA COMPLEMENTARIA Y SEÑALETICA AV. AGUASCALIENTES SUR.
UBICACIÓN: AMBAS CALZADAS DE ENTRE AV. MAHATMA GANDHI Y AV. JOSE MARIA CHAVEZ.
CONTENIDO: DETALLES SEÑALETICA HORIZONTAL

CLAVE	No. PLANO
DSH 02	05
FECHA: MAR 2022	ESCALA: INDICADA
ACOTACIÓN: METROS	No. EXP: E-000-22


Aguascalientes
LA CIUDAD DE TU VIDA

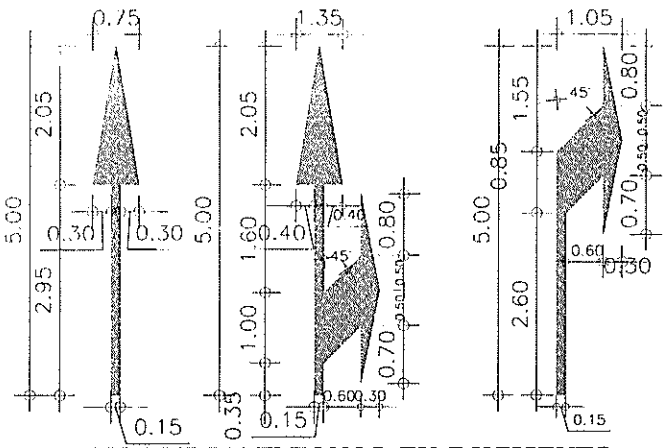

DETALLE DE FLECHAS EN PAVIMENTO
PARA VELOCIDADES HASTA DE 60KM/H
COTAS EN M

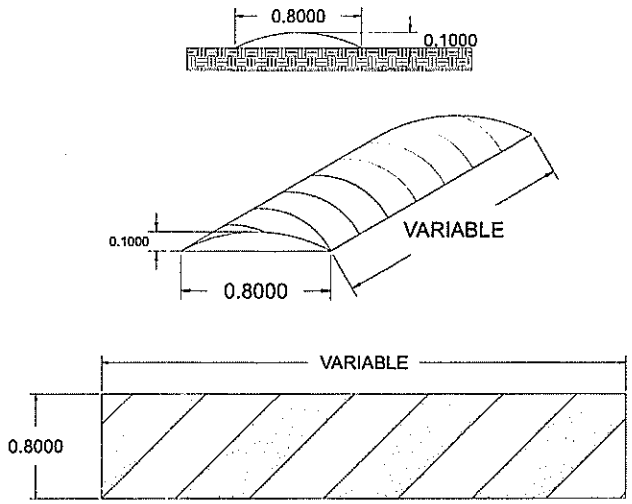


DETALLE DE TOPE VEHICULAR
COTAS EN M — SIN ESCALA

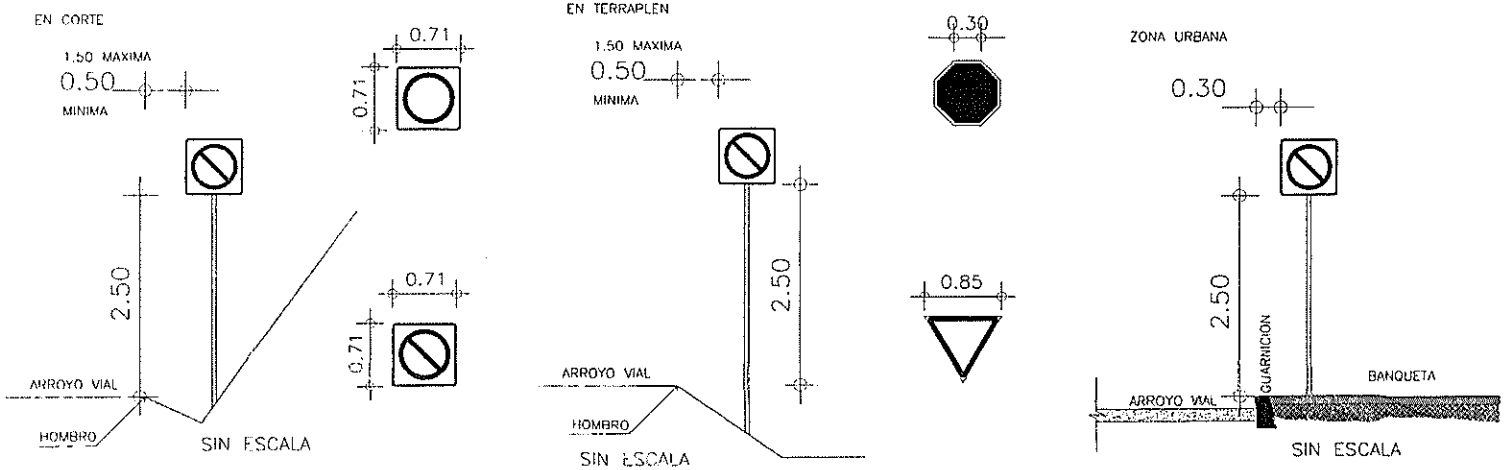

NOTA: LAS SECCIONES ESTRUCTURALES SE ENCUENTRAN EL APARTADO II.7.3. ESTRUCTURA DE SOPORTE DE SEÑALES BAJAS. DEL MANUAL DE SEÑALAMIENTO VIAL DE LA SCT

LOCALIZACIÓN:

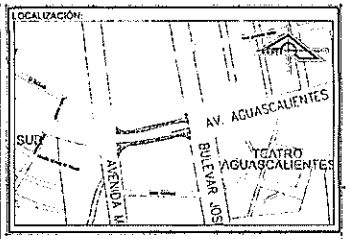

SIMBOLOGÍA

NOTA 1: En señalización horizontal suministro y aplicación de pintura termoplastica alquidalica de 120 milesimas, color amarillo o blanco, reflejante con micro esfera de vidrio en proporción según norma sct (ver detalles en planos) mca. comex o similar en precio y calidad, especificaciones que cumplan con la normativa de la sct: n-cmt-5-01-001/05, n-pry-car-10-01-002/13 aplicados al dia de hoy, material aplicado en su estado de fusión a una temperatura mínima de 204 c, la superficie de concreto o asfalto no debe presentar una temperatura menor a los 10 c. tiempo de secado en rangos de temperatura de 10 c del sustrato 2 minutos, y no mas de 12 minutos cuando el sustrato esste alrededor de 54c.

NOTA 2: Se aplicara pintura base solvente en guarniciones, en rampas para discapacitados, lineas divisorias para cajones de estacionamiento cualquier color según se requiera y según norma s.c.t. secado al tacto en 5 min y al duro en 30 min con micro esfera marca comex o similar en precio y calidad especificaciones incluye: materiales y especificaciones que cumplan con la normativa n-cmt-5-01-001/05, n-pry-car-10-01-002/13 aplicados al dia de hoy.

NOTA 3: Dosificación de micro esfera.
La cantidad de esferas de vidrio en la película de pintura en Húmedo, según su tipo, será la que se indica en la Tabla.
TABLA 2: Cantidad de esferas de vidrio en la película de pintura en humedo.

TIPO DE PINTURA	ESPESOR DE LA PELÍCULA DE PINTURA EN HÚMEDO MM	CANTIDAD DE ESFERAS kg/m2		TIPO DE GRANULOMETRÍA
		INTEGRADAS	SEMBRADAS, MÍNIMO	
BASE SOLVENTE	0.38 a 0.50	—	0.330	I
BASE AGUA	0.38 a 0.50	—	0.330	I ó II
TERMOPLASTICA	1.5 a 2.0	0.57 a 0.65	0.330	II

La Dirección de Planeación y Proyectos solo autoriza el proyecto ejecutivo, no es responsable de la correcta ejecución de la obra. Este documento no tiene validez si no presenta las firmas de los responsables para su autorización, así como los sellos respectivos.

PRESIDENTE MUNICIPAL
M.P.P. Leonardo Montañez Castro
ENCARGADA DE DESPACHO DE LA SOPMA
Arq. Gloria Guadalupe Castillo González

REV	FECHA	OBSERVACIONES

V.o. Bo. DE LA DEPENDENCIA

RESP. DE PROY EXTERNO		LOGO EXTERNO
CED. PROFESIONAL		
PROYECTO	REVISÓ	AUTORIZÓ

Dirección de Planeación y Proyectos de Obra — Secretaría de Obras Públicas

PROYECTISTA	COORDINADOR
ARQ. ALVARO DAVID MEZA CONTRERAS	ARQ. ALEJANDRO JAIME LEAL
JEFE DE DEP.	DIRECTOR
ARQ. J. JESÚS PALAFOX GONZALEZ	M. en ARQ. JOSÉ LUIS JIMÉNEZ GARCÍA

PROYECTO
OBRA COMPLEMENTARIA Y SEÑALETICA AV. AGUASCALIENTES SUR.
UBICACIÓN
AMBAS CALZADAS DE ENTRE AV. MAHATMA GANDHI Y AV. JOSÉ MARÍA CHÁVEZ.
CONTENIDO
DETALLES SEÑALETICA VERTICAL

CLAVE	No. PLANO
DSV 01	07
FECHA MAR 2022	ESCALA INDICADA
ACOTACIÓN METROS	No. EXP. E-000-22

Aguascalientes
LA CIUDAD DE TU VIDA

SEÑALES RESTRICTIVAS

SIMBOLO	CLAVE	DESCRIPCIÓN	DIMENSIÓN (cm)	UNIDAD	COLOR	CANTIDAD
	SR-6	ALTO	30 X LADO	PZA	ROJO REFLEJANTE	0
	SR-7	CEDA EL PASO	85 X LADO	PZA	BLANCO REFLEJANTE	0
	SR-9	VELOCIDAD 50 KM/H	71 X 71	PZA	BLANCO REFLEJANTE CON ANILLO ROJO REFLEJANTE	0
	SR-9	VELOCIDAD 60 KM/H	71 X 71	PZA	BLANCO REFLEJANTE CON ANILLO ROJO REFLEJANTE	0
	SR-21	ESTACIONAMIENTO PERMITIDO	71 X 71	PZA	BLANCO REFLEJANTE CON ANILLO ROJO REFLEJANTE	0
	SR-22	PROHIBIDO ESTACIONARSE	71 X 71	PZA	BLANCO REFLEJANTE CON ANILLO ROJO REFLEJANTE	0

SEÑALES PREVENTIVAS

SIMBOLO	CLAVE	DESCRIPCIÓN	DIMENSIÓN (cm)	UNIDAD	COLOR	CANTIDAD
	SP-32	PEATONES	71 X 71	PZA	AMARILLO REFLEJANTE	2
	SP-33	ESCOLARES	71 X 71	PZA	VERDE LIMON FLUORESCENTE REFLEJANTE	0
	SP-41	REDUCTOR DE VELOCIDAD	71 X 71	PZA	AMARILLO REFLEJANTE	0
	SP-19I	SALIDA A LA IZQUIERDA	71 X 71	PZA	AMARILLO REFLEJANTE	0
	SP-19	SALIDA A LA DERECHA	71 X 71	PZA	AMARILLO REFLEJANTE	0


SEÑALES TURÍSTICAS Y DE SERVICIOS

SIMBOLO	CLAVE	DESCRIPCIÓN	DIMENSIÓN (cm)	UNIDAD	COLOR	CANTIDAD
	SIS-19	PARADERO DE AUTOBUS	71 X 71	PZA	AZÚL REFLEJANTE	0
	SIS-11	GASOLINERA	71 X 71	PZA	AZÚL REFLEJANTE	0
	SIS-51	ZONA O INSTALACIONES PARA DISCAPACITADOS	71 X 71	PZA	AZÚL REFLEJANTE	4
	SIS-64	ZONA PEATONAL	71 X 71	PZA	AZÚL REFLEJANTE	0

OBRAS Y DISPOSITIVOS DIVERSOS

SIMBOLO	CLAVE	DESCRIPCIÓN	DIMENSIÓN (cm)	UNIDAD	COLOR	CANTIDAD
	OD-5I	ZONA PEATONAL	71 X 71	PZA	AMARILLO REFLEJANTE	0
	OD-5D	ZONA PEATONAL	71 X 71	PZA	AMARILLO REFLEJANTE	0
	OD-5	ZONA PEATONAL	71 X 71	PZA	AMARILLO REFLEJANTE	0

LOCALIZACIÓN

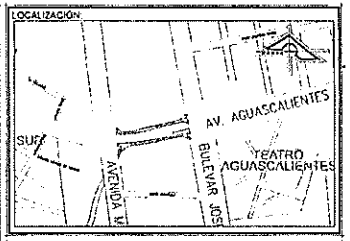

SIMBOLOGÍA

La Dirección de Planeación y Proyectos solo autoriza el proyecto ejecutivo, no es responsable de la correcta ejecución de la obra. Este documento no tiene validez si no presenta las firmas de los responsables para su autorización, así como los sellos respectivos.

PRESIDENTE MUNICIPAL
M.P.P. Leonardo Montañez Castro
ENCARGADA DE DESPACHO DE LA SOPMA
Arq. Gloria Guadalupe Castillo González

REV	FECHA	OBSERVACIONES

Vo. Bo. DE LA DEPENDENCIA

RESP DE PROY. EXTERNO		LOGO EXTERNO
CED. PROFESIONAL		
PROYECTÓ	REVISÓ	AUTORIZÓ


Dirección de Planeación y Proyectos de Obra — Secretaría de Obras Públicas

PROYECTISTA	COORDINADOR
ARQ. ALVARO DAVID MEZA CONTRERAS	ARQ. ALEJANDRO JAIME LEAL
JEFE DE DEP.	DIRECTOR
ARQ. J. JESÚS PALAFOX GONZÁLEZ	M. en ARQ. JOSÉ LUIS JIMÉNEZ GARCÍA

PROYECTO
OBRA COMPLEMENTARIA Y SEÑALETICA AV. AGUASCALIENTES SUR.
UBICACIÓN
AMBAS CALZADAS DE ENTRE AV. MAHATMA GANDHI Y AV. JOSÉ MARÍA CHAVEZ.
CONTENIDO
DETALLES SEÑALETICA VERTICAL

CLAVE	No. PLANO
DSV 02	08
FECHA MAR 2022	ESCALA INDICADA
ACOTACIÓN METROS	No. EXP. E-000-22

Aguascalientes
LA CIUDAD DE TU VIDA

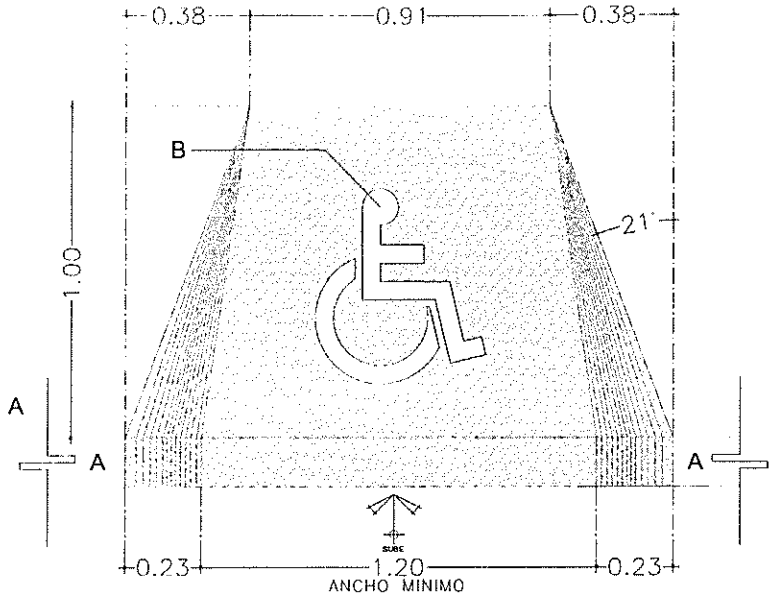


DETALLE DE LOGOTIPO ''A'' EN RAMPA

VISTA EN PLANTA S/E

A SUMINISTRO Y APLICACIÓN DE PINTURA BASE SOLVENTE COLOR AZUL (PANTONE 294) EN RAMPAS PARA DISCAPACITADOS


B SUMINISTRO Y APLICACIÓN DE LOGOTIPO "A" (SILLA DE RUEDAS) EN PINTURA BASE SOLVENTE COLOR BLANCO EN RAMPAS PARA DISCAPACITADOS TAMAÑO Y DISEÑO SEGÚN PLANOS.

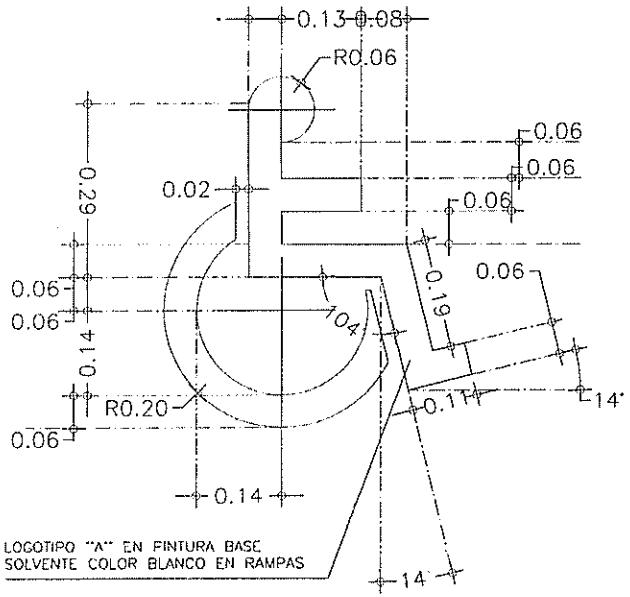

LOGOTIPO "A" EN PINTURA BASE SOLVENTE COLOR BLANCO EN RAMPAS

DETALLE DE LOGOTIPO ''A'' EN RAMPA

VISTA EN PLANTA S/E

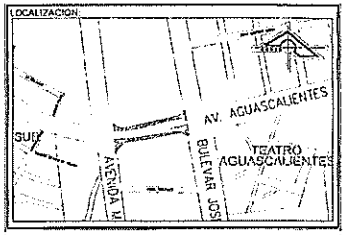

SIMBOLOGÍA

NOTA 1: En señalización horizontal suministro y aplicación de pintura termoplástica alquidálica de 120 milésimas, color amarillo o blanco, reflejante con micro esfera de vidrio en promoción según norma sct (ver detalles en planos), mca. comex o similar en precio y calidad, especificaciones que cumplan con la normativa de la sct: n-cmt-5-01-001/05, n-pry-car-10-01-002/13 aplicadas al día de hoy, material aplicado en su estado de fusión a una temperatura mínima de 204 c, la superficie de concreto o asfalto no debe presentar una temperatura menor a los 10 c, tiempo de secado en rangos de temperatura de 10 c del sustrato 2 minutos, y no mas de 10 minutos cuando el sustrato esclo alrededor de 54c.

NOTA 2: Se aplicara pintura base solvente en guarniciones, en rampas para discapacitados, líneas divisorias para cajones de estacionamiento, cualquier color según se requiera y según norma s.c.t. secado al tacto en 5 min y el duro en 30 min con micro esfera, marca comex o similar en precio y calidad especificaciones. incluye: materiales y especificaciones que cumplan con la normativa n-cmt-5-01-001/05, n-pry-car-10-01-002/13 aplicadas al día de hoy.

NOTA 3: Dosificación de micro esfera.
La cantidad de esferas de vidrio en la película de pintura en húmedo, según su tipo, será la que se indica en la tabla.
TABLA 8. Cantidad de esferas de vidrio en la película de pintura en húmedo.

TIPO DE PINTURA	ESPESOR DE LA PELÍCULA DE PINTURA EN HÚMEDO MM	CANTIDAD DE ESFERAS kg/m2		TIPO DE GRANULOMETRÍA
		INTEGRADAS	SEMBRADAS, MÍNIMO	
BASE SOLVENTE	0.38 ± 0.50	—	0.330	I
BASE AGUA	0.38 ± 0.50	—	0.330	I ó II
TERMOPLASTICA	1.5 ± 0.65	0.57 ± 0.09	0.330	II

La Dirección de Planeación y Proyectos solo autoriza el proyecto ejecutivo, no es responsable de la correcta ejecución de la obra. Este documento no tiene validez si no presenta las firmas de los responsables para su autorización, así como los sellos respectivos.

PRESIDENTE MUNICIPAL
M.P.P. Leonardo Montañez Castro
ENCARGADA DE DESPACHO DE LA SOPMA
Arq. Gloria Guadalupe Castillo González

REV	FECHA	OBSERVACIONES

V°. Bo. DE LA DEPENDENCIA

RESP. DE PROY. EXTERNO		LOGO EXTERNO
CED. PROFESIONAL		
PROYECTÓ	REVISÓ	AUTORIZÓ


Dirección de Planeación y Proyectos de Obra
Secretaría de Obras Públicas

PROYECTISTA	COORDINADOR
ARQ. ALVARO DAVID MEZA CONTRERAS	ARQ. ALEJANDRO JAIME LEAL
JEFE DE DEP.	DIRECTOR
ARQ. L. JESÚS PALAFOX GONZÁLEZ	M. en ARQ. JOSÉ LUIS JIMÉNEZ GARCÍA

PROYECTO
OBRA COMPLEMENTARIA Y SEÑALETICA AV. AGUASCALIENTES SUR.
UBICACIÓN
AMBAS CALZADAS DE ENTRE AV. MAHATMA GANDHI Y AV. JOSÉ MARÍA CHÁVEZ.
CONTENIDO
DETALLES SEÑALETICA DISCAPACITADOS


CLAVE	No. PLANO
DSD 01	12
FECHA MAR 2022	ESCALA INDICADA
ACOTACIÓN METROS	No. EXP. E-000-22

Aguascalientes
LA CIUDAD DE TU VIDA

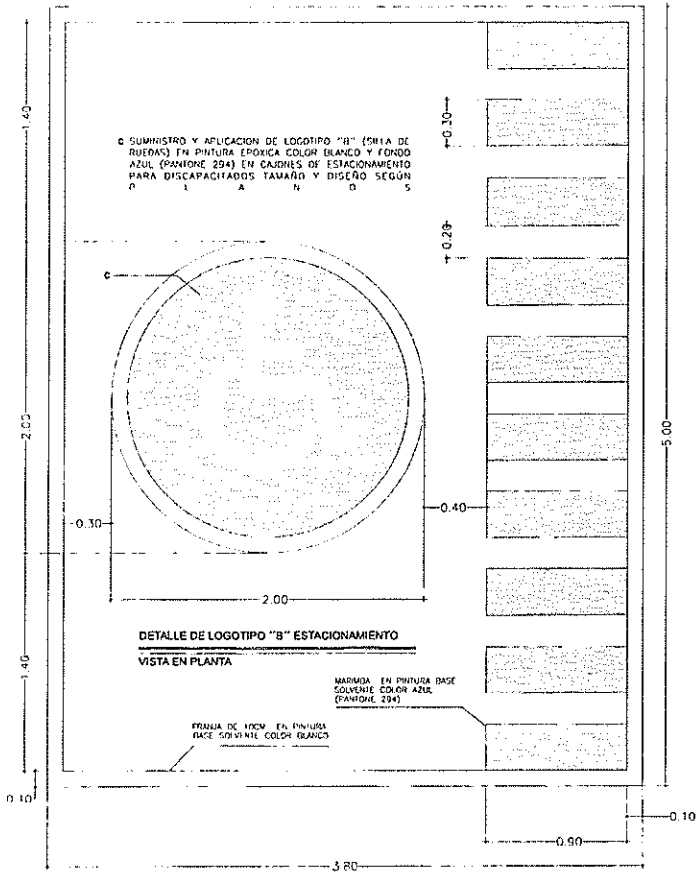

TRAZO DE ESTACIONAMIENTO PARA VEHICULOS DE PERSONAS CON DISCAPACIDAD.


VISTA EN PLANTA S/E

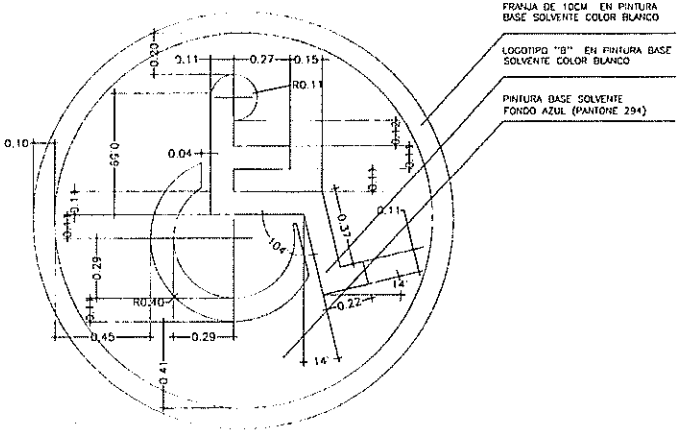

DETALLE DE LOGOTIPO "B" ESTACIONAMIENTO

VISTA EN PLANTA S/E

LOCALIZACION:

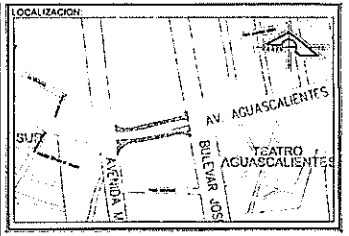

SIMBOLOGÍA

NOTA 1: En señalización horizontal suministro y aplicación de pintura termoplastica alquidalica de 120 milesimas, color amarillo o blanco, reflejante con micro esfera de vidrio en proporción según norma sct (ver detalles en planos), mca. comex o similar en precio y calidad, especificaciones que cumplan con la normativa de la sct. n-cmt-5-01-001/05, n-pry-cor-10-01-002/13 aplicadas al dia de hoy, material aplicado en su estado de fusion a una temperatura minima de 204 c. la superficie de concreto o asfalto no debe presentar una temperatura menor a los 10 c, tiempo de secado en rangos de temperatura de 10 c del sustrato 2 minutos, y no mas de 10 minutos cuando el sustrato este alrededor de 5ec.

NOTA 2: Se aplicara pintura base solvente en guarniciones, en rampas para discapacitados, lineas divisorias para cajones de estacionamiento, cualquier color según se requiera y según norma s.c.t. secado al tacto en 5 min y al duro en 20 min con micro esfera, marca comex o similar en precio y calidad especificaciones incluye: materiales y especificaciones que cumplan con la normativa n-cmt-5-01-001/05, n-pry-cor-10-01-002/13 aplicadas al dia de hoy

NOTA 3: Dosificación de micro esfera
La cantidad de esferas de vidrio en la película de pintura en húmeda, según su tipo, será la que se indica en la Tabla.

TABLA 8. Cantidad de esferas de vidrio en la película de pintura en humedo.

TIPO DE PINTURA	ESPESOR DE LA PELÍCULA DE PINTURA EN HÚMEDO MM	CANTIDAD DE ESFERAS kg/m2		TIPO DE GRANULOMETRÍA
		INTEGRADAS	SEMBRADAS, MÍNIMO	
BASE SOLVENTE	0.38 a 0.50	---	0.330	I
BASE AGUA	0.38 a 0.50	---	0.330	I & II
TERMOPLASTICA	1.5 a 0.63	0.57 a 0.69	0.330	II

La Dirección de Planeación y Proyectos solo autoriza el proyecto ejecutivo, no es responsable de la correcta ejecución de la obra. Este documento no tiene validez si no presenta las firmas de los responsables para su autorización, así como los sellos respectivos.

PRESIDENTE MUNICIPAL
M.P.P. Leonardo Montañez Castro
ENCARGADA DE DESPACHO DE LA SOPMA
Arq. Gloria Guadalupe Castillo González

REV	FECHA	OBSERVACIONES

Vo. Bo. DE LA DEPENDENCIA

RESP. DE PROY. EXTERNO		LOGO EXTERNO
CED. PROFESIONAL		
PROYECTÓ	REVISÓ	AUTORIZÓ

Dirección de Planeación y Proyectos de Obra — Secretaría de Obras Públicas

PROYECTISTA	COORDINADOR
ARQ. ALVARO DAVID MEZA CONTRERAS	ARQ. ALEJANDRO JAIME LEAL
JEFE DE DEP.	DIRECTOR
ARQ. J. JESÚS PALAFOX GONZÁLEZ	M. en ARQ. JOSÉ LUIS JIMÉNEZ GARCÍA

PROYECTO	OBRA COMPLEMENTARIA Y SEÑALETICA AV. AGUASCALIENTES SUR.
UBICACIÓN	AMBAS CALZADAS DE ENTRE AV. MAHATMA GANDHI Y AV. JOSÉ MARÍA CHÁVEZ.
CONTENIDO	DETALLES SEÑALETICA DISCAPACITADOS

CLAVE	No. PLANO
DSD 03	14
FECHA	ESCALA
MAR 2022	INDICADA
ACOTACIÓN	No. EXP.
METROS	E-000-22

Aguascalientes
LA CIUDAD DE TU VIDA