Aguascalientes
LA CIUDAD DE TU VIDA

Dirección de Programación Presupuestal
Núm. Oficio AMPP/0673/22
Aguascalientes, Ags. 29 de Diciembre del 2022
Asunto: Validación de Expediente Técnico

C.P. SERGIO ARTURO LOZANO GONZÁLEZ
SECRETARIO DE FINANZAS MUNICIPALES
P R E S E N T E

Con fundamento en los artículos 17 fracción XV, 60 fracción XVI y 76 fracción VI del Reglamento del Sistema Integral de Desarrollo Municipal y del Instituto Municipal de Planeación y Evaluación de Aguascalientes, hago referencia al oficio SOPMA/3081/2022 recibido por este Instituto el día 29 de Diciembre del 2022 por parte de la Secretaría de Obras Públicas Municipales, mediante el cual remiten el expediente técnico original de la siguiente obra para su análisis, registro y priorización, conforme al Programa Anual de Obra Pública y Programas Sociales para el ejercicio presupuestal 2022:

DEPENDENCIA EJECUTORA:	SOPMA
NOMBRE DE LA OBRA O PROYECTO:	CONSTRUCCIÓN DE SOBRECARPETA ASFÁLTICA
UBICACIÓN:	CALLE GUZMÁN, TRAMO: ENTRE CALLE JOSÉ MARÍA MORELOS Y PAVÓN Y CALLE CONDELL, ZONA CENTRO, AGUASCALIENTES, AGS.
FONDO DE INVERSIÓN:	FONDO DE INFRAESTRUCTURA SOCIAL MUNICIPAL Y DE LAS DEMARCACIONES TERRITORIALES DEL DISTRITO FEDERAL
IMPORTE:	$339,494.79 (ET FINAL)
No. DE OBRA:	2022-FISMDF-0141-11-0102
MODALIDAD DE EJECUCIÓN:	CONTRATO
EJE:	MUNICIPIO SOBRESALIENTE
ESTRATEGIA:	OBRA PÚBLICA INTELIGENTE
POLITICA:	5.8.1.REHABILITACIÓN Y MANTENIMIENTO VIALIDADES, CAMINOS, CALLES, ÁREAS DE TERRACERÍA Y CAUCES (C

Al respecto, hago de su conocimiento que dicho expediente ha sido analizado en su integración técnica y documental, con base en el artículo 168 fracción I del Reglamento de la Ley de Obras Públicas y Servicios Relacionados para el Estado de Aguascalientes y sus Municipios.

Asimismo, le comento que este Instituto valida dicha obra acorde a lo establecido en los artículos 14, 22 párrafo segundo y 23 de la Ley de Obras Públicas y Servicios Relacionados para el Estado de Aguascalientes y sus Municipios, la cual se encuentra alineada al Plan de Desarrollo Municipal vigente, para dar cumplimiento a las metas establecidas en el mismo, y a los Lineamientos Generales para la Operación de este Fondo de Inversión, toda vez que la misma cuente con la autorización del CODEMUN. De igual manera, se hace de su conocimiento que deberá cumplir con lo establecido en los ordenamientos aplicables en lo que respecta al ejercicio, control e información de los recursos de este Fondo. Cabe hacer mención que los recursos solicitados para este proyecto de inversión, estarán sujetos a la disponibilidad presupuestal para el presente ejercicio fiscal que determine la Secretaría a su digno cargo. Sin otro particular por el momento, le envío un cordial saludo.

A T E N T A M E N T E

ARQ. AUSTRIA GABRIELA DÁVILA DE LA LLAVE
DIRECTORA GENERAL DEL IMPLAN

SEDR/ CAAR / JDBC
C.c.p. I.C. ING. MIGUEL ÁNGEL HUIZAR BOTELLO .- Secretaría de Obras Públicas Municipales .Para su conocimiento.
C.c.p. Archivo.

Instituto Municipal de Planeación y Evaluación de Aguascalientes

Antonio Acevedo Escobedo 103 A. Col. Centro
Aguascalientes. Ags. C.P. 20000

(449) 9101010 Ext. 3117

www.implanags.gob.mx

GOBIERNO MUNICIPAL DE AGUASCALIENTES

INSTITUTO MUNICIPAL DE PLANEACION

IMPLAN

ANÁLISIS INTEGRAL DE EXPEDIENTE TÉCNICO

No. DE OBRA (PAOP 2020):	2022-FISMDF-0141-11-0102	REGISTRO No.	309
OFICIO DE VALIDACIÓN:	AMPP/0673/22	FECHA RECIBIDO PARA REVISIÓN:	29 de Diciembre del 2022
PROGRAMA:	URBANIZACION MUNICIPAL	LOCALIDAD O COLONIA:	ZONA CENTRO
SUB-PROGRAMA:	0411- Calles y Caminos	DELEGACIÓN:	Centro Oriente
DEPENDENCIA:	Secretaría de Obras Públicas Municipales	MOD. DE EJECUCIÓN:	CONTRATO
NOMBRE DE LA OBRA:	CONSTRUCCIÓN DE SOBRECARPETA ASFÁLTICA, CALLE GUZMÁN, TRAMO: ENTRE CALLE JOSÉ MARÍA MORELOS Y PAVÓN Y CALLE CONDELL		
FUENTE DE FINANCIAMIENTO:	FONDO DE INFRAESTRUCTURA SOCIAL MUNICIPAL Y DE LAS DEMARCACIONES TERRITORIALES DEL DISTRITO FEDERAL, FISMDF		
INVERSIÓN:	$339,494.79	CLASIFICACIÓN DE OBRA:	BIENES DE DOMINIO PUBLICA

TOTAL	FEDERAL	ESTATAL	MUNICIPAL	BENEFICIARIOS	OTROS	DIFERENCIA ENTRE MOD.
$339,494.79	$339,494.79	0.00	0.00	0.00	0.00	*$842.61*

TIPO DE EXPENDIENTE:	ET FINAL	AÑO: 2023	AÑO:	AÑO:		
AVANCES:	Financiero: 100 %		Físico: 100 %			
FECHA DE INICIO:	10 de Diciembre del 2022	FECHA DE TÉRMINO:	19 de Diciembre del 2022	REGISTRO SIMA:	141	

CHEK LIST DE LOS ANEXOS DEL EXPEDIENTE TÉCNICO

CÉDULA DE REGISTRO DE OBRA	✓
DICTAMEN DE FACTIBILIDAD	✓
MEMORIA DESCRIPTIVA	✓
PRESUPUESTO BASE	✓
FACTIBILIDAD VERIFICADA EN CAMPO	✓
CROQUIS DE UBICACIÓN (MACRO)	✓
CROQUIS DE UBICACIÓN (MACRO)	✓
PROGRAMA DE OBRA Y MONTOS MENSUALES	✓
PLANOS O ESTUDIOS TÉCNICOS	✓
PADRÓN DE BENEFICIARIOS	N/A
ACTA DE ACEPTACIÓN DEL PROYECTO	N/A
DICTAMEN DE IMPACTO AMBIENTAL	N/A
CONVENIO DE CONCERTACIÓN	N/A
ACTA CONSTITUTIVA	N/A

METAS		BENEFICIARIOS		PERIODO DE EJECUCION		OBRA PROPUESTA		CLAVE SISCO
UNIDAD DE MEDIDA	CANT	TIPO DE BENEFICIARIOS	CANTIDAD	FECHA DE INICIO	FECHA DE TERMINO	CONCEPTO	JORNALES A GENERAR	
OBRA	1	Personas	110	2022-12-10	2022-12-19	Sobrecarpeta Asfáltica	882	2399

INCLUIDO EN PLAN DE DESARROLLO MUNICIPAL Y EL PROGRAMA ANUAL DE OBRA PÚBLICA

OBSERVACIONES:

SIN OBSERVACIONES

RECIBIO: ING. JOSÉ DAVID BURGUETE CLAUSTRO
Analista de Programación e Inversión de Obra Pública

29 de Diciembre del 2022
Fecha de validación

29 de Diciembre del 2022
Fecha de validación Expediente

PROCEDE Si ✓ No

H. AYUNTAMIENTO CONSTITUCIONAL DEL MUNICIPIO DE AGUASCALIENTES 2021-2024

AYUNTAMIENTO DE AGUASCALIENTES

CEDULA DE REGISTRO POR OBRA

Aguascalientes LA CIUDAD DE TU VIDA

050400-001E00E05-05-2-2-1-00-1-E-0510-0-17-0141-21-2502-6144

2022-FISMDF-0141-0411102-077	Obra **CONSTRUCCIÓN DE SOBRECARPETA ASFÁLTICA CALLE GUZMÁN**
Tipo DEFINITIVO I 2022 Folio SISCO **2399**	Ubic. TRAMO: ENTRE CALLE JOSÉ MARÍA MORELOS Y PAVÓN Y CALLE CONDELL, CENTRO Zona , Deleg. Zona Centro

Ent. Ejecutora : **050400001E00E05**

Eje: **05**	MUNICIPIO SOBRESALIENTE
Finalidad: **2**	DESARROLLO SOCIAL
Función: **2**	VIVIENDA Y SERVICIOS A LA COMUNIDAD
Subfunción: **1**	URBANIZACIÓN
Tema: **00**	SIN TEMA
Cuenta del Gasto **1**	GASTO PROGRAMABLE
Clasif. Programatica: **E**	PRESTACIÓN DE SERVICIOS PÚBLICOS
Programa: **0510**	Movilidad Urbana
SubPrograma: **0**	SUBPROGRAMA GENÉRICO
Proyecto: **17**	
Tipo de Gasto: **21**	GASTO INVERSIÓN / OBRA PÚBLICA

I N V E R S I O N 2022

Municipal	2502	FONDO PARA LA INFRAESTRUCTURA SOCIAL MUNICIPAL Y DE LAS DEMARCACIONES TERRITORIALES DEL DISTRITO FEDERAL 2022	$339,494.79

Folio SIMA 141 Total $339,494.79

M E T A S

Unidad de Medida	Cantidad	Descripción
M2	467.92	SOBRECARPETA ASFÁLTICA CONSTRUCCIÓN DE SOBRECARPETA ASFÁLTICA CALLE GUZMÁN

Inversión Ejercida Total al 31 de Diciembre de 2021 $0.00

Avance Fisico Acumulado al 31 de Diciembre de 2021

Avance Fisico Acumulado Programado al 31 de Diciembre de 2022 100 %

Fecha de Inicio 10 Dic 2022 Fecha de Terminación 19 Dic 2022

Jornales a Generar en 2022 882

Modalidad de ejecución CONTRATO

Clasificación de la Obra Bienes de Dominio Público

Registro del Patrimonio: Obras del dominio público

OBRAS PÚBLICAS

Av. Aguascalientes Sur No. 2615
Fracc. Jardines de las Fuentes,
Aguascalientes, Ags. C.P. 20278

(449) 9 78 92 01, 06, 09

www.ags.gob.mx

GENERALES

Nombre del Proyecto : CONSTRUCCIÓN DE SOBRECARPETA ASFÁLTICA CALLE GUZMÁN

TRAMO: ENTRE CALLE JOSÉ MARÍA MORELOS Y PAVÓN Y CALLE CONDELL, CENTRO Zona , Deleg. Zona Centro

Programa : 04 URBANIZACION MUNICIPAL

Subprograma : 11 Calles y caminos (2.- Construcción; 02- Concreto Asfáltico)

Clave del Municipio : AGUASCALIENTES

Localidad :

Barrio, Colonia o Ejido : CENTRO Zona

Tipo de Obra :

DESCRIPCIÓN DEL PROYECTO:

CONSTRUCCIÓN DE SOBRECARPETA ASFÁLTICA CALLE GUZMÁN

PRELIMINARES Y DEMOLICIONES 273.16 m2
BACHEO PROFUNDO 3.90 m3
SOBRECARPETA ASFÁLTICA 467.92 m2
OBRA COMPLEMENTARIA 1.00 obra
LIMPIEZAS 273.16 m2
GUARNICIONES 12.40 m2
BANQUETA Y RAMPA 2.25 m2
SEÑALIZACIÓN HORIZONTAL 1.00 obra

Beneficiarios (No. y Tipo) :

110	PERSONAS

Hombres: 50 Mujeres: 60

OBRAS PÚBLICAS

Av. Aguascalientes Sur No. 2615
Fracc. Jardines de las Fuentes,
Aguascalientes, Ags. C.P. 20278

(449) 9 78 92 01, 06, 09

www.ags.gob.mx

Los abajo firmantes, hacen constar que el presente proyecto :

CONSTRUCCIÓN DE SOBRECARPETA ASFÁLTICA CALLE GUZMÁN

TRAMO: ENTRE CALLE JOSÉ MARÍA MORELOS Y PAVÓN Y CALLE CONDELL, CENTRO Zona , Deleg. Zona Centro

cumple con los Requisitos y Normas Técnicas establecidas por la Dependencia Normativa, por lo que es viable su ejecución. Comprometiéndose la misma a proporcionar la supervisión y asistencia técnica necesaria durante el proceso administrativo.

Por la Dependencia Ejecutora

Ing. Miguel Angel Huizar Botello
Secretario de Obras Públicas

Lic. Jaime Gallo Camacho
Secretario de Desarrollo Urbano

LUGAR :AGUASCALIENTES, AGS.

Av. Aguascalientes Sur No. 2615
Fracc. Jardines de las Fuentes,
Aguascalientes, Ags. C.P. 20278

(449) 9 78 92 01, 06, 09

www.ags.gob.mx

No. Folio SISCO 2399

H. AYUNTAMIENTO CONSTITUCIONAL DEL MUNICIPIO DE AGUASCALIENTES 2021-2024

AYUNTAMIENTO DE AGUASCALIENTES

FACTIBILIDAD VERIFICADA EN CAMPO

Aguascalientes
LA CIUDAD DE TU VIDA

MUNICIPIO: AGUASCALIENTES

LOCALIZACION: TRAMO: ENTRE CALLE JOSÉ MARÍA MORELOS Y PAVÓN Y CALLE CONDELL, CENTRO Zona , Deleg. Zona Centro

PROGRAMA: URBANIZACION MUNICIPAL

SUBPROGRAMA: Calles y caminos (2.- Construcción; 02- Concreto Asfáltico)

OBRA A REALIZAR: CONSTRUCCIÓN DE SOBRECARPETA ASFÁLTICA CALLE GUZMÁN

DEPENDENCIA EJECUTORA: SECRETARÍA DE OBRAS PUBLICAS DEL MUNICIPIO DE AGUASCALIENTES

FORMA DE EJECUCION: CONTRATO

TIPO DE OBRA PROPUESTA:

CONDICIONES ACTUALES DE LA OBRA:

CONSTRUCCIÓN DE SOBRECARPETA ASFÁLTICA CALLE GUZMÁN

CARACTERISTICAS DE LA OBRA: Pesimo

FACTIBILIDAD DE LA OBRA:

ESTA OBRA SE REQUIERE PARA EL BENEFICIO DE LA CIUDADANÍA

PROCEDE: SI [X] NO [ ]

REVISÓ: Jefa del Departamento de Expedientes Tecnicos y Costos

NOMBRE: Arq. Blanca Margarita Martinez Amador

FIRMA:

FECHA: 29 Dic 2022

SECRETARÍA DE OBRAS PÚBLICAS

Av. Aguascalientes Sur No. 2615
Fracc. Jardines de las Fuentes,
Aguascalientes, Ags. C.P. 20278

(449) 9 78 92 01, 06, 09

www.ags.gob.mx

No. Folio SISCO 2399

II. AYUNTAMIENTO CONSTITUCIONAL DEL MUNICIPIO DE AGUASCALIENTES 2021-2024

Aguascalientes
LA CIUDAD DE TU VIDA

MACRO LOCALIZACIÓN

APROBACIÓN 2022-FISMDF-0141-0411102-077

NOMBRE DE LA OBRA: CONSTRUCCIÓN DE SOBRECARPETA ASFÁLTICA CALLE GUZMÁN

UBICACIÓN: TRAMO: ENTRE CALLE JOSÉ MARÍA MORELOS Y PAVÓN Y CALLE CONDELL, CENTRO Zona

PROGRAMA: 04 URBANIZACIÓN MUNICIPAL




I.C. LAURA CECILIA MARTÍNEZ ALBA
RESIDENTE DE SUPERVISIÓN

H. AYUNTAMIENTO CONSTITUCIONAL DEL MUNICIPIO DE AGUASCALIENTES 2021-2024

Aguascalientes
LA CIUDAD DE TU VIDA

MICRO LOCALIZACIÓN

APROBACIÓN	**2022-FISMDF-0141-0411102-077**
NOMBRE DE LA OBRA:	**CONSTRUCCIÓN DE SOBRECARPETA ASFÁLTICA CALLE GUZMÁN**
UBICACIÓN:	**TRAMO: ENTRE CALLE JOSÉ MARÍA MORELOS Y PAVÓN Y CALLE CONDELL, CENTRO Zona**
PROGRAMA:	**04 URBANIZACIÓN MUNICIPAL**

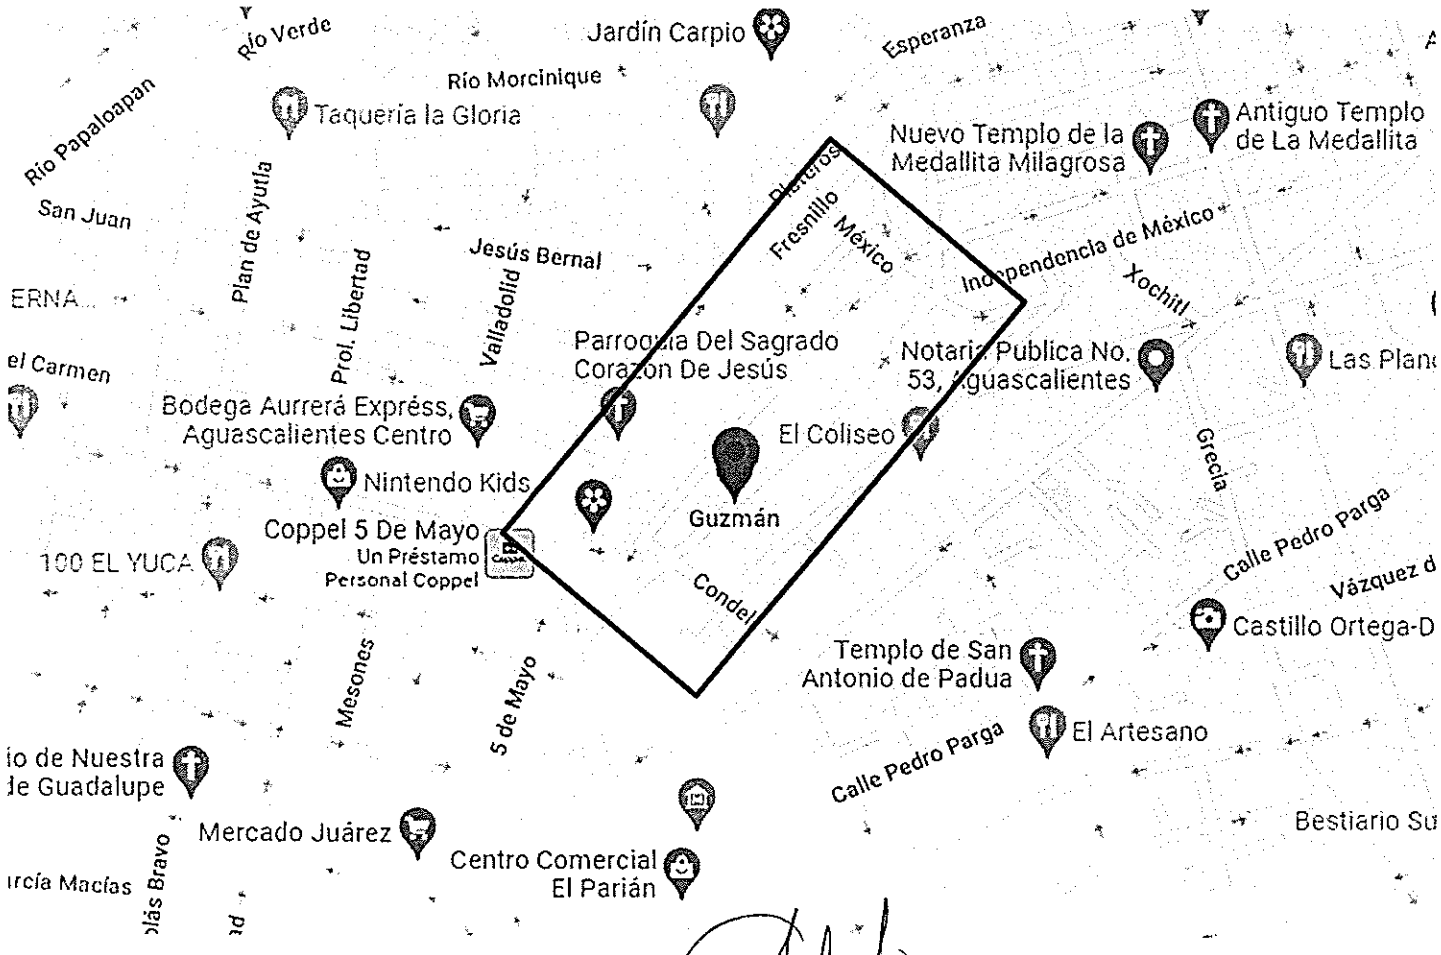

I.C. LAURA CECILIA MARTÍNEZ ALBA
RESIDENTE DE SUPERVISIÓN

PROGRAMA DE OBRA DEFINITIVO

No. DE CONTRATO : FISMDF-0141-2022

PROGRAMA: 04 URBANIZACIÓN MUNICIPAL

INICIO VIGENTE: 10-diciembre-22

No. OBRA Y NOMBRE DE LA OBRA: 2022-FISMDF-0141-0411102-077 CONSTRUCCIÓN DE SOBRECARPETA ASFÁLTICA CALLE GUZMÁN, TRAMO: ENTRE CALLE JOSÉ MARÍA MORELOS Y PAVÓN Y CALLE CONDELL, CENTRO Zona

TERMINO REAL: 19-diciembre-22

RECURSO 2022

CONCEPTO			1	2	3	4	5	6	7	8	9	10	11	12	13	14	15	16	PONDERACIÓN %	
			2022																FINANCIERO	FÍSICO
			OCTUBRE	NOVIEMBRE	DICIEMBRE	ENERO	FEBRERO	MARZO	ABRIL	MAYO	JUNIO	JULIO	AGOSTO	SEPTIEMBRE	OCTUBRE	NOVIEMBRE	DICIEMBRE	ENERO	%	%
DESCRIPCION	INVERSION																10 19			
CONSTRUCCIÓN DE SOBRECARPETA ASFÁLTICA CALLE GUZMÁN																				
TRAMO: ENTRE CALLE JOSÉ MARÍA MORELOS Y PAVÓN Y CALLE CONDELL																				
PRELIMINARES Y DEMOLICIONES	$ 29,139.14	100															50 50		9.96	9.09
BACHEO PROFUNDO	$ 5,371.74	100															50 50		1.84	18.18
SOBRE CARPETA ASFÁLTICA	$ 181,357.76	100															100		61.97	9.09
OBRA COMPLEMENTARIA	$ 4,766.40	100															50 50		1.63	18.18
LIMPIEZAS	$ 8,402.40	100															100		2.87	9.09
GUARNICIONES	$ 4,995.51	100															50 50		1.71	18.18
BANQUETA Y RAMPA	$ 1,303.20	100															100		0.45	9.09
SENALIZACIÓN HORIZONTAL	$ 57,331.77	100															100		19.59	9.09
SUBTOTAL SIN IVA	$ 292,667.93		0 0 0 0	0 0 0 0	0 0 0 0	0 0 0 0	0 0 0 0	0 0 0 0	0 0 0 0	0 0 0 0	0 0 0 0	0 0 0 0	0 0 0 0	0 0 0 0	0 0 0 0	0 0 0 0	4 7	0 0 0 0		
AVACE SEMANAL %			0% 0% 0% 0%	0% 0% 0% 0%	0% 0% 0% 0%	0% 0% 0% 0%	0% 0% 0% 0%	0% 0% 0% 0%	0% 0% 0% 0%	0% 0% 0% 0%	0% 0% 0% 0%	0% 0% 0% 0%	0% 0% 0% 0%	0% 0% 0% 0%	0% 0% 0% 0%	0% 0% 0% 0%	36% 64%	0% 0% 0% 0%		
AVANCE SEMANAL ACUMULADO %			0% 0% 0% 0%	0% 0% 0% 0%	0% 0% 0% 0%	0% 0% 0% 0%	0% 0% 0% 0%	0% 0% 0% 0%	0% 0% 0% 0%	0% 0% 0% 0%	0% 0% 0% 0%	0% 0% 0% 0%	0% 0% 0% 0%	0% 0% 0% 0%	0% 0% 0% 0%	0% 0% 0% 0%	36% 100%	100% 100% 100% 100%	100.00	100.00
EJERCIDO SEMANAL $			- - - -	- - - -	- - - -	- - - -	- - - -	- - - -	- - - -	- - - -	- - - -	- - - -	- - - -	- - - -	- - - -	- - - -	36755.97 256911.96	- - - -	$ 292,667.92	
EJERCIDO MENSUAL $			$0.00	$0.00	$0.00	$0.00	$0.00	$0.00	$0.00	$0.00	$0.00	$0.00	$0.00	$0.00	$0.00	$0.00	$292,667.92	$0.00	$ 40,826.87	IVA 16
EJERCIDO MENSUAL ACUMULADO $			0.00	0.00	0.00	0.00	0.00	0.00	0.00	0.00	0.00	0.00	0.00	0.00	0.00	0.00	292,667.92	292,667.92		
EJERCIDO SEMANAL %			0% 0% 0% 0%	0% 0% 0% 0%	0% 0% 0% 0%	0% 0% 0% 0%	0% 0% 0% 0%	0% 0% 0% 0%	0% 0% 0% 0%	0% 0% 0% 0%	0% 0% 0% 0%	0% 0% 0% 0%	0% 0% 0% 0%	0% 0% 0% 0%	0% 0% 0% 0%	0% 0% 0% 0%	13% 87%	0% 0% 0% 0%		
EJERCIDO MENSUAL %			0%	0%	0%	0%	0%	0%	0%	0%	0%	0%	0%	0%	0%	0%	100%	0%	GRAN TOTAL EJERCIDO	
EJERCIDO MENSUAL ACUMULADO %			0%	0%	0%	0%	0%	0%	0%	0%	0%	0%	0%	0%	0%	0%	100%	100%	$	339,494.7

ING. LAURA CECILIA MARTÍNEZ ALBA
RESIDENTE DE SUPERVISIÓN

PRESIDENCIA MUNICIPAL DE AGUASCALIENTES

FACTIBILIDAD VERIFICADA EN CAMPO

GENERALES

LOCALIDAD: TRAMO: ENTRE CALLE JOSÉ MARÍA MORELOS Y PAVÓN Y CALLE CONDELL

MUNICIPIO: AGUASCALIENTES

PROGRAMA: 04 URBANIZACIÓN MUNICIPAL

SUB-PROGRAMA: 11 Calles y caminos

OBRA A REALIZARSE: CONSTRUCCIÓN DE SOBRECARPETA ASFÁLTICA CALLE GUZMÁN

DEPENDENCIA EJECUTORA: SECRETARÍA DE OBRAS PÚBLICAS MUNICIPALES (S.O.P.M.A)

FORMACIÓN DE EJECUCION: CONTRATO

TIPO DE OBRA PROPUESTA

NUEVA CREACIÓN	X	CONSOLIDACIÓN	
COMPLEMENTARIA		AMPLIACIÓN	
REHABILITACIÓN		EQUIPAMIENTO	

CARACTERÍSTICAS DE LA OBRA:

CONSTRUCCIÓN DE SOBRECARPETA ASFÁLTICA CALLE GUZMÁN

CONDICIONES ACTUALES DE LA OBRA:

BUEN ESTADO	X	REGULAR		PESIMO ESTADO	

FACTIBILIDAD DE LA OBRA:

SE HACE ENTREGA DE LA OBRA DE ACUERDO A LAS METAS INICIALES, ATENDIENDO EL CONTRATISTA LOS DETALLES MARCADOS PREVIOS A LA ENTREGA.

PROCEDE	SI	X	NO		

Aguascalientes
LA CIUDAD DE TU VIDA

I.C. LAURA CECILIA MARTINEZ ALBA
SUPERVISOR

PRESIDENCIA MUNICIPAL DE AGUASCALIENTES

FACTIBILIDAD VERIFICADA EN CAMPO

GENERALES

EJERCICIO: **2022** APROBACION No: **2022-FISMDF-0141-0411102-077**

LOCALIDAD: **TRAMO: ENTRE CALLE JOSÉ MARÍA MORELOS Y PAVÓN Y CALLE CONDELL, CENTRO Zona**

MUNICIPIO: **AGUASCALIENTES, Mpio.**

TIPO DE INVERSION: **FONDO PARA LA INFRAESTRUCTURA SOCIAL MUNICIPAL Y DE LAS DEMARCACIONES TERRITORIALES DEL DISTRITO FEDERAL**

PROGRAMA: **04 URBANIZACIÓN MUNICIPAL**

SUB-PROGRAMA: **11 Calles y caminos**

OBRA A REALIZARSE: **CONSTRUCCIÓN DE SOBRECARPETA ASFÁLTICA CALLE GUZMÁN**

DEPENDENCIA EJECUTORA: **SECRETARÍA DE OBRAS PÚBLICAS MUNICIPALES (S.O.P.M.A)**

FORMACIÓN DE EJECUCION: **CONTRATO** NO. DE CONTRATO: **FISMDF-0141-2022**

NOMBRE CONTRATISTA: **GRUPO REALIZA, S.A. DE C.V.**

REPRESENTANTE: **LIC. CARLOS DAVID FRAUSTTO DÍAZ**

MONTO CONT. ORIGEN **$339,494.79** ANTICIPO: **$0.00** PLAZO **10 DÍAS**

1A AMPLIACION $: 1 AMPL DIAS

2A AMPLIACION $: 2 AMPL DIAS

FIRMA CONTRATO: **09/12/2022**

INICIO CONT: dd/mm/aa **10/12/2022** TERMINO CONT: **19/12/2022**

INICIO REAL: dd/mm/aa **10/12/2022** TERMINO REAL: **19/12/2022**

TIPO DE OBRA PROPUESTA

NUEVA CREACIÓN	X	CONSOLIDACIÓN	
COMPLEMENTARIA		AMPLIACIÓN	
REHABILITACIÓN		EQUIPAMIENTO	

CARACTERÍSTICAS DE LA OBRA:

FRESADO DE CARPETA EXISTENTE

BACHEO PROFUNDO Y RENIVELACIONES

COLOCACIÓN DE SOBRE CARPETA ASFÁLTICA

SUMINISTRO Y COLOCACIÓN DE PINTURA Y VIALETAS

CONDICIONES ACTUALES DE LA OBRA: (SELECCIONAR UNO OBLIGATORIO)

BUEN ESTADO X REGULAR PESIMO ESTADO

FACTIBILIDAD DE LA OBRA: (CONDICIONES ACTUALES DE LA OBRA)

ESTA OBRA SE ENCUENTRA EN CONDICIONES PARA OPERARSE

PROCEDE: SI: X NO:

MARQUE SOLO UNA

I.C. LAURA CECILIA MARTÍNEZ ALBA
SUPERVISOR


PRESUPUESTO MODIFICADO

Obra: **CONSTRUCCIÓN DE SOBRECARPETA ASFÁLTICA CALLE GUZMÁN**

Ubicación: **TRAMO: ENTRE CALLE JOSÉ MARÍA MORELOS Y PAVÓN Y CALLE CONDELL, CENTRO Zona**

Contratista: **GRUPO REALIZA, S.A. DE C.V. (1010)**

No.	Concepto	Unidad	Cantidad	Precio Unitario	Importe Total
	GRUPO: **PRELIMINARES**				
	PARTIDA: **PRELIMINARES Y DEMOLICIONES**				
1	LIMPIA, TRAZO Y NIVELACION EN PAVIMENTOS, CALLES Y VIALIDADES CON EQUIPO TOPOGRAFICO, INCLUYE: EJES, BANCO DE NIVEL, RENIVELACIONES LAS VECES NECESARIAS, CORRECCION DE RASANTE A PUNTOS OBLIGADOS (AUTORIZADOS POR LA SUPERVISION), ESTACAS, VARILLAS, MANO DE OBRA CALIFICADA, HERRAMIENTA NECESARIA, EQUIPO DE PRECISION CALIBRADO, TRABAJO TERMINADO.P.U.O.T.	M2	273.16	$8.59	$2,346.44
2	SONDEO A MANO O A MAQUINA PARA LOCALIZACION DE TUBERIAS CUALQUIER PROFUNDIDAD Y MATERIAL PARA VERIFICAR LA CALIDAD DE LAS INSTALACIONES HIDRAULICO SANITARIAS CUIDANDO NO DAÑARLAS PARA NO INTERFERIR EN LOS SERVICIOS, INCLUYE: EXCAVACION, EQUIPO, MANO DE OBRA, REPORTE A LA SUPERVISION, RELLENOS, COMPACTACIONES, TRABAJO TERMINADO.	SONDE	2	$2,063.23	$4,126.46
3	CORTE CON DISCO DIAMANTADO DE 14" EN PISOS DE CONCRETO ASFALTICO DE HASTA 8.00 cm. DE PROFUNDIDAD. INCLUYE: TRAZO, EQUIPO Y OPERACION, LIMPIEZAS.	ML	12	$40.65	$487.80
4	DEMOLICION PARCIAL DE PAVIMENTO HIDRAULICO Y/O ASFALTICO DE HASTA 15 CM. DE ESPESOR PROMEDIO EN PAVIMENTOS Y (BANQUETAS, LOSAS DIAMANTE Y CAJAS DE VALVULAS, TOPES) CON O SIN ARMADO DE ACERO, SIN RECUPERACION, MUROS, MOJONERAS, ANCLAJES, ETC, DE FORMA MANUAL Y MECANICA, INCLUYE ACARREO DE MATERIAL AL LUGAR DE ACOPIO, HERRAMIENTA NECESARIA Y TODO LO NECESARIO PARA SU CORRECTA EJECUCION, LIMPIEZA, TRABAJO TERMINADO	M3	1	$308.09	$308.09
5	FRESADO UNIFORME DE LA SUPERFICIE DE RODADURA EN PAVIMENTO DE CONCRETO ASFALTICO 3-7 CM (5 cm de espesor promedio) MEDIANTE FRESADORA EN FRIO COMPACTA, EQUIPADA CON BANDA TRANSPORTADORA PARA CARGA DIRECTA SOBRE CAMION DE VOLTEO, INCLUYE: TRAMO DE PRUEBA AL INICIO DEL FRESADO PARA AUTORIZACION DE SUPERVISION (SUPERFICIE FRESADA UNIFORME Y SIN PROTUBERANCIAS NI ONDEOS), ACARREOS LOCALES, CARGA Y ACARREO A KM SUBSECUENTES (11 A 15 KM APROX) DE MATERIAL PRODUCTO DEL FRESADO DE CARPETA ASFALTICA EL TRASLADO SERA A PARQUE DE MAQUINARIA DE LA SOPMA, PIEZAS DE DESGASTE, COMBUSTIBLES, CONSUMIBLES, MANO DE OBRA, CUALQUIER VOLUMEN Y AREA,EQUIPO NECESARIO, LIMPIEZA FINA Y GRUESA, TRABAJO TERMINADO.	M3	16.39	$1,276.89	$20,928.23
7	DEMOLICION CONTROLADA DE CONCRETO HIDRAULICO EN DENTELLONES Y GUARNICIONES DE 15 x 20 x 40 CM. DE FORMA MANUAL Y MECÁNICA, INCLUYE: CORTES CON DISCO, ACARREO DEL MATERIAL AL LUGAR DE ACOPIO PARA SU CARGA Y ACARREO FUERA DE LA OBRA.	ML	12.4	$29.98	$371.75
8	CARGA MECANICA Y ACARREO DE MATERIAL PRODUCTO DE EXCAVACION Y DEMOLICION EN CAMION DE VOLTEO AL 1er. KM, VOLUMEN MEDIDO COMPACTO.	M3	1.37	$68.72	$94.15
9	ACARREO DE MATERIAL PRODUCTO DE EXCAVACION Y/O DEMOLICION EN CAMION DE VOLTEO A KILOMETROS SUBSECUENTES, AL TIRADERO OFICIAL AUTORIZADO MAS CERCANO AUTORIZADO POR LA SUPERVISION, VOLUMEN MEDIDO COMPACTO.	M3-KM	41.16	$11.57	$476.22
				Totales por Partida	**$29,139.14**
				Totales por Grupo	**$29,139.14**

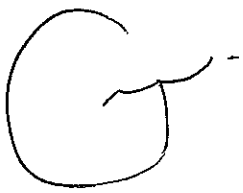

Obra: **CONSTRUCCIÓN DE SOBRECARPETA ASFÁLTICA CALLE GUZMÁN**

Ubicación: **TRAMO: ENTRE CALLE JOSÉ MARÍA MORELOS Y PAVÓN Y CALLE CONDELL, CENTRO Zona**

Contratista: **GRUPO REALIZA, S.A. DE C.V. (1010)**

No.	Concepto	Unidad	Cantidad	Precio Unitario	Importe Total
	GRUPO: **SOBRECARPETA ASFALTICA**				
	PARTIDA: **BACHEO PROFUNDO**				
10	BACHEO PROFUNDO AISLADO UTILIZANDO MATERIAL CALIDAD BASE HIDRAULICA PARA MAS DE UN MILLON DE EJES EQUIVALENTES DEL BANCO QUE ELIJA EL CONTRATISTA, INCISO N.CSV.CAR.1.02.004/03 DE LAS NORMAS DE CONSTRUCCION DE CARR. DE LA SCT, INCLUYE: PREPARACION, PERFILADO, MATERIALES, MANO DE OBRA, HERRAMIENTA MENOR Y EQUIPO NECESARIO QUE SE REQUIERA PARA LOGRAR LA COMPACTACION DE 100% PVSM, ACARREOS DENTRO Y FUERA DE LA OBRA, PREPARACION DE MATERIAL, HUMEDECIDO, NIVELADO, TRASLADO DE UN PUNTO A OTRO DENTRO DE LA OBRA, EN CUALQUIER VOLUMEN, MOVIMIENTO DE MAQUINARIA P.U.O.T	M3	3.9	$1,377.37	$5,371.74
			Totales por Partida		**$5,371.74**
	PARTIDA: **SOBRE CARPETA ASFALTICA**				
13	PREPARACIÓN DE LA SUPERFICIE DE CONTACTO EN LOS EXTREMOS DONDE LA PERFILADORA NO ALCANCE POR LÍMITES CON LA GUARNICIÓN, CON UN RASPADO SUPERFICIAL CON RETROEXCAVADORA, ELIMINANDO TECATAS QUE HAYAN QUEDADO PARA RENIVELADO, BARRIDOS ENTRE PASADA DE MOTOCONFORMADORA Y EN REMATES DE EMPATES A DETALLE A MANO, INCLUYE: RETIRO DE MATERIAL FUERA DE LA OBRA A TIRADERO OFICIAL INDICADO.	M2	49.6	$36.74	$1,822.30
14	RENIVELACIONES CON CONCRETO ASFALTICO MEZCLA EN PLANTA EN CALIENTE ASFALTO MODIFICADO CON POLIMERO TIPO I, CUMPLIENDO LAS NORMAS SCT REFERENTES DE CONSTRUCCCION Y CONSERVACION, GRANULOMETRIA DENSA 3/4" A FINOS, MEDIDO COMPACTO AL NOVENTA Y CINCO PORCIENTO (95%), INCLUYE CARGA Y ACARREO EN TRAMOS AISLADOS, MATERIALES, MANO DE OBRA, ACARREO DE MATERIALES, Y MAQUINARIA Y EQUIPO AL SIGUIENTE PUNTO EN CUALQUIER VOLUEN, PERFILADO, LIMPIEZA DE HUESO Y GRAVA SUELTA, TRABAJO TERMINADO P.U.O.T	M3	4.03	$7,230.51	$29,138.96
17	RIEGO DE LIGA CON EMULSION DE ROMPIMIENTO RAPIDO (ECR-65 %), INCLUYE, SUMINISTRO, ALMACENAMIENTO, CALENTAMIENTO, Y APLICACION DE LA EMULSION CON EQUIPO ESPECIAL PARA ESA ACTIVIDAD, ESPREAS O BACHADOR LIMPIAS Y ALINEADAS, CONTROL DE CALIDAD A CADA DOS REMESAS EN OBRA (INDEPENDIENTEMENTE DE LA CANTIDAD A UTILIZAR) EN LA PETROLIZADORA, A RAZON DE 0.8 LT DE EMULSION POR M2, O LO QUE INDIQUE EL LABORATORIO DE CALIDAD DEL CONTRATISTA, NO SE ACEPTAN "IMPREGNALIGA", TRABAJO TERMINADO, P.U.O.T.	M2	273.16	$15.88	$4,337.78
18	SUMINISTRO Y COLOCACION DE CONCRETO ASFALTICO EN CALIENTE DE GRANULOMETRIA DENSA ELABORADA CON ASFALTO MODIFICADO TIPO I, AGREGADO 3/4" A FINOS, DE 5 CM DE ESPESOR, FORMADA Y COMPACTADO AL 95%, INCLUYE MATERIALES, QUE CUMPLAN LA NORMATIVA SCT-N-CMT-04-04, SCT-CMT-4-05-002, SCT-CMT-4-05-003, SCT-CMT-4-05-004, SCT-CTR-CAR-1-04-006-14 APLICADAS AL DIA DE HOY, DISEÑO MARSHALL (DEVERÁ SER AUTORIZADO POR EL LABORATORIO DE CALIDAD DE SOPMA AL MENOS 3 DIAS ANTES DE INICIO DE TENDIDO DE LA MEZCLA ASFALTICA), INCUYE: TRAMO DE PRUEBA AL INICIO PARA REVISION Y AUTORIZACION DEL ESPESOR POR PARTE DEL SUPERVISOR, EL CONTRATISTA DEBERÁ PREVEER EL SUMINISTRO Y TIEMPOS MUERTOS POR MOVIMIENTOS DEL TREN DE MAQUINAS DE TRABAJO EN TRAMOS AISLADOS. TRABAJO TERMINADO P.U.O.T. Y LIMPIEZAS DE GRANZON Y HUESO LATERAL.	M2	167.9203845932	$310.44	$145,261.20
19	COMPACTACION SOBRE MORTERO ASFALTICO TENDIDO EN APROCHES CON GUARNICIONES CON EQUIPO LIGERO (PLANCHITA), INCLUYE: MANO DE OBRA Y EQUIPO, TRABAJO TERMINADO.	M2	55.46	$14.38	$797.51
			Totales por Partida		**$181,357.76**

PRESUPUESTO MODIFICADO

Obra: **CONSTRUCCIÓN DE SOBRECARPETA ASFÁLTICA CALLE GUZMÁN**

Ubicación: **TRAMO: ENTRE CALLE JOSÉ MARÍA MORELOS Y PAVÓN Y CALLE CONDELL, CENTRO Zona**

Contratista: **GRUPO REALIZA, S.A. DE C.V. (1010)**

No.	Concepto	Unidad	Cantidad	Precio Unitario	Importe Total
GRUPO: **SOBRECARPETA ASFALTICA**					
PARTIDA: **OBRA COMPLEMENTARIA**					
23	LIMPIEZA Y DESASOLVE DE POZOS DE VISITA Y LINEAS DE ALCANTARILLADO EXISTENTE CON CAMION TIPO VACTOR. INCLUYE: RESANE INTERIOR DEL POZO Y REMTE DE POZO CO TUBO CON SELLADOR, FESTER Y MORTERO 1:3, MANO DE OBRA, SUMINISTRO DE AGUA EN PIPA, HERRAMIENTAS Y EQUIPO PARA SU CORRECTA EJECUCION, LIMPIEZAS, RENTA DE CAMION VACTOR HASTA LA CORRECTA LIMPIEZA DE LAS LINEAS EXISTENTES DE POZO A POZO, ASI COMO EL TRASLADO DE LOS DESECHOS HASTA TIRADERO AUTORIZADO MEDIDO POZO A POZO.	LOTE	1	$4,766.40	$4,766.40
			Totales por Partida		**$4,766.40**
PARTIDA: **LIMPIEZAS**					
24	LIMPIEZA GENERAL DE LA OBRA, INCLUYE: BARRIDO, CARGA, ACARREOS Y RETIRO DE ESCOMBROS FUERA DE LA OBRA, TRABAJO TERMINADO.	M2	273.16	$30.76	$8,402.40
			Totales por Partida		**$8,402.40**
			Totales por Grupo		**$199,898.30**

Obra: **CONSTRUCCIÓN DE SOBRECARPETA ASFÁLTICA CALLE GUZMÁN**

Ubicación: **TRAMO: ENTRE CALLE JOSÉ MARÍA MORELOS Y PAVÓN Y CALLE CONDELL, CENTRO Zona**

Contratista: **GRUPO REALIZA, S.A. DE C.V. (1010)**

No.	Concepto	Unidad	Cantidad	Precio Unitario	Importe Total
	GRUPO: **GUARNICIONES Y BANQUETAS**				
	PARTIDA: **GUARNICIONES**				
25	EXCAVACION A MAQUINA Y/O A MANO EN MATERIAL TIPO II, EN SECO O PRESENCIA DE AGUA, INCLUYE. CORTE DE RAIZ DE CUALQUIER TAMAÑO Y GROSOR, HASTA UNA PROFUNDIDAD DE 40 CM DESPUES DE DESMONTE, DESPALME Y/O DEMOLICION DE SUPERFICIE O ELEMENTO ESTRUCTURAL O DE ACABADO, PROTECCION DE AREAS ADYACENTES, SIN DAÑAR AREAS ALEDAÑAS, CARGA Y ACARREO A TIRADERO OFICIAL, CONSERVACION DE LA MISMA, TRABAJO TERMINADO, LIMPIEZAS.	M3	1.98	$314.18	$622.08
26	COMPACTACION DE TERRENO NATURAL AL 90% DE SU P.V.S.M EN SU COMPACTACION., INCLUYE ESCARIFICADO, TENDIDO, HOMOGENIZADO, HUMEDECIDO OPTIMO NIVELADO Y COMPACTADO EN CAPAS DE 20 CM, CALIDAD Limite liquido máximo 50%, Valor de Soporte California (CBR) mínimo 15%, Expansión máxima 5%, Grado de Compactación minimo 90% ± 2, Y TODO LO NECESARIO PARA SU CORRECTA EJECUCION,	M2	4.96	$33.31	$165.22
27	CONSTRUCCION DE GUARNICION RECTA Y/O CURVA TRAPEZOIDAL 15-20X40 CM DE SECCION CON CONCRETO PREMEZCLADO MR=38 KGF/CM2, R.N.REVENIMIENTO DE 8 A 10 CM, T.M.A. 3/4", GRAVA TRITURADA, ACABADO PULIDO EN PARTE DE SUPERIOR Y DOBLADOR EN ARISTAS, INCLUYE: COMPACTADO DE PLANTILLA, CIMBRADO, COLADO, VIBRADO, ACABADO, DESCIMBRADO, ALINEADO, NIVELADO, Y CURADO EN SU PARTE SUPERIOR CON MEMBRANA BASE AGUA A RAZON DE 1 LTO/M2, JUNTA DE AISLAMIENTO LONGITUDINAL AL COMBINAR CON OTRO ELEMENTO Y TRANSVERSAL @ 30 MT MAXIMO, SELLADO CON SELLADOR AUTONIVELANTE LONGITUDINAL, TRABAJO TERMINADO, .P.U.O.T.	ML	12.4	$262.77	$3,258.35
28	RELLENO COMPACTADO AL 95% CON MATERIAL DE BANCO EN CAPAS DE 20 CM UTILIZANDO BAILARINA. INCLUYE: SUMINISTRO DE TEPETATE (MATERIAL DE BANCO) EN LA OBRA, ABUNDAMIENTO, ACARREOS DENTRO DE LA OBRA, CRIBADO, RETIRO DE MATERIAL, MANO DE OBRA Y EQUIPO, LIMPIEZAS, TRABAJO TERMINADO	M3	0.37	$419.27	$155.13
29	CARGA MECANICA Y ACARREO DE MATERIAL PRODUCTO DE EXCAVACION Y DEMOLICION EN CAMION DE VOLTEO AL 1er. KM, VOLUMEN MEDIDO COMPACTO.	M3	2.36	$55.83	$131.76
30	ACARREO DE MATERIAL PRODUCTO DE EXCAVACION Y/O DEMOLICION EN CAMION DE VOLTEO A KILOMETROS SUBSECUENTES, AL TIRADERO OFICIAL AUTORIZADO MAS CERCANO AUTORIZADO POR LA SUPERVISION, VOLUMEN MEDIDO COMPACTO.	M3-KM	70.68	$9.38	$662.98
				Totales por Partida	**$4,995.51**
	PARTIDA: **BANQUETA Y RAMPA**				
39	CONSTRUCCION DE RAMPA Y BANQUETA DE USO HABITACIONAL PARA TRAFICO VEHICULAR, DE 12 CM DE ESPESOR A BASE DE CONCRETO PREMEZCLADO MR=38 KGF/CM2, T.M.A. 1 1/2", R.R 7 DIAS. GRAVA TRITURADA, REVENIMIENTI DE 10+-2 CM, ACABADO RAYADO FINO CON BROCHA DE PELO, JUNTAS FRIAS CON DOBLADOR DE 2" SECCION DE LOSAS COMO INDIQUE PROYECTO, INCLUYE: JUNTA DE AISLAMIENTO Y DE EXPANSION A BASE DE ESPUMA DE POLIETILENO DE CELDAS CERRADAS DE 1/2" EN JUNTAS FRIAS LONGITUDINALES CON MUROS Y TRANSVERSALES DEL ELEMENTO, ASI COMO SU UNION CON ELEMENTOS VIEJOS O CAMBIO DE ELEMENTO, CIMBRADO, COLADO, DESCIMBRADO, CORTES CON CORTADORA DE DISCO, SELLADO DE CORTES CON SELLADOR AUTONIVELANTE Y TIRA DE RELLENO PREFORMADA NO ADHERENTE DE 1/8" (EN TODAS LAS JUNTAS DE CONTRACCCION Y CONSTRUCCION TRANSVERSALES), CURADO CON MEMBRANA QUIMICA APLICADA CON ASPERSOR, TRABAJO TERMINADO FICHA TECNICA 216	M2	2.25	$579.20	$1,303.20
				Totales por Partida	**$1,303.20**
				Totales por Grupo	**$6,298.71**

Obra: **CONSTRUCCIÓN DE SOBRECARPETA ASFÁLTICA CALLE GUZMÁN**

Ubicación: **TRAMO: ENTRE CALLE JOSÉ MARÍA MORELOS Y PAVÓN Y CALLE CONDELL, CENTRO Zona**

Contratista: **GRUPO REALIZA, S.A. DE C.V. (1010)**

No.	Concepto	Unidad	Cantidad	Precio Unitario	Importe Total
	GRUPO: **SEÑALIZACION**				
	PARTIDA: **SEÑALIZACION HORIZONTAL**				
40	SUMINISTRO Y APLICACIÓN DE PINTURA EPOXICA BASE SOLVENTE COLOR AZUL (PANTONE 294) EN RAMPAS PARA PERSONAS CON DISCAPACIDAD CUALQUIER SECCIÓN SEGÚN PLANOS. INCLUYE: TRAZO, MANO DE OBRA, LIMPIEZA PREVIA DE SUPERFICIE, EQUIPO NECESARIO PARA SU EJECUCIÓN, Y TODO LO NECESARIO PARA SU CORRECTA EJECUCIÓN, TRABAJO TERMINADO.	M2	12	$370.14	$4,441.68
41	SUMINISTRO Y APLICACIÓN DE LOGOTIPO A (SILLA DE RUEDAS) EN PINTURA EPOXICA BASE SOLVENTE COLOR BLANCO EN RAMPAS PARA PERSONAS CON DISCAPACIDAD TAMAÑO Y DISEÑO SEGÚN PLANOS. INCLUYE: TRAZO, ENMASCARILLADO, PLANTILLA, MANO DE OBRA, LIMPIEZA PREVIA DE SUPERFICIE, EQUIPO NECESARIO PARA SU EJECUCIÓN, Y TODO LO NECESARIO PARA SU CORRECTA EJECUCIÓN, TRABAJO TERMINADO.	PZA	7	$487.55	$3,412.85
42	SUMINISTRO Y APLICACIÓN DE PINTURA BASE SOLVENTE PARA MARCAS EN GUARNICIONES CLASIFICACION M-12.1, M12.2 APLICADA SOBRE GUARNICIONES Y DENTELLONES DE CUALQUIER COLOR, SEGÚN SE REQUIERA Y SEGÚN NORMA S.C.T. SECADO AL TACTO EN 5 MIN Y AL DURO EN 30 MIN CON MICRO ESFERA , DESARROLLO DE 35 CM. INCLUYE: MATERIALES Y ESPECIFICACIONES QUE CUMPLAN CON LA NORMATIVA N-CMT-5-01-001/05, N-PRY-CAR-10-01-002/13 APLICADAS AL DIA DE HOY, TRAZO, MANO DE OBRA, LIMPIEZA PREVIA DE SUPERFICIE, EQUIPO NECESARIO PARA SU EJECUCIÓN, Y TODO LO NECESARIO PARA SU CORRECTA EJECUCIÓN, TRABAJO TERMINADO.	ML	124	$80.66	$10,001.84
43	SUMINISTRO Y APLICACIÓN DE PINTURA TERMOPLASTICA ALQUIDALICA DE 120 MILESIMAS DE " (in) EN RAYA EN LA ORILLA DEL ARROYO VIAL CLASIFICACIÓN M - 3.3, CONTINUA IZQUIERDA, PARA VIALIDADES URBANAS DE FRENTE EN PISO, DE 10 CM DE ANCHO Y SEPARADA 15 CM. DE LA GUARNICION, A BASE DE PINTURA PARA TRAFICO COLOR BLANCO CON MICRO ESFERA SEGÚN MANUAL DE SEÑALIZACIÓN VIAL Y DISPOSITIVOS DE SEGURIDAD SICT (S.C.T)., INCLUYE: MATERIALES Y ESPECIFICACIONES QUE CUMPLAN CON LA NORMATIVA N-CMT-5-01-001/13, N-PRY-CAR-10-01-002/13 APLICADAS AL DIA DE HOY, MATERIAL APLICADO EN SU ESTADO DE FUSION A UNA TEMPERATURA MINIMA DE 204 C, LA SUPERFICIE DE CONCRETO O ASFALTO NO DEBE PRESENTAR UNA TEMPERATURA MENOR A LOS 10 C, ;TIEMPO DE SECADO EN RANGOS DE TEMPERATURA DE 10 C DEL SUSTRATO 2 MINUTOS, Y NO MAS DE 10 MINUTOS CUANDO EL SUSTRATO OSCILA ALREDEDOR DE 54C, TRAZO, ENMASCARILLADO, MANO DE OBRA, LIMPIEZA PREVIA Y FINAL DE SUPERFICIE, EQUIPO NECESARIO PARA SU EJECUCIÓN, Y TODO LO NECESARIO PARA SU CORRECTA EJECUCIÓN, TRABAJO TERMINADO.	ML	108	$63.33	$6,839.64



Obra: **CONSTRUCCIÓN DE SOBRECARPETA ASFÁLTICA CALLE GUZMÁN**

Ubicación: **TRAMO: ENTRE CALLE JOSÉ MARÍA MORELOS Y PAVÓN Y CALLE CONDELL, CENTRO Zona**

Contratista: **GRUPO REALIZA, S.A. DE C.V. (1010)**

No.	Concepto	Unidad	Cantidad	Precio Unitario	Importe Total
	GRUPO: **SEÑALIZACION**				
	PARTIDA: **SEÑALIZACION HORIZONTAL**				
44	SUMINISTRO Y APLICACIÓN DE PINTURA TERMOPLASTICA ALQUIDALICA DE 120 MILESIMAS DE " (in) EN RAYA PARA CRUCE PEATONAL CLASIFICACIÓN M - 7.1, PARA INDICAR " CRUCE PEATONAL EN VIAS PRIMARIAS", COLOR AMARILLO, REFLEJANTE CON MICRO ESFERA DE VIDRIO EN PROPORCIÓN SEGÚN MANUAL DE SEÑALIZACIÓN VIAL Y DISPOSITIVOS DE SEGURIDAD SICT (S.C.T). DE 0.40 MTS DE ANCHO Y 3.5 MTS. DE LONGITUD POR EL ANCHO DE LA VIALIDAD, CON UNA SEPARACIÓN DE 0.40 MTS. ENTRE ELLAS, INCLUYE: MATERIALES Y ESPECIFICACIONES QUE CUMPLAN CON LA NORMATIVA N-CMT-5-01-001/13, N-PRY-CAR-10-01-002/13 APLICADAS AL DIA DE HOY, MATERIAL APLICADO EN SU ESTADO DE FUSION A UNA TEMPERATURA MINIMA DE 204 C, LA SUPERFICIE DE CONCRETO O ASFALTO NO DEBE PRESENTAR UNA TEMPERATURA MENOR A LOS 10 C, ;TIEMPO DE SECADO EN RANGOS DE TEMPERATURA DE 10 C DEL SUSTRATO 2 MINUTOS, Y NO MAS DE 10 MINUTOS CUANDO EL SUSTRATO OSCILA ALREDEDOR DE 54C, TRAZO, ENMASCARILLADO, MANO DE OBRA, LIMPIEZA PREVIA Y FINAL DE SUPERFICIE, EQUIPO NECESARIO PARA SU EJECUCIÓN, Y TODO LO NECESARIO PARA SU CORRECTA EJECUCIÓN, TRABAJO TERMINADO.	M2	37.8	$527.92	$19,955.38
45	SUMINISTRO Y APLICACIÓN DE PINTURA TERMOPLASTICA ALQUIDALICA DE 120 MILESIMAS DE " (in) EN FLECHAS CLASIFICACIÓN M - 11.1, "FLECHA SENCILLA" PARA INDICAR SENTIDO DE CIRCULACIÓN , EN VIALIDADES PARA VELOCIDAD MENOR A 60KM POR HORA DIMENSION NORMATIVA SEGUN MANUAL DE SEÑALIZACIÓN VIAL Y DISPOSITIVOS DE SEGURIDAD SICT (SCT) Y/O (VER PLANO DE SEÑALAMIENTOS), COLOR BLANCO, REFLEJANTE CON MICRO ESFERA DE VIDRIO EN PROPORCIÓN SEGÚN NORMA SCT, INCLUYE: MATERIALES Y ESPECIFICACIONES QUE CUMPLAN CON LA NORMATIVA N-CMT-5-01-001/13, N-PRY-CAR-10-01-002/13 APLICADAS AL DIA DE HOY, MATERIAL APLICADO EN SU ESTADO DE FUSION A UNA TEMPERATURA MINIMA DE 204 C, LA SUPERFICIE DE CONCRETO O ASFALTO NO DEBE PRESENTAR UNA TEMPERATURA MENOR A LOS 10 C, ;TIEMPO DE SECADO EN RANGOS DE TEMPERATURA DE 10 C DEL SUSTRATO 2 MINUTOS, Y NO MAS DE 10 MINUTOS CUANDO EL SUSTRATO OSCILA ALREDEDOR DE 54C, TRAZO, ENMASCARILLADO, MANO DE OBRA, LIMPIEZA PREVIA Y FINAL DE SUPERFICIE, EQUIPO NECESARIO PARA SU EJECUCIÓN, Y TODO LO NECESARIO PARA SU CORRECTA EJECUCIÓN, TRABAJO TERMINADO.	PZA	1	$1,318.52	$1,318.52
46	SUMINISTRO Y APLICACIÓN DE PINTURA TERMOPLASTICA ALQUIDALICA DE 120 MILESIMAS DE " (in) EN FLECHAS CLASIFICACIÓN M - 11.1, " FLECHA CABEZA DOBLE" PARA INDICAR SENTIDO DE CIRCULACIÓN (VUELTA IZQUIERDA O DERECHA), EN VIALIDADES PARA VELOCIDAD MENOR A 60KM POR HORA SEGUN MANUAL DE SEÑALIZACIÓN VIAL Y DISPOSITIVOS DE SEGURIDAD SICT (SCT), (VER PLANO DE SEÑALAMIENTOS), EN COLOR BLANCO, REFLEJANTE CON MICRO ESFERA DE VIDRIO EN PROPORCIÓN SEGÚN NORMA SCT, INCLUYE: MATERIALES Y ESPECIFICACIONES QUE CUMPLAN CON LA NORMATIVA N-CMT-5-01-001/13, N-PRY-CAR-10-01-002/13 APLICADAS AL DIA DE HOY, MATERIAL APLICADO EN SU ESTADO DE FUSION A UNA TEMPERATURA MINIMA DE 204 C, LA SUPERFICIE DE CONCRETO O ASFALTO NO DEBE PRESENTAR UNA TEMPERATURA MENOR A LOS 10 C, ;TIEMPO DE SECADO EN RANGOS DE TEMPERATURA DE 10 C DEL SUSTRATO 2 MINUTOS, Y NO MAS DE 10 MINUTOS CUANDO EL SUSTRATO OSCILA ALREDEDOR DE 54C, TRAZO, ENMASCARILLADO, MANO DE OBRA, LIMPIEZA PREVIA Y FINAL DE SUPERFICIE, EQUIPO NECESARIO PARA SU EJECUCIÓN, Y TODO LO NECESARIO PARA SU CORRECTA EJECUCIÓN, TRABAJO TERMINADO.	PZA	1	$1,977.82	$1,977.82


Obra: **CONSTRUCCIÓN DE SOBRECARPETA ASFÁLTICA CALLE GUZMÁN**

Ubicación: **TRAMO: ENTRE CALLE JOSÉ MARÍA MORELOS Y PAVÓN Y CALLE CONDELL, CENTRO Zona**

Contratista: **GRUPO REALIZA, S.A. DE C.V. (1010)**

No.	Concepto	Unidad	Cantidad	Precio Unitario	Importe Total
	GRUPO: **SEÑALIZACION**				
	PARTIDA: **SEÑALIZACION HORIZONTAL**				
47	SUMINISTRO Y APLICACIÓN DE PINTURA TERMOPLASTICA ALQUIDALICA DE 120 MILESIMAS DE " (in) EN RAYA DE ALTO CLASIFICACIÓN M - 6, PARA INDICAR ALTO EN CRUCEROS, COLOR BLANCO, REFLEJANTE CON MICRO ESFERA DE VIDRIO EN PROPORCIÓN SEGÚN MANUAL DE SEÑALIZACIÓN VIAL Y DISPOSITIVOS DE SEGURIDAD SICT (S.C.T). DE 0.60 MTS DE ANCHO DE LONGITUD VARIABLE, INCLUYE: MATERIALES Y ESPECIFICACIONES QUE CUMPLAN CON LA NORMATIVA N-CMT-5-01-001/13, N-PRY-CAR-10-01-002/13 APLICADAS AL DIA DE HOY, MATERIAL APLICADO EN SU ESTADO DE FUSION A UNA TEMPERATURA MINIMA DE 204 C, LA SUPERFICIE DE CONCRETO O ASFALTO NO DEBE PRESENTAR UNA TEMPERATURA MENOR A LOS 10 C, ;TIEMPO DE SECADO EN RANGOS DE TEMPERATURA DE 10 C DEL SUSTRATO 2 MINUTOS, Y NO MAS DE 10 MINUTOS CUANDO EL SUSTRATO OSCILA ALREDEDOR DE 54C, TRAZO, ENMASCARILLADO, MANO DE OBRA, LIMPIEZA PREVIA Y FINAL DE SUPERFICIE, EQUIPO NECESARIO PARA SU EJECUCIÓN, Y TODO LO NECESARIO PARA SU CORRECTA EJECUCIÓN, TRABAJO TERMINADO.	ML	5.4	$372.07	$2,009.18
48	SUMINISTRO Y COLOCACION DE VIALETA STANDARD (S-200) DE 10X10CM. COLOR: CUERPO AMARILLO Y REFLEJANTE AMARILLO 1 CARA MARCA SEA O SIMILAR EN CALIDAD Y ESPECIFICACIONES DE FICHA TECNICA, ANCLADO EN PAVIMENTO SISTEMA DE SUJECION DE ALTO AGARRE BASE CUÑAS CON AB PEGAMENTO EPOXICO 50/50 RESISTENTE A ALTA TEMPERATURA (VER PLANO DE DETALLES DE SEÑALAMIENTOS HORIZONTAL Y VERTICAL). INCLUYE: TRAZO, ALINEACION, ELEVACION CUALQUIER ALTURA, TRABAJO TERMINADO, LIMPIEZAS.	PZA	18	$69.02	$1,242.36
49	SUMINISTRO Y COLOCACION DE VIALETA SOLAR DE 10X10CM. COLOR: CUERPO ALUMINIO 3 LED DOS CARAS REFLEJANTES MARCA CREATIVAL VT-29 O SIMILAR EN CALIDAD Y ESPECIFICACIONES DE FICHA TÉCNICA, FIJADO EN PAVIMENTO CON SISTEMA DE SUJECIÓN DE ALTO AGARRE PEGAMENTO EPOXICO 100 A/B (RESINA EPÓXICA/RESINA POLIAMIDA MODIFICADA), RESISTENTE A ALTA TEMPERATURA (VER PLANO DE DETALLES DE SEÑALAMIENTOS HORIZONTAL), INCLUYE: LIMPIEZA PREVIA DE LA SUPERFICIE+C92, PREPARACIÓN DE LA SUPERFICIE, TRAZO, ALINEACIÓN, Y TODO LO NECESARIO PARA SU CORRECTA EJECUCIÓN, TRABAJO TERMINADO.	PZA	9	$681.39	$6,132.51

Totales por Partida		**$57,331.77**
Totales por Grupo		**$57,331.77**
Totales Presup.		**$292,667.93**
Anticipo	**+**	**$0.00**
Amortizac. Ant.	**-**	**$0.00**
SubTotal. Ant.	**=**	**$292,667.92**
IVA	**+**	**$46,826.87**
Total	**=**	**$339,494.79**

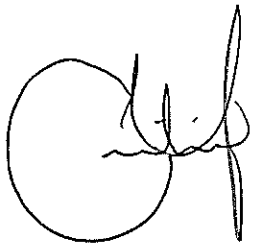

H. AYUNTAMIENTO CONSTITUCIONAL DEL MUNICIPIO DE AGUASCALIENTES 2021-2024

PRESUPUESTO MODIFICADO

Aguascalientes


Obra: CONSTRUCCIÓN DE SOBRECARPETA ASFÁLTICA CALLE GUZMÁN

Ubicación: TRAMO: ENTRE CALLE JOSÉ MARÍA MORELOS Y PAVÓN Y CALLE CONDELL, CENTRO Zona

Contratista: GRUPO REALIZA, S.A. DE C.V. (1010)

Grupo	Partida	Importe
PRELIMINARES		
	PRELIMINARES Y DEMOLICIONES	$29,139.14
	Subtotal por Grupo	**$29,139.14**
SOBRECARPETA ASFALTICA		
	BACHEO PROFUNDO	$5,371.74
	SOBRE CARPETA ASFALTICA	$181,357.76
	OBRA COMPLEMENTARIA	$4,766.40
	LIMPIEZAS	$8,402.40
	Subtotal por Grupo	**$199,898.30**
GUARNICIONES Y BANQUETAS		
	GUARNICIONES	$4,995.51
	BANQUETA Y RAMPA	$1,303.20
	Subtotal por Grupo	**$6,298.71**
SEÑALIZACION		
	SEÑALIZACION HORIZONTAL	$57,331.77
	Subtotal por Grupo	**$57,331.77**

Totales Presup.		**$292,667.93**
Anticipo	+	**$0.00**
Amortizac. Ant.	-	**$0.00**
SubTotal. Ant.	=	**$292,667.92**
IVA	+	**$46,826.87**
Total	=	**$339,494.79**

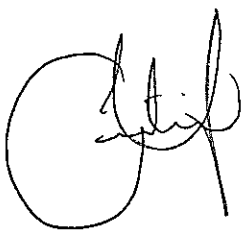

ANALISIS DEL PRESUPUESTO DE OBRA POR CONTRATO

Obra **2022-FISMDF-0141-0411102-077 CONSTRUCCIÓN DE SOBRECARPETA ASFÁLTICA CALLE GUZMÁN, TRAMO: ENTRE CALLE JOSÉ MARÍA MORELOS Y PAVÓN Y CALLE CONDELL**

Programa 04 URBANIZACION MUNICIPAL Subprograma 11 Calles y caminos

Contratista GRUPO REALIZA, S.A. DE C.V. (1010)

Contrato FISMDF-0141-2022 CONSTRUCCIÓN DE SOBRECARPETA ASFÁLTICA CALLE GUZMÁN, TRAMO: ENTRE CALLE JOSÉ MARÍA MORELOS Y PAVÓN Y CALLE CONDELL, CENTRO Zona

Ultima Estim. **2 de 10 Dic 2022 al 19 Dic 2022**

Total Contrato	$339,494.79
Total Ampliaciones	$0.00
Total Contratado	$339,494.79
Anticipo (0 %)	$0.00
Total Estimado	$339,494.79
Total por Estimar	$0.00

No.	Concepto	Unid. Med.	Volumen			% Avanc. Estimado	Precio Contratado	Importe		
			Contratado	Acumulado	Excedente			Contratado	Acumulado	Excedente
GRUPO: PRELIMINARES										
PARTIDA: PRELIMINARES Y DEMOLICIONES										
1	LIMPIA, TRAZO Y NIVELACION EN PAVIMENTOS, CALLES Y VIALIDADES CON EQUIPO TOPOGRAFICO, INCLUYE: EJES, BANCO DE NIVEL, RENIVELACIONES LAS VECES NECESARIAS, CORRECCION DE RASANTE A PUNTOS OBLIGADOS (AUTORIZADOS POR LA SUPERVISION), ESTACAS, VARILLAS, MANO DE OBRA CALIFICADA, HERRAMIENTA NECESARIA, EQUIPO DE PRECISION CALIBRADO, TRABAJO TERMINADO.P.U.O.T.	M2	322.45	273.16		84.71	$8.59	$2,769.85	$2,346.44	
2	SONDEO A MANO O A MAQUINA PARA LOCALIZACION DE TUBERIAS CUALQUIER PROFUNDIDAD Y MATERIAL PARA VERIFICAR LA CALIDAD DE LAS INSTALACIONES HIDRAULICO SANITARIAS CUIDANDO NO DAÑARLAS PARA NO INTERFERIR EN LOS SERVICIOS, INCLUYE: EXCAVACION, EQUIPO, MANO DE OBRA, REPORTE A LA SUPERVISION, RELLENOS, COMPACTACIONES, TRABAJO TERMINADO.	SONDE	2.00	2.00		100.00	$2,063.23	$4,126.46	$4,126.46	
3	CORTE CON DISCO DIAMANTADO DE 14" EN PISOS DE CONCRETO ASFALTICO DE HASTA 8.00 cm. DE PROFUNDIDAD. INCLUYE: TRAZO, EQUIPO Y OPERACION, LIMPIEZAS.	ML	34.72	12.00		34.56	$40.65	$1,411.37	$487.80	
4	DEMOLICION PARCIAL DE PAVIMENTO HIDRAULICO Y/O ASFALTICO DE HASTA 15 CM. DE ESPESOR PROMEDIO EN PAVIMENTOS Y (BANQUETAS, LOSAS DIAMANTE Y CAJAS DE VALVULAS, TOPES) CON O SIN ARMADO DE ACERO, SIN RECUPERACION, MUROS, MOJONERAS, ANCLAJES, ETC, DE FORMA MANUAL Y MECANICA, INCLUYE ACARREO DE MATERIAL AL LUGAR DE ACOPIO, HERRAMIENTA NECESARIA Y TODO LO NECESARIO PARA SU CORRECTA EJECUCION, LIMPIEZA, TRABAJO TERMINADO	M3	2.21	1.00		45.25	$308.09	$680.88	$308.09	
5	FRESADO UNIFORME DE LA SUPERFICIE DE RODADURA EN PAVIMENTO DE CONCRETO ASFALTICO 3-7 CM (5 cm de espesor promedio) MEDIANTE FRESADORA EN FRIO COMPACTA, EQUIPADA CON BANDA TRANSPORTADORA PARA CARGA DIRECTA SOBRE CAMION DE VOLTEO, INCLUYE: TRAMO DE PRUEBA AL INICIO DEL FRESADO PARA AUTORIZACION DE SUPERVISION (SUPERFICIE FRESADA UNIFORME Y SIN PROTUBERANCIAS NI ONDEOS), ACARREOS LOCALES, CARGA Y ACARREO A KM SUBSECUENTES (11 A 15 KM APROX) DE MATERIAL PRODUCTO DEL FRESADO DE CARPETA ASFALTICA EL TRASLADO SERA A PARQUE DE MAQUINARIA DE LA SOPMA, PIEZAS DE DESGASTE, COMBUSTIBLES, CONSUMIBLES, MANO DE OBRA, CUALQUIER VOLUMEN Y AREA,EQUIPO NECESARIO, LIMPIEZA FINA Y GRUESA, TRABAJO TERMINADO.	M3	12.90	16.39	3.49	127.05	$1,276.89	$16,471.88	$20,928.23	$4,456.35
7	DEMOLICION CONTROLADA DE CONCRETO HIDRAULICO EN DENTELLONES Y GUARNICIONES DE 15 x 20 x 40 CM. DE FORMA MANUAL Y MECÁNICA, INCLUYE: CORTES CON DISCO, ACARREO DEL MATERIAL AL LUGAR DE ACOPIO PARA SU CARGA Y ACARREO FUERA DE LA OBRA.	ML	12.40	12.40		100.00	$29.98	$371.75	$371.75	
8	CARGA MECANICA Y ACARREO DE MATERIAL PRODUCTO DE EXCAVACION Y DEMOLICION EN CAMION DE VOLTEO AL 1er. KM, VOLUMEN MEDIDO COMPACTO.	M3	2.36	1.37		58.05	$68.72	$162.18	$94.15	
9	ACARREO DE MATERIAL PRODUCTO DE EXCAVACION Y/O DEMOLICION EN CAMION DE VOLTEO A KILOMETROS SUBSECUENTES, AL TIRADERO OFICIAL AUTORIZADO MAS CERCANO AUTORIZADO POR LA SUPERVISION, VOLUMEN MEDIDO COMPACTO.	M3-KM	70.88	41.16		58.07	$11.57	$820.08	$476.22	
							Totales por Partida:	$26,814.45	$29,139.14	$4,456.35
							Totales por Grupo:	$26,814.45	$29,139.14	$4,456.35

GRUPO: SOBRECARPETA ASFALTICA

ANALISIS DEL PRESUPUESTO DE OBRA POR CONTRATO

No.	Concepto	Unid. Med.	Volumen			% Avanc. Estimado	Precio Contratado	Importe		
			Contratado	Acumulado	Excedente			Contratado	Acumulado	Excedente

GRUPO: SOBRECARPETA ASFALTICA

PARTIDA: BACHEO PROFUNDO

10	BACHEO PROFUNDO AISLADO UTILIZANDO MATERIAL CALIDAD BASE HIDRAULICA PARA MAS DE UN MILLON DE EJES EQUIVALENTES DEL BANCO QUE ELIJA EL CONTRATISTA, INCISO N.CSV.CAR.1.02.004/03 DE LAS NORMAS DE CONSTRUCCION DE CARR. DE LA SCT, INCLUYE: PREPARACION, PERFILADO, MATERIALES, MANO DE OBRA, HERRAMIENTA MENOR Y EQUIPO NECESARIO QUE SE REQUIERA PARA LOGRAR LA COMPACTACION DE 100% PVSM, ACARREOS DENTRO Y FUERA DE LA OBRA, PREPARACION DE MATERIAL, HUMEDECIDO, NIVELADO, TRASLADO DE UN PUNTO A OTRO DENTRO DE LA OBRA, EN CUALQUIER VOLUMEN, MOVIMIENTO DE MAQUINARIA P.U.O.T	M3	0.81	3.90	3.09	481.48	$1,377.37	$1,115.67	$5,371.74	$4,256.07
						Totales por Partida:		**$1,115.67**	**$5,371.74**	**$4,256.07**

PARTIDA: SOBRE CARPETA ASFALTICA

13	PREPARACIÓN DE LA SUPERFICIE DE CONTACTO EN LOS EXTREMOS DONDE LA PERFILADORA NO ALCANCE POR LÍMITES CON LA GUARNICIÓN, CON UN RASPADO SUPERFICIAL CON RETROEXCAVADORA, ELIMINANDO TECATAS QUE HAYAN QUEDADO PARA RENIVELADO, BARRIDOS ENTRE PASADA DE MOTOCONFORMADORA Y EN REMATES DE EMPATES A DETALLE A MANO, INCLUYE: RETIRO DE MATERIAL FUERA DE LA OBRA A TIRADERO OFICIAL INDICADO.	M2	49.60	49.60		100.00	$36.74	$1,822.30	$1,822.30	
14	RENIVELACIONES CON CONCRETO ASFALTICO MEZCLA EN PLANTA EN CALIENTE ASFALTO MODIFICADO CON POLIMERO TIPO I, CUMPLIENDO LAS NORMAS SCT REFERENTES DE CONSTRUCCCION Y CONSERVACION, GRANULOMETRIA DENSA 3/4" A FINOS, MEDIDO COMPACTO AL NOVENTA Y CINCO PORCIENTO (95%), INCLUYE CARGA Y ACARREO EN TRAMOS AISLADOS, MATERIALES, MANO DE CBRA, ACARREO DE MATERIALES, Y MAQUINARIA Y EQUIPO AL SIGUIENTE PUNTO EN CUALQUIER VOLUEN, PERFILADO, LIMPIEZA DE HUESO Y GRAVA SUELTA, TRABAJO TERMINADO P.U.O.T	M3	4.03	4.03		100.00	$7,230.51	$29,138.96	$29,138.96	
17	RIEGO DE LIGA CON EMULSION DE ROMPIMIENTO RAPIDO (ECR-65 %), INCLUYE, SUMINISTRO, ALMACENAMIENTO, CALENTAMIENTO, Y APLICACION DE LA EMULSION CON EQUIPO ESPECIAL PARA ESA ACTIVIDAD, ESPREAS O BACHADOR LIMPIAS Y ALINEADAS, CONTROL DE CALIDAD A CADA DOS REMESAS EN OBRA (INDEPENDIENTEMENTE DE LA CANTIDAD A UTILIZAR) EN LA PETROLIZADORA, A RAZON DE 0.8 LT DE EMULSION POR M2, O LO QUE INDIQUE EL LABORATORIO DE CALIDAD DEL CONTRATISTA, NO SE ACEPTAN "IMPREGNALIGA", TRABAJO TERMINADO, P.U.O.T.	M2	322.45	273.16		84.71	$15.88	$5,120.51	$4,337.78	
18	SUMINISTRO Y COLOCACION DE CONCRETO ASFALTICO EN CALIENTE DE GRANULOMETRIA DENSA ELABORADA CON ASFALTO MODIFICADO TIPO I, AGREGADO 3/4" A FINOS, DE 5 CM DE ESPESOR, FORMADA Y COMPACTADO AL 95%, INCLUYE MATERIALES, QUE CUMPLAN LA NORMATIVA SCT-N-CMT-04-04, SCT-CMT-4-05-002, SCT-CMT-4-05-003, SCT-CMT-4-05-004, SCT-CTR-CAR-1-04-006-14 APLICADAS AL DIA DE HOY, DISEÑO MARSHALL (DEVERÁ SER AUTORIZADO POR EL LABORATORIO DE CALIDAD DE SOPMA AL MENOS 3 DIAS ANTES DE INICIO DE TENDIDO DE LA MEZCLA ASFALTICA), INCUYE: TRAMO DE PRUEBA AL INICIO PARA REVISION Y AUTORIZACION DEL ESPESOR POR PARTE DEL SUPERVISOR, EL CONTRATISTA DEBERÁ PREVEER EL SUMINISTRO Y TIEMPOS MUERTOS POR MOVIMIENTOS DEL TREN DE MAQUINAS DE TRABAJO EN TRAMOS AISLADOS. TRABAJO TERMINADO P.U.O.T. Y LIMPIEZAS DE GRANZON Y HUESO LATERAL.	M2	322.45	467.92	145.47	145.11	$310.44	$100,101.38	$145,261.20	$45,159.71
19	COMPACTACION SOBRE MORTERO ASFALTICO TENDIDO EN APROCHES CON GUARNICIONES CON EQUIPO LIGERO (PLANCHITA), INCLUYE: MANO DE OBRA Y EQUIPO, TRABAJO TERMINADO.	M2	55.46	55.46		100.00	$14.38	$797.51	$797.51	
						Totales por Partida:		**$136,980.66**	**$181,357.76**	**$45,159.71**

PARTIDA: OBRA COMPLEMENTARIA

23	LIMPIEZA Y DESASOLVE DE POZOS DE VISITA Y LINEAS DE ALCANTARILLADO EXISTENTE CON CAMION TIPO VACTOR. INCLUYE: RESANE INTERIOR DEL POZO Y REMTE DE POZO CO TUBO CON SELLADOR, FESTER Y MORTERO 1:3, MANO DE OBRA, SUMINISTRO DE AGUA EN PIPA, HERRAMIENTAS Y EQUIPO PARA SU CORRECTA EJECUCION, LIMPIEZAS, RENTA DE CAMION VACTOR HASTA LA CORRECTA LIMPIEZA DE LAS LINEAS EXISTENTES DE POZO A POZO, ASI COMO EL TRASLADO DE LOS DESECHOS HASTA TIRADERO AUTORIZADO MEDIDO POZO A POZO.	LOTE	1.00	1.00		100.00	$4,766.40	$4,766.40	$4,766.40	
						Totales por Partida:		**$4,766.40**	**$4,766.40**	**$0.00**

No.	Concepto	Unid. Med.	Volumen			% Avanc. Estimado	Precio Contratado	Importe		
			Contratado	Acumulado	Excedente			Contratado	Acumulado	Excedente
GRUPO: SOBRECARPETA ASFALTICA										
PARTIDA: LIMPIEZAS										
24	LIMPIEZA GENERAL DE LA OBRA, INCLUYE: BARRIDO, CARGA, ACARREOS Y RETIRO DE ESCOMBROS FUERA DE LA OBRA, TRABAJO TERMINADO.	M2	322.45	273.16		84.71	$30.76	$9,918.56	$8,402.40	
							Totales por Partida:	$9,918.56	$8,402.40	$0.00
							Totales por Grupo:	$152,781.29	$199,898.30	$49,415.78
GRUPO: GUARNICIONES Y BANQUETAS										
PARTIDA: GUARNICIONES										
25	EXCAVACION A MAQUINA Y/O A MANO EN MATERIAL TIPO II, EN SECO O PRESENCIA DE AGUA, INCLUYE. CORTE DE RAIZ DE CUALQUIER TAMAÑO Y GROSOR, HASTA UNA PROFUNDIDAD DE 40 CM DESPUES DE DESMONTE, DESPALME Y/O DEMOLICION DE SUPERFICIE O ELEMENTO ESTRUCTURAL O DE ACABADO, PROTECCION DE AREAS ADYACENTES, SIN DAÑAR AREAS ALEDAÑAS, CARGA Y ACARREO A TIRADERO OFICIAL, CONSERVACION DE LA MISMA, TRABAJO TERMINADO, LIMPIEZAS.	M3	1.98	1.98		100.00	$314.18	$622.08	$622.08	
26	COMPACTACION DE TERRENO NATURAL AL 90% DE SU P.V.S.M EN SU COMPACTACION., INCLUYE ESCARIFICADO, TENDIDO, HOMOGENIZADO, HUMEDECIDO OPTIMO NIVELADO Y COMPACTADO EN CAPAS DE 20 CM, CALIDAD Limite liquido máximo 50%, Valor de Soporte California (CBR) mínimo 15%, Expansión máxima 5%, Grado de Compactación mínimo 90% ± 2, Y TODO LO NECESARIO PARA SU CORRECTA EJECUCION.	M2	4.96	4.96		100.00	$33.31	$165.22	$165.22	
27	CONSTRUCCION DE GUARNICION RECTA Y/O CURVA TRAPEZOIDAL 15-20X40 CM DE SECCION CON CONCRETO PREMEZCLADO MR=38 KGF/CM2, R.N.REVENIMIENTO DE 8 A 10 CM, T.M.A. 3/4", GRAVA TRITURADA, ACABADO PULIDO EN PARTE DE SUPERIOR Y DOBLADOR EN ARISTAS, INCLUYE: COMPACTADO DE PLANTILLA, CIMBRADO, COLADO, VIBRADO, ACABADO, DESCIMBRADO, ALINEADO, NIVELADO, Y CURADO EN SU PARTE SUPERIOR CON MEMBRANA BASE AGUA A RAZON DE 1 LTO/M2, JUNTA DE AISLAMIENTO LONGITUDINAL AL COMBINAR CON OTRO ELEMENTO Y TRANSVERSAL @ 30 MT MAXIMO, SELLADO CON SELLADOR AUTONIVELANTE LONGITUDINAL, TRABAJO TERMINADO, .P.U.O.T.	ML	12.40	12.40		100.00	$262.77	$3,258.35	$3,258.35	
28	RELLENO COMPACTADO AL 95% CON MATERIAL DE BANCO EN CAPAS DE 20 CM UTILIZANDO BAILARINA, INCLUYE: SUMINISTRO DE TEPETATE (MATERIAL DE BANCO) EN LA OBRA, ABUNDAMIENTO, ACARREOS DENTRO DE LA OBRA, CRIBADO, RETIRO DE MATERIAL, MANO DE OBRA Y EQUIPO, LIMPIEZAS, TRABAJO TERMINADO.	M3	0.37	0.37		100.00	$419.27	$155.13	$155.13	
29	CARGA MECANICA Y ACARREO DE MATERIAL PRODUCTO DE EXCAVACION Y DEMOLICION EN CAMION DE VOLTEO AL 1er. KM, VOLUMEN MEDIDO COMPACTO.	M3	2.36	2.36		100.00	$55.83	$131.76	$131.76	
30	ACARREO DE MATERIAL PRODUCTO DE EXCAVACION Y/O DEMOLICION EN CAMION DE VOLTEO A KILOMETROS SUBSECUENTES, AL TIRADERO OFICIAL AUTORIZADO MAS CERCANO AUTORIZADO POR LA SUPERVISION, VOLUMEN MEDIDO COMPACTO.	M3-KM	70.68	70.68		100.00	$9.38	$662.98	$662.98	
							Totales por Partida:	$4,995.51	$4,995.51	$0.00
PARTIDA: BANQUETA Y RAMPA										
39	CONSTRUCCION DE RAMPA Y BANQUETA DE USO HABITACIONAL PARA TRAFICO VEHICULAR, DE 12 CM DE ESPESOR A BASE DE CONCRETO PREMEZCLADO MR=38 KGF/CM2, T.M.A. 1 1/2", R.R 7 DIAS. GRAVA TRITURADA, REVENIMIENTI DE 10+-2 CM, ACABADO RAYADO FINO CON BROCHA DE PELO, JUNTAS FRIAS CON DOBLADOR DE 2" SECCION DE LOSAS COMO INDIQUE PROYECTO, INCLUYE: JUNTA DE AISLAMIENTO Y DE EXPANSION A BASE DE ESPUMA DE POLIETILENO DE CELDAS CERRADAS DE 1/2" EN JUNTAS FRIAS LONGITUDINALES CON MUROS Y TRANSVERSALES DEL ELEMENTO, ASI COMO SU UNION CON ELEMENTOS VIEJOS O CAMBIO DE ELEMENTO, CIMBRADO, COLADO, DESCIMBRADO, CORTES CON CORTADORA DE DISCO, SELLADO DE CORTES CON SELLADOR AUTONIVELANTE Y TIRA DE RELLENO PREFORMADA NO ADHERENTE DE 1/8" (EN TODAS LAS JUNTAS DE CONTRACCION Y CONSTRUCCION TRANSVERSALES), CURADO CON MEMBRANA QUIMICA APLICADA CON ASPERSOR, TRABAJO TERMINADO FICHA TECNICA 216	M2	6.29	2.25		35.77	$579.20	$3,643.17	$1,303.20	
							Totales por Partida:	$3,643.17	$1,303.20	$0.00
							Totales por Grupo:	$8,638.68	$6,298.71	$0.00

No.	Concepto	Unid. Med.	Volumen			% Avanc. Estimado	Precio Contratado	Importe		
			Contratado	Acumulado	Excedente			Contratado	Acumulado	Excedente

GRUPO: SEÑALIZACION

PARTIDA: SEÑALIZACION HORIZONTAL

40	SUMINISTRO Y APLICACIÓN DE PINTURA EPOXICA BASE SOLVENTE COLOR AZUL (PANTONE 294) EN RAMPAS PARA PERSONAS CON DISCAPACIDAD CUALQUIER SECCIÓN SEGÚN PLANOS. INCLUYE: TRAZO, MANC DE OBRA, LIMPIEZA PREVIA DE SUPERFICIE, EQUIPO NECESARIO PARA SU EJECUCIÓN, Y TODO LO NECESARIO PARA SU CORRECTA EJECUCIÓN, TRABAJO TERMINADO.	M2	12.00	12.00		100.00	$370.14	$4,441.68	$4,441.68	
41	SUMINISTRO Y APLICACIÓN DE LOGOTIPO A (SILLA DE RUEDAS) EN PINTURA EPOXICA BASE SOLVENTE COLOR BLANCO EN RAMPAS PARA PERSONAS CON DISCAPACIDAD TAMAÑO Y DISEÑO SEGÚN PLANOS. INCLUYE: TRAZO, ENMASCARILLADO, PLANTILLA, MANO DE OBRA, LIMPIEZA PREVIA DE SUPERFICIE, EQUIPO NECESARIO PARA SU EJECUCIÓN, Y TODO LO NECESARIO PARA SU CORRECTA EJECUCIÓN, TRABAJO TERMINADO.	PZA	7.00	7.00		100.00	$487.55	$3,412.85	$3,412.85	
42	SUMINISTRO Y APLICACIÓN DE PINTURA BASE SOLVENTE PARA MARCAS EN GUARNICIONES CLASIFICACION M-12.1, M12.2 APLICADA SOBRE GUARNICIONES Y DENTELLONES DE CUALQUIER COLOR, SEGÚN SE REQUIERA Y SEGÚN NORMA S.C.T. SECADO AL TACTO EN 5 MIN Y AL DURO EN 30 MIN CON MICRO ESFERA , DESARROLLO DE 35 CM. INCLUYE: MATERIALES Y ESPECIFICACIONES QUE CUMPLAN CON LA NORMATIVA N-CMT-5-01-001/05, N-PRY-CAR-10-01-002/13 APLICADAS AL DIA DE HOY, TRAZO, MANO DE OBRA, LIMPIEZA PREVIA DE SUPERFICIE, EQUIPO NECESARIO PARA SU EJECUCIÓN, Y TODO LO NECESARIO PARA SU CORRECTA EJECUCIÓN, TRABAJO TERMINADO.	ML	124.00	124.00		100.00	$80.66	$10,001.84	$10,001.84	
43	SUMINISTRO Y APLICACIÓN DE PINTURA TERMOPLASTICA ALQUIDALICA DE 120 MILESIMAS DE " (in) EN RAYA EN LA ORILLA DEL ARROYO VIAL CLASIFICACIÓN M - 3.3, CONTINUA IZQUIERDA, PARA VIALIDADES URBANAS DE FRENTE EN PISO, DE 10 CM DE ANCHO Y SEPARADA 15 CM. DE LA GUARNICION, A BASE DE PINTURA PARA TRAFICO COLOR BLANCO CON MICRO ESFERA SEGÚN MANUAL DE SEÑALIZACIÓN VIAL Y DISPOSITIVOS DE SEGURIDAD SICT (S.C.T)., INCLUYE: MATERIALES Y ESPECIFICACIONES QUE CUMPLAN CON LA NORMATIVA N-CMT-5-01-001/13, N-PRY-CAR-10-01-002/13 APLICADAS AL DIA DE HOY, MATERIAL APLICADO EN SU ESTADO DE FUSION A UNA TEMPERATURA MINIMA DE 204 C, LA SUPERFICIE DE CONCRETO O ASFALTO NO DEBE PRESENTAR UNA TEMPERATURA MENOR A LOS 10 C, ;TIEMPO DE SECADO EN RANGOS DE TEMPERATURA DE 10 C DEL SUSTRATO 2 MINUTOS, Y NO MAS DE 10 MINUTOS CUANDO EL SUSTRATO OSCILA ALREDEDOR DE 54C, TRAZO, ENMASCARILLADO, MANO DE OBRA, LIMPIEZA PREVIA Y FINAL DE SUPERFICIE, EQUIPO NECESARIO PARA SU EJECUCIÓN, Y TODO LO NECESARIO PARA SU CORRECTA EJECUCIÓN, TRABAJO TERMINADO.	ML	108.00	108.00		100.00	$63.33	$6,839.64	$6,839.64	
44	SUMINISTRO Y APLICACIÓN DE PINTURA TERMOPLASTICA ALQUIDALICA DE 120 MILESIMAS DE " (in) EN RAYA PARA CRUCE PEATONAL CLASIFICACIÓN M - 7.1, PARA INDICAR " CRUCE PEATONAL EN VIAS PRIMARIAS", COLOR AMARILLO, REFLEJANTE CON MICRO ESFERA DE VIDRIO EN PROPORCIÓN SEGÚN MANUAL DE SEÑALIZACIÓN VIAL Y DISPOSITIVOS DE SEGURIDAD SICT (S.C.T). DE 0.40 MTS DE ANCHO Y 3.5 MTS. DE LONGITUD POR EL ANCHO DE LA VIALIDAD, CON UNA SEPARACIÓN DE 0.40 MTS. ENTRE ELLAS, INCLUYE: MATERIALES Y ESPECIF CACIONES QUE CUMPLAN CON LA NORMATIVA N-CMT-5-01-001/13, N-PRY-CAR-10-01-002/13 APLICADAS AL DIA DE HOY, MATERIAL APLICADO EN SU ESTADO DE FUSION A UNA TEMPERATURA MINIMA DE 204 C, LA SUPERFICIE DE CONCRETO O ASFALTO NO DEBE PRESENTAR UNA TEMPERATURA MENOR A LOS 10 C, ;TIEMPO DE SECADO EN RANGOS DE TEMPERATURA DE 10 C DEL SUSTRATO 2 MINUTOS, Y NO MAS DE 10 MINUTOS CUANDO EL SUSTRATO OSCILA ALREDEDOR DE 54C, TRAZO, ENMASCARILLADO, MANO DE OBRA, LIMPIEZA PREVIA Y FINAL DE SUPERFICIE, EQUIPO NECESARIO PARA SU EJECUCIÓN, Y TODO LO NECESARIO PARA SU CORRECTA EJECUCIÓN, TRABAJO TERMINADO.	M2	37.80	37.80		100.00	$527.92	$19,955.38	$19,955.38	

No.	Concepto	Unid. Med.	Volumen			% Avanc. Estimado	Precio Contratado	Importe		
			Contratado	Acumulado	Excedente			Contratado	Acumulado	Excedente

GRUPO: SEÑALIZACION

PARTIDA: SEÑALIZACION HORIZONTAL

45	SUMINISTRO Y APLICACIÓN DE PINTURA TERMOPLASTICA ALQUIDALICA DE 120 MILESIMAS DE " (in) EN FLECHAS CLASIFICACIÓN M - 11.1, "FLECHA SENCILLA" PARA INDICAR SENTIDO DE CIRCULACIÓN , EN VIALIDADES PARA VELOCIDAD MENOR A 60KM POR HORA DIMENSION NORMATIVA SEGUN MANUAL DE SEÑALIZACIÓN VIAL Y DISPOSITIVOS DE SEGURIDAD SICT (SCT) Y/O (VER PLANO DE SEÑALAMIENTOS), COLOR BLANCO, REFLEJANTE CON MICRO ESFERA DE VIDRIO EN PROPORCIÓN SEGÚN NORMA SCT, INCLUYE: MATERIALES Y ESPECIFICACIONES QUE CUMPLAN CON LA NORMATIVA N-CMT-5-01-001/13, N-PRY-CAR-10-01-002/13 APLICADAS AL DIA DE HOY, MATERIAL APLICADO EN SU ESTADO DE FUSION A UNA TEMPERATURA MINIMA DE 204 C, LA SUPERFICIE DE CONCRETO O ASFALTO NO DEBE PRESENTAR UNA TEMPERATURA MENOR A LOS 10 C, ;TIEMPO DE SECADO EN RANGOS DE TEMPERATURA DE 10 C DEL SUSTRATO 2 MINUTOS, Y NO MAS DE 10 MINUTOS CUANDO EL SUSTRATO OSCILA ALREDEDOR DE 54C, TRAZO, ENMASCARILLADO, MANO DE OBRA, LIMPIEZA PREVIA Y FINAL DE SUPERFICIE, EQUIPO NECESARIO PARA SU EJECUCIÓN, Y TODO LO NECESARIO PARA SU CORRECTA EJECUCIÓN, TRABAJO TERMINADO.	PZA	1.00	1.00		100.00	$1,318.52	$1,318.52	$1,318.52	
46	SUMINISTRO Y APLICACIÓN DE PINTURA TERMOPLASTICA ALQUIDALICA DE 120 MILESIMAS DE " (in) EN FLECHAS CLASIFICACIÓN M - 11.1, " FLECHA CABEZA DOBLE" PARA INDICAR SENTIDO DE CIRCULACIÓN (VUELTA IZQUIERDA O DERECHA), EN VIALIDADES PARA VELOCIDAD MENOR A 60KM POR HORA SEGUN MANUAL DE SEÑALIZACIÓN VIAL Y DISPOSITIVOS DE SEGURIDAD SICT (SCT), (VER PLANO DE SEÑALAMIENTOS), EN COLOR BLANCO, REFLEJANTE CON MICRO ESFERA DE VIDRIO EN PROPORCIÓN SEGÚN NORMA SCT, INCLUYE: MATERIALES Y ESPECIFICACIONES QUE CUMPLAN CON LA NORMATIVA N-CMT-5-01-001/13, N-PRY-CAR-10-01-002/13 APLICADAS AL DIA DE HOY, MATERIAL APLICADO EN SU ESTADO DE FUSION A UNA TEMPERATURA MINIMA DE 204 C, LA SUPERFICIE DE CONCRETO O ASFALTO NO DEBE PRESENTAR UNA TEMPERATURA MENOR A LOS 10 C, ;TIEMPO DE SECADO EN RANGOS DE TEMPERATURA DE 10 C DEL SUSTRATO 2 MINUTOS, Y NO MAS DE 10 MINUTOS CUANDO EL SUSTRATO OSCILA ALREDEDOR DE 54C, TRAZO, ENMASCARILLADO, MANO DE OBRA, LIMPIEZA PREVIA Y FINAL DE SUPERFICIE, EQUIPO NECESARIO PARA SU EJECUCIÓN, Y TODO LO NECESARIO PARA SU CORRECTA EJECUCIÓN, TRABAJO TERMINADO	PZA	1.00	1.00		100.00	$1,977.82	$1,977.82	$1,977.82	
47	SUMINISTRO Y APLICACIÓN DE PINTURA TERMOPLASTICA ALQUIDALICA DE 120 MILESIMAS DE " (in) EN RAYA DE ALTO CLASIFICACIÓN M - 6, PARA INDICAR ALTO EN CRUCEROS, COLOR BLANCO, REFLEJANTE CON MICRO ESFERA DE VIDRIO EN PROPORCIÓN SEGÚN MANUAL DE SEÑALIZACIÓN VIAL Y DISPOSITIVOS DE SEGURIDAD SICT (S.C.T). DE 0.60 MTS DE ANCHO DE LONGITUD VARIABLE, INCLUYE: MATERIALES Y ESPECIFICACIONES QUE CUMPLAN CON LA NORMATIVA N-CMT-5-01-001/13, N-PRY-CAR-10-01-002/13 APLICADAS AL DIA DE HOY, MATERIAL APLICADO EN SU ESTADO DE FUSION A UNA TEMPERATURA MINIMA DE 204 C, LA SUPERFICIE DE CONCRETO O ASFALTO NO DEBE PRESENTAR UNA TEMPERATURA MENOR A LOS 10 C, ;TIEMPO DE SECADO EN RANGOS DE TEMPERATURA DE 10 C DEL SUSTRATO 2 MINUTOS, Y NO MAS DE 10 MINUTOS CUANDO EL SUSTRATO OSCILA ALREDEDOR DE 54C, TRAZO, ENMASCARILLADO, MANO DE OBRA, LIMPIEZA PREVIA Y FINAL DE SUPERFICIE, EQUIPO NECESARIO PARA SU EJECUCIÓN, Y TODO LO NECESARIO PARA SU CORRECTA EJECUCIÓN, TRABAJO TERMINADO.	ML	5.40	5.40		100.00	$372.07	$2,009.18	$2,009.18	
48	SUMINISTRO Y COLOCACION DE VIALETA STANDARD (S-200) DE 10X10CM. COLOR: CUERPO AMARILLO Y REFLEJANTE AMARILLO 1 CARA MARCA SEA O SIMILAR EN CALIDAD Y ESPECIFICACIONES DE FICHA TECNICA, ANCLADO EN PAVIMENTO SISTEMA DE SUJECION DE ALTO AGARRE BASE CUÑAS CON AB PEGAMENTO EPOXICO 50/50 RESISTENTE A ALTA TEMPERATURA (VER PLANO DE DETALLES DE SEÑALAMIENTOS HORIZONTAL Y VERTICAL). INCLUYE: TRAZO, ALINEACION, ELEVACION CUALQUIER ALTURA, TRABAJO TERMINADO, LIMPIEZAS.	PZA	18.00	18.00		100.00	$69.02	$1,242.36	$1,242.36	
49	SUMINISTRO Y COLOCACION DE VIALETA SOLAR DE 10X10CM. COLOR: CUERPO ALUMINIO 3 LED DOS CARAS REFLEJANTES MARCA CREATIVAL VT-29 O SIMILAR EN CALIDAD Y ESPECIFICACIONES DE FICHA TÉCNICA, FIJADO EN PAVIMENTO CON SISTEMA DE SUJECIÓN DE ALTO AGARRE PEGAMENTO EPOXICO 100 A/B (RESINA EPÓXICA/RESINA POLIAMIDA MODIFICADA), RESISTENTE A ALTA TEMPERATURA (VER PLANO DE DETALLES DE SEÑALAMIENTOS HORIZONTAL), INCLUYE: LIMPIEZA PREVIA DE LA SUPERFICIE+C92, PREPARACIÓN DE LA SUPERFICIE, TRAZO, ALINEACIÓN. Y TODO LO NECESARIO PARA SU CORRECTA EJECUCIÓN, TRABAJO TERMINADO.	PZA	9.00	9.00		100.00	$681.39	$6,132.51	$6,132.51	
							Totales por Partida:	**$57,331.77**	**$57,331.77**	**$0.00**

No.	Concepto	Unid. Med.	Volumen			% Avanc. Estimado	Precio Contratado	Importe		
			Contratado	Acumulado	Excedente			Contratado	Acumulado	Excedente

GRUPO: **SEÑALIZACION**

Totales por Grupo:	$57,331.77	$57,331.77	$0.00
Total del Presupuesto	$0.00	$292,667.93	$53,872.13

H. AYUNTAMIENTO DE AGUASCALIENTES
SECRETARÍA DE OBRAS PÚBLICAS
DIRECCIÓN DE SUPERVISIÓN DE OBRA


Aguascalientes
LA CIUDAD DE TU VIDA


MEMORIA FOTOGRÁFICA


OBRA:	CONSTRUCCIÓN DE SOBRECARPETA ASFÁLTICA CALLE GUZMÁN, TRAMO: ENTRE CALLE JOSÉ MARÍA MORELOS Y PAVÓN Y CALLE CONDELL, CENTRO Zona		
NO. DE CONTRATO:	FISMDF-0141-2022	CONTRATISTA:	GRUPO REALIZA, S.A. DE C.V.

INICIO



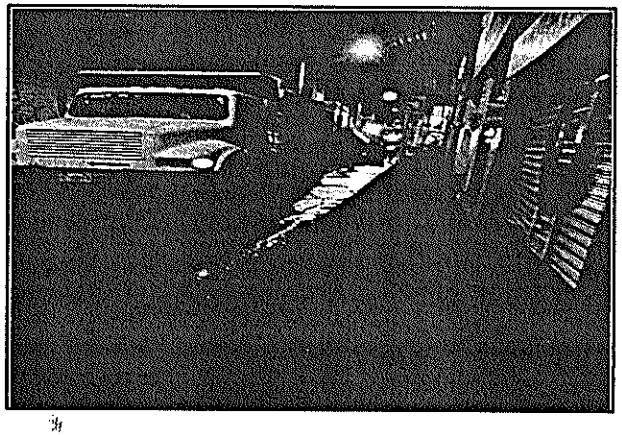

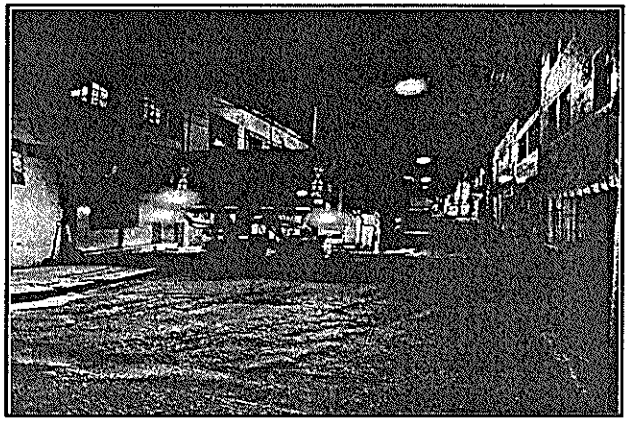

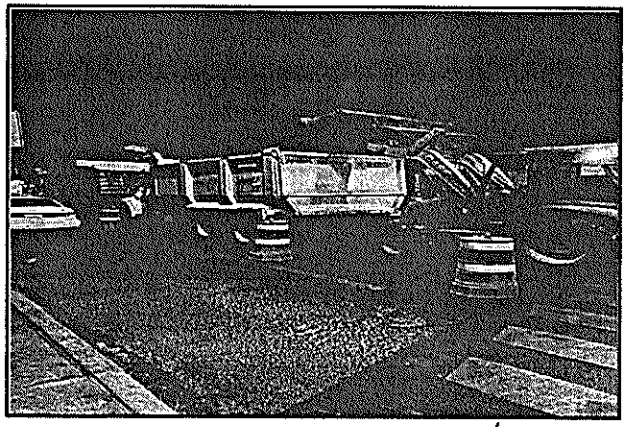

I.C. LAURA CECILIA MARTÍNEZ ALBA
RESIDENTE DE SUPERVISIÓN


H. AYUNTAMIENTO DE AGUASCALIENTES
SECRETARÍA DE OBRAS PÚBLICAS
DIRECCIÓN DE SUPERVISIÓN DE OBRA

Aguascalientes
LA CIUDAD DE TU VIDA


MEMORIA FOTOGRÁFICA


OBRA:	CONSTRUCCIÓN DE SOBRECARPETA ASFÁLTICA CALLE GUZMÁN, TRAMO: ENTRE CALLE JOSÉ MARÍA MORELOS Y PAVÓN Y CALLE CONDELL, CENTRO Zona		
NO. DE CONTRATO:	FISMDF-0141-2022	CONTRATISTA:	GRUPO REALIZA, S.A. DE C.V.

PROCESO

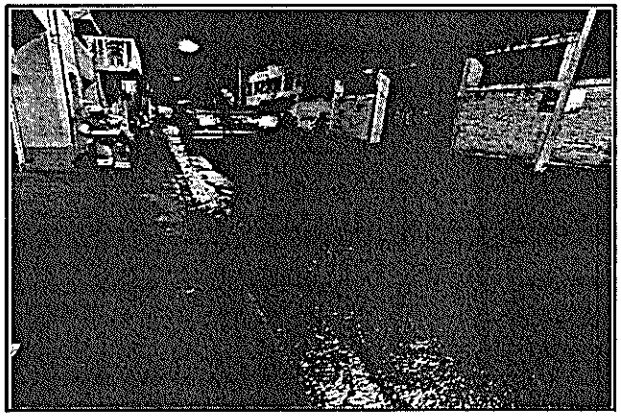



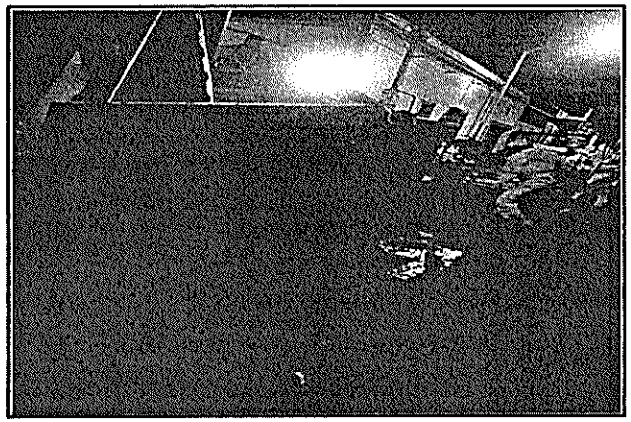

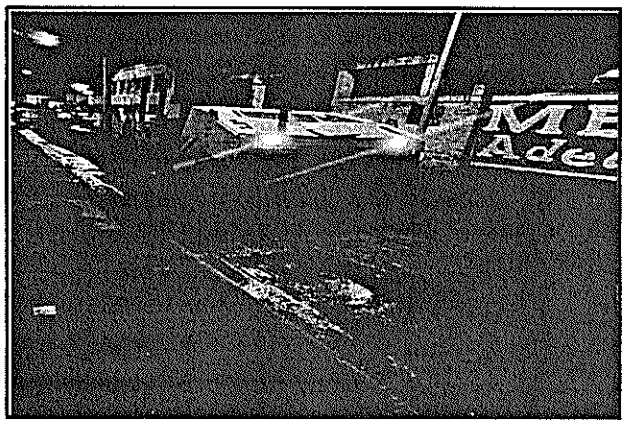

I.C. LAURA CECILIA MARTINEZ ALBA
RESIDENTE DE SUPERVISIÓN


H. AYUNTAMIENTO DE AGUASCALIENTES
SECRETARÍA DE OBRAS PÚBLICAS
DIRECCIÓN DE SUPERVISIÓN DE OBRA

Aguascalientes
LA CIUDAD DE TU VIDA

MEMORIA FOTOGRÁFICA


OBRA:	CONSTRUCCIÓN DE SOBRECARPETA ASFÁLTICA CALLE GUZMÁN, TRAMO: ENTRE CALLE JOSÉ MARÍA MORELOS Y PAVÓN Y CALLE CONDELL, CENTRO Zona		
NO. DE CONTRATO:	FISMDF-0141-2022	CONTRATISTA:	GRUPO REALIZA, S.A. DE C.V.

FINAL

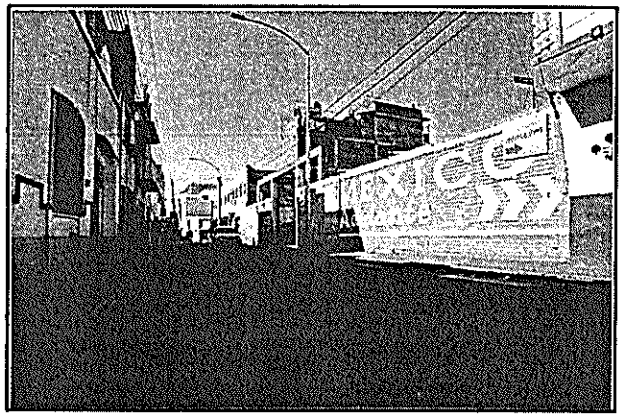





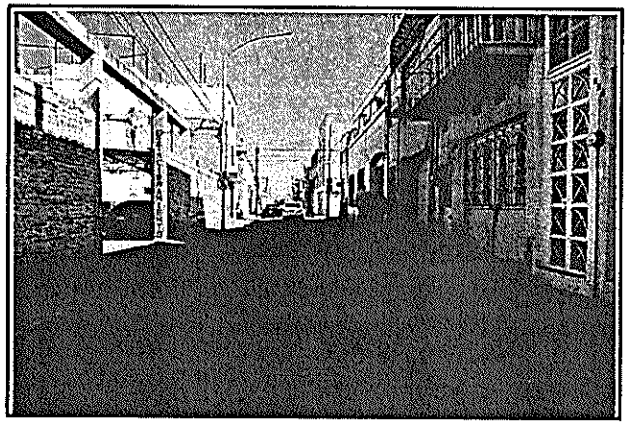

I.C. LAURA CECILIA MARTÍNEZ ALBA
RESIDENTE DE SUPERVISIÓN

EXPEDIENTE MODIFICADO

SECRETARÍA DE OBRAS PÚBLICAS

DIRECCIÓN DE SUPERVISIÓN DE OBRA

EJERCICIO: 2022

Nº DE CONTRATO: FISMDF-0141-2022

NOMBRE DE LA OBRA: CONSTRUCCIÓN DE SOBRECARPETA ASFÁLTICA CALLE GUZMÁN, TRAMO: ENTRE CALLE JOSÉ MARÍA MORELOS Y PAVÓN Y CALLE CONDELL, CENTRO Zona

MONTO MODIFICADO FINAL: $339,494.79


VOLUMEN	UNIDAD	COMPONENTE DE LA OBRA	MONTO
16.39	M3	FRESADO UNIFORME DE LA SUPERFICIE DE RODADURA EN PAVIMENTO	$ 29,139.14
3.90	M3	BACHEO PROFUNDO AISLADO UTILIZANDO MATERIAL CALIDAD BASE	$ 5,371.74
467.92	M2	SUMINISTRO Y COLOCACION DE CONCRETO ASFALTICO EN CALIENTE	$ 181,357.76
1.00	LOTE	LIMPIEZA Y DESASOLVE DE POZOS DE VISITA Y LINEAS DE	$ 4,766.40
273.16	M2	LIMPIEZA GENERAL DE LA OBRA, INCLUYE: BARRIDO, CARGA, ACARREOS	$ 8,402.40
12.40	ML	CONSTRUCCION DE GUARNICION RECTA Y/O CURVA TRAPEZOIDAL 15-	$ 4,995.51
37.80	M2	SUMINISTRO Y APLICACIÓN DE PINTURA TERMOPLASTICA ALQUIDALICA	$ 1,303.20
			$ 57,331.77


MONTO BASE: $ 292,667.92

IVA: $ 46,826.87

TOTAL: $ 339,494.79

I.C. Laura Cecilia Martínez Alba
RESIDENTE DE SUPERVISIÓN

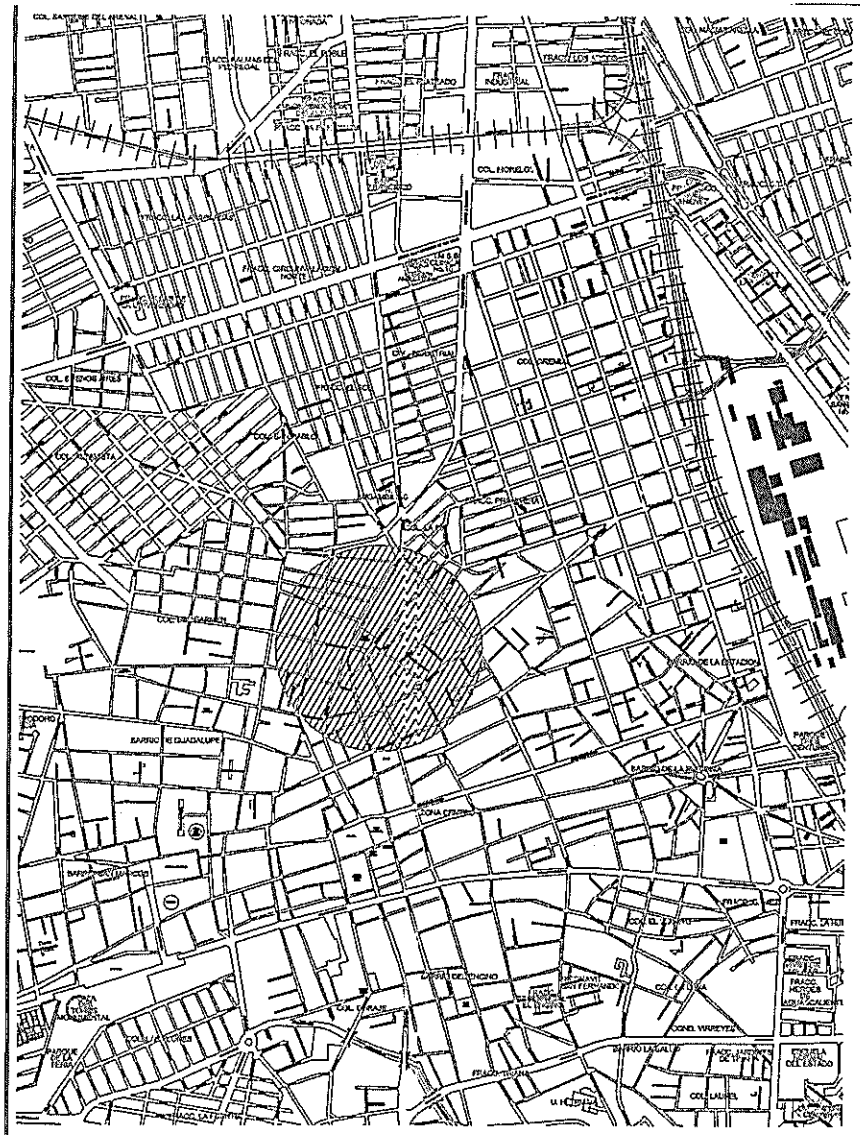

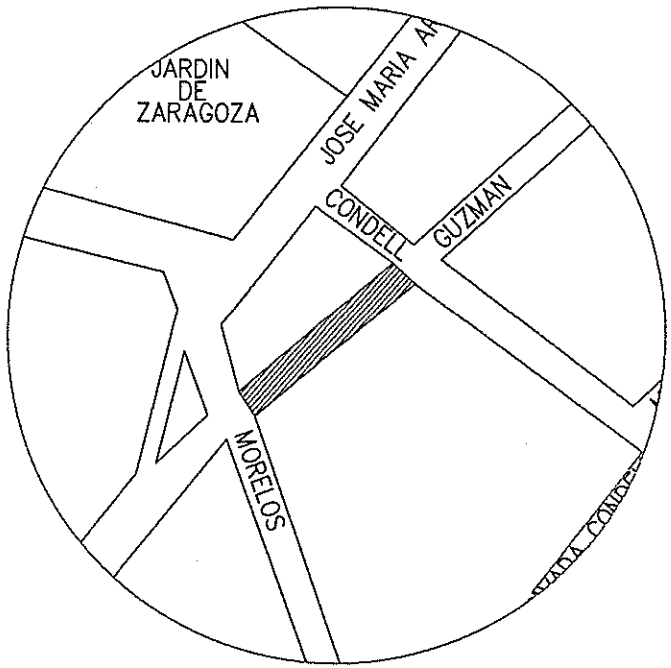


CROQUIS DE LOCALIZACIÓN

SIN ESCALA

C. GUZMAN

LOCALIZACIÓN:

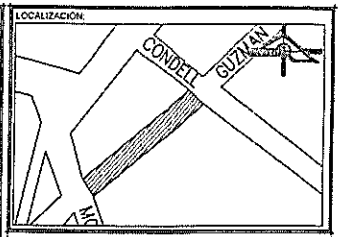

SIMBOLOGÍA

La Dirección de Planeación y Proyectos solo autoriza el proyecto ejecutivo, no es responsable de la correcta ejecución de la obra. Este documento no tiene validez si no presenta las firmas de los responsables para su autorización, así como los sellos respectivos.

PRESIDENTE MUNICIPAL
M.P.P. Leonardo Montañez Castro
SECRETARIO DE OBRAS PUBLICAS
Ing. Miguel Ángel Hulzar Botello

REV	FECHA	OBSERVACIONES

V°B° DE LA DIRECTORA

RESP. DE PROY. EXTERNO		LOGO EXTERNO
CED. PROFESIONAL		
PROYECTO	REVISO	AUTORIZO


Dirección de Planeación y Proyectos de Obra — Secretaría de Obras Públicas

PROYECTISTA	COORDINADOR
ARQ. DANIELA DEL CARMEN RODRIGUEZ LARA	ARQ. ALEJANDRO JAIME LEAL
JEFE DE DEP.	DIRECTOR
LIC. OMAR ALEJANDRO VILLALPANDO CAMPOS	ARQ. ALBERTO PONCE RODRIGUEZ

PROYECTO	CONSTRUCCIÓN DE SOBRECARPETA ASFALTICA CALLE GUZMAN COL. CENTRO
UBICACIÓN	TRAMO ENTRE C. JOSE MARIA MORELOS Y PAVON Y C. CONDELL
CONTENIDO	CROQUIS DE LOCALIZACIÓN

CLAVE	No. PLANO
LOC 01	01
FECHA NOV 2022	ESCALA INDICADA
ACOTACIÓN METROS	No. EXP. E-000-22


Aguascalientes
LA CIUDAD DE TU VIDA

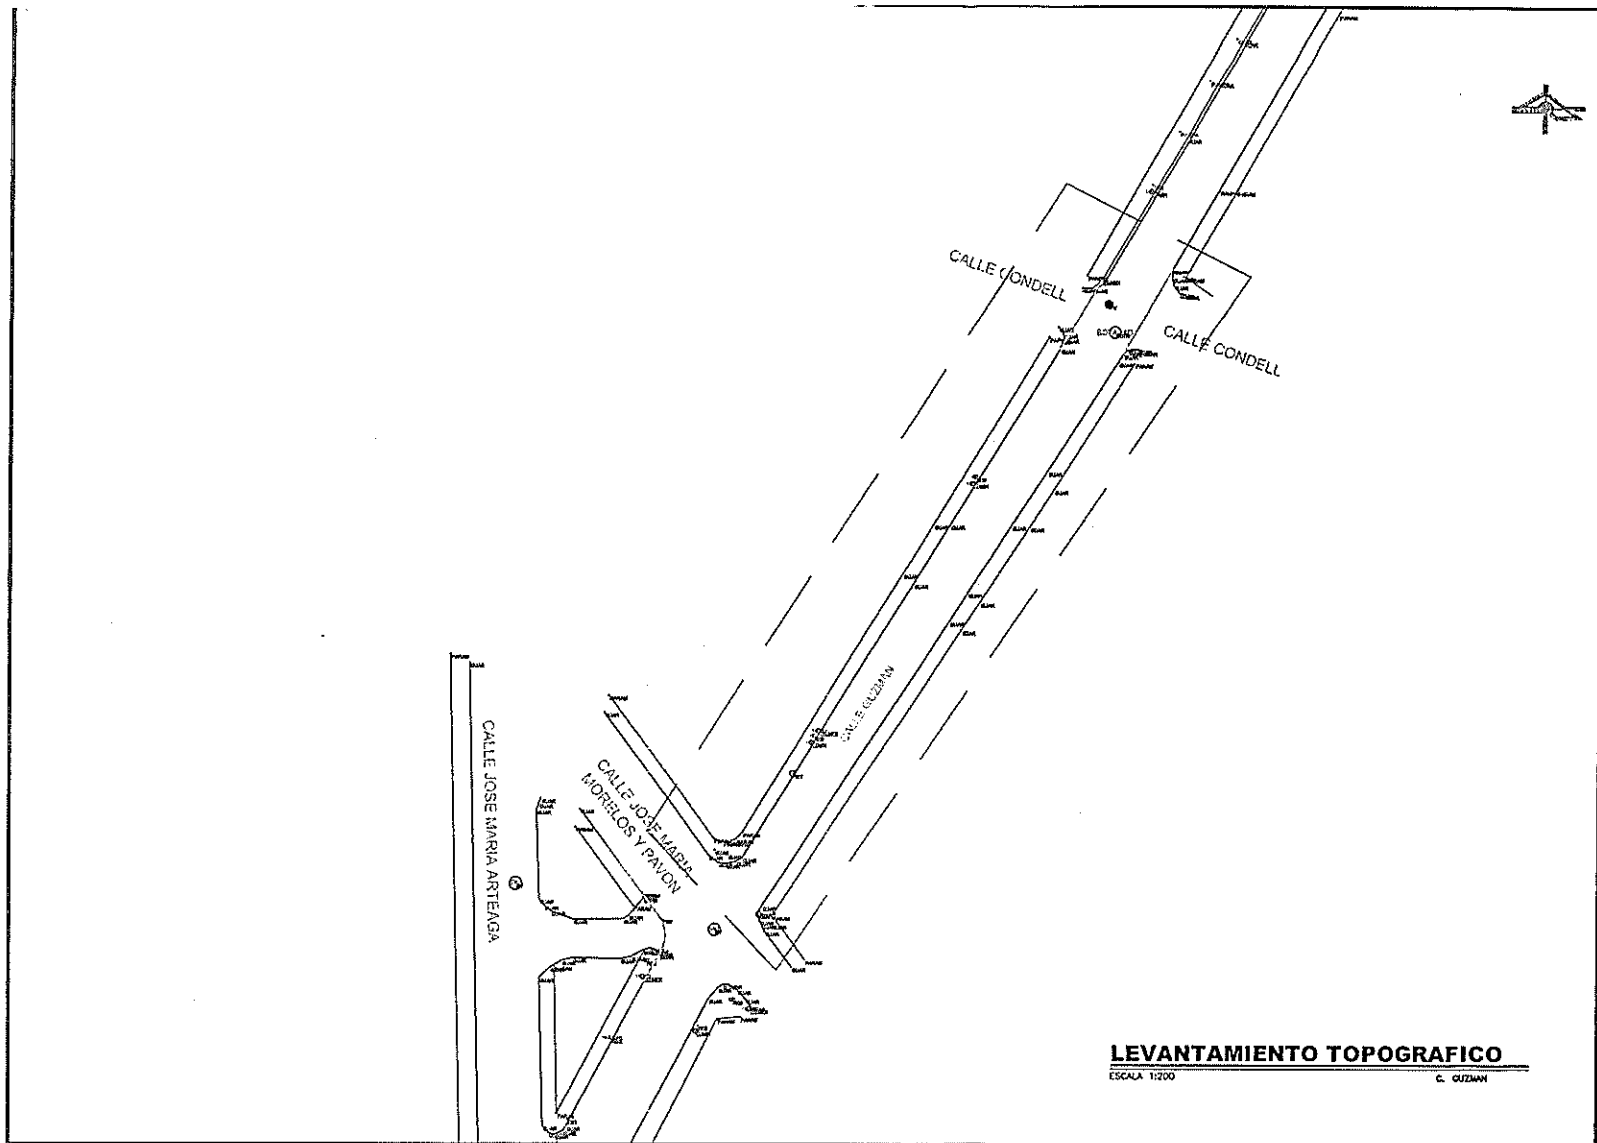

LEVANTAMIENTO TOPOGRAFICO

ESCALA 1:200

LOCALIZACIÓN

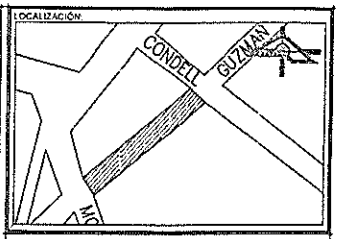

SIMBOLOGIA

SIMBOLOGIA

- LIMITE DE PROYECTO
- POSTE LUMINARIA
- POSTE DE CFE
- POSTE DE TELMEX
- REGISTRO
- POSTE
- REGISTROS CFE
- REGISTRO SEMAFORC
- REGISTROS TELMEX
- TELEFONO
- POZO DE VISITA
- BOTA-HG
- SEMAFOROS
- CAMARAS
- ANUNCIO
- RETENIDA POSTE

La Dirección de Planeación y Proyectos solo autoriza el proyecto ejecutivo, no es responsable de la correcta ejecución de la obra. Este documento no tiene validez si no presenta las firmas de los responsables paraeu autorización, así como los sellos respectivos.

PRESIDENTE MUNICIPAL
M.P.P. Leonardo Montañez Castro
SECRETARIO DE OBRAS PÚBLICAS
Ing. Miguel Ángel Huizar Botello

REV	FECHA	OBSERVACIONES

V°B° DE LA DEPENDENCIA

RESP. DE PROY. EXTERNO		LOGO EXTERNO
CED. PROFESIONAL		
PROYECTO	REVISO	AUTORIZÓ

Dirección de Planeación y Proyectos de Obra — Secretaría de Obras Públicas

PROYECTISTA	COORDINADOR
ARQ. DANIEL MURET RODRIGUEZ TAPIA	ARQ. ALEJANDRO JAIME LEAL
JEFE DE DEP.	DIRECTOR
LIC. OMAR ALEJANDRO LUJAN GARCIA	ARQ. RESNANDO PONCE RODRIGUEZ


PROYECTO
CONSTRUCCIÓN DE SOBRECARPETA ASFALTICA CALLE GUZMAN COL. CENTRO

UBICACIÓN
TRAMO ENTRE C. JOSE MARIA MORELOS Y PAVON Y C. CONDELL


CONTENIDO
LEVANTAMIENTO TOPOGRAFICO


CLAVE	No. PLANO
LEV 01	02
FECHA NOV 2022	ESCALA INDICADA
ACOTACIÓN METROS	No. EXP. E-000-22

Aguascalientes
LA CIUDAD DE TU VIDA

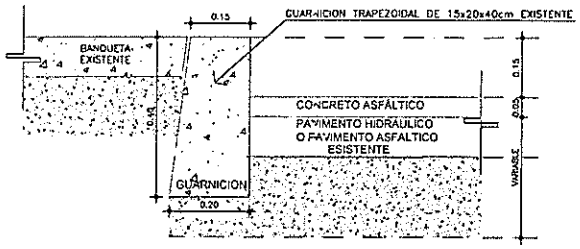

ESTADO ACTUAL

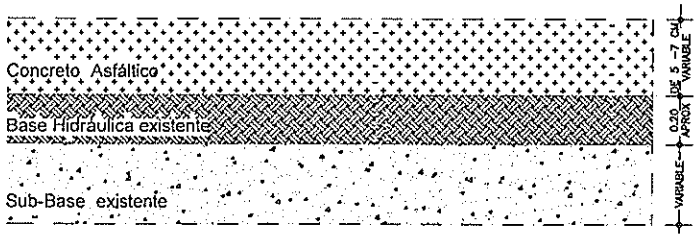


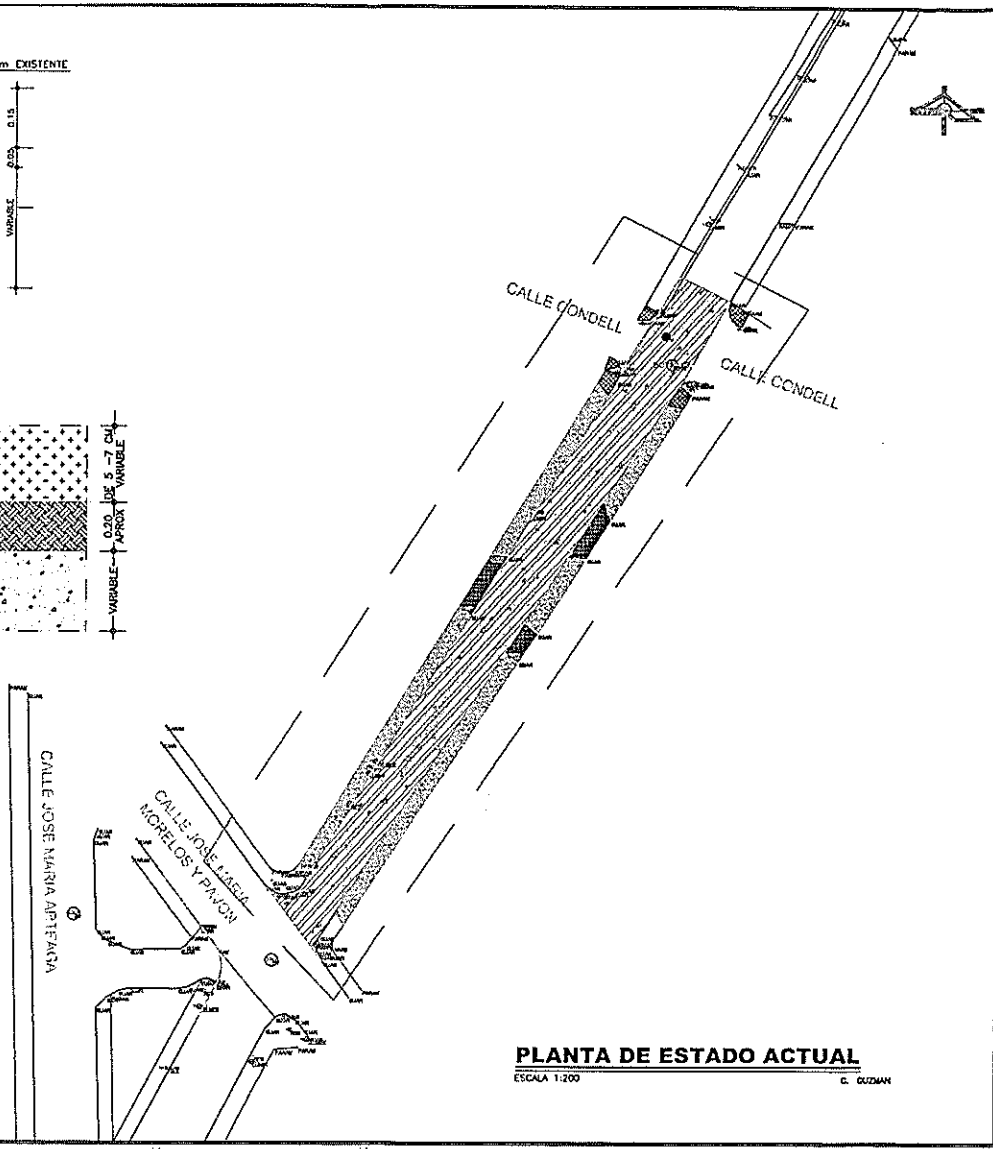

PLANTA DE ESTADO ACTUAL

ESCALA 1:200

C. GUZMAN

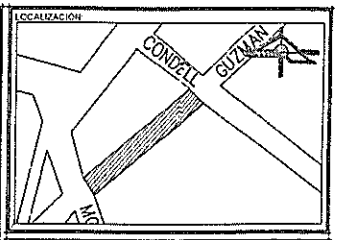

SIMBOLOGIA

- LIMITE DE PROYECTO
- PAVIMENTO ASFÁLTICO EXISTENTE
- BANQUETA DE CONCRETO EXISTENTE
- RAMPA VEHICULAR EXISTENTE
- RAMPA PEATONAL EXISTENTE
- GUARNICIÓN EXISTENTE
- LUM — POSTE LUMINARIA
- CFE — POSTE DE CFE
- TEL — POSTE DE TELMEX
- REC — REGISTRO
- POST — POSTE
- REGISTROS CFE
- REGISTRO SEMAFORO
- REGISTROS TELMEX
- TELEFONO — TELEFONO
- POZO DE VISITA
- BOTA-HID
- SEMAFOROS
- CAMARAS
- ANUNCIO
- RETENIDA POS — RETENIDA POSTE

La Dirección de Planeación y Proyectos solo autoriza el proyecto ejecutivo, no es responsable de la correcta ejecución de la obra. Este documento no tiene validez si no presenta las firmas de los responsables para su autorización, así como los sellos respectivos.

PRESIDENTE MUNICIPAL
M.P.P. Leonardo Montañez Castro
SECRETARIO DE OBRAS PÚBLICAS
Ing. Miguel Ángel Hulzar Botello

REV	FECHA	OBSERVACIONES

RESP. DE PROY. EXTERNO		LOGO EXTERNO
CED. PROFESIONAL		
PROYECTÓ	REVISO	AUTORIZO


Dirección de Planeación y Proyectos de Obra — Secretaría de Obras Públicas

PROYECTISTA	COORDINADOR
ARQ. DANIEL ALBERTO RODRIGUEZ DAVILA	ARQ. ALEJANDRO JAIME LEAL
JEFE DE DEP.	DIRECTOR
LIC. OMAR ALEJANDRO LUJAN GARCIA	ARQ. ALEJANDRO PONCE RODRIGUEZ

PROYECTO	CONSTRUCCIÓN DE SOBRECARPETA ASFALTICA CALLE GUZMAN COL. CENTRO
UBICACIÓN	TRAMO ENTRE C. JOSE MARIA MORELOS Y PAVON Y C. CONDELL
CONTENIDO	PLANTA DE ESTADO ACTUAL

CLAVE	No. PLANO
EA 01	03
FECHA NOV 2022	ESCALA INDICADA
ACOTACIÓN METROS	No. EXP E-000-22

Aguascalientes
LA CIUDAD DE TU VIDA

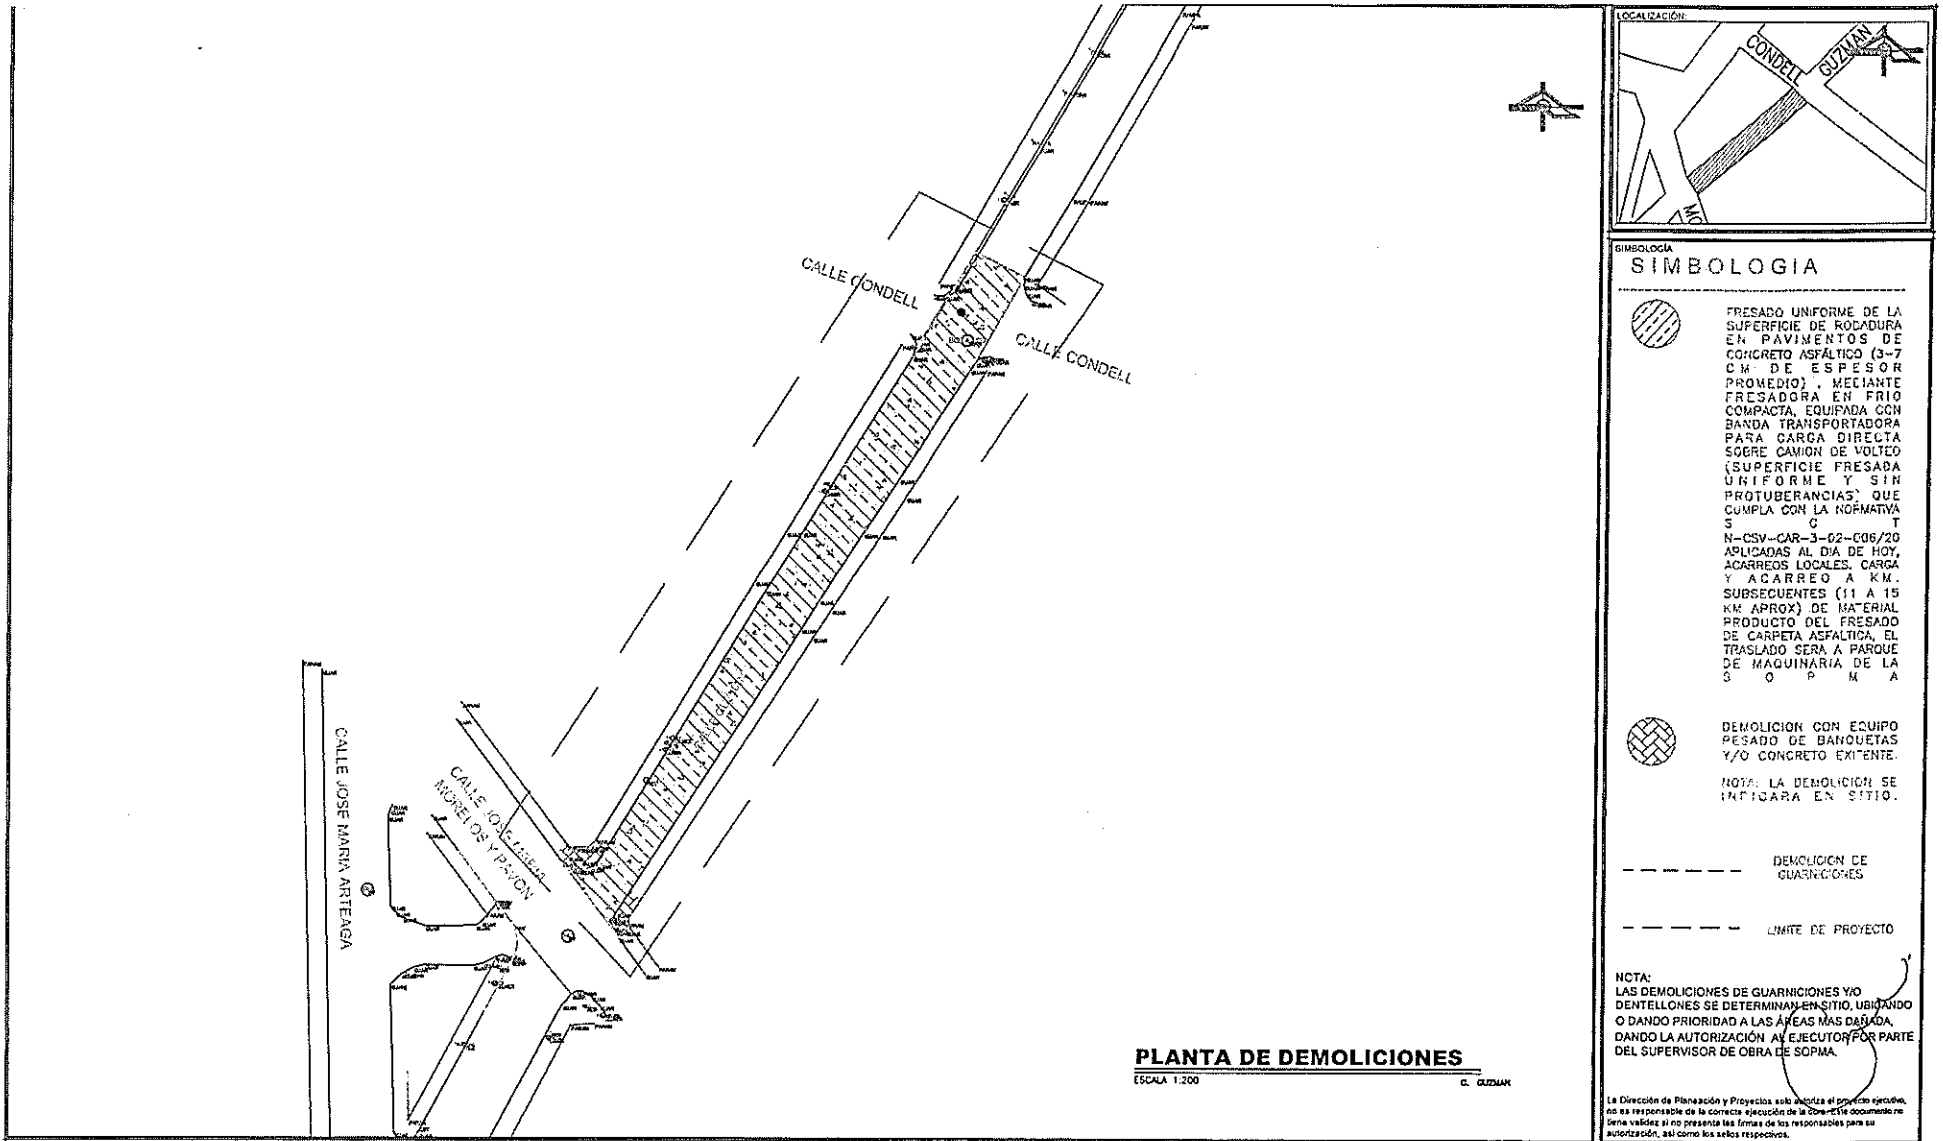

PLANTA DE DEMOLICIONES

ESCALA 1:200

LOCALIZACIÓN:

SIMBOLOGÍA

SIMBOLOGIA

FRESADO UNIFORME DE LA SUPERFICIE DE RODADURA EN PAVIMENTOS DE CONCRETO ASFÁLTICO (3-7 CM. DE ESPESOR PROMEDIO), MEDIANTE FRESADORA EN FRIO COMPACTA, EQUIPADA CON BANDA TRANSPORTADORA PARA CARGA DIRECTA SOBRE CAMION DE VOLTEO (SUPERFICIE FRESADA UNIFORME Y SIN PROTUBERANCIAS) QUE CUMPLA CON LA NORMATIVA S C T N-CSV-CAR-3-02-006/20 APLICADAS AL DIA DE HOY, ACARREOS LOCALES. CARGA Y ACARREO A KM. SUBSECUENTES (11 A 15 KM APROX) DE MATERIAL PRODUCTO DEL FRESADO DE CARPETA ASFALTICA, EL TRASLADO SERA A PARQUE DE MAQUINARIA DE LA S O P M A

DEMOLICION CON EQUIPO PESADO DE BANQUETAS Y/O CONCRETO EXITENTE.

NOTA: LA DEMOLICION SE INDICARA EN SITIO.

DEMOLICION DE GUARNICIONES

LIMITE DE PROYECTO

NOTA:
LAS DEMOLICIONES DE GUARNICIONES Y/O DENTELLONES SE DETERMINAN EN SITIO, UBICANDO O DANDO PRIORIDAD A LAS ÁREAS MAS DAÑADA, DANDO LA AUTORIZACIÓN AL EJECUTOR POR PARTE DEL SUPERVISOR DE OBRA DE SOPMA.

La Dirección de Planeación y Proyectos solo autoriza el proyecto ejecutivo, no es responsable de la correcta ejecución de la Obra-Este documento no tiene validez si no presenta las firmas de los responsables para su autorización, así como los sellos respectivos.

PRESIDENTE MUNICIPAL
M.P.P. Leonardo Montañez Castro
SECRETARIO DE OBRAS PÚBLICAS
Ing. Miguel Ángel Hulzar Botello

REV	FECHA	OBSERVACIONES

VoBo DE LA DIRECTORA

RESP. DE PROY. EXTERNO		LOGO EXTERNO
CED. PROFESIONAL		
PROYECTO	REVISO	AUTORIZO

Dirección de Planeación y Proyectos de Obra — Secretaría de Obras Públicas

PROYECTISTA	COORDINADOR
ARQ. YAEL VALDEZ RODRIGUEZ PPA	ARQ. ALEJANDRO JAIME LEAL
JEFE DE DEP.	DIRECTOR
I.I.L. OMAR ALEJANDRO LUNA GARCIA	ARQ. ALEJANDRO PONCE RODRIGUEZ

PROYECTO
CONSTRUCCIÓN DE SOBRECARPETA ASFALTICA CALLE GUZMAN COL. CENTRO

UBICACION
TRAMO ENTRE C. JOSE MARIA MORELOS Y PAVON Y C. CONDELL

CONTENIDO
PLANTA DE DEMOLICIONES

CLAVE	No. PLANO
DEM 01	04
FECHA: NOV 2022	ESCALA: INDICADA
ACOTACIÓN: METROS	No. EXP.: E-000-22

Aguascalientes
LA CIUDAD DE TU VIDA

SIMBOLOGIA


a) BACHEO PROFUNDO AISLADO UTILIZANDO MATERIAL CALIDAD BASE HIDRAULICA PARA MAS DE UN MILLON DE EJES EQUIVALENTES DEL BANCO QUE ELIJA EL CONTRATISTA, INCISO N.CSV.CAR.1.02.004/03 DE LAS NORMAS DE CONSTRUCCION DE CARR. DE LA SCT,


b) REINIVELACIONES CON CONCRETO ASFALTICO MEZCLA EN PLANTA EN CALIENTE ASFALTO MODIFICADO CON POLIMERO TIPO I, CUMPLIENDO CON LAS NORMAS SCT REFERENTES DE CONSTRUCCION Y CONSERVACION, GRANULOMETRIA DENSA 3/4" A FINOS, MEDIDO COMPACTO AL NOVENTA Y CINCO PORCIENTO (95%)


c) RIEGO DE IMPRECNACION CON EMULSION DE ROMPIMIENTO LENTO (ECL-60 %), INCLUYE BARRIDO DE LA SUPERFICIE, LIMPIEZA A DETALLE, SUMINISTRO, ALMACENAMIENTO, CALENTAMIENTO, Y APLICACION DE LA EMULSION CON EQUIPO ESPECIAL PARA ESA ACTIVIDAD, ESPREAS LIMPIAS Y ALINEADAS, EN CASO DE RECOMENDARLO EL LABORATORIO DE CALIDAD DEL CONTRATISTA SE DEBERA DAR UN RIEGO MATAPOLVO ANTES DE COLOCAR LA CAPA DE IMPREGNACION, A RAZON DE 1.5 LT DE EMULSION POR M2, O LO QUE INDIQUE EL LABORATORIO DE CALIDAD DEL CONTRATISTA

d) RIEGO DE LIGA CON EMULSION DE ROMPIMIENTO RAPIDO (ECR-65 %), INCLUYE, SUMINISTRO, ALMACENAMIENTO, CALENTAMIENTO, Y APLICACION DE LA EMULSION CON EQUIPO ESPECIAL PARA ESA ACTIVIDAD, ESPREAS O BACHADOR LIMPIAS Y ALINEADAS, EN LA PETROLIZADORA, A RAZON DE 0.8 LT DE EMULSION POR M2, O LO QUE INDIQUE EL LABORATORIO DE CALIDAD DEL CONTRATISTA, NO SE ACEPTAN "IMPREGNALIGA"

e) CONCRETO ASFALTICO EN CALIENTE DE GRANULOMETRIA DENSA ELABORADA CON ASFALTO MODIFICADO TIPO I, AGREGADO 3/4" A FINOS, DE 5 CM DE ESPESOR TOTAL, FORMADA Y COMPACTADO AL 95%, INCLUYE MATERIALES, QUE CUMPLAN LA NORMATIVA SCT-N-CMT-04-04, SCT-CMT-4-05-002, SCT-CMT-4-05-003, SCT-CMT-4-05-004, SCT-CTR-CAR-1-04-006-14 APLICADAS AL DIA DE HOY, DISEÑO MARSHALL (DEBERÁ SER AUTORIZADO POR EL LABORATORIO DE CALIDAD DE SOPMA AL MENOS 3 DIAS ANTES DE INICIO DE TENDIDO DE LA MEZCLA ASFALTICA)

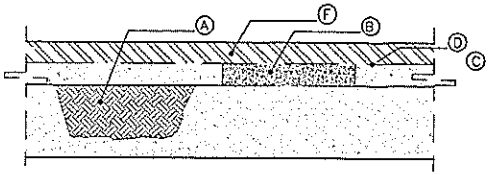


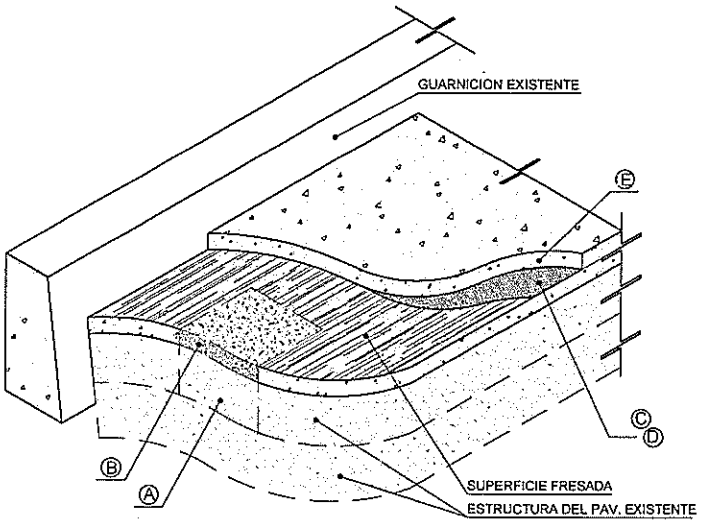

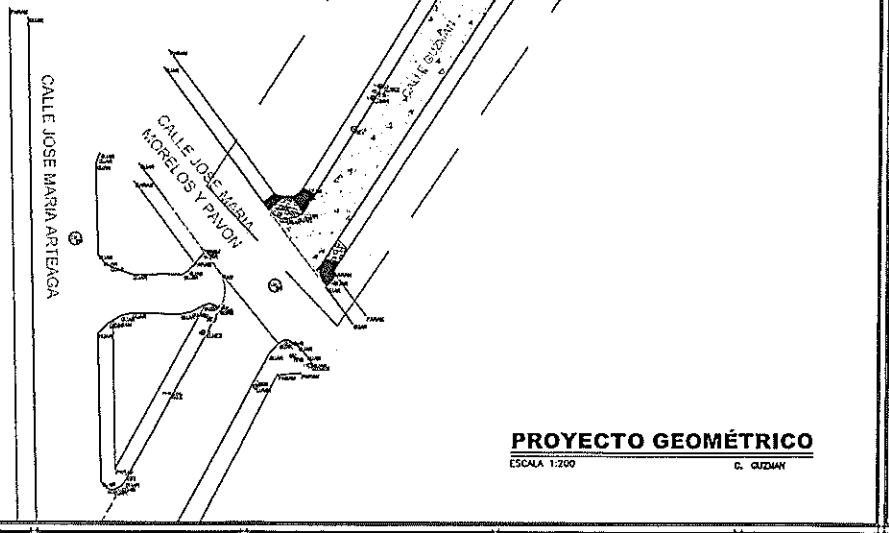

PROYECTO GEOMÉTRICO

ESCALA 1:200 C. GUZMAN

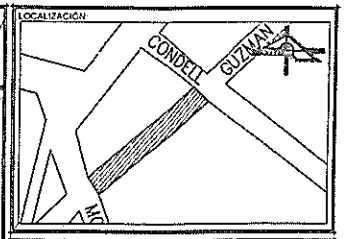

SIMBOLOGIA

SIMBOLOGIA

- LIMITE DE PROYECTO
- SUMINISTRO Y COLOCACION DE CONCRETO ASFALTICO EN CALIENTE DE GRANULOMETRIA DENSA ELABORADA CON ASFALTO MODIFICADO TIPO I, AGREGADO 3/4" A FINOS, DE 5 CM DE ESPESOR, FORMADA Y CONSTRUIDO AL 95% QUE CUMPLAN LA NORMATIVA SCT-N-CMT-04-04, SCT-CMT-4-05-002, SCT-CMT-4-05-003, SCT-CMT-4-05-004, SCT-CTR-CAR-1-04-006-14 APLICADAS AL DIA DE HOY, DISEÑO MARSHALL (DEBERÁ SER AUTORIZADO POR EL LABORATORIO DE CALIDAD DE SOPMA AL MENOS 3 DIAS ANTES DE INICIO DE TENDIDO DE LA MEZCLA ASFALTICA).
- BANQUETA PROPUESTA 10 CM ESPESOR
- PROPUESTA DE GUARNICION, O LO QUE SE INDIQUE EN SITIO
- RAMPA PEATONAL PROPUESTA
- APLICAR PINTURA EN RAMPA EXISTENTE
- LOSA DIAMANTE A BASE DE CONCRETO PREVEZCLADO (MR=45) 25 CM ESPESOR

NOTA 1:

TODOS LOS TRABAJOS SE EJECUTARAN CONFORME SE ESTABLECIDO EN LAS FICHAS TECNICAS DE EL DEPARTAMENTO DE CALIDAD, DIRECCION DE CONSTRUCCION Y CONSERVACION.

200	BANQUETAS
201	BOTELLON
204	GUARNICION TRAPEZOIDAL
208	LOSA DIAMANTE
216	RAMPA BANQUETA
303	BASES
306	PLANTILLA
309	SUB BASES
310	SUB RASANTE
808	SELLADO DE GRIETAS Y JUNTAS EN LOSA DE CONCRETO

La Dirección de Planeación y Proyectos solo autoriza el proyecto ejecutivo, no es responsable de la correcta ejecución de la obra. Este documento no tiene validez si no presenta las firmas de los responsables para su autorización, así como los sellos respectivos.

PRESIDENTE MUNICIPAL
M.P.P. Leonardo Montañez Castro
SECRETARIO DE OBRAS PÚBLICAS
Ing. Miguel Ángel Hulzar Botello

REV	FECHA	OBSERVACIONES

VO BO DELA DEPENDENCIA

RESP. DE PROY. EXTERNO		LOGO EXTERNO
CED. PROFESIONAL		
PROYECTO	REVISÓ	AUTORIZÓ

Dirección de Planeación y Proyectos de Obra — Secretaría de Obras Públicas

PROYECTISTA	COORDINACIÓN
ARQ. DANIEL ALBERTO RODRIGUEZ TAPIA	ARQ. ALEJANDRO JAIME LEAL
JEFE DE DEP.	DIRECTOR
LIC. OMAR ALEJANDRO LLAMAS GARCIA	ARQ. ALEJANDRO PONCE RODRIGUEZ


PROYECTO
CONSTRUCCIÓN DE SOBRECARPETA ASFALTICA CALLE GUZMAN COL. CENTRO

UBICACIÓN
TRAMO ENTRE C. JOSE MARIA MORELOS Y PAVON Y C. CONDELL

CONTENIDO
PROYECTO GEOMETRICO

CLAVE	No. PLANO
GEO 01	05
FECHA NOV 2022	ESCALA INDICADA
ACOTACIÓN METROS	No. EXP. E-000-22


Aguascalientes
LA CIUDAD DE TU VIDA

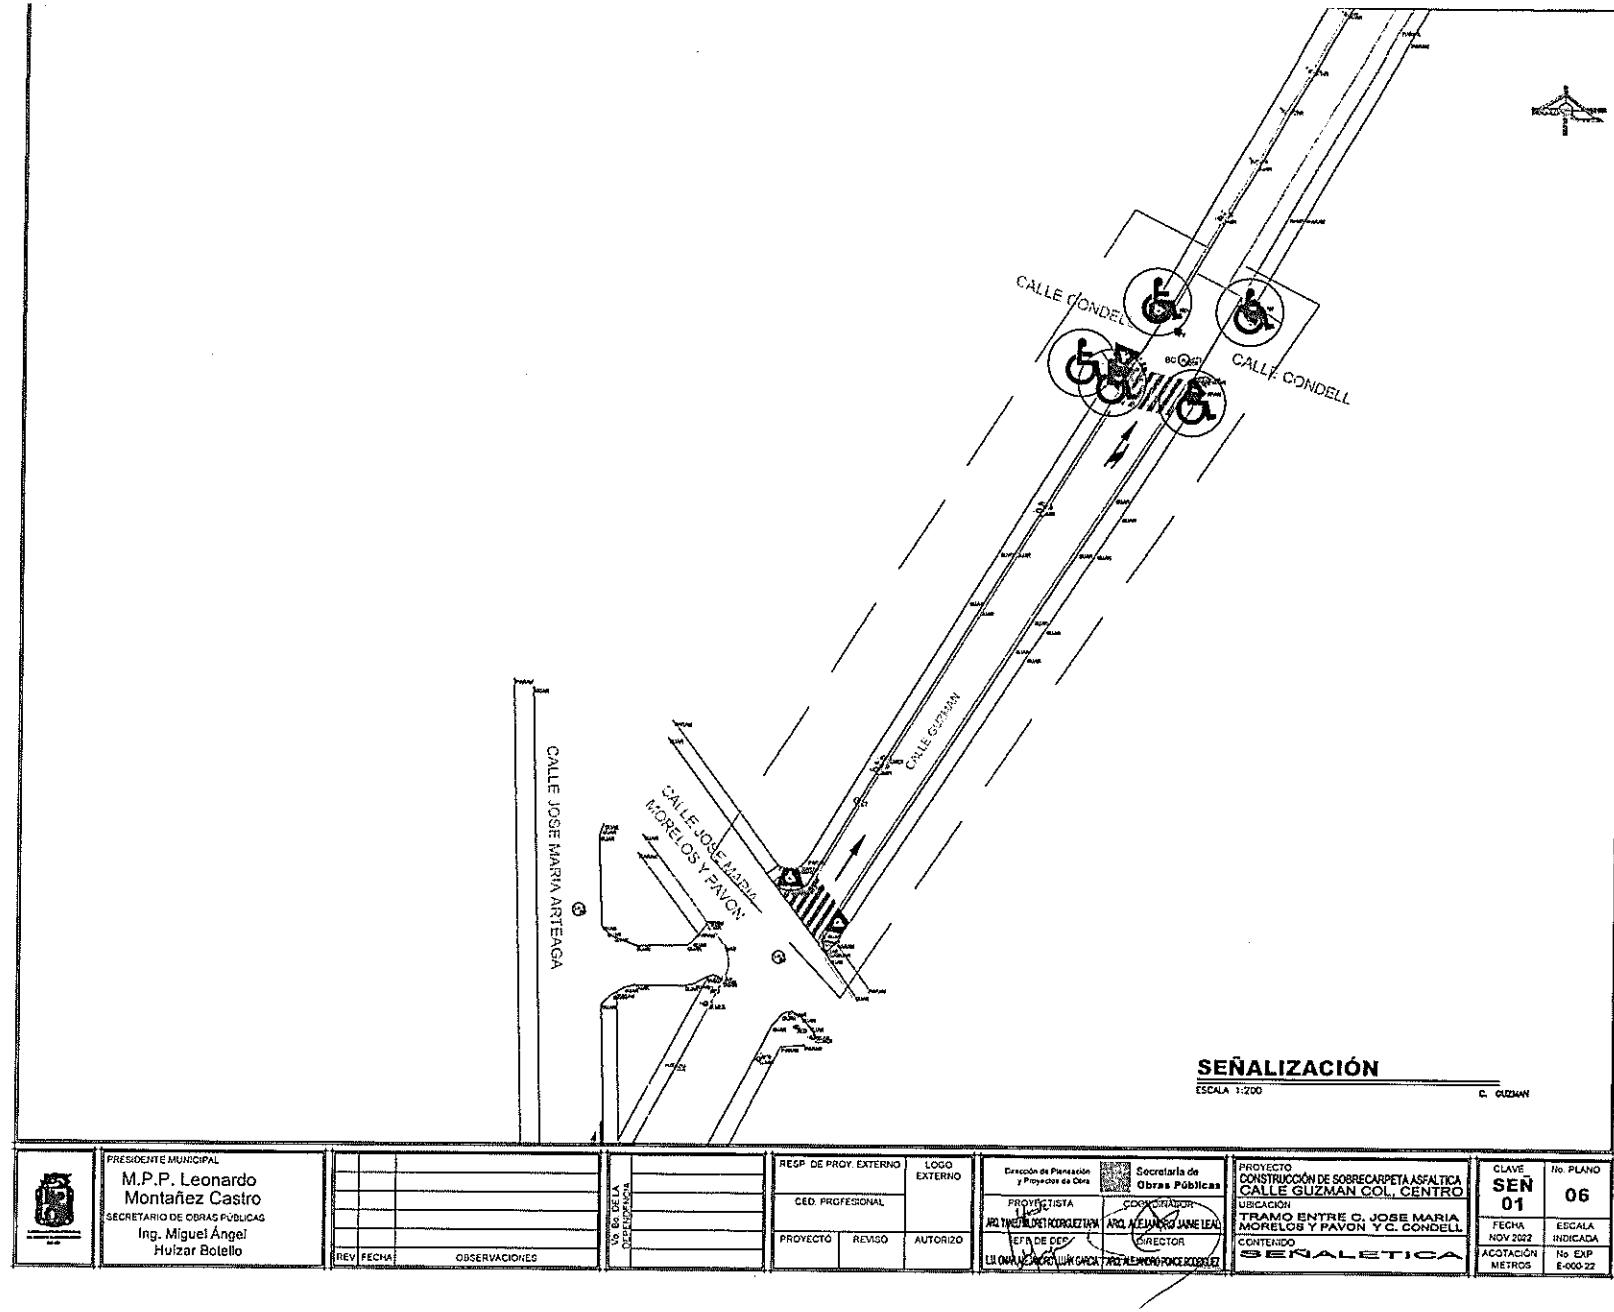

SEÑALIZACIÓN

ESCALA 1:200

LOCALIZACIÓN

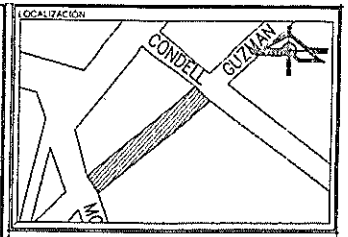

SIMBOLOGÍA

NOTA:
Se aplicará en todos los señalamientos horizontales pintura para trafico base solvente tipo alquidal de secado rápido, que cumpla con las especificaciones n-cmt-5-01-00 /05, n-pry-car-10-01-002/13 de la SCT aplicados al día de hoy.

M-12.1, M12.2 APLICADA SOBRE GUARNICIONES Y DENTELLONES DE CUALQUIER COLOR

Se aplicará en todos los señalamientos horizontales pintura para trafico Termoplastico tipo alquidal de secado rápido, que cumpla con las especificaciones n-cmt-5-01-001/05, n-pry-car-10-01-002/13 de la SCT aplicados al día de hoy.

M - 1.2, LÍNEA DISCONTINUA SENCILLA DE DIVISIÓN DE CARRILES DE FRENTE EN PISO, DE 10 CM DE ANCHO
M - 3.3, CONTINUA IZQUIERDA, PARA VIALIDADES URBANAS DE FRENTE EN PISO, SEPARADA 15 CM. DE LA GUARNICIÓN, COLOR AMARILLO
M - 4, PARA INDICAR LÍNEA GUÍA EN ZONA DE TRANSICIÓN DE FRENTE EN PISO, DESARROLLO DE 2.00 X 0.10 MTS, CON UNA SEPARACIÓN DE 4.00 M"S ENTRE SI PROMEDIO
M - 5, PARA INDICAR ENTRADA Y SALIDA EN BIFURCACIONES
M - 6, PARA INDICAR ALTO EN CRUCEROS, COLOR BLANCO
M - 7.1, PARA INDICAR " CRUCE PEATONAL EN LAS PRIMARIAS" COLOR AMARILLO
M - 11.1, "FLECHA SENCILLA" PARA INDICAR SENTIDO DE CIRCULACIÓN
M - 11.1, "FLECHA CABEZA DOBLE" PARA INDICAR SENTIDO DE CIRCULACIÓN (VUELTA IZQUIERDA O DERECHA)

Nota2: Dosificación de micro esfera
La cantidad de esferas de vidrio en la película de pintura en húmedo, según su tipo, será la que se indica en la Tabla.

TABLA 8: Cantidad de esferas de vidrio en la película de pintura en humedo.

TIPO DE PINTURA	ESPESOR DE LA PELICULA DE PINTURA EN HUMEDO (pulg)	CONTENIDO DE ESFERAS kg/m2 INTERMEDIA	CONVENCIONAL 1.2.2.2.2	EJES DE CIRCULACIÓN
BASE SOLVENTE	0.25 A 0.50	---	0.330	
BASE AGUA	0.38 A 0.50	---	0.330	
TERMOPLÁSTICA	1.00 A 0.60	0.07 A 0.15	0.330	

La Dirección de Planeación y Proyectos sólo autoriza el proyecto ejecutivo, no es responsable de la correcta ejecución de la obra. Este documento no tiene validez si no presenta las firmas de los responsables para su autorización, así como los sellos respectivos.

PRESIDENTE MUNICIPAL
M.P.P. Leonardo Montañez Castro
SECRETARIO DE OBRAS PÚBLICAS
Ing. Miguel Ángel Hulzar Botello

REV.	FECHA	OBSERVACIONES

V°B° DE LA DEPENDENCIA

RESP. DE PROY. EXTERNO		LOGO EXTERNO
CED. PROFESIONAL		
PROYECTÓ	REVISÓ	AUTORIZÓ

Dirección de Planeación y Proyectos de Obra — Secretaría de Obras Públicas

PROYECTISTA	COORDINADOR
ARQ. TANIA BELDAD RODRIGUEZ TAPIA	ARQ. ALEJANDRO JAIME LEAL
JEFA DE DEP.	DIRECTOR
LIC. DIANA JACQUELIN GARCIA	ARQ. ALEJANDRO PONCE RODRIGUEZ


PROYECTO
CONSTRUCCIÓN DE SOBRECARPETA ASFALTICA CALLE GUZMAN COL. CENTRO


UBICACIÓN
TRAMO ENTRE C. JOSE MARIA MORELOS Y PAVON Y C. CONDELL

CONTENIDO
SEÑALETICA

CLAVE	No. PLANO
SEÑ 01	06
FECHA NOV 2022	ESCALA INDICADA
ACOTACIÓN METROS	No EXP E-000-22

Aguascalientes
LA CIUDAD DE TU VIDA

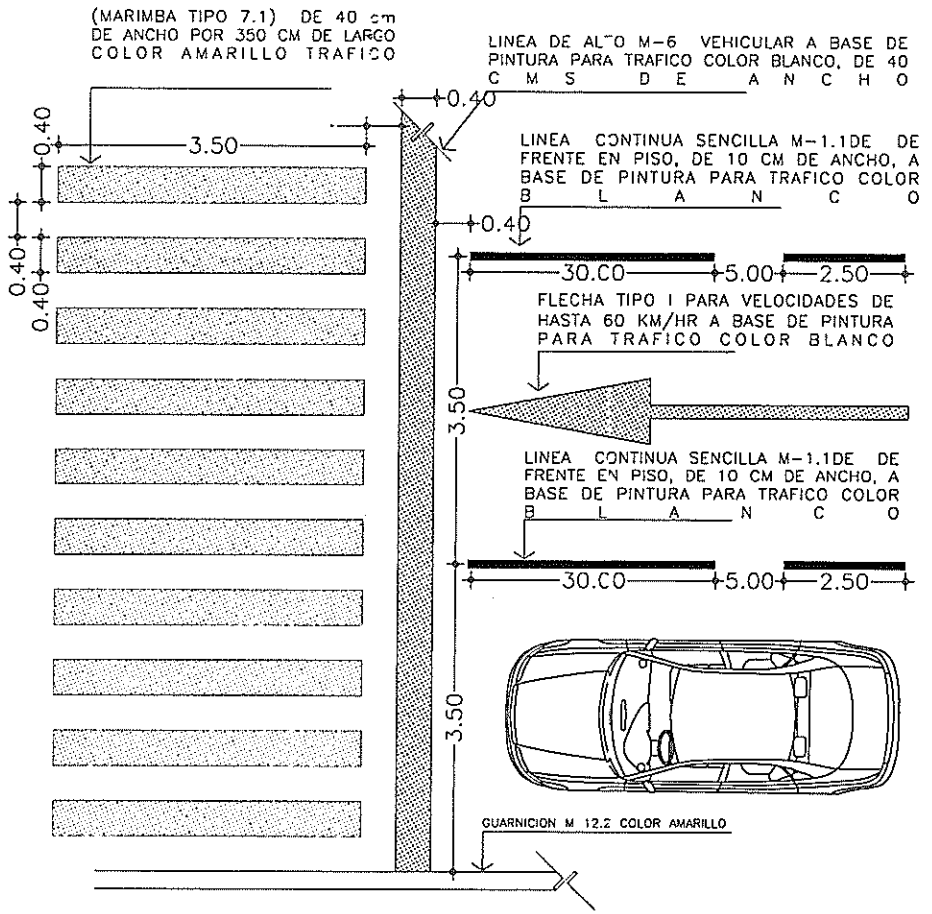

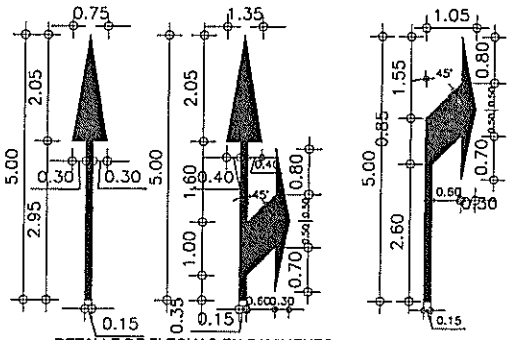


DETALLE DE FLECHAS EN PAVIMENTO
PARA VELOCIDADES HASTA DE 60KM/H
COTAS EN M

DETALLE

TRAZO PINTURA EN CRUCEROS SIN ESCALA

LOCALIZACIÓN:

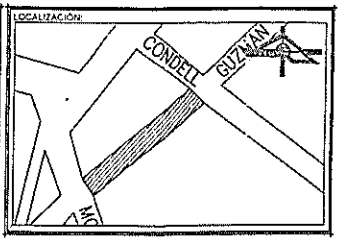

SIMBOLOGÍA

NOTA:
Se aplicará en todos los señalamientos horizontales pintura para trafico base solvente tipo alquidal de secado rápido, que cumpla con las especificaciones n-cmt-5-01-001/05, n-pry-car-10-01-002/13 de la SCT aplicadas al día de hoy.

M-12.1, M12.2 APLICADA SOBRE GUARNICIONES Y DENTELLONES DE CUALQUIER COLOR

Se aplicará en todos los señalamientos horizontales pintura para trafico Termoplastico tipo alquidal de secado rápido, que cumpla con las especificaciones n-cmt-5-01-001/05, n-pry-car-10-01-002/13 de la SCT aplicadas al día de hoy.

M - 1.2, LÍNEA DISCONTINUA SENCILLA DE DIVISIÓN DE CARRILES DE FRENTE EN PISO, DE 10 CM DE ANCHO
M - 3.3, CONTINUA IZQUIERDA, PARA VIALIDADES URBANAS DE FRENTE EN PISO, SEPARADA 15 CM, DE LA GUARNICION, COLOR AMARILLO
M - 4, PARA INDICAR LÍNEA GUÍA EN ZONA DE TRANSICIÓN DE FRENTE EN PISO, DESARROLLO DE 2.00 X 0.10 MTS, CON UNA SEPARACIÓN DE 4.00 MTS ENTRE SI PROMEDIO
M - 5, PARA INDICAR ENTRADA Y SALIDA EN BIFURCACIONES
M - 6, PARA INDICAR ALTO EN CRUCEROS, COLOR BLANCO
M - 7.1, PARA INDICAR " CRUCE PEATONAL EN VIAS PRIMARIAS" COLOR AMARILLO
M - 11.1, "FLECHA SENCILLA" PARA INDICAR SENTIDO DE CIRCULACIÓN
M - 11.1, "FLECHA CABEZA DOBLE" PARA INDICAR SENTIDO DE CIRCULACIÓN (VUELTA IZQUIERDA O DERECHA)

Nota2: Dosificación de micro esfera
La cantidad de esferas de vidrio en la película de pintura en húmedo, según su tipo, será la que se indica en la Tabla.

TABLA 5: Cantidad de esferas de vidrio en la película de pintura en humedo.

TIPO DE PINTURA	ESPESOR DE LA PELICULA DE PINTURA EN MICRAS	CANTIDAD DE ESFERAS kg/m2		TIPO DE APLICACION
		INTEGRADAS	SOBRE PUESTAS	
BASE SOLVENTE	0.30 A 0.50	--	0.350	
BASE AGUA	0.25 A 0.50	--	0.350	
TERMOPLASTICA	1.50 A 6.00	0.07 A 0.20	0.350	

La Dirección de Planeación y Proyectos, solo autoriza el proyecto ejecutivo, no es responsable de la correcta ejecución de la obra. Este documento no tiene validez si no presenta las firmas de los responsables para su autorización, así como los sellos respectivos.

PRESIDENTE MUNICIPAL	M.P.P. Leonardo Montañez Castro	SECRETARIO DE OBRAS PÚBLICAS	Ing. Miguel Ángel Huizar Botello

REV	FECHA	OBSERVACIONES

Vo. Bo. DE LA CONTRATISTA

RESP. DE PROY. EXTERNO	LOGO EXTERNO
CED. PROFESIONAL	
PROYECTO / REVISO / AUTORIZÓ	


Dirección de Planeación y Proyectos de Obra — Secretaría de Obras Públicas

PROYECTISTA	COORDINADOR
ARQ. DANIEL RUDPET RODRIGUEZ TAPIA	ARQ. ALEJANDRO JAIME LEAL
JEFE DE DEP.	DIRECTOR
LIC. DANIEL ALEJANDRO LUJAN GARCIA	ARQ. ALEJANDRO PONCE RODRIGUEZ

PROYECTO	CONSTRUCCIÓN DE SOBRECARPETA ASFALTICA CALLE GUZMAN COL. CENTRO
UBICACIÓN	TRAMO ENTRE C. JOSE MARIA MORELOS Y PAVON Y C. CONDELL
CONTENIDO	DETALLES SEÑALETICA HORIZONTAL

CLAVE	No. PLANO
DSH 01	07
FECHA NOV 2022	ESCALA INDICADA
ACOTACIÓN METROS	No. EXP. E-000-22

Aguascalientes
LA CIUDAD DE TU VIDA

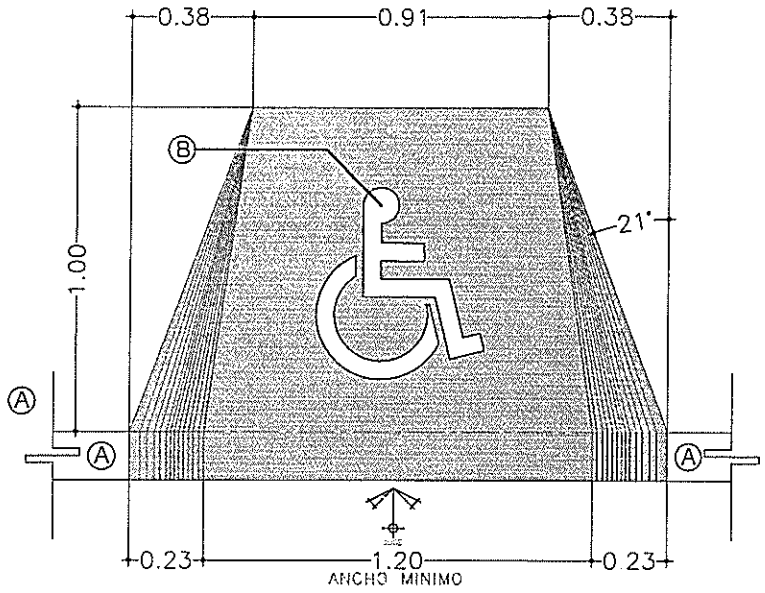


DETALLE DE LOGOTIPO "A" EN RAMPA

VISTA EN PLANTA S/E

Ⓐ SUMINISTRO Y APLICACIÓN DE PINTURA BASE SOLVENTE COLOR AZUL (PANTONE 294) EN RAMPAS PARA DISCAPACITADOS

Ⓑ SUMINISTRO Y APLICACIÓN DE LOGOTIPO "A" (SILLA DE RUEDAS) EN PINTURA BASE SOLVENTE COLOR BLANCO EN RAMPAS PARA DISCAPACITADOS TAMAÑO Y DISEÑO SEGÚN PLANOS.

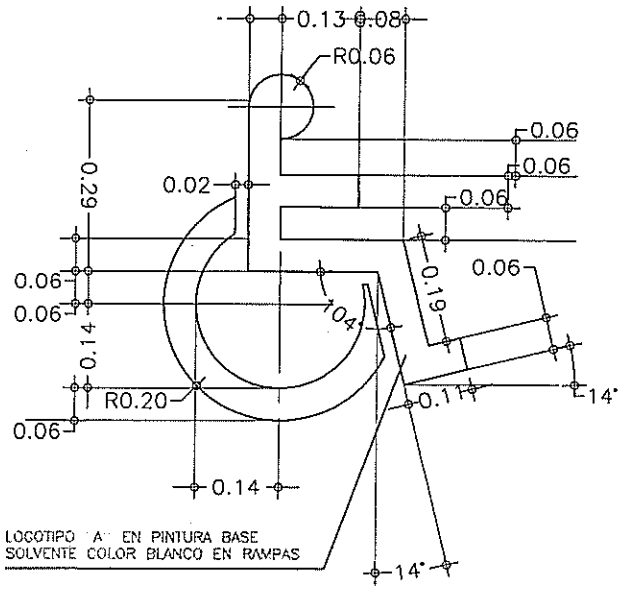


LOGOTIPO "A" EN PINTURA BASE SOLVENTE COLOR BLANCO EN RAMPAS

DETALLE DE LOGOTIPO "A" EN RAMPA

VISTA EN PLANTA S/E

LOCALIZACIÓN:

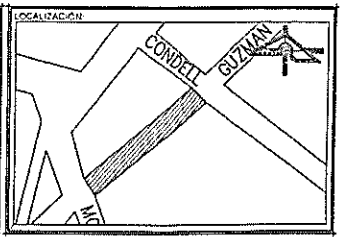

SIMBOLOGÍA

NOTA:
Se aplicará en todos los señalamientos horizontales pintura para trafico base solvente tipo alquidal de secado rápido, que cumpla con las especificaciones n-cmt-5-01-001/05, n-pry-car-10-01-002/13 de la SCT aplicadas al día de hoy.

M-12.1, M12.2 APLICADA SOBRE GUARNICIONES Y DENTELLONES DE CUALQUIER COLOR

Se aplicará en todos los señalamientos horizontales pintura para trafico Termoplastica tipo alquidal de secado rápido, que cumpla con las especificaciones n-cmt-5-01-001/05, n-pry-car-10-01-002/13 de la SCT aplicadas al día de hoy.

M - 1.2, LÍNEA DISCONTINUA SENCILLA DE DIVISIÓN DE CARRILES DE FRENTE EN PISO, DE 10 CM DE ANCHO
M - 3.3, CONTINUA IZQUIERDA, PARA VIALIDADES URBANAS DE FRENTE EN PISO, SEPARADA 15 CM. DE LA GUARNICIÓN, COLOR AMARILLO
M - 4, PARA INDICAR LÍNEA GUÍA EN ZONA DE TRANSICIÓN DE FRENTE EN PISO, DESARROLLO DE 2.00 X 0.10 MTS, CON UNA SEPARACIÓN DE 4.00 MTS ENTRE SI PROMEDIO
M - 5, PARA INDICAR ENTRADA Y SALIDA EN BIFURCACIONES
M - 6, PARA INDICAR ALTO EN CRUCEROS, COLOR BLANCO
M - 7.1, PARA INDICAR " CRUCE PEATONAL EN VIAS PRIMARIAS" COLOR AMARILLO
M - 11.1, "FLECHA SENCILLA" PARA INDICAR SENTIDO DE CIRCULACIÓN
M - 11.1, "FLECHA CABEZA DOBLE" PARA INDICAR SENTIDO DE CIRCULACIÓN (VUELTA IZQUIERDA O DERECHA)


Nota2: Dosificación de micro esfera
La cantidad de esferas de vidrio en la película de pintura en húmedo, según su tipo, será lo que se indica en la Tabla.
TABLA 8: Cantidad de esferas de vidrio en la película de pintura en humedo.

TIPO DE PINTURA	ESPESOR DE LA PELICULA DE PINTURA EN HUMEDO mm	CANTIDAD DE ESFERAS kg/m²		TIPO DE GRADACIÓN
		PROMEDIO	MINIMO	
BASE SOLVENTE	0.38 A 0.50	---	0.300	I
BASE AGUA	0.60 A 0.30	---	0.300	I-II
TERMOPLASTICA	1.50 A 0.60	0.7 A 0.45	0.350	I

La Dirección de Planeación y Proyectos solo autoriza el proyecto ejecutivo, no es responsable de la correcta ejecución de la obra. Este documento no tiene validez si no presenta las firmas de los responsables para su autorización, así como los sellos respectivos.

PRESIDENTE MUNICIPAL: M.P.P. Leonardo Montañez Castro SECRETARIO DE OBRAS PÚBLICAS: Ing. Miguel Ángel Huizar Botello	REV / FECHA / OBSERVACIONES	V°B° DE LA DEPENDENCIA	RESP. DE PROY. EXTERNO / CED. PROFESIONAL / PROYECTÓ / REVISÓ / AUTORIZÓ / LOGO EXTERNO	Dirección de Planeación y Proyectos de Obra — Secretaría de Obras Públicas PROYECTISTA: ARQ. YAZMIN MADRET RODRIGUEZ DAVILA COORDINADOR: ARQ. ALEJANDRO JAIME LEAL JEFE DE DEP.: LIC. DIANA ASUNCION DE LA GARZA DIRECTOR: ARQ. ALEJANDRO PONCE RODRIGUEZ	PROYECTO: CONSTRUCCIÓN DE SOBRECARPETA ASFALTICA CALLE GUZMAN COL. CENTRO UBICACIÓN: TRAMO ENTRE C. JOSE MARIA MORELOS Y PAVON Y C. CONDELL CONTENIDO: DETALLES SEÑALETICA HORIZONTAL	CLAVE: DSH 02 / FECHA: NOV 2022 / ACOTACIÓN: METROS	No. PLANO: 08 / ESCALA: INDICADA / No. EXP.: E-000-22	Aguascalientes LA CIUDAD DE TU VIDA


DENTELLON TRAPEZOIDAL DE 15-20X40 CM DE SECCION, CON CONCRETO PREMEZCLADO MR=38 KGF/CM2, TMA 1 1/2", R.R. 14 DIAS, REVENIMIENTO NORMAL DE 10+-2 CM, GRAVA TRITURADA, ACABADO CON DOBLADOR Y PULIDO. INCLUYE: TRAZO, NIVELACION, CIMBRADO, COLADO, VIBRADO, DESCIMBRADO, JUNTA A BASE DE ESPUMA DE POLIETILENO DE CELDAS CERRADAS DE 1/2" EN JUNTAS FRIAS LONGITUDINALES NO MAYOR A 3a a15 CORTE TRANSVERSAL CON CONTADORA A 1/3 DE SU ESPESOR MAXIMO @ 3 MTS. RELLENO PREFORMADO Y SELLADOR AUTONIVELANTE ASI COMO DE ASLAMIENTO CON OTRO ELEMENTO, Y CURADO CON MEMBRANA QUIMICA APLICADA CON ASPERSOR Y LIMPIEZA, SE DEBERA TENER CUIDADO EN EL NIVEL DE DESPLANTE PUES NO SE ACEPTAN ELLENOS FUERA DE LA BASE NUEVA. TRABAJO TERMINADO

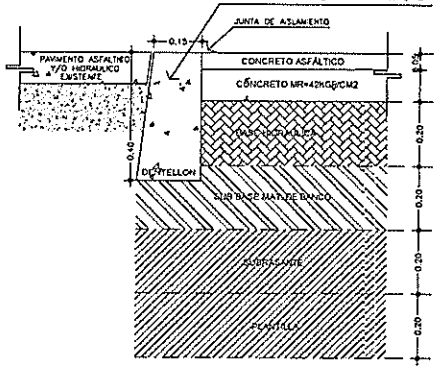

ESTRUCTURA 1-A


MR=43 KGF/CM2 1:10

CONSTRUCCION DE GUARNICION RECTA Y/O CURVA TRAPEZOIDAL DE 15X20X40 CM DE SECCION CON CONCRETO PREMEZCLADO F'C= 150 KG/CM2, REVENIMIENTO DE 8 A 10 CM. T.M.A. 1 1/2" 38 MM, GRAVA TRITURADA, ACABADO PULIDO EN PARTE DE SUPERIOR Y DOBLADOR EN ARISTAS SUPERIORES, INCLUYE: COMPACTADO DE PLANTILLA, CIMBRADO, COLADO, ACABADO, DESCIMBRADO, ALINEADO, NIVELADO, DESCIMBRADO Y CURADO EN SU PARTE SUPERIOR CON MEMBRANA BASE AGUA A RAZON DE 1 LTO/M2.

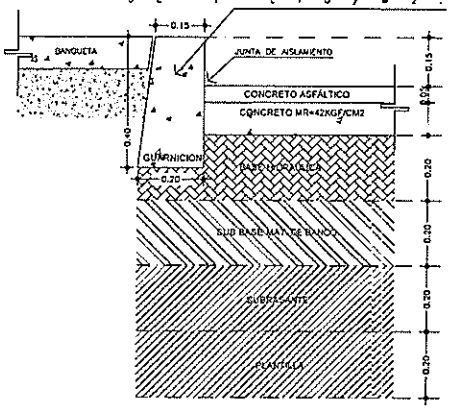

ESTRUCTURA 1

MR=43 KGF/CM2 S/E

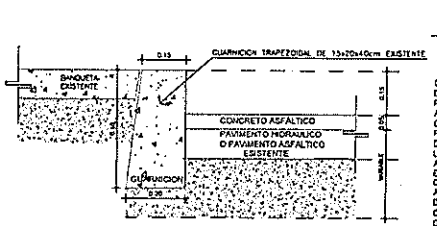


ESTADO ACTUAL

TERRACERIAS ESCALA S/E

CONSTRUCCION DE GUARNICION RECTA Y/O CURVA TRAPEZOIDAL DE 15X20X40 CM DE SECCION CON CONCRETO PREMEZCLADO F'C= 150 KG/CM2, REVENIMIENTO DE 8 A 10 CM, T.M.A. 1 1/2" 38 MM, GRAVA TRITURADA, ACABADO PULIDO EN PARTE DE SUPERIOR Y DOBLADOR EN ARISTAS SUPERIORES, INCLUYE: COMPACTADO DE PLANTILLA, CIMBRADO, COLADO, ACABADO, DESCIMBRADO, ALINEADO, NIVELADO, DESCIMBRADO Y CURADO EN SU PARTE SUPERIOR CON MEMBRANA BASE AGUA A RAZON DE 1 LTO/M2.

CONSTRUCCION DE BANQUETA DE 10 CM DE ESPESOR A BASE DE CONCRETO HECHO EN OBRA F'C=150 KG/CM2, T.M.A. 3/4", R.N. GRAVA TRITURADA, REVENIMIENTI DE 10+-2 CM, ACABADO RAYADO FINO CON BROCHA DE PELO, JUNTAS FRIAS CON DOBLADOR DE 2" SECCION DE LOSAS COMO INDIQUE PROYECTO, INCLUYE: JUNTA A BASE DE ESPUMA DE POLIETILENO DE CELDAS CERRADAS DE 1/3" EN JUNTAS FRIAS LONGITUDINALES CON MUROS Y TRANSVERSALES DEL ELEMENTO, ASI COMO SU UNION CON ELEMENTOS VIEJOS O CAMBIO DE ELEMENTO, CIMBRADO, COLADO, DESCIMBRADO, CORTES CON CONTADORA DE DISCO, SELLADO DE CORTES CON SELLADOR AUTONIVELANTE Y TIRA DE RELLENO PREFORMADA NO ADHERENTE DE 1/8" (EN TODAS LAS JUNTAS DE CONTRACCCION Y CONSTRUCCION TRANSVERSALES), CURADO CON MEMBRANA QUIMICA APLICADA CON ASPERSOR, TRABAJO TERMINADO.

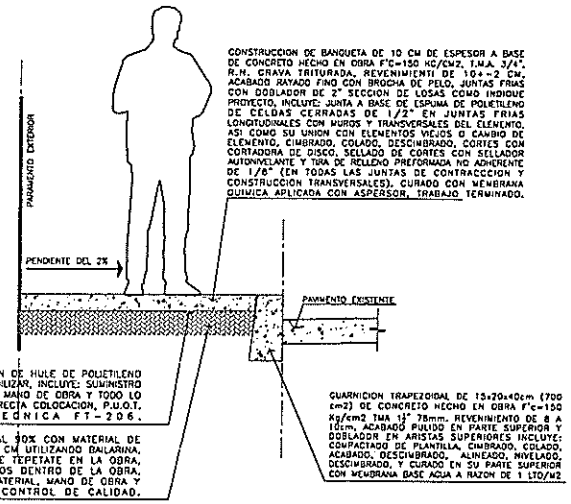

CONSTRUCCION DE BANQUETA DE 10 CM DE ESPESOR A BASE DE CONCRETO HECHO EN OBRA F'C=150 KG/CM2, T.M.A. 3/4", R.N. GRAVA TRITURADA, REVENIMIENTI DE 10+-2 CM, ACABADO RAYADO FINO CON BROCHA DE PELO, JUNTAS FRIAS CON DOBLADOR DE 2" SECCION DE LOSAS COMO INDIQUE PROYECTO, INCLUYE: JUNTA A BASE DE ESPUMA DE POLIETILENO DE CELDAS CERRADAS DE 1/2" EN JUNTAS FRIAS LONGITUDINALES CON MUROS Y TRANSVERSALES DEL ELEMENTO, ASI COMO SU UNION CON ELEMENTOS VIEJOS O CAMBIO DE ELEMENTO, CIMBRADO, COLADO, DESCIMBRADO, CORTES CON CONTADORA DE DISCO, SELLADO DE CORTES CON SELLADOR AUTONIVELANTE Y TIRA DE RELLENO PREFORMADA NO ADHERENTE DE 1/8" (EN TODAS LAS JUNTAS DE CONTRACCCION Y CONSTRUCCION TRANSVERSALES), CURADO CON MEMBRANA QUIMICA APLICADA CON ASPERSOR, TRABAJO TERMINADO.


SUMINISTRO Y COLOCACION DE HULE DE POLIETILENO CAL. 600 PARA IMPERMEABILIZAR, INCLUYE: SUMINISTRO DEL MATERIAL A LA OBRA, MANO DE OBRA Y TODO LO NECESARIO PARA SU CORRECTA COLOCACION, P.U.O.T. SEGUN FICHA TECNICA FT-206.

RELLENO COMPACTADO AL 90% CON MATERIAL DE BANCO EN CAPAS DE 20 CM UTILIZANDO BAILARINA, INCLUYE: SUMINISTRO DE TEPETATE EN LA OBRA, ABUNDAMIENTO, ACARREOS DENTRO DE LA OBRA, CIMBRADO, RETIRO DE MATERIAL, MANO DE OBRA Y EQUIPO, PRUEBA DE CONTROL DE CALIDAD.

GUARNICION TRAPEZOIDAL DE 15x20x40cm (700 cm2) DE CONCRETO HECHO EN OBRA F'c=150 Kg/cm2 TMA 1" 76mm. REVENIMIENTO DE 8 A 10cm, ACABADO PULIDO EN PARTE SUPERIOR Y DOBLADOR EN ARISTAS SUPERIORES INCLUYE: COMPACTADO DE PLANTILLA, CIMBRADO, COLADO, ACABADO, DESCIMBRADO, ALINEADO, NIVELADO, DESCIMBRADO, Y CURADO EN SU PARTE SUPERIOR CON MEMBRANA BASE AGUA A RAZON DE 1 LTO/M2

BANQUETA T-1


VISTA EN CORTE ESC: 1:15

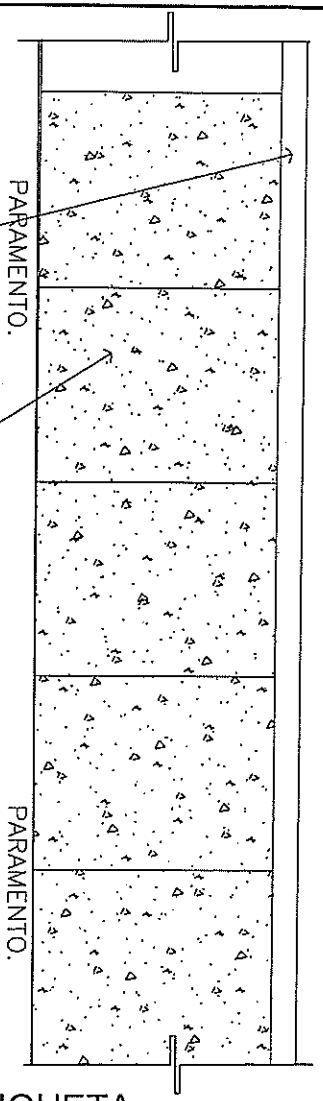

BANQUETA

VISTA EN PLANTA ESC: 1:15

LOCALIZACION

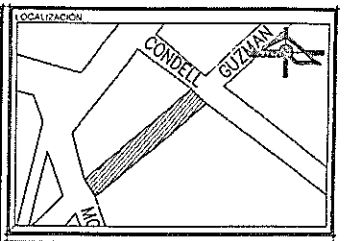

SIMBOLOGIA

NOTA 1:

TODOS LOS TRABAJOS SE EJECUTARAN CONFORME LO ESTABLECIDO EN LAS FICHAS TECNICAS DE EL DEPARTAMENTO DE CALIDAD, DIRECCION DE CONSTRUCCION Y CONSERVACION.

FT 200	BANQUETAS
FT 201	DENTELLON
FT 204	GUARNICION TRAPEZOIDAL
FT 208	LOSA DIAMANTE
FT 218	RAMPA BANQUETA
FT 303	BASES
FT 306	PLANTILLA
FT 308	SUB BASES
FT 310	SUB RASANTE
FT 505	SELLADO DE GRIETAS Y JUNTAS EN LOSAS DE CONCRETO

NOTA 2:

RESPETAR NIVELES DE PAVIMENTO EXISTENTES, EN SU CASO TOMAR NIVEL DE CORONA DE GUARNICION - 10cm COMO REFERENCIA, REINVELAR TAPAS DE POZOS DE VISITA SEGUN NIVELES EXISTENTES O NUEVOS.

La Dirección de Planeación y Proyectos solo autoriza el proyecto ejecutivo, no es responsable de la correcta ejecución de la obra. Este documento no tiene validez si no presenta las firmas de los responsables para su autorización, así como los sellos respectivos.

PRESIDENTE MUNICIPAL
M.P.P. Leonardo Montañez Castro
SECRETARIO DE OBRAS PÚBLICAS
Ing. Miguel Ángel Huizar Botello

REV	FECHA	OBSERVACIONES

Vo. Bo. DE LA DEPENDENCIA

RESP. DE PROY. EXTERNO		LOGO EXTERNO
CED. PROFESIONAL		
PROYECTO	REVISO	AUTORIZO

Dirección de Planeación y Proyectos de Obra — Secretaría de Obras Públicas

PROYECTISTA	COORDINADOR
ARQ. YARELI MEDINA RODRIGUEZ TAPIA	ARQ. ALEJANDRO JAIME LEAL
JEFE DE DEP.	DIRECTOR
LIC. CHANTAL SARAHI LUNA GARCIA	ARQ. ALEJANDRO PONCE RODRIGUEZ

PROYECTO
CONSTRUCCIÓN DE SOBRECARPETA ASFALTICA CALLE GUZMAN COL. CENTRO

UBICACIÓN
TRAMO ENTRE C. JOSE MARIA MORELOS Y PAVON Y C. CONDELL

CONTENIDO
PLANO DE DETALLES BANQUETA


CLAVE	No. PLANO
DETC 01	9
FECHA	ESCALA
NOV 2022	INDICADA
ACOTACIÓN	No. EXP.
METROS	E-000-22


Aguascalientes
LA CIUDAD DE TU VIDA

PISO EN RAMPAS DE 10.00 cm DE ESPESOR DE CONCRETO SIMPLE F'c=150 Kg/cm2, HECHO EN OBRA, TMA 3/4 19mm, GRAVA TRITURADA, ACABADO LAVADERO, INCLUYE: ESTAMPADO DE SIMBOLOGIA COMO INDICA EL PROYECTO, CIMBRADO, NIVELADO, VIBRADO, CURADO CON MEMBRANA BASE AGUA

RAMPA PEATONAL TIPO 1

VISTA EN PLANTA ESC. 1:10

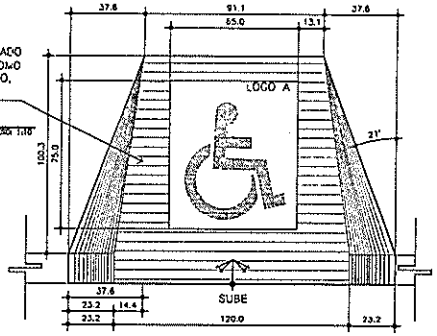


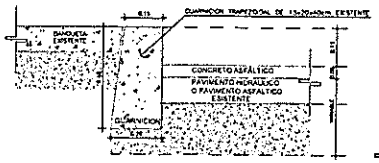

ESTADO ACTUAL

TERRACERIAS ESCALA S/E

DENTELLON TRAPEZOIDAL DE 15+-20X40 CM DE SECCION, CON CONCRETO PREMEZCLADO MR=38 KGF/CM2, TMA 1 1/2", R.R 14 DIAS. REVENIMIENTO NORMAL DE 10+-2 CM, GRAVA TRITURADA, ACABADO CON DOBLADOR Y PULIDO. INCLUYE: TRAZO, NIVELACIÓN, CIMBRADO, COLADO, VIBRADO, DESCIMBRADO, JUNTA A BASE DE ESPUMA DE POLIETILENO DE CELDAS CERRADAS DE 1/2" EN JUNTAS FRIAS LONGITUDINALES NO MAYOR A 30 MTS CORTE TRANSVERSAL CON CORTADORA A 1/3 DE SU ESPESOR MAXIMO @ 3 MTS, RELLENO PREFORMADO Y SELLADOR AUTONIVELANTE ASI COMO DE AISLAMIENTO CON OTRO ELEMENTO, Y CURADO CON MEMBRANA QUIMICA APLICADA CON ASPERSOR Y LIMPIEZA, SE DEBERA TENER CUIDADO EN EL NIVEL DE DESPLANTE PUES NO SE ACEPTAN ELLENOS FUERA DE LA BASE NUEVA. T R A B A J O T E R M I N A D O

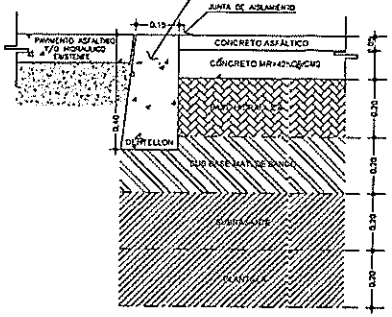


ESTRUCTURA 1-A

MR=40 KGF/CM2 1:10

PISO EN RAMPAS DE 10.00 cm DE ESPESOR DE CONCRETO SIMPLE F'c=150 Kg/cm2, HECHO EN OBRA, TMA 3/4 19mm, GRAVA TRITURADA, ACABADO LAVADERO, INCLUYE: ESTAMPADO DE SIMBOLOGIA COMO INDICA EL PROYECTO, CIMBRADO, NIVELADO, VIBRADO, CURADO CON MEMBRANA BASE AGUA

RAMPA PEATONAL TIPO 1

VISTA FRONTAL

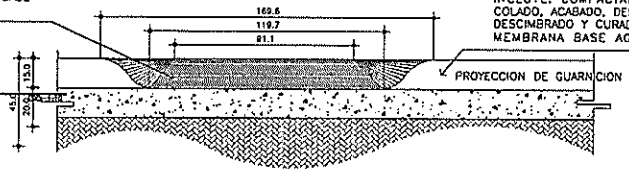


CONSTRUCCION DE GUARNICION RECTA Y/O CURVA TRAPEZOIDAL DE 15X20X40 CM DE SECCION CON CONCRETO PREMEZCLADO F'C= 150 KG/CM2, REVENIMIENTO DE 8 A 10 CM, T.M.A. 1 1/2" 38 MM, GRAVA TRITURADA, ACABADO PULIDO EN PARTE DE SUPERIOR Y DOBLADOR EN ARISTAS SUPERIORES. INCLUYE: COMPACTADO DE PLANTILLA, CIMBRADO, COLADO, ACABADO, DESCIMBRADO, ALINEADO, NIVELADO, DESCIMBRADO Y CURADO EN SU PARTE SUPERIOR CON MEMBRANA BASE AGUA A RAZON DE 1 LTO/M2.

PISO EN RAMPAS DE 10.00 cm DE ESPESOR DE CONCRETO SIMPLE F'c=150 Kg/cm2, HECHO EN OBRA, TMA 3/4 19mm, GRAVA TRITURADA, ACABADO LAVADERO, INCLUYE: ESTAMPADO DE SIMBOLOGIA COMO INDICA EL PROYECTO, CIMBRADO, NIVELADO, VIBRADO, CURADO CON MEMBRANA BASE AGUA

RAMPA PEATONAL TIPO 1

VISTA LATERAL ESC. 1:10

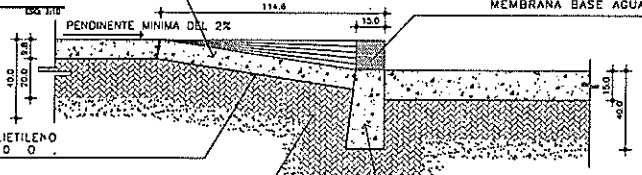


MEMBRANA IMPERMEABLE A BASE DE POLIETILENO N E G R O No. 6 0 0.

RELLENO COMPACTADO AL 90% CON MATERIAL DE BANCO EN CAPAS DE 20 CM UTILIZANDO BAILARINA, INCLUYE: SUMINISTRO DE TEPETATE EN LA OBRA, ABUNDAMIENTO, ACARREOS DENTRO DE LA OBRA, CRIBADO, RETIRO DE MATERIAL, MANO DE OBRA Y EQUIPO, PRUEBA DE CONTROL DE CALIDAD.

CONSTRUCCION DE GUARNICION RECTA Y/O CURVA TRAPEZOIDAL DE 15X20X40 CM DE SECCION CON CONCRETO PREMEZCLADO F'C= 150 KG/CM2, REVENIMIENTO DE 8 A 10 CM, T.M.A. 1 1/2" 38 MM, GRAVA TRITURADA, ACABADO PULIDO EN PARTE DE SUPERIOR Y DOBLADOR EN ARISTAS SUPERIORES. INCLUYE: COMPACTADO DE PLANTILLA, CIMBRADO, COLADO, ACABADO, DESCIMBRADO, ALINEADO, NIVELADO, DESCIMBRADO Y CURADO EN SU PARTE SUPERIOR CON MEMBRANA BASE AGUA A RAZON DE 1 LTO/M2.

DENTELLON TRAPEZOIDAL DE 15+-20X40 CM DE SECCIÓN, CON CONCRETO PREMEZCLADO MR=38 KGF/CM2, TMA 1 1/2", R.R 14 DÍAS. REVENIMIENTO NORMAL DE 10+-2 CM, GRAVA TRITURADA, ACABADO CON DOBLADOR Y PULIDO. INCLUYE: TRAZO, NIVELACIÓN, CIMBRADO, COLADO, VIBRADO, DESCIMBRADO, JUNTA A BASE DE ESPUMA DE POLIETILENO DE CELDAS CERRADAS DE 1/2" EN JUNTAS FRIAS LONGITUDINALES NO MAYOR A 30 MTS CORTE TRANSVERSAL CON CORTADORA A 1/3 DE SU ESPESOR MÁXIMO @ 3 MTS, RELLENO PREFORMADO Y SELLADOR AUTONIVELANTE ASÍ COMO DE AISLAMIENTO CON OTRO ELEMENTO, Y CURADO CON MEMBRANA QUIMICA APLICADA CON ASPERSOR Y LIMPIEZA, SE DEBERÁ TENER CUIDADO EN EL NIVEL DE DESPLANTE PUES NO SE ACEPTAN ELLENOS FUERA DE LA BASE NUEVA, TRABAJO T E R M I N A D O


CONSTRUCCION DE GUARNICION RECTA Y/O CURVA TRAPEZOIDAL DE 15X20X40 CM DE SECCION CON CONCRETO PREMEZCLADO F'C= 150 KG/CM2, REVENIMIENTO DE 8 A 10 CM, T.M.A. 1 1/2" 38 MM, GRAVA TRITURADA, ACABADO PULIDO EN PARTE DE SUPERIOR Y DOBLADOR EN ARISTAS SUPERIORES. INCLUYE: COMPACTADO DE PLANTILLA, CIMBRADO, COLADO, ACABADO, DESCIMBRADO, ALINEADO, NIVELADO, DESCIMBRADO Y CURADO EN SU PARTE SUPERIOR CON MEMBRANA BASE AGUA A RAZON DE 1 LTO/M2.

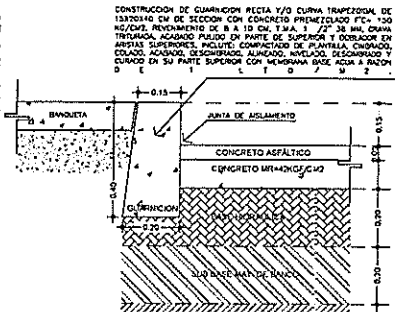

ESTRUCTURA 1

MR=40 KGF/CM2 S/E

LOCALIZACION:

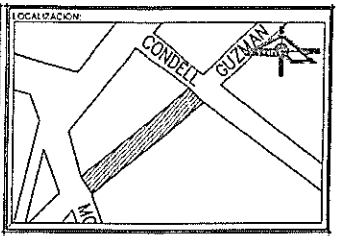

SIMBOLOGIA

NOTA 1:

TODOS LOS TRABAJOS SE EJECUTARAN CONFORME SE ESTABLECIDO EN LAS FICHAS TECNICAS DE EL DEPARTAMENTO DE CALIDAD, DIRECCION DE CONSTRUCCION Y CONSERVACION:

- FT 200 BANQUETAS
- FT 201 DENTELLON
- FT 204 GUARNICION TRAPEZOIDAL
- FT 208 LOSA DIAMANTE
- FT 211 RAMPA BANQUETA
- FT 303 BASES
- FT 308 PLANTILLA
- FT 309 SUB BASES
- FT 310 SUB PASANTE
- FT 505 SELLADO DE GRIETAS Y JUNTAS EN LOSAS DE CONCRETO


NOTA 2:


RESPETAR NIVELES DE PAVIMENTO EXISTENTES, EN SU CASO TOMAR NIVEL DE CORONA DE GUARNICION -15cm CON REFERENCIA, RENIVELAR TAPAS DE POZOS DE VISITA SEGUN NIVELES EXISTENTES O NUEVOS.


La Dirección de Planeación y Proyectos solo autoriza el proyecto ejecutivo, no es responsable de la correcta ejecución de la obra. Sin documento no tiene validez al no presenta las firmas de los responsables y su autorización, así como los sellos respectivos.

PRESIDENTE MUNICIPAL M.P.P. Leonardo Montañez Castro SECRETARIO DE OBRAS PUBLICAS Ing. Miguel Ángel Hulzar Botello	REV	FECHA	OBSERVACIONES	V°B° DE LA DEPENDENCIA	RESP. DE PROY. EXTERNO	CED. PROFESIONAL	PROYECTO / REVISO / AUTORIZÓ	Dirección de Planeación y Proyectos de Obra — Secretaría de Obras Públicas PROYECTISTA: ARQ. TANIA VALDEZ RODRIGUEZ TAPIA — COORDINADOR: ARQ. ALEJANDRO JAIME LEAL JEFE DE DEP.: LIC. DAVID MACHADO VILLALOBOS — DIRECTOR: ARQ. ALEJANDRO PONCE RODRIGUEZ	PROYECTO: CONSTRUCCIÓN DE SOBRECARPETA ASFALTICA CALLE GUZMAN COL. CENTRO UBICACIÓN: TRAMO ENTRE C. JOSE MARIA MORELOS Y PAVON Y C. CONDELL CONTENIDO: PLANO DE DETALLES BANQUETA	CLAVE: DETC 02	No. PLANO: 10
					LOGO EXTERNO						FECHA: NOV.2022	ESCALA: INDICADA
											ACOTACION: METROS	No. EXP.: E-000-22


Aguascalientes
LA CIUDAD DE TU VIDA

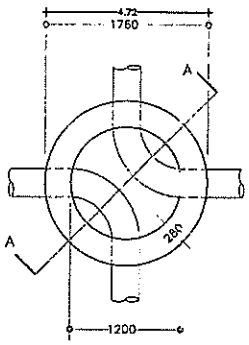

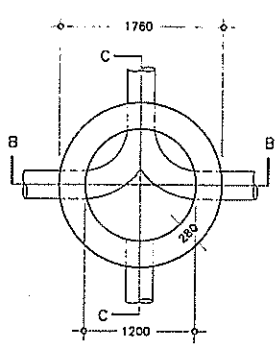

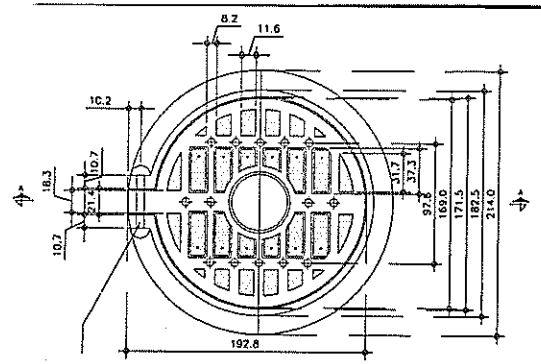


REMACHE DE CABEZA REDONDA
DE (3/4") CON LARGO DE 0.2095
(7 1/4") UN AGARRE DE 0.00156MM

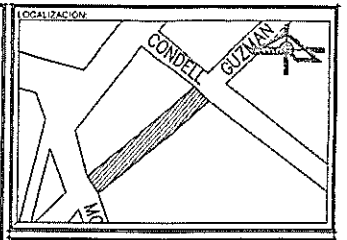



SIMBOLOGÍA


DETALLE DE BROCAL Y TAPA

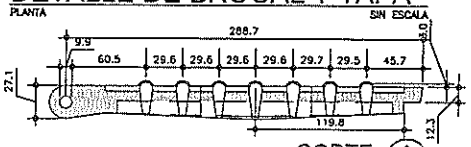

CORTE (A) — TAPA DE POZO DE VISITA-01

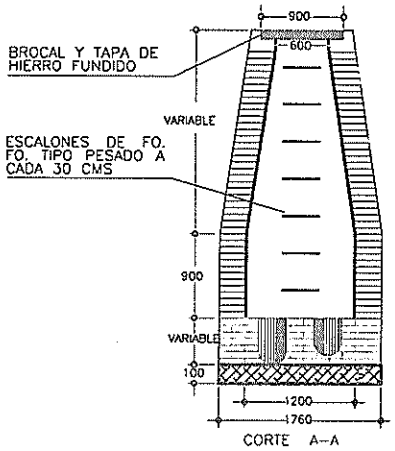

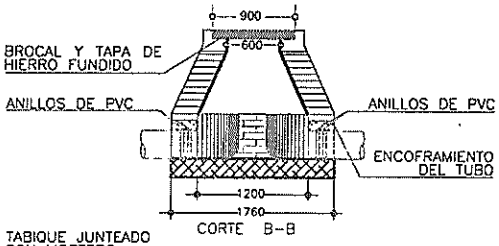


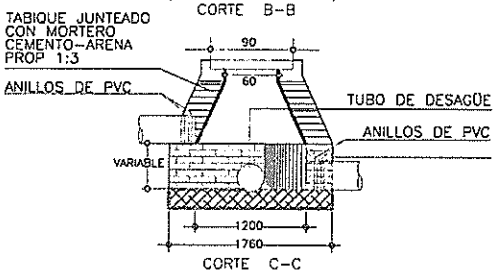

NOTA:
APLANADO INTERIOR LISO Y EXTENDIDO A BASE DE MORTERO CEMENTO–ARENA PROP. 1:3 CON IMPERMEABILIZANTE INTERGAL (2KG POR CADA SACON DE 50KG DE CEMENTO

POZO DE VISITA COMUN

SIN ESCALA

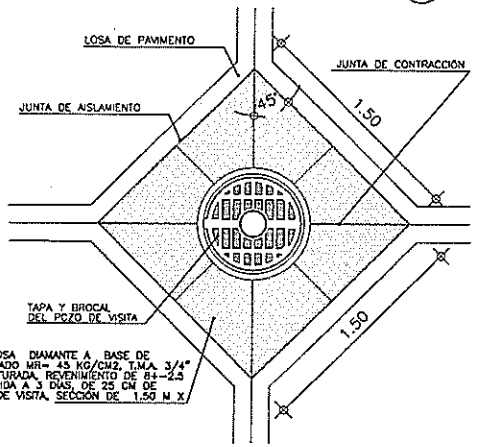

CONSTRUCCIÓN DE LOSA DIAMANTE A BASE DE CONCRETO PREMEZCLADO MR= 45 KG/CM2, T.M.A. 3/4" (19 mm), GRAVA TRITURADA, REVENIMIENTO DE 8+-2.5 cm, RESISTENCIA RAPIDA A 3 DIAS, DE 25 CM DE ESPESOR, EN POZO DE VISITA, SECCIÓN DE 1.50 M X 1.50 M.

DETALLE LOSA DIAMANTE

PLANTA — SIN ESCALA

La Dirección de Planeación y Proyectos solo autoriza el proyecto ejecutivo, no es responsable de la correcta ejecución de la obra. Este documento no tiene validez si no presenta las firmas de los responsables para su autorización, así como los sellos respectivos.

PRESIDENTE MUNICIPAL M.P.P. Leonardo Montañez Castro SECRETARIO DE OBRAS PÚBLICAS Ing. Miguel Ángel Hulzar Botello	REV. FECHA OBSERVACIONES	Vo. Bo. DE LA DEPENDENCIA	RESP. DE PROY. EXTERNO / CED. PROFESIONAL / PROYECTO / REVISÓ / AUTORIZO	LOGO EXTERNO	Dirección de Planeación y Proyectos de Obra — Secretaría de Obras Públicas PROYECTISTA: ARQ. YASMI MILDRET RODRIGUEZ TAPIA COORDINACIÓN: ARQ. ALEJANDRO JAIME LEAL JEFE DE DEP.: LIC. OMAR ALEJANDRO LUJAN GARCIA DIRECTOR: ARQ. ALEJANDRO PONCE RODRIGUEZ	PROYECTO: CONSTRUCCIÓN DE SOBRECARPETA ASFALTICA CALLE GUZMAN COL. CENTRO UBICACIÓN: TRAMO ENTRE C. JOSE MARIA MORELOS Y PAVON Y C. CONDELL CONTENIDO: PLANO DE DETALLES SANITARIOS	CLAVE: DETS 01 / No. PLANO: 11 FECHA: NOV 2022 / ESCALA: INDICADA ACOTACIÓN: METROS / No. EXP.: E-000-22	Aguascalientes — LA CIUDAD DE TU VIDA