Aguascalientes
LA CIUDAD DE TU VIDA

Dirección de Programación Presupuestal
Núm. Oficio AMPP/0591/22
Aguascalientes, Ags. 8 de Diciembre del 2022
Asunto: Validación de Expediente Técnico

C.P. SERGIO ARTURO LOZANO GONZÁLEZ
SECRETARIO DE FINANZAS MUNICIPALES
P R E S E N T E

Con fundamento en los artículos 17 fracción XV, 60 fracción XVI y 76 fracción VI del Reglamento del Sistema Integral de Desarrollo Municipal y del Instituto Municipal de Planeación y Evaluación de Aguascalientes, hago referencia al oficio SOPMA/2699/22 recibido por este Instituto el día 8 de Diciembre del 2022 por parte de la Secretaría de Obras Públicas Municipales, mediante el cual remiten el expediente técnico original de la siguiente obra para su análisis, registro y priorización, conforme al Programa Anual de Obra Pública y Programas Sociales para el ejercicio presupuestal 2022:

DEPENDENCIA EJECUTORA:	SECRETARÍA DE OBRAS PÚBLICAS MUNICIPALES
NOMBRE DE LA OBRA O PROYECTO:	PAVIMENTO HIDRÁULICO
UBICACIÓN:	CALLE INÉS MARISCAL, TRAMO: CALLE ENTRE ENRIQUE MONTOYA Y CALLE FRANCISCO ROSTRO, LOS NEGRITOS, AGUASCALIENTES, AGS.
FONDO DE INVERSIÓN:	PROGRAMA DIRECTO MUNICIPAL
IMPORTE:	$2,400,760.13 (ET FINAL)
No. DE OBRA:	2022-PDM-0115-UR-0101
MODALIDAD DE EJECUCIÓN:	CONTRATO
EJE:	MUNICIPIO SOBRESALIENTE
ESTRATEGIA:	OBRA PÚBLICA INTELIGENTE
POLITICA:	5.8.1.REHABILITACIÓN Y MANTENIMIENTO VIALIDADES, CAMINOS, CALLES, ÁREAS DE TERRACERÍA Y CAUCES (C

Al respecto, hago de su conocimiento que dicho expediente ha sido analizado en su integración técnica y documental, con base en el artículo 168 fracción I del Reglamento de la Ley de Obras Públicas y Servicios Relacionados para el Estado de Aguascalientes y sus Municipios.

Asimismo, le comento que este Instituto valida dicha obra acorde a lo establecido en los artículos 14, 22 párrafo segundo y 23 de la Ley de Obras Públicas y Servicios Relacionados para el Estado de Aguascalientes y sus Municipios, la cual se encuentra alineada al Plan de Desarrollo Municipal vigente, para dar cumplimiento a las metas establecidas en el mismo.

Cabe hacer mención que los recursos solicitados para este proyecto de inversión, estarán sujetos a la disponibilidad presupuestal para el presente ejercicio fiscal que determine la Secretaría a su digno cargo. Sin otro particular por el momento, le envío un cordial saludo.

A T E N T A M E N T E

ARQ. AUSTRIA GABRIELA DÁVILA DE LA LLAVE
DIRECTORA GENERAL DEL IMPLAN

CAAR / JDBC
C.c.p. I.C. ING. MIGUEL ÁNGEL HUIZAR BOTELLO .- Secretaría de Obras Públicas Municipales .Para su conocimiento.
C.c.p. Archivo.

Instituto Municipal de Planeación y Evaluación de Aguascalientes

Antonio Acevedo Escobedo 103 A. Col. Centro
Aguascalientes, Ags. C.P. 20000

(449) 9101010 Ext. 3117

www.implanags.gob.mx

GOBIERNO MUNICIPAL DE AGUASCALIENTES

INSTITUTO MUNICIPAL DE PLANEACION

IMPLAN

ANÁLISIS INTEGRAL DE EXPEDIENTE TÉCNICO

No. DE OBRA (PAOP 2020):	2022-PDM-0115-UR-0101	REGISTRO No.	288
OFICIO DE VALIDACIÓN:	AMPP/0591/22	FECHA RECIBIDO PARA REVISIÓN:	8 de Diciembre del 2022
PROGRAMA:	URBANIZACIÓN	LOCALIDAD O COLONIA:	Los Negritos
SUB-PROGRAMA:	Pavimentación (Const., Ampliación y Rehabilitación)	DELEGACIÓN:	San Marcos
DEPENDENCIA:	Secretaría de Obras Públicas Municipales	MOD. DE EJECUCIÓN:	CONTRATO
NOMBRE DE LA OBRA:	PAVIMENTO HIDRÁULICO, CALLE INÉS MARISCAL, TRAMO: CALLE ENTRE ENRIQUE MONTOYA Y CALLE FRANCISCO ROSTRO		
FUENTE DE FINANCIAMIENTO:	PROGRAMA DIRECTO MUNICIPAL, PDM		
INVERSIÓN:	$2,400,760.13	CLASIFICACIÓN DE OBRA:	BIENES DE DOMINIO PUBLICA

TOTAL	FEDERAL	ESTATAL	MUNICIPAL	BENEFICIARIOS	OTROS	DIFERENCIA ENTRE MOD.
$2,400,760.13	0.00	0.00	$2,400,760.13	0.00	0.00	*$0,00*

TIPO DE EXPENDIENTE:	ET FINAL	AÑO: 2022	AÑO:	AÑO:			
AVANCES:	Financiero: 1 %		Físico: 1 %				
FECHA DE INICIO:	11 de Noviembre del 2022		FECHA DE TÉRMINO:		25 de Diciembre del 2022	REGISTRO SIMA:	115

CHEK LIST DE LOS ANEXOS DEL EXPEDIENTE TÉCNICO

CÉDULA DE REGISTRO DE OBRA	✓
DICTAMEN DE FACTIBILIDAD	✓
MEMORIA DESCRIPTIVA	✓
PRESUPUESTO BASE	✓
FACTIBILIDAD VERIFICADA EN CAMPO	✓
CROQUIS DE UBICACIÓN (MACRO)	✓
CROQUIS DE UBICACIÓN (MACRO)	✓
PROGRAMA DE OBRA Y MONTOS MENSUALES	✓
PLANOS O ESTUDIOS TÉCNICOS	✓
PADRÓN DE BENEFICIARIOS	N/A
ACTA DE ACEPTACIÓN DEL PROYECTO	N/A
DICTAMEN DE IMPACTO AMBIENTAL	N/A
CONVENIO DE CONCERTACIÓN	N/A
ACTA CONSTITUTIVA	N/A

METAS		BENEFICIARIOS		PERIODO DE EJECUCION		OBRA PROPUESTA		CLAVE SISCO
UNIDAD DE MEDIDA	CANT	TIPO DE BENEFICIARIOS	CANTIDAD	FECHA DE INICIO	FECHA DE TERMINO	CONCEPTO	JORNALES A GENERAR	
M2	1108.36	Personas	120	2022-11-11	2022-12-25	Pavimentación	6241	2377

INCLUIDO EN PLAN DE DESARROLLO MUNICIPAL Y EL PROGRAMA ANUAL DE OBRA PÚBLICA

OBSERVACIONES:

SIN OBSERVACIONES

RECIBIO: ING. JOSÉ DAVID BURGUETE CLAUSTRO
Analista de Programación e Inversión de Obra Pública

8 de Diciembre del 2022
Fecha de validación

8 de Diciembre del 2022
Fecha de validación Expediente

PROCEDE Si ✓ No

AYUNTAMIENTO DE AGUASCALIENTES

CEDULA DE REGISTRO POR OBRA

050400-001E00E05-05-2-2-1-00-1-E-0510-0-17-0115-21-1521-6144

2022-PDM-0115-UR-01-020	Obra **PAVIMENTO HIDRÁULICO, CALLE INÉS MARISCAL. T-01**
Tipo DEFINITIVO 1 2022 Folio SISCO **2377**	Ubic. TRAMO: ENTRE CALLE ENRIQUE MONTOYA Y CALLE FRANCISCO ROSTRO, LOS NEGRITOS Com. , Deleg. Insurgentes

Ent. Ejecutora : **050400001E00E05**

Eje: **05**	MUNICIPIO SOBRESALIENTE
Finalidad: **2**	DESARROLLO SOCIAL
Función: **2**	VIVIENDA Y SERVICIOS A LA COMUNIDAD
Subfunción: **1**	URBANIZACIÓN
Tema: **00**	SIN TEMA
Cuenta del Gasto **1**	GASTO PROGRAMABLE
Clasif. Programatica: **E**	PRESTACIÓN DE SERVICIOS PÚBLICOS
Programa: **0510**	Movilidad Urbana
SubPrograma: **0**	SUBPROGRAMA GENÉRICO
Proyecto: **17**	
Tipo de Gasto: **21**	GASTO INVERSIÓN / OBRA PÚBLICA

INVERSION 2022

Municipal	1521	EXCEDENTES PARTICIPACIONES 2022 2022	$2,400,760.13
		Folio SIMA 115 Total	$2,400,760.13

METAS

Unidad de Medida	Cantidad	Descripción
M2	1108.36	CONSTRUCCIÓN DE PAVIMENTO PAVIMENTO HIDRÁULICO, CALLE INÉS MARISCAL. T-01

Inversión Ejercida Total al	31 de Diciembre de 2021	$0.00
Avance Fisico Acumulado al	31 de Diciembre de 2021	
Avance Fisico Acumulado Programado al	31 de Diciembre de 2022	100 %

Fecha de Inicio 11 Nov 2022 Fecha de Terminación 25 Dic 2022

Jornales a Generar en 2022 6241

Modalidad de ejecución CONTRATO

Clasificación de la Obra Bienes de Dominio Público

Registro del Patrimonio: Obras del dominio público

OBRAS PÚBLICAS

Av. Aguascalientes Sur No. 2615
Fracc. Jardines de las Fuentes,
Aguascalientes, Ags. C.P. 20278

(449) 9 78 92 01, 06, 09

www.ags.gob.mx

GENERALES

Nombre del Proyecto : PAVIMENTO HIDRÁULICO, CALLE INÉS MARISCAL. T-01

TRAMO: ENTRE CALLE ENRIQUE MONTOYA Y CALLE FRANCISCO ROSTRO, LOS NEGRITOS Com. , Deleg. Insurgentes

Programa : UR URBANIZACIÓN

Subprograma : 01 PAVIMENTACIÓN (CONST., AMPLIACIÓN Y REHABILITACIÓN) (c).- Hidráulica)

Clave del Municipio : AGUASCALIENTES

Localidad :

Barrio, Colonia o Ejido : LOS NEGRITOS Com.

Tipo de Obra : NUEVA

DESCRIPCIÓN DEL PROYECTO:

PAVIMENTO HIDRÁULICO, CALLE INÉS MARISCAL. T-01

PRELIMINARES Y DEMOLICIONES 1,031.00 M2
EXCAVACIONES, ACARREOS Y TERRACERÍAS 18,558.00 M3-KM
PAVIMENTO 1,108.36 M2
DENTELLONES DE CONCRETO 63.10 ML
GUARNICIONES 54.30 ML
BANQUETA 59.28 M2 Y RAMPA 3.20 M2
OBRA COMPLEMENTARIA 1.00 OBRA
LIMPIEZAS 1,031.00 M2
SEÑALIZACIÓ HORIZONTAL 1.00 OBRA
LÍNEA DE ALCANTARILLADO 136.88 Y 12.40 ML
DESCARGAS DOMICILIARIAS 11.000 PZAS
LÍNEA DE AGUA POTABLE 124.50 ML
TOMAS DOMICILIARIAS 20.00 PZAS

Beneficiarios (No. y Tipo) :

120	PERSONAS

Hombres: 60 Mujeres: 60

OBRAS PÚBLICAS

Av. Aguascalientes Sur No. 2615
Fracc. Jardines de las Fuentes,
Aguascalientes, Ags. C.P. 20278

(449) 9 78 92 01, 06, 09

www.ags.gob.mx

Los abajo firmantes, hacen constar que el presente proyecto :

PAVIMENTO HIDRÁULICO, CALLE INÉS MARISCAL. T-01

TRAMO: ENTRE CALLE ENRIQUE MONTOYA Y CALLE FRANCISCO ROSTRO, LOS NEGRITOS Com. , Deleg. Insurgentes

cumple con los Requisitos y Normas Técnicas establecidas por la Dependencia Normativa, por lo que es viable su ejecución. Comprometiéndose la misma a proporcionar la supervisión y asistencia técnica necesaria durante el proceso administrativo.

Por la Dependencia Ejecutora

Ing. Miguel Angel Huizar Botello
Secretario de Obras Públicas

Lic. Jaime Gallo Camacho
Secretario de Desarrollo Urbano

LUGAR :AGUASCALIENTES, AGS.

Av. Aguascalientes Sur No. 2615
Fracc. Jardines de las Fuentes,
Aguascalientes, Ags. C.P. 20278

(449) 9 78 92 01, 06, 09

www.ags.gob.mx

H. AYUNTAMIENTO CONSTITUCIONAL DEL MUNICIPIO DE AGUASCALIENTES 2021-2024

AYUNTAMIENTO DE AGUASCALIENTES

FACTIBILIDAD VERIFICADA EN CAMPO

Aguascalientes
LA CIUDAD DE TU VIDA

MUNICIPIO: AGUASCALIENTES

LOCALIZACION: TRAMO: ENTRE CALLE ENRIQUE MONTOYA Y CALLE FRANCISCO ROSTRO, LOS NEGRITOS Com. , Deleg. Insurgentes

PROGRAMA: URBANIZACIÓN

SUBPROGRAMA: PAVIMENTACIÓN (CONST., AMPLIACIÓN Y REHABILITACIÓN) (c).- Hidráulica)

OBRA A REALIZAR: PAVIMENTO HIDRÁULICO, CALLE INÉS MARISCAL. T-01

DEPENDENCIA EJECUTORA: SECRETARÍA DE OBRAS PUBLICAS DEL MUNICIPIO DE AGUASCALIENTES

FORMA DE EJECUCION: CONTRATO

TIPO DE OBRA PROPUESTA: NUEVA

CONDICIONES ACTUALES DE LA OBRA:

PAVIMENTO HIDRÁULICO, CALLE INÉS MARISCAL. T-01

CARACTERISTICAS DE LA OBRA: Bueno

FACTIBILIDAD DE LA OBRA:

ESTA OBRA SE REQUIERE PARA EL BENEFICIO DE LA CIUDADANÍA

PROCEDE: SI [X] NO [ ]

REVISÓ: Jefa del Departamento de Expedientes Tecnicos y Costos

NOMBRE: Arq. Blanca Margarita Martinez Amador

FIRMA:

FECHA: 29 Nov 2022

SECRETARÍA DE OBRAS PÚBLICAS

Av. Aguascalientes Sur No. 2615
Fracc. Jardines de las Fuentes,
Aguascalientes, Ags. C.P. 20278

(449) 9 78 92 01, 06, 09

www.ags.gob.mx


No. Folio SISCO 2377

H. AYUNTAMIENTO DE AGUASCALIENTES
SECRETARÍA DE OBRAS PÚBLICAS
DIRECCIÓN DE SUPERVISIÓN DE OBRA
LOCALIZACION

H. AYUNTAMIENTO CONSTITUCIONAL DEL MUNICIPIO DE AGUASCALIENTES 2021-2024

Aguascalientes
LA CIUDAD DE TU VIDA

OBRA:	PAVIMENTO HIDRÁULICO, CALLE INÉS MARISCAL. T-01, TRAMO: ENTRE CALLE ENRIQUE MONTOYA Y CALLE FRANCISCO ROSTRO, LOS NEGRITOS Com.					
NO. DE CONTR	DM-0115-2022	CONTRATISTA:	GRUPO CONSTRUCTOR MED CER, S.A. DE C.V.			

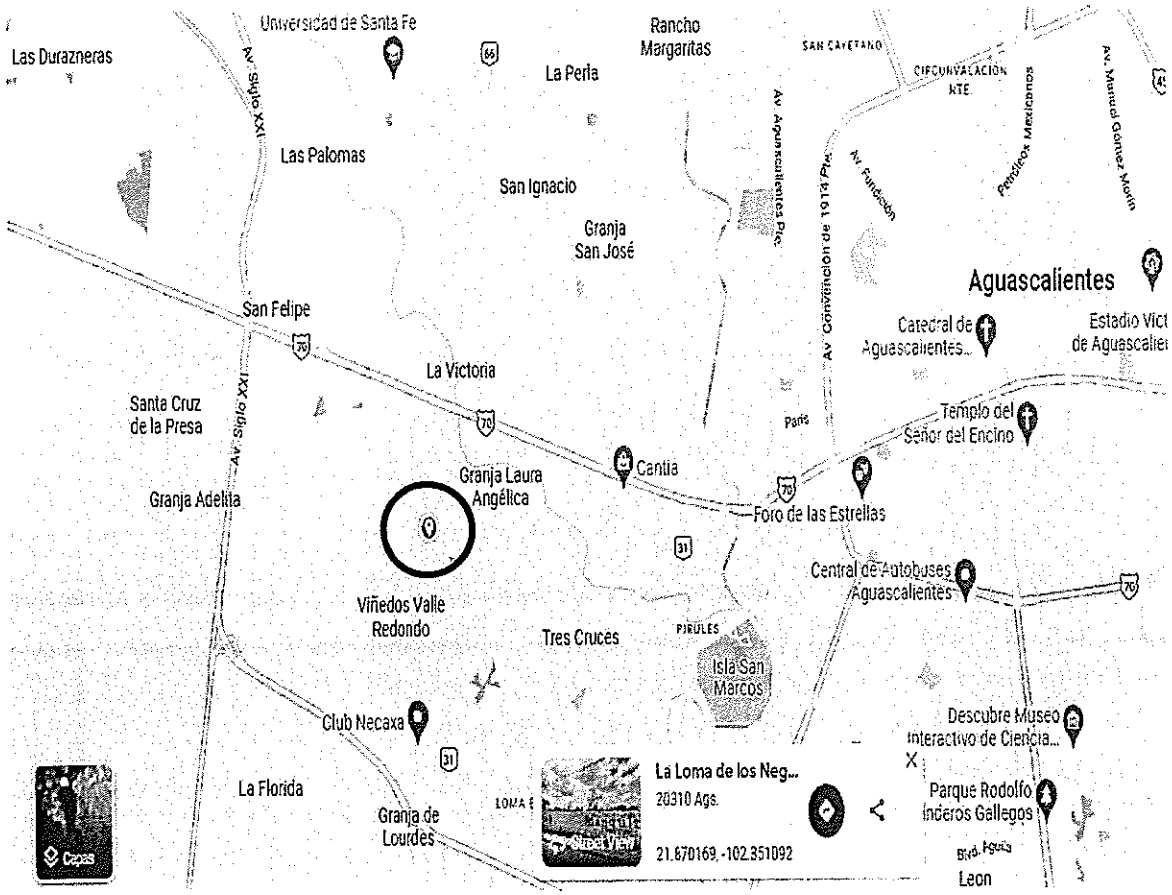

ING. IVAN ALEJANDRO RUIZ ESPARZA SOLIS
SUPERVISOR DE OBRA.

H. AYUNTAMIENTO CONSTITUCIONAL DEL MUNICIPIO DE AGUASCALIENTES 2021-2024

H. AYUNTAMIENTO DE AGUASCALIENTES
SECRETARÍA DE OBRAS PÚBLICAS
DIRECCIÓN DE SUPERVISIÓN DE OBRA
LOCALIZACION

Aguascalientes
LA CIUDAD DE TU VIDA

OBRA:	PAVIMENTO HIDRÁULICO, CALLE INÉS MARISCAL. T-01, TRAMO: ENTRE CALLE ENRIQUE MONTOYA Y CALLE FRANCISCO ROSTRO, LOS NEGRITOS Com.					
NO. DE CONTR	DM-0115-2022		CONTRATISTA:	GRUPO CONSTRUCTOR MED CER, S.A. DE C.V.		



ING. IVAN ALEJANDRO RUIZ ESPARZA SOLIS
SUPERVISOR DE OBRA.

RO3-POS-SOS-7.5.1-04	
REVISION:	00
ENTIDAD RESPONSABLE:	SUPERVISOR DE OBRA
TIEMPO DE RET:	02 AÑOS

PROGRAMA DE OBRA DEFINITIVO

No. DE CONTRATO : DM-0115-2022

PROGRAMA: UR URBANIZACIÓN

No. OBRA Y NOMBRE DE LA OBRA: PAVIMENTO HIDRÁULICO, CALLE INÉS MARISCAL T-01, TRAMO: ENTRE CALLE ENRIQUE MONTOYA Y CALLE FRANCISCO ROSTRO, LOS NEGRITOS Com.

INICIO VIGENTE: 11-noviembre-22

TERMINO REAL: 25-diciembre-22

RECURSO: 2022

CONCEPTO			1	2	3	4	5	6	7	8	9	10	11	12	13	14	15	16	PONDERACIÓN %	
			2022																FINANCIERO	FÍSICO
			OCTUBRE	NOVIEMBRE	DICIEMBRE	ENERO	FEBRERO	MARZO	ABRIL	MAYO	JUNIO	JULIO	AGOSTO	SEPTIEMBRE	OCTUBRE	NOVIEMBRE	DICIEMBRE	ENERO	%	%
DESCRIPCION	INVERSION																			
PAVIMENTO HIDRÁULICO, CALLE INÉS MARISCAL T-01, TRAMO: ENTRE CALLE ENRIQUE MONTOYA Y CALLE FRANCISCO ROSTRO, LOS NEGRITOS Com.																				
TRAMO: ENTRE CALLE ENRIQUE MONTOYA Y CALLE FRANCISCO ROSTRO, LOS NEGRITOS Com.																				
PAVIMENTO HIDRAULICO	$ 1,555,190.77	100																	75.14	40.00
SEÑALIZACION	$ 81,011.33	100																	3.91	30.00
HIDRAULICO SANITARIO	$ 433,418.71	100																	20.94	30.00
		-																		
		-																		
		-																	0.00	0.00
		-																		
		-																		
		-																		
		-																		
		-																		
		-																		
SUBTOTAL SIN IVA	$ 2,069,620.80																			
AVANCE SEMANAL %																			100.00	100.00
AVANCE SEMANAL ACUMULADO %																				
EJERCIDO SEMANAL $																$1,211,014.10	$858,606.72	$0.00	$ 2,069,620.80	
EJERCIDO MENSUAL $			$0.00	$0.00	$0.00	$0.00	$0.00	$0.00	$0.00	$0.00	$0.00	$0.00	$0.00	$0.00	$0.00	$1,211,014.10	$858,606.72	$0.00	$ 331,139.33	IVA 16%
EJERCIDO MENSUAL ACUMULADO $			0.00	0.00	0.00	0.00	0.00	0.00	0.00	0.00	0.00	0.00	0.00	0.00	0.00	1,211,014.10	2,069,620.81	2,069,620.81		
EJERCIDO SEMANAL %																59%	41%	0%		
EJERCIDO MENSUAL %			0%	0%	0%	0%	0%	0%	0%	0%	0%	0%	0%	0%	0%	59%	100%	100%	GRAN TOTAL EJERCIDO	
EJERCIDO MENSUAL ACUMULADO %			0%	0%	0%	0%	0%	0%	0%	0%	0%	0%	0%	0%	0%				$ 2,400,760.13	

ING. IVAN ALEJANDRO RUIZ ESPARZA LOUIS
SUPERVISOR

PRE

PRESIDENCIA MUNICIPAL DE AGUASCALIENTES

FACTIBILIDAD VERIFICADA EN CAMPO

GENERALES

EJERCICIO: 2022 APROBACION No: 2022-PDM-0115-UR-01-020
LOCALIDAD: TRAMO: ENTRE CALLE ENRIQUE MONTOYA Y CALLE FRANCISCO ROSTRO, LOS NEGRITOS Com.
MUNICIPIO: AGUASCALIENTES, Mpio.
TIPO DE INVERSION: EXCEDENTES PARTICIPACIONES (100%) (MUNICIPAL)
PROGRAMA: UR URBANIZACIÓN
SUB-PROGRAMA: 01 PAVIMENTACIÓN (CONST., AMPLIACIÓN Y REHABILITACIÓN) Inciso c) .Hidráulica
OBRA A REALIZARSE: PAVIMENTO HIDRÁULICO, CALLE INÉS MARISCAL T-01, TRAMO: ENTRE CALLE ENRIQUE MONTOYA Y CALLE FRANCISCO ROSTRO, LOS NEGRITOS Com.

DEPENDENCIA EJECUTORA: SECRETARÍA DE OBRAS PÚBLICAS MUNICIPALES (S.O.P.M.A)
FORMACIÓN DE EJECUCION: CONTRATO NO. DE CONTRATO: DM-0115-2022
NOMBRE CONTRATISTA: GRUPO CONSTRUCTOR MED CER, S.A. DE C.V.
REPRESENTANTE: ING. CESAR AUGUSTO MEDRANO CERVANTES
MONTO CONT. ORIGEN $ 2,279,776.95 ANTICIPO: $ 982,662.48 PLAZO 45 DIAS
1A AMPLIACION $: $ 120,983.18 1 AMPL DIAS
2A AMPLIACION $: 2 AMPL DIAS
FIRMA CONTRATO: 04/11/2022
INICIO CONT: dd/mm/aa 05/11/2022 TERMINO CONT: 19/12/2022
INICIO REAL: dd/mm/aa 11/11/2022 TERMINO REAL: 25/12/2022

TIPO DE OBRA PROPUESTA

NUEVA CREACIÓN	X	CONSOLIDACIÓN	
COMPLEMENTARIA		AMPLIACIÓN	
REHABILITACIÓN		EQUIPAMIENTO	

CARACTERÍSTICAS DE LA OBRA:

FORMACION Y COMPACTACION DE SUB-RASANTE, SUB-BASE Y BASE HIDRAULICA
PAVIMENTO HIDRAULICO A BASE CONCRETO PREMEZCLADO MR=38 KG/CM2
RED DE ALCANTARILLADO PVC SERIE 20 RED DE AGUA POTABLE PVC HIDRAULICO RD-26
CONSTRUCCION DE BANQUETAS RAMPAS Y GUARNICIONES

CONDICIONES ACTUALES DE LA OBRA: (SELECCIONAR UNO OBLIGATORIO)

BUEN ESTADO X REGULAR PESIMO ESTADO

FACTIBILIDAD DE LA OBRA: (CONDICIONES ACTUALES DE LA OBRA)

ESTA OBRA SE ENCUENTRA EN CONDICIONES PARA OPERARSE

PROCEDE: SI: X NO:
MARQUE SOLO UNA

ING. IVAN ALEJANDRO RUIZ ESPARZA SOLIS
SUPERVISOR

PRESIDENCIA MUNICIPAL DE AGUASCALIENTES

FACTIBILIDAD VERIFICADA EN CAMPO

GENERALES

LOCALIDAD: TRAMO: ENTRE CALLE ENRIQUE MONTOYA Y CALLE FRANCISCO ROSTRO, LOS NEGRITOS Com.
MUNICIPIO: AGUASCALIENTES, Mpio.
PROGRAMA: UR URBANIZACIÓN
SUB-PROGRAMA: 01 PAVIMENTACIÓN (CONST., AMPLIACIÓN Y REHABILITACIÓN) Inciso c) .Hidráulica
OBRA A REALIZARSE: PAVIMENTO HIDRÁULICO, CALLE INÉS MARISCAL. T-01, TRAMO: ENTRE CALLE ENRIQUE MONTOYA Y CALLE FRANCISCO ROSTRO, LOS NEGRITOS Com.

DEPENDENCIA EJECUTORA: SECRETARÍA DE OBRAS PÚBLICAS MUNICIPALES (S.O.P.M.A)
FORMACIÓN DE EJECUCION: CONTRATO

TIPO DE OBRA PROPUESTA

NUEVA CREACIÓN	X	CONSOLIDACIÓN	
COMPLEMENTARIA		AMPLIACIÓN	
REHABILITACIÓN		EQUIPAMIENTO	

CARACTERÍSTICAS DE LA OBRA:

FORMACION Y COMPACTACION DE SUB-RASANTE, SUB-BASE Y BASE HIDRAULICA
PAVIMENTO HIDRAULICO A BASE CONCRETO PREMEZCLADO MR=38 KG/CM2
RED DE ALCANTARILLADO PVC SERIE 20 RED DE AGUA POTABLE PVC HIDRAULICO RD-26
CONSTRUCCION DE BANQUETAS RAMPAS Y GUARNICIONES

CONDICIONES ACTUALES DE LA OBRA:

BUEN ESTADO: X REGULAR: PESIMO ESTADO:

FACTIBILIDAD DE LA OBRA:

ESTA OBRA SE ENCUENTRA EN CONDICIONES PARA OPERARSE

PROCEDE **SI:** X **NO:**

ING. IVAN ALEJANDRO RUIZ ESPARZA SOLIS
SUPERVISOR

H. AYUNTAMIENTO CONSTITUCIONAL DEL MUNICIPIO DE AGUASCALIENTES 2021-2024

PRESUPUESTO MODIFICADO

Aguascalientes

Obra: **PAVIMENTO HIDRÁULICO, CALLE INÉS MARISCAL. T-01**

Ubicación: **TRAMO: ENTRE CALLE ENRIQUE MONTOYA Y CALLE FRANCISCO ROSTRO, LOS NEGRITOS Com.**

Contratista: **GRUPO CONSTRUCTOR MED CER, S.A. DE C.V. (201)**

No.	Concepto	Unidad	Cantidad	Precio Unitario	Importe Total
	GRUPO: **PAVIMENTO HIDRAULICO**				
	PARTIDA: **PRELIMINARES Y DEMOLICIONES**				
1	LIMPIA, TRAZO Y NIVELACION EN PAVIMENTOS, CALLES Y VIALIDADES CON EQUIPO TOPOGRAFICO, INCLUYE: EJES, BANCO DE NIVEL, RENIVELACIONES LAS VECES NECESARIAS, CORRECCION DE RASANTE A PUNTOS OBLIGADOS (AUTORIZADOS POR LA SUPERVISION), ESTACAS, VARILLAS, MANO DE OBRA CALIFICADA, HERRAMIENTA NECESARIA, EQUIPO DE PRECISION CALIBRADO, TRABAJO TERMINADO.P.U.O.T.	M2	1031	$10.96	$11,299.76
2	SONDEO A MANO O A MAQUINA PARA LOCALIZACION DE TUBERIAS CUALQUIER PROFUNDIDAD Y MATERIAL PARA VERIFICAR LA CALIDAD DE LAS INSTALACIONES HIDRAULICO SANITARIAS CUIDANDO NO DAÑARLAS PARA NO INTERFERIR EN LOS SERVICIOS, INCLUYE: EXCAVACION, EQUIPO, MANO DE OBRA, REPORTE A LA SUPERVISION, RELLENOS, COMPACTACIONES, TRABAJO TERMINADO.	SONDE	4	$1,153.10	$4,612.40
3	CORTE CON DISCO DIAMANTADO DE 14" EN PISOS DE CONCRETO ASFALTICO DE HASTA 8.00 cm. DE PROFUNDIDAD. INCLUYE: TRAZO, EQUIPO Y OPERACION, LIMPIEZAS.	ML	97.68	$41.89	$4,091.82
4	DEMOLICION PARCIAL DE PAVIMENTO HIDRAULICO Y/O ASFALTICO DE HASTA 15 CM. DE ESPESOR PROMEDIO EN PAVIMENTOS Y (BANQUETAS, LOSAS DIAMANTE Y CAJAS DE VALVULAS, TOPES) CON O SIN ARMADO DE ACERO, SIN RECUPERACION, MUROS, MOJONERAS, ANCLAJES, ETC, DE FORMA MANUAL Y MECANICA, INCLUYE ACARREO DE MATERIAL AL LUGAR DE ACOPIO, HERRAMIENTA NECESARIA Y TODO LO NECESARIO PARA SU CORRECTA EJECUCION, LIMPIEZA, TRABAJO TERMINADO	M3	2.62	$198.89	$521.09
5	DEMOLICION CONTROLADA DE CONCRETO HIDRAULICO EN DENTELLONES Y GUARNICIONES DE 15 x 20 x 40 CM. DE FORMA MANUAL Y MECÁNICA, INCLUYE: CORTES CON DISCO, ACARREO DEL MATERIAL AL LUGAR DE ACOPIO PARA SU CARGA Y ACARREO FUERA DE LA OBRA.	ML	15.4	$468.89	$7,220.91
6	DESPALME DE TERRENO CON MAQUINA CUALQUIER SECCIÓN HASTA EL NIVEL O PROFUNDIDAD QUE MARQUE SUPERVISIÓN EN MATERIAL TIPO 1 TODAS LAS ZONAS. INCLUYE: ACARREOS LOCALES a 1 estacion Y LIMPIEZAS.	M3	154.65	$29.66	$4,586.92
7	DEMOLICION DE POZO DE VISITA DE TABIQUE ROJO CON UNA ALTURA DE 1.50 a 3.50 MTS. . INCLUYE: , DEMOLICION TOTAL DE MUROS DE TABIQUE ASENTADO A 28CM, DEMOLICION DE PLANTILLA DE PIEDRA, RETIRO SIN RECURACION DE CERO DE REFUERZO Y TUBERIAS, RETIRO DE TAPA Y BROCAL SIN RECUPACION ACARREO DEL MATERIAL AL LUGAR DE ACOPIO PARA SU CARGA Y ACARREO FUERA DE LA OBRA.	PZA	3	$1,164.57	$3,493.71
8	CARGA MECANICA Y ACARREO DE MATERIAL PRODUCTO DE EXCAVACION Y DEMOLICION EN CAMION DE VOLTEO AL 1er. KM, VOLUMEN MEDIDO COMPACTO.	M3	157.45	$33.49	$5,273.00
9	ACARREO DE MATERIAL PRODUCTO DE EXCAVACION Y/O DEMOLICION EN CAMION DE VOLTEO A KILOMETROS SUBSECUENTES, AL TIRADERO OFICIAL AUTORIZADO MAS CERCANO AUTORIZADO POR LA SUPERVISION, VOLUMEN MEDIDO COMPACTO.	M3-KM	4723.58	$11.85	$55,974.42
				Totales por Partida	**$97,074.03**
	PARTIDA: **EXCAVACIONES, ACARREOS Y TERRACERIAS**				
10	EXCAVACION EN CORTE CON MAQUINA HASTA UNA PROFUNDIDAD DE 75 CM, EN MATERIAL TIPO II, INCLUYE: AFLOJE Y EXTRACCION DE MATERIAL, ACARREOS AL LUGAR DE ACOPIO PARA SU CARGA Y ACARREO FUERA DE LA OBRA, VOLUMEN MEDIDO COMPACTO.	M3	773.25	$23.06	$17,831.15

Obra: **PAVIMENTO HIDRÁULICO, CALLE INÉS MARISCAL. T-01**

Ubicación: **TRAMO: ENTRE CALLE ENRIQUE MONTOYA Y CALLE FRANCISCO ROSTRO, LOS NEGRITOS Com.**

Contratista: **GRUPO CONSTRUCTOR MED CER, S.A. DE C.V. (201)**

No.	Concepto	Unidad	Cantidad	Precio Unitario	Importe Total
	GRUPO: **PAVIMENTO HIDRAULICO**				
	PARTIDA: **EXCAVACIONES, ACARREOS Y TERRACERIAS**				
11	COMPACTACION DE TERRENO NATURAL AL 90% DE SU P.V.S.M EN SU COMPACTACION., INCLUYE ESCARIFICADO, TENDIDO, HOMOGENIZADO, HUMEDECIDO OPTIMO NIVELADO Y COMPACTADO EN CAPAS DE 20 CM, CALIDAD Limite liquido máximo 50%, Valor de Soporte California (CBR) mínimo 15%, Expansión máxima 5%, Grado de Compactación minimo 90% ± 2, Y TODO LO NECESARIO PARA SU CORRECTA EJECUCION,	M2	257.75	$19.92	$5,134.38
12	FORMACION Y COMPACTACION DE SUB-RRASANTE, CON EL USO DE EQUIPO MAYOR, HASTA ALCANZAR EL 100% AASHTO MODIFICADA. EN CAPAS DE 20 CM MAXIMO, INCLUYE: SUMINISTRO DE MATERIAL DE BANCO QUE CUMPLA CON LA NORMA, HUMEDAD OPTIMA Y TODO LO NECESARIO PARA SU CORRECTA COLOCACION, EL MATERIAL DEBERA CUMPLIR CON UN C.B.R. DEL 60% PARA LO CUAL EL CONTRATISTA DEBERA PROPONER UN BANCO DE MATERIAL Y UN FRENTE, DEBERA PRESENTAR EL ESTUDIO DE CALIDAD QUE AVALE EL CUMPLIMIENTO AL 100 % DE LA NORMA Y DEMAS CARACTERISTICAS SOLICITADAS, P.U.O.T.	M3	206.2	$328.49	$67,734.64
13	FORMACION Y COMPACTACION DE SUB-BASE PARA MAS DE UN MILLON DE EJES EQUIVALENTES, CON EL USO DE EQUIPO MAYOR, HASTA ALCANZAR EL 100% AASHTO MODIFICADA. EN CAPAS DE 20 CM MAXIMO, INCLUYE: SUMINISTRO DE MATERIAL DE BANCO QUE CUMPLA CON LA NORMA, HUMEDAD OPTIMA Y TODO LO NECESARIO PARA SU CORRECTA COLOCACION, EL MATERIAL DEBERA CUMPLIR CON UN C.B.R. DEL 60% PARA LO CUAL EL CONTRATISTA DEBERA PROPONER UN BANCO DE MATERIAL Y UN FRENTE, DEBERA PRESENTAR EL ESTUDIO DE CALIDAD QUE AVALE EL CUMPLIMIENTO AL 100 % DE LA NORMA N-CMT-4-02-001. Y DEMAS CARACTERISTICAS SOLICITADAS, P.U.O.T.	M3	206.2	$308.87	$63,688.99
14	FORMACION Y COMPACTACION DE BASE HIDRAULICA PARA MAS DE UN MILLON DE EJES EQUIVALENTES DE 20 CMS. DE ESPESOR, PARA CARPETA DE CONCRETO HIDRAULICO, CON MATERIAL 100% TRITURADO (SOLAMENTE) 1 1/2" A FINOS QUE CUMPLA CON LA NORMA COMPACTADA AL 100 % DE PRUEBA AASHTO. COMBINANDO COMPACTADOR DE RODILLO EN BAJA Y MUERTO Y LLANTEO CON EQUIPO PESADO (CAMION DE VOLTEO CARGADO AL MAXIMO), INCLUYE HOMOGENEIZADO, TENDIDO, COMPACTADO, E INCORPORACION DE AGUA HASTA ALCANZAR LA HUMEDAD OPTIMA Y NIVELACIONES,	M3	206.2	$630.74	$130,058.59
15	CARGA MECANICA Y ACARREO DE MATERIAL PRODUCTO DE EXCAVACION Y DEMOLICION EN CAMION DE VOLTEO AL 1er. KM, VOLUMEN MEDIDO COMPACTO.	M3	618.6	$33.49	$20,716.91
16	ACARREO DE MATERIAL PRODUCTO DE EXCAVACION Y/O DEMOLICION EN CAMION DE VOLTEO A KILOMETROS SUBSECUENTES, AL TIRADERO OFICIAL AUTORIZADO MAS CERCANO AUTORIZADO POR LA SUPERVISION, VOLUMEN MEDIDO COMPACTO.	M3-KM	18558	$11.85	$219,912.30
			Totales por Partida		**$525,076.96**

Obra: **PAVIMENTO HIDRÁULICO, CALLE INÉS MARISCAL. T-01**

Ubicación: **TRAMO: ENTRE CALLE ENRIQUE MONTOYA Y CALLE FRANCISCO ROSTRO, LOS NEGRITOS Com.**

Contratista: **GRUPO CONSTRUCTOR MED CER, S.A. DE C.V. (201)**

No.	Concepto	Unidad	Cantidad	Precio Unitario	Importe Total
	GRUPO: **PAVIMENTO HIDRAULICO**				
	PARTIDA: **PAVIMENTO**				
17	CONSTRUCCION DE PAVIMENTO HIDRAULICO A BASE DE CONCRETO PREMEZCLADO MR=38 KG/CM2 TMA 1 1/2" GRAVA TRITURADA, REVENIMIENTO DE 6 A 8 CM FRAGUADO NORMAL DE 15 CM DE ESPESOR MODULADO EN LOSAS DE 3.5 MTS. (ANCHO) X 3.5 MTS (LARGO) COMO MAXIMO, CON CORTES EN LAS LOSAS DE 1/3 DEL ESPESOR DE LA LOSA (5 CM) Y SELLADO CON COLA DE RATA Y MATERIAL ELASTOMERICO Y TIRA PREFORMADA (FOAMTECH DE 1/2X15) EN JUNTAS Y CORTES LONGITUDINALES Y TRANSVERSALES, ASI COMO EL APROCHE CON GUARNICION Y DENTELLON. INCLUYE: CIMBRADO, COLADO, VIBRADO CON INMERSION Y REGLA VIBRATORIA, DESCIMBRADO, REGLEADO FINAL, ACABADO CEPILLO DE ALUMINIO Y CON DOBLADOR, CALAFATEO, CURADO CON MEMBRANA BASE AGUA Y TODO LO NECESARIO PARA SU CORRECTA COLOCACION, P.U.O.T.	M2	1108.36377	$573.49	$635,635.54
18	SUMINISTRO Y COLOCACION DE RELLENO PARA JUNTAS DE EXPANSION A BASE DE ESPUMA DE POLIETILENO DE CELDAS CERRADAS (FOAMTECH) DE 1/2" DE ESPESOR Y 20 CM DE ALTURA DE ACUERDO AL DISEÑO ANEXO EN PLANOS, INCLUYE: MATERIAL, SELLADOR AUTONIVELANTE,MANO DE OBRA, CORTES, AJUSTES, DESPERDICIOS, ACARREO, FLETES DENTRO Y FUERA DE LA OBRA DE ACUERDO A ESPECIFICACIONES DE CONTROL DE CALIDAD (LA FICHA TECNICA DEL FABRICANTE DEBERA CUMPLIR CON LAS ESPECIFICACIONES DE LA NORMA)	ML	310	$131.93	$40,898.30
				Totales por Partida	**$676,533.84**
	PARTIDA: **DENTELLONES DE CONCRETO**				
19	EXCAVACION A MANO EN MATERIAL TIPO B DE 0.00 A 2.00 M DE PROFUNDIDAD, INCLUYE: TRASPALEO VERTICAL, AFINE DE TALUDES CONSERVACION DE LA EXCAVACION Y ACARREO DE MATERIAL AL LUGAR DE ACOPIO PARA SU POSTERIOR CARGA Y ACARREO FUERA DE LA OBRA.	M3	5.05	$232.91	$1,176.20
20	COMPACTACION DE TERRENO NATURAL AL 90% DE SU P.V.S.M EN SU COMPACTACION., INCLUYE ESCARIFICADO, TENDIDO, HOMOGENIZADO, HUMEDECIDO OPTIMO NIVELADO Y COMPACTADO EN CAPAS DE 20 CM, CALIDAD Limite liquido máximo 50%, Valor de Soporte California (CBR) mínimo 15%, Expansión máxima 5%, Grado de Compactación minimo 90% ± 2, Y TODO LO NECESARIO PARA SU CORRECTA EJECUCION,	M2	12.62	$19.92	$251.39
21	RELLENO COMPACTADO AL 90% CON MATERIAL DE BANCO EN CAPAS DE 20 CM UTILIZANDO BAILARINA. INCLUYE: SUMINISTRO DE TEPETATE (MATERIAL DE BANCO) EN LA OBRA, ABUNDAMIENTO, ACARREOS DENTRO DE LA OBRA, CRIBADO, RETIRO DE MATERIAL, MANO DE OBRA Y EQUIPO, LIMPIEZAS, TRABAJO TERMINADO.	M3	6.31	$341.50	$2,154.86
22	CARGA MECANICA Y ACARREO DE MATERIAL PRODUCTO DE EXCAVACION Y DEMOLICION EN CAMION DE VOLTEO AL 1er. KM, VOLUMEN MEDIDO COMPACTO.	M3	5.05	$33.49	$169.13
23	ACARREO DE MATERIAL PRODUCTO DE EXCAVACION Y/O DEMOLICION EN CAMION DE VOLTEO A KILOMETROS SUBSECUENTES, AL TIRADERO OFICIAL AUTORIZADO MAS CERCANO AUTORIZADO POR LA SUPERVISION, VOLUMEN MEDIDO COMPACTO.	M3-KM	151.44	$11.85	$1,794.56

Obra: **PAVIMENTO HIDRÁULICO, CALLE INÉS MARISCAL. T-01**

Ubicación: **TRAMO: ENTRE CALLE ENRIQUE MONTOYA Y CALLE FRANCISCO ROSTRO, LOS NEGRITOS Com.**

Contratista: **GRUPO CONSTRUCTOR MED CER, S.A. DE C.V. (201)**

No.	Concepto	Unidad	Cantidad	Precio Unitario	Importe Total
	GRUPO: **PAVIMENTO HIDRAULICO**				
	PARTIDA: **DENTELLONES DE CONCRETO**				
24	CONSTRUCCION DE DENTELLON RECTO Y/O CURVO 20-20X40 CM DE SECCION, CON CONCRETO PREMEZCLADO MR=38 KGF/CM2, TMA 1 1/2", R.N. REVENIMIENTO NORMAL DE 10+-2 CM, GRAVA TRITURADA, ACABADO CON DOBLADOR Y PULIDO. INCLUYE: TRAZO, NIVELACION, CIMBRADO, COLADO, VIBRADO, DESCIMBRADO, JUNTA A BASE DE ESPUMA DE POLIETILENO DE CELDAS CERRADAS DE 1/2" EN JUNTAS FRIAS LONGITUDINALES NO MAYOR A 30 MTS CORTE TRANSVERSAL CON CORTADORA A 1/3 DE SU ESPESOR MAXIMO @ 3 MTS, RELLENO PREFORMADOY SELLADOR AUTONIVELANTE ASI COMO DE AISLAMIENTO CON OTRO ELEMENTO, Y CURADO CON MEMBRANA QUIMICA APLICADA CON ASPERSOR Y LIMPIEZA, REMATE CON PAVIMENTO EXISTENTE DEL MISMO MATERIAL Y TIPO, TRABAJO TERMINADO P.U.O.T.	ML	63.1	$327.87	$20,688.60
			Totales por Partida		**$26,234.74**
	PARTIDA: **GUARNICIONES**				
25	EXCAVACION A MANO EN MATERIAL TIPO B DE 0.00 A 2.00 M DE PROFUNDIDAD, INCLUYE: TRASPALEO VERTICAL, AFINE DE TALUDES CONSERVACION DE LA EXCAVACION Y ACARREO DE MATERIAL AL LUGAR DE ACOPIO PARA SU POSTERIOR CARGA Y ACARREO FUERA DE LA OBRA.	M3	3.26	$232.91	$759.29
26	COMPACTACION DE TERRENO NATURAL AL 90% DE SU P.V.S.M EN SU COMPACTACION., INCLUYE ESCARIFICADO, TENDIDO, HOMOGENIZADO, HUMEDECIDO OPTIMO NIVELADO Y COMPACTADO EN CAPAS DE 20 CM, CALIDAD Limite liquido máximo 50%, Valor de Soporte California (CBR) mínimo 15%, Expansión máxima 5%, Grado de Compactación minimo 90% ± 2, Y TODO LO NECESARIO PARA SU CORRECTA EJECUCION.	M2	21.72	$19.92	$432.66
27	CONSTRUCCION DE GUARNICION RECTA Y/O CURVA TRAPEZOIDAL 15-20X40 CM DE SECCION CON CONCRETO PREMEZCLADO MR=38 KGF/CM2, R.N.REVENIMIENTO DE 8 A 10 CM, T.M.A. 3/4", GRAVA TRITURADA, ACABADO PULIDO EN PARTE DE SUPERIOR Y DOBLADOR EN ARISTAS, INCLUYE: COMPACTADO DE PLANTILLA, CIMBRADO, COLADO, VIBRADO, ACABADO, DESCIMBRADO, ALINEADO, NIVELADO, Y CURADO EN SU PARTE SUPERIOR CON MEMBRANA BASE AGUA A RAZON DE 1 LTO/M2, JUNTA DE AISLAMIENTO LONGITUDINAL AL COMBINAR CON OTRO ELEMENTO Y TRANSVERSAL @ 30 MT MAXIMO, SELLADO CON SELLADOR AUTONIVELANTE LONGITUDINAL, TRABAJO TERMINADO, .P.U.O.T.	ML	54.3	$284.31	$15,438.03
28	RELLENO COMPACTADO AL 90% CON MATERIAL DE BANCO EN CAPAS DE 20 CM UTILIZANDO BAILARINA. INCLUYE: SUMINISTRO DE TEPETATE (MATERIAL DE BANCO) EN LA OBRA, ABUNDAMIENTO, ACARREOS DENTRO DE LA OBRA, CRIBADO, RETIRO DE MATERIAL, MANO DE OBRA Y EQUIPO, LIMPIEZAS, TRABAJO TERMINADO.	M3	1.63	$341.50	$556.64
29	CARGA MECANICA Y ACARREO DE MATERIAL PRODUCTO DE EXCAVACION Y DEMOLICION EN CAMION DE VOLTEO AL 1er. KM, VOLUMEN MEDIDO COMPACTO.	M3	1.63	$33.49	$54.59
30	ACARREO DE MATERIAL PRODUCTO DE EXCAVACION Y/O DEMOLICION EN CAMION DE VOLTEO A KILOMETROS SUBSECUENTES, AL TIRADERO OFICIAL AUTORIZADO MAS CERCANO AUTORIZADO POR LA SUPERVISION, VOLUMEN MEDIDO COMPACTO.	M3-KM	48.87	$11.85	$579.11
			Totales por Partida		**$17,820.33**

Obra: **PAVIMENTO HIDRÁULICO, CALLE INÉS MARISCAL. T-01**

Ubicación: **TRAMO: ENTRE CALLE ENRIQUE MONTOYA Y CALLE FRANCISCO ROSTRO, LOS NEGRITOS Com.**

Contratista: **GRUPO CONSTRUCTOR MED CER, S.A. DE C.V. (201)**

GRUPO: **PAVIMENTO HIDRAULICO**

PARTIDA: **BANQUETA Y RAMPA**

No.	Concepto	Unidad	Cantidad	Precio Unitario	Importe Total
31	EXCAVACION A MAQUINA Y/O A MANO EN MATERIAL TIPO II, EN SECO O PRESENCIA DE AGUA, INCLUYE. CORTE DE RAIZ DE CUALQUIER TAMAÑO Y GROSOR, HASTA UNA PROFUNDIDAD DE 40 CM DESPUES DE DESMONTE, DESPALME Y/O DEMOLICION DE SUPERFICIE O ELEMENTO ESTRUCTURAL O DE ACABADO, PROTECCION DE AREAS ADYACENTES, SIN DAÑAR AREAS ALEDAÑAS, CARGA Y ACARREO A TIRADERO OFICIAL, CONSERVACION DE LA MISMA, TRABAJO TERMINADO, LIMPIEZAS.	M3	12.5	$78.42	$980.25
32	CARGA MECANICA Y ACARREO DE MATERIAL PRODUCTO DE EXCAVACION Y DEMOLICION EN CAMION DE VOLTEO AL 1er. KM, VOLUMEN MEDIDO COMPACTO.	M3	12.5	$33.49	$418.63
33	ACARREO DE MATERIAL PRODUCTO DE EXCAVACION Y/O DEMOLICION EN CAMION DE VOLTEO A KILOMETROS SUBSECUENTES, AL TIRADERO OFICIAL AUTORIZADO MAS CERCANO AUTORIZADO POR LA SUPERVISION, VOLUMEN MEDIDO COMPACTO.	M3-KM	374.88	$11.85	$4,442.33
34	COMPACTACION POR MEDIOS MECANICOS DEL TERRENO NATURAL AL 95% DE SU PVSM EN UN ESPESOR DE 20 cm. INCLUYE: ESCARIFICACION, MANIOBRAS, HUMEDECIDO, SELECCION DE MATERIAL, ACARREOS DENTRO DE LA OBRA, MEDIDO COMPACTO, LIMPIEZAS, Y TODO LO NECESARIO PARA SU CORRECTA APLICACION, TRABAJO TERMINADO.	M2	62.48	$17.82	$1,113.39
35	RELLENO COMPACTADO AL 90% CON MATERIAL DE BANCO EN CAPAS DE 20 CM UTILIZANDO BAILARINA. INCLUYE: SUMINISTRO DE TEPETATE (MATERIAL DE BANCO) EN LA OBRA, ABUNDAMIENTO, ACARREOS DENTRO DE LA OBRA, CRIBADO, RETIRO DE MATERIAL, MANO DE OBRA Y EQUIPO, LIMPIEZAS, TRABAJO TERMINADO.	M3	12.5	$341.50	$4,268.75
36	SUMINISTRO Y COLOCACION DE HULE DE POLIETILENO CAL 600 PARA IMPERMEABILIZAR, INCLUYE: SUMINISTRO DEL MATERIAL A LA OBRA, MANO DE OBRA Y TODO LO NECESARIO PARA SU CORRECTA COLOCACION, P.U.O.T. SEGUN FICHA TECNICA FT-206	M2	62.48	$19.34	$1,208.36
37	CONSTRUCCION DE BANQUETA DE 10 CM DE ESPESOR A BASE DE CONCRETO PREMEZCLADO F'C=150 KG/CM2, T.M.A. 3/4", R.N. GRAVA TRITURADA, REVENIMIENTI DE 10+-2 CM, ACABADO RAYADO FINO CON BROCHA DE PELO, JUNTAS FRIAS CON DOBLADOR DE 2" SECCION DE LOSAS COMO INDIQUE PROYECTO, INCLUYE: JUNTA A BASE DE ESPUMA DE POLIETILENO DE CELDAS CERRADAS DE 1/2" EN JUNTAS FRIAS LONGITUDINALES CON MUROS Y TRANSVERSALES DEL ELEMENTO, ASI COMO SU UNION CON ELEMENTOS VIEJOS O CAMBIO DE ELEMENTO, CIMBRADO, COLADO, DESCIMBRADO, CORTES CON CORTADORA DE DISCO, SELLADO DE CORTES CON SELLADOR AUTONIVELANTE Y TIRA DE RELLENO PREFORMADA NO ADHERENTE DE 1/8" (EN TODAS LAS JUNTAS DE CONTRACCCION Y CONSTRUCCION TRANSVERSALES), CURADO CON MEMBRANA QUIMICA APLICADA CON ASPERSOR, TRABAJO TERMINADO	M2	59.28	$399.50	$23,682.36
38	CONSTRUCCION DE rampa para personas con discapacidad DE 10 CM DE ESPESOR A BASE DE CONCRETO PREMEZCLADO F'C=150 KG/CM2, T.M.A. 3/4", R.N. GRAVA TRITURADA, REVENIMIENTI DE 10+-2 CM, ACABADO RAYADO tipo lavadero, JUNTAS FRIAS CON DOBLADOR DE 2" SECCION DE LOSAS COMO INDIQUE PROYECTO, INCLUYE: JUNTA A BASE DE ESPUMA DE POLIETILENO DE CELDAS CERRADAS DE 1/2" EN JUNTAS FRIAS LONGITUDINALES CON MUROS Y TRANSVERSALES DEL ELEMENTO, ASI COMO SU UNION CON ELEMENTOS VIEJOS O CAMBIO DE ELEMENTO, CIMBRADO, COLADO, DESCIMBRADO, CORTES CON CORTADORA DE DISCO, SELLADO DE CORTES CON SELLADOR AUTONIVELANTE Y TIRA DE RELLENO PREFORMADA NO ADHERENTE DE 1/8" (EN TODAS LAS JUNTAS DE CONTRACCCION Y CONSTRUCCION TRANSVERSALES), CURADO CON MEMBRANA QUIMICA APLICADA CON ASPERSOR, TRABAJO TERMINADO	M2	3.2	$410.25	$1,312.80
				Totales por Partida	**$37,426.87**

Obra: **PAVIMENTO HIDRÁULICO, CALLE INÉS MARISCAL. T-01**

Ubicación: **TRAMO: ENTRE CALLE ENRIQUE MONTOYA Y CALLE FRANCISCO ROSTRO, LOS NEGRITOS Com.**

Contratista: **GRUPO CONSTRUCTOR MED CER, S.A. DE C.V. (201)**

No.	Concepto	Unidad	Cantidad	Precio Unitario	Importe Total
	GRUPO: **PAVIMENTO HIDRAULICO**				
	PARTIDA: **OBRA COMPLEMENTARIA**				
39	CONSTRUCCION DE CAJA DE VALVULAS TIPO 2 SECCION 1.28 X 1.18 MTS Y PROFUNDIDAD DE HASTA 1.27 MTS (MEDIDAS EXTERIORES) PARA ALOJAR UNA VALVULA DE HASTA 6" (150 mm) INCLUYE: TRAZO, EXCAVACION, NIVELACIONES Y RELLENOS CON MATERIAL DE BANCO COMPACTACIÓN AL 95% DE SU P.V.S.M., HUMEDAD OPTIMA, PLANTILLA DE 10 CM. DE ESPESOR DE CONCRETO F'C= 150 KG/CM2. T.M.A. 19mm. HECHO EN OBRA, LOSA DE CONCRETO F'C= 200 KG/CM2 DE 10 CM. DE ESPESOR, ARMADA CON VS. NO.3 @ 30 CM. EN AMBOS SENTIDOS (PISO), MUROS DE TABICON PESADO DE CONCRETO 10X14X28 CM. ASENTADO EN 14 CM, JUNTEADO CON MORTERO CEMENTO-ARENA 1:3, APLANADO INTERIOR CON MORTERO CEMENTO ARENA 1:3 DE 2.00 CM. DE ESPESOR ACABADO PULIDO, CASTILLOS SECCION 14 X 14 CM ARMADO CON 4 VRS DE 3/8" Y ESTRIBOS DEL No.2 A CADA 15 CM CONCRETO F'C= 200 KG/CM2 T.M.A. 19MM, UN MARCO Y CONTRAMARCO SENCILLO DE CANAL DE FO. FO. DE 4"(100mm) X 1.10 MTS. CON TAPA DE FO.FO DE 50X50 CM TIPO PESADO(130 KG) LOSA TAPA DE CONCRETO ARMADO MR-45KG/CM2 T.MA 3/4", RR A 3 DIAS, DE 20 CM DE ESPESOR ARMADA CON VRS DE 3/8" A CADA 10 CM, DOBLE PARRILLA, CERRAMIENTO DE CONCRETO ARMADO DE 14 X 20 CM CONCRETO F'C= 200 KG/CM2 T.M.A. 3/4" ARMADO CON 4 VRS DEL N.o. 3 , ESTRIBOS DEL No. 2 ACADA 15 CM. SILLETA y/o DADO DE CONCRETO HECHO EN OBRA PARA APOYO DE VALVULA, CARGAS Y ACARREOS DENTRO DE LA OBRA, CIMBRADO, DESCIMBRADO, COLADO, VIBRADO, CURADO, LIMPIEZAS Y TODO LO NECESARIO PARA LA CORRECTA EJECUCION, TRABAJO TERMINADO (VER DETALLE CAJA VALVULAS TIPO 2)	PZA	3	$17,818.12	$53,454.36
40	CONSTRUCCION DE POZO DE VISITA CON CAIDA LIBRE DE HASTA 2.50 M DE PROFUNDIDAD, CON PLANTILLA DE MAMPOSTERIA DE PIEDRA, ASENTADA CON MORTERO CEM-ARENA 1:3, CON MURO DE TABIQUE ROJO RECOCIDO DE 28 CM DE ESPESOR JUNTADO CON MORTERO CEMENTO-ARENA 1:3 NO MAYOR DE 1.5 CM DE ESPESOR EN FORMA CUATRAPEADA, APLANADO INTERIOR DE MORTERO CEM-ARENA 1:3 DE UN ESPESOR MINIMO DE 1 CM, ACABADO PULIDO FINO DE CEMENTO, LAS INTERSECCIONES DE LAS TUBERIAS SE EMBOQUILLARAN, LOS ESCALONES DE VARILLA DEL No. 5 (5/8"), LA HECHURA DE LA MEDIA CAÑA DE CONCRETO HECHO EN OBRA F'C=150 KG/CM, DONDE SE AHOGARA TUBERIA CORTADA A MEDIA CAÑA Y SE PULIRA CUIDADOSAMENTE, INCLUYE: EXCAVACION, RELLENO, MATERIALES, ACARREOS, FLETES, MANO DE OBRA, MANIOBRAS LOCALES SUMINISTRO Y COLOCACION DE TAPA Y BROCAL DE FOFO E INSTALACION Y EQUIPO NECESARIO PARA SU CORRECTA CONSTRUCCION Y FUNCIONAMIENTO.	PZA	3	$18,941.30	$56,823.90
41	CONSTRUCCION DE LOSA DE DIAMANTE DE CONCRETO MR= 45 , T.M.A. DE 3/4" (19MM), GRAVA TRITURADA, REVENIMIENTO DE 8+-2.5CM CM, FRAGUADO RAPIDOA A 3 DIAS, DE 25 CM DE ESPESOR, EN POZO DE VISITA, Y 1.50 M POR LADO, INCLUYE: SUMINISTRO DE MATERIALES, ESPUMA DE POLIURETANO DE ALTA DENSIDAD EN TODO EL PERIMETRO EXTERIOR DE 1/2" ASI COMO DE LAS JUNTAS DIAGONALES PARA FORMAR 4 PARTES, BROCAL Y TAPA DE Fo. Fo. TIPO PESADO, (165 KG), CIMBRADO, COLADO, VIBRADO, DESCIMBRADO, CURADO CON MEMBRANA QUIMICA BASE AGUA, APLANADO FINO EN RECEPCION DE BROCAL, CORTES CON CORTADORA DE DISCO DE 5 CM ENTRE JUNTAS DIAGONALES FORMADO 8 PIEZAS Y SELLADO DE JUNTAS Y CORTES CON MATERIAL PREFORMADO Y SELLADOR AUTONIVELANTE, MANO DE OBRA, ACARREOS DE MATERIAL DENTRO Y FUERA DE LA OBRA, TRABAJO TERMINADO. P.U.O.T.	PZA	3	$9,389.24	$28,167.72

Obra: **PAVIMENTO HIDRÁULICO, CALLE INÉS MARISCAL. T-01**

Ubicación: **TRAMO: ENTRE CALLE ENRIQUE MONTOYA Y CALLE FRANCISCO ROSTRO, LOS NEGRITOS Com.**

Contratista: **GRUPO CONSTRUCTOR MED CER, S.A. DE C.V. (201)**

No.	Concepto	Unidad	Cantidad	Precio Unitario	Importe Total
	GRUPO: **PAVIMENTO HIDRAULICO**				
	PARTIDA: **OBRA COMPLEMENTARIA**				
42	LIMPIEZA Y DESASOLVE DE POZOS DE VISITA Y LINEAS DE ALCANTARILLADO EXISTENTE CON CAMION TIPO VACTOR. INCLUYE: RESANE INTERIOR DEL POZO Y REMTE DE POZO CO TUBO CON SELLADOR, FESTER Y MORTERO 1:3, MANO DE OBRA, SUMINISTRO DE AGUA EN PIPA, HERRAMIENTAS Y EQUIPO PARA SU CORRECTA EJECUCION, LIMPIEZAS, RENTA DE CAMION VACTOR HASTA LA CORRECTA LIMPIEZA DE LAS LINEAS EXISTENTES DE POZO A POZO, ASI COMO EL TRASLADO DE LOS DESECHOS HASTA TIRADERO AUTORIZADO MEDIDO POZO A POZO.	LOTE	4	$6,739.70	$26,958.80
			Totales por Partida		**$165,404.78**
	PARTIDA: **LIMPIEZAS**				
43	LIMPIEZA GENERAL DE LA OBRA, INCLUYE: BARRIDO, CARGA, ACARREOS Y RETIRO DE ESCOMBROS FUERA DE LA OBRA, TRABAJO TERMINADO.	M2	1031	$9.33	$9,619.23
			Totales por Partida		**$9,619.23**
			Totales por Grupo		**$1,555,190.77**

Obra: **PAVIMENTO HIDRÁULICO, CALLE INÉS MARISCAL. T-01**

Ubicación: **TRAMO: ENTRE CALLE ENRIQUE MONTOYA Y CALLE FRANCISCO ROSTRO, LOS NEGRITOS Com.**

Contratista: **GRUPO CONSTRUCTOR MED CER, S.A. DE C.V. (201)**

No.	Concepto	Unidad	Cantidad	Precio Unitario	Importe Total
	GRUPO: **SEÑALIZACION**				
	PARTIDA: **SEÑALIZACION HORIZONTAL**				
44	SUMINISTRO Y APLICACIÓN DE PINTURA EPOXICA BASE SOLVENTE COLOR AZUL (PANTONE 294) EN RAMPAS PARA PERSONAS CON DISCAPACIDAD CUALQUIER SECCIÓN SEGÚN PLANOS. INCLUYE: TRAZO, MANO DE OBRA, LIMPIEZA PREVIA DE SUPERFICIE, EQUIPO NECESARIO PARA SU EJECUCIÓN, Y TODO LO NECESARIO PARA SU CORRECTA EJECUCIÓN, TRABAJO TERMINADO.	M2	11.2	$105.92	$1,186.30
45	SUMINISTRO Y APLICACIÓN DE LOGOTIPO A (SILLA DE RUEDAS) EN PINTURA EPOXICA BASE SOLVENTE COLOR BLANCO EN RAMPAS PARA PERSONAS CON DISCAPACIDAD TAMAÑO Y DISEÑO SEGÚN PLANOS. INCLUYE: TRAZO, ENMASCARILLADO, PLANTILLA, MANO DE OBRA, LIMPIEZA PREVIA DE SUPERFICIE, EQUIPO NECESARIO PARA SU EJECUCIÓN, Y TODO LO NECESARIO PARA SU CORRECTA EJECUCIÓN, TRABAJO TERMINADO.	PZA	8	$317.10	$2,536.80
46	SUMINISTRO Y APLICACIÓN DE PINTURA BASE SOLVENTE PARA MARCAS EN GUARNICIONES CLASIFICACION M-12.1, M12.2 APLICADA SOBRE GUARNICIONES Y DENTELLONES DE CUALQUIER COLOR, SEGÚN SE REQUIERA Y SEGÚN NORMA S.C.T. SECADO AL TACTO EN 5 MIN Y AL DURO EN 30 MIN CON MICRO ESFERA , DESARROLLO DE 35 CM. INCLUYE: MATERIALES Y ESPECIFICACIONES QUE CUMPLAN CON LA NORMATIVA N-CMT-5-01-001/05, N-PRY-CAR-10-01-002/13 APLICADAS AL DIA DE HOY, TRAZO, MANO DE OBRA, LIMPIEZA PREVIA DE SUPERFICIE, EQUIPO NECESARIO PARA SU EJECUCIÓN, Y TODO LO NECESARIO PARA SU CORRECTA EJECUCIÓN, TRABAJO TERMINADO.	ML	272	$50.96	$13,861.12
47	SUMINISTRO Y APLICACIÓN DE PINTURA TERMOPLASTICA ALQUIDALICA DE 120 MILESIMAS DE PULGADA " EN RAYA SEPARADORA CLASIFICACIÓN M - 1.6, CONTINUA DOBLE, PARA DELIMITAR CARRILES EN CONTRASENTIDO DE FRENTE EN PISO, 0.10 MTS DE ANCHO, CON UNA SEPARACIÓN IGUAL AL ANCHO DE LA LINEA A BASE DE PINTURA PARA TRAFICO COLOR AMARILLO O BLANCO CON MICRO ESFERA SEGÚN NORMA SCT, INCLUYE: MATERIALES Y ESPECIFICACIONES QUE CUMPLAN CON LA NORMATIVA N-CMT-5-01-001/05, N-PRY-CAR-10-01-002/13 APLICADAS AL DIA DE HOY, MATERIAL APLICADO EN SU ESTADO DE FUSION A UNA TEMPERATURA MINIMA DE 204 C, LA SUPERFICIE DE CONCRETO O ASFALTO NO DEBE PRESENTAR UNA TEMPERATURA MENOR A LOS 10 C, ;TIEMPO DE SECADO EN RANGOS DE TEMPERATURA DE 10 C DEL SUSTRATO 2 MINUTOS, Y NO MAS DE 10 MINUTOS CUANDO EL SUSTRATO OSCILA ALREDEDOR DE 54C, TRAZO, ENMASCARILLADO, MANO DE OBRA, LIMPIEZA PREVIA Y FINAL DE SUPERFICIE, EQUIPO NECESARIO PARA SU EJECUCIÓN, Y TODO LO NECESARIO PARA SU CORRECTA EJECUCIÓN, TRABAJO TERMINADO.	ML	96.5	$42.63	$4,113.80
48	SUMINISTRO Y APLICACIÓN DE PINTURA TERMOPLASTICA ALQUIDALICA DE 120 MILESIMAS DE " (in) EN LETRAS Y NUMEROS CLASIFICACIÓN M - 11.1 "LETRAS Y NUMEROS" EN VIALIDADES PARA VELOCIDAD MENOR A 60KM POR HORA SEGUN MANUAL DE SEÑALIZACIÓN VIAL Y DISPOSITIVOS DE SEGURIDAD SICT (SCT), (VER PLANO DE SEÑALAMIENTOS) EN COLOR BLANCO, REFLEJANTE CON MICRO ESFERA DE VIDRIO EN PROPORCIÓN SEGÚN NORMA SCT DE (VER DETALLES EN PLANOS) INCLUYE: MATERIALES Y ESPECIFICACIONES QUE CUMPLAN CON LA NORMATIVA N-CMT-5-01-001/13, N-PRY-CAR-10-01-002/13 APLICADAS AL DIA DE HOY, MATERIAL APLICADO EN SU ESTADO DE FUSION A UNA TEMPERATURA MINIMA DE 204 C, LA SUPERFICIE DE CONCRETO O ASFALTO NO DEBE PRESENTAR UNA TEMPERATURA MENOR A LOS 10 C, ;TIEMPO DE SECADO EN RANGOS DE TEMPERATURA DE 10 C DEL SUSTRATO 2 MINUTOS, Y NO MAS DE 10 MINUTOS CUANDO EL SUSTRATO OSCILA ALREDEDOR DE 54C, TRAZO, ENMASCARILLADO, MANO DE OBRA, LIMPIEZA PREVIA Y FINAL DE SUPERFICIE, EQUIPO NECESARIO PARA SU EJECUCIÓN, Y TODO LO NECESARIO PARA SU CORRECTA EJECUCIÓN, TRABAJO TERMINADO.	PZA	32	$321.22	$10,279.04

Obra: **PAVIMENTO HIDRÁULICO, CALLE INÉS MARISCAL. T-01**

Ubicación: **TRAMO: ENTRE CALLE ENRIQUE MONTOYA Y CALLE FRANCISCO ROSTRO, LOS NEGRITOS Com.**

Contratista: **GRUPO CONSTRUCTOR MED CER, S.A. DE C.V. (201)**

No.	Concepto	Unidad	Cantidad	Precio Unitario	Importe Total
	GRUPO: **SEÑALIZACION**				
	PARTIDA: **SEÑALIZACION HORIZONTAL**				
49	SUMINISTRO Y APLICACIÓN DE PINTURA TERMOPLASTICA ALQUIDALICA DE 120 MILESIMAS DE " (in) EN RAYA PARA CRUCE PEATONAL CLASIFICACIÓN M - 7.1, PARA INDICAR " CRUCE PEATONAL EN VIAS PRIMARIAS", COLOR AMARILLO, REFLEJANTE CON MICRO ESFERA DE VIDRIO EN PROPORCIÓN SEGÚN MANUAL DE SEÑALIZACIÓN VIAL Y DISPOSITIVOS DE SEGURIDAD SICT (S.C.T). DE 0.40 MTS DE ANCHO Y 3.5 MTS. DE LONGITUD POR EL ANCHO DE LA VIALIDAD, CON UNA SEPARACIÓN DE 0.40 MTS. ENTRE ELLAS, INCLUYE: MATERIALES Y ESPECIFICACIONES QUE CUMPLAN CON LA NORMATIVA N-CMT-5-01-001/13, N-PRY-CAR-10-01-002/13 APLICADAS AL DIA DE HOY, MATERIAL APLICADO EN SU ESTADO DE FUSION A UNA TEMPERATURA MINIMA DE 204 C, LA SUPERFICIE DE CONCRETO O ASFALTO NO DEBE PRESENTAR UNA TEMPERATURA MENOR A LOS 10 C, ;TIEMPO DE SECADO EN RANGOS DE TEMPERATURA DE 10 C DEL SUSTRATO 2 MINUTOS, Y NO MAS DE 10 MINUTOS CUANDO EL SUSTRATO OSCILA ALREDEDOR DE 54C, TRAZO, ENMASCARILLADO, MANO DE OBRA, LIMPIEZA PREVIA Y FINAL DE SUPERFICIE, EQUIPO NECESARIO PARA SU EJECUCIÓN, Y TODO LO NECESARIO PARA SU CORRECTA EJECUCIÓN, TRABAJO TERMINADO.	M2	66	$513.86	$33,914.76
50	SUMINISTRO Y APLICACIÓN DE PINTURA TERMOPLASTICA ALQUIDALICA DE 120 MILESIMAS DE " (in) EN FLECHAS CLASIFICACIÓN M - 11.1, "FLECHA SENCILLA" PARA INDICAR SENTIDO DE CIRCULACIÓN , EN VIALIDADES PARA VELOCIDAD MENOR A 60KM POR HORA DIMENSION NORMATIVA SEGUN MANUAL DE SEÑALIZACIÓN VIAL Y DISPOSITIVOS DE SEGURIDAD SICT (SCT) Y/O (VER PLANO DE SEÑALAMIENTOS), COLOR BLANCO, REFLEJANTE CON MICRO ESFERA DE VIDRIO EN PROPORCIÓN SEGÚN NORMA SCT, INCLUYE: MATERIALES Y ESPECIFICACIONES QUE CUMPLAN CON LA NORMATIVA N-CMT-5-01-001/13, N-PRY-CAR-10-01-002/13 APLICADAS AL DIA DE HOY, MATERIAL APLICADO EN SU ESTADO DE FUSION A UNA TEMPERATURA MINIMA DE 204 C, LA SUPERFICIE DE CONCRETO O ASFALTO NO DEBE PRESENTAR UNA TEMPERATURA MENOR A LOS 10 C, ;TIEMPO DE SECADO EN RANGOS DE TEMPERATURA DE 10 C DEL SUSTRATO 2 MINUTOS, Y NO MAS DE 10 MINUTOS CUANDO EL SUSTRATO OSCILA ALREDEDOR DE 54C, TRAZO, ENMASCARILLADO, MANO DE OBRA, LIMPIEZA PREVIA Y FINAL DE SUPERFICIE, EQUIPO NECESARIO PARA SU EJECUCIÓN, Y TODO LO NECESARIO PARA SU CORRECTA EJECUCIÓN, TRABAJO TERMINADO.	PZA	8	$1,045.90	$8,367.20
51	SUMINISTRO Y COLOCACION DE VIALETA STANDARD (S-200) DE 10X10CM. COLOR: CUERPO AMARILLO Y REFLEJANTE AMARILLO 1 CARA MARCA SEA O SIMILAR EN CALIDAD Y ESPECIFICACIONES DE FICHA TECNICA, ANCLADO EN PAVIMENTO SISTEMA DE SUJECION DE ALTO AGARRE BASE CUÑAS CON AB PEGAMENTO EPOXICO 50/50 RESISTENTE A ALTA TEMPERATURA (VER PLANO DE DETALLES DE SEÑALAMIENTOS HORIZONTAL Y VERTICAL). INCLUYE: TRAZO, ALINEACION, ELEVACION CUALQUIER ALTURA, TRABAJO TERMINADO, LIMPIEZAS.	PZA	12	$48.95	$587.40
52	SUMINISTRO Y COLOCACION DE VIALETA SOLAR DE 10X10CM. COLOR: CUERPO ALUMINIO 3 LED DOS CARAS REFLEJANTES MARCA CREATIVAL VT-29 O SIMILAR EN CALIDAD Y ESPECIFICACIONES DE FICHA TECNICA, ANCLADO EN PAVIMENTO SISTEMA DE SUJECION DE ALTO AGARRE BASE CUÑAS CON AB PEGAMENTO EPOXICO 50/50 RESISTENTE A ALTA TEMPERATURA (VER PLANO DE DETALLES DE SEÑALAMIENTOS HORIZONTAL Y VERTICAL). INCLUYE: TRAZO, ALINEACION, ELEVACION CUALQUIER ALTURA, TRABAJO TERMINADO, LIMPIEZAS.	PZA	9	$684.99	$6,164.91
				Totales por Partida	**$81,011.31**
				Totales por Grupo	**$81,011.31**

Obra: **PAVIMENTO HIDRÁULICO, CALLE INÉS MARISCAL. T-01**

Ubicación: **TRAMO: ENTRE CALLE ENRIQUE MONTOYA Y CALLE FRANCISCO ROSTRO, LOS NEGRITOS Com.**

Contratista: **GRUPO CONSTRUCTOR MED CER, S.A. DE C.V. (201)**

No.	Concepto	Unidad	Cantidad	Precio Unitario	Importe Total
	GRUPO: **HIDRAULICO SANITARIO**				
	PARTIDA: **LINEA DE ALCANTARILLADO**				
53	TRAZO Y NIVELACION DE TERRENO CON APARATO TOPOGRAFICO, PARA LINEAS DE AGUA POTABLE Y ALCANTARILLADO, INCLUYE: EJES, BANCOS DE NIVEL, RENIVELACIONES, CORRECCION DE ARRASTRES Y NIVELES A PUNTOS OBLIGADOS (AUTORIZADOS POR LA SUPERVISION), ESTACAS, VARILLAS, MANO DE OBRA CALIFICADA, HERRAMIENTA NECESARIA, EQUIPO DE PRECISION CALIBRADO, (SE ENTREGARA A LA DEPENDENCIA PLANO DE PERFIL Y SECCIONES ORIGINAL Y FINAL CON PUNTOS X,Y,Z) TRABAJO TERMINADO.P.U.O.T.	ML	136.88	$12.53	$1,715.11
54	EXCAVACION A MAQUINA EN ZANJAS EN MATERIAL TIPO II DE 0.00 A 2.00 M DE PROFUNDIDAD, INCLUYE: AFLOJE Y EXTRACCION DEL MATERIAL, AFINE, TRASPALEO VERTICAL PARA SU EXTRACCION, CONSERVACION DE LA EXCAVACION, ACARREO HASTA EL LUGAR DE ACOPIO PARA SU CARGA Y ACARREO FUERA DE LA OBRA, SEÑALAMIENTOS, COLOCACION DE PASOS PEATONALES Y PROTECCION PERIMETRAL DE LA ZANJA.	M3	280	$78.42	$21,957.60
55	PLANTILLA Y ACOSTILLADO CON ARENA Y PISON DE MANO, INCLUYE: SUMINISTRO DE MATERIAL EN LA OBRA, ACARREO EN CARRETILLA, DESCARGA EN LA ZANJA, EXTENDIDO, NIVELADO Y APISONADO, APOYO SEMICIRCULAR PARA LA TUBERIA SE CONSTRUIRA INMEDIATAMENTE ANTES DE TENDER LA TUBERIA, DEBIENDO COLOCAR HILOS LONGITUDINALMENTE PARA VERIFICAR LA UNIFORMIDAD DE LA PLANTILLA.	M3	8.21	$683.83	$5,614.24
56	ACOSTILLADO CON MATERIAL DE PROD. DE EXCAVACION EN CAPAS DE 20 CMS. AL 85% DE SU P.V.M.S. CON EL USO DE BAILARINA, HOMOGENIZACION DEL MATERIAL, AGUA LA NECESARIA, EXTENDIDO Y COMPACTADO.	M3	16.43	$69.93	$1,148.95
57	RELLENO COMPACTADO AL 90% CON MATERIAL DE BANCO EN CAPAS DE 20 CM UTILIZANDO BAILARINA. INCLUYE: SUMINISTRO DE TEPETATE (MATERIAL DE BANCO) EN LA OBRA, ABUNDAMIENTO, ACARREOS DENTRO DE LA OBRA, CRIBADO, RETIRO DE MATERIAL, MANO DE OBRA Y EQUIPO, LIMPIEZAS, TRABAJO TERMINADO.	M3	164.26	$319.12	$52,418.65
58	RELLENO COMPACTADO AL 95% CON MATERIAL DE BANCO EN CAPAS DE 20 CM UTILIZANDO BAILARINA, INCLUYE: SELECCION DEL MATERIAL, ABUNDAMIENTO, ACARREOS DENTRO DE LA OBRA, CRIBADO, MANO DE OBRA Y EQUIPO, PRUEBA DE CONTROL DE CALIDAD.	M3	16.43	$328.93	$5,404.32
59	CARGA MECANICA Y ACARREO DE MATERIAL PRODUCTO DE EXCAVACION Y DEMOLICION EN CAMION DE VOLTEO AL 1er. KM, VOLUMEN MEDIDO COMPACTO.	M3	188.89	$33.49	$6,325.93
60	ACARREO DE MATERIAL PRODUCTO DE EXCAVACION Y/O DEMOLICION EN CAMION DE VOLTEO A KILOMETROS SUBSECUENTES, AL TIRADERO OFICIAL AUTORIZADO MAS CERCANO AUTORIZADO POR LA SUPERVISION, VOLUMEN MEDIDO COMPACTO.	M3-KM	5666.83	$11.85	$67,151.93
61	SUMINISTRO DE TUBERIA DE PVC PARA ALCANTARILLADO SERIE 20 DE 10", CON JUNTA HERMETICA, INCLUYE: FLETES Y ACARREO HASTA EL SITIO DE SU COLOCACION, ALINEADO, MATERIAL, CUBIERTA DE PROTECCION, ESTIBADO, MANO DE OBRA.	ML	136.88	$356.79	$48,837.42
62	SUMINISTRO DE TUBERIA DE PVC PARA ALCANTARILLADO SERIE 20 DE 8", CON JUNTA HERMETICA, CON COPLES, TEES, CODOS, EXTREMIDADES, INCLUYE: FLETES Y ACARREO HASTA EL SITIO DE SU COLOCACION, ALINEADO, MATERIAL, MANO DE OBRA.	ML	12.4	$228.93	$2,838.73
63	INSTALACION DE TUBERIA DE PVC PARA ALCANTARILLADO SERIE 20 DE 10", CON JUNTA HERMETICA. INCLUYE: FLETES Y ACARREO HASTA EL SITIO DE SU COLOCACION, MATERIALES DE LIMPIEZA, LUBRICACION, NIVELADO, MATERIAL Y MANO DE OBRA.	ML	136.88	$142.87	$19,556.05

Obra: **PAVIMENTO HIDRÁULICO, CALLE INÉS MARISCAL. T-01**

Ubicación: **TRAMO: ENTRE CALLE ENRIQUE MONTOYA Y CALLE FRANCISCO ROSTRO, LOS NEGRITOS Com.**

Contratista: **GRUPO CONSTRUCTOR MED CER, S.A. DE C.V. (201)**

No.	Concepto	Unidad	Cantidad	Precio Unitario	Importe Total
	GRUPO: **HIDRAULICO SANITARIO**				
	PARTIDA: **LINEA DE ALCANTARILLADO**				
64	INSTALACION DE TUBERIA DE PVC PARA ALCANTARILLADO SERIE 20 DE 8", CON JUNTA HERMETICA. INCLUYE: FLETES Y ACARREO HASTA EL SITIO DE SU COLOCACION, MATERIALES DE LIMPIEZA, LUBRICACION, PEGAMENTO DE ALTA HUMEDAD, NIVELADO, MATERIAL Y MANO DE OBRA.	ML	12.4	$123.51	$1,531.52
65	CONEXION DE TUBERIA DE PVC DE 8-16" A POZO DE VISITA, INCLUYE: DEMOLICION DE MURO DE POZO, CONEXION Y NIVELACION DEL TUBO, RESANE DEL MURO, APLANADO INTERIOR ACABADO PULIDO, LIGAS, LIMPIEZA Y RETIRO DE ESCOMBRO A 20 M.	PZA	6	$757.15	$4,542.90
			Totales por Partida		**$239,043.35**
	PARTIDA: **DESCARGAS DOMICILIARIAS**				
66	EXCAVACION A MAQUINA EN ZANJAS EN MATERIAL TIPO II DE 0.00 A 2.00 M DE PROFUNDIDAD, INCLUYE: AFLOJE Y EXTRACCION DEL MATERIAL, AFINE, TRASPALEO VERTICAL PARA SU EXTRACCION, CONSERVACION DE LA EXCAVACION, ACARREO HASTA EL LUGAR DE ACOPIO PARA SU CARGA Y ACARREO FUERA DE LA OBRA, SEÑALAMIENTOS, COLOCACION DE PASOS PEATONALES Y PROTECCION PERIMETRAL DE LA ZANJA.	M3	6.86	$78.42	$537.96
67	PLANTILLA Y ACOSTILLADO CON ARENA Y PISON DE MANO, INCLUYE: SUMINISTRO DE MATERIAL EN LA OBRA, ACARREO EN CARRETILLA, DESCARGA EN LA ZANJA, EXTENDIDO, NIVELADO Y APISONADO, APOYO SEMICIRCULAR PARA LA TUBERIA SE CONSTRUIRA INMEDIATAMENTE ANTES DE TENDER LA TUBERIA, DEBIENDO COLOCAR HILOS LONGITUDINALMENTE PARA VERIFICAR LA UNIFORMIDAD DE LA PLANTILLA.	M3	14	$683.83	$9,573.62
68	RELLENO COMPACTADO AL 90% CON MATERIAL DE BANCO EN CAPAS DE 20 CM UTILIZANDO BAILARINA. INCLUYE: SUMINISTRO DE TEPETATE (MATERIAL DE BANCO) EN LA OBRA, ABUNDAMIENTO, ACARREOS DENTRO DE LA OBRA, CRIBADO, RETIRO DE MATERIAL, MANO DE OBRA Y EQUIPO, LIMPIEZAS, TRABAJO TERMINADO.	M3	14	$319.12	$4,467.68
69	RELLENO COMPACTADO AL 95% CON MATERIAL DE BANCO EN CAPAS DE 20 CM UTILIZANDO BAILARINA, INCLUYE: SELECCION DEL MATERIAL, ABUNDAMIENTO, ACARREOS DENTRO DE LA OBRA, CRIBADO, MANO DE OBRA Y EQUIPO, PRUEBA DE CONTROL DE CALIDAD.	M3	14	$328.93	$4,605.02
70	CARGA MECANICA Y ACARREO DE MATERIAL PRODUCTO DE EXCAVACION Y DEMOLICION EN CAMION DE VOLTEO AL 1er. KM, VOLUMEN MEDIDO COMPACTO.	M3	14	$33.49	$468.86
71	ACARREO DE MATERIAL PRODUCTO DE EXCAVACION Y/O DEMOLICION EN CAMION DE VOLTEO A KILOMETROS SUBSECUENTES, AL TIRADERO OFICIAL AUTORIZADO MAS CERCANO AUTORIZADO POR LA SUPERVISION, VOLUMEN MEDIDO COMPACTO.	M3-KM	205.92	$11.85	$2,440.15
72	DESCARGA DOMICILIARIA NUEVA PARA REMPLAZO DE 6.00 M DE LONGITUD (NOMINAL), A BASE DE TUBO DE PVC ALCANTARILLADO SERIE 20 DE 6" DE DIAMETRO, INCLUYE: SILLETA DE 8" X 6", CODO DE 6" X 45°, CONEXION A REGISTRO NUEVO O EXISTENTE, ALINEACION, PRUEBAS DE ESCURRIMIENTO, SUMINISTROS, ACARREOS, TRABAJO TERMINADO.	PZA	11	$1,581.97	$17,401.67
73	DESCARGA DOMICILIARIA PARA USO FUTURO DE 6.00 M DE LONGITUD (NOMINAL), A BASE DE TUBO DE PVC ALCANTARILLADO SERIE 20 DE 6" DE DIAMETRO, INCLUYE: SILLETA DE 10" X 6", CODO DE 6" X 45°, TAPON HEMBRA, ALINEACION, INDICACION DE UBICACION CON VARILLA EN PREDIO, PRUEBAS DE ESCURRIMIENTO, SUMINISTROS, ACARREOS, TRABAJO TERMINADO.	PZA	11	$1,619.11	$17,810.21

Obra: **PAVIMENTO HIDRÁULICO, CALLE INÉS MARISCAL. T-01**

Ubicación: **TRAMO: ENTRE CALLE ENRIQUE MONTOYA Y CALLE FRANCISCO ROSTRO, LOS NEGRITOS Com.**

Contratista: **GRUPO CONSTRUCTOR MED CER, S.A. DE C.V. (201)**

No.	Concepto	Unidad	Cantidad	Precio Unitario	Importe Total
	GRUPO: **HIDRAULICO SANITARIO**				
	PARTIDA: **DESCARGAS DOMICILIARIAS**				
74	REGISTRO SANTARIO DE 0.40X0.60X0.80 M (MEDIDAS INTERIORES) DE TABIQUE ROJO RECOCIDO (14 CM DE ESPESOR) JUNTEADO CON MORTERO CEMENTO-ARENA 1:4 Y APLANADO DE 2.00 CM CON EL MISMO MORTERO, ACABADO PULIDO INTERIOR, PLANTILLA DE 7.00 CM DE ESPESOR DE CONCRETO F'C=150 KG/CM2, HECHO EN OBRA, TMA 19 MM. INCLUYE: MARCO Y CONTRAMARCO DE ANGULO DE 2" X 3/16" COLADA CON EL MISMO CONCRETO, PLOMEADO, ALINEADO, NIVELADO, ACARREOS DENTRO DE LA OBRA Y CONEXION A RED EXISTENTE, LIMPIEZAS.	PZA	11	$1,535.24	$16,887.64
			Totales por Partida		**$74,192.81**
	PARTIDA: **LINEA DE AGUA POTABLE**				
75	TRAZO Y NIVELACION DE TERRENO CON APARATO TOPOGRAFICO, PARA LINEAS DE AGUA POTABLE Y ALCANTARILLADO, INCLUYE: EJES, BANCOS DE NIVEL, RENIVELACIONES, CORRECCION DE ARRASTRES Y NIVELES A PUNTOS OBLIGADOS (AUTORIZADOS POR LA SUPERVISION), ESTACAS, VARILLAS, MANO DE OBRA CALIFICADA, HERRAMIENTA NECESARIA, EQUIPO DE PRECISION CALIBRADO, (SE ENTREGARA A LA DEPENDENCIA PLANO DE PERFIL Y SECCIONES ORIGINAL Y FINAL CON PUNTOS X,Y,Z) TRABAJO TERMINADO.P.U.O.T.	ML	136.9	$12.53	$1,715.36
76	EXCAVACION A MAQUINA EN ZANJAS EN MATERIAL TIPO II DE 0.00 A 2.00 M DE PROFUNDIDAD, INCLUYE: AFLOJE Y EXTRACCION DEL MATERIAL, AFINE, TRASPALEO VERTICAL PARA SU EXTRACCION, CONSERVACION DE LA EXCAVACION, ACARREO HASTA EL LUGAR DE ACOPIO PARA SU CARGA Y ACARREO FUERA DE LA OBRA, SEÑALAMIENTOS, COLOCACION DE PASOS PEATONALES Y PROTECCION PERIMETRAL DE LA ZANJA.	M3	82.14	$78.42	$6,441.42
77	BOMBEO DE ACHIQUE CON BOMBA DE 3" Y 8 H.P., OPERACION BOMBA Y EQUIPO COMPLEMENTARIO CON MANGUERA Y PICHANCHA.	HR	2	$160.76	$321.52
78	PLANTILLA Y ACOSTILLADO CON ARENA Y PISON DE MANO, INCLUYE: SUMINISTRO DE MATERIAL EN LA OBRA, ACARREO EN CARRETILLA, DESCARGA EN LA ZANJA, EXTENDIDO, NIVELADO Y APISONADO, APOYO SEMICIRCULAR PARA LA TUBERIA SE CONSTRUIRA INMEDIATAMENTE ANTES DE TENDER LA TUBERIA, DEBIENDO COLOCAR HILOS LONGITUDINALMENTE PARA VERIFICAR LA UNIFORMIDAD DE LA PLANTILLA.	M3	54	$683.83	$36,926.82
79	RELLENO COMPACTADO AL 90% CON MATERIAL DE BANCO EN CAPAS DE 20 CM UTILIZANDO BAILARINA. INCLUYE: SUMINISTRO DE TEPETATE (MATERIAL DE BANCO) EN LA OBRA, ABUNDAMIENTO, ACARREOS DENTRO DE LA OBRA, CRIBADO, RETIRO DE MATERIAL, MANO DE OBRA Y EQUIPO, LIMPIEZAS, TRABAJO TERMINADO.	M3	36.96	$319.12	$11,794.67
80	RELLENO COMPACTADO AL 95% CON MATERIAL DE BANCO EN CAPAS DE 20 CM UTILIZANDO BAILARINA, INCLUYE: SELECCION DEL MATERIAL, ABUNDAMIENTO, ACARREOS DENTRO DE LA OBRA, CRIBADO, MANO DE OBRA Y EQUIPO, PRUEBA DE CONTROL DE CALIDAD.	M3	16.43	$328.93	$5,404.32
81	CARGA MECANICA Y ACARREO DE MATERIAL PRODUCTO DE EXCAVACION Y DEMOLICION EN CAMION DE VOLTEO AL 1er. KM, VOLUMEN MEDIDO COMPACTO.	M3	53.39	$33.49	$1,788.03
82	ACARREO DE MATERIAL PRODUCTO DE EXCAVACION Y/O DEMOLICION EN CAMION DE VOLTEO A KILOMETROS SUBSECUENTES, AL TIRADERO OFICIAL AUTORIZADO MAS CERCANO AUTORIZADO POR LA SUPERVISION, VOLUMEN MEDIDO COMPACTO.	M3-KM	1601.73	$11.85	$18,980.5(

Obra: **PAVIMENTO HIDRÁULICO, CALLE INÉS MARISCAL. T-01**

Ubicación: **TRAMO: ENTRE CALLE ENRIQUE MONTOYA Y CALLE FRANCISCO ROSTRO, LOS NEGRITOS Com.**

Contratista: **GRUPO CONSTRUCTOR MED CER, S.A. DE C.V. (201)**

No.	Concepto	Unidad	Cantidad	Precio Unitario	Importe Total
	GRUPO: **HIDRAULICO SANITARIO**				
	PARTIDA: **LINEA DE AGUA POTABLE**				
83	SUMINISTRO DE TUBERIA DE PVC HIDRAULICO RD-26 DE 3" CON CAMPANA INTEGRAL, COPLES, CODOS, TEES, INCLUYE: ACARREOS HASTA EL SITIO DE SU COLOCACION, BAJADO, ALINEADO, INSTALACION DE COPLES, ANILLO Y PRUEBA HIDROSTATICA.	ML	124.5	$74.77	$9,308.86
84	INSTALACION DE TUBERIA DE PVC HIDRAULICO RD-26 DE 3" CON CAMPANA INTEGRAL. INCLUYE: ACARREO HASTA EL SITIO DE SU COLOCACION, BAJADO, ALINEAMIENTO, INSTALACION DE COPLES, ANILLO Y PRUEBA HIDROSTATICA.	ML	124.5	$30.33	$3,776.09
85	SUMINISTRO Y COLOCACION DE TEE DE 3" DE PVC, INCLUYE: SUMINISTROS, MANO DE OBRA, NIVELACION, MATERIALES, PRUEBA HIDROSTATICA JUNTO CON LA TUBERIA, ACARREOS LOCALES, HERRAMIENTA NECESARIA Y TODO LO NECESARIO PARA SU CORRECTA EJECUCION, LIMPIEZA, TRABAJO TERMINADO.	PZA	2	$161.74	$323.48
86	SUMINISTRO Y COLOCACION DE EXTREMIDAD ESPIGA/CAMPANA DE 3", INCLUYE: SUMINISTROS, MANO DE OBRA, NIVELACION, MATERIALES, PRUEBA HIDROSTATICA JUNTO CON LA TUBERIA, ACARREOS LOCALES, HERRAMIENTA NECESARIA Y TODO LO NECESARIO PARA SU CORRECTA EJECUCION, LIMPIEZA, TRABAJO TERMINADO.	PZA	1	$202.08	$202.08
87	SUMINISTRO Y COLOCACION DE TAPON CAMPANA DE PVC HIDRAULICO DE 3". INCLUYE: SUMINISTRO, MANO DE OBRA, NIVELACION, PRUEBA JUNTO CON LA TUBERIA, ACARREOS LOCALES, TRABAJO TERMINADO.	PZA	2	$115.49	$230.98
88	CONSTRUCCION DE ATRAQUE PARA CRUCERO Y TUBERIAS HECHO A BASE DE CONCRETO HECHO EN OBRA F´c=150 KG/CM2, TMA 3/4" GRAVA TRITURADA SEGUN NORMAS OFICIALES PARA UN DIAMETRO DE HASTA 14", INCLUYE: MATERIALES DE BANCO, MANO DEOBRA, CARGA Y ACARREOS LOCALES, ELEVACIONES, MANIOBRAS LOCALES, TRABAJO TERMINADO, LIMPIEZAS	M3	0.1	$3,356.35	$335.63
89	SUMINISTRO E INSTALACION DE JUNTA GIBAULT DE 3" DE DIAMETRO, INCLUYE: SUMINISTROS, MANO DE OBRA, TORNILLOS, NIVELACION, PRUEBA JUNTO CON LA TUBERIA, ACARREOS LOCALES, TRABAJO TERMINADO.	PZA	1	$311.18	$311.18
				Totales por Partida	**$97,860.95**
	PARTIDA: **TOMAS DOMICILIARIAS**				
90	EXCAVACION A MAQUINA EN ZANJAS EN MATERIAL TIPO II DE 0.00 A 2.00 M DE PROFUNDIDAD, INCLUYE: AFLOJE Y EXTRACCION DEL MATERIAL, AFINE, TRASPALEO VERTICAL PARA SU EXTRACCION, CONSERVACION DE LA EXCAVACION, ACARREO HASTA EL LUGAR DE ACOPIO PARA SU CARGA Y ACARREO FUERA DE LA OBRA, SEÑALAMIENTOS, COLOCACION DE PASOS PEATONALES Y PROTECCION PERIMETRAL DE LA ZANJA.	M3	0.48	$78.42	$37.64
91	RELLENO COMPACTADO AL 90% CON MATERIAL DE BANCO EN CAPAS DE 20 CM UTILIZANDO BAILARINA. INCLUYE: SUMINISTRO DE TEPETATE (MATERIAL DE BANCO) EN LA OBRA, ABUNDAMIENTO, ACARREOS DENTRO DE LA OBRA, CRIBADO, RETIRO DE MATERIAL, MANO DE OBRA Y EQUIPO, LIMPIEZAS, TRABAJO TERMINADO.	M3	0.29	$319.12	$92.55
92	RELLENO COMPACTADO AL 95% CON MATERIAL DE BANCO EN CAPAS DE 20 CM UTILIZANDO BAILARINA, INCLUYE: SELECCION DEL MATERIAL, ABUNDAMIENTO, ACARREOS DENTRO DE LA OBRA, CRIBADO, MANO DE OBRA Y EQUIPO, PRUEBA DE CONTROL DE CALIDAD.	M3	0.19	$328.93	$62.50
93	CARGA MECANICA Y ACARREO DE MATERIAL PRODUCTO DE EXCAVACION Y DEMOLICION EN CAMION DE VOLTEO AL 1er. KM, VOLUMEN MEDIDO COMPACTO.	M3	0.48	$33.49	$16.07

Obra: **PAVIMENTO HIDRÁULICO, CALLE INÉS MARISCAL. T-01**

Ubicación: **TRAMO: ENTRE CALLE ENRIQUE MONTOYA Y CALLE FRANCISCO ROSTRO, LOS NEGRITOS Com.**

Contratista: **GRUPO CONSTRUCTOR MED CER, S.A. DE C.V. (201)**

No.	Concepto	Unidad	Cantidad	Precio Unitario	Importe Total
	GRUPO: **HIDRAULICO SANITARIO**				
	PARTIDA: **TOMAS DOMICILIARIAS**				
94	ACARREO DE MATERIAL PRODUCTO DE EXCAVACION Y/O DEMOLICION EN CAMION DE VOLTEO A KILOMETROS SUBSECUENTES, AL TIRADERO OFICIAL AUTORIZADO MAS CERCANO AUTORIZADO POR LA SUPERVISION, VOLUMEN MEDIDO COMPACTO.	M3-KM	14.4	$11.85	$170.64
95	CONSTRUCCION DE TOMA DOMICILIARIA DE REMPLAZO DE 6 A 8 MTS DE LONGITUD (NOMINAL) A BASE DE TUBO KITEC DE 5/8" AZUL, CONECTORES PHILMAC MACHO Y HEMBRA, ABRAZADERAS SIN FIN, CONEXION A TUBO GALVANIZADO O EXISTENTE, ABRAZADERA DE PVC DE 3" X 1/2", INCLUYE: ENCAMISADO CON POLIDUCTO ELECTRICO DE 1 1/2", PRUEBAS, SUMINISTROS, ACARREOS LOCALES, MANO DE OBRA, TRABAJO TERMINADO.	PZA	10	$1,312.33	$13,123.30
96	CONSTRUCCION DE TOMA DOMICILIARIA DE REMPLAZO DE 2 A 3 MTS DE LONGITUD (NOMINAL) A BASE DE TUBO KITEC DE 5/8" AZUL, CONECTORES PHILMAC MACHO Y HEMBRA, ABRAZADERAS SIN FIN, CONEXION A TUBO GALVANIZADO O EXISTENTE, ABRAZADERA DE PVC DE 3" X 1/2", INCLUYE: ENCAMISADO CON POLIDUCTO ELECTRICO DE 1 1/2", PRUEBAS, SUMINISTROS, ACARREOS LOCALES, MANO DE OBRA, TRABAJO TERMINADO.	PZA	10	$881.89	$8,818.90

Totales por Partida		**$22,321.60**
Totales por Grupo		**$433,418.71**
Totales Presup.		**$2,069,620.80**
Anticipo	+	**$982,662.48**
Amortizac. Ant.	-	**$982,662.48**
SubTotal. Ant.	=	**$2,069,620.80**
IVA	+	**$331,139.33**
Total	=	**$2,400,760.13**

H. AYUNTAMIENTO CONSTITUCIONAL DEL MUNICIPIO DE AGUASCALIENTES 2021-2024

PRESUPUESTO MODIFICADO

Aguascalientes

Obra: **PAVIMENTO HIDRÁULICO, CALLE INÉS MARISCAL. T-01**

Ubicación: **TRAMO: ENTRE CALLE ENRIQUE MONTOYA Y CALLE FRANCISCO ROSTRO, LOS NEGRITOS Com.**

Contratista: **GRUPO CONSTRUCTOR MED CER, S.A. DE C.V. (201)**

Grupo	Partida		Importe
PAVIMENTO HIDRAULICO			
	PRELIMINARES Y DEMOLICIONES		$97,074.03
	EXCAVACIONES, ACARREOS Y TERRACERIAS		$525,076.96
	PAVIMENTO		$676,533.84
	DENTELLONES DE CONCRETO		$26,234.74
	GUARNICIONES		$17,820.33
	BANQUETA Y RAMPA		$37,426.87
	OBRA COMPLEMENTARIA		$165,404.78
	LIMPIEZAS		$9,619.23
		Subtotal por Grupo	**$1,555,190.77**
SEÑALIZACION			
	SEÑALIZACION HORIZONTAL		$81,011.33
		Subtotal por Grupo	**$81,011.33**
HIDRAULICO SANITARIO			
	LINEA DE ALCANTARILLADO		$239,043.35
	DESCARGAS DOMICILIARIAS		$74,192.81
	LINEA DE AGUA POTABLE		$97,860.95
	TOMAS DOMICILIARIAS		$22,321.60
		Subtotal por Grupo	**$433,418.71**

Totales Presup.		**$2,069,620.80**
Anticipo	**+**	**$982,662.48**
Amortizac. Ant.	**-**	**$982,662.48**
SubTotal. Ant.	**=**	**$2,069,620.80**
IVA	**+**	**$331,139.33**
Total	**=**	**$2,400,760.13**

H. AYUNTAMIENTO CONSTITUCIONAL DEL MUNICIPIO DE AGUASCALIENTES 2021-2024

H. AYUNTAMIENTO DE AGUASCALIENTES
SECRETARÍA DE OBRAS PÚBLICAS
DIRECCIÓN DE SUPERVISIÓN DE OBRA


Aguascalientes
LA CIUDAD DE TU VIDA

MEMORIA FOTOGRAFICA


OBRA:	PAVIMENTO HIDRÁULICO, CALLE INÉS MARISCAL. T-01, TRAMO: ENTRE CALLE ENRIQUE MONTOYA Y CALLE FRANCISCO ROSTRO, LOS NEGRITOS Com.					
NO. DE CONTRATO:	OM-0115-2022		CONTRATISTA:	GRUPO CONSTRUCTOR MED CER, S.A. DE C.V.		

INICIO.



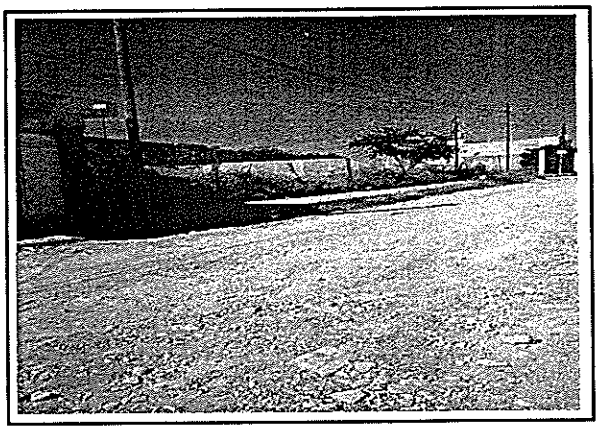



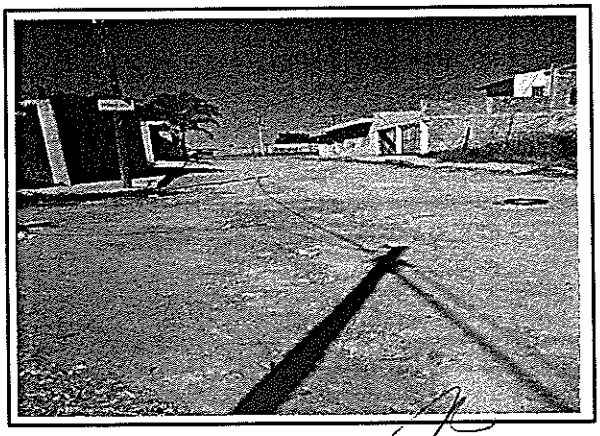

ING. IVAN ALEJANDRO RUIZ ESPARZA SOLIS
SUPERVISOR DE OBRA.

H. AYUNTAMIENTO CONSTITUCIONAL
DEL MUNICIPIO DE AGUASCALIENTES
2021-2024

H. AYUNTAMIENTO DE AGUASCALIENTES
SECRETARÍA DE OBRAS PÚBLICAS
DIRECCIÓN DE SUPERVISIÓN DE OBRA

Aguascalientes
LA CIUDAD DE TU VIDA


MEMORIA FOTOGRAFICA


OBRA:	PAVIMENTO HIDRÁULICO, CALLE INÉS MARISCAL. T-01, TRAMO: ENTRE CALLE ENRIQUE MONTOYA Y CALLE FRANCISCO ROSTRO, LOS NEGRITOS Com.					
NO. DE CONTRATO:	DM-0115-2022		CONTRATISTA:	GRUPO CONSTRUCTOR MED CER, S.A. DE C.V.		

PROCESO





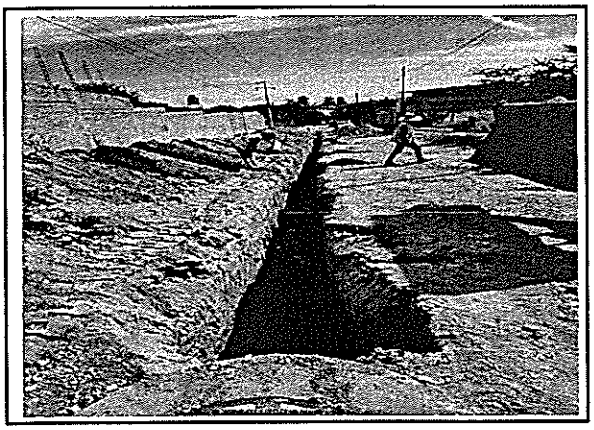

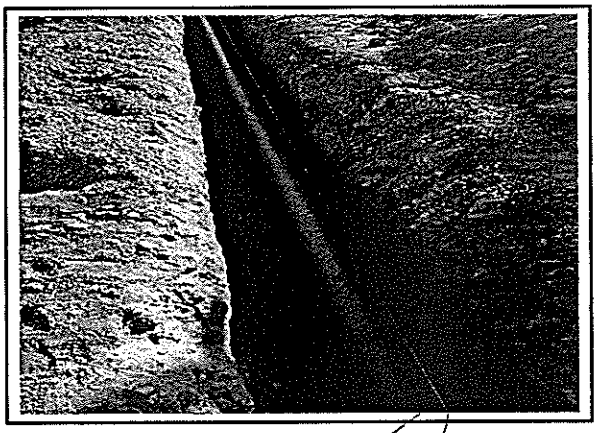

ING. IVAN ALEJANDRO RUIZ ESPARZA SOLIS
SUPERVISOR DE OBRA.

H. AYUNTAMIENTO DE AGUASCALIENTES
SECRETARÍA DE OBRAS PÚBLICAS
DIRECCIÓN DE SUPERVISIÓN DE OBRA

H. AYUNTAMIENTO CONSTITUCIONAL DEL MUNICIPIO DE AGUASCALIENTES 2021-2024


Aguascalientes
LA CIUDAD DE TU VIDA


MEMORIA FOTOGRAFICA

OBRA:	PAVIMENTO HIDRÁULICO, CALLE INÉS MARISCAL. T-01, TRAMO: ENTRE CALLE ENRIQUE MONTOYA Y CALLE FRANCISCO ROSTRO, LOS NEGRITOS Com.					
NO. DE CONTRATO:	DM-0115-2022		CONTRATISTA:	GRUPO CONSTRUCTOR MED CER, S.A. DE C.V.		

TERMINO



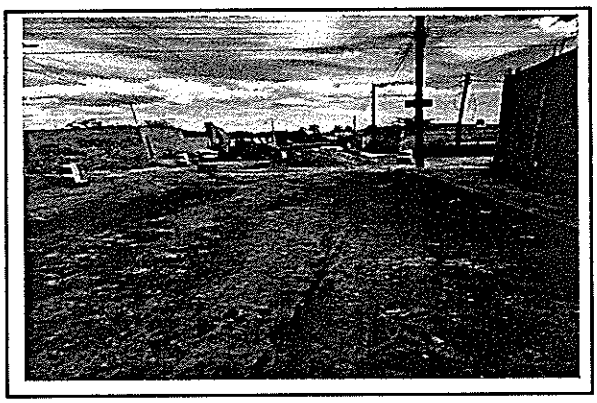

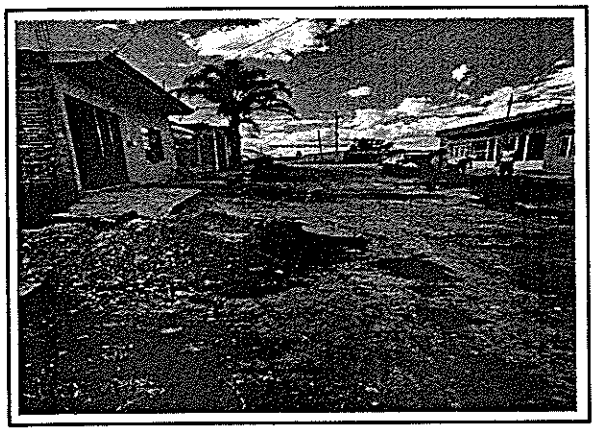



ING. IVAN ALEJANDRO RUIZ ESPARZA SOLIS
SUPERVISOR DE OBRA.

MODIFICADO

SECRETARÍA DE OBRAS PÚBLICAS

DIRECCIÓN DE SUPERVISIÓN DE OBRA

EJERCICIO 2022

N° DE CONTRATO: DM-0115-2022


NOMBRE DE LA OBRA: PAVIMENTO HIDRÁULICO, CALLE INÉS MARISCAL. T-01, TRAMO: ENTRE CALLE ENRIQUE MONTOYA Y CALLE FRANCISCO ROSTRO, LOS NEGRITOS Com.


MONTO MODIFICADO FINAL: $ 2,400,760.13

VOLUMEN	UNIDAD	COMPONENTE DE LA OBRA	MONTO
1108.36	M2	CONSTRUCCION DE PAVIMENTO HIDRAULICO A BASE DE CONCRETO PREMEZCLADO MR=38 KG/CM2 TMA 1 1/2" GRAVA TRITURADA, REVENIMIENTO DE 6 A 8 CM FRAGUADO NORMAL DE 15 CM DE ESPESOR MODULADO EN LOSAS DE 3.5 MTS. (ANCHO) X 3.5 MTS (LARGO) COMO MAXIMO, CON CORTES EN LAS LOSAS DE 1/3 DEL ESPESOR DE LA LOSA (5 CM) Y SELLADO CON COLA DE RATA Y	$ 1,555,190.77
66.00	M2	SUMINISTRO Y APLICACIÓN DE PINTURA TERMOPLASTICA ALQUIDALICA DE 120 MILESIMAS DE " (in) EN RAYA PARA CRUCE PEATONAL CLASIFICACIÓN M - 7.1, PARA INDICAR " CRUCE PEATONAL EN VIAS PRIMARIAS", COLOR AMARILLO, REFLEJANTE CON MICRO ESFERA DE VIDRIO EN PROPORCIÓN SEGÚN MANUAL DE SEÑALIZACIÓN VIAL Y DISPOSITIVOS DE SEGURIDAD SICT (6 C.T). DE 0.12 MTS DE ANCHO Y	$ 81,011.33
5666.83	M3-KM	ACARREO DE MATERIAL PRODUCTO DE EXCAVACION Y/O DEMOLICION EN CAMION DE VOLTEO A KILOMETROS SUBSECUENTES, AL TIRADERO OFICIAL AUTORIZADO MAS CERCANO AUTORIZADO POR LA SUPERVISION, VOLUMEN MEDIDO COMPACTO.	$ 433,418.71

TOTAL PRESUP.	$	2,069,620.80
IVA	$	331,139.33
TOTAL	$	2,400,760.13

NOMBRE DEL SUPERVISOR: ING. IVAN ALEJANDRO RUIZ ESPARZA SOLIS

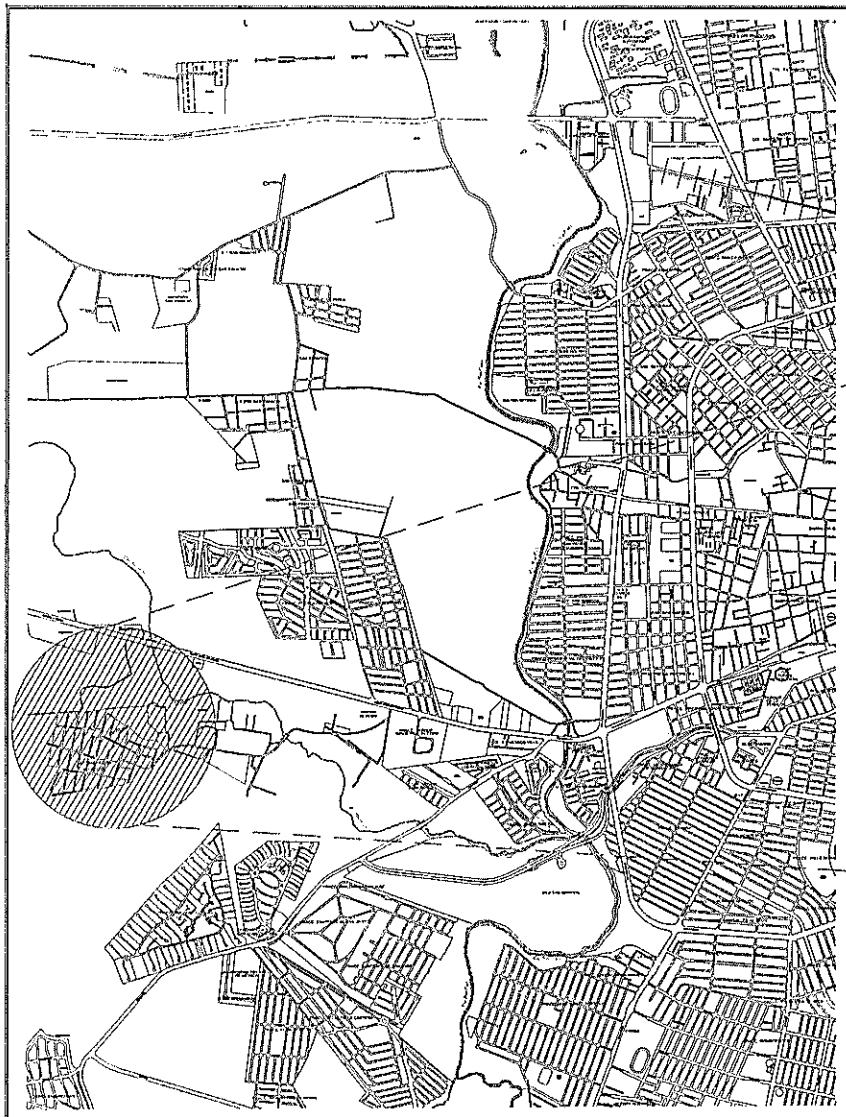


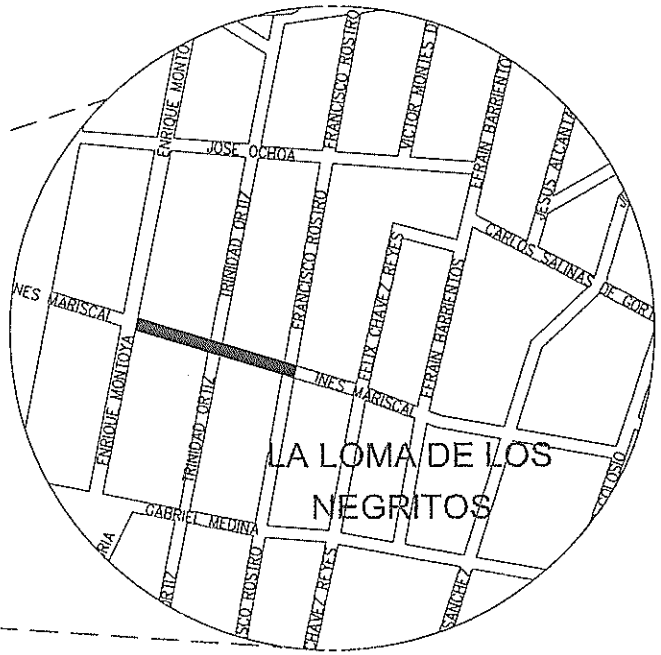

CROQUIS DE LOCALIZACIÓN

SIN ESCALA — CALLE INES MARISCAL

LOCALIZACIÓN:

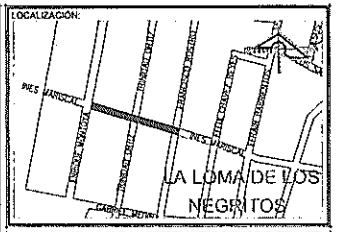

SIMBOLOGÍA

La Dirección de Planeación y Proyectos solo autoriza el proyecto ejecutivo, no es responsable de la correcta ejecución de la obra. Este documento no tiene validez si no presenta las firmas de los responsables para su autorización, así como los sellos respectivos.

PRESIDENTE MUNICIPAL
M.P.P. Leonardo Montañez Castro
SECRETARIO DE OBRAS PÚLICAS DEL MUNICIPIO DE AGUASCALIENTES
Ing. Miguel Ángel Huizar Botello

REV	FECHA	OBSERVACIONES

V.o. Bo. DE LA DEPENDENCIA

RESP. DE PROY. EXTERNO		LOGO EXTERNO
CED. PROFESIONAL		
PROYECTÓ	REVISÓ	AUTORIZÓ

Dirección de Planeación y Proyectos de Obra — Secretaría de Obras Públicas

PROYECTISTA	COORDINADOR
BLANCA ESTHER AGUAYO PEREZ	ARQ. ALEJANDRO JAIME LEAL
JEFE DE DEP.	DIRECTOR
ARQ. J. JESÚS PALAFOX GONZÁLEZ	M. en ARQ. JOSÉ LUIS JIMÉNEZ GARCÍA

PROYECTO
CONSTRUCCIÓN DE PAVIMENTO HIDRAULICO CALLE INES MARISCAL
UBICACIÓN
TRAMO ENTRE CALLE ENRIQUE MONTOYA Y CALLE FRANCISCO ROSTRO, LA LOMA DE LOS NEGRITOS
CONTENIDO
CROQUIS DE LOCALIZACIÓN

CLAVE	No. PLANO
LOC 01	01
FECHA	ESCALA
OCTUBRE 2022	INDICADA
ACOTACIÓN	No. EXP.
METROS	E-000-22


Aguascalientes
LA CIUDAD DE TU VIDA

CONSTRUCCION DE GUARNICION RECTA Y/O CURVA TRAPEZOIDAL DE 15x20x40 CM DE SECCION CON CONCRETO PREMEZCLADO F'c= 150 KG/CM2, REVENIMIENTO DE 8 A 10 CM, T.M.A. 1 1/2" 38 MM, GRAVA TRITURADA, ACABADO PULIDO EN PARTE DE SUPERIOR Y DOBLADOR EN ARISTAS SUPERIORES, INCLUYE: COMPACTADO DE PLANTILLA, CIMBRADO, COLADO, ACABADO, DESCIMBRADO, ALINEADO, NIVELADO, DESCIMBRADO Y CURADO EN SU PARTE SUPERIOR CON MEMBRANA BASE AGUA A RAZON D E 1 L T O / M 2

CONSTRUCCION DE BANQUETA DE 10 CM DE ESPESOR A BASE DE CONCRETO HECHO EN OBRA F'C=150 KG/CM2, T.M.A. 3/4", R.N. GRAVA TRITURADA, REVENIMIENTI DE 10+-2 CM, ACABADO RAYADO FINO CON BROCHA DE PELO, JUNTAS FRIAS CON DOBLADOR DE 7" SECCION DE LOSAS COMO INDIQUE PROYECTO, INCLUYE: JUNTA A BASE DE ESPUMA DE POLIETILENO DE CELDAS CERRADAS DE 1/2" EN JUNTAS FRIAS LONGITUDINALES CON MUROS Y TRANSVERSALES DEL ELEMENTO, ASI COMO SU UNION CON ELEMENTOS VIEJOS O CAMBIO DE ELEMENTO, CIMBRADO, COLADO, DESCIMBRADO, CORTES CON CORTADORA DE DISCO, SELLADO DE CORTES CON SELLADOR AUTONIVELANTE Y TIRA DE RELLENO PREFORMADA NO ADHERENTE DE 1/8" (EN TODAS LAS JUNTAS DE CONTRACCCION Y CONSTRUCCION TRANSVERSALES), CURADO CON MEMBRANA QUIMICA APLICADA CON ASPERSOR, TRABAJO TERMINADO.


PARAMENTO.

ARROYO VEHICULAR

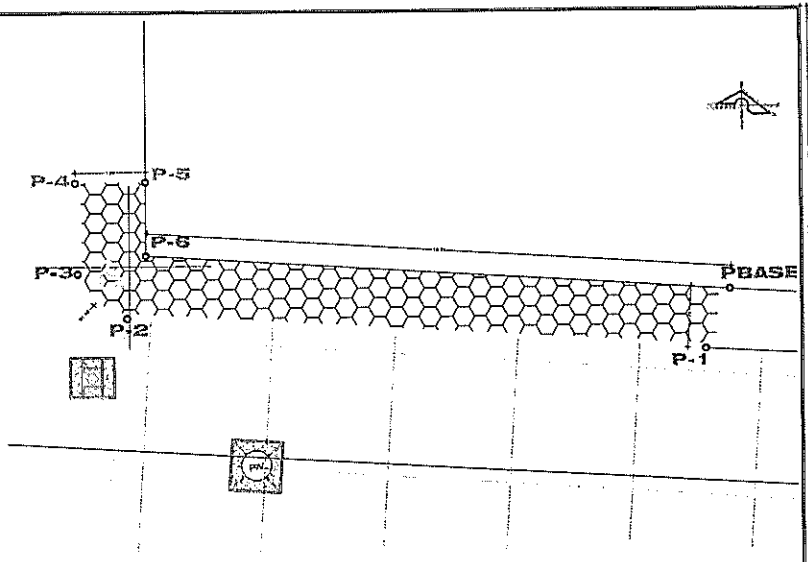


PLANTA DE ESTADO ACTUAL

ESCALA 1:200 — CALLE INES MARISCAL

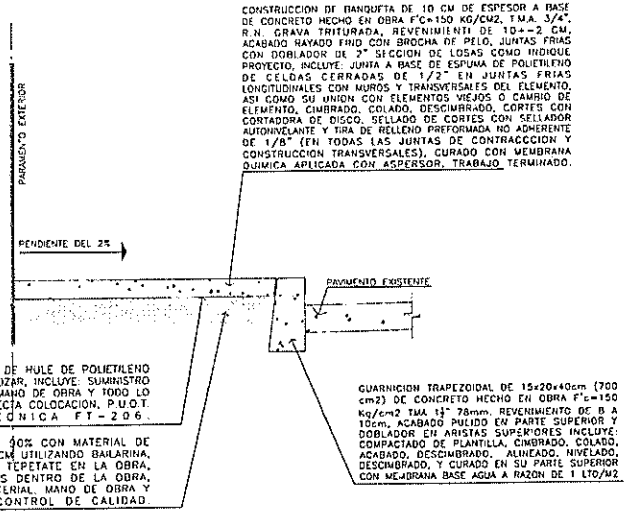

PUNTOS	X	Y	RADIO
PBASE	769.7739	821.4875	--
P01	769.0917	819.7799	--
P02	752.5587	820.7693	1.50
P03	751.1622	822.0452	--
P04	751.1108	824.6545	--
P05	753.0981	824.6686	--
P06	753.0977	822.5572	--

LOCALIZACION:

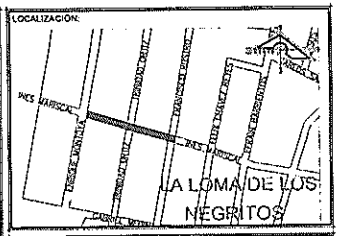

SIMBOLOGÍA

La Dirección de Planeación y Proyectos solo autoriza el proyecto ejecutivo, no es responsable de la correcta ejecución de la obra. Este documento no tiene validez si no presenta las firmas de los responsables para su autorización, así como los sellos respectivos.

PRESIDENTE MUNICIPAL
M.P.P. Leonardo Montañez Castro
SECRETARIO DE OBRAS PUBLICAS DEL MUNICIPIO DE AGUASCALIENTES
Ing. Miguel Ángel Huizar Botello

REV	FECHA	OBSERVACIONES

VO. Bo. DE LA DEPENDENCIA

RESP. DE PROY. EXTERNO		LOGO EXTERNO
CED. PROFESIONAL		
PROYECTÓ	REVISO	AUTORIZO


Dirección de Planeación y Proyectos de Obra — Secretaría de Obras Públicas

PROYECTISTA	COORDINADOR
BLANCA ESTHER AGUAYO PEREZ	ARQ. ALEJANDRO JAIME LEAL
JEFE DE DEP.	DIRECTOR
ARQ. J. JESUS PALAFOX GONZALEZ	M. en ARQ. JOSÉ LUIS JIMÉNEZ GARCÍA

PROYECTO
CONSTRUCCIÓN DE PAVIMENTO HIDRAULICO
CALLE INES MARISCAL
UBICACIÓN
TRAMO ENTRE CALLE ENRIQUE MONTOYA Y CALLE FRANCISCO ROSTRO, LA LOMA DE LOS NEGRITOS
CONTENIDO
PLANTA TRAZO
TRAZO DE GUARNICION Y DETALLES


CLAVE	No. PLANO
TZ 01	06
FECHA: OCTUBRE 2022	ESCALA: INDICADA
ACOTACION: METROS	No. EXP.: E-000-22


Aguascalientes
LA CIUDAD DE TU VIDA

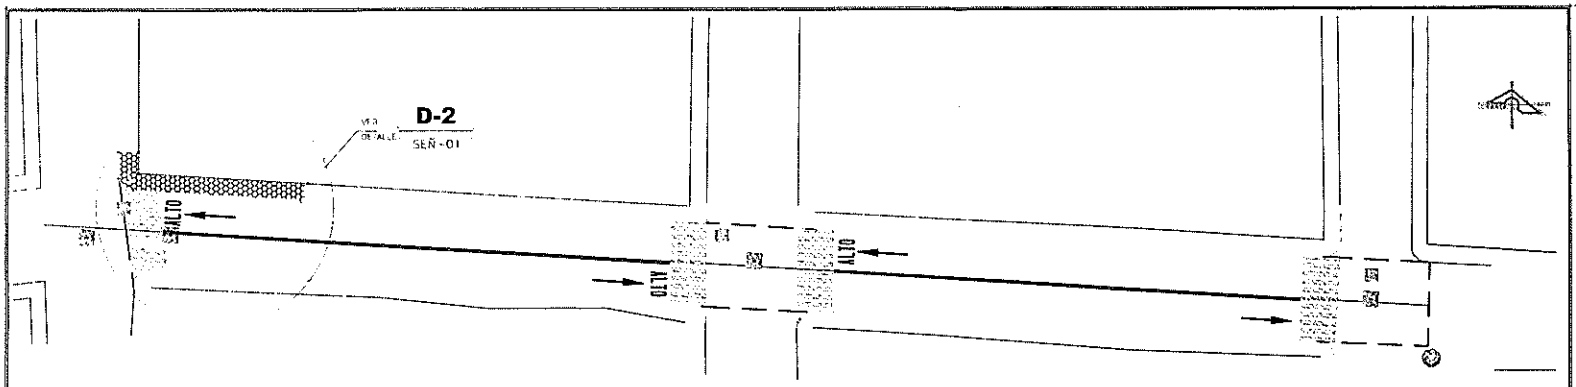


DETALLE 2 SEÑALIZACION HORIZONTAL


ESCALA 1:75 COTAS: cm.

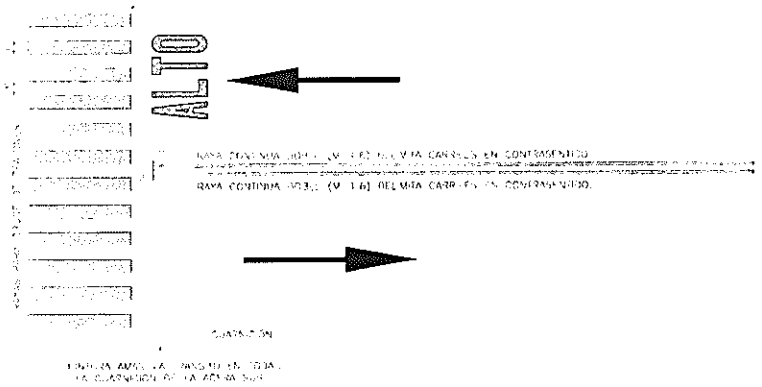

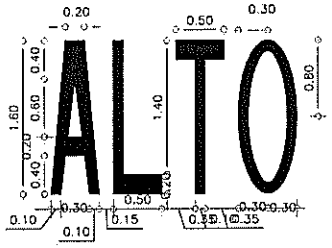

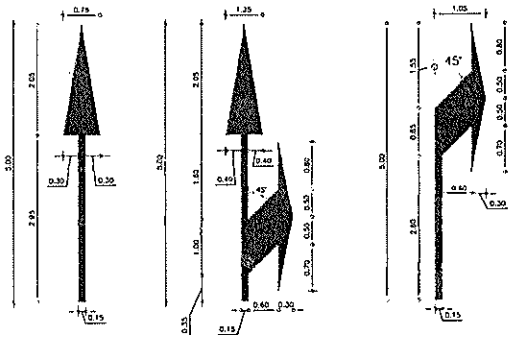

DETALLE DE FLECHAS EN PAVIMENTO
PARA VELOCIDADES HASTA DE 60KM/H
COTAS EN M

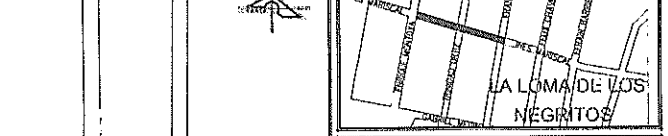

SIMBOLOGIA

NOTA:
Se aplicará en todos los señalamientos horizontales pintura para trafico base solvente tipo alquidal de secado rápido, que cumpla con las especificaciones n-cmt-5-01-001/05, n-pry-car-10-01-002/13 de la SCT aplicados al día de hoy.

Se aplicará en todos los señalamientos horizontales pintura para trafico Termoplastico tipo alquidal de secado rápido, que cumpla con las especificaciones n-cmt-5-01-001/05, n-pry-car-10-01-002/13 de la SCT aplicados al día de hoy.

M – 1.2, Linea discontinua sencilla de división de carriles de frente en piso, de 10 cm de ancho.
M – 3.3, Continua izquierda, para vialidades urbanas de frente en piso, separada 15 cm de la guarnición, color amarillo.
M – 4, Para indicar linea guia en zona de transición de frejte en piso, desarrolo de 2.00 x 0.10 mts entre si promedio.
M – 5, Para indicar entrada y salida en bifurcaciones.
M – 6, Para indicar alto en cruceros, color blanco.
M – 7.1, Para indicar "cruce peatonal en primarios" color amarilla.
M – 11.1 "Flecha sencilla" para indicar sentido de circulación.
M – 11.1, "Flecha doble cabeza" para indicar sentido de circulación (vuelta izquierda o derecha).

NOTA:
Nota1: Se aplicará en todos los señalamientos horizontales pintura para trafico base solvente y/o termoplastica tipo alquidal de secado rápido, que cumpla con las especificaciones n-cmt-5-01-001/05, n-pry-car-10-01-002/13 de la SCT aplicados al día de hoy.

Nota2: Dosificación de micro esfera
La cantidad de esferas de vidrio en la película de pintura en húmedo, según su tipo, será la que se indica en la Tabla.

TABLA 8: Cantidad de esferas de vidrio en la película de pintura en humedo.

CANTIDAD DE ESFERAS DE VIDRIO EN LA PELÍCULA DE PINTURA EN HÚMEDO				
TIPO DE PINTURA	ESPESOR DE LA PELÍCULA DE PINTURA EN HÚMEDO mm	CANTIDAD DE ESFERAS KG/M² INTEGRADAS	SEMBRADAS, MÍNIMO	TIPO DE GRANULOMETRÍA
BASE SOLVENTE	0.30 A 0.50	-	0.330	I
BASE AGUA	0.30 A 0.50	-	0.330	I o II
TERMOPLÁSTICA	1.50 A 3.00	-	0.330	II

La Dirección de Planeación y Proyectos solo autoriza el proyecto ejecutivo, no es responsable de la correcta ejecución de la obra. Este documento no tiene validez si no presenta las firmas de los responsables para su autorización, así como los sellos respectivos.

PRESIDENTE MUNICIPAL
M.P.P. Leonardo Montañez Castro
SECRETARIO DE OBRAS PUBLICAS DEL MUNICIPIO DE AGUASCALIENTES
Ing. Miguel Ángel Huizar Botello

REV.	FECHA	OBSERVACIONES

No. DE LA DERROPOSICIÓN

RESP. DE PROY. EXTERNO		LOGO EXTERNO
CED. PROFESIONAL		
PROYECTÓ	REVISO	AUTORIZÓ

Dirección de Planeación y Proyectos de Obra | Secretaría de Obras Públicas

PROYECTISTA	COORDINADOR
BLANCA ESTHER AGUAYO PEREZ	ARQ. ALEJANDRO JAIME LEAL
JEFE DE DEP.	DIRECTOR
ARQ. J. JESUS PALAFOX GONZÁLEZ	M. en ARQ. JOSE LUIS JIMÉNEZ GARCÍA


PROYECTO
CONSTRUCCIÓN DE PAVIMENTO HIDRAULICO
CALLE INÉS MARISCAL


UBICACIÓN
TRAMO ENTRE CALLE ENRIQUE MONTOYA Y CALLE FRANCISCO ROSTRO, LA LOMA DE LOS NEGRITOS

CONTENIDO
PROYECTO SEÑALIZACIÓN HORIZONTAL

CLAVE	No PLANO
SEÑ 01	08
FECHA OCTUBRE 2022	ESCALA INDICADA
ACOTACIÓN METROS	No. EXP. E-000-22

Aguascalientes
LA CIUDAD DE TU VIDA

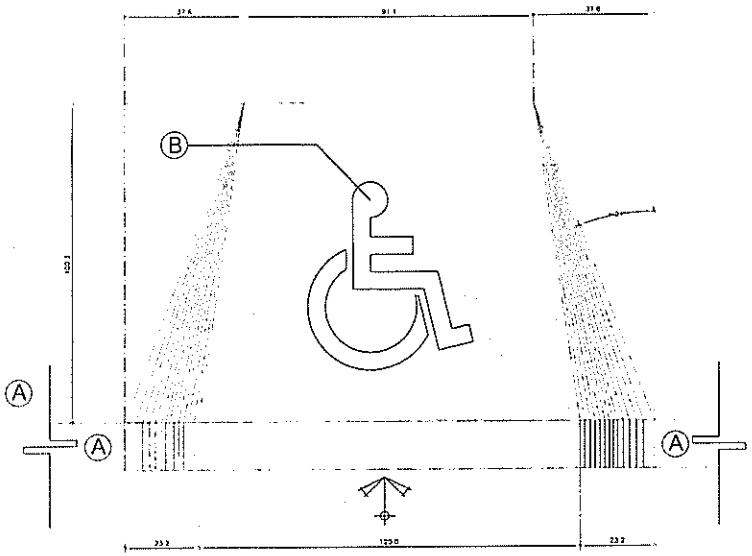


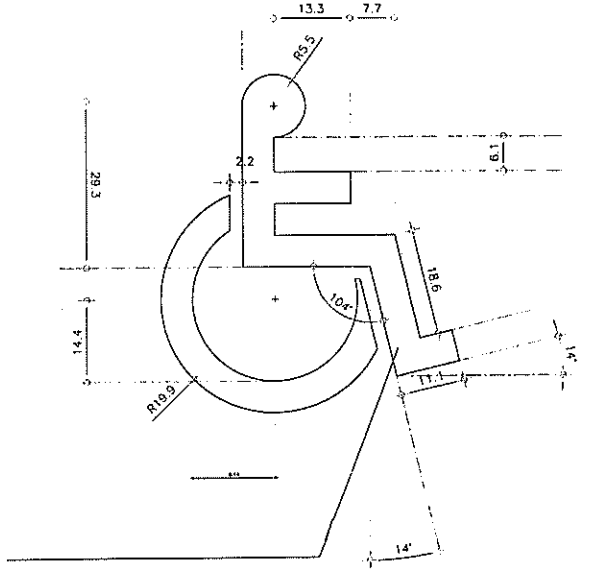

A

B

LOCALIZACIÓN.

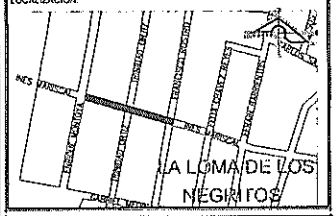

SIMBOLOGÍA

NOTA:
Nota1: Se aplicará en todos los señalamientos horizontales pintura para tráfico base solvente tipo alkidal de secado rápido, que cumpla con las especificaciones n-cmt-5-01-001/05, n-pry-car-10-01-002/13 de la SCT aplicadas al día de hoy.

Nota2: Dosificación de micro esfera
La cantidad de esferas de vidrio en la película de pintura en húmedo, según su tipo, será la que se indica en la Tabla.

TABLA 8. Cantidad de esferas de vidrio en la película de pintura en humedo.

ing or invalid reference /Users/febiola.gomez/Desktop/TABLA8.pdf
9t: 1

La Dirección de Planeación y Proyectos solo autoriza el proyecto ejecutivo, no es responsable de la correcta ejecución de la obra. Este documento no tiene validez si no presenta las firmas de los responsables para su autorización, así como los sellos respectivos.

PRESIDENTE MUNICIPAL
M.P.P. Leonardo Montañez Castro
SECRETARIO DE OBRAS PÚBLICAS DEL MUNICIPIO DE AGUASCALIENTES
Ing. Miguel Ángel Huizar Botello

REV	FECHA	OBSERVACIONES

V°.B° DE LA DEPENDENCIA

RESP. DE PROY EXTERNO		LOGO EXTERNO
CED. PROFESIONAL		
PROYECTÓ	REVISÓ	AUTORIZÓ


Dirección de Planeación y Proyectos de Obra — Secretaría de Obras Públicas

PROYECTISTA	COORDINADOR
BLANCA ESTHER AGUAYO PEREZ	ARQ. ALEJANDRO JAIME LEAL
JEFE DE DEP.	DIRECTOR
ARQ. J. JESÚS PALAFOX GONZÁLEZ	M. en ARQ. JOSÉ LUIS JIMÉNEZ GARCÍA

PROYECTO
CONSTRUCCIÓN DE PAVIMENTO HIDRAÚLICO
CALLE INES MARISCAL
UBICACIÓN
TRAMO ENTRE CALLE ENRIQUE MONTOYA Y CALLE FRANCISCO ROSTRO, LA LOMA DE LOS NEGRITOS
CONTENIDO
DETALLES SEÑALETICA DISCAPACITADOS

CLAVE	No. PLANO
DSD 01	09
FECHA: OCTUBRE 2023	ESCALA: INDICADA
ACOTACIÓN: METROS	No. EXP: E-000-22

Aguascalientes
LA CIUDAD DE TU VIDA

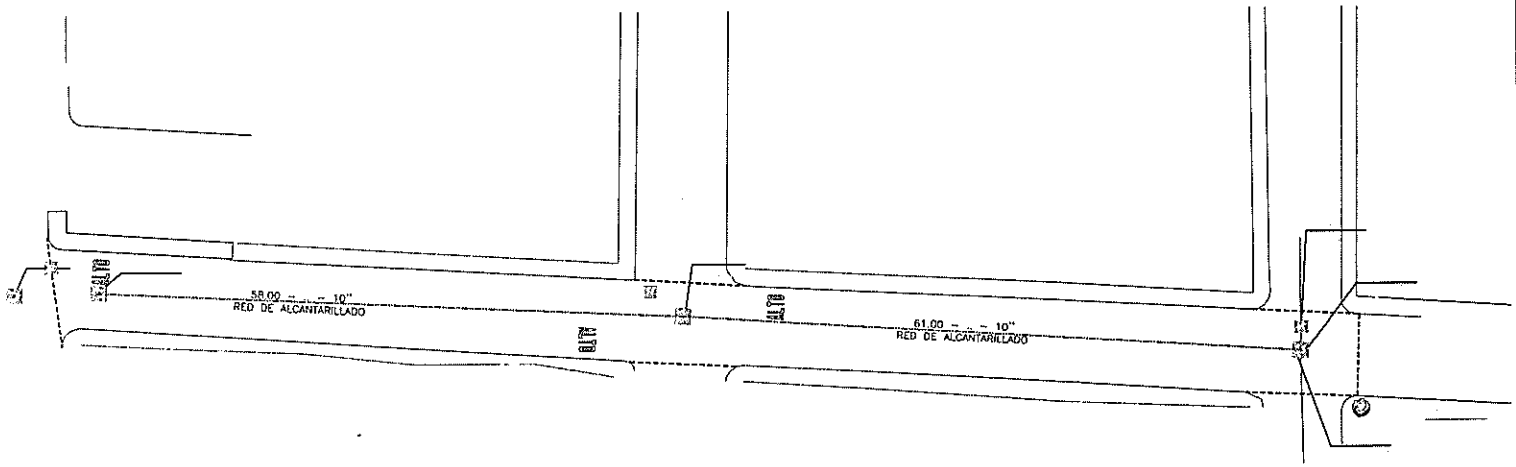


RED SANITARIA


ESCALA 1:200

CALLE INES MARISCAL

LOCALIZACIÓN:

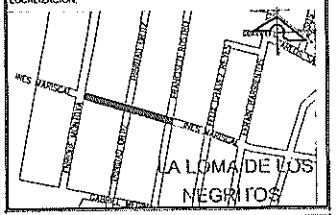

SIMBOLOGÍA

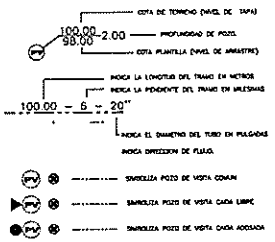

NOTA:
LA LINEA DE ALCANTARILLADO SE UBICARA EN SITIO, MEDIANTE UN SONDEO DE PARTE DE LA DEPENDENCIA RESPONSABLE DE LA MISMA (CCAPAMA), PARA PODER UBICAR TRAYECTOS, PROFUNDIAD, DIMENSIONES, TERIALES ETC.

NOTA:
LA DEMOLICION DE LOS POZOS DE VISITA SE LLEVARA A CABO DESPUES DE HACER UNA INSPECION FISICA CON PERSONAL DE CCAPAMA, DETERMINANDO EN SITIO SE DETERMINARA SI ES NECESARIO SU DEMOLICION Y SUSTITUCION.

La Dirección de Planeación y Proyectos solo autoriza el proyecto ejecutivo, no es responsable de la correcta ejecución de la obra. Este documento no tiene validez si no presenta las firmas de los responsables para su autorización, así como los sellos respectivos.

PRESIDENTE MUNICIPAL
M.P.P. Leonardo Montañez Castro
SECRETARIO DE OBRAS PÚBLICAS DEL MUNICIPIO DE AGUASCALIENTES
Ing. Miguel Ángel Huizar Botello

REV	FECHA	OBSERVACIONES

V° B° DE LA DEPENDENCIA

RESP. DE PROY. EXTERNO		LOGO EXTERNO
CED. PROFESIONAL		
PROYECTO	REVISÓ	AUTORIZÓ


Dirección de Planeación y Proyectos de Obra — Secretaría de Obras Públicas

PROYECTISTA	COORDINADOR
BLANCA ESTHER AGUAYO PEREZ	ARQ. ALEJANDRO JAIME LEAL
JEFE DE DEP	DIRECTOR
ARQ. J. JESÚS PALACIOS GONZÁLEZ	M. en ARQ. JOSÉ LUIS JIMÉNEZ GARCÍA

PROYECTO
CONSTRUCCIÓN DE PAVIMENTO HIDRAULICO CALLE INES MARISCAL
UBICACIÓN
TRAMO ENTRE CALLE ENRIQUE MONTOYA Y CALLE FRANCISCO ROSTRO, LA LOMA DE LOS NEGRITOS
CONTENIDO
PLANO DE ALCANTARILLADO

CLAVE	No. PLANO
SAN 01	10
FECHA: OCTUBRE 2022	ESCALA: INDICADA
ACOTACIÓN: METROS	No. EXP: E-000-22

Aguascalientes
LA CIUDAD DE TU VIDA

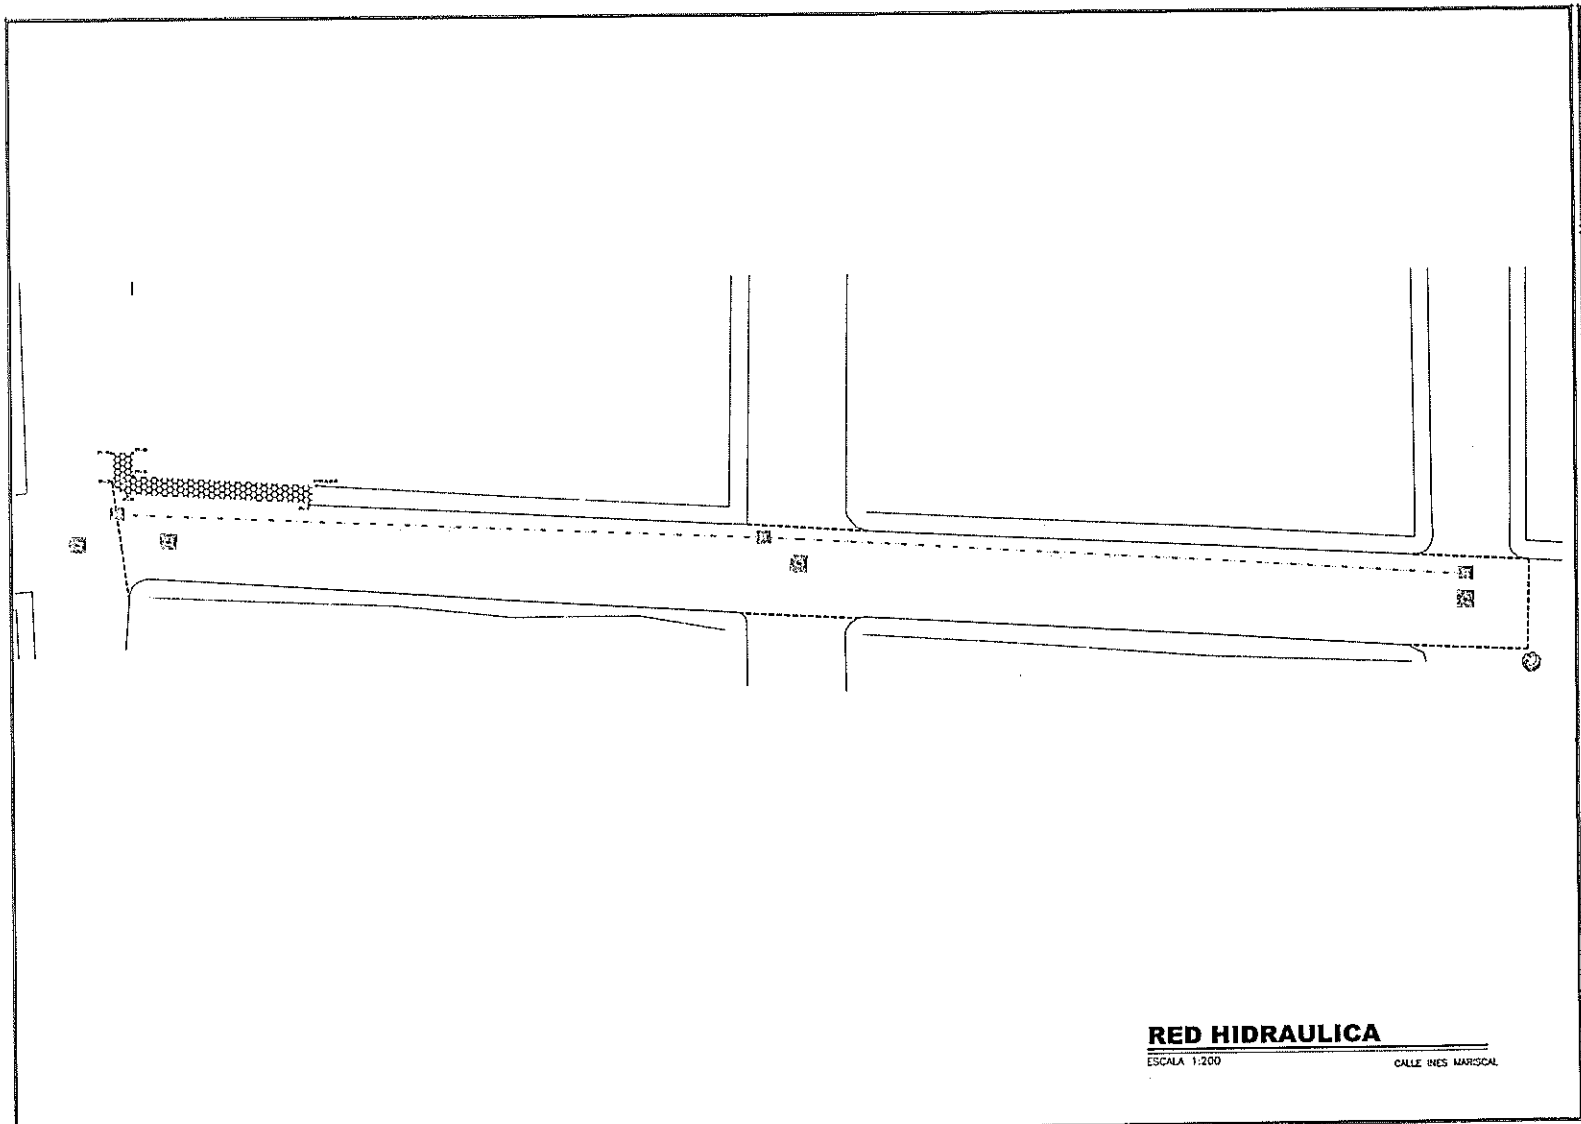


RED HIDRAULICA

ESCALA 1:200

CALLE INES MARISCAL

LOCALIZACIÓN:

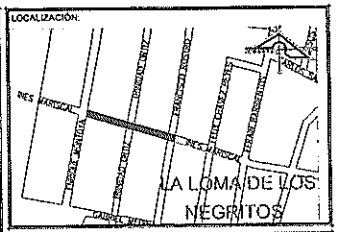

SIMBOLOGÍA

INDICA LA LONGITUD DEL TRAMO EN METROS

25–T6 INDICA EL DIAMETRO DEL TUBO EN PULGADAS

La Dirección de Planeación y Proyectos solo autoriza el proyecto ejecutivo, no es responsable de la correcta ejecución de la obra. Este documento no tiene validez si no presenta las firmas de los responsables para su autorización, así como los sellos respectivos.

PRESIDENTE MUNICIPAL
M.P.P. Leonardo Montañez Castro
SECRETARIO DE OBRAS PÚLICAS DEL MUNICIPIO DE AGUASCALIENTES
Ing. Miguel Ángel Huizar Botello

REV.	FECHA	OBSERVACIONES

Vía Ref. DE LA DEPENDENCIA

RESP. DE PROY. EXTERNO		LOGO EXTERNO
CED. PROFESIONAL		
PROYECTO	REVISO	AUTORIZÓ

Dirección de Planeación y Proyectos de Obra — Secretaría de Obras Públicas

PROYECTISTA	COORDINADOR
BLANCA ESTHER AGUAYO PEREZ	ARQ. ALEJANDRO JAIME LEAL
JEFE DE DEP.	DIRECTOR
ARQ. J. JESÚS PALAFOX GONZÁLEZ	M. en ARQ. JOSÉ LUIS JIMÉNEZ GARCÍA

PROYECTO
CONSTRUCCIÓN DE PAVIMENTO HIDRAULICO CALLE INES MARISCAL

UBICACIÓN
TRAMO ENTRE CALLE ENRIQUE MONTOYA Y CALLE FRANCISCO ROSTRO, LA LOMA DE LOS NEGRITOS

CONTENIDO
PLANTA HIDRAULICA

CLAVE	No. PLANO
HID 01	12
FECHA	ESCALA
OCTUBRE 2022	INDICADA
ACOTACIÓN	No. EXP.
METROS	E-000-22

Aguascalientes
LA CIUDAD DE TU VIDA