Aguascalientes
LA CIUDAD DE TU VIDA

Dirección de Programación Presupuestal
Núm. Oficio AMPP/0624/22
Aguascalientes, Ags. 27 de Diciembre del 2022
Asunto: Validación de Expediente Técnico

C.P. SERGIO ARTURO LOZANO GONZÁLEZ
SECRETARIO DE FINANZAS MUNICIPALES
P R E S E N T E

Con fundamento en los artículos 17 fracción XV, 60 fracción XVI y 76 fracción VI del Reglamento del Sistema Integral de Desarrollo Municipal y del Instituto Municipal de Planeación y Evaluación de Aguascalientes, hago referencia al oficio SOPMA/2869/2022 recibido por este Instituto el día 27 de Diciembre del 2022 por parte de la Secretaría de Obras Públicas Municipales, mediante el cual remiten el expediente técnico original de la siguiente obra para su análisis, registro y priorización, conforme al Programa Anual de Obra Pública y Programas Sociales para el ejercicio presupuestal 2022:

DEPENDENCIA EJECUTORA:	SOPMA
NOMBRE DE LA OBRA O PROYECTO:	OBRA COMPLEMENTARIA Y SEÑALIZACIÓN
UBICACIÓN:	LIC. MIGUEL DE LA MADRID HURTADO (CALZADA ORIENTE), TRAMO: ENTRE CALLE GRANEROS Y ACCESO A TERZETTO, VARIAS COLONIAS, AGUASCALIENTES, AGS.
FONDO DE INVERSIÓN:	FONDO DE INFRAESTRUCTURA SOCIAL MUNICIPAL Y DE LAS DEMARCACIONES TERRITORIALES DEL DISTRITO FEDERAL
IMPORTE:	$1,967,931.13 (ET FINAL)
No. DE OBRA:	2022-FISMDF-0082-04-1101
MODALIDAD DE EJECUCIÓN:	CONTRATO
EJE:	MUNICIPIO SOBRESALIENTE
ESTRATEGIA:	OBRA PÚBLICA INTELIGENTE
POLITICA:	5.8.1.REHABILITACIÓN Y MANTENIMIENTO VIALIDADES, CAMINOS, CALLES, ÁREAS DE TERRACERÍA Y CAUCES (C

Al respecto, hago de su conocimiento que dicho expediente ha sido analizado en su integración técnica y documental, con base en el artículo 168 fracción I del Reglamento de la Ley de Obras Públicas y Servicios Relacionados para el Estado de Aguascalientes y sus Municipios.

Asimismo, le comento que este Instituto valida dicha obra acorde a lo establecido en los artículos 14, 22 párrafo segundo y 23 de la Ley de Obras Públicas y Servicios Relacionados para el Estado de Aguascalientes y sus Municipios, la cual se encuentra alineada al Plan de Desarrollo Municipal vigente, para dar cumplimiento a las metas establecidas en el mismo, y a los Lineamientos Generales para la Operación de este Fondo de Inversión, toda vez que la misma cuente con la autorización del CODEMUN. De igual manera, se hace de su conocimiento que deberá cumplir con lo establecido en los ordenamientos aplicables en lo que respecta al ejercicio, control e información de los recursos de este Fondo. Cabe hacer mención que los recursos solicitados para este proyecto de inversión, estarán sujetos a la disponibilidad presupuestal para el presente ejercicio fiscal que determine la Secretaría a su digno cargo. Sin otro particular por el momento, le envío un cordial saludo.

A T E N T A M E N T E

ARQ. AUSTRIA GABRIELA DÁVILA DE LA LLAVE
DIRECTORA GENERAL DEL IMPLAN

SBDR/ CAAR / JDBC
C.c.p. I.C. ING. MIGUEL ÁNGEL HUIZAR BOTELLO .- Secretaría de Obras Públicas Municipales .Para su conocimiento.
C.c.p. Archivo.

Instituto Municipal de Planeación y Evaluación de Aguascalientes
Antonio Acevedo Escobedo 103 A. Col. Centro
Aguascalientes. Ags. C.P. 20000
(449) 9101010 Ext. 3117
www.implanags.gob.mx

GOBIERNO MUNICIPAL DE AGUASCALIENTES

INSTITUTO MUNICIPAL DE PLANEACION

IMPLAN

ANÁLISIS INTEGRAL DE EXPEDIENTE TÉCNICO

No. DE OBRA (PAOP 2020):	2022-FISMDF-0082-04-1101	REGISTRO No.	245
OFICIO DE VALIDACIÓN:	AMPP/0624/22	FECHA RECIBIDO PARA REVISIÓN:	27 de Diciembre del 2022
PROGRAMA:	URBANIZACION MUNICIPAL	LOCALIDAD O COLONIA:	VARIAS COLONIAS
SUB-PROGRAMA:	0411- Calles y Caminos	DELEGACIÓN:	Aguascalientes
DEPENDENCIA:	Secretaría de Obras Públicas Municipales	MOD. DE EJECUCIÓN:	CONTRATO
NOMBRE DE LA OBRA:	OBRA COMPLEMENTARIA Y SEÑALIZACIÓN, LIC. MIGUEL DE LA MADRID HURTADO (CALZADA ORIENTE), TRAMO: ENTRE CALLE GRANEROS Y ACCESO A TERZETTO		
FUENTE DE FINANCIAMIENTO:	FONDO DE INFRAESTRUCTURA SOCIAL MUNICIPAL Y DE LAS DEMARCACIONES TERRITORIALES DEL DISTRITO FEDERAL, FISMDF		
INVERSIÓN:	$1,967,931.13	CLASIFICACIÓN DE OBRA:	BIENES DE DOMINIO PUBLICA

TOTAL	FEDERAL	ESTATAL	MUNICIPAL	BENEFICIARIOS	OTROS	DIFERENCIA ENTRE MOD.
$1,967,931.13	$1,967,931.13	0.00	0.00	0.00	0.00	*$0.00*

TIPO DE EXPENDIENTE:	ET FINAL	AÑO: 2022	AÑO:	AÑO:		
AVANCES:	Financiero: 68 %	Físico: 98 %				
FECHA DE INICIO:	19 de Agosto del 2022	FECHA DE TÉRMINO:	24 de Septiembre del 2022	REGISTRO SIMA:	82	

CHEK LIST DE LOS ANEXOS DEL EXPEDIENTE TÉCNICO

CÉDULA DE REGISTRO DE OBRA	✓
DICTAMEN DE FACTIBILIDAD	✓
MEMORIA DESCRIPTIVA	✓
PRESUPUESTO BASE	✓
FACTIBILIDAD VERIFICADA EN CAMPO	✓
CROQUIS DE UBICACIÓN (MACRO)	✓
CROQUIS DE UBICACIÓN (MACRO)	✓
PROGRAMA DE OBRA Y MONTOS MENSUALES	✓
PLANOS O ESTUDIOS TÉCNICOS	✓
PADRÓN DE BENEFICIARIOS	N/A
ACTA DE ACEPTACIÓN DEL PROYECTO	N/A
DICTAMEN DE IMPACTO AMBIENTAL	N/A
CONVENIO DE CONCERTACIÓN	N/A
ACTA CONSTITUTIVA	N/A

METAS		BENEFICIARIOS		PERIODO DE EJECUCION		OBRA PROPUESTA		CLAVE SISCO
UNIDAD DE MEDIDA	CANT	TIPO DE BENEFICIARIOS	CANTIDAD	FECHA DE INICIO	FECHA DE TERMINO	CONCEPTO	JORNALES A GENERAR	
OBRA	1	Personas	200	2022-08-19	2022-09-24	Obra Complementaria y/o Señalización	5116	2353

INCLUIDO EN PLAN DE DESARROLLO MUNICIPAL Y EL PROGRAMA ANUAL DE OBRA PÚBLICA

OBSERVACIONES:

SIN OBSERVACIONES

RECIBIO: ING. JOSÉ DAVID BURGUETE CLAUSTRO
Analista de Programación e Inversión de Obra Pública

27 de Diciembre del 2022
Fecha de validación

27 de Diciembre del 2022
Fecha de validación Expediente

PROCEDE Si ✓ No

H. AYUNTAMIENTO CONSTITUCIONAL DEL MUNICIPIO DE AGUASCALIENTES 2021-2024

AYUNTAMIENTO DE AGUASCALIENTES

CEDULA DE REGISTRO POR OBRA

Aguascalientes LA CIUDAD DE TU VIDA

050400-001E00E05-05-2-2-1-00-1-E-0510-0-17-0082-21-2502-6144

2022-FISMDF-0082-0411109-037	Obra **OBRA COMPLEMENTARIA Y SEÑALIZACIÓN BLVD. MIGUEL DE LA MADRID (CALZADA ORIENTE)**
Tipo DEFINITIVO 2 2022 Folio SISCO **2353**	Ubic. TRAMO: ENTRE CALLE GRANEROS Y ACCESO A TERZETTO, AGUASCALIENTES Mpio.

Ent. Ejecutora : **050400001E00E05**

Eje: **05**	MUNICIPIO SOBRESALIENTE
Finalidad: **2**	DESARROLLO SOCIAL
Función: **2**	VIVIENDA Y SERVICIOS A LA COMUNIDAD
Subfunción: **1**	URBANIZACIÓN
Tema: **00**	SIN TEMA
Cuenta del Gasto **1**	GASTO PROGRAMABLE
Clasif. Programatica: **E**	PRESTACIÓN DE SERVICIOS PÚBLICOS
Programa: **0510**	Movilidad Urbana
SubPrograma: **0**	SUBPROGRAMA GENÉRICO
Proyecto: **17**	
Tipo de Gasto: **21**	GASTO INVERSIÓN / OBRA PÚBLICA

I N V E R S I O N 2022

Municipal	2502	FONDO PARA LA INFRAESTRUCTURA SOCIAL MUNICIPAL Y DE LAS DEMARCACIONES TERRITORIALES DEL DISTRITO FEDERAL 2022	$1,967,931.13

Folio SIMA 82 Total $1,967,931.13

M E T A S

Unidad de Medida	Cantidad	Descripción
OBRA	1	OBRA OBRA COMPLEMENTARIA Y SEÑALIZACIÓN BLVD. MIGUEL DE LA MADRID (CALZADA ORIENTE)

Inversión Ejercida Total al 31 de Diciembre de 2021 $0.00

Avance Fisico Acumulado al 31 de Diciembre de 2021

Avance Fisico Acumulado Programado al 31 de Diciembre de 2022 100 %

Fecha de Inicio 19 Ago 2022 Fecha de Terminación 24 Sep 2022

Jornales a Generar en 2022 5116

Modalidad de ejecución CONTRATO

Clasificación de la Obra Bienes de Dominio Público

Registro del Patrimonio: Obras del dominio público

OBRAS PÚBLICAS

Av. Aguascalientes Sur No. 2615
Fracc. Jardines de las Fuentes,
Aguascalientes, Ags. C.P. 20278

(449) 9 78 92 01, 06, 09

www.ags.gob.mx

GENERALES

Nombre del Proyecto : OBRA COMPLEMENTARIA Y SEÑALIZACIÓN BLVD. MIGUEL DE LA MADRID (CALZADA ORIENTE)

TRAMO: ENTRE CALLE GRANEROS Y ACCESO A TERZETTO, AGUASCALIENTES Mpio.

Programa : 04 URBANIZACION MUNICIPAL

Subprograma : 11 Calles y caminos (428.- Rehabilitación: 0411208- Señalización)

Clave del Municipio : AGUASCALIENTES

Localidad :

Barrio, Colonia o Ejido : AGUASCALIENTES Mpio.

Tipo de Obra : NUEVA

DESCRIPCIÓN DEL PROYECTO:

OBRA COMPLEMENTARIA Y SEÑALIZACIÓN BLVD. MIGUEL DE LA MADRID (CALZADA ORIENTE)

Beneficiarios (No. y Tipo) :

200	PERSONAS

Hombres: 90 Mujeres: 110

OBRAS PÚBLICAS

Av. Aguascalientes Sur No. 2615
Fracc. Jardines de las Fuentes,
Aguascalientes, Ags. C.P. 20278

(449) 9 78 92 01, 06, 09

www.ags.gob.mx

Los abajo firmantes, hacen constar que el presente proyecto :

OBRA COMPLEMENTARIA Y SEÑALIZACIÓN BLVD. MIGUEL DE LA MADRID (CALZADA ORIENTE)

TRAMO: ENTRE CALLE GRANEROS Y ACCESO A TERZETTO, AGUASCALIENTES Mpio.

cumple con los Requisitos y Normas Técnicas establecidas por la Dependencia Normativa, por lo que es viable su ejecución. Comprometiéndose la misma a proporcionar la supervisión y asistencia técnica necesaria durante el proceso administrativo.

Por la Dependencia Ejecutora

Ing. Miguel Angel Huizar Botello
Secretario de Obras Públicas

Lic. Jaime Gallo Camacho
Secretario de Desarrollo Urbano

LUGAR :AGUASCALIENTES, AGS.

Av. Aguascalientes Sur No. 2615
Fracc. Jardines de las Fuentes,
Aguascalientes, Ags. C.P. 20278

(449) 9 78 92 01, 06, 09

www.ags.gob.mx

H. AYUNTAMIENTO CONSTITUCIONAL DEL MUNICIPIO DE AGUASCALIENTES 2021-2024

AYUNTAMIENTO DE AGUASCALIENTES

FACTIBILIDAD VERIFICADA EN CAMPO

Aguascalientes
LA CIUDAD DE TU VIDA

MUNICIPIO: AGUASCALIENTES

LOCALIZACION: TRAMO: ENTRE CALLE GRANEROS Y ACCESO A TERZETTO, AGUASCALIENTES Mpio.

PROGRAMA: URBANIZACION MUNICIPAL

SUBPROGRAMA: Calles y caminos (428.- Rehabilitación: 0411208- Señalización)

OBRA A REALIZAR: OBRA COMPLEMENTARIA Y SEÑALIZACIÓN BLVD. MIGUEL DE LA MADRID (CALZADA ORIENTE)

DEPENDENCIA EJECUTORA: SECRETARÍA DE OBRAS PUBLICAS DEL MUNICIPIO DE AGUASCALIENTES

FORMA DE EJECUCION: CONTRATO

TIPO DE OBRA PROPUESTA: NUEVA

CONDICIONES ACTUALES DE LA OBRA:

OBRA COMPLEMENTARIA Y SEÑALIZACIÓN BLVD. MIGUEL DE LA MADRID (CALZADA ORIENTE)

CARACTERISTICAS DE LA OBRA: Bueno

FACTIBILIDAD DE LA OBRA:

ESTA OBRA SE REQUIERE PARA EL BENEFICIO DE LA CIUDADANÍA

PROCEDE: SI [X] NO [ ]

REVISÓ: Jefa del Departamento de Expedientes Tecnicos y Costos

NOMBRE: Arq. Blanca Margarita Martinez Amador

FIRMA:

FECHA: 07 Dic 2022

SECRETARÍA DE OBRAS PÚBLICAS

Av. Aguascalientes Sur No. 2615
Fracc. Jardines de las Fuentes,
Aguascalientes, Ags. C.P. 20278

(449) 9 78 92 01, 06, 09

www.ags.gob.mx

No. Folio SISCO 2353


H. AYUNTAMIENTO CONSTITUCIONAL DEL MUNICIPIO DE AGUASCALIENTES 2019-2021

SECRETARIA DE OBRAS PUBLICAS MUNICIPALES

DIRECCION DE SUPERVISION

OBRA COMPLEMENTARIA Y SEÑALIZACIÓN BLVD. MIGUEL DE LA MADRID (CALZADA ORIENTE), TRAMO: ENTRE CALLE GRANEROS Y ACCESO A TERZETTO, AGUASCALIENTES Mpio.

Aguascalientes
LA CIUDAD DE TU VIDA

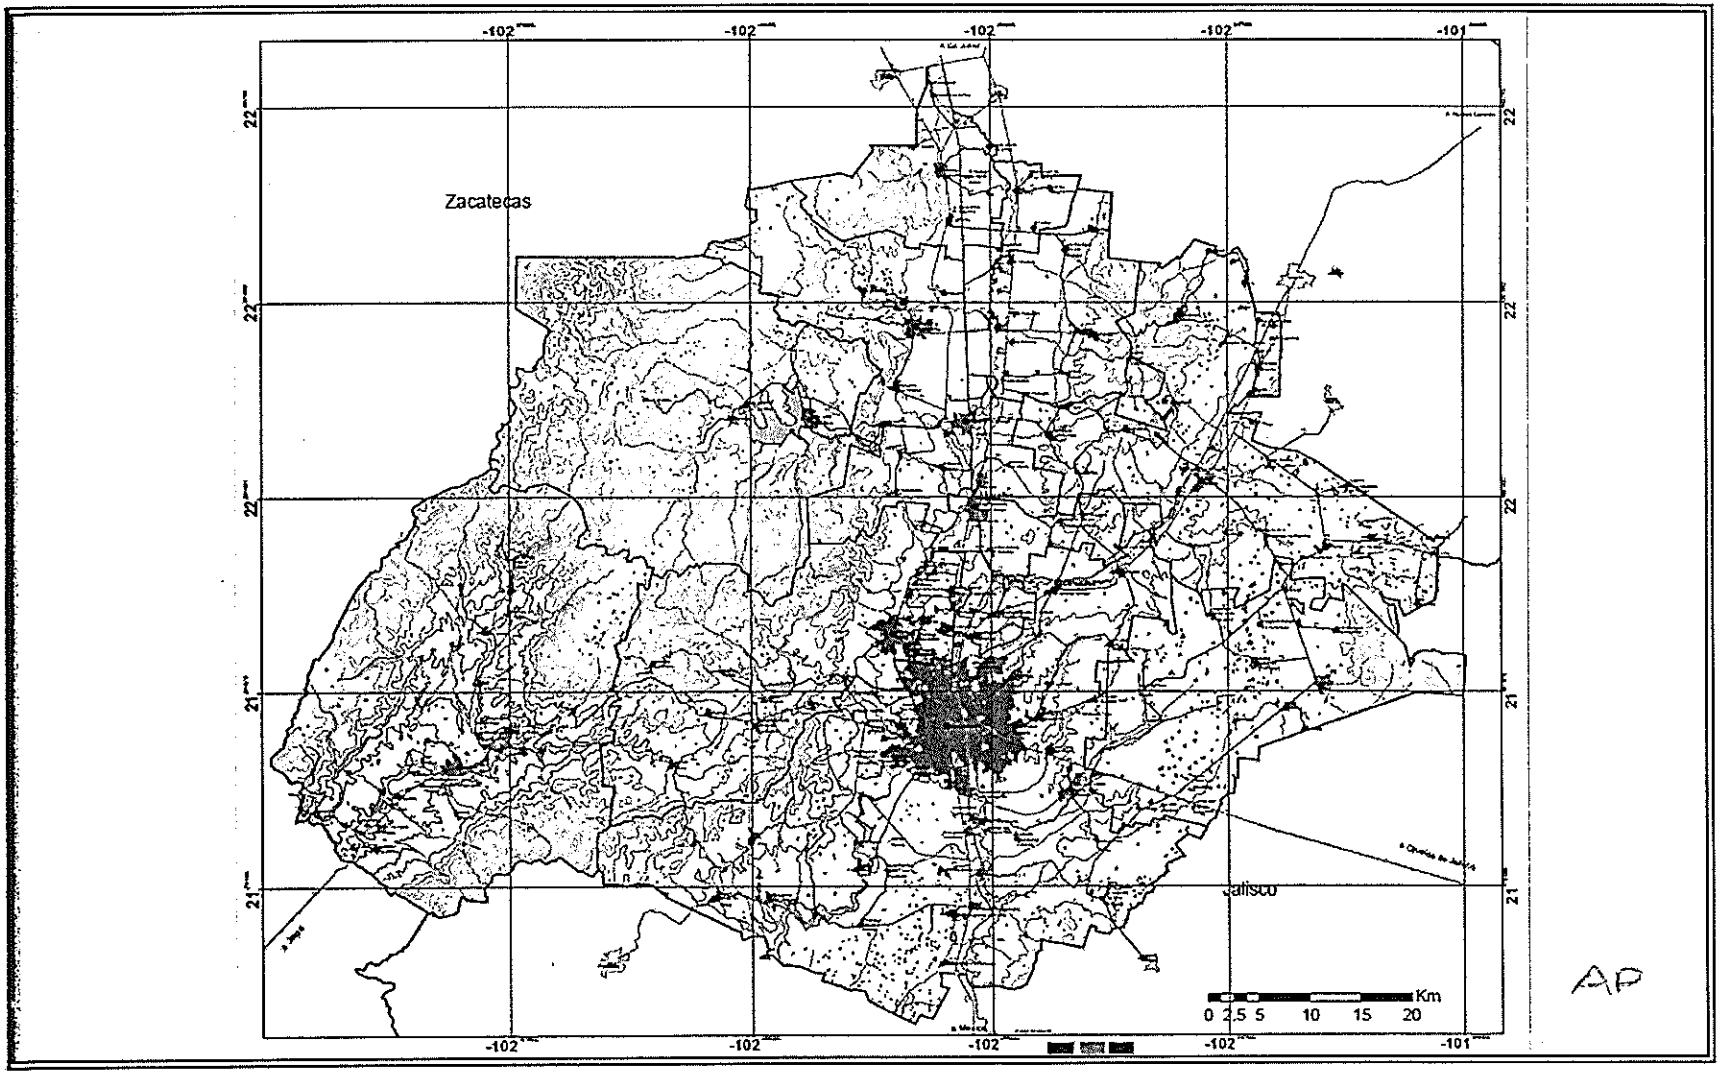

AP

LOCALIZACION A NIVEL MACRO


H. AYUNTAMIENTO CONSTITUCIONAL DEL MUNICIPIO DE AGUASCALIENTES 2019 2021

SECRETARIA DE OBRAS PUBLICAS MUNICIPALES

DIRECCION DE SUPERVISION

OBRA COMPLEMENTARIA Y SEÑALIZACIÓN BLVD. MIGUEL DE LA MADRID (CALZADA ORIENTE), TRAMO: ENTRE CALLE GRANEROS Y ACCESO A TERZETTO, AGUASCALIENTES Mpio.

Aguascalientes
LA CIUDAD DE TU VIDA

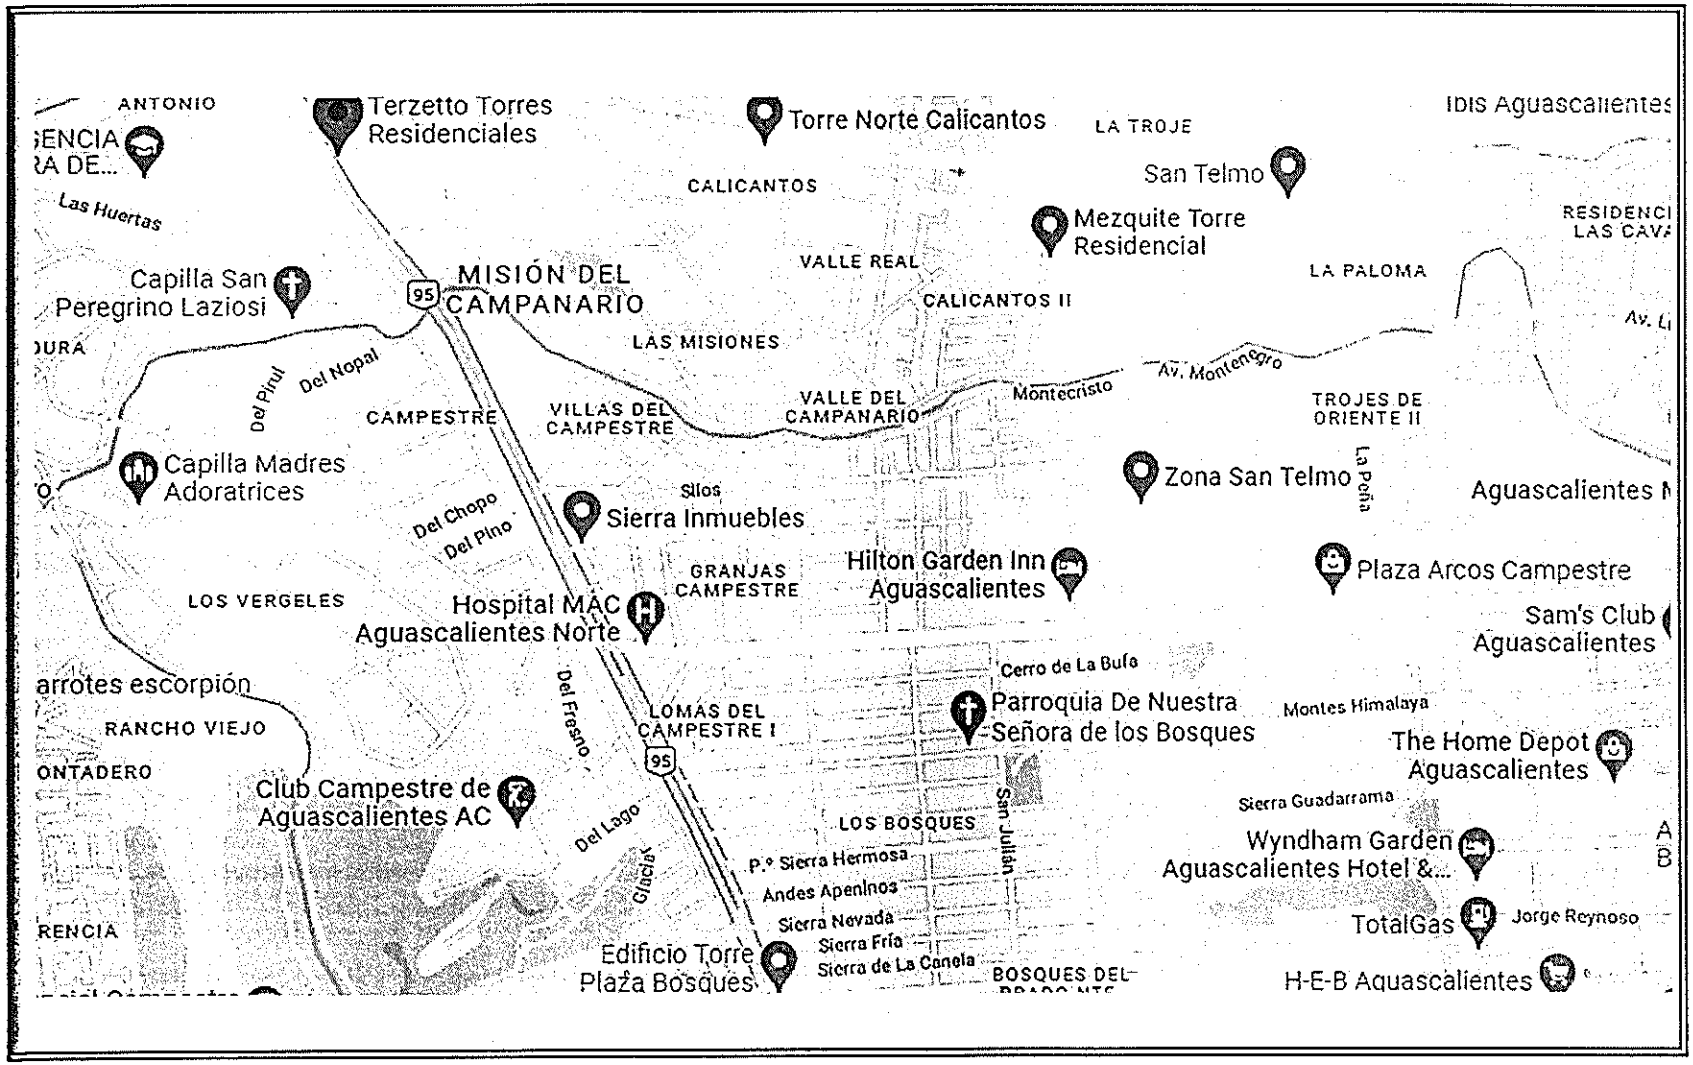

LOCALIZACION A NIVEL MICRO

AP

H. AYUNTAMIENTO CONSTITUCIONAL
EL MUNICIPIO DE AGUASCALIENTES
2019 - 2021

PROGRAMA DE OBRA DEFINITIVO

Aguascalientes
LA CIUDAD DE TU VIDA

RO3-POS-SOS-7.5.1-04	
REVISION:	00
FECHA DE REVISION:	
RESPONSABLE:	SUPERVISOR DE OBRA
TIEMPO DE RET:	02 AÑOS

No. DE CONTRATO : FISMDF-0082-2022

PROGRAMA: 04-URBANIZACION MUNICIPAL

No. OBRA Y NOMBRE DE LA OBRA: OBRA COMPLEMENTARIA Y SENALIZACIÓN BLVD. MIGUEL DE LA MADRID (CALZADA ORIENTE), TRAMO: ENTRE CALLE GRANEROS Y ACCESO A TERZETTO, AGUASCALIENTES Mpio.

INICIO VIGENTE: 19-agosto-22

TERMINO REAL: 24-septiembre-22

RECURSO: 2022

CONCEPTO			2021																PONDERACIÓN %	
			OCTUBRE	NOVIEMBRE	DICIEMBRE	ENERO	FEBRERO	MARZO	ABRIL	MAYO	JUNIO	JULIO	AGOSTO	SEPTIEMBRE	OCTUBRE	NOVIEMBRE	DICIEMBRE	ENERO	FINANCIERO	FISICO
			1 2 3 4	1 2 3 4	1 2 3 4	1 2 3 4	1 2 3 4	1 2 3 4	1 2 3 4	1 2 3 4	1 2 3 4	1 2 3 4	1 2 3 4	1 2 3 4	1 2 3 4	1 2 3 4	1 2 3 4	1 2 3 4	%	%
DESCRIPCION	INVERSION															20	6			
OBRA COMPLEMENTARIA Y SENALIZACION BLVD. MIGUEL DE LA MADRID (CALZADA ORIENTE), TRAMO: ENTRE CALLE GRANEROS Y ACCESO A TERZETTO, AGUASCALIENTES Mpio.																				
TRAMO: ENTRE CALLE GRANEROS Y ACCESO A TERZETTO, AGUASCALIENTES Mpio.																				
SEÑALIZACION HORIZONTAL	$ 1,089,151.58	60											25 25 25 25						60.00	60.00
SEÑALIZACION VERTICAL	$ 17,947.93	10												100					10.00	10.00
EXTRAORDINARIOS	$ 609,392.83	30												50 50					30.00	30.00
SUBTOTAL SIN IVA	$ 1,696,492.34		0 0 0 0	0 0 0 0	0 0 0 0	0 0 0 0	0 0 0 0	0 0 0 0	0 0 0 0	0 0 0 0	0 0 0 0	0 0 0 0	0 0 1 1	2 2 1 0	0 0 0 0	0 0 0 0	0 0 0 0	0 0 0 0		
AVANCE SEMANAL %			0% 0% 0% 0%	0% 0% 0% 0%	0% 0% 0% 0%	0% 0% 0% 0%	0% 0% 0% 0%	0% 0% 0% 0%	0% 0% 0% 0%	0% 0% 0% 0%	0% 0% 0% 0%	0% 0% 0% 0%	0% 0% 14% 14%	25% 25% 14% 0%	0% 0% 0% 0%	0% 0% 0% 0%	0% 0% 0% 0%	0% 0% 0% 0%		
AVANCE SEMANAL ACUMULADO %			0% 0% 0% 0%	0% 0% 0% 0%	0% 0% 0% 0%	0% 0% 0% 0%	0% 0% 0% 0%	0% 0% 0% 0%	0% 0% 0% 0%	0% 0% 0% 0%	0% 0% 0% 0%	0% 0% 0% 0%	0% 0% 14% 14%	25% 50% 64% 64%	64% 64% 64% 64%	64% 64% 64% 64%	64% 64% 64% 64%	64% 64% 64% 64%	100.00	100.00
EJERCIDO SEMANAL $													292,287.50	571,954.31					$ 1,696,492.34	
EJERCIDO MENSUAL $			$0.00	$0.00	$0.00	$0.00	$0.00	$0.00	$0.00	$0.00	$0.00	$0.00	$534,575.79	$1,161,916.55	$0.00	$0.00	$0.00	$0.00	$ 271,438.76	IVA 16%
EJERCIDO MENSUAL ACUMULADO $			0.00	0.00	0.00	0.00	0.00	0.00	0.00	0.00	0.00	0.00	534,575.79	1,696,492.34	1,696,492.34	1,696,492.34	1,696,492.34	1,696,492.34		
EJERCIDO SEMANAL %			0% 0% 0% 0%	0% 0% 0% 0%	0% 0% 0% 0%	0% 0% 0% 0%	0% 0% 0% 0%	0% 0% 0% 0%	0% 0% 0% 0%	0% 0% 0% 0%	0% 0% 0% 0%	0% 0% 0% 0%	0% 0% 11% 11%	23% 45% 1% 0%	0% 0% 0% 0%	0% 0% 0% 0%	0% 0% 0% 0%	0% 0% 0% 0%		
EJERCIDO MENSUAL %			0%	0%	0%	0%	0%	0%	0%	0%	0%	0%	32%	68%	0%	0%	0%	0%	GRAN TOTAL EJERCIDO	
EJERCIDO MENSUAL ACUMULADO %			0%	0%	0%	0%	0%	0%	0%	0%	0%	0%	32%	100%	100%	100%	100%	100%	$ 1,967,931.13	

PRE

AP
ALICIA PEÑA
SUPERVISOR

PRESIDENCIA MUNICIPAL DE AGUASCALIENTES

FACTIBILIDAD VERIFICADA EN CAMPO

GENERALES

EJERCICIO: 2022 APROBACION No: 2022-FISMDF-0082-001-0411109-037 MO
LOCALIDAD: TRAMO: ENTRE CALLE GRANEROS Y ACCESO A TERZETTO, AGUASCALIENTES Mpio.
MUNICIPIO: AGUASCALIENTES, Mpio.
TIPO DE INVERSION: FONDO PARA LA INFRAESTRUCTURA SOCIAL MUNICIPAL Y DE LAS DEMARCACIONES TERRITORIALES DEL DISTRITO FEDERAL
PROGRAMA: 04-URBANIZACION MUNICIPAL
SUB-PROGRAMA:
OBRA A REALIZARSE: OBRA COMPLEMENTARIA Y SEÑALIZACIÓN BLVD. MIGUEL DE LA MADRID (CALZADA ORIENTE), TRAMO: ENTRE CALLE GRANEROS Y ACCESO A TERZETTO, AGUASCALIENTES Mpio.
DEPENDENCIA EJECUTORA: SECRETARÍA DE OBRAS PÚBLICAS MUNICIPALES (S.O.P.M.A)
FORMACIÓN DE EJECUCION: CONTRATO NO. DE CONTRATO: FISMDF-0082-2022
NOMBRE CONTRATISTA: JAIME VALDIVIA CONSTRUCCIONES, S.A. DE C.V.
REPRESENTANTE:
MONTO CONT. ORIGEN $1,967,931.13 ANTICIPO: $ 590,379.34 PLAZO: 30 dias
1A AMPLIACION $: 1 AMPL DIAS 7 DIAS
2A AMPLIACION $: 2 AMPL DIAS
FIRMA CONTRATO: 11/08/2022
INICIO CONT: dd/mm/aa 12/08/2022 ERMINO CONT: 10 de octubre de 2022
INICIO REAL: dd/mm/aa 19 de agosto de 2022 TERMINO REAL: 24 de septiembre de 2022

TIPO DE OBRA PROPUESTA

NUEVA CREACIÓN		CONSOLIDACIÓN	
COMPLEMENTARIA	X	AMPLIACIÓN	
REHABILITACIÓN		EQUIPAMIENTO	

CARACTERÍSTICAS DE LA OBRA:

OBRA COMPLEMENTARIA Y SEÑALIZACIÓN BLVD. MIGUEL DE LA MADRID (CALZADA ORIENTE), TRAMO: ENTRE C

CONDICIONES ACTUALES DE LA OBRA: (SELECCIONAR UNO OBLIGATORIO)

BUEN ESTADO X REGULAR PESIMO ESTADO

FACTIBILIDAD DE LA OBRA: (CONDICIONES ACTUALES DE LA OBRA)

ESTA OBRA SE ENCUENTRA EN CONDICIONES PARA OPERARSE

PROCEDE: SI: X NO:
MARQUE SOLO UNA

A.P.

ALICIA RIVERA ROJAS
SUPERVISOR

PRESIDENCIA MUNICIPAL DE AGUASCALIENTES

FACTIBILIDAD VERIFICADA EN CAMPO

GENERALES

LOCALIDAD: TRAMO: ENTRE CALLE GRANEROS Y ACCESO A TERZETTO, AGUASCALIENTES Mpio.
MUNICIPIO: AGUASCALIENTES, Mpio.
PROGRAMA: 04-URBANIZACION MUNICIPAL
SUB-PROGRAMA: 0
OBRA A REALIZARSE: OBRA COMPLEMENTARIA Y SEÑALIZACIÓN BLVD. MIGUEL DE LA MADRID (CALZADA ORIENTE), TRAMO: ENTRE CALLE GRANEROS Y ACCESO A TERZETTO, AGUASCALIENTES Mpio.
DEPENDENCIA EJECUTORA: SECRETARÍA DE OBRAS PÚBLICAS MUNICIPALES (S.O.P.M.A)
FORMACIÓN DE EJECUCION: CONTRATO

TIPO DE OBRA PROPUESTA

NUEVA CREACIÓN		CONSOLIDACIÓN	
COMPLEMENTARIA	X	AMPLIACIÓN	
REHABILITACIÓN		EQUIPAMIENTO	

CARACTERÍSTICAS DE LA OBRA:

OBRA COMPLEMENTARIA Y SEÑALIZACIÓN BLVD. MIGUEL DE LA MADRID (CALZADA ORIENTE), TRAMO: ENTRE CALLE GRANEROS

CONDICIONES ACTUALES DE LA OBRA:

BUEN ESTADO:	X	REGULAR:		PESIMO ESTADO:	

FACTIBILIDAD DE LA OBRA:

ESTA OBRA SE ENCUENTRA EN CONDICIONES PARA OPERARSE

PROCEDE	**SI:**	X	**NO:**		

AP
ALICIA PEÑA ACERO
SUPERVISOR

H. AYUNTAMIENTO CONSTITUCIONAL DEL MUNICIPIO DE AGUASCALIENTES 2021-2024

PRESUPUESTO MODIFICADO

Aguascalientes

Obra: OBRA COMPLEMENTARIA Y SEÑALIZACIÓN BLVD. MIGUEL DE LA MADRID (CALZADA ORIENTE)

Ubicación: TRAMO: ENTRE CALLE GRANEROS Y ACCESO A TERZETTO, AGUASCALIENTES Mpio.

Contratista: JAIME VALDIVIA CONSTRUCCIONES, S.A. DE C.V. (503)

No.	Concepto	Unidad	Cantidad	Precio Unitario	Importe Total
	GRUPO: **OBRA COMPLEMENTARIA Y SEÑALIZACION**				
	PARTIDA: **SEÑALIZACION HORIZONTAL**				
1	SUMINISTRO Y APLICACIÓN DE PINTURA BASE SOLVENTE COLOR AZUL (PANTONE 294) EN RAMPAS PARA PERSONAS CON DISCAPACIDAD CUALQUIER SECCIÓN SEGÚN PLANOS. INCLUYE: TRAZO, MANO DE OBRA, LIMPIEZA PREVIA Y FINAL DE SUPERFICIE, EQUIPO NECESARIO PARA SU EJECUCIÓN, Y TODO LO NECESARIO PARA SU CORRECTA EJECUCIÓN, TRABAJO TERMINADO.	M2	7.39	$342.59	$2,531.74
2	SUMINISTRO Y APLICACIÓN DE LOGOTIPO A (SILLA DE RUEDAS) EN PINTURA BASE SOLVENTE COLOR BLANCO EN RAMPAS PARA PERSONAS CON DISCAPACIDAD TAMAÑO Y DISEÑO SEGÚN PLANOS Y PROYECTO. INCLUYE: TRAZO, ENMASCARILLADO, PLANTILLA, MANO DE OBRA, LIMPIEZA PREVIA Y FINAL DE SUPERFICIE, EQUIPO NECESARIO PARA SU EJECUCIÓN, Y TODO LO NECESARIO PARA SU CORRECTA EJECUCIÓN, TRABAJO TERMINADO.	PZA	3	$1,424.34	$4,273.02
3	SUMINISTRO Y APLICACIÓN DE PINTURA BASE SOLVENTE (ESMALTE) PARA MARCAS EN GUARNICIONES CLASIFICACION M-12.1, M12.2 APLICADA SOBRE GUARNICIONES Y DENTELLONES COLOR BLANCA Y/O AMARILLA, SEGÚN SE REQUIERA Y SEGÚN MANUAL DE SEÑALIZACIÓN VIAL Y DISPOSITIVOS DE SEGURIDAD SICT (S.C.T). SECADO AL TACTO EN 5 MIN Y AL DURO EN 30 MIN CON MICRO ESFERA , DESARROLLO DE 35 CM. INCLUYE: MATERIALES Y ESPECIFICACIONES QUE CUMPLAN CON LA NORMATIVA N-CMT-5-01-001/13, N-PRY-CAR-10-01-002/13 APLICADAS AL DIA DE HOY, TRAZO, MANO DE OBRA, LIMPIEZA PREVIA Y FINAL DE SUPERFICIE, EQUIPO NECESARIO PARA SU EJECUCIÓN, Y TODO LO NECESARIO PARA SU CORRECTA EJECUCIÓN, TRABAJO TERMINADO.	ML	2041.7	$63.27	$129,178.36
4	SUMINISTRO Y APLICACIÓN DE PINTURA TERMOPLASTICA ALQUIDALICA DE 120 MILESIMAS DE " (in) EN RAYA SEPARADORA DE SENTIDOS DE CIRCULACION CLASIFICACIÓN M - 1.1, LÍNEA CONTINUA SENCILLA DE DIVISIÓN DE CARRILES DE FRENTE EN PISO, DE 10 CM DE ANCHO, COLOR BLANCO Y/O AMARILLO CON MICRO ESFERA SEGÚN MANUAL DE SEÑALIZACIÓN VIAL Y DISPOSITIVOS DE SEGURIDAD SICT, SECADO AL TACTO EN 5 MIN Y AL DURO EN 30 MIN. INCLUYE: MATERIALES Y ESPECIFICACIONES QUE CUMPLAN CON LA NORMATIVA N-CMT-5-01-001/13, N-PRY-CAR-10-01-002/13 APLICADAS AL DIA DE HOY, MATERIAL APLICADO EN SU ESTADO DE FUSION A UNA TEMPERATURA MINIMA DE 204 C, LA SUPERFICIE DE CONCRETO O ASFALTO NO DEBE PRESENTAR UNA TEMPERATURA MENOR A LOS 10 C, ;TIEMPO DE SECADO EN RANGOS DE TEMPERATURA DE 10 C DEL SUSTRATO 2 MINUTOS, Y NO MAS DE 10 MINUTOS CUANDO EL SUSTRATO OSCILA ALREDEDOR DE 54C, TRAZO, ENMASCARILLADO, MANO DE OBRA, LIMPIEZA PREVIA Y FINAL DE SUPERFICIE, EQUIPO NECESARIO PARA SU EJECUCIÓN, Y TODO LO NECESARIO PARA SU CORRECTA EJECUCIÓN, TRABAJO TERMINADO.	ML	166	$56.36	$9,355.76

AP

Obra: OBRA COMPLEMENTARIA Y SEÑALIZACIÓN BLVD. MIGUEL DE LA MADRID (CALZADA ORIENTE)

Ubicación: TRAMO: ENTRE CALLE GRANEROS Y ACCESO A TERZETTO, AGUASCALIENTES Mpio.

Contratista: JAIME VALDIVIA CONSTRUCCIONES, S.A. DE C.V. (503)

No.	Concepto	Unidad	Cantidad	Precio Unitario	Importe Total
	GRUPO: **OBRA COMPLEMENTARIA Y SEÑALIZACION**				
	PARTIDA: **SEÑALIZACION HORIZONTAL**				
5	SUMINISTRO Y APLICACIÓN DE PINTURA TERMOPLASTICA ALQUIDALICA DE 120 MILESIMAS DE " (in) EN RAYA SEPARADORA DE SENTIDOS DE CIRCULACION CLASIFICACIÓN M - 1.2, RAYA DISCONTINUA SENCILLA, DE DIVISIÓN DE CARRILES PARA VELOCIDADES MENORES A 60 KM/HR DE FRENTE EN PISO, DESARROLLO DE 2.50 ML X 0.10 MTS DE ANCHO, CON UNA SEPARACIÓN DE 5.00 MTS ENTRE SI PROMEDIO, A BASE DE PINTURA PARA TRAFICO COLOR BLANCO CON MICRO ESFERA SEGÚN MANUAL DE SEÑALIZACIÓN VIAL Y DISPOSITIVOS DE SEGURIDAD SICT (S.C.T). INCLUYE: MATERIALES Y ESPECIFICACIONES QUE CUMPLAN CON LA NORMATIVA N-CMT-5-01-001/13, N-PRY-CAR-10-01-002/13 APLICADAS AL DIA DE HOY, MATERIAL APLICADO EN SU ESTADO DE FUSION A UNA TEMPERATURA MINIMA DE 204 C, LA SUPERFICIE DE CONCRETO O ASFALTO NO DEBE PRESENTAR UNA TEMPERATURA MENOR A LOS 10 C, ;TIEMPO DE SECADO EN RANGOS DE TEMPERATURA DE 10 C DEL SUSTRATO 2 MINUTOS, Y NO MAS DE 10 MINUTOS CUANDO EL SUSTRATO OSCILA ALREDEDOR DE 54C, TRAZO, ENMASCARILLADO, MANO DE OBRA, LIMPIEZA PREVIA Y FINAL DE SUPERFICIE, EQUIPO NECESARIO PARA SU EJECUCIÓN, Y TODO LO NECESARIO PARA SU CORRECTA EJECUCIÓN, TRABAJO TERMINADO.	ML	727.5	$56.36	$41,001.90
6	SUMINISTRO Y APLICACIÓN DE PINTURA TERMOPLASTICA ALQUIDALICA DE 120 MILESIMAS DE " (in) EN RAYA SEPARADORA DE SENTIDOS DE CIRCULACION CLASIFICACIÓN M - 1.6, RAYA CONTINUA DOBLE, DE DIVISION DE CARRILES DE FRENTE EN PISO, 0.10 MTS DE ANCHO, CON UNA SEPARACIÓN IGUAL AL ANCHO DE LA LINEA A BASE DE PINTURA PARA TRAFICO COLOR AMARILLO CON MICRO ESFERA SEGÚN MANUAL DE SEÑALIZACIÓN VIAL Y DISPOSITIVOS DE SEGURIDAD SICT (S.C.T)., INCLUYE: MATERIALES Y ESPECIFICACIONES QUE CUMPLAN CON LA NORMATIVA N-CMT-5-01-001/13, N-PRY-CAR-10-01-002/13 APLICADAS AL DIA DE HOY, MATERIAL APLICADO EN SU ESTADO DE FUSION A UNA TEMPERATURA MINIMA DE 204 C, LA SUPERFICIE DE CONCRETO O ASFALTO NO DEBE PRESENTAR UNA TEMPERATURA MENOR A LOS 10 C, ;TIEMPO DE SECADO EN RANGOS DE TEMPERATURA DE 10 C DEL SUSTRATO 2 MINUTOS, Y NO MAS DE 10 MINUTOS CUANDO EL SUSTRATO OSCILA ALREDEDOR DE 54C, TRAZO, ENMASCARILLADO, MANO DE OBRA, LIMPIEZA PREVIA Y FINAL DE SUPERFICIE, EQUIPO NECESARIO PARA SU EJECUCIÓN, Y TODO LO NECESARIO PARA SU CORRECTA EJECUCIÓN, TRABAJO TERMINADO.	ML	1215.1	$108.59	$131,947.71
7	SUMINISTRO Y APLICACIÓN DE PINTURA TERMOPLASTICA ALQUIDALICA DE 120 MILESIMAS DE " (in) EN RAYA EN LA ORILLA DEL ARROYO VIAL CLASIFICACIÓN M - 3.3, CONTINUA IZQUIERDA, PARA VIALIDADES URBANAS DE FRENTE EN PISO, DE 10 CM DE ANCHO Y SEPARADA 15 CM. DE LA GUARNICION, A BASE DE PINTURA PARA TRAFICO COLOR BLANCO CON MICRO ESFERA SEGÚN MANUAL DE SEÑALIZACIÓN VIAL Y DISPOSITIVOS DE SEGURIDAD SICT (S.C.T)., INCLUYE: MATERIALES Y ESPECIFICACIONES QUE CUMPLAN CON LA NORMATIVA N-CMT-5-01-001/13, N-PRY-CAR-10-01-002/13 APLICADAS AL DIA DE HOY, MATERIAL APLICADO EN SU ESTADO DE FUSION A UNA TEMPERATURA MINIMA DE 204 C, LA SUPERFICIE DE CONCRETO O ASFALTO NO DEBE PRESENTAR UNA TEMPERATURA MENOR A LOS 10 C, ;TIEMPO DE SECADO EN RANGOS DE TEMPERATURA DE 10 C DEL SUSTRATO 2 MINUTOS, Y NO MAS DE 10 MINUTOS CUANDO EL SUSTRATO OSCILA ALREDEDOR DE 54C, TRAZO, ENMASCARILLADO, MANO DE OBRA, LIMPIEZA PREVIA Y FINAL DE SUPERFICIE, EQUIPO NECESARIO PARA SU EJECUCIÓN, Y TODO LO NECESARIO PARA SU CORRECTA EJECUCIÓN, TRABAJO TERMINADO.	ML	1118	$85.98	$96,125.64

AP

PRESUPUESTO MODIFICADO

Obra: OBRA COMPLEMENTARIA Y SEÑALIZACIÓN BLVD. MIGUEL DE LA MADRID (CALZADA ORIENTE)

Ubicación: TRAMO: ENTRE CALLE GRANEROS Y ACCESO A TERZETTO, AGUASCALIENTES Mpio.

Contratista: JAIME VALDIVIA CONSTRUCCIONES, S.A. DE C.V. (503)

No.	Concepto	Unidad	Cantidad	Precio Unitario	Importe Total
	GRUPO: **OBRA COMPLEMENTARIA Y SEÑALIZACION**				
	PARTIDA: **SEÑALIZACION HORIZONTAL**				
	SUMINISTRO Y APLICACIÓN DE PINTURA TERMOPLASTICA ALQUIDALICA DE 120 MILESIMAS DE " (in) EN RAYA CANALIZADORA CLASIFICACIÓN M - 5, PARA INDICAR ENTRADA Y SALIDA EN BIFURCACIONES, COLOR BLANCO O AMARILLO, REFLEJANTE CON MICRO ESFERA DE VIDRIO EN PROPORCIÓN SEGÚN MANUAL DE SEÑALIZACIÓN VIAL Y DISPOSITIVOS DE SEGURIDAD SICT (S.C.T). DE 0.20 MTS DE ANCHO DE LONGITUD Y TRAZO VARIABLE (SEGUN PROYECTO), INCLUYE: MATERIALES Y ESPECIFICACIONES QUE CUMPLAN CON LA NORMATIVA N-CMT-5-01-001/13, N-PRY-CAR-10-01-002/13 APLICADAS AL DIA DE HOY, MATERIAL APLICADO EN SU ESTADO DE FUSION A UNA TEMPERATURA MINIMA DE 204 C, LA SUPERFICIE DE CONCRETO O ASFALTO NO DEBE PRESENTAR UNA TEMPERATURA MENOR A LOS 10 C, ;TIEMPO DE SECADO EN RANGOS DE TEMPERATURA DE 10 C DEL SUSTRATO 2 MINUTOS, Y NO MAS DE 10 MINUTOS CUANDO EL SUSTRATO OSCILA ALREDEDOR DE 54C, TRAZO, ENMASCARILLADO, MANO DE OBRA, LIMPIEZA PREVIA Y FINAL DE SUPERFICIE, EQUIPO NECESARIO PARA SU EJECUCIÓN, Y TODO LO NECESARIO PARA SU CORRECTA EJECUCIÓN, TRABAJO TERMINADO.	ML	70	$108.59	$7,601.30
	SUMINISTRO Y APLICACIÓN DE PINTURA TERMOPLASTICA ALQUIDALICA DE 120 MILESIMAS DE " (in) EN RAYA DE ALTO CLASIFICACIÓN M - 6, PARA INDICAR ALTO EN CRUCEROS, COLOR BLANCO, REFLEJANTE CON MICRO ESFERA DE VIDRIO EN PROPORCIÓN SEGÚN MANUAL DE SEÑALIZACIÓN VIAL Y DISPOSITIVOS DE SEGURIDAD SICT (S.C.T). DE 0.60 MTS DE ANCHO DE LONGITUD VARIABLE, INCLUYE: MATERIALES Y ESPECIFICACIONES QUE CUMPLAN CON LA NORMATIVA N-CMT-5-01-001/13, N-PRY-CAR-10-01-002/13 APLICADAS AL DIA DE HOY, MATERIAL APLICADO EN SU ESTADO DE FUSION A UNA TEMPERATURA MINIMA DE 204 C, LA SUPERFICIE DE CONCRETO O ASFALTO NO DEBE PRESENTAR UNA TEMPERATURA MENOR A LOS 10 C, ;TIEMPO DE SECADO EN RANGOS DE TEMPERATURA DE 10 C DEL SUSTRATO 2 MINUTOS, Y NO MAS DE 10 MINUTOS CUANDO EL SUSTRATO OSCILA ALREDEDOR DE 54C, TRAZO, ENMASCARILLADO, MANO DE OBRA, LIMPIEZA PREVIA Y FINAL DE SUPERFICIE, EQUIPO NECESARIO PARA SU EJECUCIÓN, Y TODO LO NECESARIO PARA SU CORRECTA EJECUCIÓN, TRABAJO TERMINADO.	ML	10	$455.75	$4,557.50
)	SUMINISTRO Y APLICACIÓN DE PINTURA TERMOPLASTICA ALQUIDALICA DE 120 MILESIMAS DE " (in) EN RAYA PARA CRUCE PEATONAL CLASIFICACIÓN M - 7.1, PARA INDICAR " CRUCE PEATONAL EN VIAS PRIMARIAS", COLOR AMARILLO, REFLEJANTE CON MICRO ESFERA DE VIDRIO EN PROPORCIÓN SEGÚN MANUAL DE SEÑALIZACIÓN VIAL Y DISPOSITIVOS DE SEGURIDAD SICT (S.C.T). DE 0.40 MTS DE ANCHO Y 3.5 MTS. DE LONGITUD POR EL ANCHO DE LA VIALIDAD, CON UNA SEPARACIÓN DE 0.40 MTS. ENTRE ELLAS, INCLUYE: MATERIALES Y ESPECIFICACIONES QUE CUMPLAN CON LA NORMATIVA N-CMT-5-01-001/13, N-PRY-CAR-10-01-002/13 APLICADAS AL DIA DE HOY, MATERIAL APLICADO EN SU ESTADO DE FUSION A UNA TEMPERATURA MINIMA DE 204 C, LA SUPERFICIE DE CONCRETO O ASFALTO NO DEBE PRESENTAR UNA TEMPERATURA MENOR A LOS 10 C, ;TIEMPO DE SECADO EN RANGOS DE TEMPERATURA DE 10 C DEL SUSTRATO 2 MINUTOS, Y NO MAS DE 10 MINUTOS CUANDO EL SUSTRATO OSCILA ALREDEDOR DE 54C, TRAZO, ENMASCARILLADO, MANO DE OBRA, LIMPIEZA PREVIA Y FINAL DE SUPERFICIE, EQUIPO NECESARIO PARA SU EJECUCIÓN, Y TODO LO NECESARIO PARA SU CORRECTA EJECUCIÓN, TRABAJO TERMINADO.	M2	15.4	$963.69	$14,840.83

Obra: OBRA COMPLEMENTARIA Y SEÑALIZACIÓN BLVD. MIGUEL DE LA MADRID (CALZADA ORIENTE)

Ubicación: TRAMO: ENTRE CALLE GRANEROS Y ACCESO A TERZETTO, AGUASCALIENTES Mpio.

Contratista: JAIME VALDIVIA CONSTRUCCIONES, S.A. DE C.V. (503)

No.	Concepto	Unidad	Cantidad	Precio Unitario	Importe Total
	GRUPO: OBRA COMPLEMENTARIA Y SEÑALIZACION				
	PARTIDA: SEÑALIZACION HORIZONTAL				
1	SUMINISTRO Y APLICACIÓN DE PINTURA TERMOPLASTICA ALQUIDALICA DE 120 MILESIMAS DE " (in) EN RAYA LOGARITMICA CLASIFICACIÓN M - 9, PARA INDICAR REDUCCION DE VELOCIDAD, COLOR BLANCO, REFLEJANTE CON MICRO ESFERA DE VIDRIO EN PROPORCIÓN SEGÚN MANUAL DE SEÑALIZACIÓN VIAL Y DISPOSITIVOS DE SEGURIDAD SICT (S.C.T). DE 0.60 MTS DE ANCHO DE LONGITUD VARIABLE, ESPACIADAS SEGUN PROYECTO Y/O TABLA III.2-3 DEL MANUAL DE SEÑALIZACIÓN VIAL Y DISPOSITIVOS DE SEGURIDAD DE LA SICT (SCT) INCLUYE: MATERIALES Y ESPECIFICACIONES QUE CUMPLAN CON LA NORMATIVA N-CMT-5-01-001/13, N-PRY-CAR-10-01-002/13 APLICADAS AL DIA DE HOY, MATERIAL APLICADO EN SU ESTADO DE FUSION A UNA TEMPERATURA MINIMA DE 204 C, LA SUPERFICIE DE CONCRETO O ASFALTO NO DEBE PRESENTAR UNA TEMPERATURA MENOR A LOS 10 C, ;TIEMPO DE SECADO EN RANGOS DE TEMPERATURA DE 10 C DEL SUSTRATO 2 MINUTOS, Y NO MAS DE 10 MINUTOS CUANDO EL SUSTRATO OSCILA ALREDEDOR DE 54C, TRAZO, ENMASCARILLADO, MANO DE OBRA, LIMPIEZA PREVIA Y FINAL DE SUPERFICIE, EQUIPO NECESARIO PARA SU EJECUCIÓN, Y TODO LO NECESARIO PARA SU CORRECTA EJECUCIÓN, TRABAJO TERMINADO.	ML	221	$455.75	$100,720.75
2	SUMINISTRO Y APLICACIÓN DE PINTURA TERMOPLASTICA ALQUIDALICA DE 120 MILESIMAS DE " (in) EN FLECHAS CLASIFICACIÓN M - 11.1, "FLECHA SENCILLA" PARA INDICAR SENTIDO DE CIRCULACIÓN , EN VIALIDADES PARA VELOCIDAD MENOR A 60KM POR HORA DIMENSION NORMATIVA SEGUN MANUAL DE SEÑALIZACIÓN VIAL Y DISPOSITIVOS DE SEGURIDAD SICT (SCT) Y/O (VER PLANO DE SEÑALAMIENTOS), COLOR BLANCO, REFLEJANTE CON MICRO ESFERA DE VIDRIO EN PROPORCIÓN SEGÚN NORMA SCT, INCLUYE: MATERIALES Y ESPECIFICACIONES QUE CUMPLAN CON LA NORMATIVA N-CMT-5-01-001/13, N-PRY-CAR-10-01-002/13 APLICADAS AL DIA DE HOY, MATERIAL APLICADO EN SU ESTADO DE FUSION A UNA TEMPERATURA MINIMA DE 204 C, LA SUPERFICIE DE CONCRETO O ASFALTO NO DEBE PRESENTAR UNA TEMPERATURA MENOR A LOS 10 C, ;TIEMPO DE SECADO EN RANGOS DE TEMPERATURA DE 10 C DEL SUSTRATO 2 MINUTOS, Y NO MAS DE 10 MINUTOS CUANDO EL SUSTRATO OSCILA ALREDEDOR DE 54C, TRAZO, ENMASCARILLADO, MANO DE OBRA, LIMPIEZA PREVIA Y FINAL DE SUPERFICIE, EQUIPO NECESARIO PARA SU EJECUCIÓN, Y TODO LO NECESARIO PARA SU CORRECTA EJECUCIÓN, TRABAJO TERMINADO.	PZA	15	$1,203.65	$18,054.75
4	SUMINISTRO Y APLICACIÓN DE PINTURA TERMOPLASTICA ALQUIDALICA DE 120 MILESIMAS DE " (in) EN LETRAS Y NUMEROS CLASIFICACIÓN M - 11.1 "LETRAS Y NUMEROS" EN VIALIDADES PARA VELOCIDAD MENOR A 60KM POR HORA SEGUN MANUAL DE SEÑALIZACIÓN VIAL Y DISPOSITIVOS DE SEGURIDAD SICT (SCT), (VER PLANO DE SEÑALAMIENTOS) EN COLOR BLANCO, REFLEJANTE CON MICRO ESFERA DE VIDRIO EN PROPORCIÓN SEGÚN NORMA SCT DE (VER DETALLES EN PLANOS) INCLUYE: MATERIALES Y ESPECIFICACIONES QUE CUMPLAN CON LA NORMATIVA N-CMT-5-01-001/13, N-PRY-CAR-10-01-002/13 APLICADAS AL DIA DE HOY, MATERIAL APLICADO EN SU ESTADO DE FUSION A UNA TEMPERATURA MINIMA DE 204 C, LA SUPERFICIE DE CONCRETO O ASFALTO NO DEBE PRESENTAR UNA TEMPERATURA MENOR A LOS 10 C, ;TIEMPO DE SECADO EN RANGOS DE TEMPERATURA DE 10 C DEL SUSTRATO 2 MINUTOS, Y NO MAS DE 10 MINUTOS CUANDO EL SUSTRATO OSCILA ALREDEDOR DE 54C, TRAZO, ENMASCARILLADO, MANO DE OBRA, LIMPIEZA PREVIA Y FINAL DE SUPERFICIE, EQUIPO NECESARIO PARA SU EJECUCIÓN, Y TODO LO NECESARIO PARA SU CORRECTA EJECUCIÓN, TRABAJO TERMINADO.	PZA	72	$732.14	$52,714.08

A.P.

Obra: OBRA COMPLEMENTARIA Y SEÑALIZACIÓN BLVD. MIGUEL DE LA MADRID (CALZADA ORIENTE)

Ubicación: TRAMO: ENTRE CALLE GRANEROS Y ACCESO A TERZETTO, AGUASCALIENTES Mpio.

Contratista: JAIME VALDIVIA CONSTRUCCIONES, S.A. DE C.V. (503)

No.	Concepto	Unidad	Cantidad	Precio Unitario	Importe Total
	GRUPO: **OBRA COMPLEMENTARIA Y SEÑALIZACION**				
	PARTIDA: **SEÑALIZACION HORIZONTAL**				
5	SUMINISTRO Y COLOCACIÓN DE VIALETA STANDARD (S-200) DE 10X10CM. COLOR: CUERPO AMARILLO Y/O BLANCO Y REFLEJANTE AMARILLO 1 CARA MARCA SEA O SIMILAR EN CALIDAD Y ESPECIFICACIONES DE FICHA TÉCNICA, FIJADO EN PAVIMENTO CON SISTEMA DE SUJECIÓN DE ALTO AGARRE PEGAMENTO EPOXICO 100 A/B (RESINA EPÓXICA/RESINA POLIAMIDA MODIFICADA), RESISTENTE A ALTA TEMPERATURA (VER PLANO DE DETALLES DE SEÑALAMIENTOS HORIZONTAL), INCLUYE: LIMPIEZA PREVIA Y FINAL DE LA SUPERFICIE, PREPARACIÓN DE LA SUPERFICIE, TRAZO, ALINEACIÓN, Y TODO LO NECESARIO PARA SU CORRECTA EJECUCIÓN, TRABAJO TERMINADO.	PZA	409	$99.42	$40,662.78
6	SUMINISTRO Y COLOCACION DE VIALETA SOLAR DE 10X10CM. COLOR: CUERPO ALUMINIO 3 LED DOS CARAS REFLEJANTES MARCA CREATIVAL VT-29 O SIMILAR EN CALIDAD Y ESPECIFICACIONES DE FICHA TÉCNICA, FIJADO EN PAVIMENTO CON SISTEMA DE SUJECIÓN DE ALTO AGARRE PEGAMENTO EPOXICO 100 A/B (RESINA EPÓXICA/RESINA POLIAMIDA MODIFICADA), RESISTENTE A ALTA TEMPERATURA (VER PLANO DE DETALLES DE SEÑALAMIENTOS HORIZONTAL), INCLUYE: LIMPIEZA PREVIA Y FINAL DE LA SUPERFICIE+C92, PREPARACIÓN DE LA SUPERFICIE, TRAZO, ALINEACIÓN, Y TODO LO NECESARIO PARA SU CORRECTA EJECUCIÓN, TRABAJO TERMINADO.	PZA	131	$727.20	$95,263.20
7	SUMINISTRO Y COLOCACION DE BOYA DE PLASTICO OJO DE GATO (VT-38), MARCA CREATIVAL O SIMILAR EN CALIDAD Y PRECIO, CON REFLEJANTE COLOR BLANCO, GRADO ALTA INTENSIDAD, FIJACION A SUPERFICIE CON CLAVOS DE ACERO ALTA RESISTENCIA, INCLUYE: MATERIAL, MANO DE OBRA, HERRAMIENTA, ELEMENTOS DE FIJACION, ALINEADO, LIMPIEZAS Y TODO LO NECESARIO PARA SU CORRECTA EJEUCION, TRABAJO TERMINADO.	PZA	97	$283.37	$27,486.89
8	SUMINISTRO Y COLOCACIÓN DE BOTON DH-3 CERAMICO DE ALTA RESISTENCIA COLOR BLANCO, SEGÚN NORMA SCT. INCLUYE: MATERIAL, MANO DE OBRA, LIMPIEZA DE LA SUPERFICIE, ANCLADO A PAVIMENTO, ELEMENTOS DE SUJECION Y PEGAMENTO, ACARREOS DENTRO DE LA OBRA, LIMPIEZAS Y TODO LO NECESARIO PARA SU CORRECTA EJECUCION.	PZA	2867	$102.14	$292,835.38
				Totales por Partida	**$1,069,151.58**
	PARTIDA: **SEÑALIZACION VERTICAL**				
9	SUMINISTRO Y COLOCACION DE SEÑALAMIENTO VERTICAL DE RESTRICCION SR-9 (VELOCIDAD MAXIMA), DISEÑO NORMATIVO SCT, HECHO A ABASE DE LAMINA GALVANIZADA CON CEJA DE 72 X 72 CM CALIBRE 16, CON TERMINADO GRADO INGENIERIA EN SU TOTALIDAD, EL COLOR SERA REFLEJANTE GRADO INGENIERIA Y SIMBOLOS EN COLOR REFLEJANTE, TODOS LOS COLORES RESISTENTES A LA INTEMPERIE, FIJADA MEDIANTE BARRENADO Y TORNILLOS DE 2 1/2" X 5/16" A UN POSTE DE PTR DE 2 X 2" CALIBRE 14 EN ACABADO GALVANIZADO Y CON UNA ALTURA DE 2.5 MTS AL NIVEL DE BANQUETA A LA PARTE INFERIOR DE LA LAMINA MAS EL EXCEDENTE REQUERIDO PARA FIJAR LAS LAMINAS Y ANCLADO DE 50 CM DE PROFUNDIDAD CON ANGULO TRANSVERSAL DE 1 X 1" DE 25 CM, EN DADO DE CONCRETO F´c=150 KG/CM2 DE 30 CM DE LADO (VER PLANO DE DETALLES CRITERIOS DE ANCLAJE DE SEÑALAMIENTO VERTICAL, DETALLE SEÑ-02 Y SEÑ 03), MCA ASEA O SIMILAR EN CALIDAD Y ESPECIFICACIONES, INCLUYE: MANO DE OBRA, FLETES, MANIOBRAS LIMPIEZAS Y RETIRO DEL SOBRANTE FUERA DE LA OBRA HASTA TIRADERO OFICIAL, TRABAJO TERMINADO.	PZA	7	$2,563.99	$17,947.93
				Totales por Partida	**$17,947.93**
				Totales por Grupo	**$1,087,099.51**

A P

PRESUPUESTO MODIFICADO

Obra: OBRA COMPLEMENTARIA Y SEÑALIZACIÓN BLVD. MIGUEL DE LA MADRID (CALZADA ORIENTE)

Ubicación: TRAMO: ENTRE CALLE GRANEROS Y ACCESO A TERZETTO, AGUASCALIENTES Mpio.

Contratista: JAIME VALDIVIA CONSTRUCCIONES, S.A. DE C.V. (503)

No.	Concepto	Unidad	Cantidad	Precio Unitario	Importe Total
GRUPO: EXTRAORDINARIO					
PARTIDA: EXTRAORDINARIOS					
26	RENIVELACION DE POZO DE VISITA DE HASTA 0.25 M A BASE DE TABIQUE ROJO RECOCIDO JUNTEADO CON MORTERO Y LOSA DE CONCRETO PREMEZCLADO MR=45 RR3D, ARMADO CON VARILLA DE 3/8" @ 10 CM EN AMBOS SENTIDOS DE 1.50 X 1.50M Y 15 CM DE ESPESOR CON RECUPERACION DE BROCAL, INCLUYE: 4 CORTES DEL PERIMETROCON CORTADORA DE DISCO PARA DEMOLICION DE LOSA EXISTENTE, DEMOLICION DEL PAVIMENTO EXISTENTE RETIRANDO EL MATERIAL FUERA DE LA OBRA, 4 CORTES DE LOSA DE DIAMANTE PARA JUNTAS DE DILATACION, CURADO CON CURADOR BASE AGUA Y SELLADO	PZA	5	$6,649.30	$33,246.50
27	RENIVELACION DE CAJA DE VALVULA DE 1.60X1.6 M Y HASTA 0.25M A BASE DE MURO DE TABIQUE ROJO RECOCIDO JUNTEADO CON MORTERO 1:3 ENJARRADO Y PULIDO, LOSA DE 1.6 X 1.60M Y 0.15 M DE ESPESOR, COLADA CON CONCRETO PREMEZCLADO MR=45 RR3D, ARMADA CON VRS DE 3/8"@10CM EN AMBOS SENTIDOS, CONTRAMARCO Y TAPA CON RECUPERACION, INCLUYE: LIMPIA, TRAZO, 4 CORTES PARA DEMOLICION, DEMOLICION, CARGA Y ACARREO DEL MATERIAL PRODUCTO DE LA DEMOLICION, CIMBRA MUERTA DE MADERA, CURADO, 4 CORTES PARA JUNTA DE DILATACION Y SELLADO.	PZA	1	$7,406.34	$7,406.34
28	RENIVELACION DE CAJA DE VALVULA DE 1.60X1.6 M Y HASTA 0.25M A BASE DE MURO EN FORMA CILINDRICA DE TABIQUE ROJO RECOCIDO JUNTEADO CON MORTERO 1:3 ENJARRADO Y PULIDO, LOSA DE 1.6 X 1.60M Y 0.15 M DE ESPESOR, COLADA CON CONCRETO PREMEZCLADO MR=45 RR3D, ARMADA CON VRS DE 3/8"@10CM EN AMBOS SENTIDOS, CONTRAMARCO Y TAPA CON RECUPERACION, INCLUYE: LIMPIA, TRAZO, 4 CORTES PARA DEMOLICION, DEMOLICION, CARGA Y ACARREO DEL MATERIAL PRODUCTO DE LA DEMOLICION, CIMBRA MUERTA DE MADERA, CURADO, 4 CORTES PARA JUNTA DE DILATACION Y SELLADO.	PZA	1	$7,034.66	$7,034.66
29	SUMINISTRO Y APLICACIÓN DE PINTURA TERMOPLASTICA ALQUIDALICA DE 120 MILESIMAS DE " (in) EN FLECHAS, "FLECHA RETORNO " PARA INDICAR VUELTA EN RETORNO CON MEDIDA DE 5 MTS, SEÑALIZACIÓN VIAL Y DISPOSITIVOS DE SEGURIDAD SICT (SCT) COLOR BLANCO, REFLEJANTE CON MICRO ESFERA DE VIDRIO EN PROPORCIÓN SEGÚN NORMA SCT, INCLUYE: MATERIALES Y ESPECIFICACIONES QUE CUMPLAN CON LA NORMATIVA N-CMT-5-01-001/13, N-PRY-CAR-10-01-002/13 APLICADAS AL DIA DE HOY, MATERIAL APLICADO EN SU ESTADO DE FUSION A UNA TEMPERATURA MINIMA DE 204 C, LA SUPERFICIE DE CONCRETO O ASFALTO NO DEBE PRESENTAR UNA TEMPERATURA MENOR A LOS 10 C, ;TIEMPO DE SECADO EN RANGOS DE TEMPERATURA DE 10 C DEL SUSTRATO 2 MINUTOS, Y NO MAS DE 10 MINUTOS CUANDO EL SUSTRATO OSCILA ALREDEDOR DE 54C, TRAZO, ENMASCARILLADO, MANO DE OBRA, LIMPIEZA PREVIA Y FINAL DE SUPERFICIE, EQUIPO NECESARIO PARA SU EJECUCIÓN, Y TODO LO NECESARIO PARA SU CORRECTA EJECUCIÓN, TRABAJO TERMINADO.	PZA	1	$1,516.41	$1,516.41

AP

Obra: **OBRA COMPLEMENTARIA Y SEÑALIZACIÓN BLVD. MIGUEL DE LA MADRID (CALZADA ORIENTE)**

Ubicación: **TRAMO: ENTRE CALLE GRANEROS Y ACCESO A TERZETTO, AGUASCALIENTES Mpio.**

Contratista: **JAIME VALDIVIA CONSTRUCCIONES, S.A. DE C.V. (503)**

No.	Concepto	Unidad	Cantidad	Precio Unitario	Importe Total
GRUPO: **EXTRAORDINARIO**					
PARTIDA: **EXTRAORDINARIOS**					
30	SUMINISTRO Y APLICACIÓN DE PINTURA TERMOPLASTICA ALQUIDALICA DE 120 MILESIMAS DE " (in) EN RAYA PARA CRUCE DE CICLOVIA, PARA INDICAR " CICLOVIA", COLOR VERDE, REFLEJANTE CON MICRO ESFERA DE VIDRIO EN PROPORCIÓN SEGÚN MANUAL DE SEÑALIZACIÓN VIAL Y DISPOSITIVOS DE SEGURIDAD SICT (S.C.T). DE 0.40 MTS DE ANCHO Y 1.00 MTS. DE LONGITUD APROXIMADO YA QUE PODRIA VARIAR POR ENCHO DE CICLOVIA, CON UNA SEPARACIÓN DE 0.40 MTS. ENTRE ELLAS, INCLUYE: MATERIALES Y ESPECIFICACIONES QUE CUMPLAN CON LA NORMATIVA N-CMT-5-01-001/13, N-PRY-CAR-10-01-002/13 APLICADAS AL DIA DE HOY, MATERIAL APLICADO EN SU ESTADO DE FUSION A UNA TEMPERATURA MINIMA DE 204 C, LA SUPERFICIE DE CONCRETO O ASFALTO NO DEBE PRESENTAR UNA TEMPERATURA MENOR A LOS 10 C, ;TIEMPO DE SECADO EN RANGOS DE TEMPERATURA DE 10 C DEL SUSTRATO 2 MINUTOS, Y NO MAS DE 10 MINUTOS CUANDO EL SUSTRATO OSCILA ALREDEDOR DE 54C, TRAZO, ENMASCARILLADO, MANO DE OBRA, LIMPIEZA PREVIA Y FINAL DE SUPERFICIE, EQUIPO NECESARIO PARA SU EJECUCIÓN, Y TODO LO NECESARIO PARA SU CORRECTA EJECUCIÓN, TRABAJO TERMINADO.	M2	239.6776042	$977.00	$234,165.02
31	SUMINISTRO Y APLICACIÓN DE PINTURA TERMOPLASTICA ALQUIDALICA DE 120 MILESIMAS DE " (in) EN TAPETE DE CICLOVIA, PARA INDICAR " CICLOVIA", COLOR VERDE, REFLEJANTE CON MICRO ESFERA DE VIDRIO EN PROPORCIÓN SEGÚN MANUAL DE SEÑALIZACIÓN VIAL Y DISPOSITIVOS DE SEGURIDAD SICT (S.C.T). DE 1.0 MTS DE ANCHO Y 0.60 MTS. DE LONGITUD APROXIMADO YA QUE PODRIA VARIAR POR ENCHO DE CICLOVIA, INCLUYE: MATERIALES Y ESPECIFICACIONES QUE CUMPLAN CON LA NORMATIVA N-CMT-5-01-001/13, N-PRY-CAR-10-01-002/13 APLICADAS AL DIA DE HOY, MATERIAL APLICADO EN SU ESTADO DE FUSION A UNA TEMPERATURA MINIMA DE 204 C, LA SUPERFICIE DE CONCRETO O ASFALTO NO DEBE PRESENTAR UNA TEMPERATURA MENOR A LOS 10 C, ;TIEMPO DE SECADO EN RANGOS DE TEMPERATURA DE 10 C DEL SUSTRATO 2 MINUTOS, Y NO MAS DE 10 MINUTOS CUANDO EL SUSTRATO OSCILA ALREDEDOR DE 54C, TRAZO, ENMASCARILLADO, MANO DE OBRA, LIMPIEZA PREVIA Y FINAL DE SUPERFICIE, EQUIPO NECESARIO PARA SU EJECUCIÓN, Y TODO LO NECESARIO PARA SU CORRECTA EJECUCIÓN, TRABAJO TERMINADO.	M2	153.95	$937.39	$144,311.19
32	SUMINISTRO Y APLICACIÓN DE LOGOTIPO BICICLETAS EN PINTURA BASE SOLVENTE COLOR BLANCO EN TAPETES DE CICLOVIA TAMAÑO DE 1.4 Y DISEÑO SEGÚN PLANOS Y PROYECTO, INCLUYE: TRAZO, ENMASCARILLADO, PLANTILLA, MANO DE OBRA, LIMPIEZA PREVIA Y FINAL DE LA SUPERFICIE, EQUIPO NECESARIO PARA SU EJECUCION, Y TODO LO NECESARIO PARA SU CORRECTA EJECUCION, TRABAJO TERMINADO.	PZA	22	$1,285.11	$28,272.42
33	SUMINISTRO Y APLICACIÓN DE NUMERO O LETRA EN PINTURA BASE SOLVENTE COLOR BLANCO EN TAPETES DE CICLOVIA TAMAÑO DE 0.50M Y DISEÑO SEGÚN PLANOS Y PROYECTO, INCLUYE: TRAZO, ENMASCARILLADO, PLANTILLA, MANO DE OBRA, LIMPIEZA PREVIA Y FINAL DE LA SUPERFICIE, EQUIPO NECESARIO PARA SU EJECUCION, Y TODO LO NECESARIO PARA SU CORRECTA EJECUCION, TRABAJO TERMINADO.	PZA	88	$1,075.42	$94,636.96
34	SUMINISTRO Y APLICACIÓN DE FLECHA EN PINTURA BASE SOLVENTE COLOR BLANCO EN TAPETES DE CICLOVIA TAMAÑO DE 2.0M Y DISEÑO SEGÚN PLANOS Y PROYECTO, INCLUYE: TRAZO, ENMASCARILLADO, PLANTILLA, MANO DE OBRA, LIMPIEZA PREVIA Y FINAL DE LA SUPERFICIE, EQUIPO NECESARIO PARA SU EJECUCION, Y TODO LO NECESARIO PARA SU CORRECTA EJECUCION, TRABAJO TERMINADO.	PZA	22	$582.70	$12,819.40

AP

Obra: OBRA COMPLEMENTARIA Y SEÑALIZACIÓN BLVD. MIGUEL DE LA MADRID (CALZADA ORIENTE)

Ubicación: TRAMO: ENTRE CALLE GRANEROS Y ACCESO A TERZETTO, AGUASCALIENTES Mpio.

Contratista: JAIME VALDIVIA CONSTRUCCIONES, S.A. DE C.V. (503)

No.	Concepto	Unidad	Cantidad	Precio Unitario	Importe Total
GRUPO: **EXTRAORDINARIO**					
PARTIDA: **EXTRAORDINARIOS**					
35	SUMINISTRO Y COLOCACION DE SEÑALAMIENTO VERTICAL DE BICICLETA, DISEÑO NORMATIVO SCT, HECHO A ABASE DE LAMINA GALVANIZADA CON CEJA DE 72 X 72 CM CALIBRE 16, CON TERMINADO GRADO INGENIERIA EN SU TOTALIDAD, EL COLOR SERA REFLEJANTE GRADO INGENIERIA Y SIMBOLOS EN COLOR REFLEJANTE, TODOS LOS COLORES RESISTENTES A LA INTEMPERIE, FIJADA MEDIANTE BARRENADO Y TORNILLOS DE 2 1/2" X 5/16" A UN POSTE DE PTR DE 2 X 2" CALIBRE 14 EN ACABADO GALVANIZADO Y CON UNA ALTURA DE 2.5 MTS AL NIVEL DE BANQUETA A LA PARTE INFERIOR DE LA LAMINA MAS EL EXCEDENTE REQUERIDO PARA FIJAR LAS LAMINAS Y ANCLADO DE 50 CM DE PROFUNDIDAD CON ANGULO TRANSVERSAL DE 1 X 1" DE 25 CM, EN DADO DE CONCRETO F´c=150 KG/CM2 DE 30 CM DE LADO (VER PLANO DE DETALLES CRITERIOS DE ANCLAJE DE SEÑALAMIENTO VERTICAL, DETALLE SEÑ-02 Y SEÑ 03), MCA ASEA O SIMILAR EN CALIDAD Y ESPECIFICACIONES, INCLUYE: MANO DE OBRA, FLETES, MANIOBRAS LIMPIEZAS Y RETIRO DEL SOBRANTE FUERA DE LA OBRA HASTA TIRADERO OFICIAL, TRABAJO TERMINADO.	PZA	5	$2,563.99	$12,819.95
36	SUMINISTRO Y COLOCACION DE SEÑALAMIENTO VERTICAL INFORMATIVO DE CURVA, DISEÑO NORMATIVO SCT, HECHO A ABASE DE LAMINA GALVANIZADA CON CEJA DE 72 X 72 CM CALIBRE 16, CON TERMINADO GRADO INGENIERIA EN SU TOTALIDAD, EL COLOR SERA REFLEJANTE GRADO INGENIERIA Y SIMBOLOS EN COLOR REFLEJANTE, TODOS LOS COLORES RESISTENTES A LA INTEMPERIE, FIJADA MEDIANTE BARRENADO Y TORNILLOS DE 2 1/2" X 5/16" A UN POSTE DE PTR DE 2 X 2" CALIBRE 14 EN ACABADO GALVANIZADO Y CON UNA ALTURA DE 2.5 MTS AL NIVEL DE BANQUETA A LA PARTE INFERIOR DE LA LAMINA MAS EL EXCEDENTE REQUERIDO PARA FIJAR LAS LAMINAS Y ANCLADO DE 50 CM DE PROFUNDIDAD CON ANGULO TRANSVERSAL DE 1 X 1" DE 25 CM, EN DADO DE CONCRETO F´c=150 KG/CM2 DE 30 CM DE LADO (VER PLANO DE DETALLES CRITERIOS DE ANCLAJE DE SEÑALAMIENTO VERTICAL, DETALLE SEÑ-02 Y SEÑ 03), MCA ASEA O SIMILAR EN CALIDAD Y ESPECIFICACIONES, INCLUYE: MANO DE OBRA, FLETES, MANIOBRAS LIMPIEZAS Y RETIRO DEL SOBRANTE FUERA DE LA OBRA HASTA TIRADERO OFICIAL, TRABAJO TERMINADO.	PZA	2	$2,563.99	$5,127.98
37	COLOCACION DE TOPE SEPARADOR DE CONCRETO Y/O PLASTICO, PARA DELIMITACION DE CICLOVIA, INCLUYE: RECOLECCIONES EN SITIO INDICADO POR SUPERVISION, TRASLADO A LA OBRA Y SU CORRECTA INSTALACION	PZA	100	$280.36	$28,036.00

Totales por Partida		**$609,392.83**
Totales por Grupo		**$609,392.83**
Totales Presup.		**$1,696,492.34**
Anticipo	**+**	**$508,947.71**
Amortizac. Ant.	**-**	**$508,947.71**
SubTotal. Ant.	**=**	**$1,696,492.35**
IVA	**+**	**$271,438.78**
Total	**=**	**$1,967,931.13**

AP

PRESUPUESTO MODIFICADO

Aguascalientes

bra: OBRA COMPLEMENTARIA Y SEÑALIZACIÓN BLVD. MIGUEL DE LA MADRID (CALZADA ORIENTE)

bicación: TRAMO: ENTRE CALLE GRANEROS Y ACCESO A TERZETTO, AGUASCALIENTES Mpio.

ontratista: JAIME VALDIVIA CONSTRUCCIONES, S.A. DE C.V. (503)

Grupo	Partida	Importe
BRA COMPLEMENTARIA Y SEÑALIZACION		
	SEÑALIZACION HORIZONTAL	$1,069,151.58
	SEÑALIZACION VERTICAL	$17,947.93
	Subtotal por Grupo	$1,087,099.51
XTRAORDINARIO		
	EXTRAORDINARIOS	$609,392.83
	Subtotal por Grupo	$609,392.83

Totales Presup.		$1,696,492.34
Anticipo	+	$508,947.71
Amortizac. Ant.	-	$508,947.71
SubTotal. Ant.	=	$1,696,492.35
IVA	+	$271,438.78
Total	=	$1,967,931.13

PRESUPUESTO MODIFICADO

Obra: OBRA COMPLEMENTARIA Y SEÑALIZACIÓN BLVD. MIGUEL DE LA MADRID (CALZADA ORIENTE)

Ubicación: TRAMO: ENTRE CALLE GRANEROS Y ACCESO A TERZETTO, AGUASCALIENTES Mpio.

Contratista: JAIME VALDIVIA CONSTRUCCIONES, S.A. DE C.V. (503)

Grupo	Partida		Importe
OBRA COMPLEMENTARIA Y SEÑALIZACION			
	SEÑALIZACION HORIZONTAL		$1,069,151.58
	SEÑALIZACION VERTICAL		$17,947.93
		Subtotal por Grupo	$1,087,099.51
EXTRAORDINARIO			
	EXTRAORDINARIOS		$609,392.83
		Subtotal por Grupo	$609,392.83
		Totales Presup.	$1,696,492.34
		Anticipo +	$508,947.71
		Amortizac. Ant. -	$508,947.71
		SubTotal. Ant. =	$1,696,492.35
		IVA +	$271,438.78
		Total =	$1,967,931.13

MODIFICADO 1

SECRETARÍA DE OBRAS PÚBLICAS

DIRECCIÓN DE SUPERVISIÓN DE OBRA

EJERCICIO 2022

N° DE CONTRATO: FISMDF-0082-2022

NOMBRE DE LA OBRA: OBRA COMPLEMENTARIA Y SEÑALIZACIÓN BLVD. MIGUEL DE LA MADRID (CALZADA ORIENTE), TRAMO: ENTRE CALLE GRANEROS Y ACCESO A TERZETTO, AGUASCALIENTES Mpio.

MONTO MODIFICADO FINAL: $ 2,699,890.64

VOLUMEN	UNIDAD	COMPONENTE DE LA OBRA	MONTO
2867.00	PZA	SUMINISTRO Y COLOCACIÓN DE BOTON DH-3 CERAMICO DE ALTA RESISTENCIA COLOR BLANCO, SEGÚN NORMA SCT. INCLUYE:	$ 1,069,151.58
7.00	PZA	SUMINISTRO Y COLOCACION DE SEÑALAMIENTO VERTICAL DE RESTRICCION SR-9 (VELOCIDAD MAXIMA), DISEÑO NORMATIVO SCT,	$ 17,947.93
239.68	M2	SUMINISTRO Y APLICACIÓN DE PINTURA TERMOPLASTICA ALQUIDALICA DE 120 MILESIMAS	$ 609,392.83

TOTAL PRESUP.	$	1,696,492.34
IVA	$	271,438.78
TOTAL	$	1,967,931.13

AP

NOMBRE DEL SUPERVISOR: ALICIA PEÑA ACERO

H. AYUNTAMIENTO DE AGUASCALIENTES
SECRETARÍA DE OBRAS PÚBLICAS
DIRECCIÓN DE SUPERVISIÓN DE OBRA

Aguascalientes
LA CIUDAD DE TU VIDA


MEMORIA FOTOGRAFICA


OBRA: OBRA COMPLEMENTARIA Y SEÑALIZACIÓN BLVD. MIGUEL DE LA MADRID (CALZADA ORIENTE).
UBICACIÓN: TRAMO: ENTRE CALLE GRANEROS Y ACCESO A TERZETTO, AGUASCALIENTES Mpio.
CONTRATISTA: JAIME VALDIVIA CONSTRUCCIONES, S.A. DE C.V.


NO. DE CONTRATO: FISMDF-0082-2022
LOCALIDAD: AGS

INICIO



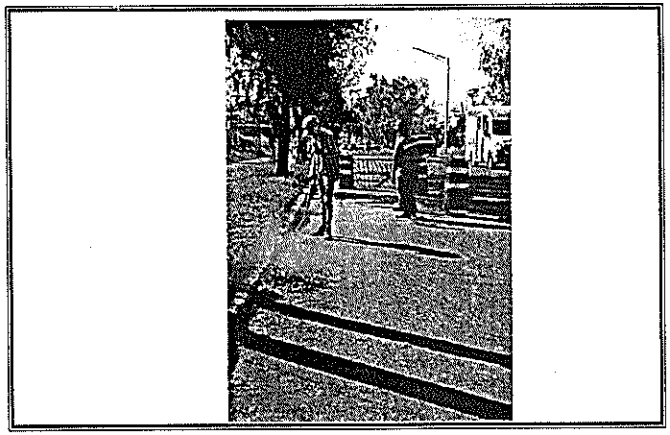

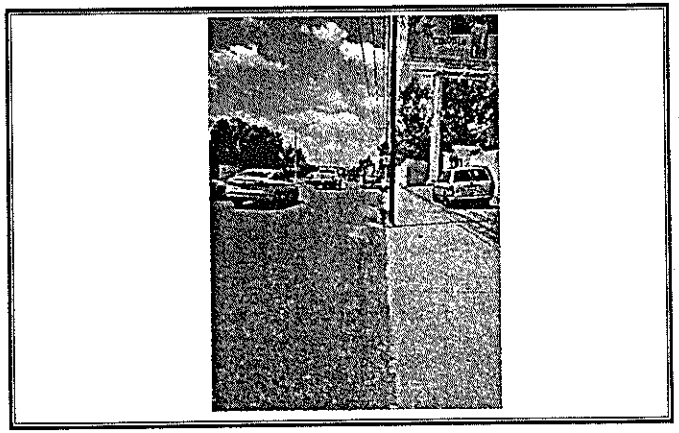

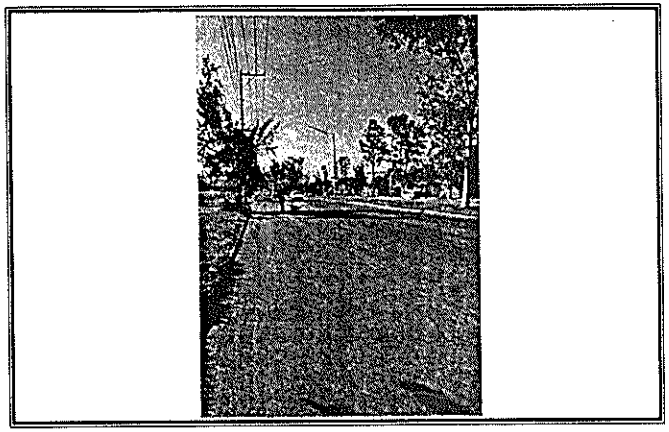

AO
ALICIA PEÑA ACERO

H. AYUNTAMIENTO DE AGUASCALIENTES
SECRETARÍA DE OBRAS PÚBLICAS
DIRECCIÓN DE SUPERVISIÓN DE OBRA

Aguascalientes
LA CIUDAD DE TU VIDA


MEMORIA FOTOGRAFICA


OBRA: OBRA COMPLEMENTARIA Y SEÑALIZACIÓN BLVD. MIGUEL DE LA MADRID (CALZADA ORIENTE).
UBICACIÓN: TRAMO: ENTRE CALLE GRANEROS Y ACCESO A TERZETTO, AGUASCALIENTES Mpio.
CONTRATISTA: JAIME VALDIVIA CONSTRUCCIONES, S.A. DE C.V.

NO. DE CONTRATO: FISMDF-0082-2022
LOCALIDAD: AGS

PROCESO



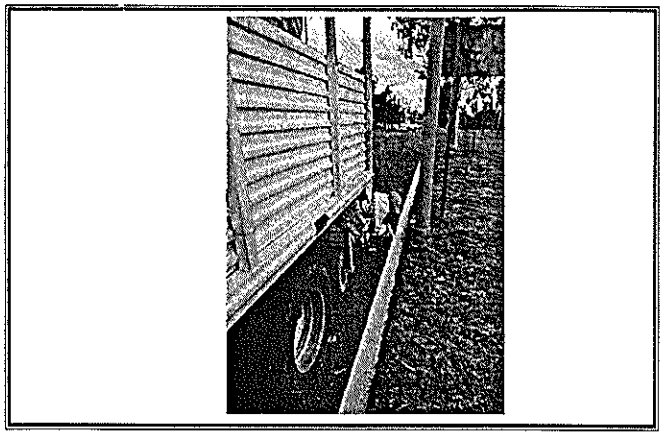

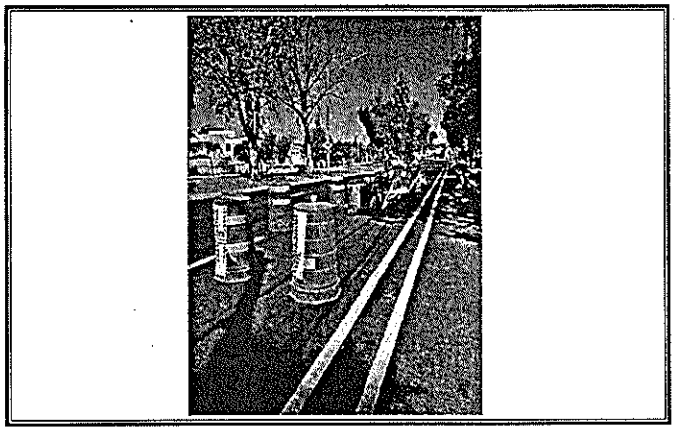



AP.
ALICIA PEÑA ACERO

H. AYUNTAMIENTO DE AGUASCALIENTES
SECRETARÍA DE OBRAS PÚBLICAS
DIRECCIÓN DE SUPERVISIÓN DE OBRA


Aguascalientes
LA CIUDAD DE TU VIDA


MEMORIA FOTOGRAFICA


OBRA: OBRA COMPLEMENTARIA Y SEÑALIZACIÓN BLVD. MIGUEL DE LA MADRID (CALZADA ORIENTE).
UBICACIÓN: TRAMO: ENTRE CALLE GRANEROS Y ACCESO A TERZETTO, AGUASCALIENTES Mpio.
CONTRATISTA: JAIME VALDIVIA CONSTRUCCIONES, S.A. DE C.V.


NO. DE CONTRATO: FISMDF-0082-2022
LOCALIDAD: AGS

TERMINO

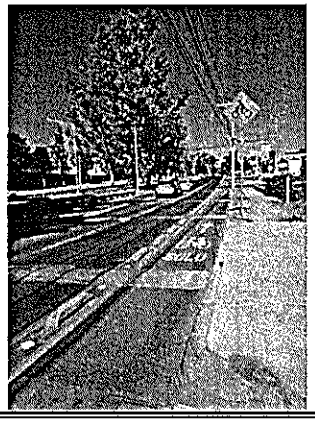


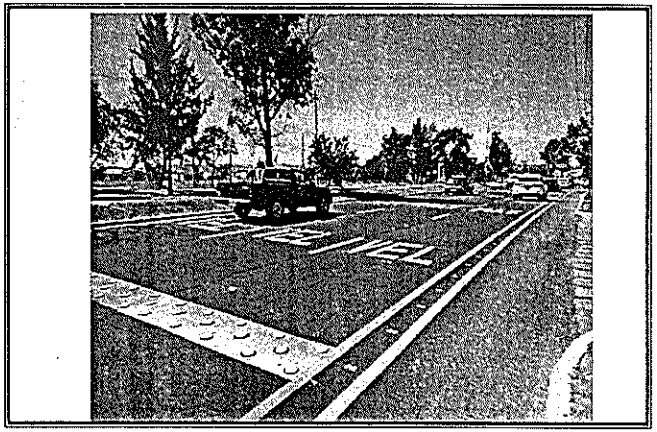


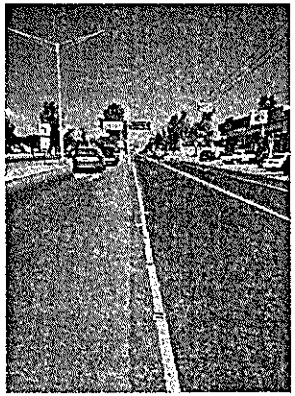

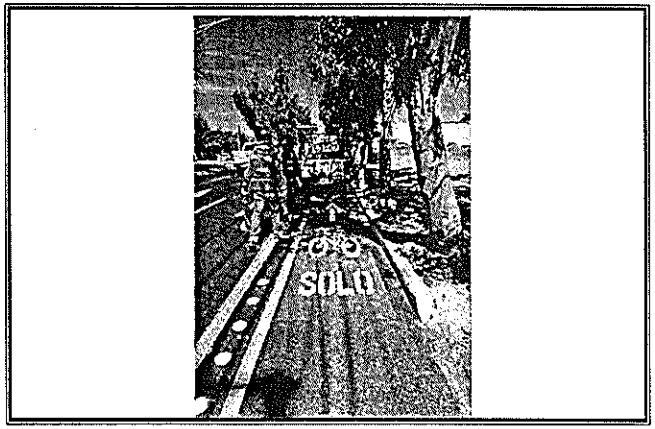

AP
ALICIA PEÑA ACERO

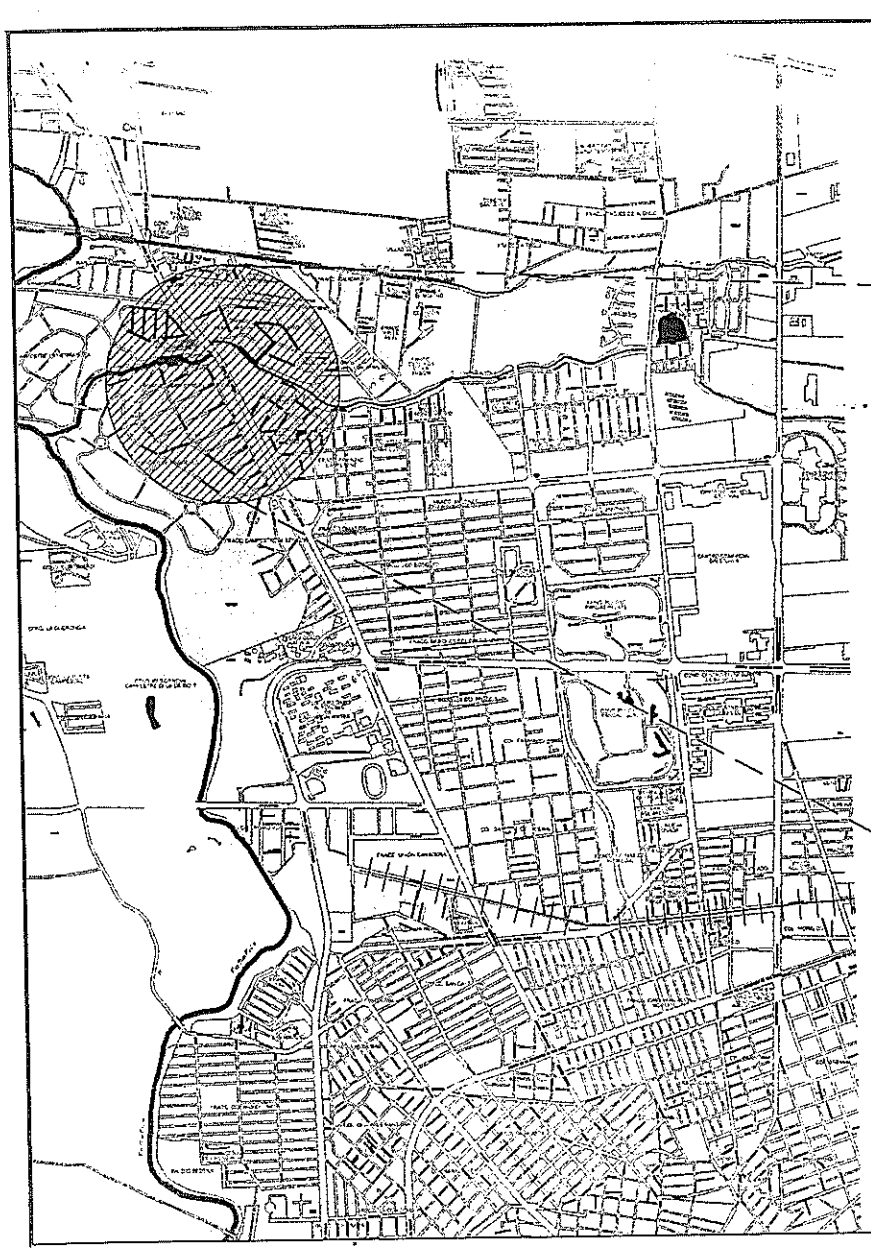

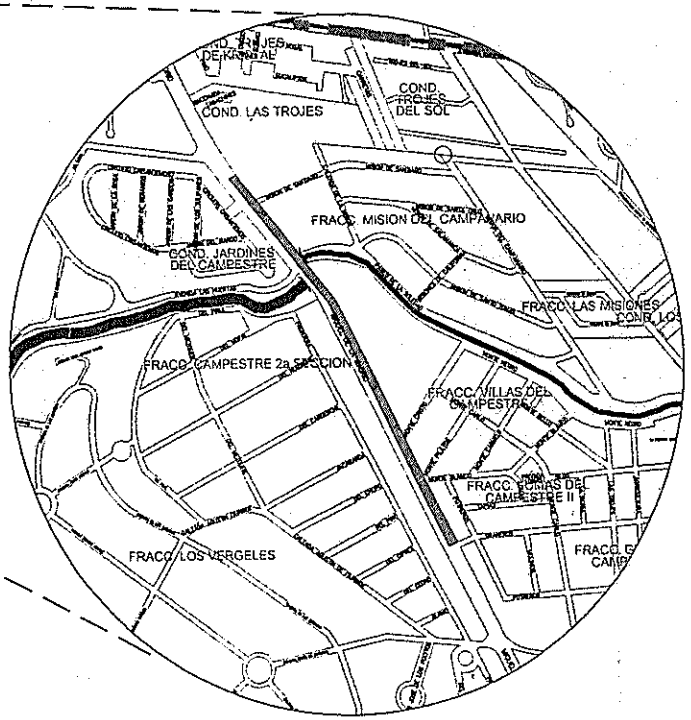


CROQUIS DE LOCALIZACIÓN

SIN ESCALA

AVENIDA CONVENCIÓN DE 1914 OTE.


LOCALIZACIÓN

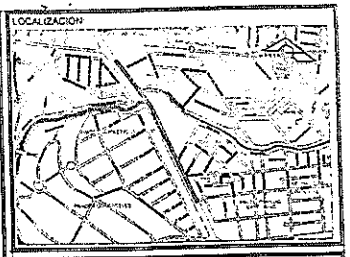


SIMBOLOGÍA

FISMDF – 0082 – 2022

La Dirección de Planeación y Proyectos solo autoriza el proyecto ejecutivo, no es responsable de la correcta ejecución de la obra. Este documento no tiene validez si no presenta las firmas de los responsables para su autorización, así como los sellos respectivos.

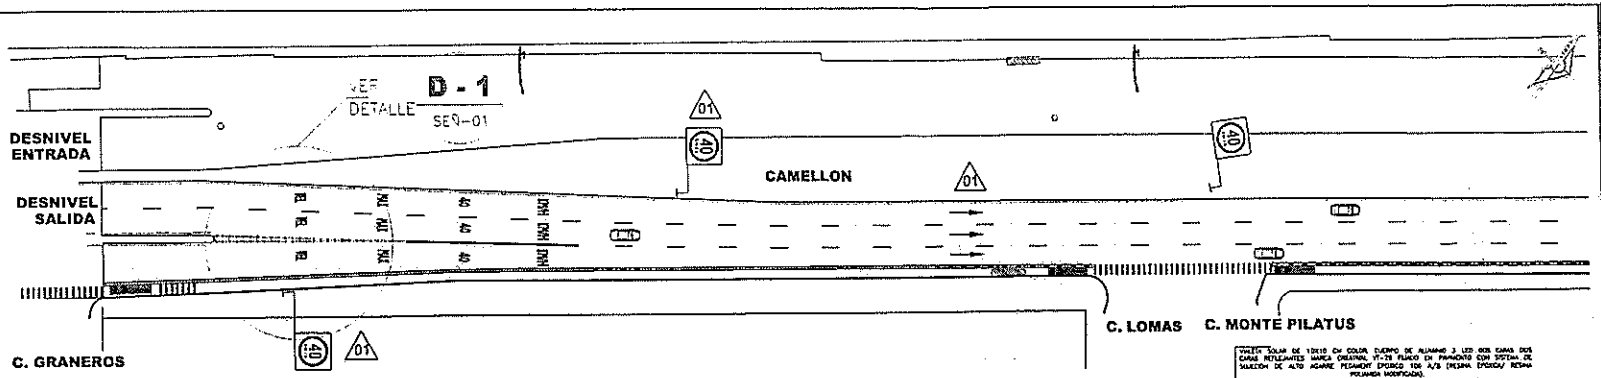

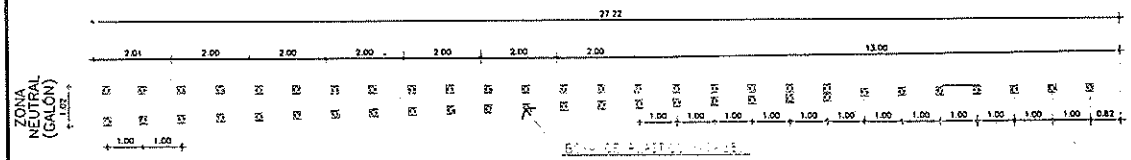


RAYAS CANALIZADORAS
ZONA NEUTRAL

ESCALA 1:50 COTAS EN m




DETALLE DE TRAZO DE TEXTO PARA SEÑALIZACIÓN HORIZONTAL

ESCALA 1:50 COTAS EN m

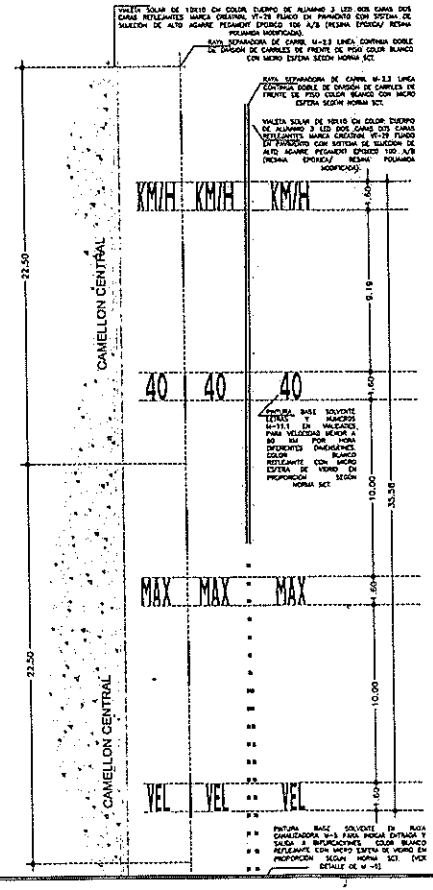

LOCALIZACIÓN

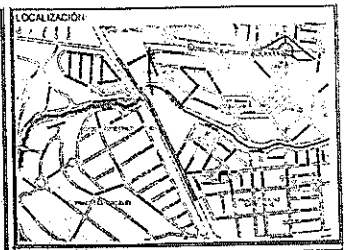

SIMBOLOGÍA

NOTA:

Nota1:

Se aplicará en todos los señalamientos horizontales pintura para trafico termoplastica base alquidalica de secado rápido, que cumpla con las especificaciones n-cmt-5-01-001/05, n-pry-car-10-01-002/13 de la SCT aplicadas al día de hoy.

Nota2:
Dosificación de micro esfera

La cantidad de esferas de vidrio en la película de pintura en húmedo, según su tipo, será la que se indica en la Tabla.

Nota 3:

Se aplicará solo en señalamiento de guarnicion conpintura para trafico base solvente tipo alquidal de secado rápido, que cumpla con las especificaciones n-cmt-5-01-001/05, n-pry-car-10-01-002/13 de la SCT aplicadas al día de hoy.

TABLA 8: Cantidad de esferas de vidrio en la pelicula de pintura en humedo.

CANTIDAD DE ESFERAS DE VIDRIO EN LA PELÍCULA DE PINTURA EN HÚMEDO				
TIPO DE PINTURA	ESPESOR DE LA PELÍCULA DE PINTURA EN HÚMEDO mm	CANTIDAD DE ESFERAS kg/m2		TIPO DE GRANULOMETRÍA
		INTEGRADAS	SEMBRADAS, ESPARCIDAS	
BASE SOLVENTE	0,38 A 0,50	-	0,330	1
BASE AGUA	0,38 A 0,50	-	0,330	1 Ó 2
TERMOPLÁSTICA	1,50 A 3,00	-	0,330	2


LIMITE DE PROYECTO ------

INDICA REVISIÓN NUMERO 1 01


SUSTITUYE A PLANO SEÑ-01, No. 02, JUNIO 2022 POR PLANO SEÑ-01, No. 02, SEPT 2022.

NOTA: LA SEÑALIZACION HORIZONTAL Y VERTICAL DE LA CICLOVIA NO ESTA CONSIDERADA EN ESTE PROYECTO.

La Dirección de Planeación y Proyectos solo autoriza el proyecto ejecutivo, no es responsable de la correcta ejecución de la obra. Este documento no tiene validez si no presenta las firmas de los responsables para su autorización, así como los sellos respectivos.

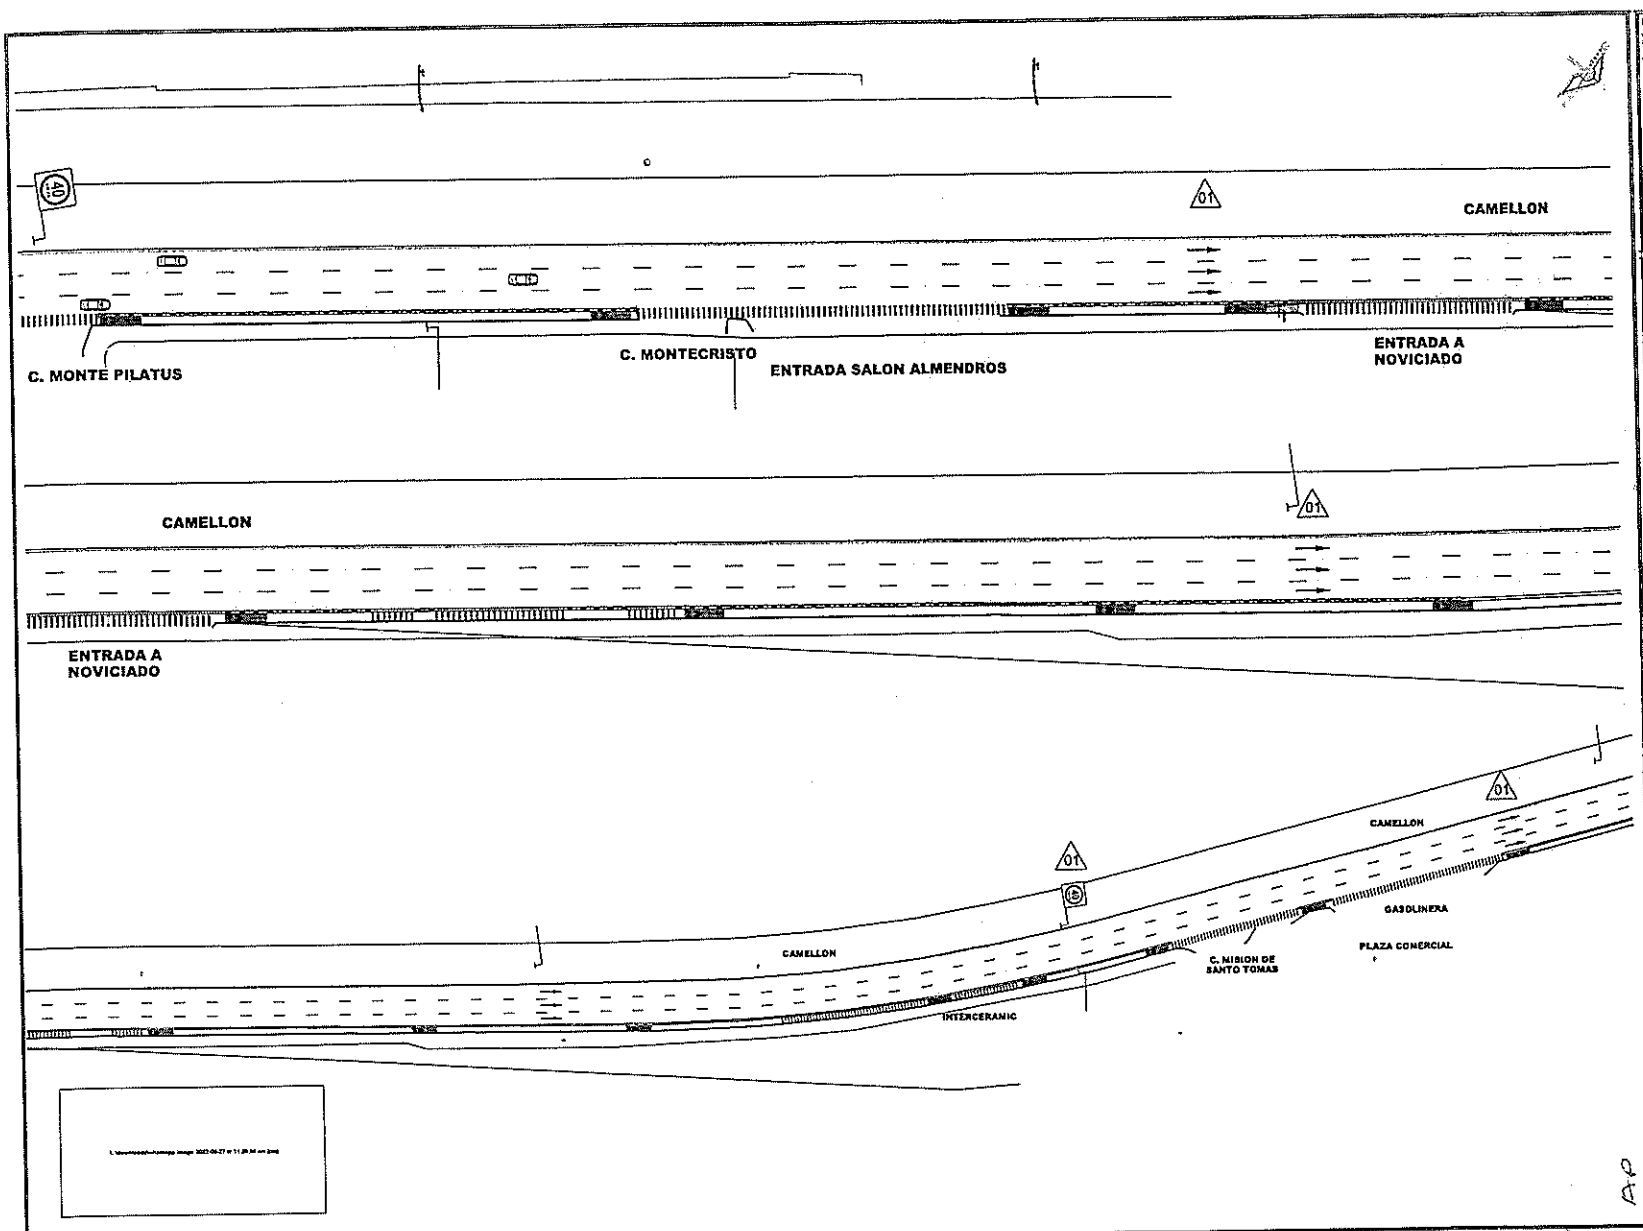

LOCALIZACIÓN:

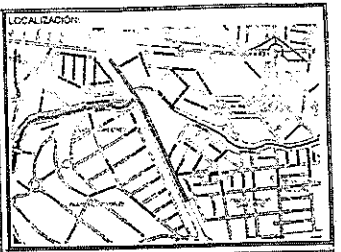

SIMBOLOGÍA

NOTA:

Nota1:

Se aplicará en todos los señalamientos horizontales pintura para trafico termoplastica base alquidalica de secado rápido, que cumpla con las especificaciones n-cmt-5-01-001/05, n-pry-car-10-01-002/13 de la SCT aplicadas al día de hoy.

Nota2:
Dosificación de micro esfera

La cantidad de esferas de vidrio en la película de pintura en húmedo, según su tipo, será la que se indica en la Tabla.

Nota 3:

Se aplicará solo en señalamiento de guarnicion conpintura para trafico base solvente tipo alquidal de secado rápido, que cumpla con las especificaciones n-cmt-5-01-001/05, n-pry-car-10-01-002/13 de la SCT aplicadas al día de hoy.

TABLA 8: Cantidad de esferas de vidrio en la película de pintura en humedo.

CANTIDAD DE ESFERAS DE VIDRIO EN LA PELÍCULA DE PINTURA EN HÚMEDO				
TIPO DE PINTURA	ESPESOR DE LA PELÍCULA DE PINTURA EN HÚMEDO mm	CANTIDAD DE ESFERAS kG/M2		TIPO DE GRANULOMETRÍA
		INTEGRADAS	SEMBRADAS, MÍNIMO	
BASE SOLVENTE	0,30 A 0,50	-	0,330	I
BASE AGUA	0,30 A 0,50	-	0,330	I II
TERMOPLÁSTICA	1,50 A 3,00	-	0,330	II


INDICA REVISIÓN NUMERO 1

01

SUSTITUYE A PLANO SEÑ-02, No. 03, JUNIO 2022 POR PLANO SEÑ-02, No. 03, SEPTIEMBRE 2022.


NOTA: LA SEÑALIZACIÓN HORIZONTAL Y VERTICAL DE LA CICLOVIA NO ESTA CONSIDERADA EN ESTE PROYECTO.

La Dirección de Planeación y Proyectos solo autoriza el proyecto ejecutivo, no es responsable de la correcta ejecución de la obra. Este documento no tiene validez si no presenta las firmas de los responsables para su autorización, así como los sellos respectivos.

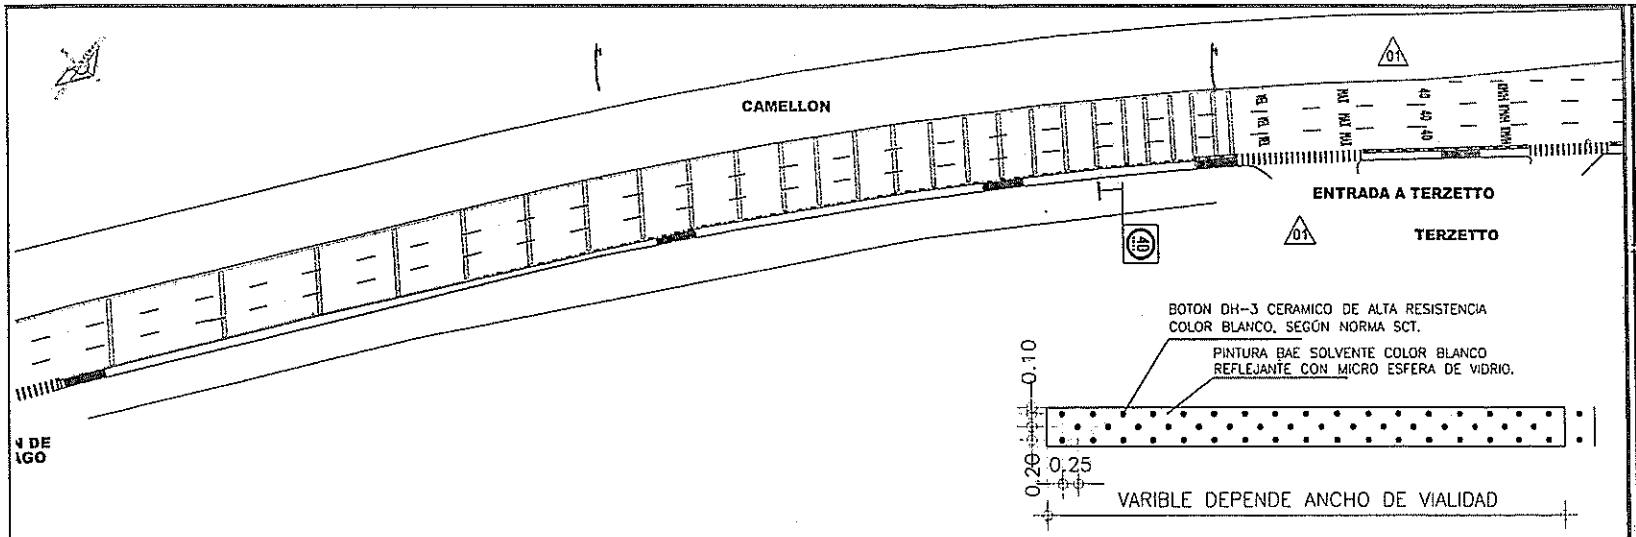

DETALLE 1 SEPARACION DE DH-3 EN RAYAS DE ESPARCIMIENTO LOGARITMICO

ESCALA 1:25

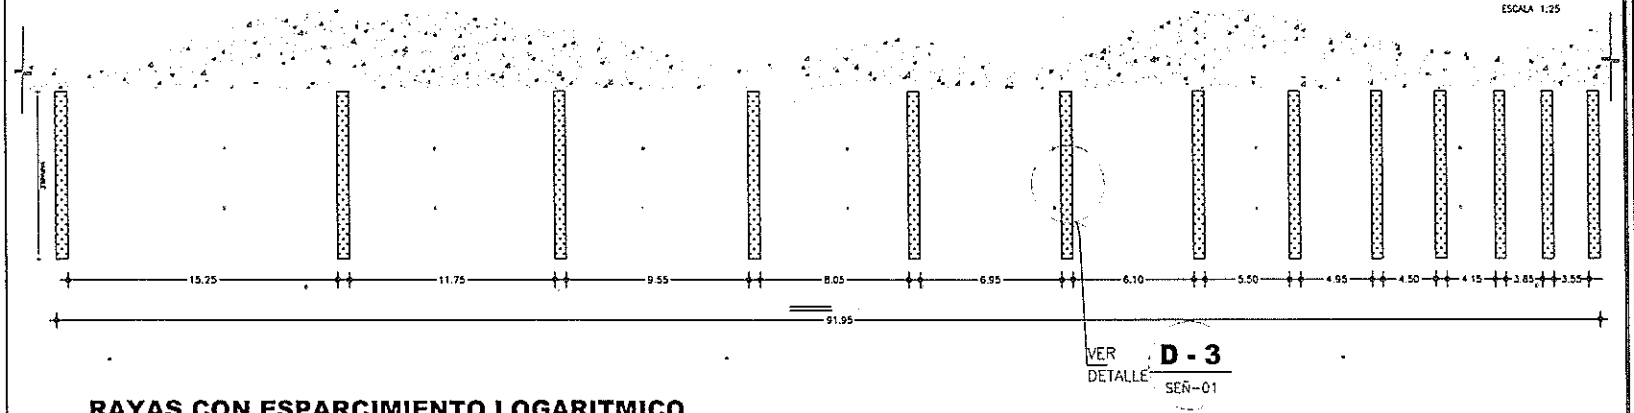


RAYAS CON ESPARCIMIENTO LOGARITMICO

ESCALA S/E

PINTURA TERMOPLASTICA BASE ALQUIDALICA EN "RAYAS DE ESPARCIMIENTO LOGARITMICO M-9 EN VIALIDADES PARA DISMINUIR LA VELOCIDAD DE LOS VEHICULOS DIFERENTES DIMENSIONES COLOR BLANCO REFLEJANTE CON MICROSESFERA DE VIDRIO, SEGÚN NORMA SCT. SE COMPONE DE UNA LINEAS DE 50 CM DE ANCHO Y DE UN LARGO VARIABLE REFERENTE A LA VIALIDAD CON BOTONES DH-3 CERAMICO DE ALTA RESISTENCIA COLOR BLANCO, LA LONGITUD TOTAL DE LA ZONA A MARCAR, EL NUMERO DE RAYAS Y SU SEPARACION, SE DEBEN DETEMINAR CONFORME A LO SEÑALADO EN LA TABLA III.2-3. DEL MANUAL DE SCT.

LOCALIZACIÓN:

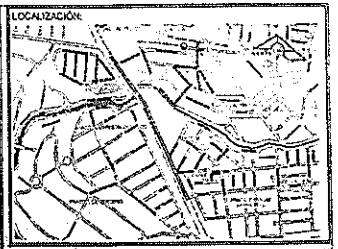

SIMBOLOGÍA

NOTA:

Nota1:

Se aplicará en todos los señalamientos horizontales pintura para trafico termoplastica base alquidafica de secado rápido, que cumpla con las especificaciones n-cmt-5-01-001/05, n-pry-car-10-01-002/13 de la SCT aplicadas al día de hoy.

Nota2:
Dosificación de micro esfera

La cantidad de esferas de vidrio en la pelicula de pintura en húmedo, según su tipo, será la que se indica en la Tabla.

Nota 3:

Se aplicará solo en señalamiento de guarnicion conpintura para trafico base solvente tipo alquidal de secado rápido, que cumpla con las especificaciones n-cmt-5-01-001/05, n-pry-car-10-01-002/13 de la SCT aplicadas al día de hoy.

TABLA 8: Cantidad de esferas de vidrio en la pelicula de pintura en humedo.


CANTIDAD DE ESFERAS DE VIDRIO EN LA PELÍCULA DE PINTURA EN HÚMEDO				
TIPO DE PINTURA	ESPESOR DE LA PELÍCULA DE PINTURA EN HÚMEDO mm	CANTIDAD DE ESFERAS KG/M2 INTEGRADAS	SEMBRADAS, MÍNIMO	TIPO DE GRANULOMETRÍA
BASE SOLVENTE	0,30 A 0,50	-	0,350	I
BASE AGUA	0,30 A 0,50	-	0,350	I o II
TERMOPLÁSTICA	1,50 A 3,00	-	0,350	II


INDICA REVISIÓN NUMERO 1 — 01

SUSTITUYE A PLANO SEÑ-03, No. 04, SEPTIEMBRE 2022 POR PLANO SEÑ-03, No. 04, SEPTIEMBRE 2022.


NOTA: LA SEÑALIZACIÓN HORIZONTAL Y VERTICAL DE LA CICLOVIA NO ESTÁ CONSIDERADA EN ESTE PROYECTO.

La Dirección de Planeación y Proyectos solo autoriza el proyecto ejecutivo, no es responsable de la correcta ejecución de la obra. Este documento no tiene validez si no presenta las firmas de los responsables para su autorización, así como los sellos respectivos.

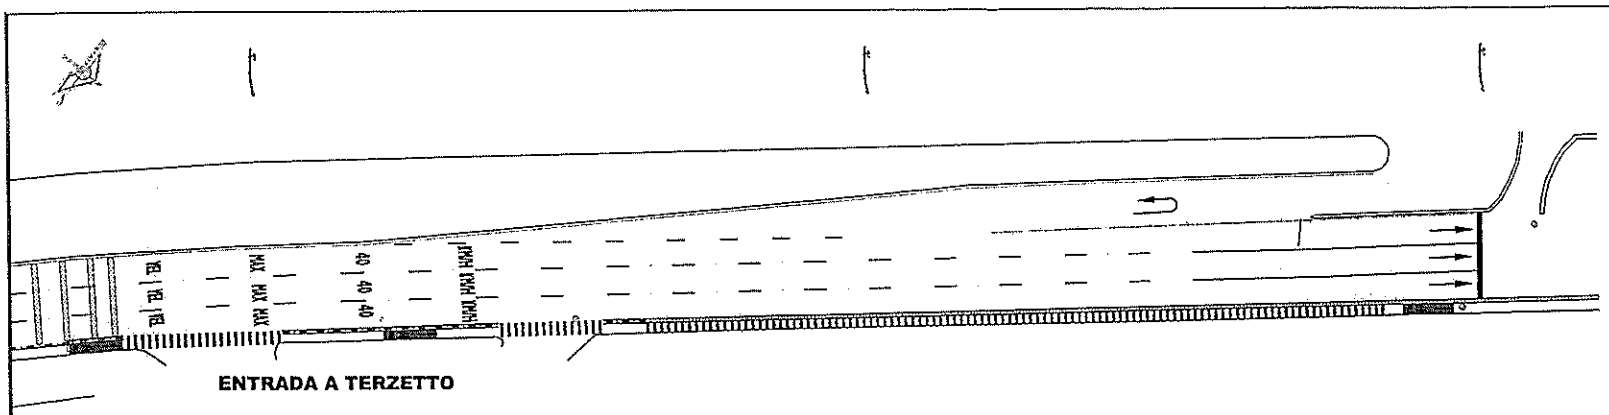


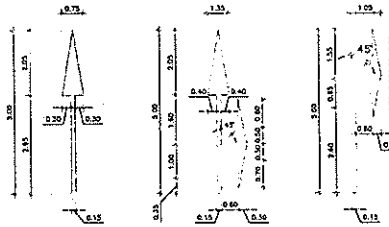


DETALLE DE FLECHAS EN PAVIMENTO
PARA VELOCIDADES HASTA DE 60KM/H
ESCALA 1:50 COTAS EN m

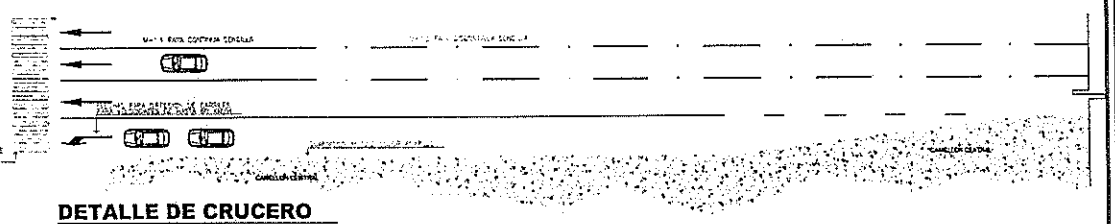

DETALLE DE CRUCERO
ESCALA 1:200 COTAS EN m

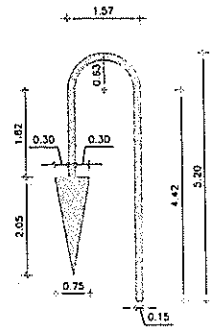


AREA: 2.04 m2
PERIMETRO: 21.84

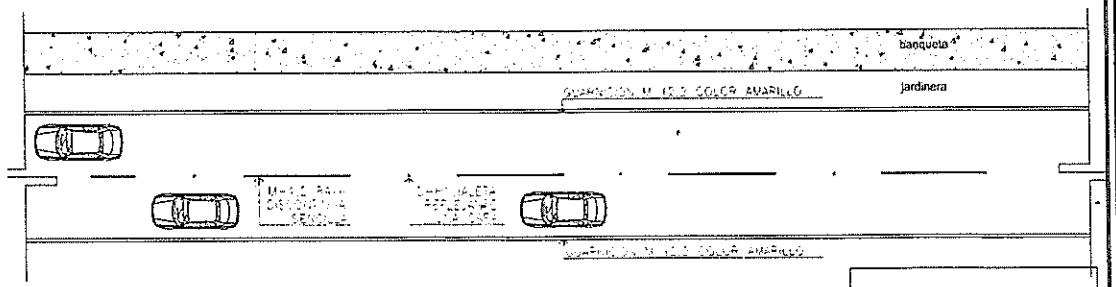

DETALLE DE FLECHA VUELTA U EN PAVIMENTO
PARA VELOCIDADES HASTA DE 60KM/H
ESCALA 1:50 COTAS EN m

LOCALIZACIÓN:

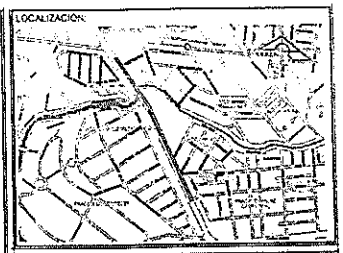

SIMBOLOGÍA

NOTA:

Nota1:

Se aplicará en todos los señalamientos horizontales pintura para trafico termoplastica base alquidalica de secado rápido, que cumpla con las especificaciones n-cmt-5-01-001/05, n-pry-car-10-01-002/13 de la SCT aplicadas al día de hoy.

Nota2:
Dosificación de micro esfera

La cantidad de esferas de vidrio en la película de pintura en húmedo, según su tipo, será la que se indica en la Tabla.


Nota 3:

Se aplicará solo en señalamiento de guarnicion conpintura para trafico base solvente tipo alquidal de secado rápido, que cumpla con las especificaciones n-cmt-5-01-001/05, n-pry-car-10-01-002/13 de la SCT aplicadas al día de hoy.

TABLA 8: Cantidad de esferas de vidrio en la pelicula de pintura en humedo.

CANTIDAD DE ESFERAS DE VIDRIO EN LA PELÍCULA DE PINTURA EN HÚMEDO				
TIPO DE PINTURA	ESPESOR DE LA PELÍCULA DE PINTURA EN HÚMEDO mm	CANTIDAD DE ESFERAS KG/LT		TIPO DE GRANULOMETRÍA
		INTEGRADAS	SEMBRADAS SOBRE	
BASE SOLVENTE	0,38 A 0,50	-	0,330	I
BASE AGUA	0,38 A 0,50	-	0,330	I Ó II
TERMOPLÁSTICA	1,50 A 3,00	-	0,330	II

La Dirección de Planeación y Proyectos solo autoriza el proyecto ejecutivo, no es responsable de la correcta ejecución de la obra. Este documento no tiene validez si no presenta las firmas de los responsables para su autorización, así como los sellos respectivos.

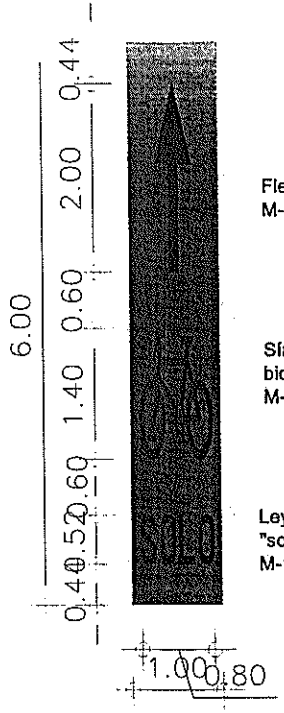


DETALLE DE CAJA BICI Y MARCAS DE CARRIL EXCLUSIVO

ESCALA 1:25

PINTURA TERMOPLASTICA BASE ALQUIDALICA EN MARCAS PARA INDENTIFICAR CICLOVÍA, COLOR BLANCO REFLEJANTE CON MICROSESFERA DE VIDRIO, SEGÚN NORMA SCT. SE COMPONE DE UNA FLECHA QUE INDIQUE EL SENTIDO DE CIRCULACIÓN, LA LEYENDA "SOLO" Y EL SÍMBOLO DE LA BICICLETA.

PINTURA BASE SOLVENTE EN FONDO DE GRUPO DE MARCAS PARA IDENTIFICAR CAJA BICI, COLOR VERDE 7481 C PANTONE. REFLEJANTE CON MICROSESFERA, SEGÚN NORMA SCT. DE 1.00 X 6.00 MTS. SOBRE EL EJE DE LA CICLOVÍA.


VER PLANOS PG-01 Y PG-02

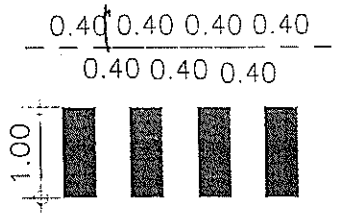

RAYA PARA CRUCE DE CICLISTAS


ESCALA 1:25

PINTURA TERMOPLASTICA BASE ALQUIDAL EN RAYA PARA INDICAR CRUCE CICLISTA CLASIFICACIÓN M-7.1, COLOR VERDE 7481 C PANTONE REFLEJANTE, CON MICROESFERA DE VIDRIO, SEGÚN NORMA SCT. DE 0.40 X 1.00 M Y SEPARACIÓN ENTRE SI DE 0.40 M.

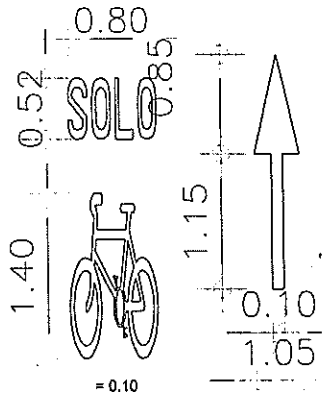

DIMENCIONES DE MARCAS


SIN ESCALA

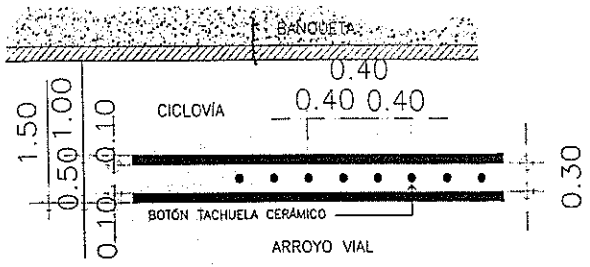

DETALLE DE CICLOCARRIL

ESCALA 1:25

PINTURA TERMOPLASTICA BASE ALQUIDALICO EN RAYA CLASIFICACIÓN M-2.2 LÍNEA CONTINUA DOBLE DE DIMISIÓN DE CARRILES DE FRENTE EN PISO, DE 10 CM. DE ANCHO Y SEPARACIÓN DE 30 CM. ENTRE ELLAS, COLOR BLANCO REFLEJANTE CON MICROSESFERA DE VIDRIO, SEGÚN NORMA SCT.

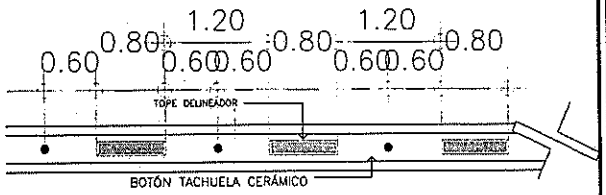


DETALLE DE DIMENSIONES PARA MARCAS DE CARRIL EXCLUSIVO

ESCALA 1:25

DELINEADOR DE CARRIL EXCLUSIVO TIPO "A" DE POLIETILENO DE ALTA DENSIDAD CON PROTECCION DE ESTABILIZADO DE RAYOS UV, COLOR AMARILLO REFLEJANTES EN ROJO DE 80*50*20 CMS MARCA HERSAN, PARA COLOCAR EN CARRIL CONFINADO CICLISTA. INDICA EL INICIO DE CICLOVÍA SEGREGADA, COLOCACIÓN AL CENTRO DEL ESPACIO QUE SEPARA LA LÍNEA CONTINUA DOBLE.

BOTÓN TACHUELA DE ABS CERÁMICO DE ALTA RESISTENCIA COLOR BLANCO (VT-32), DIÁMETRO DE 10 CM. ALTURA NO MAYOR DE 2 CM. MARCA CREATIVIAL O SIMILAR EN CALIDAD Y ESPECIFICACIONES DE FICHA TÉCNICA, SEGÚN NORMA SCT.

LOCALIZACIÓN

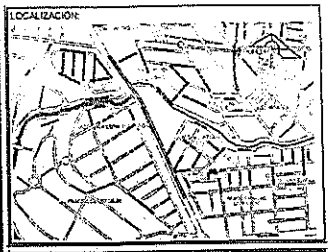

SIMBOLOGÍA

NOTA:

Nota1:

Se aplicará en todos los señalamientos horizontales pintura para trafico termoplastica base alquidalica de secado rápido, que cumpla con las especificaciones n-cmt-5-01-001/05, n-pry-car-10-01-002/13 de la SCT aplicadas al día de hoy.

Nota2:
Dosificación de micro esfera

La cantidad de esferas de vidrio en la película de pintura en húmedo, según su tipo, será la que se indica en la Tabla.


Nota 3:


Se aplicará solo en señalamiento de guarnicion conpintura para trafico base solvente tipo alquidal de secado rápido, que cumpla con las especificaciones n-cmt-5-01-001/05, n-pry-car-10-01-002/13 de la SCT aplicadas al día de hoy.

TABLA 8: Cantidad de esferas de vidrio en la película de pintura en humedo.


CANTIDAD DE ESFERAS DE VIDRIO EN LA PELÍCULA DE PINTURA EN HÚMEDO				
TIPO DE PINTURA	ESPESOR DE LA PELÍCULA DE PINTURA EN HÚMEDO mm	CANTIDAD DE ESFERAS Kg/m2		TIPO DE GRANULOMETRÍA
		INTEGRADAS	SEMBRADAS, MÍNIMO	
BASE SOLVENTE	0,30 A 0,50	-	0,330	I
BASE AGUA	0,30 A 0,50	-	0,330	I o II
TERMOPLÁSTICA	2,50 A 3,00	-	0,330	II

La Dirección de Planeación y Proyectos solo autoriza el proyecto ejecutivo, no es responsable de la correcta ejecución de la obra. Esta documento no tiene validez si no presenta las firmas de los responsables para su autorización, así como los sellos respectivos.

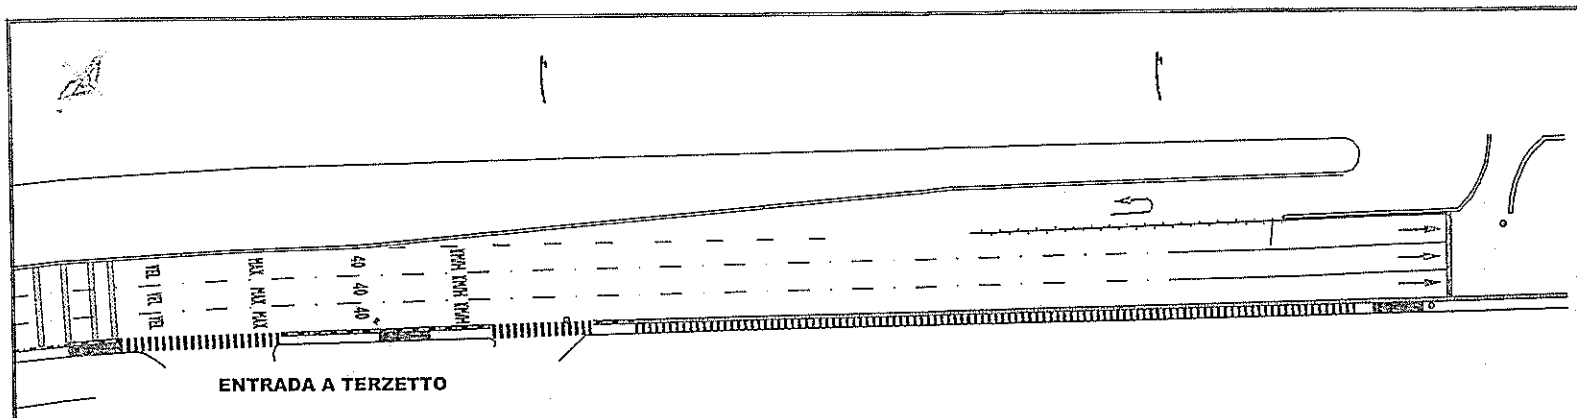


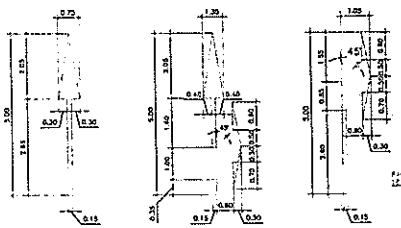


DETALLE DE FLECHAS EN PAVIMENTO
PARA VELOCIDADES HASTA DE 60KM/H
ESCALA 1:50 COTAS EN m

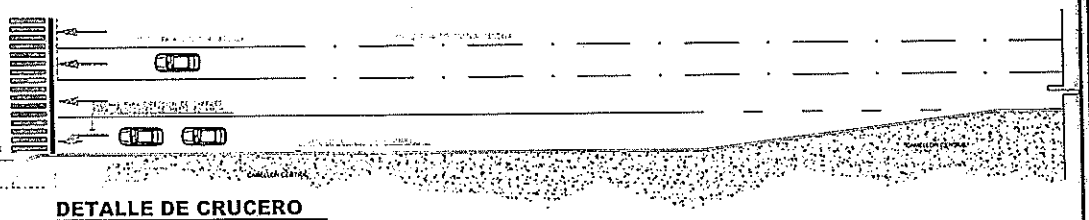


DETALLE DE CRUCERO
ESCALA 1:200 COTAS EN m

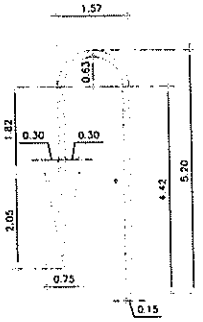

AREA: 2.04 m2
PERIMETRO: 21.84

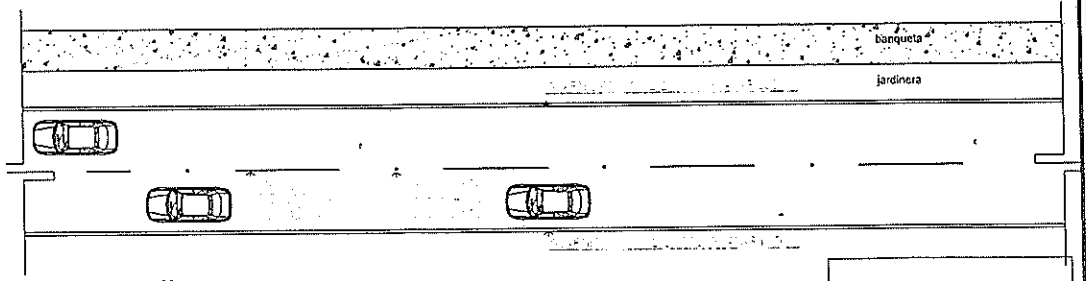

DETALLE DE FLECHA VUELTA U EN PAVIMENTO
PARA VELOCIDADES HASTA DE 60KM/H
ESCALA 1:50 COTAS EN m

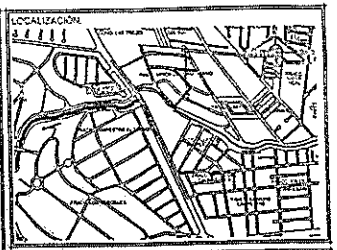

SIMBOLOGÍA

NOTA:

Nota1:

Se aplicará en todos los señalamientos horizontales pintura para trafico termoplastica base alquidalica de secado rápido, que cumpla con las especificaciones n-cmt-5-01-001/05, n-pry-car-10-01-002/13 de la SCT aplicadas al día de hoy.

Nota2:
Dosificación de micro esfera

La cantidad de esferas de vidrio en la pelicula de pintura en húmedo, según su tipo, será la que se indica en la Tabla.


Nota 3:

Se aplicará solo en señalamiento de guarnicion conpintura para trafico base solvente tipo alquidal de secado rápido, que cumpla con las especificaciones n-cmt-5-01-001/05, n-pry-car-10-01-002/13 de la SCT aplicadas al dia de hoy.

TABLA 8: Cantidad de esferas de vidrio en la pelicula de pintura en humedo.

CANTIDAD DE ESFERAS DE VIDRIO EN LA PELICULA DE PINTURA EN HUMEDO				
TIPO DE PINTURA	ESPESOR DE LA PELÍCULA DE PINTURA EN HÚMEDO mm	CANTIDAD DE ESFERAS kG/M2 INTEGRADAS	SEMBRADAS MÍNIMO	TIPO DE GRANULOMETRÍA
BASE SOLVENTE	0.30 a 0.50	-	0.330	3
BASE AGUA	0.30 a 0.50	-	0.330	1 ó 3
TERMOPLÁSTICA	1.50 a 3.00	-	0.330	3

La Dirección de Planeación y Proyectos solo autoriza el proyecto ejecutivo, no es responsable de la correcta ejecución de la obra. Este documento no tiene validez si no presenta las firmas de los responsables para su autorización, así como los sellos respectivos.

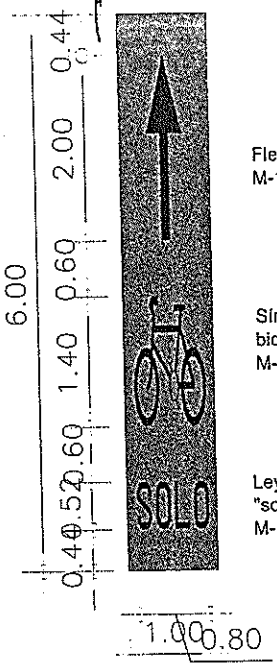

Flecha
M-11.1

Símbolo de
bicicleta
M-15

Leyenda
"solo"
M-11.3


DETALLE DE CAJA BICI Y MARCAS DE CARRIL EXCLUSIVO

ESCALA 1:25

PINTURA TERMOPLASTICA BASE ALQUIDALICA EN MARCAS PARA INDENTIFICAR CICLOVÍA, COLOR BLANCO REFLEJANTE CON MICROSESFERA DE VIDRIO, SEGÚN NORMA SCT. SE COMPONE DE UNA FLECHA QUE INDIQUE EL SENTIDO DE CIRCULACIÓN, LA LEYENDA "SOLO" Y EL SÍMBOLO DE LA BICICLETA.

PINTURA BASE SOLVENTE EN FONDO DE GRUPO DE MARCAS PARA IDENTIFICAR CAJA BICI, COLOR VERDE 7481 C PANTONE, REFLEJANTE CON MICROSESFERA, SEGÚN NORMA SCT. DE 1.00 X 6.00 MTS. SOBRE EL EJE DE LA CICLOVIA.


VER PLANOS PG-01 Y PG-02

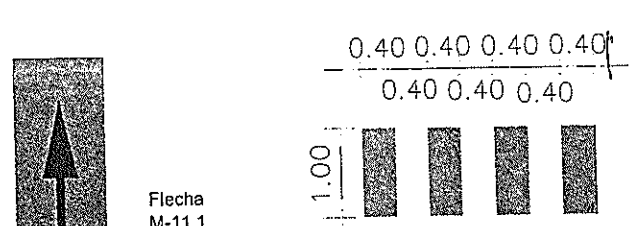

RAYA PARA CRUCE DE CICLISTAS

ESCALA 1:25


PINTURA TERMOPLASTICA BASE ALQUIDAL EN RAYA PARA INDICAR CRUCE CICLISTA CLASIFICACIÓN M-7.1, COLOR VERDE 7481 C PANTONE REFLEJANTE, CON MICROESFERA DE VIDRIO, SEGÚN NORMA SCT. DE 0.40 X 1.00 M. Y SEPARACIÓN ENTRE SI DE 0.40 M.

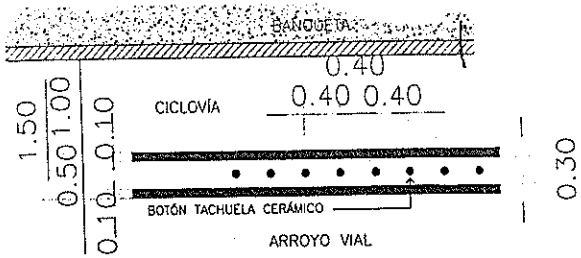

DETALLE DE CICLOCARRIL

ESCALA 1:25

PINTURA TERMOPLASTICA BASE ALQUIDALICO EN RAYA CLASIFICACIÓN M-2.2 LÍNEA CONTINUA DOBLE DE DIVISIÓN DE CARRILES DE FRENTE EN PISO, DE 10 CM. DE ANCHO Y SEPARACIÓN DE 30 CM. ENTRE ELLAS, COLOR BLANCO REFLEJANTE CON MICROSESFERA DE VIDRIO, SEGÚN NORMA SCT.

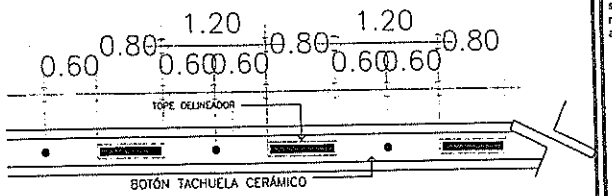


DETALLE DE DIMENSIONES PARA MARCAS DE CARRIL EXCLUSIVO

ESCALA 1:25


DELINEADOR DE CARRIL EXCLUSIVO TIPO "A" DE POLIETILENO DE ALTA DENSIDAD CON PROTECCION DE ESTABILIZADO DE RAYOS UV, COLOR AMARILLO REFLEJANTES EN ROJO DE 80*50*20 CMS MARCA HERSAN, PARA COLOCAR EN CARRIL CONFINADO CICLISTA. INDICA EL INICIO DE CICLOVÍA SEGREGADA, COLOCACIÓN AL CENTRO DEL ESPACIO QUE SEPARA LA LÍNEA CONTINUA DOBLE.

BOTÓN TACHUELA DE ABS CERÁMICO DE ALTA RESISTENCIA COLOR BLANCO (VT-32), DIÁMETRO DE 10 CM. ALTURA NO MAYOR DE 2 CM. MARCA CREATIVIAL O SIMILAR EN CALIDAD Y ESPECIFICACIONES DE FICHA TÉCNICA, SEGÚN NORMA SCT.

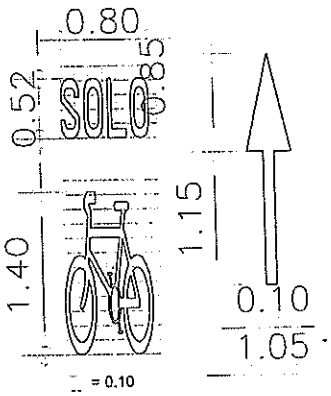

DIMENCIONES DE MARCAS

SIN ESCALA

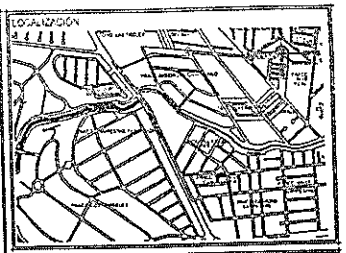

SIMBOLOGIA

NOTA:

Nota1:

Se aplicará en todos los señalamientos horizontales pintura para trafico termoplastica base alquidalica de secado rápido, que cumpla con las especificaciones n-cmt-5-01-001/05, n-pry-car-10-01-002/13 de la SCT aplicadas al día de hoy.

Nota2:
Desificación de micro esfera

La cantidad de esferas de vidrio en la película de pintura en húmedo, según su tipo, será la que se indica en la Tabla.

Nota 3:


Se aplicará solo en señalamiento de guarnicion conpintura para trafico base solvente tipo alquidal de secado rápido, que cumpla con las especificaciones n-cmt-5-01-001/05, n-pry-car-10-01-002/13 de la SCT aplicadas al día de hoy.


TABLA 8: Cantidad de esferas de vidrio en la película de pintura en humedo.

CANTIDAD DE ESFERAS DE VIDRIO EN LA PELÍCULA DE PINTURA EN HÚMEDO				
TIPO DE PINTURA	ESPESOR DE LA PELÍCULA DE PINTURA EN HÚMEDO (mm)	CANTIDAD DE ESFERAS AGUJ INTEGRADAS	AGREGADAS MÍNIMO	TIPO DE GRANULOMETRÍA
BASE SOLVENTE	0.30 A 0.50	-	0.350	I
BASE AGUA	0.28 A 0.50	-	0.350	I & II
TERMOPLASTICA	1.50 A 3.00	-	0.300	II

AP


La Dirección de Planeación y Proyectos solo autoriza el proyecto ejecutivo, no es responsable de la correcta ejecución de la obra. Este documento no tiene validez si no presenta las firmas de los responsables para su autorización, así como los sellos respectivos.

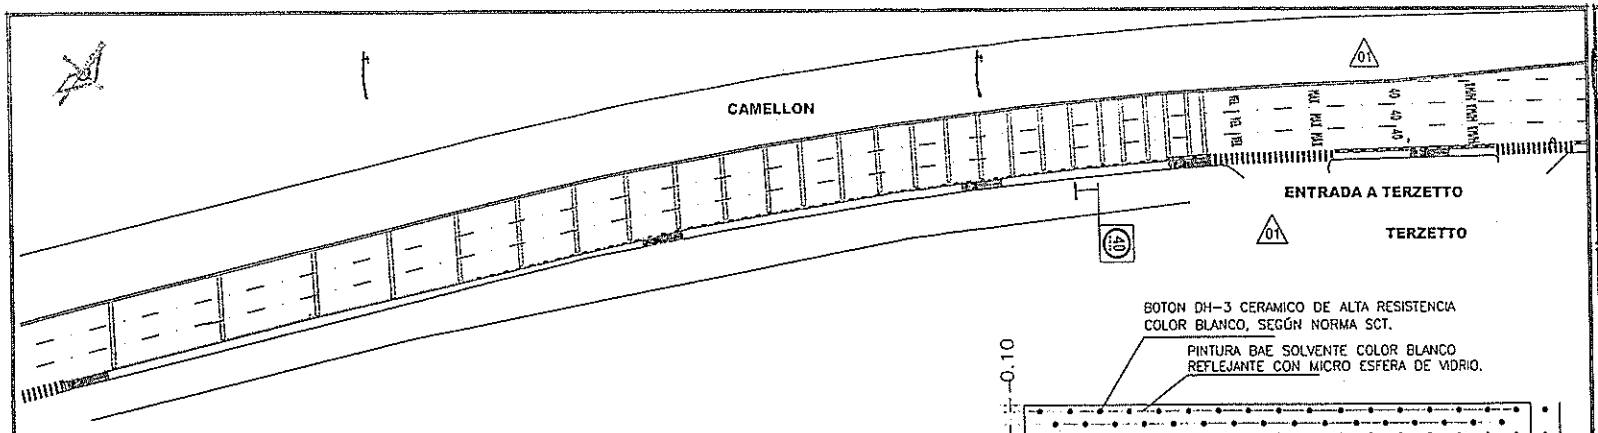

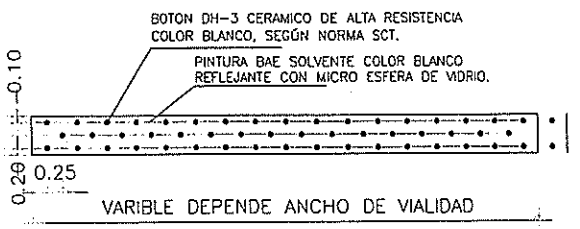

DETALLE 1 SEPARACION DE DH-3 EN RAYAS DE ESPARCIMIENTO LOGARITMICO

ESCALA 1:25

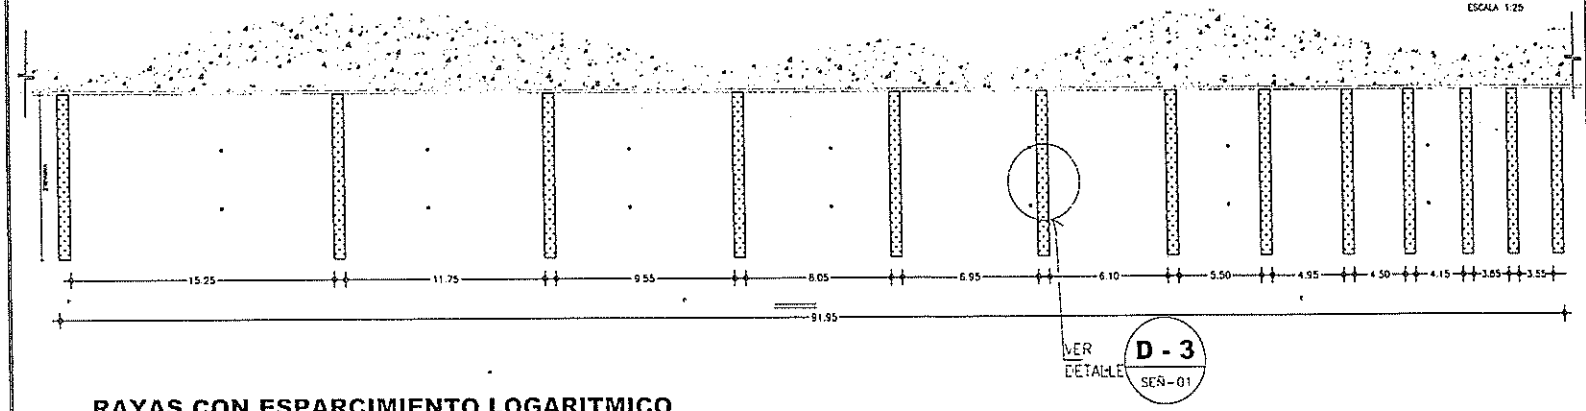


RAYAS CON ESPARCIMIENTO LOGARITMICO

ESCALA S/E

PINTURA TERMOPLASTICA BASE ALQUIDALICA EN "RAYAS DE ESPARCIMIENTO LOGARITMICO M-9 EN VIALIDADES PARA DISMINUIR LA VELOCIDAD DE LOS VEHICULOS DIFERENTES DIMENSIONES COLOR BLANCO REFLEJANTE CON MICROSESFERA DE VIDRIO, SEGÚN NORMA SCT. SE COMPONE DE UNA LINEAS DE 60 CM DE ANCHO Y DE UN LARGO VARIABLE REFERTE A LA VALIDAD CON BOTONES DH-3 CERAMICO DE ALTA RESISTENCIA COLOR BLANCO, LA LONCITUD TOTAL DE LA ZONA A MARCAR, EL NUMERO DE RAYAS Y SU SEPARACIÓN. SE DEBEN DETEMINAR CONFORME A LO SEÑALADO EN LA TABLA III.2-3. DEL MANUAL DE SCT.

LOCALIZACIÓN:

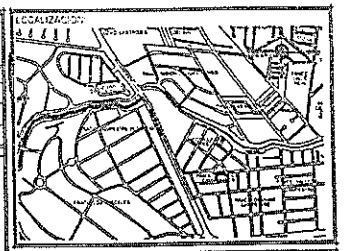

SIMBOLOGÍA

NOTA:

Nota1:

Se aplicará en todos los señalamientos horizontales pintura para trafico termoplastica base alquidalica de secado rápido, que cumpla con las especificaciones n-cmt-5-01-001/05, n-pry-car-10-01-002/13 de la SCT aplicadas al dia de hoy.

Nota2:
Dosificación de micro esfera

La cantidad de esferas de vidrio en la pelicula de pintura en húmedo, según su tipo, será la que se indica en la Tabla.

Nota 3:

Se aplicará solo en señalamiento de guarnicion conpintura para trafico base solvente tipo alquidal de secado rápido, que cumpla con las especificaciones n-cmt-5-01-001/05. n-pry-car-10-01-002/13 de la SCT aplicadas al dia de hoy.

TABLA 8: Cantidad de esferas de vidrio en la pelicula de pintura en humedo.


CANTIDAD DE ESFERAS DE VIDRIO EN LA PELICULA DE PINTURA EN HUMEDO				
TIPO DE PINTURA	ESPESOR DE LA PELÍCULA DE PINTURA EN HÚMEDO mm	CANTIDAD DE ESFERAS KG/M2		TIPO DE GRANULOMETRIA
		INTEGRADAS	SEMBRADAS, MÍNIMO	
BASE SOLVENTE	0.30 A 0.50	-	0.330	I
BASE AGUA	0.30 A 0.50	-	0.330	I o II
TERMOPLÁSTICA	3.50 A 5.00	-	0.330	II


INDICA REVISIÓN NUMERO 1 — 01

SUSTITUYE A PLANO SEÑ-01, No. 04, SEPTIEMBRE 2022 POR PLANO SEÑ-01, No. 04, SEPTIEMBRE 2022.

NOTA: LA SEÑALIZACIÓN HORIZONTAL Y VERTICAL DE LA CICLOVIA NO ESTA CONSIDERADA EN ESTE PROYECTO.

La Dirección de Planeación y Proyectos solo autoriza el proyecto ejecutivo, no es responsable de la correcta ejecución de la obra. Este documento no tiene validez si no presenta las firmas de los responsables para su autorización, así como los sellos respectivos.

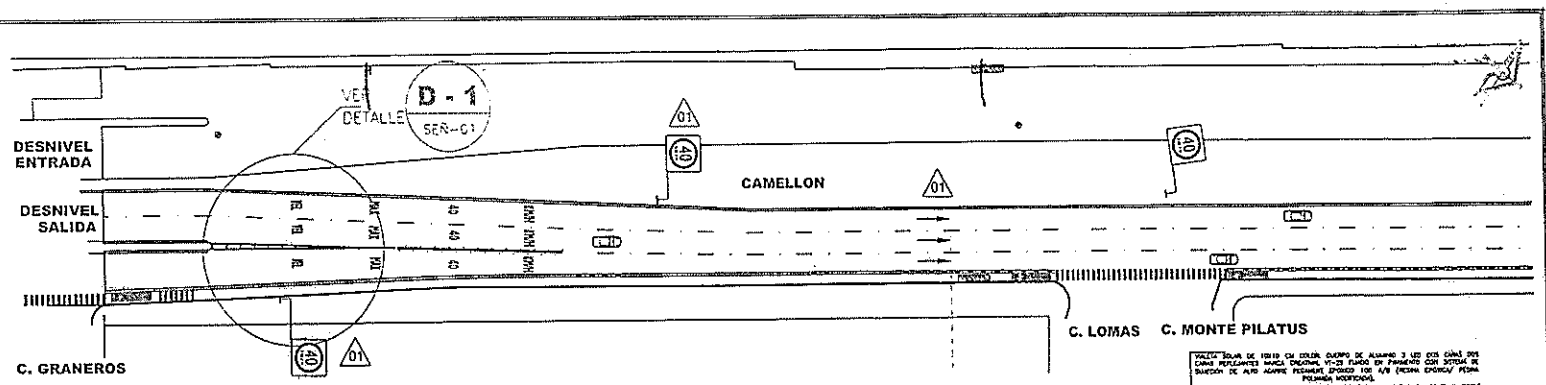

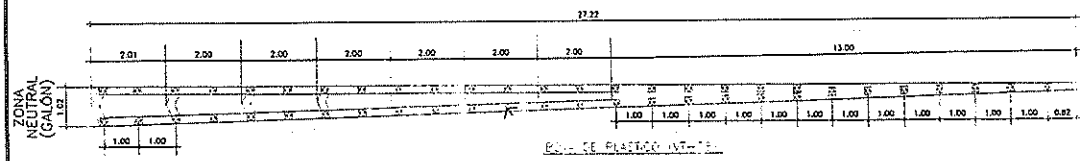


RAYAS CANALIZADORAS
ZONA NEUTRAL


ESCALA 1:50 COTAS EN m



DETALLE DE TRAZO DE TEXTO PARA SEÑALIZACIÓN HORIZONTAL

ESCALA 1:50 COTAS EN m

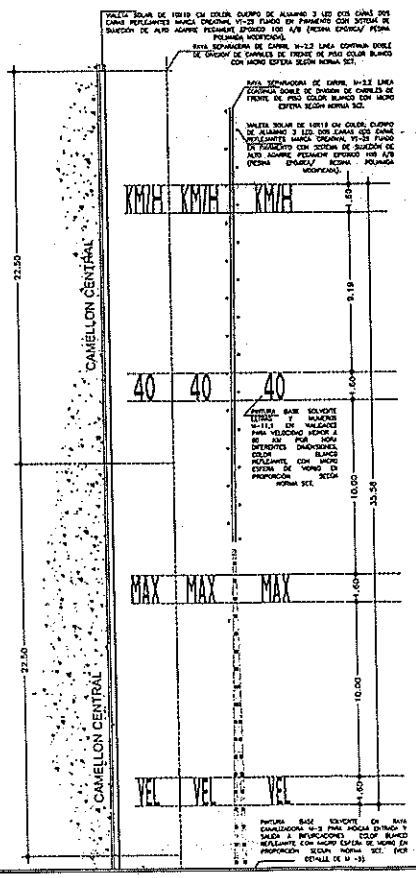

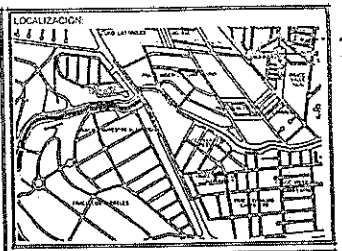

SIMBOLOGIA

NOTA:

Nota1:

Se aplicará en todos los señalamientos horizontales pintura para trafico termoplastica base alquidalica de secado rápido, que cumpla con las especificaciones n-cmt-5-01-001/05, n-pry-car-10-01-002/13 de la SCT aplicadas al día de hoy.

Nota2:
Dosificación de micro esfera

La cantidad de esferas de vidrio en la película de pintura en húmedo, según su tipo, será la que se indica en la Tabla.

Nota 3:

Se aplicará solo en señalamiento de guarnicion conpintura para trafico base solvente tipo alquidal de secado rápido, que cumpla con las especificaciones n-cmt-5-01-001/05, n-pry-car-10-01-002/13 de la SCT aplicadas al día de hoy.

TABLA 8: Cantidad de esferas de vidrio en la película de pintura en humedo.

CANTIDAD DE ESFERAS DE VIDRIO EN LA PELICULA DE PINTURA EN HUMEDO

TIPO DE PINTURA	ESPESOR DE LA PELIKULA DE PINTURA EN HUMEDO mm	CANTIDAD DE ESFERAS KG/M2 INTEGRADAS	SOBRADAS	TIPO DE GRANULOMETRIA
BASE SOLVENTE	0.30 A 0.50	0.330		I
BASE AGUA	0.30 A 0.50	0.330		I o II
TERMOPLASTICA	1.50 A 3.00	0.330		II


LIMITE DE PROYECTO ------

INDICA REVISIÓN NUMERO 1 01


SUSTITUYE A PLANO SER-01 No. 02, JUNIO 2022 POR PLANO SER-01, No. 02, [illegible] 2022.

NOTA: LA SEÑALIZACIÓN HORIZONTAL Y VERTICAL DE LA CICLOVIA NO ESTA CONSIDERADA EN ESTE PROYECTO.

La Dirección de Planeación y Proyectos solo autoriza el proyecto ejecutivo, no es responsable de la correcta ejecución de la obra. Este documento no tiene validez si no presenta las firmas de los responsables para su autorización, así como los sellos respectivos.

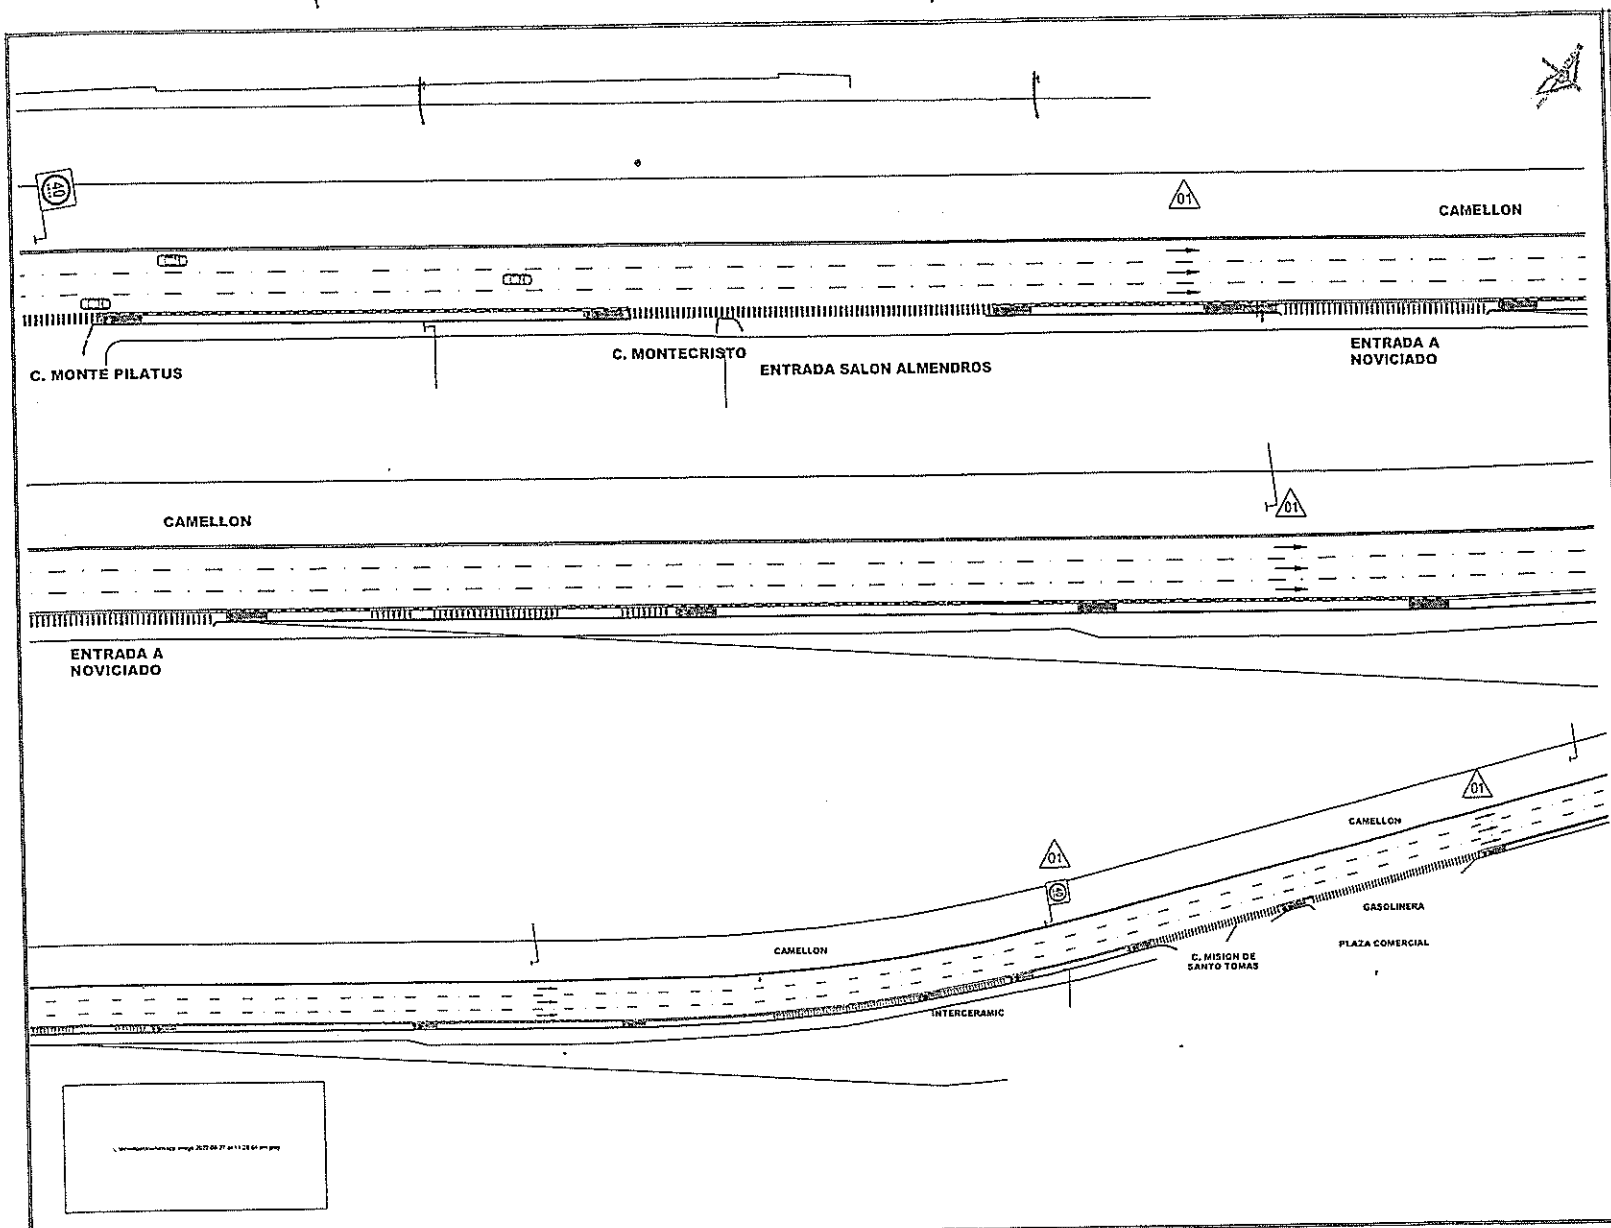

LOCALIZACIÓN:

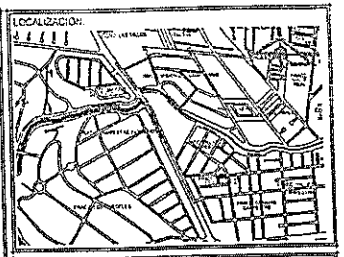

SIMBOLOGÍA

NOTA:

Nota1:

Se aplicará en todos los señalamientos horizontales pintura para trafico termoplastica base alquidalica de secado rápido, que cumpla con las especificaciones n-cmt-5-01-001/05, n-pry-car-10-01-002/13 de la SCT aplicadas al día de hoy.

Nota2:
Dosificación de micro esfera

La cantidad de esferas de vidrio en la película de pintura en húmedo, según su tipo, será la que se indica en la Tabla.

Nota 3:

Se aplicará solo en señalamiento de guarnicion conpintura para trafico base solvente tipo alquidal de secado rápido, que cumpla con las especificaciones n-cmt-5-01-001/05, n-pry-car-10-01-002/13 de la SCT aplicadas al día de hoy.

TABLA 8: Cantidad de esferas de vidrio en la pelicula de pintura en humedo.

CANTIDAD DE ESFERAS DE VIDRIO EN LA PELÍCULA DE PINTURA EN HÚMEDO				
TIPO DE PINTURA	ESPESOR DE LA PELÍCULA DE PINTURA EN HÚMEDO mm	CANTIDAD DE ESFERAS EN PESO		TIPO DE GRANULOMETRÍA
		INTEGRADAS	SUPERFICIAL MÍNIMO	
BASE SOLVENTE	0.30 A 0.50	-	0.330	I
BASE AGUA	0.30 A 0.50	-	0.330	I o II
TERMOPLÁSTICA	1.50 A 3.00	-	0.330	II


INDICA REVISIÓN NUMERO 1


01

SUSTITUYE A PLANO SEÑ-02 No. 03, JUNIO 2022 POR PLANO SEÑ-02, No. 03, SEPTIEMBRE 2022.


NOTA: LA SEÑALIZACIÓN HORIZONTAL Y VERTICAL DE LA CICLOVIA NO ESTA CONSIDERADA EN ESTE PROYECTO.

La Dirección de Planeación y Proyectos solo autoriza el proyecto ejecutivo, no es responsable de la correcta ejecución de la obra. Este documento no tiene validez si no presenta las firmas de los responsables para su autorización, así como los sellos respectivos.

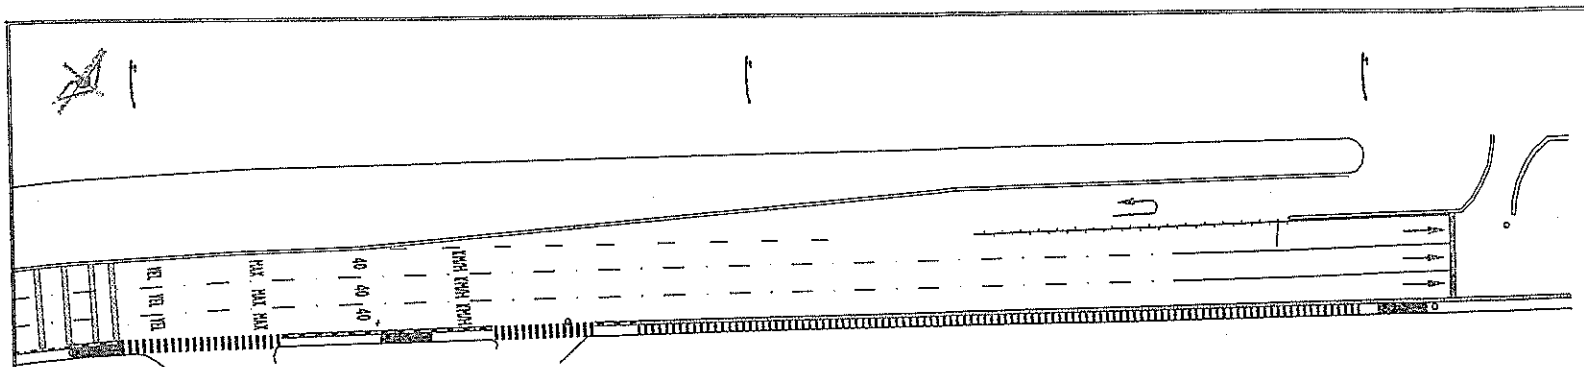


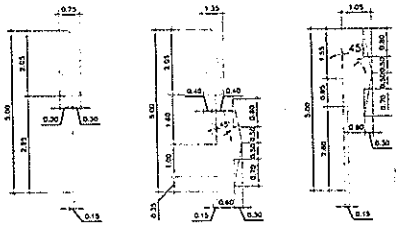


DETALLE DE FLECHAS EN PAVIMENTO
PARA VELOCIDADES HASTA DE 60KM/H
ESCALA 1:50 COTAS EN m

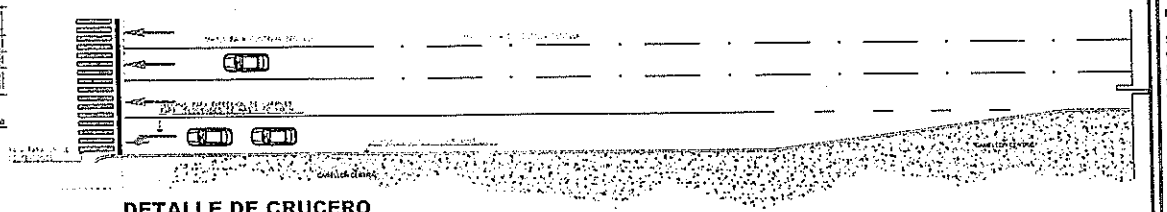


DETALLE DE CRUCERO
ESCALA 1:200 COTAS EN m

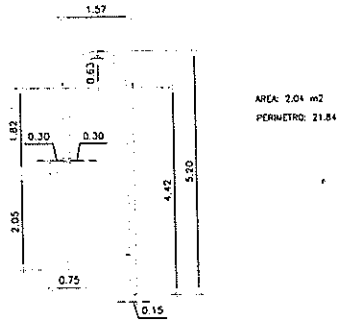

AREA: 2.04 m2
PERIMETRO: 21.84

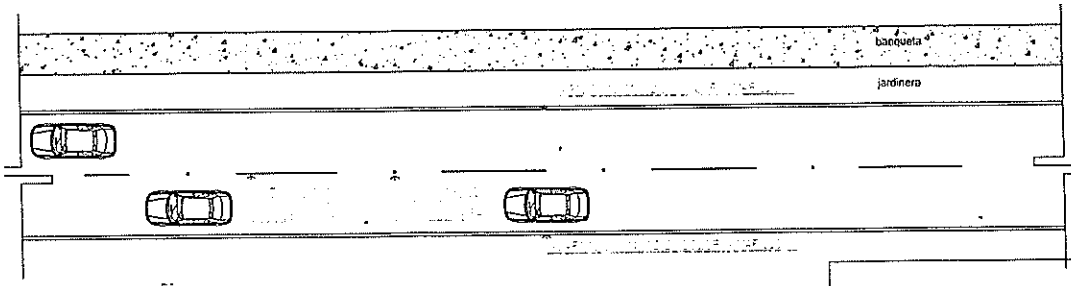

DETALLE DE FLECHA VUELTA U EN PAVIMENTO
PARA VELOCIDADES HASTA DE 60KM/H
ESCALA 1:50 COTAS EN m

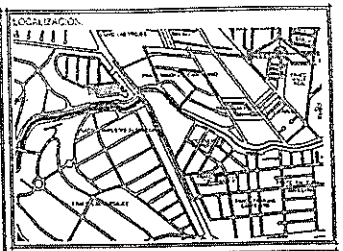

SIMBOLOGÍA

NOTA:

Nota1:

Se aplicará en todos los señalamientos horizontales pintura para trafico termoplastica base alquidalica de secado rápido, que cumpla con las especificaciones n-cmt-5-01-001/05, n-pry-car-10-01-002/13 de la SCT aplicadas al día de hoy.

Nota2:
Dosificación de micro esfera

La cantidad de esferas de vidrio en la película de pintura en húmedo, según su tipo, será la que se indica en la Tabla.

Nota 3:


Se aplicará solo en señalamiento de guarnicion conpintura para trafico base solvente tipo alquidal de secado rápido, que cumpla con las especificaciones n-cmt-5-01-001/05, n-pry-car-10-01-002/13 de la SCT aplicadas al día de hoy.

TABLA 8: Cantidad de esferas de vidrio en la pelicula de pintura en humedo.

CANTIDAD DE ESFERAS DE VIDRIO EN LA PELÍCULA DE PINTURA EN HÚMEDO

TIPO DE PINTURA	ESPESOR DE LA PELÍCULA DE PINTURA EN HÚMEDO mm	CANTIDAD DE ESFERAS EQ/M2 INTEGRADAS	MINERALIZADAS, MÍNIMO	TIPO DE GRANULOMETRÍA
BASE SOLVENTE	0.30 A 0.50		0.330	I
BASE AGUA	0.38 A 0.50		0.330	I O II
TERMOPLASTICA	3.50 A 3.60		0.330	II

La Dirección de Planeación y Proyectos solo autoriza el proyecto ejecutivo, no es responsable de la correcta ejecución de la obra. Este documento no tiene validez si no presenta las firmas de los responsables para su autorización, así como los sellos respectivos.

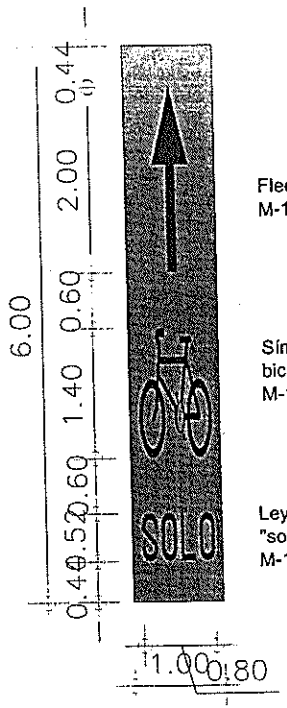

Flecha
M-11.1

Símbolo de
bicicleta
M-15

Leyenda
"solo"
M-11.3


DETALLE DE CAJA BICI Y MARCAS DE CARRIL EXCLUSIVO

ESCALA 1:25

PINTURA TERMOPLASTICA BASE ALQUIDALICA EN MARCAS PARA INDENTIFICAR CICLOVÍA, COLOR BLANCO REFLEJANTE CON MICROSESFERA DE VIDRIO, SEGÚN NORMA SCT. SE COMPONE DE UNA FLECHA QUE INDIQUE EL SENTIDO DE CIRCULACIÓN, LA LEYENDA "SOLO" Y EL SÍMBOLO DE LA BICICLETA.

PINTURA BASE SOLVENTE EN FONDO DE GRUPO DE MARCAS PARA IDENTIFICAR CAJA BICI, COLOR VERDE 7481 C PANTONE, REFLEJANTE CON MICROSESFERA, SEGÚN NORMA SCT. DE 1.00 X 6.00 MTS. SOBRE EL EJE DE LA CICLOVÍA.


VER PLANOS PG-01 Y PG-02

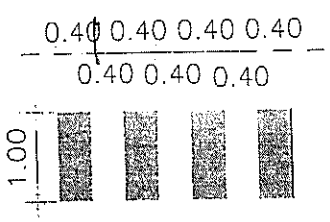

RAYA PARA CRUCE DE CICLISTAS

ESCALA 1:25


PINTURA TERMOPLASTICA BASE ALQUIDAL EN RAYA PARA INDICAR CRUCE CICLISTA CLASIFICACIÓN M-7.1, COLOR VERDE 7481 C PANTONE REFLEJANTE, CON MICROESFERA DE VIDRIO, SEGÚN NORMA SCT. DE 0.40 X 1.00 M. Y SEPARACIÓN ENTRE SI DE 0.40 M.

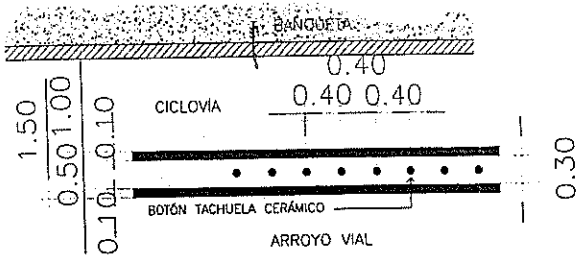

DETALLE DE CICLOCARRIL

ESCALA 1:25

PINTURA TERMOPLASTICA BASE ALQUIDALICO EN RAYA CLASIFICACIÓN M-2.2 LÍNEA CONTINUA DOBLE DE DIVISIÓN DE CARRILES DE FRENTE EN PISO, DE 10 CM. DE ANCHO Y SEPARACIÓN DE 30 CM. ENTRE ELLAS, COLOR BLANCO REFLEJANTE CON MICROSESFERA DE VIDRIO, SEGÚN NORMA SCT.

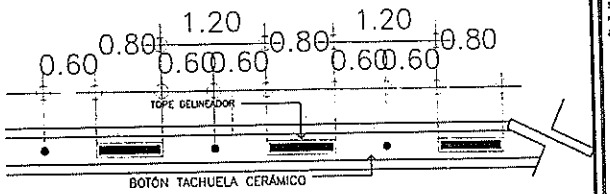


DETALLE DE DIMENSIONES PARA MARCAS DE CARRIL EXCLUSIVO

ESCALA 1:25


DELINEADOR DE CARRIL EXCLUSIVO TIPO "A" DE POLIETILENO DE ALTA DENSIDAD CON PROTECCION DE ESTABILIZADO DE RAYOS UV, COLOR AMARILLO REFLEJANTES EN ROJO DE 80*50*20 CMS MARCA HERSAN, PARA COLOCAR EN CARRIL CONFINADO CICLISTA. INDICA EL INICIO DE CICLOVÍA SEGREGADA, COLOCACIÓN AL CENTRO DEL ESPACIO QUE SEPARA LA LÍNEA CONTINUA DOBLE.

BOTÓN TACHUELA DE ABS CERÁMICO DE ALTA RESISTENCIA COLOR BLANCO (VT-32), DIÁMETRO DE 10 CM. ALTURA NO MAYOR DE 2 CM. MARCA CREATIVIAL O SIMILAR EN CALIDAD Y ESPECIFICACIONES DE FICHA TÉCNICA, SEGÚN NORMA SCT.

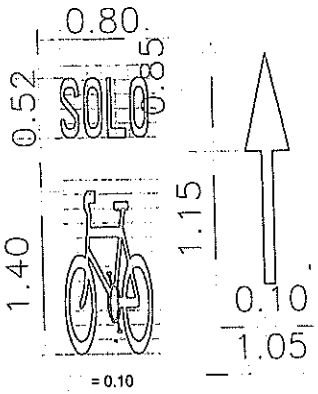

DIMENCIONES DE MARCAS

SIN ESCALA

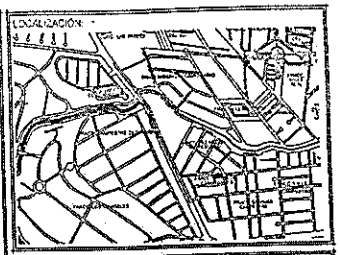

SIMBOLOGÍA

NOTA:

Nota1:

Se aplicará en todos los señalamientos horizontales pintura para trafico termoplastica base alquidalica de secado rápido, que cumpla con las especificaciones n-crnt-5-01-001/05, n-pry-car-10-01-002/13 de la SCT aplicadas al día de hoy.

Nota2:
Dosificación de micro esfera

La cantidad de esferas de vidrio en la película de pintura en húmedo, según su tipo, será la que se indica en la Tabla.


Nota 3:

Se aplicará solo en señalamiento de guarnicion conpintura para tráfico base solvente tipo alquidal de secado rápido, que cumpla con las especificaciones n-crnt-5-01-001/05, n-pry-car-10-01-002/13 de la SCT aplicadas al día de hoy.


TABLA 8: Cantidad de esferas de vidrio en la pelicula de pintura en humedo.

CANTIDAD DE ESFERAS DE VIDRIO EN LA PELÍCULA DE PINTURA EN HÚMEDO				
TIPO DE PINTURA	ESPESOR DE LA PELÍCULA DE PINTURA EN HÚMEDO mm	CANTIDAD DE ESFERAS KG/M2		TIPO DE GRANULOMETRIA
		INTEGRADA	SEMBRADA, MÍNIMO	
BASE SOLVENTE	0,30 A 0,38	-	0,330	I
BASE AGUA	0,33 A 0,38	-	0,330	I-II
TERMOPLÁSTICA	3,50 A 3,00	-	0,330	II

La Dirección de Planeación y Proyectos solo autoriza el proyecto ejecutivo, no es responsable de la correcta ejecución de la obra. Este documento no tiene validez si no presenta las firmas de los responsables para su autorización, así como los sellos respectivos.

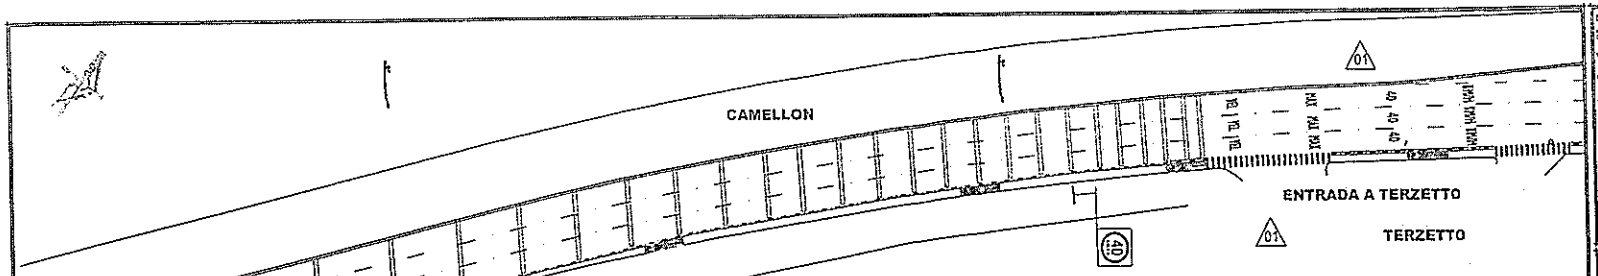


N DE
AGO

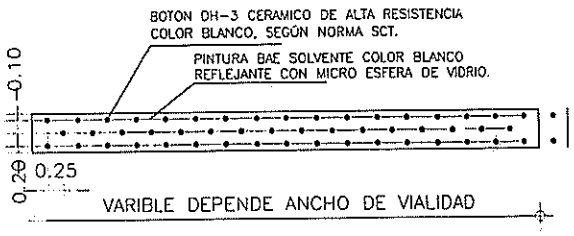

DETALLE 1 SEPARACION DE DH-3 EN RAYAS DE ESPARCIMIENTO LOGARITMICO

ESCALA 1:25

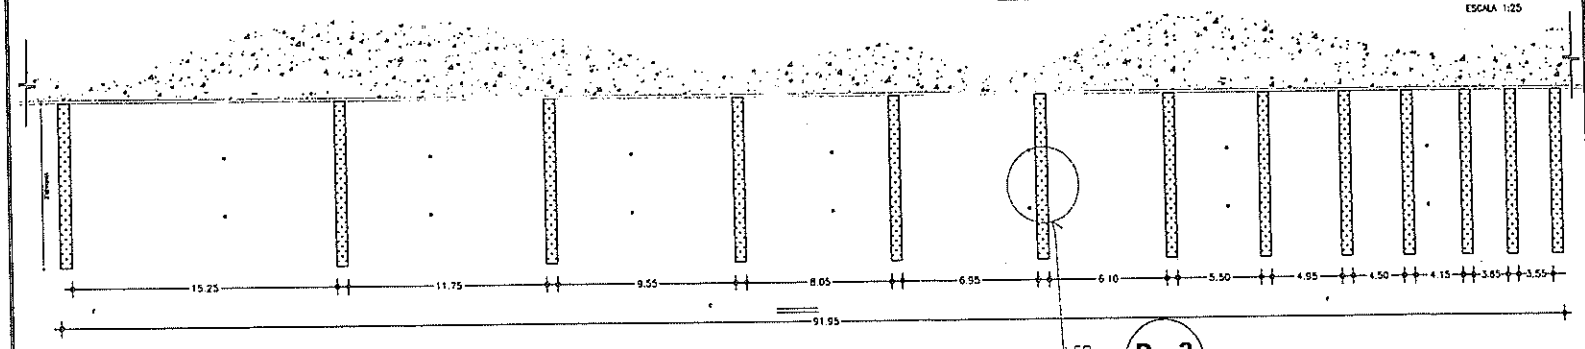


VER DETALLE D - 3 SER-01

RAYAS CON ESPARCIMIENTO LOGARITMICO

ESCALA S/E

PINTURA TERMOPLASTICA BASE ALQUIDALICA EN "RAYAS DE ESPARCIMIENTO LOGARITMICO M-9 EN VIALIDADES PARA DISMINUIR LA VELOCIDAD DE LOS VEHICULOS DIFERENTES DIMENSIONES COLOR BLANCO REFLEJANTE CON MICROSESFERA DE VIDRIO, SEGÚN NORMA SCT. SE COMPONE DE UNA LINEAS DE 60 CM DE ANCHO Y DE UN LARGO VARIABLE REFENTE A LA VIALIDAD CON BOTONES DH-3 CERAMICO DE ALTA RESISTENCIA COLOR BLANCO, LA LONGITUD TOTAL DE LA ZONA A MARCAR, EL NUMERO DE RAYAS Y SU SEPARACIÓN, SE DEBEN DETEMINAR CONFORME A LO SEÑALADO EN LA TABLA III.2-3. DEL MANUAL DE SCT.

LOCALIZACIÓN:

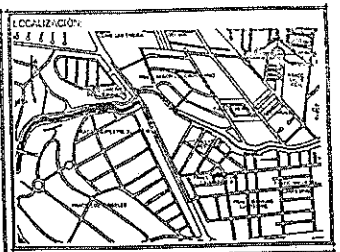

SIMBOLOGÍA

NOTA:

Nota1:

Se aplicará en todos los señalamientos horizontales pintura para trafico termoplastica base alquidalica de secado rápido, que cumpla con las especificaciones n-cmt-5-01-001/05, n-pry-car-10-01-002/13 de la SCT aplicadas al día de hoy.

Nota2:
Dosificación de micro esfera

La cantidad de esferas de vidrio en la película de pintura en húmedo, según su tipo, será la que se indica en la Tabla.

Nota 3:

Se aplicará solo en señalamiento de guarnición conpintura para trafico base solvente tipo alquidal de secado rápido, que cumpla con las especificaciones n-cmt-5-01-001/05, n-pry-car-10-01-002/13 de la SCT aplicadas al día de hoy.

TABLA 8: Cantidad de esferas de vidrio en la pelicula de pintura en humedo.


CANTIDAD DE ESFERAS DE VIDRIO EN LA PELICULA DE PINTURA EN HÚMEDO				
TIPO DE PINTURA	ESPESOR DE LA PELÍCULA DE PINTURA EN HÚMEDO mm	CANTIDAD DE ESFERAS KG/M2 INTEGRADAS	SEMBRADAS MÍNIMO	TIPO DE GRANULOMETRIA
BASE SOLVENTE	0.30 A 0.50	-	0.330	I
BASE AGUA	0.34 A 0.50	-	0.330	I o II
TERMOPLÁSTICA	1.50 A 3.00	-	0.330	II


INDICA REVISIÓN NUMERO 1 — 01

SUSTITUYE A PLANO SER-01, No. 04, SEPTIEMBRE 2022 POR PLANO SER-01, No. 04, SEPTIEMBRE 2022

NOTA: LA SEÑALIZACIÓN HORIZONTAL Y VERTICAL DE LA CICLOVÍA NO ESTÁ CONSIDERADA EN ESTE PROYECTO.

La Dirección de Planeación y Proyectos solo autoriza el proyecto ejecutivo, no es responsable de la correcta ejecución de la obra. Este documento no tiene validez si no presenta las firmas de los responsables para su autorización, así como los sellos respectivos.

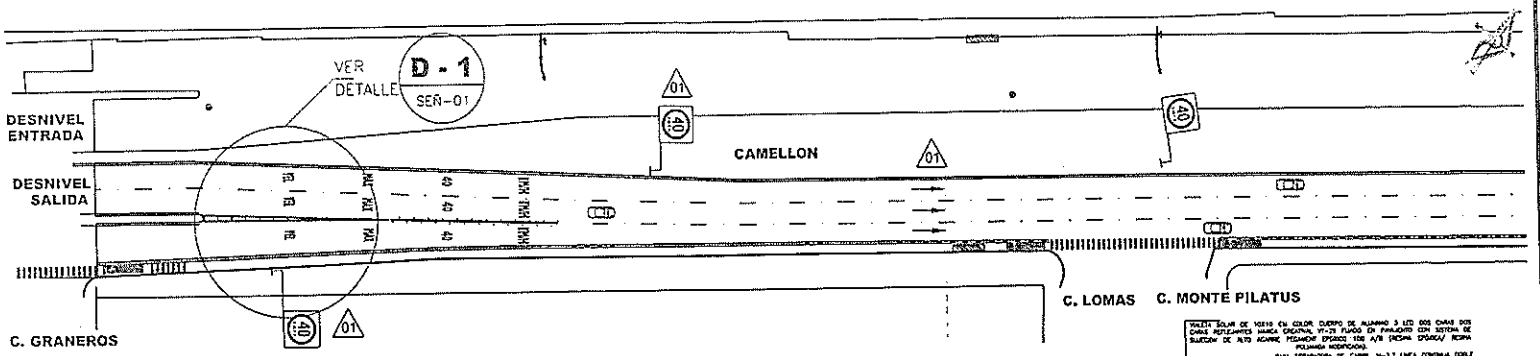

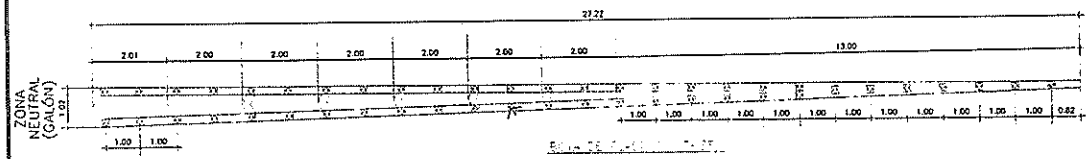


RAYAS CANALIZADORAS
ZONA NEUTRAL


ESCALA 1:50 COTAS EN m



DETALLE DE TRAZO DE TEXTO PARA SEÑALIZACIÓN HORIZONTAL

ESCALA 1:50 COTAS EN m

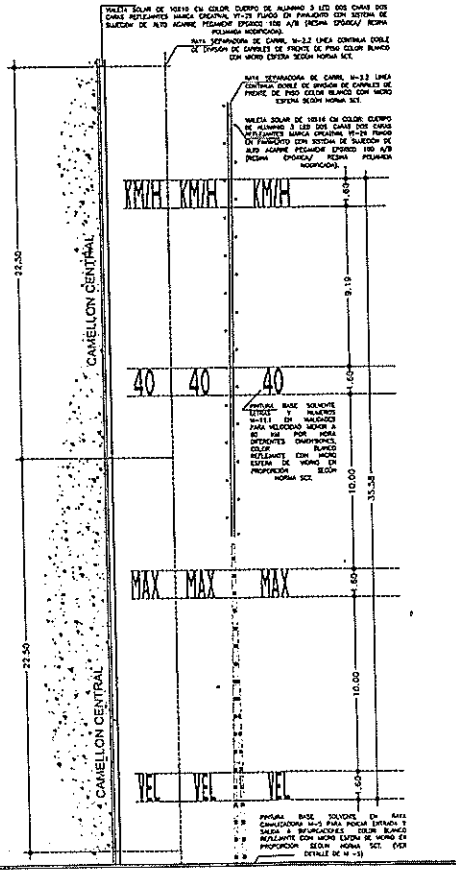

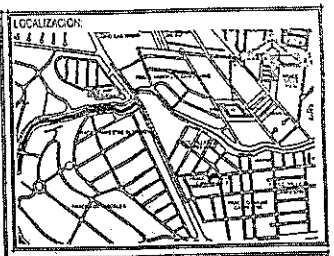

SIMBOLOGIA

NOTA:

Nota1:

Se aplicará en todos los señalamientos horizontales pintura para trafico termoplastica base alquidalica de secado rápido, que cumpla con las especificaciones n-cmt-5-01-001/05, m-pry-car-10-01-002/13 de la SCT aplicadas al día de hoy.

Nota2:
Dosificación de micro esfera

La cantidad de esferas de vidrio en la película de pintura en húmedo, según su tipo, será la que se indica en la Tabla.

Nota 3:

Se aplicará solo en señalamiento de guarnicion conpintura para trafico base solvente tipo alquidal de secado rápido, que cumpla con las especificaciones n-cmt-5-01-001/05, m-pry-car-10-01-002/13 de la SCT aplicadas al día de hoy.

TABLA 8: Cantidad de esferas de vidrio en la película de pintura en humedo.

CANTIDAD DE ESFERAS DE VIDRIO EN LA PELÍCULA DE PINTURA EN HUMEDO				
TIPO DE PINTURA	ESPESOR DE LA PELÍCULA DE PINTURA EN HÚMEDO mm	CANTIDAD DE ESFERAS KG/M2 INTEGRADAS	SUBMERGIDAS MÍNIMO	TIPO DE GRANULOMETRÍA
BASE SOLVENTE	0,30 A 0,50		0,350	I
BASE AGUA	0,38 A 0,50		0,330	I o II
TERMOPLÁSTICA	0,50 A 3,00		0,330	II

LIMITE DE PROYECTO


INDICA REVISIÓN NUMERO 1

01


SUSTITUYE A PLANO SER-01, No. 02, JUNIO 2022 POR PLANO SER-01, No. 02, SEPT 2022.

NOTA: LA SEÑALIZACIÓN HORIZONTAL Y VERTICAL DE LA CICLOVIA NO ESTÁ CONSIDERADA EN ESTE PROYECTO.

La Dirección de Planeación y Proyectos solo autoriza el proyecto ejecutivo, no es responsable de la correcta ejecución de la obra. Este documento no tiene validez si no presenta las firmas de los responsables para su autorización, así como los sellos respectivos.

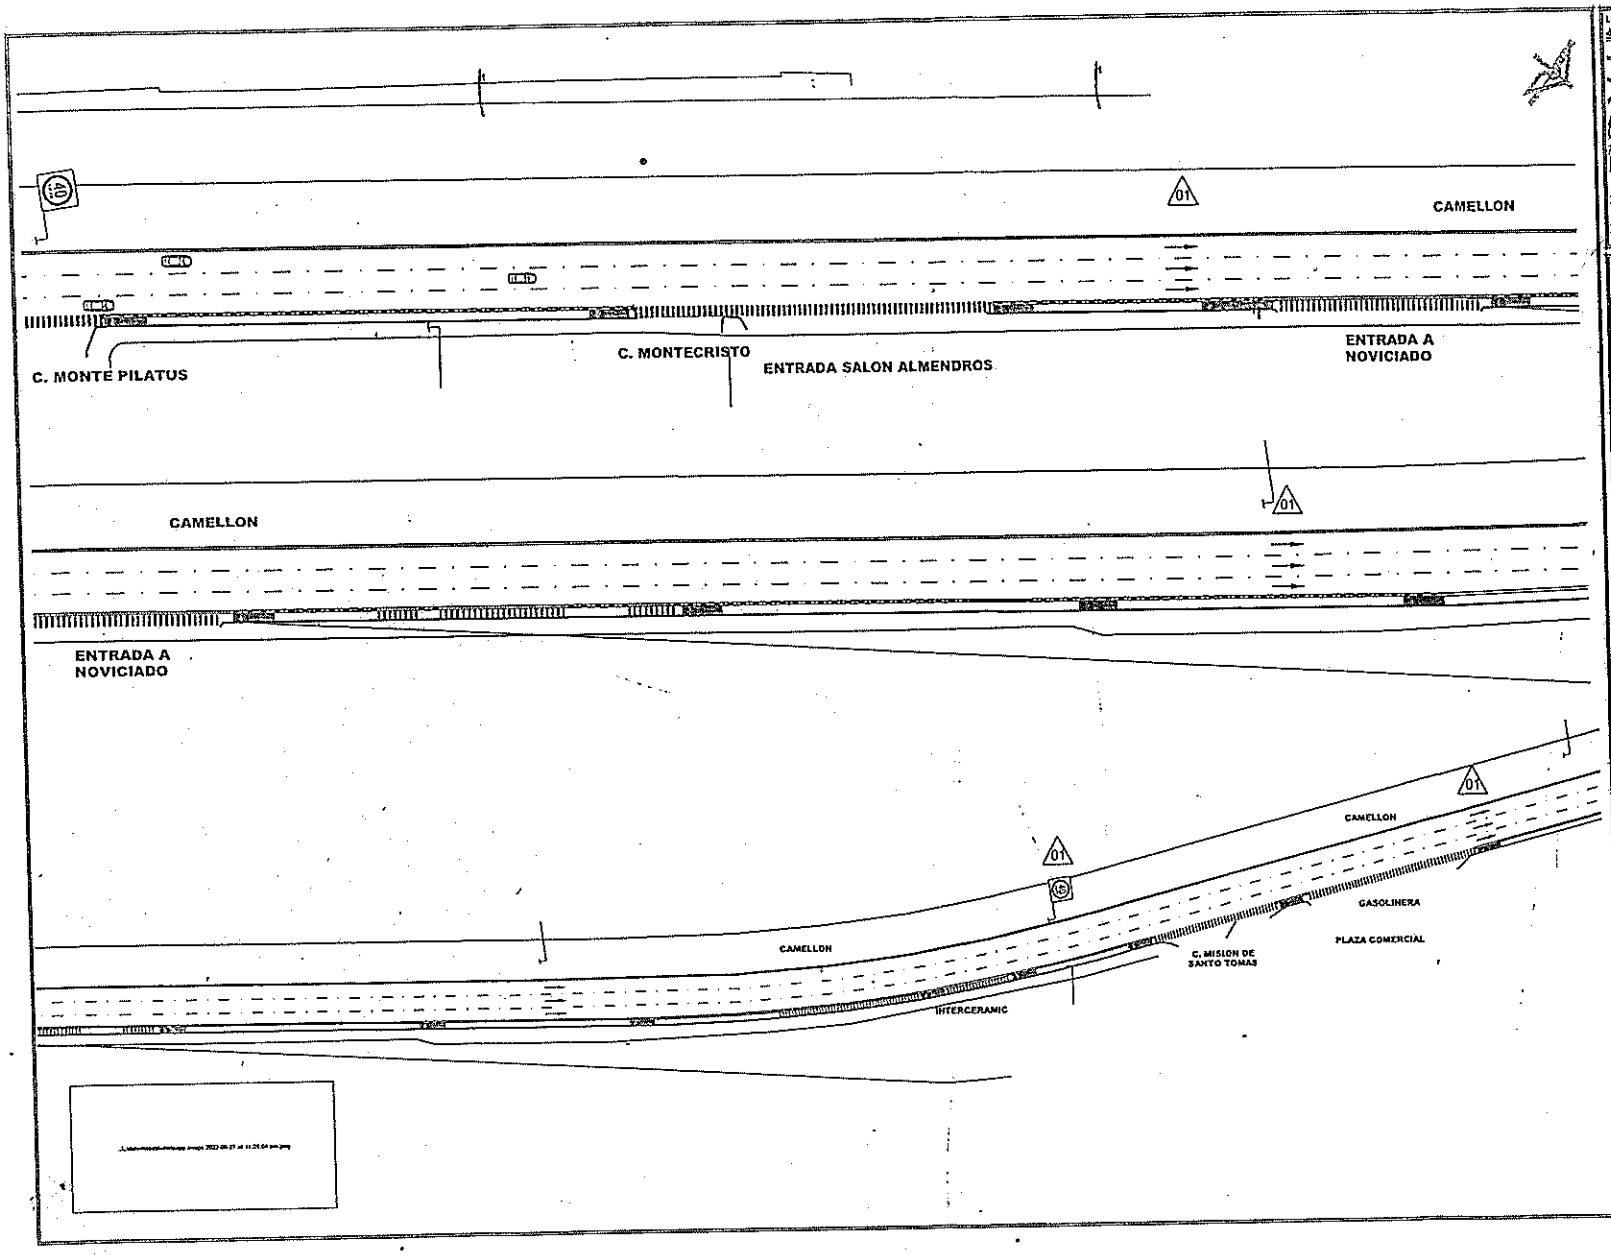

LOCALIZACIÓN:

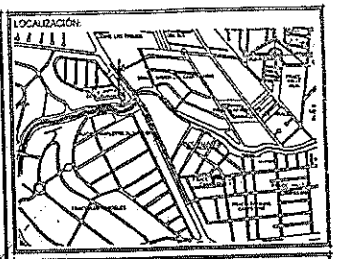

SIMBOLOGÍA

NOTA:

Nota1:

Se aplicará en todos los señalamientos horizontales pintura para trafico termoplastica base alquidalica de secado rápido, que cumpla con las especificaciones n-cmt-5-01-001/05, n-pry-car-10-01-002/13 de la SCT aplicadas al día de hoy.

Nota2:
Dosificación de micro esfera

La cantidad de esferas de vidrio en la pelicula de pintura en húmedo, según su tipo, será la que se indica en la Tabla.

Nota 3:

Se aplicará solo en señalamiento de guarnicion conpintura para trafico base solvente tipo alquidal de secado rápido, que cumpla con las especificaciones n-cmt-5-01-001/05, n-pry-car-10-01-002/13 de la SCT aplicadas al día de hoy.

TABLA 8: Cantidad de esferas de vidrio en la pelicula de pintura en humedo.

CANTIDAD DE ESFERAS DE VIDRIO EN LA PELÍCULA DE PINTURA EN HÚMEDO				
TIPO DE PINTURA	ESPESOR DE LA PELÍCULA DE PINTURA EN HÚMEDO mm	CANTIDAD DE ESFERAS KG/M2		TIPO DE GRANULOMETRÍA
		INTEGRADAS	SUPERFICIAL MÍNIMO	
BASE SOLVENTE	0,30 A 0,50	-	0,330	I
BASE AGUA	0,20 A 0,30	-	0,330	I o II
TERMOPLÁSTICA	1,50 A 3,00	-	0,330	II

INDICA REVISIÓN NUMERO 1 01

SUSTITUYE A PLANO SEÑ-02, No. 03, JUNIO 2022 POR PLANO SEÑ-02, No. 01, SEPTIEMBRE 2022.

NOTA: LA SEÑALIZACIÓN HORIZONTAL Y VERTICAL DE LA CICLOVIA NO ESTA CONSIDERADA EN ESTE PROYECTO.

La Dirección de Planeación y Proyectos solo autoriza el proyecto ejecutivo, no es responsable de la correcta ejecución de la obra. Este documento no tiene validez si no presenta las firmas de los responsables para su autorización, así como los sellos respectivos.