Aguascalientes
LA CIUDAD DE TU VIDA

Dirección de Programación Presupuestal
Núm. Oficio AMPP/0579/22
Aguascalientes, Ags. 8 de Diciembre del 2022
Asunto: Validación de Expediente Técnico

C.P. SERGIO ARTURO LOZANO GONZÁLEZ
SECRETARIO DE FINANZAS MUNICIPALES
P R E S E N T E

Con fundamento en los artículos 17 fracción XV, 60 fracción XVI y 76 fracción VI del Reglamento del Sistema Integral de Desarrollo Municipal y del Instituto Municipal de Planeación y Evaluación de Aguascalientes, hago referencia al oficio SOPMA/2736/2022 recibido por este Instituto el día 8 de Diciembre del 2022 por parte de la Secretaría de Obras Públicas Municipales, mediante el cual remiten el expediente técnico original de la siguiente obra para su análisis, registro y priorización, conforme al Programa Anual de Obra Pública y Programas Sociales para el ejercicio presupuestal 2022:

DEPENDENCIA EJECUTORA:	SOPMA
NOMBRE DE LA OBRA O PROYECTO:	OBRA COMPLEMENTARIA Y SEÑALIZACIÓN
UBICACIÓN:	AV MAHATMA GANDHI (CALZADA PONIENTE), ENTRE AV. SIGLO XXI Y CENTRAL DE ABASTOS, VARIAS COLONIAS, AGUASCALIENTES, AGS.
FONDO DE INVERSIÓN:	FONDO DE INFRAESTRUCTURA SOCIAL MUNICIPAL Y DE LAS DEMARCACIONES TERRITORIALES DEL DISTRITO FEDERAL
IMPORTE:	$1,195,639.63 (ET FINAL)
No. DE OBRA:	2022-FISMDF-0097-04-1101
MODALIDAD DE EJECUCIÓN:	CONTRATO
EJE:	MUNICIPIO SOBRESALIENTE
ESTRATEGIA:	OBRA PÚBLICA INTELIGENTE
POLITICA:	5.8.1.REHABILITACIÓN Y MANTENIMIENTO VIALIDADES, CAMINOS, CALLES, ÁREAS DE TERRACERÍA Y CAUCES (C

Al respecto, hago de su conocimiento que dicho expediente ha sido analizado en su integración técnica y documental, con base en el artículo 168 fracción I del Reglamento de la Ley de Obras Públicas y Servicios Relacionados para el Estado de Aguascalientes y sus Municipios.

Asimismo, le comento que este Instituto valida dicha obra acorde a lo establecido en los artículos 14, 22 párrafo segundo y 23 de la Ley de Obras Públicas y Servicios Relacionados para el Estado de Aguascalientes y sus Municipios, la cual se encuentra alineada al Plan de Desarrollo Municipal vigente, para dar cumplimiento a las metas establecidas en el mismo, y a los Lineamientos Generales para la Operación de este Fondo de Inversión, toda vez que la misma cuente con la autorización del CODEMUN. De igual manera, se hace de su conocimiento que deberá cumplir con lo establecido en los ordenamientos aplicables en lo que respecta al ejercicio, control e información de los recursos de este Fondo. Cabe hacer mención que los recursos solicitados para este proyecto de inversión, estarán sujetos a la disponibilidad presupuestal para el presente ejercicio fiscal que determine la Secretaría a su digno cargo. Sin otro particular por el momento, le envío un cordial saludo.

A T E N T A M E N T E

ARQ. AUSTRIA GABRIELA DÁVILA DE LA LLAVE
DIRECTORA GENERAL DEL IMPLAN

SEDR/ CAAR / JDBC
C.c.p. I.C. ING. MIGUEL ÁNGEL HUIZAR BOTELLO .- Secretaría de Obras Públicas Municipales .Para su conocimiento.
C.c.p. Archivo.

Instituto Municipal de Planeación y Evaluación de Aguascalientes
Antonio Acevedo Escobedo 103 A. Col. Centro
Aguascalientes. Ags. C.P. 20000
(449) 9101010 Ext. 3117
www.implanags.gob.mx

GOBIERNO MUNICIPAL DE AGUASCALIENTES

INSTITUTO MUNICIPAL DE PLANEACION

IMPLAN

ANÁLISIS INTEGRAL DE EXPEDIENTE TÉCNICO

No. DE OBRA (PAOP 2020):	2022-FISMDF-0097-04-1101	REGISTRO No.	262
OFICIO DE VALIDACIÓN:	AMPP/0579/22	FECHA RECIBIDO PARA REVISIÓN:	8 de Diciembre del 2022
PROGRAMA:	URBANIZACION MUNICIPAL	LOCALIDAD O COLONIA:	VARIAS COLONIAS
SUB-PROGRAMA:	0411- Calles y Caminos	DELEGACIÓN:	Aguascalientes
DEPENDENCIA:	Secretaría de Obras Públicas Municipales	MOD. DE EJECUCIÓN:	CONTRATO
NOMBRE DE LA OBRA:	OBRA COMPLEMENTARIA Y SEÑALIZACIÓN, AV MAHATMA GANDHI (CALZADA PONIENTE), ENTRE AV. SIGLO XXI Y CENTRAL DE ABASTOS		
FUENTE DE FINANCIAMIENTO:	FONDO DE INFRAESTRUCTURA SOCIAL MUNICIPAL Y DE LAS DEMARCACIONES TERRITORIALES DEL DISTRITO FEDERAL, FISMDF		
INVERSIÓN:	$1,195,639.63	CLASIFICACIÓN DE OBRA:	BIENES DE DOMINIO PUBLICA

TOTAL	FEDERAL	ESTATAL	MUNICIPAL	BENEFICIARIOS	OTROS	DIFERENCIA ENTRE MOD.
$1,195,639.63	$1,195,639.63	0.00	0.00	0.00	0.00	*$0,00*

TIPO DE EXPENDIENTE:	ET FINAL	AÑO: 2022	AÑO:	AÑO:		
AVANCES:	Financiero: 84 %		Físico: 100 %			
FECHA DE INICIO:	23 de Septiembre del 2022	FECHA DE TÉRMINO:	22 de Octubre del 2022	REGISTRO SIMA:	97	

CHEK LIST DE LOS ANEXOS DEL EXPEDIENTE TÉCNICO

CÉDULA DE REGISTRO DE OBRA	✓
DICTAMEN DE FACTIBILIDAD	✓
MEMORIA DESCRIPTIVA	✓
PRESUPUESTO BASE	✓
FACTIBILIDAD VERIFICADA EN CAMPO	✓
CROQUIS DE UBICACIÓN (MACRO)	✓
CROQUIS DE UBICACIÓN (MACRO)	✓
PROGRAMA DE OBRA Y MONTOS MENSUALES	✓
PLANOS O ESTUDIOS TÉCNICOS	✓
PADRÓN DE BENEFICIARIOS	N/A
ACTA DE ACEPTACIÓN DEL PROYECTO	N/A
DICTAMEN DE IMPACTO AMBIENTAL	N/A
CONVENIO DE CONCERTACIÓN	N/A
ACTA CONSTITUTIVA	N/A

METAS		BENEFICIARIOS		PERIODO DE EJECUCION		OBRA PROPUESTA		CLAVE SISCO
UNIDAD DE MEDIDA	CANT	TIPO DE BENEFICIARIOS	CANTIDAD	FECHA DE INICIO	FECHA DE TERMINO	CONCEPTO	JORNALES A GENERAR	
OBRA	1	Personas	400	2022-09-23	2022-10-22	Obra Complementaria y/o Señalización	3108	2366

INCLUIDO EN PLAN DE DESARROLLO MUNICIPAL Y EL PROGRAMA ANUAL DE OBRA PÚBLICA

OBSERVACIONES:

SIN OBSERVACIONES

RECIBIO: ING. JOSÉ DAVID BURGUETE CLAUSTRO
Analista de Programación e Inversión de Obra Pública

8 de Diciembre del 2022
Fecha de validación

8 de Diciembre del 2022
Fecha de validación Expediente

PROCEDE Si ✓ No

H. AYUNTAMIENTO CONSTITUCIONAL DEL MUNICIPIO DE AGUASCALIENTES 2021-2024

AYUNTAMIENTO DE AGUASCALIENTES

CEDULA DE REGISTRO POR OBRA

Aguascalientes

050400-001E00E05-05-2-2-1-00-1-E-0510-0-17-0097-21-2502-6144

2022-FISMDF-0097-0411109-051	Obra **OBRA COMPLEMENTARIA Y SEÑALIZACIÓN AV. MAHATMA GANDHI (CALZADA PONIENTE)**
Tipo DEFINITIVO 2 2022	Ubic. TRAMO: ENTRE BLVD. SIGLO XXI Y CENTRAL DE ABASTOS, AGUASCALIENTES Mpio.
Folio SISCO **2366**	

Ent. Ejecutora : **050400001E00E05**

Eje: **05**	MUNICIPIO SOBRESALIENTE
Finalidad: **2**	DESARROLLO SOCIAL
Función: **2**	VIVIENDA Y SERVICIOS A LA COMUNIDAD
Subfunción: **1**	URBANIZACIÓN
Tema: **00**	SIN TEMA
Cuenta del Gasto **1**	GASTO PROGRAMABLE
Clasif. Programatica: **E**	PRESTACIÓN DE SERVICIOS PÚBLICOS
Programa: **0510**	Movilidad Urbana
SubPrograma: **0**	SUBPROGRAMA GENÉRICO
Proyecto: **17**	
Tipo de Gasto: **21**	GASTO INVERSIÓN / OBRA PÚBLICA

I N V E R S I O N 2022

Municipal	2502	FONDO PARA LA INFRAESTRUCTURA SOCIAL MUNICIPAL Y DE LAS DEMARCACIONES TERRITORIALES DEL DISTRITO FEDERAL 2022	$1,195,639.63

Folio SIMA 97 Total $1,195,639.63

M E T A S

Unidad de Medida	Cantidad	Descripción
OBRA	1	OBRA OBRA COMPLEMENTARIA Y SEÑALIZACIÓN AV. MAHATMA GANDHI (CALZADA PONIENTE)

Inversión Ejercida Total al 31 de Diciembre de 2021 $0.00

Avance Fisico Acumulado al 31 de Diciembre de 2021

Avance Fisico Acumulado Programado al 31 de Diciembre de 2022 100 %

Fecha de Inicio 23 Sep 2022 Fecha de Terminación 22 Oct 2022

Jornales a Generar en 2022 3108

Modalidad de ejecución CONTRATO

Clasificación de la Obra Bienes de Dominio Público

Registro del Patrimonio: Obras del dominio público

OBRAS PÚBLICAS

Av. Aguascalientes Sur No. 2615
Fracc. Jardines de las Fuentes,
Aguascalientes, Ags. C.P. 20278

(449) 9 78 92 01, 06, 09

www.ags.gob.mx

GENERALES

Nombre del Proyecto : OBRA COMPLEMENTARIA Y SEÑALIZACIÓN AV. MAHATMA GANDHI (CALZADA PONIENTE)

TRAMO: ENTRE BLVD. SIGLO XXI Y CENTRAL DE ABASTOS, AGUASCALIENTES Mpio.

Programa : 04 URBANIZACION MUNICIPAL

Subprograma : 11 Calles y caminos (428.- Rehabilitación: 0411208- Señalización)

Clave del Municipio : AGUASCALIENTES

Localidad :

Barrio, Colonia o Ejido : AGUASCALIENTES Mpio.

Tipo de Obra : NUEVA

DESCRIPCIÓN DEL PROYECTO:

OBRA COMPLEMENTARIA Y SEÑALIZACIÓN AV. MAHATMA GANDHI (CALZADA PONIENTE) 1.00 OBRA

Beneficiarios (No. y Tipo) :

400	PERSONAS

Hombres: 200 Mujeres: 200

OBRAS PÚBLICAS

Av. Aguascalientes Sur No. 2615
Fracc. Jardines de las Fuentes,
Aguascalientes, Ags. C.P. 20278

(449) 9 78 92 01, 06, 09

www.ags.gob.mx

Los abajo firmantes, hacen constar que el presente proyecto :

OBRA COMPLEMENTARIA Y SEÑALIZACIÓN AV. MAHATMA GANDHI (CALZADA PONIENTE)

TRAMO: ENTRE BLVD. SIGLO XXI Y CENTRAL DE ABASTOS, AGUASCALIENTES Mpio.

cumple con los Requisitos y Normas Técnicas establecidas por la Dependencia Normativa, por lo que es viable su ejecución. Comprometiéndose la misma a proporcionar la supervisión y asistencia técnica necesaria durante el proceso administrativo.

Por la Dependencia Ejecutora

Ing. Miguel Angel Huizar Botello
Secretario de Obras Públicas

Lic. Jaime Gallo Camacho
Secretario de Desarrollo Urbano

LUGAR :AGUASCALIENTES, AGS.

No. Folio SISCO 2366

H. AYUNTAMIENTO CONSTITUCIONAL DEL MUNICIPIO DE AGUASCALIENTES 2021-2024

AYUNTAMIENTO DE AGUASCALIENTES

FACTIBILIDAD VERIFICADA EN CAMPO

Aguascalientes
LA CIUDAD DE TU VIDA

MUNICIPIO: AGUASCALIENTES

LOCALIZACION: TRAMO: ENTRE BLVD. SIGLO XXI Y CENTRAL DE ABASTOS, AGUASCALIENTES Mpio.

PROGRAMA: URBANIZACION MUNICIPAL

SUBPROGRAMA: Calles y caminos (428.- Rehabilitación: 0411208- Señalización)

OBRA A REALIZAR: OBRA COMPLEMENTARIA Y SEÑALIZACIÓN AV. MAHATMA GANDHI (CALZADA PONIENTE)

DEPENDENCIA EJECUTORA: SECRETARÍA DE OBRAS PUBLICAS DEL MUNICIPIO DE AGUASCALIENTES

FORMA DE EJECUCION: CONTRATO

TIPO DE OBRA PROPUESTA: NUEVA

CONDICIONES ACTUALES DE LA OBRA:

OBRA COMPLEMENTARIA Y SEÑALIZACIÓN AV. MAHATMA GANDHI (CALZADA PONIENTE)

CARACTERISTICAS DE LA OBRA: Bueno

FACTIBILIDAD DE LA OBRA:

ESTA OBRA SE REQUIERE PARA EL BENEFICIO DE LA CIUDADANÍA

PROCEDE: SI [X] NO [ ]

REVISÓ: Jefa del Departamento de Expedientes Tecnicos y Costos

NOMBRE: Arq. Blanca Margarita Martinez Amador



FIRMA

FECHA: 28 Nov 2022

SECRETARÍA DE OBRAS PÚBLICAS

Av. Aguascalientes Sur No. 2615
Fracc. Jardines de las Fuentes,
Aguascalientes, Ags. C.P. 20278

(449) 9 78 92 01, 06, 09

www.ags.gob.mx

No. Folio SISCO 2366

H. AYUNTAMIENTO CONSTITUCIONAL DEL MUNICIPIO DE AGUASCALIENTES 2021 2024

Aguascalientes
LA CIUDAD DE TU VIDA

MACRO LOCALIZACIÓN

APROBACIÓN	**2022-FISMDF-0097-001-0411109-051**
NOMBRE DE LA OBRA:	**OBRA COMPLEMENTARIA Y SEÑALIZACIÓN AV. MAHATMA GANDHI (CALZADA PONIENTE)**
UBICACIÓN:	**TRAMO: ENTRE BLVD. SIGLO XXI Y CENTRAL DE ABASTOS, AGUASCALIENTES Mpio.**
PROGRAMA:	**04 - URBANIZACIÓN MUNICIPAL**




I.C. LAURA CECILIA MARTÍNEZ ALBA
RESIDENTE DE SUPERVISIÓN

H. AYUNTAMIENTO CONSTITUCIONAL DEL MUNICIPIO DE AGUASCALIENTES 2021 2024

Aguascalientes
LA CIUDAD DE TU VIDA

MICRO LOCALIZACIÓN

APROBACIÓN	**2022-FISMDF-0097-001-0411109-051**
NOMBRE DE LA OBRA:	**OBRA COMPLEMENTARIA Y SEÑALIZACIÓN AV. MAHATMA GANDHI (CALZADA PONIENTE)**
UBICACIÓN:	**TRAMO: ENTRE BLVD. SIGLO XXI Y CENTRAL DE ABASTOS, AGUASCALIENTES Mpio.**
PROGRAMA:	**04 - URBANIZACIÓN MUNICIPAL**

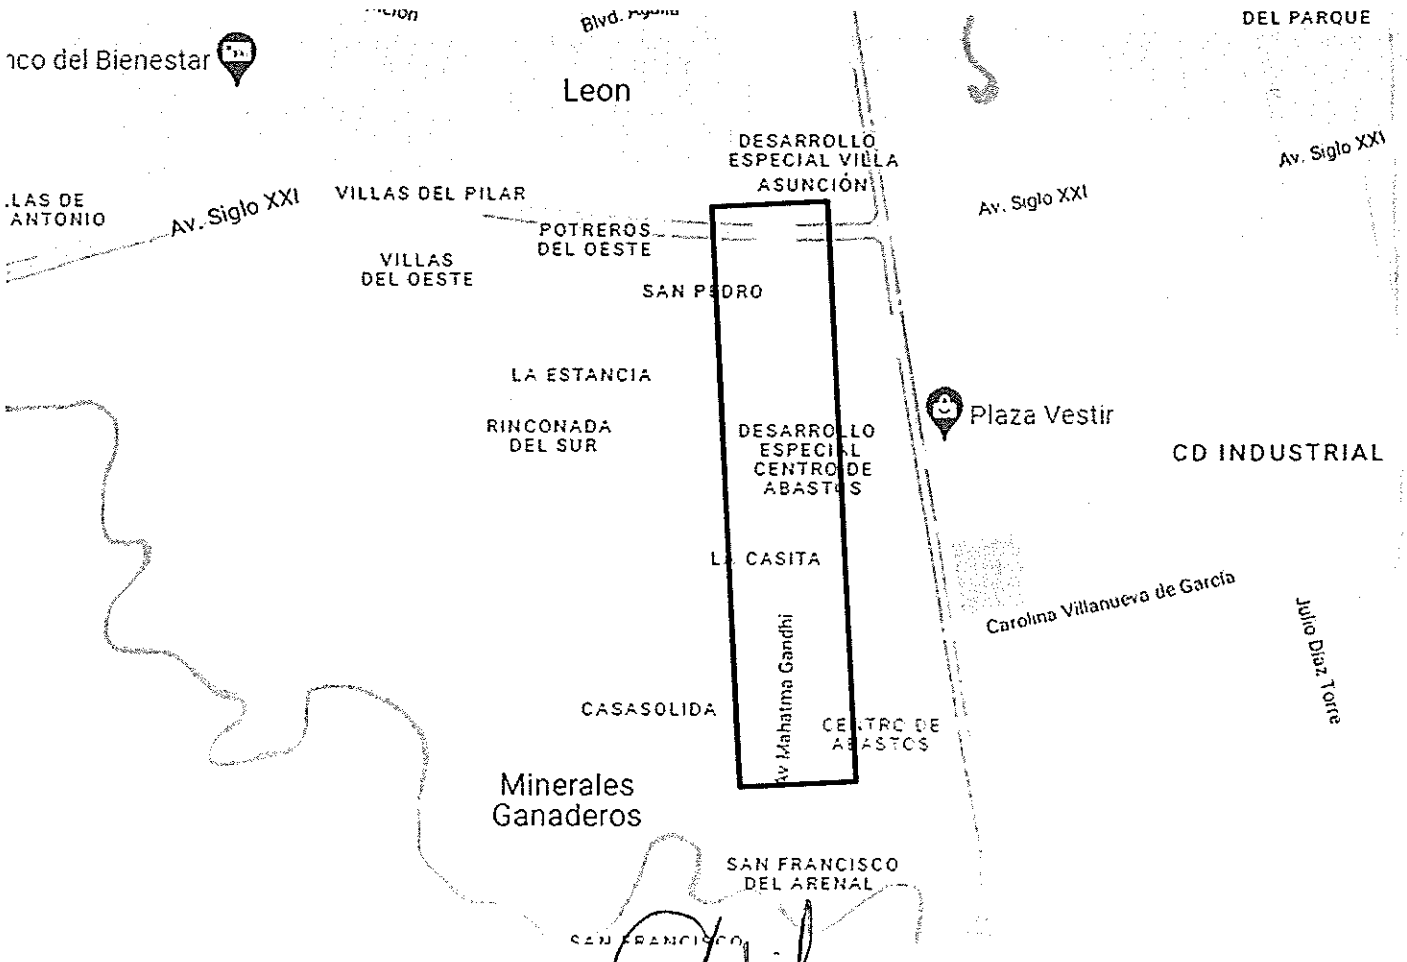

I.C. LAURA CECILIA MARTÍNEZ ALBA
RESIDENTE DE SUPERVISIÓN

PROGRAMA DE OBRA DEFINITIVO

Aguascalientes
LA CIUDAD DE TU VIDA

No. DE CONTRATO : FISMDF-0097-2022

PROGRAMA: 04 URBANIZACION MUNICIPAL

No. OBRA Y NOMBRE DE LA OBRA: 2022-FISMDF-0097-0411109-051 OBRA COMPLEMENTARIA Y SEÑALIZACIÓN AV. MAHATMA GANDHI (CALZADA PONIENTE), TRAMO: ENTRE BLVD. SIGLO XXI Y CENTRAL DE ABASTOS, AGUASCALIENTES Mpio.

INICIO VIGENTE: 23-septiembre-22

TERMINO REAL: 22-octubre-22

RECURSO 2022

CONCEPTO			1	2	3	4	5	6	7	8	9	10	11	12	13	14	15	16	PONDERACIÓN %	
			2021																	
			OCTUBRE	NOVIEMBRE	DICIEMBRE	ENERO	FEBRERO	MARZO	ABRIL	MAYO	JUNIO	JULIO	AGOSTO	SEPTIEMBRE	OCTUBRE	NOVIEMBRE	DICIEMBRE	ENERO	FINANCIERO	FÍSICO
DESCRIPCION	INVERSION													20	22					
OBRA COMPLEMENTARIA Y SENALIZACION AV. MAHATMA GANDHI (CALZADA PONIENTE)																				
TRAMO: ENTRE BLVD. SIGLO XXI Y ACCESO A CENTRAL DE ABASTOS, AGUASCALIENTES Mpio.																				
PRELIMINARES	$ 19,319.01	100												100					1.87	11.11
OBRA COMPLEMENTARIA	$ 496,300.58	100												50	50				48.15	22.22
LIMPIEZAS	$ 2,258.15	100												0	100				0.22	22.22
SENALIZACION HORIZONTAL	$ 512,846.07	100												25	75				49.76	44.44
SUBTOTAL SIN IVA	$ 1,030,723.81		0	0	0	0	0	0	0	0	0	0	0	4	2	1	2	0	100.00	100.00
AVANCE SEMANAL %			0%	0%	0%	0%	0%	0%	0%	0%	0%	0%	0%	44%	22%	11%	22%	0%		
AVANCE SEMANAL ACUMULADO %			0%	0%	0%	0%	0%	0%	0%	0%	0%	0%	0%	44%	67%	78%	100%	100%		
EJERCIDO SEMANAL $														396,809.89	136,803.51	129,211.52	170,340.89			
EJERCIDO MENSUAL $			$0.00	$0.00	$0.00	$0.00	$0.00	$0.00	$0.00	$0.00	$0.00	$0.00	$0.00	$396,809.89	$533,913.92	$0.00	$0.00	$0.00	$ 1,030,723.81	
EJERCIDO MENSUAL ACUMULADO $			0.00	0.00	0.00	0.00	0.00	0.00	0.00	0.00	0.00	0.00	0.00	396,809.89	1,030,723.81	1,030,723.81	1,030,723.81	1,030,723.81	$ 164,915.81	IVA 16%
EJERCIDO SEMANAL %			0%	0%	0%	0%	0%	0%	0%	0%	0%	0%	0%	38%	13%	13%	16%	0%		
EJERCIDO MENSUAL %			0%	0%	0%	0%	0%	0%	0%	0%	0%	0%	0%	38%	52%	0%	0%	0%	GRAN TOTAL EJERCIDO	
EJERCIDO MENSUAL ACUMULADO %			0%	0%	0%	0%	0%	0%	0%	0%	0%	0%	0%	38%	100%	100%	100%	100%	$	1,195,639.63

ING. LAURA CECILIA MARTÍNEZ ALBA
RESIDENTE DE SUPERVISIÓN

PRESIDENCIA MUNICIPAL DE AGUASCALIENTES

FACTIBILIDAD VERIFICADA EN CAMPO

GENERALES

EJERCICIO: 2022 APROBACION No: 2022-FISMDF-0097-001-0411109-051

LOCALIDAD: TRAMO: ENTRE BLVD. SIGLO XXI Y CENTRAL DE ABASTOS, AGUASCALIENTES Mpio.

MUNICIPIO: AGUASCALIENTES, Mpio.

TIPO DE INVERSION: FONDO PARA LA INFRAESTRUCTURA SOCIAL MUNICIPAL Y DE LAS DEMARCACIONES TERRITORIALES DEL DISTRITO FEDERAL

PROGRAMA: 04 URBANIZACION MUNICIPAL

SUB-PROGRAMA:

OBRA A REALIZARSE: OBRA COMPLEMENTARIA Y SEÑALIZACIÓN AV. MAHATMA GANDHI (CALZADA PONIENTE)

DEPENDENCIA EJECUTORA: SECRETARÍA DE OBRAS PÚBLICAS MUNICIPALES (S.O.P.M.A)

FORMACIÓN DE EJECUCION: CONTRATO NO. DE CONTRATO: FISMDF-0097-2022

NOMBRE CONTRATISTA: CASLOP DISEÑO ARTE Y CONSTRUCCION, S.A. DE C.V.

REPRESENTANTE: CASTAÑEDA LÓPEZ, JAIME FRANCISCO, ING.

MONTO CONT. ORIGEN	$1,195,639.63	ANTICIPO:	$309,217.15	PLAZO	30 DIAS
1A AMPLIACION $:	$ -	1 AMPL DIAS			
2A AMPLIACION $:		2 AMPL DIAS			
FIRMA CONTRATO:	19/09/2022				
INICIO CONT: dd/mm/aa	20/09/2022	TERMINO CONT:	19/10/2022		
INICIO REAL: dd/mm/aa	23/09/2022	TERMINO REAL:	22/10/2022		

TIPO DE OBRA PROPUESTA

NUEVA CREACIÓN		CONSOLIDACIÓN	
COMPLEMENTARIA	X	AMPLIACIÓN	
REHABILITACIÓN		EQUIPAMIENTO	

CARACTERÍSTICAS DE LA OBRA:

RENIVELACION DE POZOS DE VISITA, CAJAS DE VALVULAS

PINTURA EN GUARNICION

PINTURA PASOS PEATONALES

VIALETAS SOLARES, VIALETAS ESTÁNDAR

CONDICIONES ACTUALES DE LA OBRA: (SELECCIONAR UNO OBLIGATORIO)


BUEN ESTADO X REGULAR PESIMO ESTADO

FACTIBILIDAD DE LA OBRA: (CONDICIONES ACTUALES DE LA OBRA)

ESTA OBRA SE ENCUENTRA EN CONDICIONES PARA OPERARSE

PROCEDE: SI: X NO:

MARQUE SOLO UNA

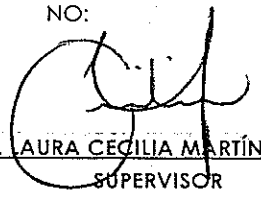

I.C. LAURA CECILIA MARTÍNEZ ALBA

SUPERVISOR

PRESIDENCIA MUNICIPAL DE AGUASCALIENTES

FACTIBILIDAD VERIFICADA EN CAMPO

GENERALES

LOCALIDAD: OBRA COMPLEMENTARIA Y SEÑALIZACIÓN AV. MAHATMA GANDHI (CALZADA PONIENTE), TRAMO: ENTRE BLVD. SIGLO XXI Y CENTRAL DE ABASTOS, AGUASCALIENTES Mpio.

MUNICIPIO: AGUASCALIENTES

PROGRAMA: 04 - URBANIZACIÓN MUNICIPAL

SUB-PROGRAMA:

OBRA A REALIZARSE: OBRA COMPLEMENTARIA Y SEÑALIZACIÓN AV. MAHATMA GANDHI (CALZADA PONIENTE)

DEPENDENCIA EJECUTORA: SECRETARÍA DE OBRAS PÚBLICAS MUNICIPALES (S.O.P.M.A)

FORMACIÓN DE EJECUCION: CONTRATO

TIPO DE OBRA PROPUESTA

NUEVA CREACIÓN		CONSOLIDACIÓN	
COMPLEMENTARIA	X	AMPLIACIÓN	
REHABILITACIÓN		EQUIPAMIENTO	

CARACTERÍSTICAS DE LA OBRA:

OBRA COMPLEMENTARIA Y SEÑALIZACIÓN AV. MAHATMA GANDHI (CALZADA PONIENTE)

CONDICIONES ACTUALES DE LA OBRA:

BUEN ESTADO	X	REGULAR		PESIMO ESTADO	

FACTIBILIDAD DE LA OBRA:

SE HACE ENTREGA DE LA OBRA DE ACUERDO A LAS METAS INICIALES, ATENDIENDO EL CONTRATISTA LOS DETALLES MARCADOS PREVIOS A LA ENTREGA.

PROCEDE	SI	X	NO		

Aguascalientes
LA CIUDAD DE TU VIDA

I.C. LAURA CECILIA MARTINEZ ALBA
SUPERVISOR

H. AYUNTAMIENTO CONSTITUCIONAL DEL MUNICIPIO DE AGUASCALIENTES 2021-2024

PRESUPUESTO MODIFICADO

Aguascalientes

Obra: **OBRA COMPLEMENTARIA Y SEÑALIZACIÓN AV. MAHATMA GANDHI (CALZADA PONIENTE)**

Ubicación: **TRAMO: ENTRE BLVD. SIGLO XXI Y CENTRAL DE ABASTOS, AGUASCALIENTES Mpio.**

Contratista: **CASLOP DISEÑO ARTE Y CONSTRUCCION, S.A. DEC.V. (502)**

No.	Concepto	Unidad	Cantidad	Precio Unitario	Importe Total
	GRUPO: **OBRA COMPLEMENTARIA Y SEÑALIZACION**				
	PARTIDA: **PRELIMINARES**				
1	CORTE CON DISCO DIAMANTADO DE 14" EN PISOS DE CONCRETO ASFÁLTICO DE HASTA (HASTA 8.00 cm. DE PROFUNDIDAD). INCLUYE: TRAZO, EQUIPO Y OPERACIÓN, LIMPIEZAS.	ML	152.08	$55.92	$8,504.31
2	DEMOLICIÓN A MANO Y MECÁNICA DE PAVIMENTO HIDRÁULICO Y/O ASFÁLTICO EN CUALQUIER ESPESOR, EN PAVIMENTOS, LOSAS DIAMANTE, LOSAS DE CAJAS DE VÁLVULAS, LOSAS DE LLAVE HIDRAULICA, CAIMANES, ETC., CON O SIN ARMADO DE ACERO SIN RECUPERACIÓN., INCLUYE: CARGA Y ACARREO LOCAL DE MATERIAL AL LUGAR DE ACOPIO, HERRAMIENTA NECESARIA, CORTES CON DISCO Y TODO LO NECESARIO PARA SU CORRECTA EJECUCIÓN, LIMPIEZA, TRABAJO TERMINADO.	M3	12.01	$710.59	$8,534.19
4	CARGA MECANICA Y ACARREO DE MATERIAL PRODUCTO DE EXCAVACION Y DEMOLICION EN CAMION DE VOLTEO AL 1er. KM, VOLUMEN MEDIDO COMPACTO.	M3	12.01	$32.32	$388.16
5	ACARREO DE MATERIAL PRODUCTO DE EXCAVACION Y/O DEMOLICION EN CAMION DE VOLTEO A KILOMETROS SUBSECUENTES, AL TIRADERO OFICIAL AUTORIZADO MAS CERCANO AUTORIZADO POR LA SUPERVISION, VOLUMEN MEDIDO COMPACTO.	M3-KM	226.9	$8.34	$1,892.35
			Totales por Partida		**$19,319.01**
	PARTIDA: **OBRA COMPLEMENTARIA**				
6	RE NIVELACIÓN DE POZO DE VISITA HASTA 30 cm DE ALTURA. INCLUYE: RETIRO SIN RECUPERACIÓN DE BROCAL EXISTENTE, DEMOLICIONES, NIVELADO CON TABIQUE ROJO RECOCIDO 7X14X28, ASENTADO CON MORTERO CEMENTO-ARENA 1:3 DE 28 cm DE ESPESOR, APLANADO CON MORTERO CEMENTO-ARENA 1:3 , PLOMEADO, NIVELADO, DEMOLICIONES, CARGAS Y ACARREOS DENTRO DE LA OBRA, LIMPIEZA PREVIA Y FINAL.	PZA	22	$1,943.90	$42,765.80
7	CONSTRUCCIÓN DE LOSA DIAMANTE A BASE DE CONCRETO PREMEZCLADO MR= 45 KG/CM2, T.M.A. 3/4" (19 mm), GRAVA TRITURADA, REVENIMIENTO DE 8+-2.5 cm, RESISTENCIA RÁPIDA A 3 DÍAS, DE 25 CM DE ESPESOR, EN POZO DE VISITA, SECCIÓN DE 1.50 M X 1.50 M , INCLUYE: TRAZO, NIVELACIÓN, LIMPIEZA PREVIA Y PREPARACIÓN DE LA SUPERFICIE, COMPACTACIÓN DE TERRENO AL 95% DE SU PVSM, ESCARIFICADO, SUMINISTRO DE MATERIALES, DEMOLICIÓN Y RECONSTRUCCIÓN DE APROCHES, ESPUMA DE POLIURETANO DE ALTA DENSIDAD EN TODO EL PERÍMETRO EXTERIOR DE 1/2", ASÍ COMO EN LAS JUNTAS DIAGONALES PARA FORMAR 4 PARTES, BROCAL Y TAPA DE Fo. Fo. TIPO PESADO (165 KG), CIMBRADO, COLADO, VIBRADO, DESCIMBRADO, CURADO CON MEMBRANA QUÍMICA BASE AGUA, APLANADO FINO EN RECEPCIÓN DE BROCAL, CORTES CON CORTADORA DE DISCO DE 5 CM ENTRE JUNTAS DIAGONALES FORMANDO 8 PIEZAS Y SELLADO DE JUNTAS, CORTES RELLENOS CON MATERIAL PREFORMADO Y SELLADOR AUTONIVELANTE, MANO DE OBRA, CARGA Y ACARREOS DE MATERIAL DENTRO Y FUERA DE LA OBRA, LIMPIEZA FINAL, TRABAJO TERMINADO P.U.O.T	PZA	21.65	$9,226.16	$199,746.36

PRESUPUESTO MODIFICADO

Obra: **OBRA COMPLEMENTARIA Y SEÑALIZACIÓN AV. MAHATMA GANDHI (CALZADA PONIENTE)**

Ubicación: **TRAMO: ENTRE BLVD. SIGLO XXI Y CENTRAL DE ABASTOS, AGUASCALIENTES Mpio.**

Contratista: **CASLOP DISEÑO ARTE Y CONSTRUCCION, S.A. DEC.V. (502)**

No.	Concepto	Unidad	Cantidad	Precio Unitario	Importe Total
	GRUPO: **OBRA COMPLEMENTARIA Y SEÑALIZACION**				
	PARTIDA: **OBRA COMPLEMENTARIA**				
9	RENIVELACION DE DE RASANTE (PARTE SUPERIOR) CAIMAN SECCION DE 6.00 x 0.70 HASTA 7.00 X 1.2 MTS Y HASTA 0.30 m DE ALTURA. INCLUYE: DESMONTAJE, RETIRO DE REJILLA, CONSERVACIÓN DE LA MISMA PARA RECOLOCACIÓN POSTERIOR, DEMOLICIONES NECESARIAS, NIVELADO CON TABIQUE COMUN, ASENTADO EN 28CM CON MORTERO CEMENTO-ARENA 1:3 DE ESPESOR, APLANADO CON MORTERO CEMENTO-ARENA 1:3, ANCLAJES, Y TRASLAPES EN CASTILLOS SECCION 28 X 28 CM ARMADO CON 8 VRS DEL No. 3 ESTRIBOS DEL No. 2 @ 15 CM CONCRETO F´C 250 KG/CM2 T.M.A. 1 1/2", DALA DE REMATE SECCION 30X30 CM ARMADO CON 7 VRS DEL No. 3 ESTRIBOS DEL No. 2 @ 15 CM CONCRETO F´C 250 KG/CM2 T.M.A. 1 1/2", CIMBRADO, DESCIMBRADO, COLADO Y VIBRADO, CURADO CON MEMPBRANA BASE AGUA, COLOCACION DE REJILLA, MARCO Y/O CONTRAMARCO , TRABAJOS DE TALLER PARA AJUSTES, PLOMEADO, NIVELADO, RECONSTRUCCIÓN DE APROCHES, DEMOLICIONES, CARGAS Y ACARREOS DENTRO DE LA OBRA, LIMPIEZA PREVIA, FINAL Y TODO LO NECESARIO PARA SU CORRECTA EJECUCIÓN DEL CONCEPTO.	PZA	3	$20,103.91	$60,311.73
10	LIMPIEZA Y DESAZOLVE DE POZOS DE VISITA Y LÍNEAS DE ALCANTARILLADO EXISTENTE CON CAMIÓN TIPO VACTOR. INCLUYE: RESANE INTERIOR DEL POZO Y REMATE DE POZO CON TUBO SELLADOR FESTER Y MORTERO 1:3, MANO DE OBRA, SUMINISTRO DE AGUA EN PIPA, HERRAMIENTAS Y EQUIPO PARA SU CORRECTA EJECUCIÓN, LIMPIEZAS, RENTA DE CAMIÓN VACTOR HASTA LA CORRECTA LIMPIEZA DE LAS LÍNEAS EXISTENTES DE POZO A POZO ASÍ COMO EL TRASLADO DE LOS DESECHOS HASTA TIRADERO AUTORIZADO, LA UNIDAD DE MEDIDA SE PAGARA DE POZO A POZO.	LOTE	20	$9,282.33	$185,646.60
11	LIMPIEZA Y DESASOLVE DE CAIMANES DE HASTA 6.00 X 1.50 M DE LONGITUD, INCLUYE: MANO DE OBRA, SUMINISTRO DE AGUA EN PIPA, HERRAMIENTAS Y EQUIPO PARA SU CORRECTA EJECUCION, LIMPIEZAS MANUALES, CARGAS Y ACARREOS LOCALES ASI COMO RETIRO DE MATERIAL PRODUCTO DEL DESASOLVE A TIRADERO AUTORIZADO.	PZA	3	$2,610.03	$7,830.09
				Totales por Partida	**$496,300.58**
	PARTIDA: **LIMPIEZAS**				
13	LIMPIEZA FINAL DE LA OBRA, INCLUYE: BARRIDO, CARGA, ACARREOS Y RETIRO DE ESCOMBROS FUERA DE LA OBRA, TRABAJO TERMINADO.	M2	201.4404054262	$11.21	$2,258.15
				Totales por Partida	**$2,258.15**
	PARTIDA: **SEÑALIZACION HORIZONTAL**				
16	SUMINISTRO Y APLICACIÓN DE PINTURA BASE SOLVENTE (ESMALTE) PARA MARCAS EN GUARNICIONES CLASIFICACION M-12.1, M12.2 APLICADA SOBRE GUARNICIONES Y DENTELLONES COLOR BLANCA Y/O AMARILLA, SEGÚN SE REQUIERA Y SEGÚN MANUAL DE SEÑALIZACIÓN VIAL Y DISPOSITIVOS DE SEGURIDAD SICT (S.C.T). SECADO AL TACTO EN 5 MIN Y AL DURO EN 30 MIN CON MICRO ESFERA , DESARROLLO DE 35 CM. INCLUYE: MATERIALES Y ESPECIFICACIONES QUE CUMPLAN CON LA NORMATIVA N-CMT-5-01-001/13, N-PRY-CAR-10-01-002/13 APLICADAS AL DIA DE HOY, TRAZO, MANO DE OBRA, LIMPIEZA PREVIA Y FINAL DE SUPERFICIE, EQUIPO NECESARIO PARA SU EJECUCIÓN, Y TODO LO NECESARIO PARA SU CORRECTA EJECUCIÓN, TRABAJO TERMINADO.	ML	1615.45	$30.54	$49,335.84

Obra: **OBRA COMPLEMENTARIA Y SEÑALIZACIÓN AV. MAHATMA GANDHI (CALZADA PONIENTE)**

Ubicación: **TRAMO: ENTRE BLVD. SIGLO XXI Y CENTRAL DE ABASTOS, AGUASCALIENTES Mpio.**

Contratista: **CASLOP DISEÑO ARTE Y CONSTRUCCION, S.A. DEC.V. (502)**

No.	Concepto	Unidad	Cantidad	Precio Unitario	Importe Total
	GRUPO: **OBRA COMPLEMENTARIA Y SEÑALIZACION**				
	PARTIDA: **SEÑALIZACION HORIZONTAL**				
18	SUMINISTRO Y APLICACIÓN DE PINTURA TERMOPLASTICA ALQUIDALICA DE 120 MILESIMAS DE " (in) EN RAYA EN LA ORILLA DEL ARROYO VIAL CLASIFICACIÓN M - 3.3, CONTINUA IZQUIERDA, PARA VIALIDADES URBANAS DE FRENTE EN PISO, DE 10 CM DE ANCHO Y SEPARADA 15 CM. DE LA GUARNICION, A BASE DE PINTURA PARA TRAFICO COLOR BLANCO CON MICRO ESFERA SEGÚN MANUAL DE SEÑALIZACIÓN VIAL Y DISPOSITIVOS DE SEGURIDAD SICT (S.C.T)., INCLUYE: MATERIALES Y ESPECIFICACIONES QUE CUMPLAN CON LA NORMATIVA N-CMT-5-01-001/13, N-PRY-CAR-10-01-002/13 APLICADAS AL DIA DE HOY, MATERIAL APLICADO EN SU ESTADO DE FUSION A UNA TEMPERATURA MINIMA DE 204 C, LA SUPERFICIE DE CONCRETO O ASFALTO NO DEBE PRESENTAR UNA TEMPERATURA MENOR A LOS 10 C, ;TIEMPO DE SECADO EN RANGOS DE TEMPERATURA DE 10 C DEL SUSTRATO 2 MINUTOS, Y NO MAS DE 10 MINUTOS CUANDO EL SUSTRATO OSCILA ALREDEDOR DE 54C, TRAZO, ENMASCARILLADO, MANO DE OBRA, LIMPIEZA PREVIA Y FINAL DE SUPERFICIE, EQUIPO NECESARIO PARA SU EJECUCIÓN, Y TODO LO NECESARIO PARA SU CORRECTA EJECUCIÓN, TRABAJO TERMINADO.	ML	1569.75	$51.66	$81,093.29
20	SUMINISTRO Y APLICACIÓN DE PINTURA TERMOPLASTICA ALQUIDALICA DE 120 MILESIMAS DE " (in) EN RAYA DE ALTO CLASIFICACIÓN M - 6, PARA INDICAR ALTO EN CRUCEROS, COLOR BLANCO, REFLEJANTE CON MICRO ESFERA DE VIDRIO EN PROPORCIÓN SEGÚN MANUAL DE SEÑALIZACIÓN VIAL Y DISPOSITIVOS DE SEGURIDAD SICT (S.C.T). DE 0.60 MTS DE ANCHO DE LONGITUD VARIABLE, INCLUYE: MATERIALES Y ESPECIFICACIONES QUE CUMPLAN CON LA NORMATIVA N-CMT-5-01-001/13, N-PRY-CAR-10-01-002/13 APLICADAS AL DIA DE HOY, MATERIAL APLICADO EN SU ESTADO DE FUSION A UNA TEMPERATURA MINIMA DE 204 C, LA SUPERFICIE DE CONCRETO O ASFALTO NO DEBE PRESENTAR UNA TEMPERATURA MENOR A LOS 10 C, ;TIEMPO DE SECADO EN RANGOS DE TEMPERATURA DE 10 C DEL SUSTRATO 2 MINUTOS, Y NO MAS DE 10 MINUTOS CUANDO EL SUSTRATO OSCILA ALREDEDOR DE 54C, TRAZO, ENMASCARILLADO, MANO DE OBRA, LIMPIEZA PREVIA Y FINAL DE SUPERFICIE, EQUIPO NECESARIO PARA SU EJECUCIÓN, Y TODO LO NECESARIO PARA SU CORRECTA EJECUCIÓN, TRABAJO TERMINADO.	ML	53.45	$313.90	$16,777.96
21	SUMINISTRO Y APLICACIÓN DE PINTURA TERMOPLASTICA ALQUIDALICA DE 120 MILESIMAS DE " (in) EN RAYA PARA CRUCE PEATONAL CLASIFICACIÓN M - 7.1, PARA INDICAR " CRUCE PEATONAL EN VIAS PRIMARIAS", COLOR AMARILLO, REFLEJANTE CON MICRO ESFERA DE VIDRIO EN PROPORCIÓN SEGÚN MANUAL DE SEÑALIZACIÓN VIAL Y DISPOSITIVOS DE SEGURIDAD SICT (S.C.T). DE 0.40 MTS DE ANCHO Y 3.5 MTS. DE LONGITUD POR EL ANCHO DE LA VIALIDAD, CON UNA SEPARACIÓN DE 0.40 MTS. ENTRE ELLAS, INCLUYE: MATERIALES Y ESPECIFICACIONES QUE CUMPLAN CON LA NORMATIVA N-CMT-5-01-001/13, N-PRY-CAR-10-01-002/13 APLICADAS AL DIA DE HOY, MATERIAL APLICADO EN SU ESTADO DE FUSION A UNA TEMPERATURA MINIMA DE 204 C, LA SUPERFICIE DE CONCRETO O ASFALTO NO DEBE PRESENTAR UNA TEMPERATURA MENOR A LOS 10 C, ;TIEMPO DE SECADO EN RANGOS DE TEMPERATURA DE 10 C DEL SUSTRATO 2 MINUTOS, Y NO MAS DE 10 MINUTOS CUANDO EL SUSTRATO OSCILA ALREDEDOR DE 54C, TRAZO, ENMASCARILLADO, MANO DE OBRA, LIMPIEZA PREVIA Y FINAL DE SUPERFICIE, EQUIPO NECESARIO PARA SU EJECUCIÓN, Y TODO LO NECESARIO PARA SU CORRECTA EJECUCIÓN, TRABAJO TERMINADO.	M2	341.47	$552.64	$188,709.98

Obra: **OBRA COMPLEMENTARIA Y SEÑALIZACIÓN AV. MAHATMA GANDHI (CALZADA PONIENTE)**

Ubicación: **TRAMO: ENTRE BLVD. SIGLO XXI Y CENTRAL DE ABASTOS, AGUASCALIENTES Mpio.**

Contratista: **CASLOP DISEÑO ARTE Y CONSTRUCCION, S.A. DEC.V. (502)**

No.	Concepto	Unidad	Cantidad	Precio Unitario	Importe Total
	GRUPO: **OBRA COMPLEMENTARIA Y SEÑALIZACION**				
	PARTIDA: **SEÑALIZACION HORIZONTAL**				
22	SUMINISTRO Y APLICACIÓN DE PINTURA TERMOPLASTICA ALQUIDALICA DE 120 MILESIMAS DE " (in) EN FLECHAS CLASIFICACIÓN M - 11.1, "FLECHA SENCILLA" PARA INDICAR SENTIDO DE CIRCULACIÓN , EN VIALIDADES PARA VELOCIDAD MENOR A 60KM POR HORA DIMENSION NORMATIVA SEGUN MANUAL DE SEÑALIZACIÓN VIAL Y DISPOSITIVOS DE SEGURIDAD SICT (SCT) Y/O (VER PLANO DE SEÑALAMIENTOS), COLOR BLANCO, REFLEJANTE CON MICRO ESFERA DE VIDRIO EN PROPORCIÓN SEGÚN NORMA SCT, INCLUYE: MATERIALES Y ESPECIFICACIONES QUE CUMPLAN CON LA NORMATIVA N-CMT-5-01-001/13, N-PRY-CAR-10-01-002/13 APLICADAS AL DIA DE HOY, MATERIAL APLICADO EN SU ESTADO DE FUSION A UNA TEMPERATURA MINIMA DE 204 C, LA SUPERFICIE DE CONCRETO O ASFALTO NO DEBE PRESENTAR UNA TEMPERATURA MENOR A LOS 10 C, ;TIEMPO DE SECADO EN RANGOS DE TEMPERATURA DE 10 C DEL SUSTRATO 2 MINUTOS, Y NO MAS DE 10 MINUTOS CUANDO EL SUSTRATO OSCILA ALREDEDOR DE 54C, TRAZO, ENMASCARILLADO, MANO DE OBRA, LIMPIEZA PREVIA Y FINAL DE SUPERFICIE, EQUIPO NECESARIO PARA SU EJECUCIÓN, Y TODO LO NECESARIO PARA SU CORRECTA EJECUCIÓN, TRABAJO TERMINADO.	PZA	25	$959.58	$23,989.50
23	SUMINISTRO Y APLICACIÓN DE PINTURA TERMOPLASTICA ALQUIDALICA DE 120 MILESIMAS DE " (in) EN LETRAS Y NUMEROS CLASIFICACIÓN M - 11.1 "LETRAS Y NUMEROS" EN VIALIDADES PARA VELOCIDAD MENOR A 60KM POR HORA SEGUN MANUAL DE SEÑALIZACIÓN VIAL Y DISPOSITIVOS DE SEGURIDAD SICT (SCT), (VER PLANO DE SEÑALAMIENTOS) EN COLOR BLANCO, REFLEJANTE CON MICRO ESFERA DE VIDRIO EN PROPORCIÓN SEGÚN NORMA SCT DE (VER DETALLES EN PLANOS) INCLUYE: MATERIALES Y ESPECIFICACIONES QUE CUMPLAN CON LA NORMATIVA N-CMT-5-01-001/13, N-PRY-CAR-10-01-002/13 APLICADAS AL DIA DE HOY, MATERIAL APLICADO EN SU ESTADO DE FUSION A UNA TEMPERATURA MINIMA DE 204 C, LA SUPERFICIE DE CONCRETO O ASFALTO NO DEBE PRESENTAR UNA TEMPERATURA MENOR A LOS 10 C, ;TIEMPO DE SECADO EN RANGOS DE TEMPERATURA DE 10 C DEL SUSTRATO 2 MINUTOS, Y NO MAS DE 10 MINUTOS CUANDO EL SUSTRATO OSCILA ALREDEDOR DE 54C, TRAZO, ENMASCARILLADO, MANO DE OBRA, LIMPIEZA PREVIA Y FINAL DE SUPERFICIE, EQUIPO NECESARIO PARA SU EJECUCIÓN, Y TODO LO NECESARIO PARA SU CORRECTA EJECUCIÓN, TRABAJO TERMINADO.	PZA	108	$785.86	$84,872.88
25	SUMINISTRO Y COLOCACIÓN DE VIALETA STANDARD (S-200) DE 10X10CM. COLOR: CUERPO AMARILLO Y/O BLANCO Y REFLEJANTE AMARILLO 1 CARA MARCA SEA O SIMILAR EN CALIDAD Y ESPECIFICACIONES DE FICHA TÉCNICA, FIJADO EN PAVIMENTO CON SISTEMA DE SUJECIÓN DE ALTO AGARRE PEGAMENTO EPOXICO 100 A/B (RESINA EPÓXICA/RESINA POLIAMIDA MODIFICADA), RESISTENTE A ALTA TEMPERATURA (VER PLANO DE DETALLES DE SEÑALAMIENTOS HORIZONTAL), INCLUYE: LIMPIEZA PREVIA Y FINAL DE LA SUPERFICIE, PREPARACIÓN DE LA SUPERFICIE, TRAZO, ALINEACIÓN, Y TODO LO NECESARIO PARA SU CORRECTA EJECUCIÓN, TRABAJO TERMINADO.	PZA	219	$56.15	$12,296.85
26	SUMINISTRO Y COLOCACION DE VIALETA SOLAR DE 10X10CM. COLOR: CUERPO ALUMINIO 3 LED DOS CARAS REFLEJANTES MARCA CREATIVAL VT-29 O SIMILAR EN CALIDAD Y ESPECIFICACIONES DE FICHA TÉCNICA, FIJADO EN PAVIMENTO CON SISTEMA DE SUJECIÓN DE ALTO AGARRE PEGAMENTO EPOXICO 100 A/B (RESINA EPÓXICA/RESINA POLIAMIDA MODIFICADA), RESISTENTE A ALTA TEMPERATURA (VER PLANO DE DETALLES DE SEÑALAMIENTOS HORIZONTAL), INCLUYE: LIMPIEZA PREVIA Y FINAL DE LA SUPERFICIE+C92, PREPARACIÓN DE LA SUPERFICIE, TRAZO, ALINEACIÓN, Y TODO LO NECESARIO PARA SU CORRECTA EJECUCIÓN, TRABAJO TERMINADO.	PZA	106	$526.13	$55,769.78
				Totales por Partida	**$512,846.07**

Obra: OBRA COMPLEMENTARIA Y SEÑALIZACIÓN AV. MAHATMA GANDHI (CALZADA PONIENTE)

Ubicación: TRAMO: ENTRE BLVD. SIGLO XXI Y CENTRAL DE ABASTOS, AGUASCALIENTES Mpio.

Contratista: CASLOP DISEÑO ARTE Y CONSTRUCCION, S.A. DEC.V. (502)

No.	Concepto	Unidad	Cantidad	Precio Unitario	Importe Total

GRUPO: **OBRA COMPLEMENTARIA Y SEÑALIZACION**

Totales por Grupo		$1,030,723.81
Totales Presup.		$1,030,723.81
Anticipo	+	$309,217.15
Amortizac. Ant.	-	$309,217.15
SubTotal. Ant.	=	$1,030,723.82
IVA	+	$164,915.81
Total	=	$1,195,639.63

H. AYUNTAMIENTO CONSTITUCIONAL DEL MUNICIPIO DE AGUASCALIENTES 2021-2024

PRESUPUESTO MODIFICADO

Aguascalientes

Obra: **OBRA COMPLEMENTARIA Y SEÑALIZACIÓN AV. MAHATMA GANDHI (CALZADA PONIENTE)**

Ubicación: **TRAMO: ENTRE BLVD. SIGLO XXI Y CENTRAL DE ABASTOS, AGUASCALIENTES Mpio.**

Contratista: **CASLOP DISEÑO ARTE Y CONSTRUCCION, S.A. DEC.V. (502)**

Grupo	Partida	Importe
OBRA COMPLEMENTARIA Y SEÑALIZACION		
	PRELIMINARES	$19,319.01
	OBRA COMPLEMENTARIA	$496,300.58
	LIMPIEZAS	$2,258.15
	SEÑALIZACION HORIZONTAL	$512,846.07
	Subtotal por Grupo	**$1,030,723.81**

Totales Presup.		**$1,030,723.81**
Anticipo	+	**$309,217.15**
Amortizac. Ant.	-	**$309,217.15**
SubTotal. Ant.	=	**$1,030,723.82**
IVA	+	**$164,915.81**
Total	=	**$1,195,639.63**



H. AYUNTAMIENTO DE AGUASCALIENTES
SECRETARÍA DE OBRAS PÚBLICAS
DIRECCIÓN DE SUPERVISIÓN DE OBRA


Aguascalientes
LA CIUDAD DE TU VIDA


MEMORIA FOTOGRÁFICA

OBRA:	**OBRA COMPLEMENTARIA Y SEÑALIZACIÓN AV. MAHATMA GANDHI (CALZADA PONIENTE), TRAMO: ENTRE BLVD. SIGLO XXI Y CENTRAL DE ABASTOS, AGUASCALIENTES Mpio.**		
NO. DE CONTRATO:	**FISMDF-0097-2022**	CONTRATISTA:	**CASLOP DISEÑO ARTE Y CONSTRUCCION, S.A. DE C.V.**

INICIO



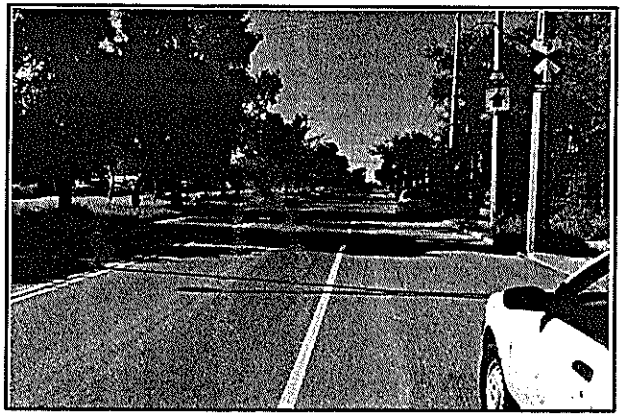

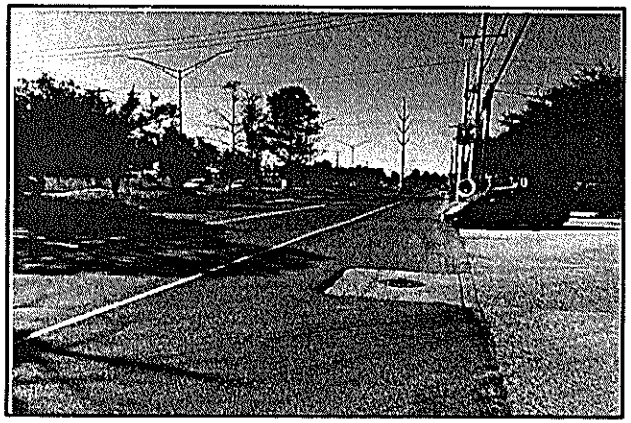



I.C. LAURA CECILIA MARTÍNEZ ALBA
RESIDENTE DE SUPERVISIÓN

H. AYUNTAMIENTO DE AGUASCALIENTES
SECRETARÍA DE OBRAS PÚBLICAS
DIRECCIÓN DE SUPERVISIÓN DE OBRA

Aguascalientes
LA CIUDAD DE TU VIDA


MEMORIA FOTOGRÁFICA


OBRA:	**OBRA COMPLEMENTARIA Y SEÑALIZACIÓN AV. MAHATMA GANDHI (CALZADA PONIENTE), TRAMO: ENTRE BLVD. SIGLO XXI Y CENTRAL DE ABASTOS, AGUASCALIENTES Mpio.**		
NO. DE CONTRATO:	**FISMDF-0097-2022**	CONTRATISTA:	**CASLOP DISEÑO ARTE Y CONSTRUCCION, S.A. DE C.V.**

PROCESO





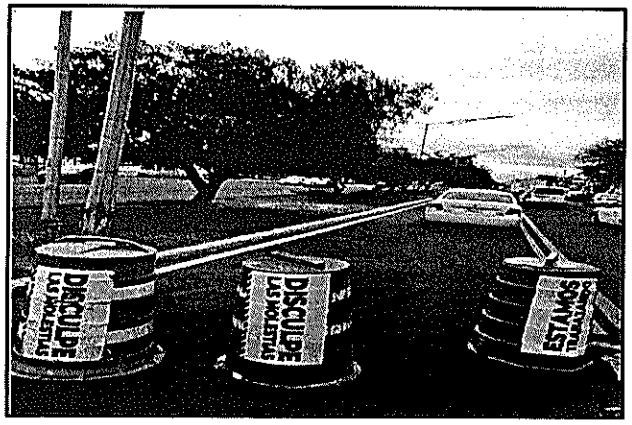

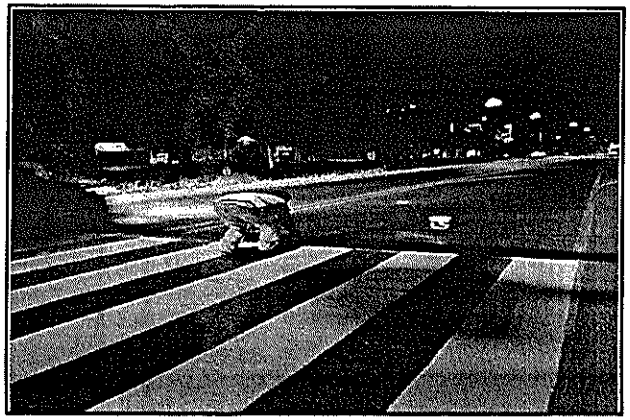

I.C. LAURA CECILIA MARTÍNEZ ALBA
RESIDENTE DE SUPERVISIÓN


H. AYUNTAMIENTO DE AGUASCALIENTES
SECRETARÍA DE OBRAS PÚBLICAS
DIRECCIÓN DE SUPERVISIÓN DE OBRA


Aguascalientes
LA CIUDAD DE TU VIDA


MEMORIA FOTOGRÁFICA


OBRA:	**OBRA COMPLEMENTARIA Y SEÑALIZACIÓN AV. MAHATMA GANDHI (CALZADA PONIENTE), TRAMO: ENTRE BLVD. SIGLO XXI Y CENTRAL DE ABASTOS, AGUASCALIENTES Mpio.**		
NO. DE CONTRATO:	**FISMDF-0097-2022**	CONTRATISTA:	**CASLOP DISEÑO ARTE Y CONSTRUCCION, S.A. DE C.V.**

FINAL

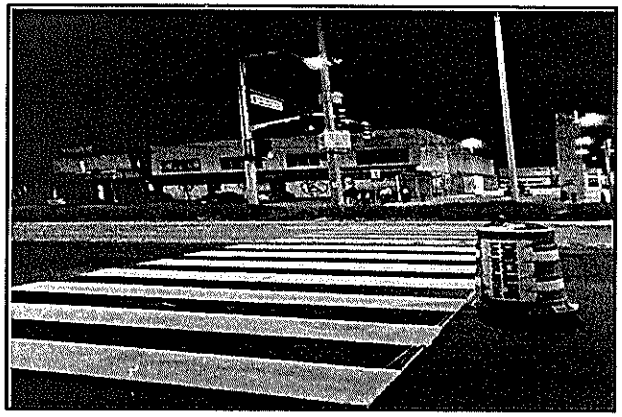

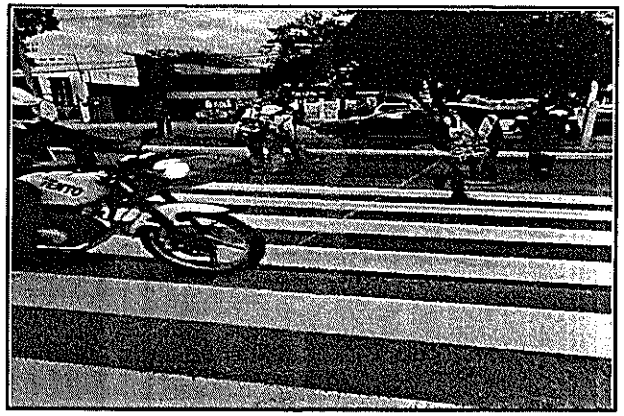

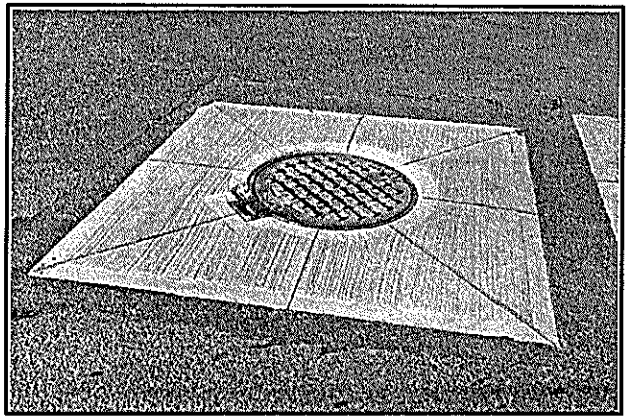

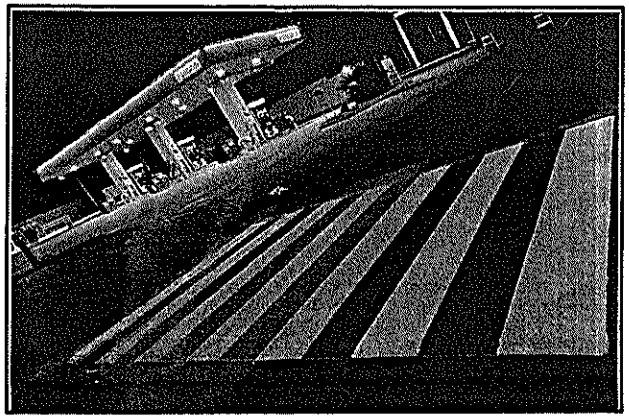

I.C. LAURA CECILIA MARTINEZ ALBA
RESIDENTE DE SUPERVISIÓN

EXPEDIENTE MODIFICADO

SECRETARÍA DE OBRAS PÚBLICAS

DIRECCIÓN DE SUPERVISIÓN DE OBRA

EJERCICIO: 2022

N° DE CONTRATO: FISMDF-0097-2022

NOMBRE DE LA OBRA: OBRA COMPLEMENTARIA Y SEÑALIZACIÓN AV. MAHATMA GANDHI (CALZADA PONIENTE), TRAMO: ENTRE BLVD. SIGLO XXI Y CENTRAL DE ABASTOS

MONTO MODIFICADO FINAL: $1,195,639.63

VOLUMEN	UNIDAD	COMPONENTE DE LA OBRA	MONTO
12.01	M3	DEMOLICIÓN A MANO Y MECÁNICA DE PAVIMENTO HIDRÁULICO Y/O	$ 19,319.01
22.00	PZA	CONSTRUCCIÓN DE LOSA DIAMANTE A BASE DE CONCRETO	$ 496,300.58
201.44	M2	LIMPIEZA FINAL DE LA OBRA, INCLUYE: BARRIDO, CARGA, ACARREOS Y	$ 2,258.15
341.47	M2	SUMINISTRO Y APLICACIÓN DE PINTURA TERMOPLASTICA ALQUIDALICA	$ 512,846.07

MONTO BASE:	$	1,030,723.82
IVA:	$	164,915.81
TOTAL:	$	1,195,639.63


I.C. Laura Cecilia Martínez Alba
RESIDENTE DE SUPERVISIÓN



PLANTA DE SEÑALIZACIÓN A


ESCALA 1:1200

MAHATMA GANDI

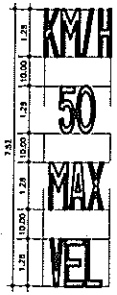


SEÑALAMIENTO VELOCIDAD MÁXIMA

ESCALA 1:50 COTAS EN m

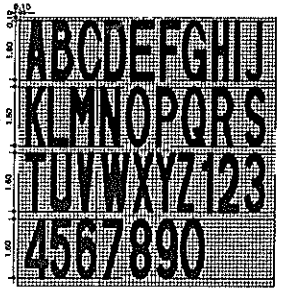

DETALLE DE TRAZO DE TEXTO PARA SEÑALIZACIÓN HORIZONTAL


ESCALA 1:50 COTAS EN m

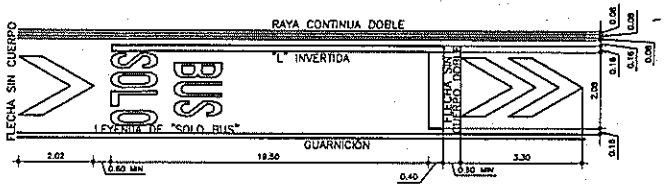

SEÑALAMIENTO DE PARADA DE AUTOBUS


PARA VELOCIDADES DE HASTA DE 60KM/H

ESCALA 1:100 COTAS EN m

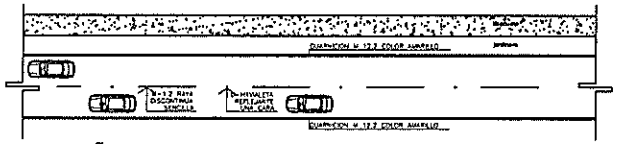

SEÑALIZACION EN PISO


ESCALA 1:200 COTAS EN m

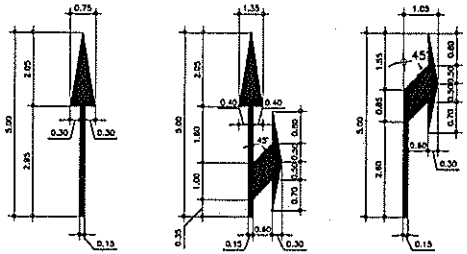

DETALLE DE FLECHAS EN PAVIMENTO

PARA VELOCIDADES HASTA DE 60KM/H


ESCALA 1:50 COTAS EN m

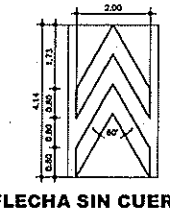

FLECHA SIN CUERPO


PARA VELOCIDADES DE HASTA DE 60KM/H

ESCALA 1:50 COTAS EN m

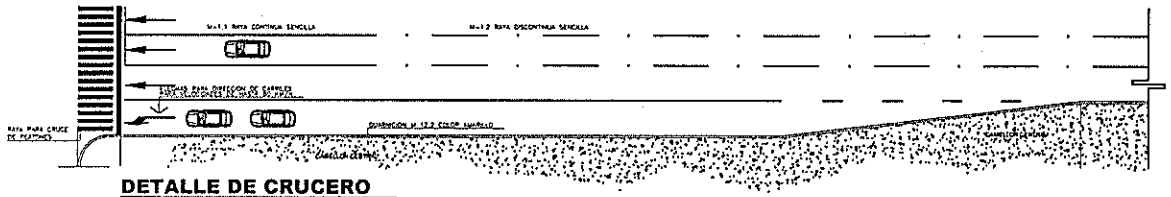

DETALLE DE CRUCERO

ESCALA 1:200 COTAS EN m

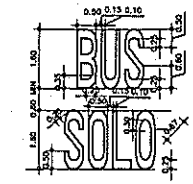

LEYENDA DE "SOLO BUS"

PARA VELOCIDADES DE HASTA DE 60KM/H

ESCALA 1:50 COTAS EN m

CASLOP

DISEÑO, ARTE Y CONSTRUCCIÓN S.A. DE C.V.

UBICACCION



SIMBOLOGIA

- LIMITE DE PROYECTO
- BANQUETAS
- PAVIMENTO
- VIALETA ESTANDAR
- VIALETA SOLAR
- FLECHA DE SENTIDO
- LINEAS AMARILLAS DE CRUCE PEATONAL
- LINEA DE ALTO
- POZO DE VISITA
- PARADA DE AUTOBUS

Aguascalientes

LA CIUDAD DE TU VIDA

DIGITALIZO:
CASLOP DISEÑO ARTE Y COSTRUCCION, S.A. DE C.V.

REVISO:
I.C. LAURA CECILIA MARTINEZ ALBA

PROYECTO: OBRA COMPLEMENTARIA Y SEÑALIZACIÓN


UBICACIÓN: AV. MAHATMA GANDI (CALZADA PONIENTE) ENTRE BLVD. SIGLO XXI Y CENTRAL DE ABASTOS, AGUASCALIENTES MPIO.

CONTRATO: FISMDF-0097-2022

CONTENIDO:
PLANO DE OBRA TERMINADA


CLAVE: SEÑ-01 ESCALA: S/E FECHA: OCT DEL 2022 Nº DE PLANO: 1

ELABORO:
CASLOP DISEÑO ARTE Y COSTRUCCION, S.A. DE C.V.
CONTRATISTA

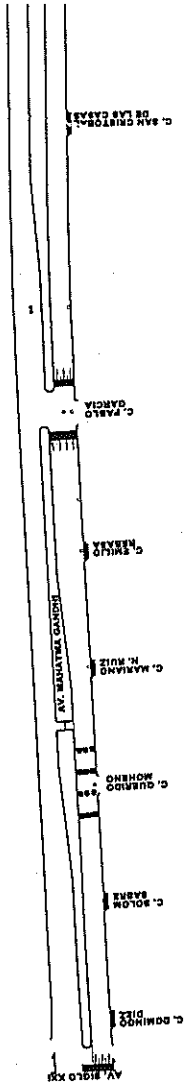


PLANTA DE SEÑALIZACIÓN A

ESCALA 1:1200 AV. MAHATMA GANDI

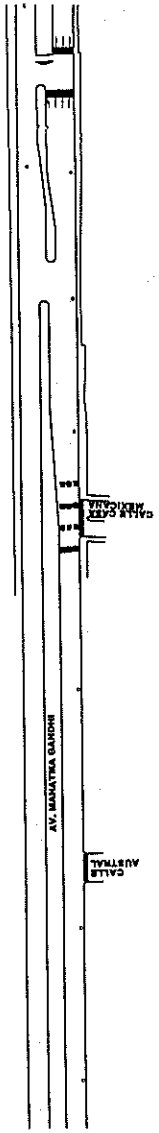

PLANTA DE SEÑALIZACIÓN B

ESCALA 1:1200 AV. MAHATMA GANDI

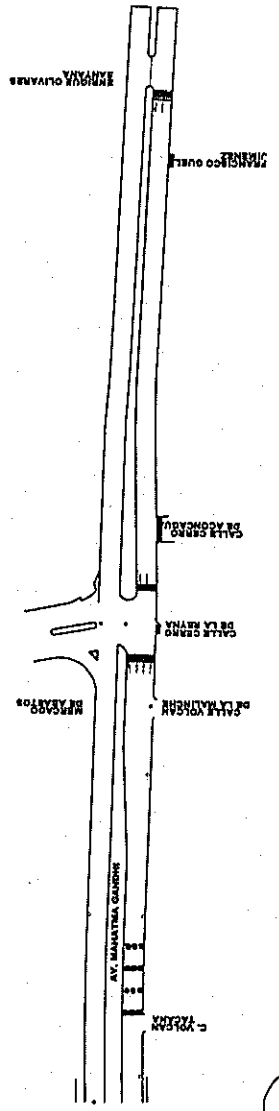

PLANTA DE SEÑALIZACIÓN C

ESCALA 1:1200 AV. MAHATMA GANDI

CASLOP
DISEÑO ARTE Y CONSTRUCCIÓN S.A. DE C.V.

UBICACCION



SIMBOLOGIA

LIMITE DE PROYECTO	
BANQUETAS	
PAVIMENTO	
VALETA ESTANDAR	
VALETA SOLAR	
FLECHA DE SENTIDO	
LINEAS AMARILLAS DE CRUCE PEATONAL	
LINEA DE ALTO	
POZO DE VISITA	
PARADA DE AUTOBUS	

Aguascalientes
LA CIUDAD DE TU VIDA


DIGITALIZO:
CASLOP DISEÑO ARTE Y COSTRUCCION, S.A. DE C.V.

REVISO:
I.C. LAURA CECILIA MARTINEZ ALBA


PROYECTO:	OBRA COMPLEMENTARIA Y SEÑALIZACIÓN
UBICACIÓN:	AV. MAHATMA GANDI (CALZADA PONIENTE) ENTRE BLVD. SIGLO XXI Y CENTRAL DE ABASTOS, AGUASCALIENTES MPIO.
CONTRATO:	FISMDF-0097-2022
CONTENIDO:	PLANO DE OBRA TERMINADA
CLAVE: SEÑ-02	ESCALA: S/E FECHA: SEP DEL 2022 Nº DE PLANO: 1


ELABORO:
CASLOP DISEÑO ARTE Y COSTRUCCION, S.A. DE C.V.
CONTRATISTA

PLANTA POZO "A"

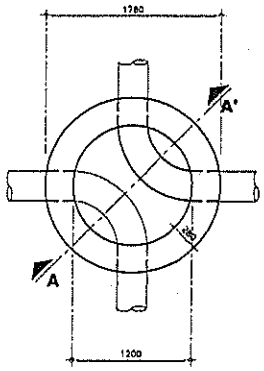


PLANTA POZO "B"

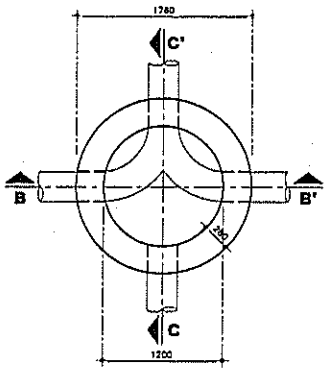

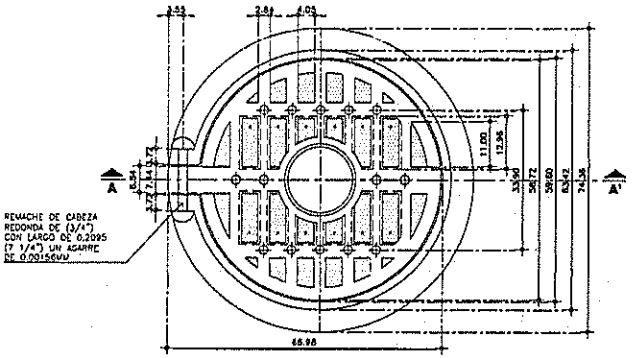


DETALLE DE BROCAL Y TAPA EN PLANTA

SIN ESCALA — COTAS EN cm

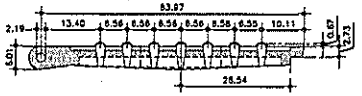


BROCAL Y TAPA EN ALZADO


SIN ESCALA — COTAS EN cm

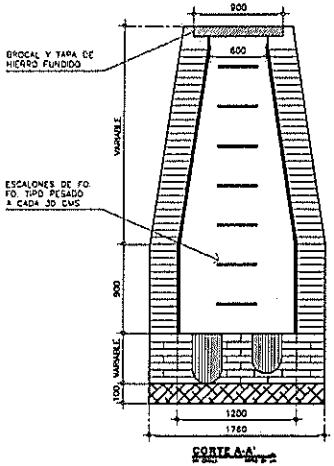

CORTE A-A'

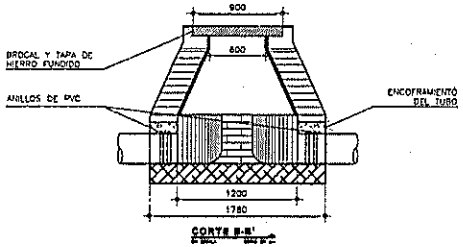

CORTE B-B'

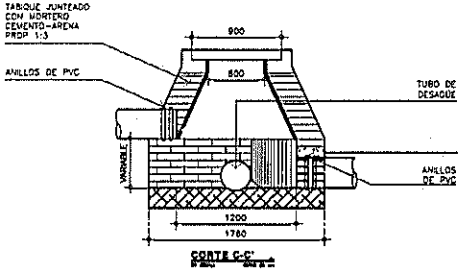


CORTE C-C'

NOTA:
APLANADO INTERIOR LISO Y EXTENDIDO A BASE DE MORTERO CEMENTO-ARENA PROP. 1:3 CON IMPERMEABILIZANTE INTERGAL 12KG POR CADA SACON DE 50KG DE CEMENTO

POZO DE VISITA COMUN

SIN ESCALA — COTAS EN cm

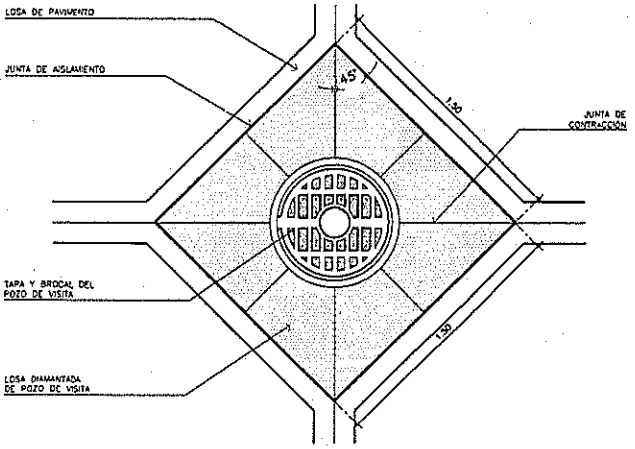

DETALLE LOSA DIAMANTE

SIN ESCALA — COTAS EN cm

CASLOP
DISEÑO, ARTE Y CONSTRUCCION S.A. DE C.V.

UBICACCION



SIMBOLOGIA

Aguascalientes
LA CIUDAD DE TU VIDA

DIGITALIZO:
CASLOP DISEÑO ARTE Y COSTRUCCION, S.A. DE C.V.

REVISO:
I.C. LAURA CECILIA MARTINEZ ALBA

PROYECTO:	OBRA COMPLEMENTARIA Y SEÑALIZACIÓN
UBICACIÓN:	AV. MAHATMA GANDI (CALZADA PONIENTE) ENTRE BLVD. BIOLO XXI Y CENTRAL DE ABASTOS, AGUASCALIENTES MPIO.
CONTRATO:	FISMDF-0097-2022
CONTENIDO:	PLANO DE OBRA TERMINADA
CLAVE:	INS-01
ESCALA:	S/E
FECHA:	OCT DEL 2022
Nº DE PLANO:	1

ELABORO:
CASLOP DISEÑO ARTE Y COSTRUCCION, S.A. DE C.V.
CONTRATISTA