Aguascalientes
LA CIUDAD DE TU VIDA

Dirección de Programación Presupuestal
Núm. Oficio AMPP/0574/22
Aguascalientes, Ags. 8 de Diciembre del 2022
Asunto: Validación de Expediente Técnico

C.P. SERGIO ARTURO LOZANO GONZÁLEZ
SECRETARIO DE FINANZAS MUNICIPALES
P R E S E N T E

Con fundamento en los artículos 17 fracción XV, 60 fracción XVI y 76 fracción VI del Reglamento del Sistema Integral de Desarrollo Municipal y del Instituto Municipal de Planeación y Evaluación de Aguascalientes, hago referencia al oficio SOPMA/2731/2022 recibido por este Instituto el día 8 de Diciembre del 2022 por parte de la Secretaría de Obras Públicas Municipales, mediante el cual remiten el expediente técnico original de la siguiente obra para su análisis, registro y priorización, conforme al Programa Anual de Obra Pública y Programas Sociales para el ejercicio presupuestal 2022:

DEPENDENCIA EJECUTORA:	SOPMA
NOMBRE DE LA OBRA O PROYECTO:	PAVIMENTO HIDRÁULICO
UBICACIÓN:	CALLE SANTA MÓNICA, ENTRE AV. EUGENIO GARZA SADA Y MARCOS CORONADO, LOS POCITOS, AGUASCALIENTES, AGS.
FONDO DE INVERSIÓN:	FONDO DE INFRAESTRUCTURA SOCIAL MUNICIPAL Y DE LAS DEMARCACIONES TERRITORIALES DEL DISTRITO FEDERAL
IMPORTE:	$4,442,257.87 (ET FINAL)
No. DE OBRA:	2022-FISMDF-0067-04-1101
MODALIDAD DE EJECUCIÓN:	CONTRATO
EJE:	MUNICIPIO SOBRESALIENTE
ESTRATEGIA:	OBRA PÚBLICA INTELIGENTE
POLITICA:	5.8.1.REHABILITACIÓN Y MANTENIMIENTO VIALIDADES, CAMINOS, CALLES, ÁREAS DE TERRACERÍA Y CAUCES (C

Al respecto, hago de su conocimiento que dicho expediente ha sido analizado en su integración técnica y documental, con base en el artículo 168 fracción I del Reglamento de la Ley de Obras Públicas y Servicios Relacionados para el Estado de Aguascalientes y sus Municipios.

Asimismo, le comento que este Instituto valida dicha obra acorde a lo establecido en los artículos 14, 22 párrafo segundo y 23 de la Ley de Obras Públicas y Servicios Relacionados para el Estado de Aguascalientes y sus Municipios, la cual se encuentra alineada al Plan de Desarrollo Municipal vigente, para dar cumplimiento a las metas establecidas en el mismo, y a los Lineamientos Generales para la Operación de este Fondo de Inversión, toda vez que la misma cuente con la autorización del CODEMUN. De igual manera, se hace de su conocimiento que deberá cumplir con lo establecido en los ordenamientos aplicables en lo que respecta al ejercicio, control e información de los recursos de este Fondo. Cabe hacer mención que los recursos solicitados para este proyecto de inversión, estarán sujetos a la disponibilidad presupuestal para el presente ejercicio fiscal que determine la Secretaría a su digno cargo. Sin otro particular por el momento, le envío un cordial saludo.

A T E N T A M E N T E

ARQ. AUSTRIA GABRIELA DÁVILA DE LA LLAVE
DIRECTORA GENERAL DEL IMPLAN

SEDR/ CAAR / JDBC
C.c.p. I.C. ING. MIGUEL ÁNGEL HUIZAR BOTELLO .- Secretaría de Obras Públicas Municipales .Para su conocimiento.
C.c.p. Archivo.

Instituto Municipal de Planeación y Evaluación de Aguascalientes

Antonio Acevedo Escobedo 103 A. Col. Centro
Aguascalientes. Ags. C.P. 20000

(449) 9101010 Ext. 3117

www.implanags.gob.mx

GOBIERNO MUNICIPAL DE AGUASCALIENTES

INSTITUTO MUNICIPAL DE PLANEACION

IMPLAN

ANÁLISIS INTEGRAL DE EXPEDIENTE TÉCNICO

No. DE OBRA (PAOP 2020):	2022-FISMDF-0067-04-1101	REGISTRO No.	236
OFICIO DE VALIDACIÓN:	AMPP/0574/22	FECHA RECIBIDO PARA REVISIÓN:	8 de Diciembre del 2022
PROGRAMA:	URBANIZACION MUNICIPAL	LOCALIDAD O COLONIA:	LOS POCITOS
SUB-PROGRAMA:	0411- Calles y Caminos	DELEGACIÓN:	Pocitos
DEPENDENCIA:	Secretaría de Obras Públicas Municipales	MOD. DE EJECUCIÓN:	CONTRATO
NOMBRE DE LA OBRA:	PAVIMENTO HIDRÁULICO, CALLE SANTA MÓNICA, ENTRE AV. EUGENIO GARZA SADA Y MARCOS CORONADO		
FUENTE DE FINANCIAMIENTO:	FONDO DE INFRAESTRUCTURA SOCIAL MUNICIPAL Y DE LAS DEMARCACIONES TERRITORIALES DEL DISTRITO FEDERAL, FISMDF		
INVERSIÓN:	$4,442,257.87	CLASIFICACIÓN DE OBRA:	BIENES DE DOMINIO PUBLICA

TOTAL	FEDERAL	ESTATAL	MUNICIPAL	BENEFICIARIOS	OTROS	DIFERENCIA ENTRE MOD.
$4,442,257.87	$4,442,257.87	0.00	0.00	0.00	0.00	*$153.757,74*

TIPO DE EXPENDIENTE:	ET FINAL	AÑO: 2022	AÑO:	AÑO:
AVANCES:	Financiero: 29 %	Físico: 65 %		
FECHA DE INICIO:	1 de Julio del 2022	FECHA DE TÉRMINO:	31 de Agosto del 2022	REGISTRO SIMA: 67

CHEK LIST DE LOS ANEXOS DEL EXPEDIENTE TÉCNICO

CÉDULA DE REGISTRO DE OBRA	✓
DICTAMEN DE FACTIBILIDAD	✓
MEMORIA DESCRIPTIVA	✓
PRESUPUESTO BASE	✓
FACTIBILIDAD VERIFICADA EN CAMPO	✓
CROQUIS DE UBICACIÓN (MACRO)	✓
CROQUIS DE UBICACIÓN (MACRO)	✓
PROGRAMA DE OBRA Y MONTOS MENSUALES	✓
PLANOS O ESTUDIOS TÉCNICOS	✓
PADRÓN DE BENEFICIARIOS	N/A
ACTA DE ACEPTACIÓN DEL PROYECTO	N/A
DICTAMEN DE IMPACTO AMBIENTAL	N/A
CONVENIO DE CONCERTACIÓN	N/A
ACTA CONSTITUTIVA	N/A

METAS		BENEFICIARIOS		PERIODO DE EJECUCION		OBRA PROPUESTA		CLAVE SISCO
UNIDAD DE MEDIDA	CANT	TIPO DE BENEFICIARIOS	CANTIDAD	FECHA DE INICIO	FECHA DE TERMINO	CONCEPTO	JORNALES A GENERAR	
M2	1666.37	Personas	400	2022-07-01	2022-08-31	Pavimentación	11549	2340

INCLUIDO EN PLAN DE DESARROLLO MUNICIPAL Y EL PROGRAMA ANUAL DE OBRA PÚBLICA

OBSERVACIONES:

SIN OBSERVACIONES

RECIBIO: ING. JOSÉ DAVID BURGUETE CLAUSTRO
Analista de Programación e Inversión de Obra Pública

8 de Diciembre del 2022
Fecha de validación

8 de Diciembre del 2022
Fecha de validación Expediente

PROCEDE Si ✓ No

H. AYUNTAMIENTO CONSTITUCIONAL DEL MUNICIPIO DE AGUASCALIENTES 2021-2024

AYUNTAMIENTO DE AGUASCALIENTES

CEDULA DE REGISTRO POR OBRA

Aguascalientes

050400-001E00E05-05-2-2-1-00-1-E-0510-0-17-0067-21-2502-6144

2022-FISMDF-0067-0411101-023	Obra **PAVIMENTO HIDRÁULICO CALLE SANTA MÓNICA**
Tipo DEFINITIVO 1 2022 Folio SISCO **2340**	Ubic. TRAMO: ENTRE AV. EUGENIO GARZA SADA Y CALLE MARCOS CORONADO, LOS POCITOS Ej. , Deleg. Pocitos

Ent. Ejecutora : **050400001E00E05**

Eje: **05**	MUNICIPIO SOBRESALIENTE
Finalidad: **2**	DESARROLLO SOCIAL
Función: **2**	VIVIENDA Y SERVICIOS A LA COMUNIDAD
Subfunción: **1**	URBANIZACIÓN
Tema: **00**	SIN TEMA
Cuenta del Gasto **1**	GASTO PROGRAMABLE
Clasif. Programatica: **E**	PRESTACIÓN DE SERVICIOS PÚBLICOS
Programa: **0510**	Movilidad Urbana
SubPrograma: **0**	SUBPROGRAMA GENÉRICO
Proyecto: **17**	
Tipo de Gasto: **21**	GASTO INVERSIÓN / OBRA PÚBLICA

I N V E R S I O N 2022

Municipal	2502	FONDO PARA LA INFRAESTRUCTURA SOCIAL MUNICIPAL Y DE LAS DEMARCACIONES TERRITORIALES DEL DISTRITO FEDERAL 2022	$4,442,257.87

Folio SIMA 67 Total $4,442,257.87

M E T A S

Unidad de Medida	Cantidad	Descripción
M2	1666.37	CONSTRUCCIÓN DE PAVIMENTO PAVIMENTO HIDRÁULICO CALLE SANTA MÓNICA

Inversión Ejercida Total al 31 de Diciembre de 2021 $0.00

Avance Fisico Acumulado al 31 de Diciembre de 2021

Avance Fisico Acumulado Programado al 31 de Diciembre de 2022 100 %

Fecha de Inicio 09 Sep 2022 Fecha de Terminación 22 Nov 2022

Jornales a Generar en 2022 11549

Modalidad de ejecución CONTRATO

Clasificación de la Obra Bienes de Dominio Público

Registro del Patrimonio: Obras del dominio público

OBRAS PÚBLICAS

Av. Aguascalientes Sur No. 2615
Fracc. Jardines de las Fuentes,
Aguascalientes, Ags. C.P. 20278

(449) 9 78 92 01, 06, 09

www.ags.gob.mx

GENERALES

Nombre del Proyecto : PAVIMENTO HIDRÁULICO CALLE SANTA MÓNICA

TRAMO: ENTRE AV. EUGENIO GARZA SADA Y CALLE MARCOS CORONADO, LOS POCITOS Ej. , Deleg. Pocitos

Programa : 04 URBANIZACION MUNICIPAL

Subprograma : 11 Calles y caminos (1.- Construcción; 01- Concreto Hidraúlico)

Clave del Municipio : AGUASCALIENTES

Localidad :

Barrio, Colonia o Ejido : LOS POCITOS Ej.

Tipo de Obra :

DESCRIPCIÓN DEL PROYECTO:

PAVIMENTO HIDRÁULICO CALLE SANTA MÓNICA

PRELIMINARES 12.42 M3
PAVIMENTO HIDRÁULICO 1,666.37 M2
ALCANTARILLADO 333.00 ML
AGUA POTABLE 333.00 ML
BANQUETAS, RAMPAS Y GUARNICIONES 1,026.34 M2, 221.71 M2 Y 670.96 ML
LIMPIEZAS 2,820.00 M2
SEÑALIZACIÓN 1.00 OBRA

Beneficiarios (No. y Tipo) :

400	PERSONAS

Hombres: 180 Mujeres: 220

OBRAS PÚBLICAS

No. Folio SISCO 2340

Los abajo firmantes, hacen constar que el presente proyecto :

PAVIMENTO HIDRÁULICO CALLE SANTA MÓNICA

TRAMO: ENTRE AV. EUGENIO GARZA SADA Y CALLE MARCOS CORONADO, LOS POCITOS Ej. , Deleg. Pocitos

cumple con los Requisitos y Normas Técnicas establecidas por la Dependencia Normativa, por lo que es viable su ejecución. Comprometiéndose la misma a proporcionar la supervisión y asistencia técnica necesaria durante el proceso administrativo.

Por la Dependencia Ejecutora

Ing. Miguel Angel Huizar Botello
Secretario de Obras Públicas

Lic. Jaime Gallo Camacho
Secretario de Desarrollo Urbano

LUGAR :AGUASCALIENTES, AGS.

SECRETARÍA DE OBRAS PÚBLICAS

Av. Aguascalientes Sur No. 2615
Fracc. Jardines de las Fuentes,
Aguascalientes, Ags. C.P. 20278

(449) 9 78 92 01, 06, 09

www.ags.gob.mx

H. AYUNTAMIENTO CONSTITUCIONAL DEL MUNICIPIO DE AGUASCALIENTES 2021-2024

AYUNTAMIENTO DE AGUASCALIENTES

FACTIBILIDAD VERIFICADA EN CAMPO

Aguascalientes
LA CIUDAD DE TU VIDA

MUNICIPIO: AGUASCALIENTES

LOCALIZACION: TRAMO: ENTRE AV. EUGENIO GARZA SADA Y CALLE MARCOS CORONADO, LOS POCITOS Ej. , Deleg. Pocitos

PROGRAMA: URBANIZACION MUNICIPAL

SUBPROGRAMA: Calles y caminos (1.- Construcción; 01- Concreto Hidraúlico)

OBRA A REALIZAR: PAVIMENTO HIDRÁULICO CALLE SANTA MÓNICA

DEPENDENCIA EJECUTORA: SECRETARÍA DE OBRAS PUBLICAS DEL MUNICIPIO DE AGUASCALIENTES

FORMA DE EJECUCION: CONTRATO

TIPO DE OBRA PROPUESTA:

CONDICIONES ACTUALES DE LA OBRA:

PAVIMENTO HIDRÁULICO CALLE SANTA MÓNICA

CARACTERISTICAS DE LA OBRA: Bueno

FACTIBILIDAD DE LA OBRA:

ESTA OBRA SE REQUIERE PARA EL BENEFICIO DE LA CIUDADANÍA

PROCEDE: SI [X] NO [ ]

REVISÓ: Jefa del Departamento de Expedientes Tecnicos y Costos

NOMBRE: Arq. Blanca Margarita Martinez Amador

FIRMA:

FECHA: 29 Nov 2022

SECRETARÍA DE OBRAS PÚBLICAS

Av. Aguascalientes Sur No. 2615
Fracc. Jardines de las Fuentes,
Aguascalientes, Ags. C.P. 20278

(449) 9 78 92 01, 06, 09

www.ags.gob.mx

No. Folio SISCO 2340

H. AYUNTAMIENTO DE AGUASCALIENTES
SECRETARÍA DE OBRAS PÚBLICAS
DIRECCIÓN DE SUPERVISIÓN DE OBRA
LOCALIZACION

H. AYUNTAMIENTO CONSTITUCIONAL DEL MUNICIPIO DE AGUASCALIENTES 2021-2024

Aguascalientes
LA CIUDAD DE TU VIDA

OBRA:	PAVIMENTO HIDRÁULICO CALLE SANTA MÓNICA, TRAMO: ENTRE AV. EUGENIO GARZA SADA Y CALLE MARCOS CORONADO, LOS POCITOS EJ.					
NO. DE CONTR	FISMDF-0067-2022		CONTRATISTA:	ATECO, S.A. DE C.V.		




ING. IVAN ALEJANDRO RUIZ ESPARZA SOLIS
SUPERVISOR DE OBRA.

H. AYUNTAMIENTO CONSTITUCIONAL DEL MUNICIPIO DE AGUASCALIENTES 2021-2024

H. AYUNTAMIENTO DE AGUASCALIENTES
SECRETARÍA DE OBRAS PÚBLICAS
DIRECCIÓN DE SUPERVISIÓN DE OBRA
LOCALIZACION

Aguascalientes
LA CIUDAD DE TU VIDA

OBRA:	PAVIMENTO HIDRÁULICO CALLE SANTA MÓNICA, TRAMO: ENTRE AV. EUGENIO GARZA SADA Y CALLE MARCOS CORONADO, LOS POCITOS Ej.					
NO. DE CONTR	FISMDF-0067-2022		CONTRATISTA:	ATECO, S.A. DE C.V.		

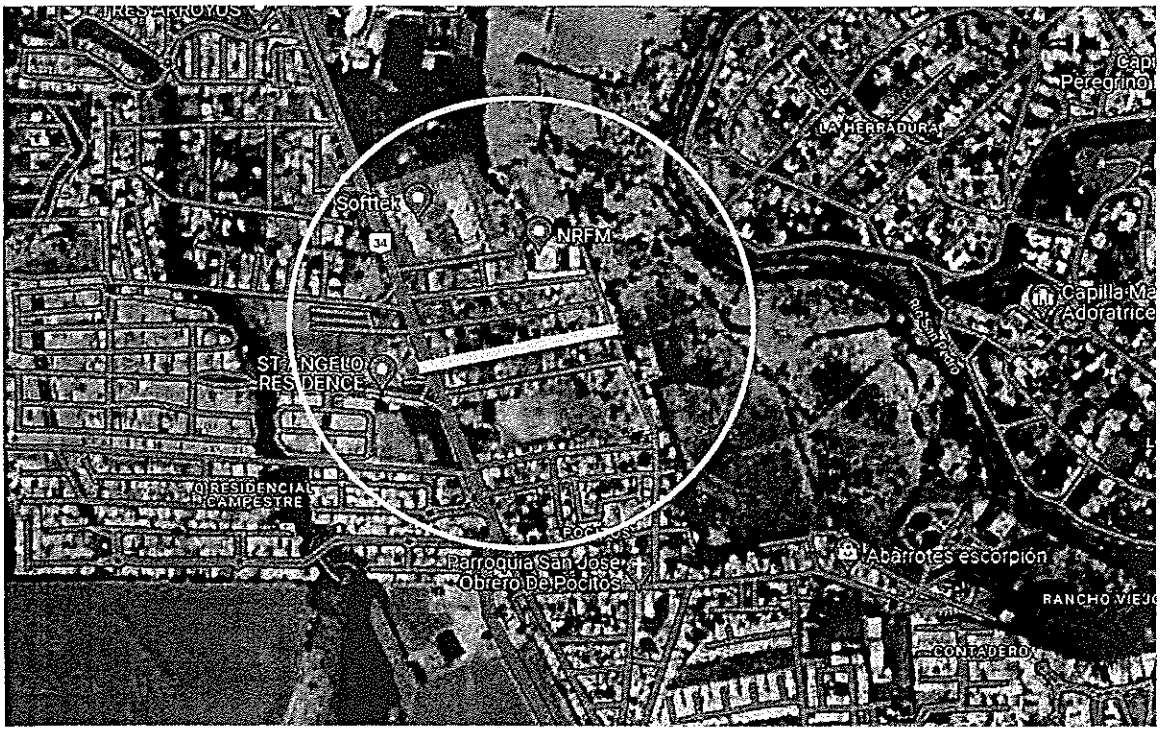

ING. IVAN ALEJANDRO RUIZ ESPARZA SOLIS
SUPERVISOR DE OBRA.

RO3-POS-SGS-7.5.1-04	
REVISION:	00
FECHA DE REVISION:	
RESPONSABLE:	SUPERVISOR DE OBRA
TIEMPO DE RET:	02 AÑOS

PROGRAMA DE OBRA DEFINITIVO

No. DE CONTRATO : FISMDF-0067-2022

PROGRAMA: 04 URBANIZACION MUNICIPAL

No. OBRA Y NOMBRE DE LA OBRA: PAVIMENTO HIDRÁULICO CALLE SANTA MÓNICA, TRAMO: ENTRE AV. EUGENIO GARZA SADA Y CALLE MARCOS CORONADO, LOS POCITOS EJ.

INICIO VIGENTE: 09-septiembre-22

TERMINO REAL: 22-noviembre-22

RECURSO 2022

CONCEPTO			1	2	3	4	5	6	7	8	9	10	11	12	13	14	15	16	PONDERACIÓN %	
			2022																FINANCIERO	FÍSICO
			OCTUBRE	NOVIEMBRE	DICIEMBRE	ENERO	FEBRERO	MARZO	ABRIL	MAYO	JUNIO	JULIO	AGOSTO	SEPTIEMBRE	OCTUBRE	NOVIEMBRE	DICIEMBRE	ENERO	%	%
DESCRIPCION		INVERSION														20	6			
PAVIMENTO HIDRAULICO CALLE SANTA MONICA, TRAMO: ENTRE AV. EUGENIO GARZA SADA Y CALLE MARCOS CORONADO, LOS POCITOS EJ.																				
TRAMO: ENTRE AV. EUGENIO GARZA SADA Y CALLE MARCOS CORONADO, LOS POCITOS EJ.																				
PRELIMINARES	$	4,168.25	100											50 50					0.11	7.69
PAVIMENTO HIDRAULICO	$	1,914,244.98	100											25 25		25 15 10			49.99	19.23
ALCANTARILLADO	$	519,134.30	100											10 30 50 10					13.56	15.38
AGUA POTABLE	$	159,809.00	100											10 30 50 10					4.17	15.38
BANQUETAS, RAMPAS Y GUA.	$	1,130,299.11	100											20 20 20 20 20					29.52	19.23
LIMPIEZAS	$	20,952.60	100											40		20 40			0.55	
SEÑALIZACION	$	80,924.40	100													50 30 20			2.11	11.54
			-																0.00	0.00
			-																	
			-																	
			-																	
			-																	
			-																	
SUBTOTAL SIN IVA	$	3,829,532.63	0 0 0 0	0 0 0 0	0 0 0 0	0 0 0 0	0 0 0 0	0 0 0 0	0 0 0 0	0 0 0 0	0 0 0 0	0 0 0 0	0 0 0 0	5 4 3 3	2 2 1 1	2 2 1 2	0 0 0 0	0 0 0		
AVACE SEMANAL %			0% 0% 0% 0%	0% 0% 0% 0%	0% 0% 0% 0%	0% 0% 0% 0%	0% 0% 0% 0%	0% 0% 0% 0%	0% 0% 0% 0%	0% 0% 0% 0%	0% 0% 0% 0%	0% 0% 0% 0%	0% 0% 0% 0%	19% 16% 17% 17%	8% 4% 4% 4%	4% 4% 4% 4%	0% 0% 0% 0%	0% 0% 0%		
AVANCE SEMANAL ACUMULADO %			0% 0% 0% 0%	0% 0% 0% 0%	0% 0% 0% 0%	0% 0% 0% 0%	0% 0% 0% 0%	0% 0% 0% 0%	0% 0% 0% 0%	0% 0% 0% 0%	0% 0% 0% 0%	0% 0% 0% 0%	0% 0% 0% 0%	19% 35% 52% 69%	77% 81% 85% 89%	93% 97% 100% 100%	100% 100% 100% 100%	100% 100% 100%	100.00	88.46
EJERCIDO SEMANAL $			- - - -	- - - -	- - - -	- - - -	- - - -	- - - -	- - - -	- - - -	- - - -	- - - -	- - - -	766,699.66 652,366.66 533,959.67 357,677.75	242,543.72 226,559.93 478,561.25 291,337.77	231,886.70 21,277.32 24,455.92 -	- - - -	- - -	$ 3,829,532.63		
EJERCIDO MENSUAL $			$0.00	$0.00	$0.00	$0.00	$0.00	$0.00	$0.00	$0.00	$0.00	$0.00	$0.00	$2,310,813.65	$1,237,089.06	$280,729.94	$0.00	$0.00	$ 612,725.22	IVA 16%
EJERCIDO MENSUAL ACUMULADO $			0.00	0.00	0.00	0.00	0.00	0.00	0.00	0.00	0.00	0.00	0.00	2,310,813.65	3,548,902.70	3,829,532.64	3,829,532.64	3,829,532.64		
EJERCIDO SEMANAL %			0% 0% 0% 0%	0% 0% 0% 0%	0% 0% 0% 0%	0% 0% 0% 0%	0% 0% 0% 0%	0% 0% 0% 0%	0% 0% 0% 0%	0% 0% 0% 0%	0% 0% 0% 0%	0% 0% 0% 0%	0% 0% 0% 0%	20% 17% 14% 9%	6% 6% 7% 7%	7% 1% 1% 0%	0% 0% 0% 0%	0% 0% 0%		
EJERCIDO MENSUAL %			0%	0%	0%	0%	0%	0%	0%	0%	0%	0%	0%	60%	32%	7%	0%	0%	GRAN TOTAL EJERCIDO	
EJERCIDO MENSUAL ACUMULADO %			0%	0%	0%	0%	0%	0%	0%	0%	0%	0%	0%	60%	93%	100%	100%	100%	$	4,442,257.87

PRE

ING. IVAN ALEJANDRO RUIZ ESPARZA SOLIS
SUPERVISOR

PRESIDENCIA MUNICIPAL DE AGUASCALIENTES

FACTIBILIDAD VERIFICADA EN CAMPO

GENERALES

EJERCICIO: 2022 APROBACION No: 2022-FISMDF-0067-0411101-023
LOCALIDAD: TRAMO: ENTRE AV. EUGENIO GARZA SADA Y CALLE MARCOS CORONADO, LOS POCITOS Ej.
MUNICIPIO: AGUASCALIENTES, Mpio.
TIPO DE INVERSION: FONDO PARA LA INFRAESTRUCTURA SOCIAL MUNICIPAL Y DE LAS DEMARCACIONES TERRITORIALES DEL DISTRITO FEDERAL (100%) (MUNICIPAL)
PROGRAMA: 04 URBANIZACION MUNICIPAL
SUB-PROGRAMA: 11 Calles y caminos

OBRA A REALIZARSE: PAVIMENTO HIDRÁULICO CALLE SANTA MÓNICA, TRAMO: ENTRE AV. EUGENIO GARZA SADA Y CALLE MARCOS CORONADO, LOS POCITOS Ej.

DEPENDENCIA EJECUTORA: SECRETARÍA DE OBRAS PÚBLICAS MUNICIPALES (S.O.P.M.A)
FORMACIÓN DE EJECUCION: CONTRATO NO. DE CONTRATO: FISMDF-0067-2022
NOMBRE CONTRATISTA: ATECO, S.A. DE C.V.
REPRESENTANTE: ARQ. LUIS FERNANDO GUTIERREZ PADILLA
MONTO CONT. ORIGEN $ 4,442,257.87 ANTICIPO: $ 1,148,859.79 PLAZO 75 DIAS
1A AMPLIACION $: $ - 1 AMPL DIAS
2A AMPLIACION $: 2 AMPL DIAS
FIRMA CONTRATO: 31/08/2022
INICIO CONT: dd/mm/aa 01/09/2022 TERMINO CONT: 14/11/2022
INICIO REAL: dd/mm/aa 09/09/2022 TERMINO REAL: 22/11/2022

TIPO DE OBRA PROPUESTA

NUEVA CREACIÓN	X	CONSOLIDACIÓN	
COMPLEMENTARIA		AMPLIACIÓN	
REHABILITACIÓN		EQUIPAMIENTO	

CARACTERÍSTICAS DE LA OBRA:

FORMACION Y COMPACTACION DE SUB-RASANTE, SUB-BASE Y BASE HIDRAULICA
PAVIMENTO HIDRAULICO A BASE CONCRETO PREMEZCLADO MR=38 KG/CM2
RED DE ALCANTARILLADO PVC SERIE 20 RED DE AGUA POTABLE PVC HIDRAULICO RD-26
CONSTRUCCION DE BANQUETAS RAMPAS Y GUARNICIONES

CONDICIONES ACTUALES DE LA OBRA: (SELECCIONAR UNO OBLIGATORIO)

BUEN ESTADO X REGULAR PESIMO ESTADO

FACTIBILIDAD DE LA OBRA: (CONDICIONES ACTUALES DE LA OBRA)

ESTA OBRA SE ENCUENTRA EN CONDICIONES PARA OPERARSE

PROCEDE: SI: X NO:
MARQUE SOLO UNA

ING. IVAN ALEJANDRO RUIZ ESPARZA SOLIS
SUPERVISOR

PRESIDENCIA MUNICIPAL DE AGUASCALIENTES

FACTIBILIDAD VERIFICADA EN CAMPO

GENERALES

LOCALIDAD: TRAMO: ENTRE AV. EUGENIO GARZA SADA Y CALLE MARCOS CORONADO, LOS POCITOS Ej.
MUNICIPIO: AGUASCALIENTES, Mpio.
PROGRAMA: 04 URBANIZACION MUNICIPAL
SUB-PROGRAMA: 11 Calles y caminos
OBRA A REALIZARSE: PAVIMENTO HIDRÁULICO CALLE SANTA MÓNICA, TRAMO: ENTRE AV. EUGENIO GARZA SADA Y CALLE MARCOS CORONADO, LOS POCITOS Ej.

DEPENDENCIA EJECUTORA: SECRETARÍA DE OBRAS PÚBLICAS MUNICIPALES (S.O.P.M.A)
FORMACIÓN DE EJECUCION: CONTRATO

TIPO DE OBRA PROPUESTA

NUEVA CREACIÓN	X	CONSOLIDACIÓN	
COMPLEMENTARIA		AMPLIACIÓN	
REHABILITACIÓN		EQUIPAMIENTO	

CARACTERÍSTICAS DE LA OBRA:

FORMACION Y COMPACTACION DE SUB-RASANTE, SUB-BASE Y BASE HIDRAULICA
PAVIMENTO HIDRAULICO A BASE CONCRETO PREMEZCLADO MR=38 KG/CM2
RED DE ALCANTARILLADO PVC SERIE 20 RED DE AGUA POTABLE PVC HIDRAULICO RD-26
CONSTRUCCION DE BANQUETAS RAMPAS Y GUARNICIONES

CONDICIONES ACTUALES DE LA OBRA:

BUEN ESTADO: X REGULAR: PESIMO ESTADO:

FACTIBILIDAD DE LA OBRA:

ESTA OBRA SE ENCUENTRA EN CONDICIONES PARA OPERARSE

PROCEDE **SI:** X **NO:**

ING. IVAN ALEJANDRO RUIZ ESPARZA SOLIS
SUPERVISOR

PRESUPUESTO MODIFICADO

Obra: **PAVIMENTO HIDRÁULICO CALLE SANTA MÓNICA**

Ubicación: **TRAMO: ENTRE AV. EUGENIO GARZA SADA Y CALLE MARCOS CORONADO, LOS POCITOS Ej.**

Contratista: **ATECO, S.A. DE C.V. (102)**

No.	Concepto	Unidad	Cantidad	Precio Unitario	Importe Total
	GRUPO: **PRELIMINARES**				
	PARTIDA: **DEMOLICIONES Y DESMONTAJES**				
2	DEMOLICION PARCIAL DE PAVIMENTO HIDRAULICO Y/O ASFALTICO DE HASTA 15 CM. DE ESPESOR PROMEDIO EN PAVIMENTOS (LOSAS DIAMANTE Y CAJAS DE VALVULAS, TOPES) CON O SIN ARMADO DE ACERO, SIN RECUPERACION, MUROS, MOJONERAS, ANCLAJES, ETC, DE FORMA MANUAL Y MECANICA, INCLUYE CORTE CON DISCO, ACARREO DE MATERIAL AL LUGAR DE ACOPIO, HERRAMIENTA NECESARIA Y TODO LO NECESARIO PARA SU CORRECTA EJECUCION, LIMPIEZA, TRABAJO TERMINADO	M3	12.42	$269.02	$3,341.23
4	CARGA MECANICA Y ACARREO DE MATERIAL PRODUCTO DE EXCAVACION Y DEMOLICION EN CAMION DE VOLTEO AL 1er. KM, VOLUMEN MEDIDO COMPACTO.	M3	12.42	$28.82	$357.94
5	ACARREO DE MATERIAL PRODUCTO DE EXCAVACION Y/O DEMOLICION EN CAMION DE VOLTEO A KILOMETROS SUBSECUENTES, AL TIRADERO OFICIAL AUTORIZADO MAS CERCANO AUTORIZADO POR LA SUPERVISION, VOLUMEN MEDIDO COMPACTO.	M3-KM	49.69	$9.44	$469.07
				Totales por Partida	**$4,168.25**
				Totales por Grupo	**$4,168.25**

Obra: **PAVIMENTO HIDRÁULICO CALLE SANTA MÓNICA**

Ubicación: **TRAMO: ENTRE AV. EUGENIO GARZA SADA Y CALLE MARCOS CORONADO, LOS POCITOS Ej.**

Contratista: **ATECO, S.A. DE C.V. (102)**

No.	Concepto	Unidad	Cantidad	Precio Unitario	Importe Total
	GRUPO: **PAVIMENTO HIDRAULICO**				
	PARTIDA: **PRELIMINARES**				
6	LIMPIA, TRAZO Y NIVELACION EN PAVIMENTOS, CALLES Y VIALIDADES CON EQUIPO TOPOGRAFICO, INCLUYE: EJES, BANCO DE NIVEL, RENIVELACIONES LAS VECES NECESARIAS, CORRECCION DE RASANTE A PUNTOS OBLIGADOS (AUTORIZADOS POR LA SUPERVISION), ESTACAS, VARILLAS, MANO DE OBRA CALIFICADA, HERRAMIENTA NECESARIA, EQUIPO DE PRECISION CALIBRADO, TRABAJO TERMINADO.P.U.O.T.	M2	2820	$7.18	$20,247.6(
7	SONDEO A MANO O A MAQUINA PARA LOCALIZACION DE TUBERIAS CUALQUIER PROFUNDIDAD Y MATERIAL PARA VERIFICAR LA CALIDAD DE LAS INSTALACIONES HIDRAULICO SANITARIAS CUIDANDO NO DAÑARLAS PARA NO INTERFERIR EN LOS SERVICIOS, INCLUYE: EXCAVACION, EQUIPO, MANO DE OBRA, REPORTE A LA SUPERVISION, RELLENOS, COMPACTACIONES, TRABAJO TERMINADO.	SONDE	4	$2,468.54	$9,874.1(
			Totales por Partida		**$30,121.7(**
	PARTIDA: **EXCAVACIONES, ACARREOS Y TERRACERIAS**				
8	EXCAVACION EN CORTE CON MAQUINA HASTA UNA PROFUNDIDAD DE 75 CM, EN MATERIAL TIPO II, INCLUYE: AFLOJE Y EXTRACCION DE MATERIAL, ACARREOS AL LUGAR DE ACOPIO PARA SU CARGA Y ACARREO FUERA DE LA OBRA, VOLUMEN MEDIDO COMPACTO.	M3	1501.4	$72.64	$109,061.7(
9	COMPACTACION DE TERRENO NATURAL AL 90% DE SU P.V.S.M EN SU COMPACTACION., INCLUYE ESCARIFICADO, TENDIDO, HOMOGENIZADO, HUMEDECIDO OPTIMO NIVELADO Y COMPACTADO EN CAPAS DE 20 CM, CALIDAD Limite liquido máximo 50%, Valor de Soporte California (CBR) mínimo 15%, Expansión máxima 5%, Grado de Compactación minimo 90% ± 2, Y TODO LO NECESARIO PARA SU CORRECTA EJECUCION.	M2	1860	$20.32	$37,795.2(
10	FORMACION Y COMPACTACION DE SUB-RRASANTE, CON EL USO DE EQUIPO MAYOR, HASTA ALCANZAR EL 100% AASHTO MODIFICADA. EN CAPAS DE 20 CM MAXIMO, INCLUYE: SUMINISTRO DE MATERIAL DE BANCO QUE CUMPLA CON LA NORMA, HUMEDAD OPTIMA Y TODO LO NECESARIO PARA SU CORRECTA COLOCACION, EL MATERIAL DEBERA CUMPLIR CON UN C.B.R. DEL 60% PARA LO CUAL EL CONTRATISTA DEBERA PROPONER UN BANCO DE MATERIAL Y UN FRENTE, DEBERA PRESENTAR EL ESTUDIO DE CALIDAD QUE AVALE EL CUMPLIMIENTO AL 100 % DE LA NORMA Y DEMAS CARACTERISTICAS SOLICITADAS, P.U.O.T.	M3	558	$339.66	$189,530.28
11	FORMACION Y COMPACTACION DE SUB-BASE PARA MAS DE UN MILLON DE EJES EQUIVALENTES, CON EL USO DE EQUIPO MAYOR, HASTA ALCANZAR EL 100% AASHTO MODIFICADA. EN CAPAS DE 20 CM MAXIMO, INCLUYE: SUMINISTRO DE MATERIAL DE BANCO QUE CUMPLA CON LA NORMA, HUMEDAD OPTIMA Y TODO LO NECESARIO PARA SU CORRECTA COLOCACION, EL MATERIAL DEBERA CUMPLIR CON UN C.B.R. DEL 60% PARA LO CUAL EL CONTRATISTA DEBERA PROPONER UN BANCO DE MATERIAL Y UN FRENTE, DEBERA PRESENTAR EL ESTUDIO DE CALIDAD QUE AVALE EL CUMPLIMIENTO AL 100 % DE LA NORMA N-CMT-4-02-001. Y DEMAS CARACTERISTICAS SOLICITADAS, P.U.O.T.	M3	372	$342.57	$127,436.04
12	FORMACION Y COMPACTACION DE BASE HIDRAULICA PARA MAS DE UN MILLON DE EJES EQUIVALENTES DE 20 CMS. DE ESPESOR, PARA CARPETA DE CONCRETO HIDRAULICO, CON MATERIAL 100% TRITURADO (SOLAMENTE) 1 1/2" A FINOS QUE CUMPLA CON LA NORMA COMPACTADA AL 100 % DE PRUEBA AASHTO. COMBINANDO COMPACTADOR DE RODILLO EN BAJA Y MUERTO Y LLANTEO CON EQUIPO PESADO (CAMION DE VOLTEO CARGADO AL MAXIMO), INCLUYE HOMOGENEIZADO, TENDIDO, COMPACTADO, E INCORPORACION DE AGUA HASTA ALCANZAR LA HUMEDAD OPTIMA Y NIVELACIONES.	M3	372	$694.84	$258,480.48

Obra: **PAVIMENTO HIDRÁULICO CALLE SANTA MÓNICA**

Ubicación: **TRAMO: ENTRE AV. EUGENIO GARZA SADA Y CALLE MARCOS CORONADO, LOS POCITOS Ej.**

Contratista: **ATECO, S.A. DE C.V. (102)**

No.	Concepto	Unidad	Cantidad	Precio Unitario	Importe Total
	GRUPO: **PAVIMENTO HIDRAULICO**				
	PARTIDA: **EXCAVACIONES, ACARREOS Y TERRACERIAS**				
13	CARGA MECANICA Y ACARREO DE MATERIAL PRODUCTO DE EXCAVACION Y DEMOLICION EN CAMION DE VOLTEO AL 1er. KM, VOLUMEN MEDIDO COMPACTO.	M3	1501.4	$28.82	$43,270.35
14	ACARREO DE MATERIAL PRODUCTO DE EXCAVACION Y/O DEMOLICION EN CAMION DE VOLTEO A KILOMETROS SUBSECUENTES, AL TIRADERO OFICIAL AUTORIZADO MAS CERCANO AUTORIZADO POR LA SUPERVISION, VOLUMEN MEDIDO COMPACTO.	M3-KM	6005.6	$9.44	$56,692.86
			Totales por Partida		**$822,266.91**
	PARTIDA: **PAVIMENTO HIDRAULICO**				
15	CONSTRUCCION DE PAVIMENTO HIDRAULICO A BASE DE CONCRETO PREMEZCLADO MR=38 KG/CM2 TMA 1 1/2" GRAVA TRITURADA, REVENIMIENTO DE 6 A 8 CM FRAGUADO NORMAL DE 15 CM DE ESPESOR MODULADO EN LOSAS DE 3.5 MTS. (ANCHO) X 3.5 MTS (LARGO) COMO MAXIMO, CON CORTES EN LAS LOSAS DE 1/3 DEL ESPESOR DE LA LOSA (5 CM) Y SELLADO CON COLA DE RATA Y MATERIAL ELASTOMERICO Y TIRA PREFORMADA (FOAMTECH DE 1/2X15) EN JUNTAS Y CORTES LONGITUDINALES Y TRANSVERSALES, ASI COMO EL APROCHE CON GUARNICION Y DENTELLON. INCLUYE: CIMBRADO, COLADO, VIBRADO CON INMERSION Y REGLA VIBRATORIA, DESCIMBRADO, REGLEADO FINAL, ACABADO CEPILLO DE ALUMINIO Y CON DOBLADOR, CALAFATEO, CURADO CON MEMBRANA BASE AGUA Y TODO LO NECESARIO PARA SU CORRECTA COLOCACION, P.U.O.T.	M2	1666.369711	$596.29	$993,639.59
			Totales por Partida		**$993,639.59**
	PARTIDA: **OBRA COMPLEMENTARIA**				
24	RENIVELACION DE POZO DE VISITA HASTA 0.30 m DE ALTURA. INCLUYE: RETIRO SIN RECUPERACION DE BROCAL EXISTENTE, NIVELADO CON TABIQUE ROJO RECOCIDO 7X14X28, ASENTADO CON MORTERO CEMENTO-ARENA 1:3 DE 28 cm DE ESPESOR, APLANADO CON MORTERO CEMENTO-ARENA 1:3, PLOMEADO, NIVELADO, DEMOLICIONES, CARGAS Y ACARREOS DENTRO DE LA OBRA, LIMPIEZAS	PZA	4	$1,767.76	$7,071.04
25	CONSTRUCCION DE LOSA DE DIAMANTE DE CONCRETO MR= 45 , T.M.A. DE 3/4" (19MM), GRAVA TRITURADA, REVENIMIENTO DE 8+-2.5CM CM, FRAGUADO RAPIDOA A 3 DIAS, DE 25 CM DE ESPESOR, EN POZO DE VISITA, Y 1.50 M POR LADO, INCLUYE: SUMINISTRO DE MATERIALES, ESPUMA DE POLIURETANO DE ALTA DENSIDAD EN TODO EL PERIMETRO EXTERIOR DE 1/2" ASI COMO DE LAS JUNTAS DIAGONALES PARA FORMAR 4 PARTES, BROCAL Y TAPA DE Fo. Fo. TIPO PESADO, (165 KG), CIMBRADO, COLADO, VIBRADO, DESCIMBRADO, CURADO CON MEMBRANA QUIMICA BASE AGUA, APLANADO FINO EN RECEPCION DE BROCAL, CORTES CON CORTADORA DE DISCO DE 5 CM ENTRE JUNTAS DIAGONALES FORMADO 8 PIEZAS Y SELLADO DE JUNTAS Y CORTES CON MATERIAL PREFORMADO Y SELLADOR AUTONIVELANTE, MANO DE OBRA, ACARREOS DE MATERIAL DENTRO Y FUERA DE LA OBRA, TRABAJO TERMINADO. P.U.O.T.	PZA	4	$8,144.83	$32,579.32

Obra: **PAVIMENTO HIDRÁULICO CALLE SANTA MÓNICA**

Ubicación: **TRAMO: ENTRE AV. EUGENIO GARZA SADA Y CALLE MARCOS CORONADO, LOS POCITOS Ej.**

Contratista: **ATECO, S.A. DE C.V. (102)**

No.	Concepto	Unidad	Cantidad	Precio Unitario	Importe Total
	GRUPO: **PAVIMENTO HIDRAULICO**				
	PARTIDA: **OBRA COMPLEMENTARIA**				
26	LIMPIEZA Y DESASOLVE DE POZOS DE VISITA Y LINEAS DE ALCANTARILLADO EXISTENTE CON CAMION TIPO VACTOR. INCLUYE: RESANE INTERIOR DEL POZO Y REMTE DE POZO CO TUBO CON SELLADOR, FESTER Y MORTERO 1:3, MANO DE OBRA, SUMINISTRO DE AGUA EN PIPA, HERRAMIENTAS Y EQUIPO PARA SU CORRECTA EJECUCION, LIMPIEZAS, RENTA DE CAMION VACTOR HASTA LA CORRECTA LIMPIEZA DE LAS LINEAS EXISTENTES DE POZO A POZO, ASI COMO EL TRASLADO DE LOS DESECHOS HASTA TIRADERO AUTORIZADO MEDIDO POZO A POZO.	LOTE	4	$7,141.59	$28,566.36
				Totales por Partida	**$68,216.72**
				Totales por Grupo	**$1,914,244.98**

Obra: **PAVIMENTO HIDRÁULICO CALLE SANTA MÓNICA**

Ubicación: **TRAMO: ENTRE AV. EUGENIO GARZA SADA Y CALLE MARCOS CORONADO, LOS POCITOS Ej.**

Contratista: **ATECO, S.A. DE C.V. (102)**

No.	Concepto	Unidad	Cantidad	Precio Unitario	Importe Total
	GRUPO: **ALCANTARILLADO**				
	PARTIDA: **RED DE ALCANTARILLADO**				
28	TRAZO Y NIVELACION DE TERRENO CON APARATO TOPOGRAFICO, PARA LINEAS DE AGUA POTABLE Y ALCANTARILLADO, INCLUYE: EJES, BANCOS DE NIVEL, RENIVELACIONES, TRABAJO TERMINADO.	ML	333	$10.23	$3,406.5
29	EXCAVACION A MAQUINA EN ZANJAS EN MATERIAL TIPO II DE 0.00 A 2.00 M DE PROFUNDIDAD, INCLUYE: AFLOJE Y EXTRACCION DEL MATERIAL, AFINE, TRASPALEO VERTICAL PARA SU EXTRACCION, CONSERVACION DE LA EXCAVACION, ACARREO HASTA EL LUGAR DE ACOPIO PARA SU CARGA Y ACARREO FUERA DE LA OBRA, SEÑALAMIENTOS, COLOCACION DE PASOS PEATONALES Y PROTECCION PERIMETRAL DE LA ZANJA.	M3	169.83	$80.42	$13,657.7
30	PLANTILLA Y ACOSTILLADO CON GRAVA CANTO RODADO MEZCLADO DE 3/4 A 1" Y ARENA (50-50) Y PISON DE MANO, INCLUYE: SUMINISTRO DE MATERIAL EN LA OBRA, ACARREO EN CARRETILLA, DESCARGA EN LA ZANJA, EXTENDIDO, NIVELADO Y APISONADO, APOYO SEMICIRCULAR PARA LA TUBERIA SE CONSTRUIRA INMEDIATAMENTE ANTES DE TENDER LA TUBERIA, DEBIENDO COLOCAR HILOS LONGITUDINALMENTE PARA VERIFICAR LA UNIFORMIDAD DE LA PLANTILLA.	M3	22.91	$799.24	$18,310.5
31	ACOSTILLADO CON MATERIAL DE PROD. DE EXCAVACION EN CAPAS DE 20 CMS. AL 85% DE SU P.V.M.S. CON EL USO DE BAILARINA, HOMOGENIZACION DEL MATERIAL, AGUA LA NECESARIA, EXTENDIDO Y COMPACTADO.	M3	30.55	$211.83	$6,471.4
32	RELLENO COMPACTADO AL 90% CON MATERIAL DE BANCO EN CAPAS DE 20 CM UTILIZANDO BAILARINA. INCLUYE: SUMINISTRO DE TEPETATE EN LA OBRA, ABUNDAMIENTO, ACARREOS DENTRO DE LA OBRA, CIMBRADO, RETIRO DE MATERIAL, MANO DE OBRA Y EQUIPO, PRUEBA DE CONTROL DE CALIDAD.	M3	109.89	$358.89	$39,438.4
34	CARGA MECANICA Y ACARREO DE MATERIAL PRODUCTO DE EXCAVACION Y DEMOLICION EN CAMION DE VOLTEO AL 1er. KM, VOLUMEN MEDIDO COMPACTO.	M3	127.87	$28.82	$3,685.2
35	ACARREO DE MATERIAL PRODUCTO DE EXCAVACION Y/O DEMOLICION EN CAMION DE VOLTEO A KILOMETROS SUBSECUENTES, AL TIRADERO OFICIAL AUTORIZADO MAS CERCANO AUTORIZADO POR LA SUPERVISION, VOLUMEN MEDIDO COMPACTO.	M3-KM	519.48	$9.44	$4,903.8
36	SUMINISTRO DE TUBERIA DE PVC PARA ALCANTARILLADO SERIE 20 DE 10", CON JUNTA HERMETICA, INCLUYE: FLETES Y ACARREO HASTA EL SITIO DE SU COLOCACION, ALINEADO, MATERIAL, CUBIERTA DE PROTECCION, ESTIBADO, MANO DE OBRA.	ML	333	$467.25	$155,594.2
37	INSTALACION DE TUBERIA DE PVC PARA ALCANTARILLADO SERIE 20 DE 10", CON JUNTA HERMETICA. INCLUYE: FLETES Y ACARREO HASTA EL SITIO DE SU COLOCACION, MATERIALES DE LIMPIEZA, LUBRICACION, NIVELADO, MATERIAL Y MANO DE OBRA.	ML	333	$93.37	$31,092.2
38	CONEXION DE TUBERIA DE PVC DE 8-16" A POZO DE VISITA, INCLUYE: DEMOLICION DE MURO DE POZO, CONEXION Y NIVELACION DEL TUBO, RESANE DEL MURO, APLANADO INTERIOR ACABADO PULIDO, LIGAS, LIMPIEZA Y RETIRO DE ESCOMBRO A 20 M.	PZA	6	$2,154.89	$12,929.3
			Totales por Partida		**$289,489.6**
	PARTIDA: **DESCARGAS DOMICILIARIAS**				
39	EXCAVACION A MAQUINA EN ZANJAS EN MATERIAL TIPO II DE 0.00 A 2.00 M DE PROFUNDIDAD, INCLUYE: AFLOJE Y EXTRACCION DEL MATERIAL, AFINE, TRASPALEO VERTICAL PARA SU EXTRACCION, CONSERVACION DE LA EXCAVACION, ACARREO HASTA EL LUGAR DE ACOPIO PARA SU CARGA Y ACARREO FUERA DE LA OBRA, SEÑALAMIENTOS, COLOCACION DE PASOS PEATONALES Y PROTECCION PERIMETRAL DE LA ZANJA.	M3	28.69	$80.42	$2,307.2

Obra: **PAVIMENTO HIDRÁULICO CALLE SANTA MÓNICA**

Ubicación: **TRAMO: ENTRE AV. EUGENIO GARZA SADA Y CALLE MARCOS CORONADO, LOS POCITOS Ej.**

Contratista: **ATECO, S.A. DE C.V. (102)**

No.	Concepto	Unidad	Cantidad	Precio Unitario	Importe Total
	GRUPO: **ALCANTARILLADO**				
	PARTIDA: **DESCARGAS DOMICILIARIAS**				
40	PLANTILLA Y ACOSTILLADO CON GRAVA CANTO RODADO MEZCLADO DE 3/4 A 1" Y ARENA (50-50) Y PISON DE MANO, INCLUYE: SUMINISTRO DE MATERIAL EN LA OBRA, ACARREO EN CARRETILLA, DESCARGA EN LA ZANJA, EXTENDIDO, NIVELADO Y APISONADO, APOYO SEMICIRCULAR PARA LA TUBERIA SE CONSTRUIRA INMEDIATAMENTE ANTES DE TENDER LA TUBERIA, DEBIENDO COLOCAR HILOS LONGITUDINALMENTE PARA VERIFICAR LA UNIFORMIDAD DE LA PLANTILLA.	M3	6.01	$799.24	$4,803.4
41	ACOSTILLADO CON MATERIAL DE PROD. DE EXCAVACION EN CAPAS DE 20 CMS. AL 85% DE SU P.V.M.S. CON EL USO DE BAILARINA, HOMOGENIZACION DEL MATERIAL, AGUA LA NECESARIA, EXTENDIDO Y COMPACTADO.	M3	8.03	$211.83	$1,700.9
42	RELLENO COMPACTADO AL 90% CON MATERIAL DE BANCO EN CAPAS DE 20 CM UTILIZANDO BAILARINA. INCLUYE: SUMINISTRO DE TEPETATE EN LA OBRA, ABUNDAMIENTO, ACARREOS DENTRO DE LA OBRA, CIMBRADO, RETIRO DE MATERIAL, MANO DE OBRA Y EQUIPO, PRUEBA DE CONTROL DE CALIDAD.	M3	2.97	$358.89	$1,065.9
44	CARGA MECANICA Y ACARREO DE MATERIAL PRODUCTO DE EXCAVACION Y DEMOLICION EN CAMION DE VOLTEO AL 1er. KM, VOLUMEN MEDIDO COMPACTO.	M3	20.66	$28.82	$595.4
45	ACARREO DE MATERIAL PRODUCTO DE EXCAVACION Y/O DEMOLICION EN CAMION DE VOLTEO A KILOMETROS SUBSECUENTES, AL TIRADERO OFICIAL AUTORIZADO MAS CERCANO AUTORIZADO POR LA SUPERVISION, VOLUMEN MEDIDO COMPACTO.	M3-KM	82.62	$9.44	$779.9
46	DESCARGA DOMICILIARIA PARA USO FUTURO DE 6.00 A 9.00 M DE LONGITUD (NOMINAL), A BASE DE TUBO DE PVC ALCANTARILLADO SERIE 20 DE 6" DE DIAMETRO, INCLUYE: SILLETA DE 10" X 6", CODO DE 6" X 45°, TAPON HEMBRA, ALINEACION, INDICACION DE UBICACION CON VARILLA EN PREDIO, PRUEBAS DE ESCURRIMIENTO, SUMINISTROS, ACARREOS, TRABAJO TERMINADO.	PZA	37	$2,480.29	$91,770.7
47	REGISTRO SANTARIO DE 0.40X0.60X0.80 M (MEDIDAS INTERIORES) DE TABIQUE ROJO RECOCIDO (14 CM DE ESPESOR) JUNTEADO CON MORTERO CEMENTO-ARENA 1:4 Y APLANADO DE 2.00 CM CON EL MISMO MORTERO, ACABADO PULIDO INTERIOR, PLANTILLA DE 7.00 CM DE ESPESOR DE CONCRETO F'C=150 KG/CM2, HECHO EN OBRA, TMA 19 MM. INCLUYE: MARCO Y CONTRAMARCO DE ANGULO DE 2" X 3/16" COLADA CON EL MISMO CONCRETO, PLOMEADO, ALINEADO, NIVELADO, ACARREOS DENTRO DE LA OBRA Y CONEXION A RED EXISTENTE, LIMPIEZAS.	PZA	50	$2,532.42	$126,621.0
				Totales por Partida	**$229,644.6**
				Totales por Grupo	**$519,134.3**

Obra: **PAVIMENTO HIDRÁULICO CALLE SANTA MÓNICA**

Ubicación: **TRAMO: ENTRE AV. EUGENIO GARZA SADA Y CALLE MARCOS CORONADO, LOS POCITOS Ej.**

Contratista: **ATECO, S.A. DE C.V. (102)**

No.	Concepto	Unidad	Cantidad	Precio Unitario	Importe Total
	GRUPO: **AGUA POTABLE**				
	PARTIDA: **RE DE AGUA POTABLE**				
48	TRAZO Y NIVELACION DE TERRENO CON APARATO TOPOGRAFICO, PARA LINEAS DE AGUA POTABLE Y ALCANTARILLADO, INCLUYE: EJES, BANCOS DE NIVEL, RENIVELACIONES, TRABAJO TERMINADO.	ML	333	$10.23	$3,406.59
49	EXCAVACION A MAQUINA EN ZANJAS EN MATERIAL TIPO II DE 0.00 A 2.00 M DE PROFUNDIDAD, INCLUYE: AFLOJE Y EXTRACCION DEL MATERIAL, AFINE, TRASPALEO VERTICAL PARA SU EXTRACCION, CONSERVACION DE LA EXCAVACION, ACARREO HASTA EL LUGAR DE ACOPIO PARA SU CARGA Y ACARREO FUERA DE LA OBRA, SEÑALAMIENTOS, COLOCACION DE PASOS PEATONALES Y PROTECCION PERIMETRAL DE LA ZANJA.	M3	79.92	$80.42	$6,427.17
51	PLANTILLA Y ACOSTILLADO CON GRAVA CANTO RODADO MEZCLADO DE 3/4 A 1" Y ARENA (50-50) Y PISON DE MANO, INCLUYE: SUMINISTRO DE MATERIAL EN LA OBRA, ACARREO EN CARRETILLA, DESCARGA EN LA ZANJA, EXTENDIDO, NIVELADO Y APISONADO, APOYO SEMICIRCULAR PARA LA TUBERIA SE CONSTRUIRA INMEDIATAMENTE ANTES DE TENDER LA TUBERIA, DEBIENDO COLOCAR HILOS LONGITUDINALMENTE PARA VERIFICAR LA UNIFORMIDAD DE LA PLANTILLA.	M3	21.15	$799.24	$16,903.93
52	ACOSTILLADO CON MATERIAL DE PROD. DE EXCAVACION EN CAPAS DE 20 CMS. AL 85% DE SU P.V.M.S. CON EL USO DE BAILARINA, HOMOGENIZACION DEL MATERIAL, AGUA LA NECESARIA, EXTENDIDO Y COMPACTADO.	M3	42.3	$211.83	$8,960.41
53	RELLENO COMPACTADO AL 90% CON MATERIAL DE BANCO EN CAPAS DE 20 CM UTILIZANDO BAILARINA. INCLUYE: SUMINISTRO DE TEPETATE EN LA OBRA, ABUNDAMIENTO, ACARREOS DENTRO DE LA OBRA, CIMBRADO, RETIRO DE MATERIAL, MANO DE OBRA Y EQUIPO, PRUEBA DE CONTROL DE CALIDAD.	M3	19.98	$358.89	$7,170.62
55	CARGA MECANICA Y ACARREO DE MATERIAL PRODUCTO DE EXCAVACION Y DEMOLICION EN CAMION DE VOLTEO AL 1er. KM, VOLUMEN MEDIDO COMPACTO.	M3	59.94	$28.82	$1,727.47
56	ACARREO DE MATERIAL PRODUCTO DE EXCAVACION Y/O DEMOLICION EN CAMION DE VOLTEO A KILOMETROS SUBSECUENTES, AL TIRADERO OFICIAL AUTORIZADO MAS CERCANO AUTORIZADO POR LA SUPERVISION, VOLUMEN MEDIDO COMPACTO.	M3-KM	239.76	$9.44	$2,263.33
57	SUMINISTRO DE TUBERIA DE PVC HIDRAULICO RD-26 DE 3" CON CAMPANA INTEGRAL, COPLES, CODOS, TEES, INCLUYE: ACARREOS HASTA EL SITIO DE SU COLOCACION, BAJADO, ALINEADO, INSTALACION DE COPLES, ANILLO Y PRUEBA HIDROSTATICA.	ML	333	$98.02	$32,640.66
58	INSTALACION DE TUBERIA DE PVC HIDRAULICO RD-26 DE 3" CON CAMPANA INTEGRAL. INCLUYE: ACARREO HASTA EL SITIO DE SU COLOCACION, BAJADO, ALINEAMIENTO, INSTALACION DE COPLES, ANILLO Y PRUEBA HIDROSTATICA.	ML	333	$35.08	$11,681.64
			Totales por Partida		**$91,181.82**
	PARTIDA: **TOMAS DOMICILIARIAS**				
70	CONSTRUCCION DE TOMA DOMICILIARIA DE 6 A 9 M DE LONGITUD (NOMINAL) A BASE DE TUBO KITEC DE 1/2" AZUL, CONECTORES PHILMAC MACHO Y HEMBRA, ABRAZADERAS SIN FIN, CONECTOR A TUBO GALVANIZADO, ABRAZADERA DE PVC DE 3" X 1/2", TAPON HEMBRA. INCLUYE: ENCAMISADO CON POLIDUCTO ELECTRICO DE 1 1/2", PRUEBAS, SUMINISTROS, ACARREOS LOCALES, MANO DE OBRA, TRABAJO TERMINADO.	PZA	62	$1,106.89	$68,627.18
			Totales por Partida		**$68,627.18**
			Totales por Grupo		**$159,809.00**

Obra: **PAVIMENTO HIDRÁULICO CALLE SANTA MÓNICA**

Ubicación: **TRAMO: ENTRE AV. EUGENIO GARZA SADA Y CALLE MARCOS CORONADO, LOS POCITOS Ej.**

Contratista: **ATECO, S.A. DE C.V. (102)**

No.	Concepto	Unidad	Cantidad	Precio Unitario	Importe Total
	GRUPO: **BANQUETAS, RAMPAS Y GUARNICIONES**				
	PARTIDA: **BANQUETAS Y RAMPAS**				
75	COMPACTACION POR MEDIOS MECANICOS DE TERRENO NATURAL AL 90% DE SU PVSM EN UN ESPESOR DE 20 CM , INCLUYE: ESCARIFICADO, MANIOBRAS, HUMEDECIDO, SELECCION DE MATERIAL, ACARREOS DENTRO DE LA OBRA, MEDIDO COMPACTO, LIMPIEZAS Y TODO LO NECESARIO PARA SU CORRECTA APLICACION, TRABAJO TERMINADO.	M2	740.5	$30.31	$22,444.5(
76	RELLENO COMPACTADO AL 90% CON MATERIAL DE BANCO EN CAPAS DE 20 CM UTILIZANDO BAILARINA. INCLUYE: SUMINISTRO DE TEPETATE EN LA OBRA, ABUNDAMIENTO, ACARREOS DENTRO DE LA OBRA, CIMBRADO, RETIRO DE MATERIAL, MANO DE OBRA Y EQUIPO, PRUEBA DE CONTROL DE CALIDAD.	M3	261.52	$358.89	$93,856.9
78	CONSTRUCCION DE RAMPA DE ACCESO HABITACIONAL O DOMESTICO DE 10 CM DE ESPESOR A BASE DE CONCRETO PREMEZCLADO MR 38 KGF/CM2, T.M.A. 1 1/2", R.N. GRAVA TRITURADA, REVENIMIENTI DE 10+-2 CM, ACABADO RAYADO GRUESO CON ESCOBA DOMESTICA, JUNTAS FRIAS CON DOBLADOR DE 2" SECCION DE LOSAS COMO INDIQUE PROYECTO, INCLUYE: JUNTA A BASE DE ESPUMA DE POLIETILENO DE CELDAS CERRADAS DE 1/2" EN JUNTAS FRIAS LONGITUDINALES CON MUROS Y TRANSVERSALES DEL ELEMENTO, ASI COMO SU UNION CON ELEMENTOS VIEJOS O CAMBIO DE ELEMENTO O PENDIENTE, CIMBRADO, COLADO, DESCIMBRADO, CORTES CON CORTADORA DE DISCO, SELLADO DE CORTES CON SELLADOR AUTONIVELANTE Y TIRA DE RELLENO PREFORMADA NO ADHERENTE DE 1/8" (EN TODAS LAS JUNTAS DE CONTRACCCION Y CONSTRUCCION TRANSVERSALES), CURADO CON MEMBRANA QUIMICA APLICADA CON ASPERSOR, TRABAJO TERMINADO P.U.O.T.	M2	20.29	$484.22	$9,824.8
79	CONSTRUCCION DE BANQUETA DE 10 CM DE ESPESOR A BASE DE CONCRETO PREMEZCLADO F'C=150 KG/CM2, T.M.A. 3/4", R.N. GRAVA TRITURADA, REVENIMIENTI DE 10+-2 CM, ACABADO RAYADO FINO CON BROCHA DE PELO, JUNTAS FRIAS CON DOBLADOR DE 2" SECCION DE LOSAS COMO INDIQUE PROYECTO, INCLUYE: JUNTA A BASE DE ESPUMA DE POLIETILENO DE CELDAS CERRADAS DE 1/2" EN JUNTAS FRIAS LONGITUDINALES CON MUROS Y TRANSVERSALES DEL ELEMENTO, ASI COMO SU UNION CON ELEMENTOS VIEJOS O CAMBIO DE ELEMENTO, CIMBRADO, COLADO, DESCIMBRADO, CORTES CON CORTADORA DE DISCO, SELLADO DE CORTES CON SELLADOR AUTONIVELANTE Y TIRA DE RELLENO PREFORMADA NO ADHERENTE DE 1/8" (EN TODAS LAS JUNTAS DE CONTRACCCION Y CONSTRUCCION TRANSVERSALES), CURADO CON MEMBRANA QUIMICA APLICADA CON ASPERSOR, TRABAJO TERMINADO	M2	597.14	$437.67	$261,350.2(
80	CONSTRUCCION DE RAMPA Y BANQUETA DE USO HABITACIONAL PARA TRAFICO VEHICULAR, DE 12 CM DE ESPESOR A BASE DE CONCRETO PREMEZCLADO MR=38 KGF/CM2, T.M.A. 1 1/2", R.R 7 DIAS. GRAVA TRITURADA, REVENIMIENTI DE 10+-2 CM, ACABADO RAYADO FINO CON BROCHA DE PELO, JUNTAS FRIAS CON DOBLADOR DE 2" SECCION DE LOSAS COMO INDIQUE PROYECTO, INCLUYE: JUNTA DE AISLAMIENTO Y DE EXPANSION A BASE DE ESPUMA DE POLIETILENO DE CELDAS CERRADAS DE 1/2" EN JUNTAS FRIAS LONGITUDINALES CON MUROS Y TRANSVERSALES DEL ELEMENTO, ASI COMO SU UNION CON ELEMENTOS VIEJOS O CAMBIO DE ELEMENTO, CIMBRADO, COLADO, DESCIMBRADO, CORTES CON CORTADORA DE DISCO, SELLADO DE CORTES CON SELLADOR AUTONIVELANTE Y TIRA DE RELLENO PREFORMADA NO ADHERENTE DE 1/8" (EN TODAS LAS JUNTAS DE CONTRACCCION Y CONSTRUCCION TRANSVERSALES), CURADO CON MEMBRANA QUIMICA APLICADA CON ASPERSOR, TRABAJO TERMINADO FICHA TECNICA 216	M2	429.2 / 1026.34	$562.38	$241,373.5(

Obra: **PAVIMENTO HIDRÁULICO CALLE SANTA MÓNICA**

Ubicación: **TRAMO: ENTRE AV. EUGENIO GARZA SADA Y CALLE MARCOS CORONADO, LOS POCITOS Ej.**

Contratista: **ATECO, S.A. DE C.V. (102)**

No.	Concepto	Unidad	Cantidad	Precio Unitario	Importe Total
	GRUPO: **BANQUETAS, RAMPAS Y GUARNICIONES**				
	PARTIDA: **BANQUETAS Y RAMPAS**				
81	CONSTRUCCION DE CENEFA EN RAMPAS DE 30 CM DE ANCHO Y 10 CM DE ESPESOR A BASE DE CONCRETO PREMEZCLADO F'c= 150 KG/CM2, T.M.A. 3/4", GRAVA TRITURADA REVENIMIENTO DE 10 +- 2 CM, ACABADO ESTAMPADO SEGUN DISEÑO(VER PLANOS DE RAMPA TIPO) COLOR ROJO OSCURO CLAVE C-007, DESMONDANTE D-001, SELLADOR ACRILICO AL 25% SOLIDOS JUNTAS FRIAS ASERRADAS SECCION DE LOSAS COMO INDIQUE PROYECTO, INCLUYE: SUMINISTRO Y HECHURA DE TAPETE DE POLIURETANO SEGUN DISEÑO DE ESTAMPADO, CIMBRADO, COLADO, DESCIMBRADO Y CURADO CON MEMBRANA QUIMICA APLICADA CON ASPERSOR, TRABAJO TERMINADO SEGUN FICHA TECNICA FT-200.	M2	201.42	$984.06	$198,209.36
			Totales por Partida		**$827,059.42**
	PARTIDA: **GUARNICIONES DE CONCRETO**				
83	EXCAVACION A MAQUINA Y/O A MANO EN MATERIAL TIPO II, EN SECO O PRESENCIA DE AGUA, INCLUYE. CORTE DE RAIZ DE CUALQUIER TAMAÑO Y GROSOR, HASTA UNA PROFUNDIDAD DE 40 CM DESPUES DE DESMONTE, DESPALME Y/O DEMOLICION DE SUPERFICIE O ELEMENTO ESTRUCTURAL O DE ACABADO, PROTECCION DE AREAS ADYACENTES, SIN DAÑAR AREAS ALEDAÑAS, CARGA Y ACARREO A TIRADERO OFICIAL, CONSERVACION DE LA MISMA, TRABAJO TERMINADO, LIMPIEZAS.	M3	75.54	$103.68	$7,831.99
84	COMPACTACION POR MEDIOS MECANICOS DE TERRENO NATURAL AL 90% DE SU PVSM EN UN ESPESOR DE 20 CM , INCLUYE: ESCARIFICADO, MANIOBRAS, HUMEDECIDO, SELECCION DE MATERIAL, ACARREOS DENTRO DE LA OBRA, MEDIDO COMPACTO, LIMPIEZAS Y TODO LO NECESARIO PARA SU CORRECTA APLICACION, TRABAJO TERMINADO.	M2	402.58	$30.31	$12,202.20
85	CONSTRUCCION DE GUARNICION RECTA Y/O CURVA TRAPEZOIDAL 15-20X40 CM DE SECCION CON CONCRETO PREMEZCLADO MR=38 KGF/CM2, R.N.REVENIMIENTO DE 8 A 10 CM, T.M.A. 3/4", GRAVA TRITURADA, ACABADO PULIDO EN PARTE DE SUPERIOR Y DOBLADOR EN ARISTAS, INCLUYE: COMPACTADO DE PLANTILLA, CIMBRADO, COLADO, VIBRADO, ACABADO, DESCIMBRADO, ALINEADO, NIVELADO, Y CURADO EN SU PARTE SUPERIOR CON MEMBRANA BASE AGUA A RAZON DE 1 LTO/M2, JUNTA DE AISLAMIENTO LONGITUDINAL AL COMBINAR CON OTRO ELEMENTO Y TRANSVERSAL @ 30 MT MAXIMO, SELLADO CON SELLADOR AUTONIVELANTE LONGITUDINAL, TRABAJO TERMINADO, .P.U.O.T.	ML	670.96	$422.09	$283,205.51
			Totales por Partida		**$303,239.69**
			Totales por Grupo		**$1,130,299.11**

Obra: **PAVIMENTO HIDRÁULICO CALLE SANTA MÓNICA**

Ubicación: **TRAMO: ENTRE AV. EUGENIO GARZA SADA Y CALLE MARCOS CORONADO, LOS POCITOS Ej.**

Contratista: **ATECO, S.A. DE C.V. (102)**

No.	Concepto	Unidad	Cantidad	Precio Unitario	Importe Total
GRUPO: **LIMPIEZAS**					
PARTIDA: **LIMPIEZAS**					
89	LIMPIEZA GENERAL DE LA OBRA, INCLUYE: ACARREOS DE ESCOMBROS, RETIRO FUERA DE LA OBRA DEL MISMO.	M2	2820	$7.43	$20,952.60
			Totales por Partida		**$20,952.60**
			Totales por Grupo		**$20,952.60**

Obra: **PAVIMENTO HIDRÁULICO CALLE SANTA MÓNICA**

Ubicación: **TRAMO: ENTRE AV. EUGENIO GARZA SADA Y CALLE MARCOS CORONADO, LOS POCITOS Ej.**

Contratista: **ATECO, S.A. DE C.V. (102)**

No.	Concepto	Unidad	Cantidad	Precio Unitario	Importe Total
	GRUPO: **SEÑALIZACION**				
	PARTIDA: **SEÑALAMIENTO HORIZONTAL**				
90	SUMINISTRO Y APLICACIÓN DE PINTURA BASE SOLVENTE " EN RAYA DE ALTO CLASIFICACIÓN M - 6, PARA INDICAR ALTO EN CRUCEROS, COLOR BLANCO, REFLEJANTE CON MICRO ESFERA DE VIDRIO EN PROPORCIÓN SEGÚN NORMA SCT DE 0.60 MTS DE ANCHO DE LONGITUD VARIABLE, INCLUYE: MATERIALES Y ESPECIFICACIONES QUE CUMPLAN CON LA NORMATIVA N-CMT-5-01-001/05, N-PRY-CAR-10-01-002/13 APLICADAS AL DIA DE HOY, MATERIAL, TRAZO, ENMASCARILLADO, MANO DE OBRA, LIMPIEZA PREVIA DE SUPERFICIE, EQUIPO NECESARIO PARA SU EJECUCIÓN, Y TODO LO NECESARIO PARA SU CORRECTA EJECUCIÓN, TRABAJO TERMINADO.	ML	9.7	$123.15	$1,194.56
91	SUMINISTRO Y APLICACIÓN DE PINTURA BASE SOLVENTE PARA INDICAR "CRUCE PEATONAL EN CAJON DE ESTACIONAMIENTO PARA PERSONAS CON DISCAPACIDAD" COLOR AZUL PANTONE 294 DE 0.40 MTS DE ANCHO Y LONGITUD VARIABLE, CON UNA SEPARACION DE 0.40 MTS. ENTRE ELLAS, SECADO AL TACTO EN 5 MIN Y AL DURO EN 30 MIN. INCLUYE: MATERIAL, Y ESPECIFICACIONES QUE CUMPLAN CON LA NORMATIVA N-CMT-5-01-001/05,N-PRY-CAR-10-01-002/13 APLICADAS AL DIA DE HOY MANO DE OBRA, TRAZO, ENMASCARILLADO, LIMPIEZAS PREVIAS Y POSTERIORES DE LA SUPERFICIE, Y TODO LO NECESARIO PARA SU CORRECTA EJECUCION, TRABAJO TERMINADO.	M2	28	$307.86	$8,620.08
92	SUMINISTRO Y APLICACIÓN DE PINTURA BASE SOLVENTE " EN FLECHAS CLASIFICACIÓN M - 11.1, "FLECHA SENCILLA" PARA INDICAR SENTIDO DE CIRCULACIÓN , EN VIALIDADES PARA VELOCIDAD MENOR A 60KM POR HORA DIFERENTES DIMENSIONES (VER PLANO DE SEÑALAMIENTOS) COLOR BLANCO, REFLEJANTE CON MICRO ESFERA DE VIDRIO EN PROPORCIÓN SEGÚN NORMA SCT, INCLUYE: MATERIALES Y ESPECIFICACIONES QUE CUMPLAN CON LA NORMATIVA N-CMT-5-01-001/05, N-PRY-CAR-10-01-002/13 APLICADAS AL DIA DE HOY, MATERIAL, TRAZO, ENMASCARILLADO, MANO DE OBRA, LIMPIEZA PREVIA DE SUPERFICIE, EQUIPO NECESARIO PARA SU EJECUCIÓN, Y TODO LO NECESARIO PARA SU CORRECTA EJECUCIÓN, TRABAJO TERMINADO.	PZA	2	$431.03	$862.06
93	SUMINISTRO Y COLOCACION DE VIALETA STANDARD (S-200) DE 10X10CM. COLOR: CUERPO AMARILLO Y REFLEJANTE AMARILLO 1 CARA MARCA SEA O SIMILAR EN CALIDAD Y ESPECIFICACIONES DE FICHA TECNICA, ANCLADO EN PAVIMENTO SISTEMA DE SUJECION DE ALTO AGARRE BASE CUÑAS CON AB PEGAMENTO EPOXICO 50/50 RESISTENTE A ALTA TEMPERATURA (VER PLANO DE DETALLES DE SEÑALAMIENTOS HORIZONTAL Y VERTICAL). INCLUYE: TRAZO, ALINEACION, ELEVACION CUALQUIER ALTURA, TRABAJO TERMINADO, LIMPIEZAS.	PZA	69	$73.89	$5,098.41
94	SUMINISTRO Y APLICACIÓN DE LOGOTIPO A (SILLA DE RUEDAS) EN PINTURA EPOXICA BASE SOLVENTE COLOR BLANCO EN RAMPAS PARA PERSONAS CON DISCAPACIDAD TAMAÑO Y DISEÑO SEGÚN PLANOS. INCLUYE: TRAZO, ENMASCARILLADO, PLANTILLA, MANO DE OBRA, LIMPIEZA PREVIA DE SUPERFICIE, EQUIPO NECESARIO PARA SU EJECUCIÓN, Y TODO LO NECESARIO PARA SU CORRECTA EJECUCIÓN, TRABAJO TERMINADO.	PZA	4	$677.25	$2,709.00
95	SUMINISTRO Y APLICACIÓN DE PINTURA EPOXICA BASE SOLVENTE COLOR AZUL (PANTONE 294) EN RAMPAS PARA PERSONAS CON DISCAPACIDAD CUALQUIER SECCIÓN SEGÚN PLANOS. INCLUYE: TRAZO, MANO DE OBRA, LIMPIEZA PREVIA DE SUPERFICIE, EQUIPO NECESARIO PARA SU EJECUCIÓN, Y TODO LO NECESARIO PARA SU CORRECTA EJECUCIÓN, TRABAJO TERMINADO.	M2	5.76	$554.15	$3,191.90

Obra: **PAVIMENTO HIDRÁULICO CALLE SANTA MÓNICA**

Ubicación: **TRAMO: ENTRE AV. EUGENIO GARZA SADA Y CALLE MARCOS CORONADO, LOS POCITOS Ej.**

Contratista: **ATECO, S.A. DE C.V. (102)**

No.	Concepto	Unidad	Cantidad	Precio Unitario	Importe Total
	GRUPO: **SEÑALIZACION**				
	PARTIDA: **SEÑALAMIENTO HORIZONTAL**				
96	SUMINISTRO Y APLICACIÓN DE PINTURA BASE SOLVENTE " EN RAYA SEPARADORA CLASIFICACIÓN M -1.6, CONTINUA DOBLE, PARA DELIMITAR CARRIL EXCLUSIVO DE FRENTE EN PISO, 0.10 MTS DE ANCHO, CON UNA SEPARACIÓN IGUAL AL ANCHO DE LA LINEA A BASE DE PINTURA PARA TRAFICO COLOR AMARILLO CON MICRO ESFERA SEGÚN NORMA SCT, INCLUYE: MATERIALES Y ESPECIFICACIONES QUE CUMPLAN CON LA NORMATIVA N-CMT-5-01-001/05, N-PRY-CAR-10-01-002/13 APLICADAS AL DIA DE HOY, MATERIAL, TRAZO, ENMASCARILLADO, MANO DE OBRA, LIMPIEZA PREVIA DE SUPERFICIE, EQUIPO NECESARIO PARA SU EJECUCIÓN, Y TODO LO NECESARIO PARA SU CORRECTA EJECUCIÓN, TRABAJO TERMINADO.	ML	170	$61.58	$10,468.60
97	SUMINISTRO Y APLICACIÓN DE PINTURA BASE SOLVENTE PARA MARCAS EN GUARNICIONES CLASIFICACION M-12.1, M12.2 APLICADA SOBRE GUARNICIONES Y DENTELLONES DE CUALQUIER COLOR, SEGÚN SE REQUIERA Y SEGÚN NORMA S.C.T. SECADO AL TACTO EN 5 MIN Y AL DURO EN 30 MIN CON MICRO ESFERA , DESARROLLO DE 35 CM. INCLUYE: MATERIALES Y ESPECIFICACIONES QUE CUMPLAN CON LA NORMATIVA N-CMT-5-01-001/05, N-PRY-CAR-10-01-002/13 APLICADAS AL DIA DE HOY, TRAZO, MANO DE OBRA, LIMPIEZA PREVIA DE SUPERFICIE, EQUIPO NECESARIO PARA SU EJECUCIÓN, Y TODO LO NECESARIO PARA SU CORRECTA EJECUCIÓN, TRABAJO TERMINADO.	ML	375	$55.42	$20,782.50
98	SUMINISTRO Y APLICACIÓN DE PINTURA EPOXICA COLOR AZUL YBLANCO PARA LOGO EN RAMPAS PARA DISCAPACITADOS, SECCION 0.75 X 0.65 MTS. SEGÚN PLANOS. INCLUYE: TRAZO, PREPARACION DE LA SUPERFICIE, PROTECCION DE AREAS ADYACENTES, LIMPIEZAS.	PZA	2	$615.63	$1,231.26
99	SUMINISTRO Y APLICACIÓN DE LOGOTIPO A (SILLA DE RUEDAS) EN PINTURA EPOXICA BASE SOLVENTE COLOR BLANCO EN RAMPAS PARA PERSONAS CON DISCAPACIDAD TAMAÑO Y DISEÑO SEGÚN PLANOS. INCLUYE: TRAZO, ENMASCARILLADO, PLANTILLA, MANO DE OBRA, LIMPIEZA PREVIA DE SUPERFICIE, EQUIPO NECESARIO PARA SU EJECUCIÓN, Y TODO LO NECESARIO PARA SU CORRECTA EJECUCIÓN, TRABAJO TERMINADO.	PZA	2	$677.25	$1,354.50
100	SUMINISTRO Y COLOCACION DE BOYA DE PLASTICO OJO DE GATO (VT-38), MARCA CREATIVAL O SIMILAR EN CALIDAD Y PRECIO, CON REFLEJANTE COLOR BLANCO, GRADO ALTA INTENSIDAD, FIJACION A SUPERFICIE CON CLAVOS DE ACERO ALTA RESISTENCIA, INCLUYE: MATERIAL, MANO DE OBRA, HERRAMIENTA, ELEMENTOS DE FIJACION, ALINEADO, LIMPIEZAS Y TODO LO NECESARIO PARA SU CORRECTA EJEUCION, TRABAJO TERMINADO.	PZA	70	$307.89	$21,552.30
				Totales por Partida	**$77,065.17**

Obra: **PAVIMENTO HIDRÁULICO CALLE SANTA MÓNICA**

Ubicación: **TRAMO: ENTRE AV. EUGENIO GARZA SADA Y CALLE MARCOS CORONADO, LOS POCITOS Ej.**

Contratista: **ATECO, S.A. DE C.V. (102)**

No.	Concepto	Unidad	Cantidad	Precio Unitario	Importe Total
	GRUPO: **SEÑALIZACION**				
	PARTIDA: **SEÑALAMIENTO VERTICAL**				
101	SUMINISTRO Y COLOCACION DE SEÑALAMIENTO VERTICAL DE RESTRICCION SR-9 (VELOCIDAD MAXIMA), DISEÑO NORMATIVO SCT, HECHO A ABASE DE LAMINA GALVANIZADA CON CEJA DE 72 X 72 CM CALIBRE 16, CON TERMINADO GRADO INGENIERIA EN SU TOTALIDAD, EL COLOR SERA REFLEJANTE GRADO INGENIERIA Y SIMBOLOS EN COLOR REFLEJANTE, TODOS LOS COLORES RESISTENTES A LA INTEMPERIE, FIJADA MEDIANTE BARRENADO Y TORNILLOS DE 2 1/2" X 5/16" A UN POSTE DE PTR DE 2 X 2" CALIBRE 14 EN ACABADO GALVANIZADO Y CON UNA ALTURA DE 2.5 MTS AL NIVEL DE BANQUETA A LA PARTE INFERIOR DE LA LAMINA MAS EL EXCEDENTE REQUERIDO PARA FIJAR LAS LAMINAS Y ANCLADO DE 50 CM DE PROFUNDIDAD CON ANGULO TRANSVERSAL DE 1 X 1" DE 25 CM, EN DADO DE CONCRETO F'c=150 KG/CM2 DE 30 CM DE LADO (VER PLANO DE DETALLES CRITERIOS DE ANCLAJE DE SEÑALAMIENTO VERTICAL, DETALLE SEÑ-02 Y SEÑ 03), MCA ASEA O SIMILAR EN CALIDAD Y ESPECIFICACIONES, INCLUYE: MANO DE OBRA, FLETES, MANIOBRAS LIMPIEZAS Y RETIRO DEL SOBRANTE FUERA DE LA OBRA HASTA TIRADERO OFICIAL, TRABAJO TERMINADO.	PZA	1	$3,859.23	$3,859.2

Totales por Partida		**$3,859.2**
Totales por Grupo		**$80,924.4**
Totales Presup.		**$3,829,532.6**
Anticipo	+	**$1,148,859.7**
Amortizac. Ant.	-	**$1,148,859.7**
SubTotal. Ant.	=	**$3,829,532.6**
IVA	+	**$612,725.2**
Total	=	**$4,442,257.8**

H. AYUNTAMIENTO CONSTITUCIONAL DEL MUNICIPIO DE AGUASCALIENTES 2021-2024

PRESUPUESTO MODIFICADO

Aguascalientes

Obra: **PAVIMENTO HIDRÁULICO CALLE SANTA MÓNICA**

Ubicación: **TRAMO: ENTRE AV. EUGENIO GARZA SADA Y CALLE MARCOS CORONADO, LOS POCITOS Ej.**

Contratista: **ATECO, S.A. DE C.V. (102)**

Grupo	Partida	Importe
PRELIMINARES		
	DEMOLICIONES Y DESMONTAJES	$4,168.25
	Subtotal por Grupo	**$4,168.25**
PAVIMENTO HIDRAULICO		
	PRELIMINARES	$30,121.76
	EXCAVACIONES, ACARREOS Y TERRACERIAS	$822,266.91
	PAVIMENTO HIDRAULICO	$993,639.59
	OBRA COMPLEMENTARIA	$68,216.72
	Subtotal por Grupo	**$1,914,244.98**
ALCANTARILLADO		
	RED DE ALCANTARILLADO	$289,489.64
	DESCARGAS DOMICILIARIAS	$229,644.66
	Subtotal por Grupo	**$519,134.30**
AGUA POTABLE		
	RE DE AGUA POTABLE	$91,181.82
	TOMAS DOMICILIARIAS	$68,627.18
	Subtotal por Grupo	**$159,809.00**
BANQUETAS, RAMPAS Y GUARNICIONES		
	BANQUETAS Y RAMPAS	$827,059.42
	GUARNICIONES DE CONCRETO	$303,239.69
	Subtotal por Grupo	**$1,130,299.11**
LIMPIEZAS		
	LIMPIEZAS	$20,952.60
	Subtotal por Grupo	**$20,952.60**
SEÑALIZACION		
	SEÑALAMIENTO HORIZONTAL	$77,065.17
	SEÑALAMIENTO VERTICAL	$3,859.23
	Subtotal por Grupo	**$80,924.40**

Totales Presup.		**$3,829,532.64**
Anticipo	**+**	**$1,148,859.79**
Amortizac. Ant.	**-**	**$1,148,859.79**
SubTotal. Ant.	**=**	**$3,829,532.64**
IVA	**+**	**$612,725.23**
Total	**=**	**$4,442,257.87**

H. AYUNTAMIENTO CONSTITUCIONAL DEL MUNICIPIO DE AGUASCALIENTES 2021-2024

H. AYUNTAMIENTO DE AGUASCALIENTES

SECRETARÍA DE OBRAS PÚBLICAS


DIRECCIÓN DE SUPERVISIÓN DE OBRA


Aguascalientes
LA CIUDAD DE TU VIDA

MEMORIA FOTOGRAFICA


OBRA:	PAVIMENTO HIDRÁULICO CALLE SANTA MÓNICA, TRAMO: ENTRE AV. EUGENIO GARZA SADA Y CALLE MARCOS CORONADO, LOS POCITOS Ej.					
NO. DE CONTRATO:	FISMDF-0067-2022		CONTRATISTA:	ATECO, S.A. DE C.V.		

INICIO.

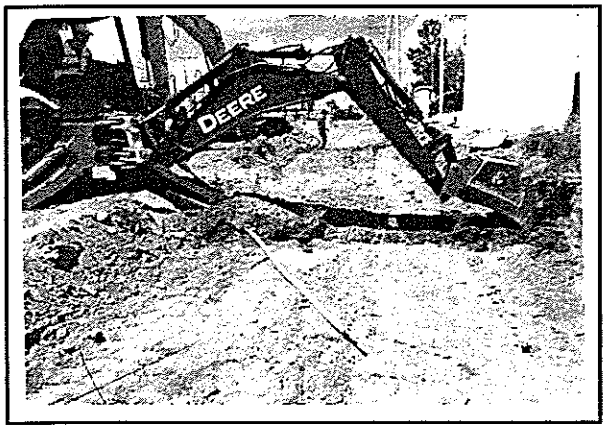

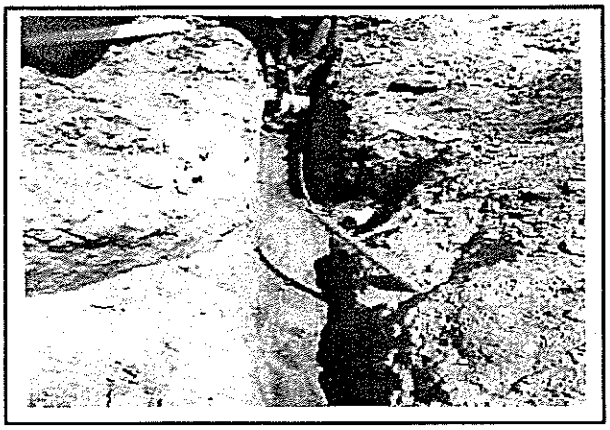



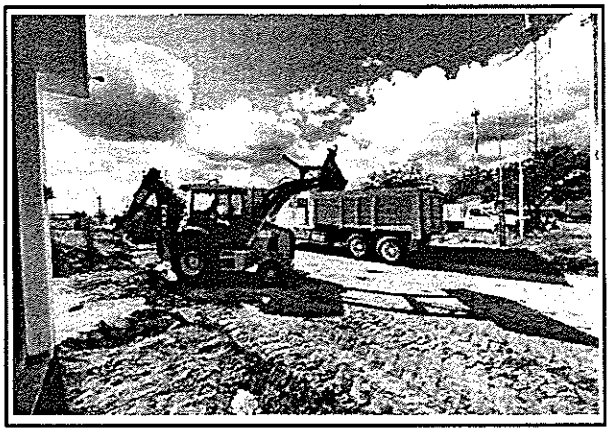

ING. IVAN ALEJANDRO RUIZ ESPARZA SOLIS
SUPERVISOR DE OBRA.

H. AYUNTAMIENTO CONSTITUCIONAL DEL MUNICIPIO DE AGUASCALIENTES 2021-2024


H. AYUNTAMIENTO DE AGUASCALIENTES
SECRETARÍA DE OBRAS PÚBLICAS
DIRECCIÓN DE SUPERVISIÓN DE OBRA


Aguascalientes
LA CIUDAD DE TU VIDA

MEMORIA FOTOGRAFICA

OBRA:	PAVIMENTO HIDRÁULICO CALLE SANTA MÓNICA, TRAMO: ENTRE AV. EUGENIO GARZA SADA Y CALLE MARCOS CORONADO, LOS POCITOS EJ.					
NO. DE CONTRATO:	FISMDF-0067-2022		CONTRATISTA:	ATECO, S.A. DE C.V.		

PROCESO

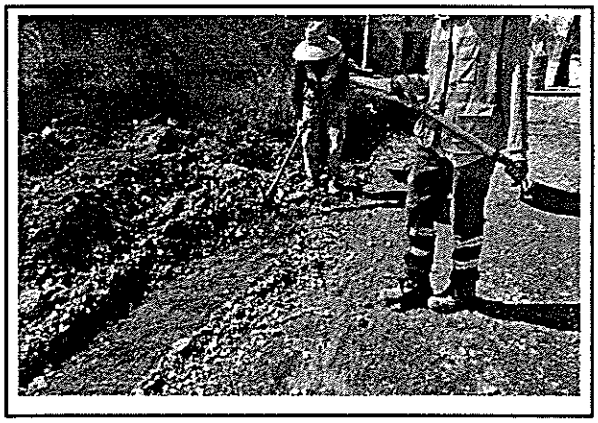

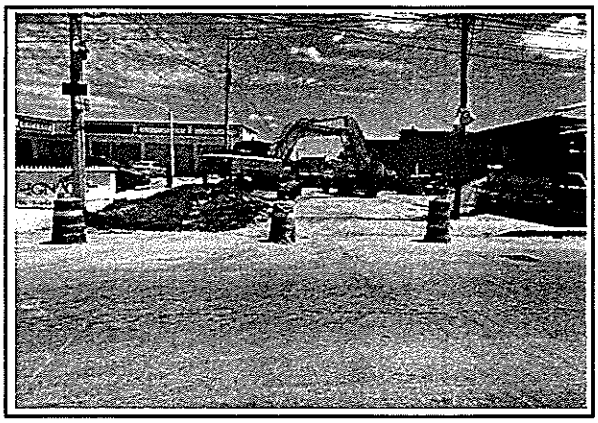





ING. IVAN ALEJANDRO RUIZ ESPARZA SOLIS
SUPERVISOR DE OBRA.

H. AYUNTAMIENTO CONSTITUCIONAL DEL MUNICIPIO DE AGUASCALIENTES 2021-2024


H. AYUNTAMIENTO DE AGUASCALIENTES
SECRETARÍA DE OBRAS PÚBLICAS
DIRECCIÓN DE SUPERVISIÓN DE OBRA


Aguascalientes
LA CIUDAD DE TU VIDA


MEMORIA FOTOGRAFICA


OBRA:	PAVIMENTO HIDRÁULICO CALLE SANTA MÓNICA, TRAMO: ENTRE AV. EUGENIO GARZA SADA Y CALLE MARCOS CORONADO, LOS POCITOS EJ.					
NO. DE CONTRATO:	FISMDF-0067-2022		CONTRATISTA:	ATECO, S.A. DE C.V.		

TERMINO

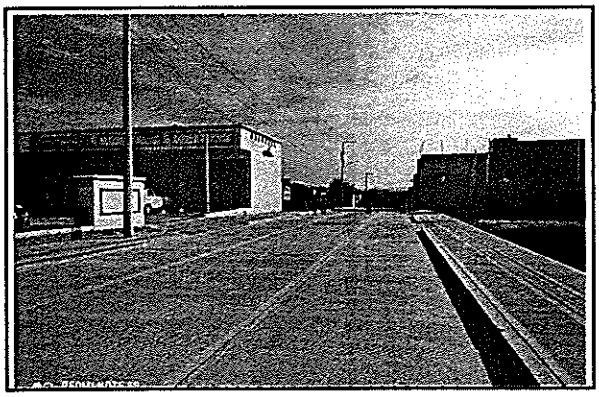

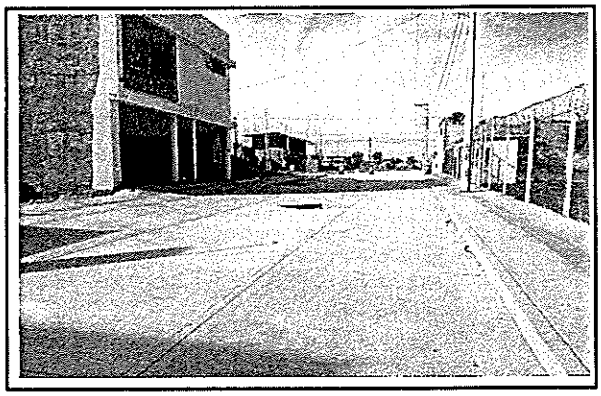

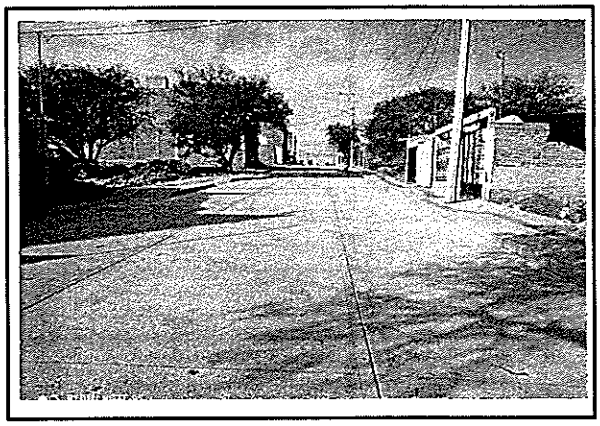

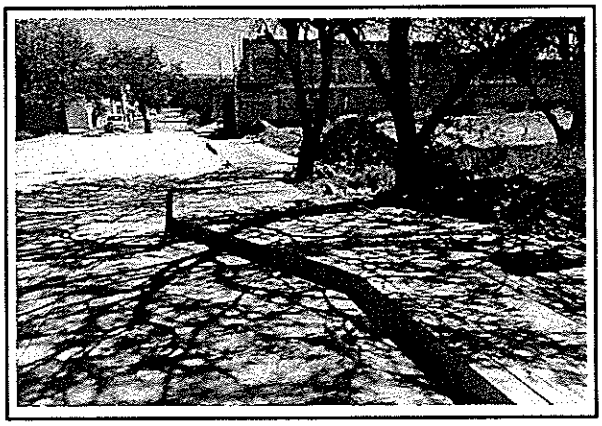

ING. IVAN ALEJANDRO RUIZ ESPARZA SOLIS
SUPERVISOR DE OBRA.

MODIFICADO

SECRETARÍA DE OBRAS PÚBLICAS

DIRECCIÓN DE SUPERVISIÓN DE OBRA

EJERCICIO 2022


N° DE CONTRATO: FISMDF-0067-2022


NOMBRE DE LA OBRA: PAVIMENTO HIDRÁULICO CALLE SANTA MÓNICA, TRAMO: ENTRE AV. EUGENIO GARZA SADA Y CALLE MARCOS CORONADO, LOS POCITOS Ej.

MONTO MODIFICADO FINAL: $ 4,442,257.87

VOLUMEN	UNIDAD	COMPONENTE DE LA OBRA	MONTO
2820.00	M2	LIMPIA, TRAZO Y NIVELACION EN PAVIMENTOS, CALLES Y VIALIDADES CON EQUIPO TOPOGRAFICO, INCLUYE: EJES, BANCO DE NIVEL, RENIVELACIONES LAS VECES NECESARIAS, CORRECCION DE RASANTE A PUNTOS OBLIGADOS (AUTORIZADOS POR LA SUPERVISION), ESTACAS, VARILLAS, MANO DE OBRA CALIFICADA,	$ 4,168.25
1666.37	M2	CONSTRUCCION DE PAVIMENTO HIDRAULICO A BASE DE CONCRETO PREMEZCLADO MR=38 KG/CM2 TMA 1 1/2" GRAVA TRITURADA, REVENIMIENTO DE 6 A 8 CM FRAGUADO NORMAL DE 15 CM DE ESPESOR MODULADO EN LOSAS DE 3.5 MTS. (ANCHO) X 3.5 MTS (LARGO) COMO MAXIMO, CON CORTES EN LAS LOSAS DE 1/3 DEL	$ 1,914,244.98
333.00	ML	SUMINISTRO DE TUBERIA DE PVC PARA ALCANTARILLADO SERIE 20 DE 10", CON JUNTA HERMETICA, INCLUYE: FLETES Y ACARREO HASTA EL SITIO DE SU COLOCACION, ALINEADO, MATERIAL, CUBIERTA DE PROTECCION, ESTIBADO, MANO DE OBRA.	$ 519,134.30
62.00	PZA	CONSTRUCCION DE TOMA DOMICILIARIA DE 6 A 9 M DE LONGITUD (NOMINAL) A BASE DE TUBO KITEC DE 1/2" AZUL, CONECTORES PHILMAC MACHO Y HEMBRA, ABRAZADERAS SIN FIN, CONECTOR A TUBO GALVANIZADO, ABRAZADERA DE PVC DE 3" X 1/2", TAPON HEMBRA. INCLUYE: ENCAMISADO CON POLIDUCTO ELECTRICO DE 1	$ 159,809.00
670.96	ML	CONSTRUCCION DE GUARNICION RECTA Y/O CURVA TRAPEZOIDAL 15-20X40 CM DE SECCION CON CONCRETO PREMEZCLADO MR=38 KGF/CM2, R.N.REVENIMIENTO DE 8 A 10 CM, T.M.A. 3/4", GRAVA TRITURADA, ACABADO PULIDO EN PARTE DE SUPERIOR Y DOBLADOR EN ARISTAS, INCLUYE: COMPACTADO DE PLANTILLA, CIMBRADO,	$ 1,130,299.11
2820.00	M2	LIMPIEZA GENERAL DE LA OBRA, INCLUYE: ACARREOS DE ESCOMBROS, RETIRO FUERA DE LA OBRA DEL MISMO.	$ 20,952.60
70.00	PZA	SUMINISTRO Y COLOCACION DE BOYA DE PLASTICO OJO DE GATO (VT-38), MARCA CREATIVAL O SIMILAR EN CALIDAD Y PRECIO, CON REFLEJANTE COLOR BLANCO, GRADO ALTA INTENSIDAD, FIJACION A SUPERFICIE CON CLAVOS DE ACERO ALTA RESISTENCIA, INCLUYE: MATERIAL, MANO DE OBRA, HERRAMIENTA, ELEMENTOS DE	$ 80,924.40
		TOTAL PRESUP.	$ 3,829,532.64
		IVA	$ 612,725.23
		TOTAL	$ 4,442,257.87

NOMBRE DEL SUPERVISOR: ING. IVAN ALEJANDRO RUIZ ESPARZA SOLIS

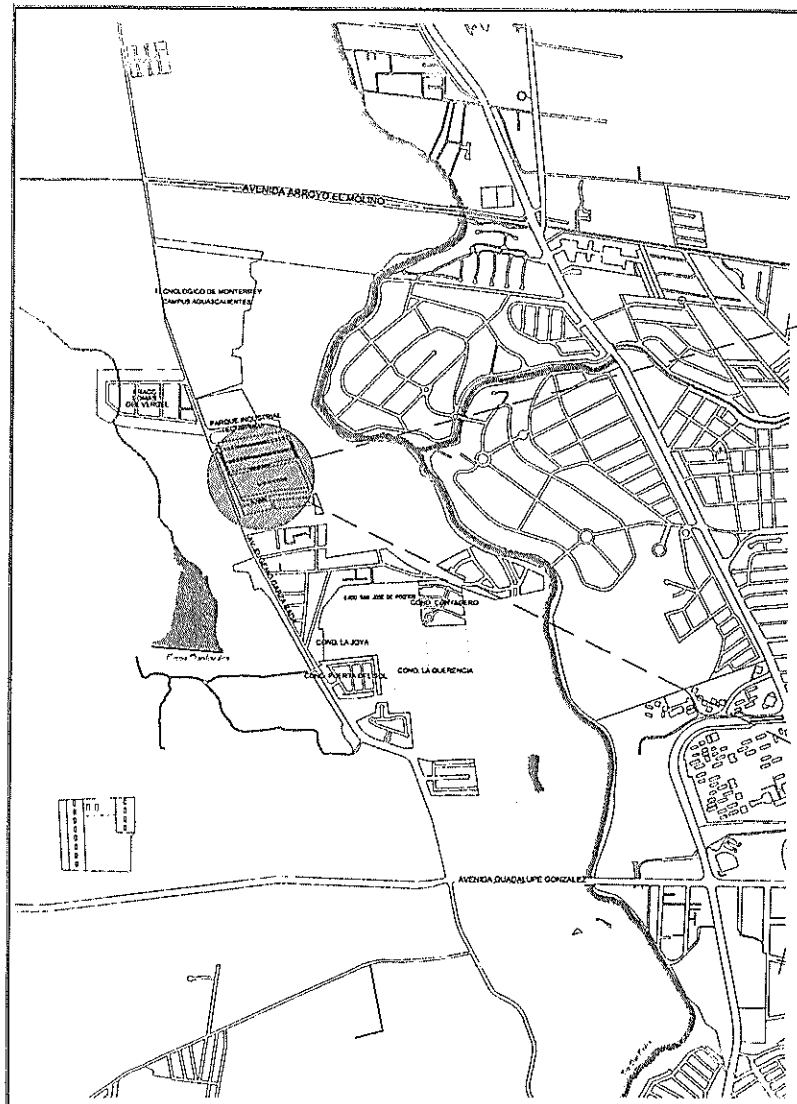


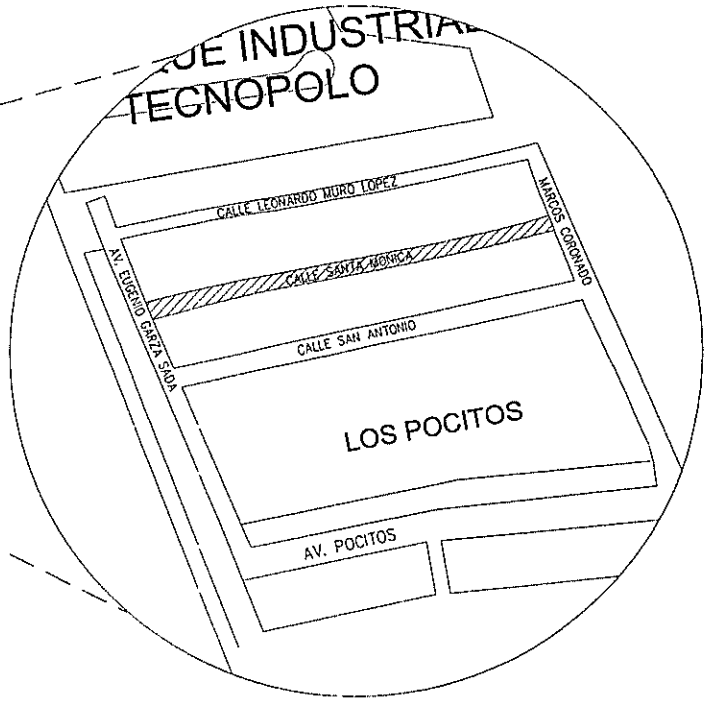

CROQUIS DE LOCALIZACIÓN

SIN ESCALA — CALLE SANTA MONICA

LOCALIZACIÓN:

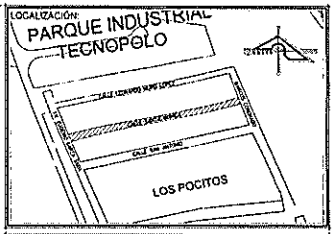

SIMBOLOGÍA

La Dirección de Planeación y Proyectos solo autoriza el proyecto ejecutivo, no es responsable de la correcta ejecución de la obra. Este documento no tiene validez si no presenta las firmas de los responsables para su autorización, así como los sellos respectivos.

PRESIDENTE MUNICIPAL
M.P.P. Leonardo Montañez Castro
SECRETARIO DE OBRAS PÚBLICAS DEL MUNICIPIO DE AGUASCALIENTES
Ing. Miguel Ángel Hulzar Botello

REV	FECHA	OBSERVACIONES

Vo. Bo. OFICIA DEPENDENCIA

RESP. DE PROY. EXTERNO		LOGO EXTERNO
CED. PROFESIONAL		
PROYECTÓ	REVISÓ	AUTORIZÓ


Dirección de Planeación y Proyectos de Obra — Secretaría de Obras Públicas

PROYECTISTA	COORDINADOR
ING. DIEGO RICMO AGUILERA	ARQ. ALEJANDRO JAIME LEAL
JEFE DE DEP.	DIRECTOR
ARQ. J. JESÚS ESPARZA GONZÁLEZ	M. en ARQ. JOSÉ LUIS JIMÉNEZ GARCÍA

PROYECTO: CONSTRUCCIÓN DE CONCRETO HIDRAULICO CALLE SANTA MONICA (COL. LOS POCITOS)
UBICACIÓN: COLONIA LOS POCITOS
TRAMO ENTRE AV. EUGENIO GARZA SADA Y MARCOS CORONADO
CONTENIDO: CROQUIS DE LOCALIZACIÓN


CLAVE	No. PLANO
LOC 01	01
FECHA: MAYO 2022	ESCALA: INDICADA
ACOTACIÓN: METROS	No. EXP: E-000-22

Aguascalientes
LA CIUDAD DE TU VIDA

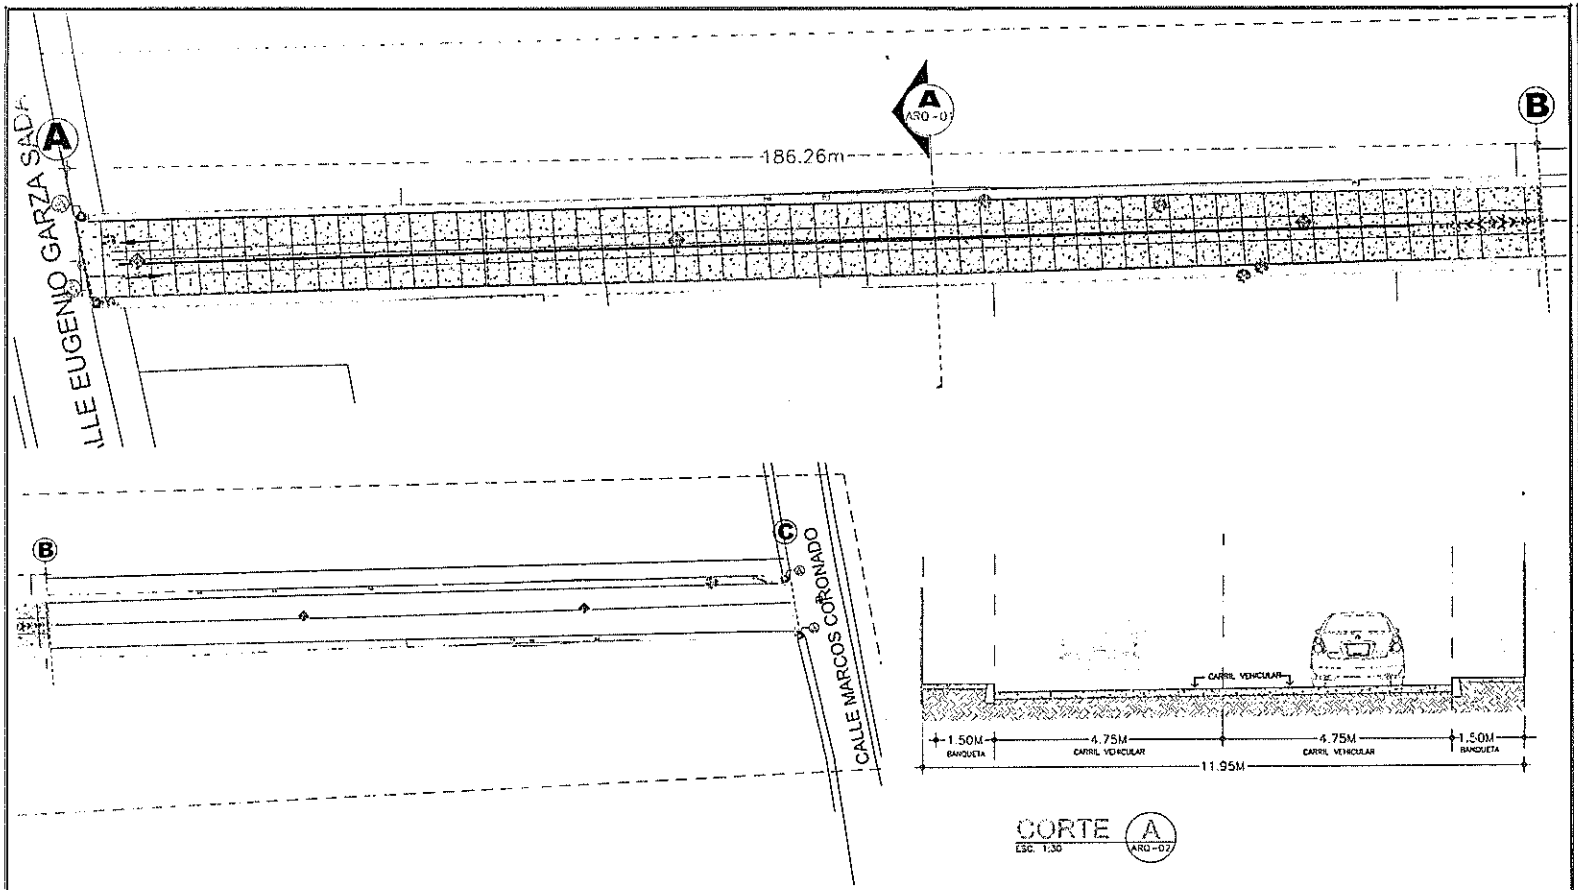

PROYECTO GEOMÉTRICO

ESCALA 1:750 CALLE SANTA MONICA

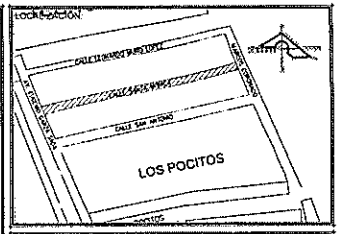

SIMBOLOGÍA

SIMBOLOGIA

1,685.83 M2

La Dirección de Planeación y Proyectos solo autoriza el proyecto ejecutivo, no es responsable de la correcta ejecución de la obra. Este documento no tiene validez si no presenta las firmas de los responsables para su autorización, así como los sellos respectivos.

PRESIDENTE MUNICIPAL
M.P.P. Leonardo Montañez Castro
SECRETARIO DE OBRAS PÚBLICAS DEL MUNICIPIO DE AGUASCALIENTES
Ing. Miguel Ángel Hulzar Botello

REV	FECHA	OBSERVACIONES

Vo. Bo. DE LA DEPENDENCIA

RESP. DE PROY. EXTERNO		LOGO EXTERNO
CED. PROFESIONAL		
PROYECTÓ	REVISÓ	AUTORIZÓ


Dirección de Planeación y Proyectos de Obra — Secretaría de Obras Públicas


PROYECTISTA	COORDINADOR
ING. DIEGO ROMO AGUILERA	ARQ. ALEJANDRO JAIME LEAL
JEFE DE DEP.	DIRECTOR
ARQ. J. JESÚS PALAFOX GONZÁLEZ	M. en ARQ. JOSÉ LUIS JIMÉNEZ GARCÍA

PROYECTO: CONSTRUCCIÓN DE CONCRETO HIDRAULICO CALLE SANTA MONICA (COL. LOS POCITOS)
UBICACIÓN: COLONIA LOS POCITOS TRAMO ENTRE AV. EUGENIO GARZA SADA Y MARCOS CORONADO
CONTENIDO: PROYECTO GEOMETRICO

CLAVE	No. PLANO
PG 01	04
FECHA: MAYO 2022	ESCALA: INDICADA
ACOTACIÓN: METROS	No. EXP.: E-000-22

Aguascalientes
LA CIUDAD DE TU VIDA

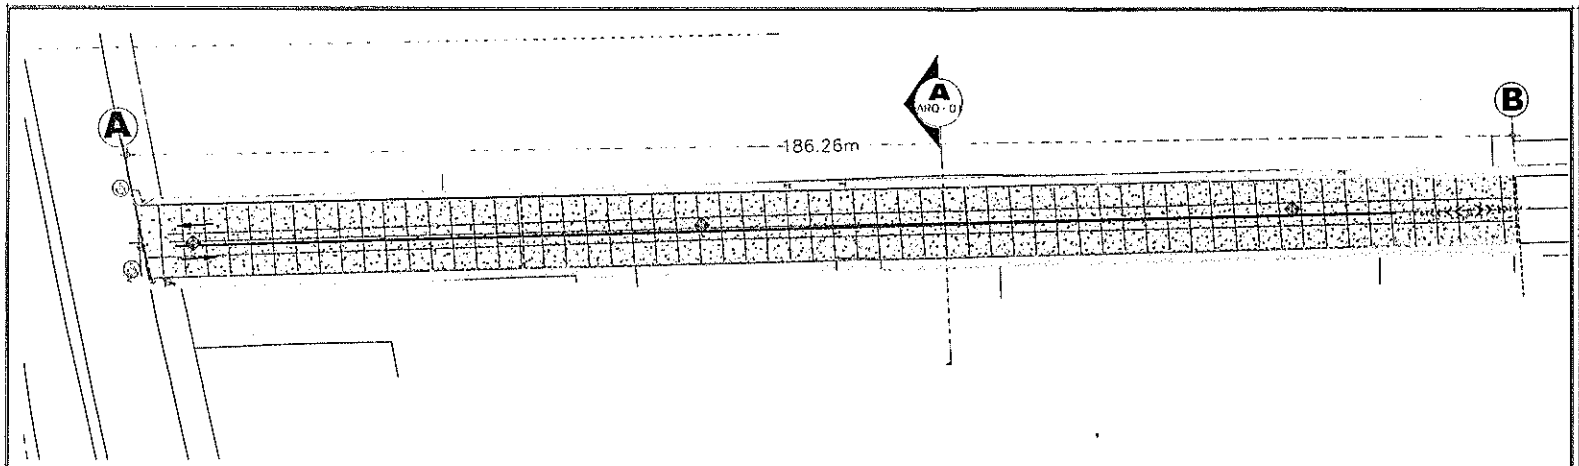

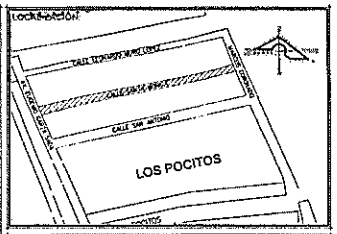


SIMBOLOGÍA

1,685.83 M2

CONSTRUCCION DE PAVIMENTO HIDRAULICO A BASE DE CONCRETO PREMEZCLADO MR=38 KG/CM2 TMA 1 1/2" GRAVA TRITURADA, REVENIMIENTO DE 6 A 8 CM FRAGUADO NORMAL DE 15 CM DE ESPESOR MODULADO EN LOSAS DE 3.5 MTS (ANCHO) X 3.5 MTS (LARGO) COMO MAXIMO, CON CORTES EN LAS LOSAS DE 1/3 DEL ESPESOR DE LA LOSA (5 CM) Y SELLADO CON COLA DE RATA Y MATERIAL ELASTOMERICO Y TIRA PREFORMADA (FOAMTECH DE 1/2X15) EN JUNTAS Y CORTES LONGITUDINALES Y TRANSVERSALES, ASI COMO EL APROCHE CON GUARNICION Y DENTELLON. INCLUYE: CIMBRADO, COLADO, VIBRADO CON INMERSION Y REGLA VIBRATORIA, DESCIMBRADO, REGLEADO FINAL, ACABADO CEPILLO DE ALUMINIO Y CON DOBLADOR, CALAFATEO, CURADO CON MEMBRANA BASE AGUA Y TODO LO NECESARIO PARA SU CORRECTA COLOCACION. P.U.O.


CONSTRUCCION DE GUARNICION TRAPEZOIDAL DE 15x20x40 CM DE SECCION CON CONCRETO SIMPLE MR=38KGF/CM2 , REVENIMIENTO DE 10 +- 2.5 CM, T.M.A. 3/4" (19MM), GRAVA TRITURADA, ACABADO PULIDO EN PARTE DE SUPERIOR Y DOBLADOR EN ARISTAS SUPERIORES, INCLUYE: COMPACTADO DE PLANTILLA, CIMBRADO, COLADO, ACABADO, DESCIMBRADO, ALINEADO, NIVELADO, DESCIMBRADO Y CURADO EN SU PARTE SUPERIOR CON MEMBRANA BASE AGUA A RAZON DE 1 LTO/M2 SEGUN FICHA TECNICA 204

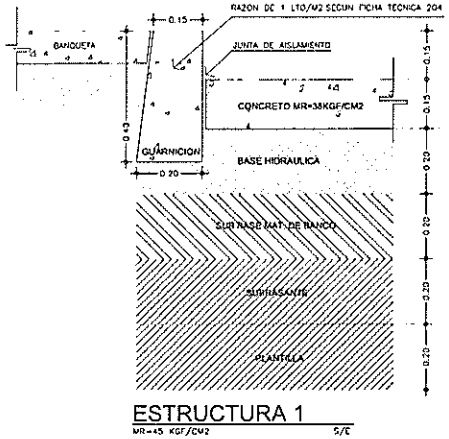

ESTRUCTURA 1

MR=45 KGF/CM2 S/E


DENTELLON TRAPEZOIDAL DE 15+20+40cm (700 cm2) DE CONCRETO HECHO EN OBRA MR= 38 KGF/CM2, REVENIMIENTO NORMAL DE 8 +- 2.5 CM, T.M.A. 3/4", GRAVA TRITURADA, RESISTENCIA RAPIDA A TRES DIAS , ACABADO PULIDO EN PARTE SUPERIOR Y DOBLADOR EN ARISTAS SUPERIORES. INCLUYE: COMPACTADO DE PLANTILLA,CURADO EN SU PARTE SUPERIOR CON MEMBRANA BASE AGUA APLICADA CON ASPERSOR

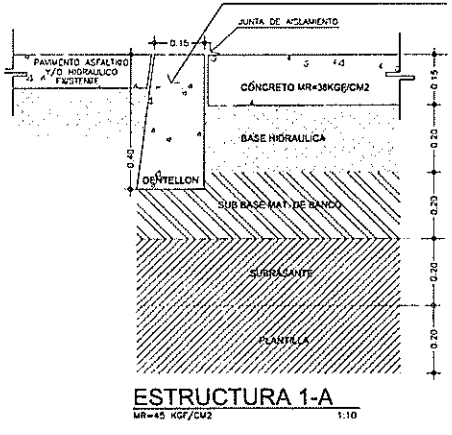

ESTRUCTURA 1-A


MR=45 KGF/CM2 1:10

PASAJUNTAS USO SIEMPRE Y CUANDO LO ESPECIFIQUE EL DISEÑO

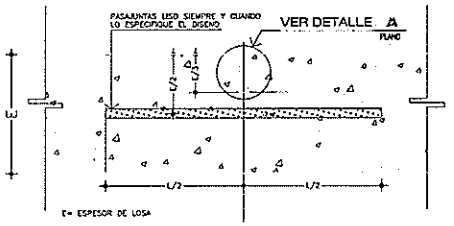

SELLADO DE JUNTAS

S/E

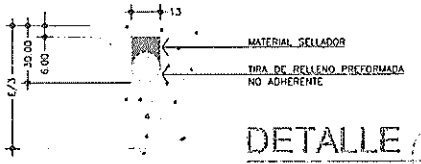

DETALLE A

PLANO

S/E

COTAS EN mm

E= ESPESOR DE LOSA

PAVIMENTACION

ESCALA 1:750 CALLE SANTA MONICA

La Dirección de Planeación y Proyectos solo autoriza el proyecto ejecutivo, no es responsable de la correcta ejecución de la obra. Este documento no tiene validez si no presenta las firmas de los responsables para su autorización, así como los sellos respectivos.

PRESIDENTE MUNICIPAL
M.P.P. Leonardo Montañez Castro
SECRETARIO DE OBRAS PÚBLICAS DEL MUNICIPIO DE AGUASCALIENTES
Ing. Miguel Ángel Huizar Botello

REV	FECHA	OBSERVACIONES

V.o. Bo. DE LA DEPENDENCIA

RESP. DE PROY. EXTERNO		LOGO EXTERNO
CED. PROFESIONAL		
PROYECTO	REVISÓ	AUTORIZÓ


Dirección de Planeación y Proyectos de Obra — Secretaría de Obras Públicas

PROYECTISTA	COORDINADOR
ING. DIEGO ROMO AGUILERA	ARQ. ALEJANDRO JAIME LEAL
JEFE DE DEP.	DIRECTOR
ARQ. J. JESÚS PALAFOX GONZÁLEZ	M. en ARQ. JOSÉ LUIS JIMÉNEZ GARCÍA

PROYECTO
CONSTRUCCIÓN DE CONCRETO HIDRAULICO CALLE SANTA MONICA (COL. LOS POCITOS)
UBICACIÓN
COLONIA LOS POCITOS
TRAMO ENTRE AV. EUGENIO GARZA SADA Y MARCOS CORONADO
CONTENIDO
PROYECTO GEOMETRICO "DETALLES CONSTRUCTIVOS"


CLAVE	No. PLANO
PG 02	05
FECHA	ESCALA
MAYO 2022	INDICADA
ACOTACIÓN	No. EXP.
METROS	E-000-22

Aguascalientes
LA CIUDAD DE TU VIDA

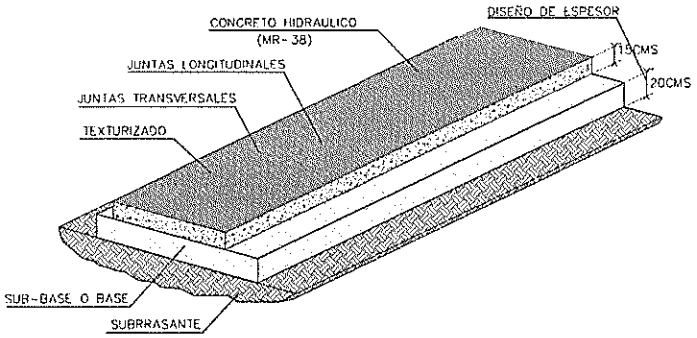


ESTRUCTURA DEL PAVIMENTO ISOMETRICO

SIN ESCALA

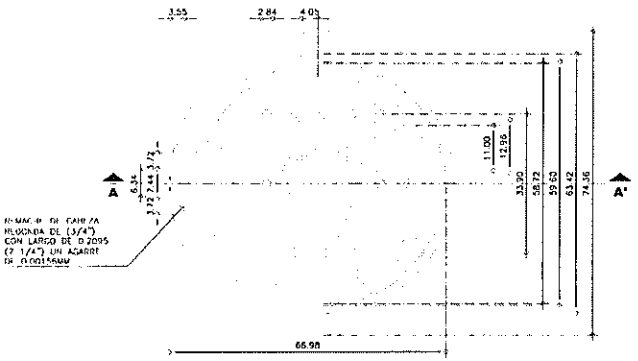


DETALLE DE BROCAL Y TAPA EN PLANTA

SIN ESCALA — COTAS EN cm

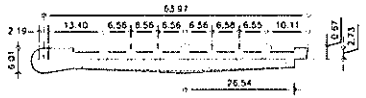

BROCAL Y TAPA EN ALZADO


SIN ESCALA — COTAS EN cm

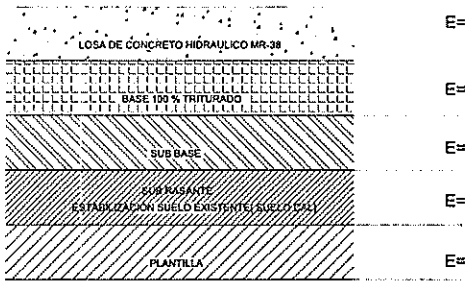

ESTRUCTURA DEL PAVIMENTO


SIN ESCALA

CONSTRUCCIÓN DE LOSA DIAMANTE A BASE DE CONCRETO PREMEZCLADO MR= 45 KG/CM2, T.M.A. 3/4" (19 mm), GRAVA TRITURADA, REVENIMIENTO DE 8+-2.5 cm, RESISTENCIA RÁPIDA A 3 DÍAS, DE 25 CM DE ESPESOR, EN POZO DE VISITA, SECCIÓN DE 1.50 M X 1.50 M, INCLUYE: TRAZO, NIVELACIÓN, LIMPIEZA PREVIA Y PREPARACIÓN DE LA SUPERFICIE, COMPACTACIÓN DE TERRENO AL 90% DE Su PVSM, ESCARIFICADO, SUMINISTRO DE MATERIALES, DEMOLICIÓN Y RECONSTRUCCIÓN DE APROCHES, ESPUMA DE POLIURETANO DE ALTA DENSIDAD EN TODO EL PERÍMETRO EXTERIOR DE 1/2", ASÍ COMO EN LAS JUNTAS DIAGONALES PARA FORMAR 4 PARTES, BROCAL Y TAPA DE Fo. Fo. TIPO PESADO (165 KG).

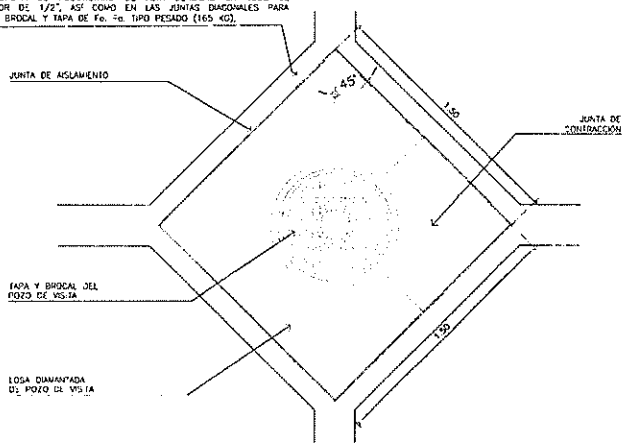

DETALLE LOSA DIAMANTE

SIN ESCALA — COTAS EN cm

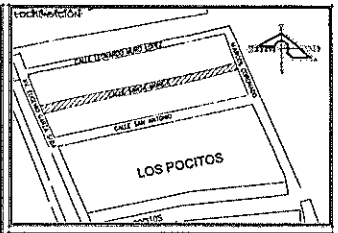


SIMBOLOGÍA

CONSTRUCCION DE PAVIMENTO HIDRAULICO A BASE DE CONCRETO PREMEZCLADO MR=38 KG/CM2 TMA 1 1/2" GRAVA TRITURADA, REVENIMIENTO DE 6 A 8 CM FRAGUADO NORMAL DE 15 CM DE ESPESOR MODULADO EN LOSAS DE 3.5 MTS. (ANCHO) X 3.5 MTS (LARGO) COMO MAXIMO, CON CORTES EN LAS LOSAS DE 1/3 DEL ESPESOR DE LA LOSA (5 CM) Y SELLADO CON COLA DE RATA Y MATERIAL ELASTOMERICO Y TIRA PREFORMADA (FOAMTECH DE 1/2X15) EN JUNTAS Y CORTES LONGITUDINALES Y TRANSVERSALES, ASI COMO EL APROCHE CON CUARNICION Y DENTELLON. INCLUYE: CIMBRADO, COLADO, VIBRADO CON INMERSION Y REGLA VIBRATORIA, DESCIMBRADO, REGLEADO FINAL, ACABADO CEPILLO DE ALUMINIO Y CON DOBLADOR, CALAFATEO, CURADO CON MEMBRANA BASE ACUA Y TODO LO NECESARIO PARA SU CORRECTA COLOCACION, P.U.O.

La Dirección de Planeación y Proyectos solo autoriza el proyecto ejecutivo, no es responsable de la correcta ejecución de la obra. Este documento no tiene validez si no presenta las firmas de los responsables para su autorización, así como los sellos respectivos.

| | | |

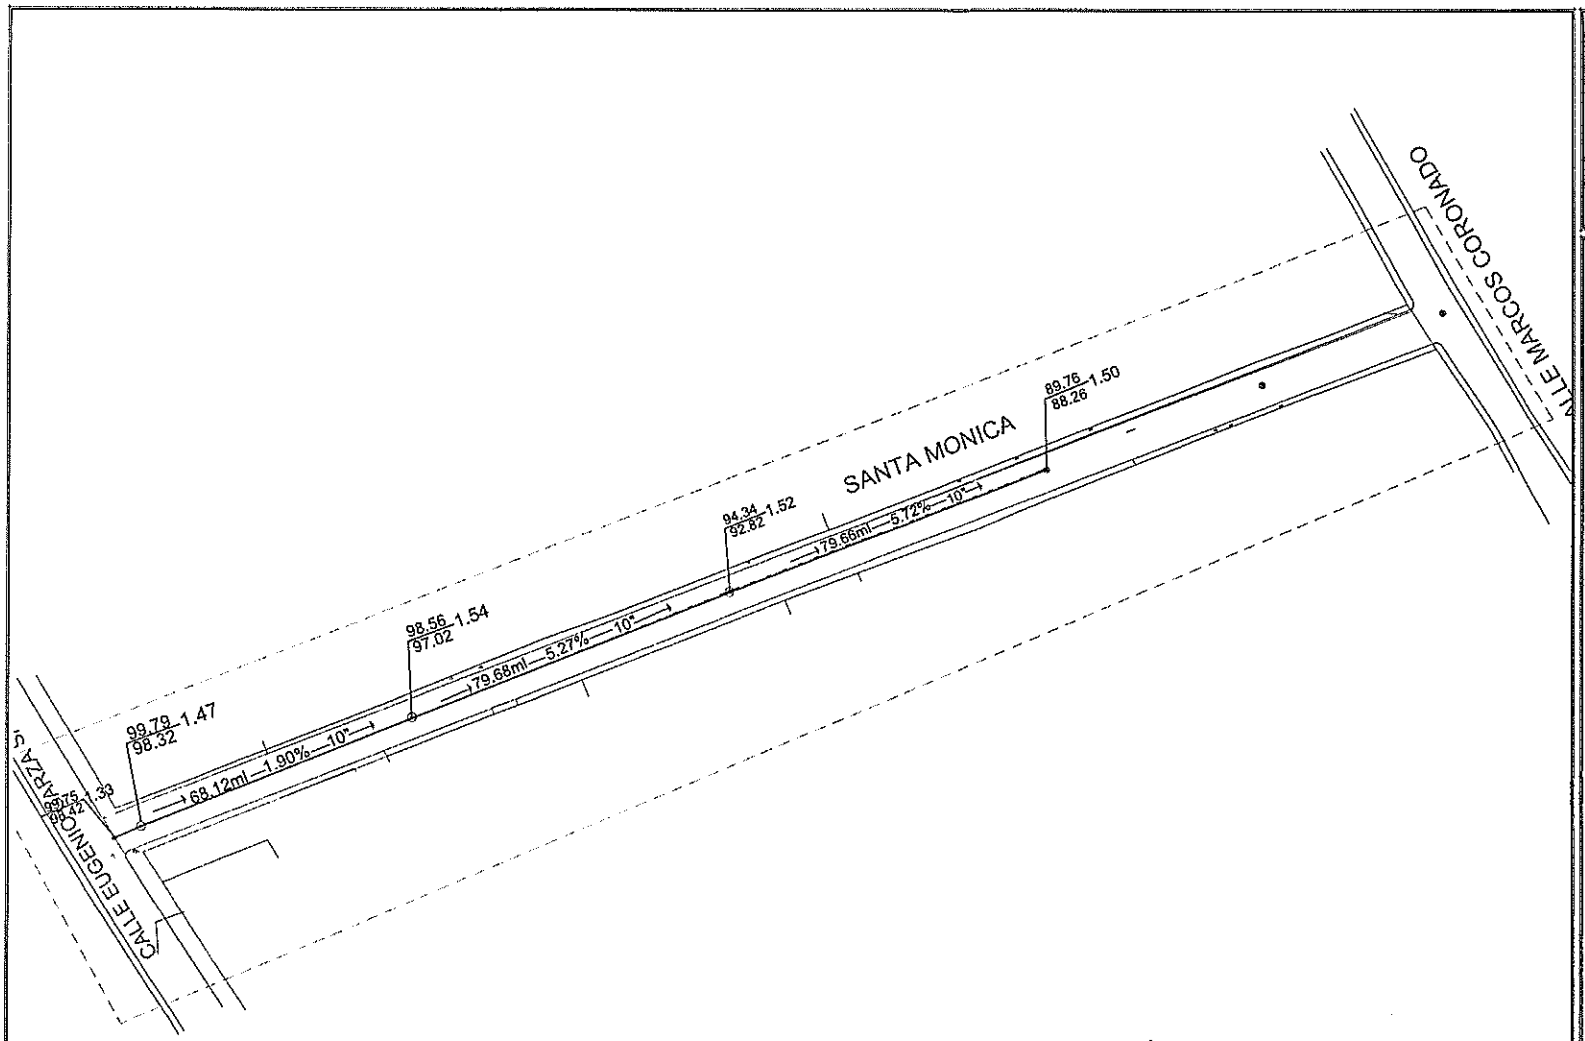


ALCANTARILLADO Y RED SANITARIA


ESCALA 1:500

CALLE SANTA MONICA

LOCALIZACIÓN:

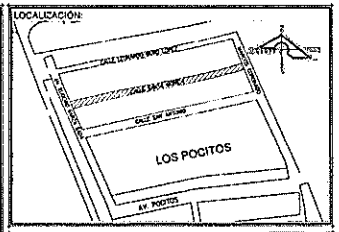

SIMBOLOGÍA

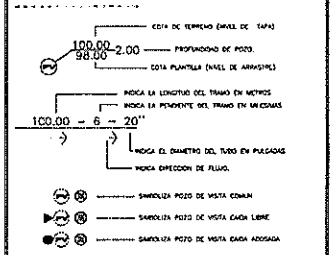

ESPECIFICACIONES

1. EL "E" PLANO SE USARA SOLAMENTE PARA LA INSTALACION SANITARIA.
2. CUALQUIER CAMBIO DE PROYECTO DEBERA SER AVALADO POR PROYECTOS SOPIMA Y/O COAPAMA.
3. LAS REVISIONES DEBERAN HACERSE CON LA MINUCIOSIDAD NECESARIA PARA COMPROBAR LA EXACTA CORRESPONDENCIA DE LOS TRABAJOS CON LO INDICADO EN EL PROYECTO; LAS ESPECIFICACIONES Y ORDENES COMPLEMENTARIAS.
4. TODA LA INSTALACIÓN DEBERÁ DE CUMPLIR CON LOS REQUISITOS Y LINEAMIENTOS QUE MARCA EL "MANUAL DE AGUA POTABLE, ALCANTARILLADO Y SANEAMIENTO", DE LA COMISIÓN NACIONAL DEL AGUA.
5. SE DEBE DE CUMPLIR CON LA HERMETICIDAD DE LA INSTALACIÓN DE ACUERDO A LA NORMA NOM-001-CONAGUA-1995 Y NT-008-CNA-2001. LAS JUNTAS DEBEN DE CUMPLIR COMO MÍNIMO LAS CARACTERÍSTICAS, ESPECIFICACIONES Y MÉTODOS DE PRUEBAS ESTIPULADOS EN LA NORMA NMX-E-111.
6. LAS TUBERIAS DEBEN DE CUMPLIR CON LA NORMA NMX-E-211/1-SCFI-2003, NMX-E-211/2-CNCP-2003 Y LAS CONEXIONES CON LA NORMA NMX-E-149/SCFI-2001.
7. LA PROFUNDIDAD MINIMA DE COLOCACION DE TUBERIA SERA DE 0.90 M DE NIVEL DE TERRENO O PISO TERMINADO A LOMO SUPERIOR DE TUBO.
8. LA CONEXION PARA LA DESCARGA SANITARIA SE VERIFICARA EN CAMPO YA QUE NO SE TIENE LA PROFUNDIDAD DE LOS POZOS.
9. TODOS LOS MATERIALES CON LOS QUE SE EJECUTEN LAS INSTALACIONES SERAN NUEVOS Y DE PRIMERA CALIDAD Y CUANDO EXISTA ALGUNA DUDA O DISCREPANCIA RESPECTO A DICHA CALIDAD, ESTA SERA RESUELTA POR EL SUPERVISOR, POR LO QUE SE REFIERE A LA CALIDAD DE LOS MATERIALES DEBERA SUJETARSE A LO ESTABLECIDO AL EFECTO EN LAS NORMAS OFICIALES MEXICANAS Y DE LA DIRECCION GENERAL DE NORMAS DE LA SECRETARIA DE COMERCIO Y FOMENTO.
10. LA TUBERIA NO SE DEBERA DOBLAR, PARA EVITAR REDUCCION DE SU SECCION Y DE SU UNIFORMIDAD EN SU ESPESOR DEL MATERIAL.
11. LAS TUBERIAS DEBERAN DE CONSERVARSE LIMPIAS TANTO EN SU EXTERIOR COMO EN SU INTERIOR HASTA LA TERMINACION TOTAL Y ENTREGA DE LOS TRABAJOS.
12. LOS TRAMOS RECTOS DE TUBERIA ENTRE CONEXIONES, DEBERAN QUEDAR ALINEADOS SEAN VERTICALES U HORIZONTALES.
13. LOS CORTES EN LOS TUBOS SE EJECUTARAN EN ANGULO RECTO CON RESPECTO AL EJE LONGITUDINAL DEL MISMO.

NOTA; LA INSTALACION DE RED DE ALCANTARILLADO DE EJECUTARSE, ESTE PLANO ES PARA UBICAR LA RED DE ALCANTARILLADO EXISTENTES INDICANDO UBICACION DE POZOS DE VISITA,NIVELESOE TAPA Y ARRASTRE, ASI COMO DIRECCIONES , CUIDANDO DE NO AFECTAR O ALTERAR, AL MOMENTO DE EJECUTAR ALGUN TRABAJO O MANIOBRA COMO DEMOLICIONES, EXCAVACIONES, COMPACTACIONES, ETC.

La Dirección de Planeación y Proyectos solo autoriza el proyecto ejecutivo, no es responsable de la correcta ejecución de la obra. Este documento no tiene validez si no presenta las firmas de los responsables para su autorización, así como los sellos respectivos.

PRESIDENTE MUNICIPAL
M.P.P. Leonardo Montañez Castro
SECRETARIO DE OBRAS PÚBLICAS DEL MUNICIPIO DE AGUASCALIENTES
Ing. Miguel Ángel Hulzar Botello

REV	FECHA	OBSERVACIONES

V°B° DE LA DEPENDENCIA

RESP. DE PROY. EXTERNO		LOGO EXTERNO
CED. PROFESIONAL		
PROYECTO	REVISO	AUTORIZO


Dirección de Planeación y Proyectos de Obra — Secretaría de Obras Públicas

PROYECTISTA	COORDINADOR
ING. DIEGO ROMO AGUILERA	ARQ. ALEJANDRO JAIME LEAL
JEFE DE DEP.	DIRECTOR
ARQ. J. JESÚS PALAFOX GONZÁLEZ	M. en ARQ. JOSÉ LUIS JIMÉNEZ GARCÍA


PROYECTO: CONSTRUCCIÓN DE CONCRETO HIDRAULICO CALLE SANTA MONICA (COL. LOS POCITOS)
UBICACIÓN: COLONIA LOS POCITOS
TRAMO ENTRE AV. EUGENIO GARZA SADA Y MARCOS CORONADO
CONTENIDO: RED SANITARIA

CLAVE	No. PLANO
SAN 01	12
FECHA: MAYO 2022	ESCALA: INDICADA
ACOTACIÓN: METROS	No. EXP.: E-000-22

Aguascalientes
LA CIUDAD DE TU VIDA

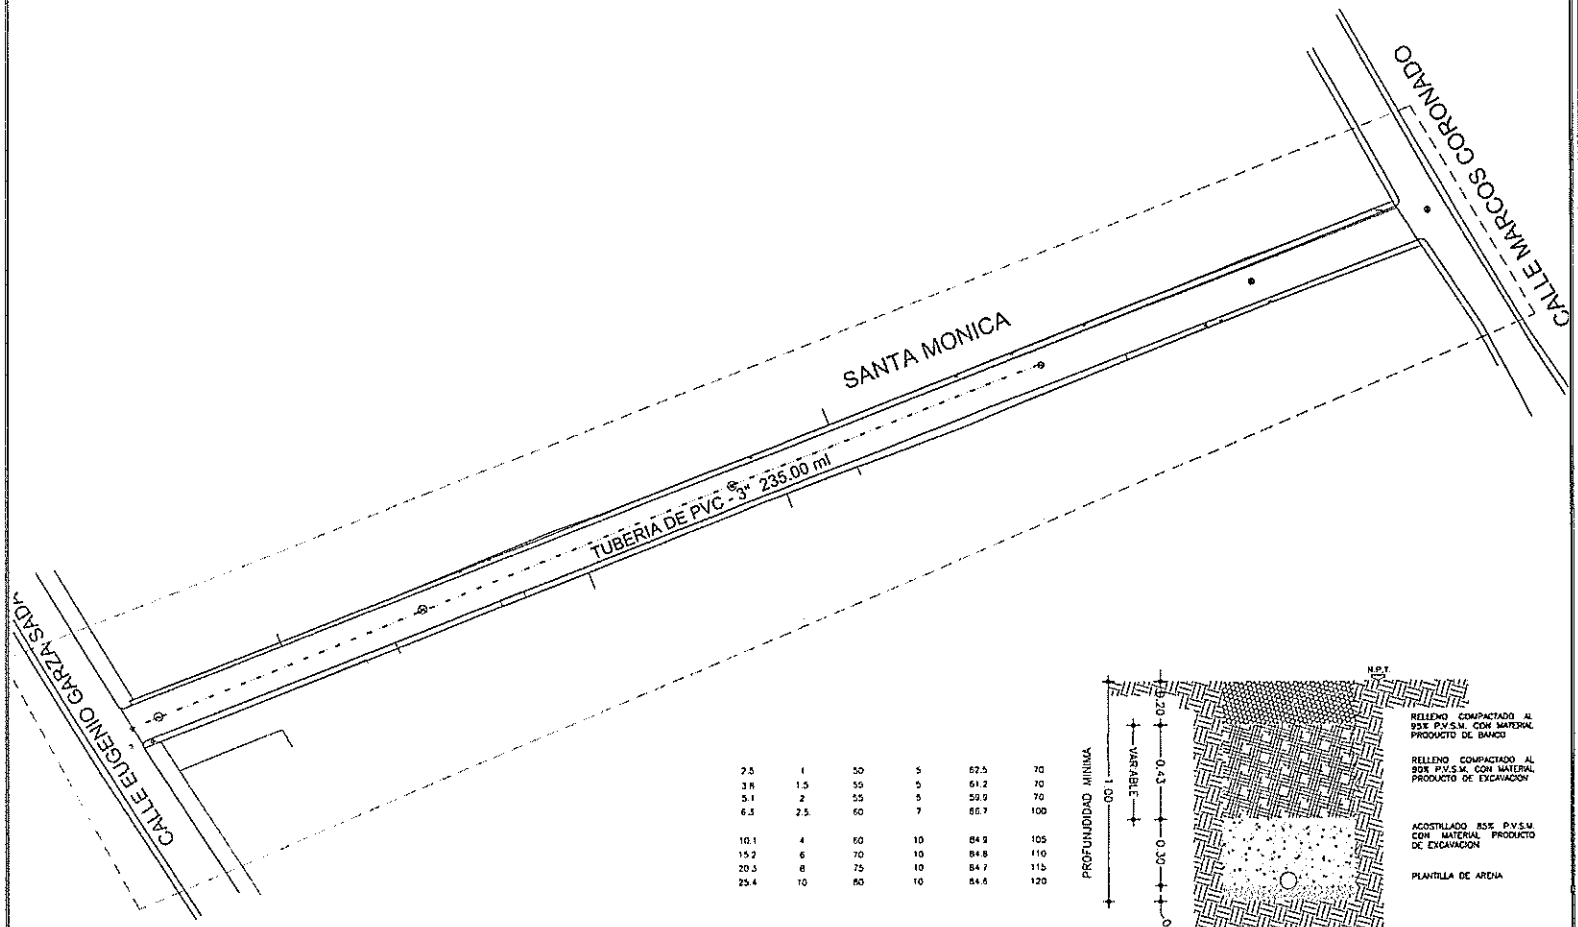

2.5	1	50	5	62.5	70
3.8	1.5	55	5	61.2	70
5.1	2	55	5	59.9	70
6.3	2.5	60	7	86.7	100
10.1	4	60	10	84.9	105
15.2	6	70	10	84.8	110
20.3	8	75	10	84.7	115
25.4	10	80	10	84.6	120

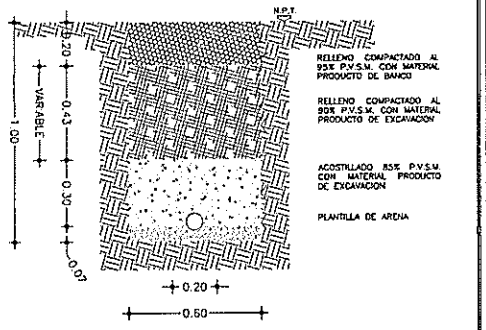


S / E

RED DE AGUA POTABLE

ESCALA 1:500 CALLE SANTA MONICA

LOCALIZACIÓN:

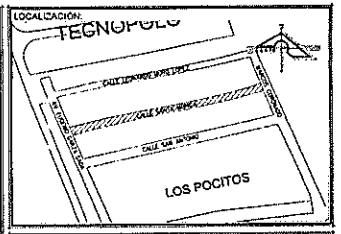

SIMBOLOGÍA

NUMERO DE CASA ;

01 CAJA DE VALVULAS

INDICA LA LONGITUD DEL TRAMO EN METROS

25—T.6 INDICA EL DIAMETRO DEL TUBO EN PULGADAS

ESPECIFICACIONES

1. ESTE PLANO SE USARA SOLAMENTE PARA LA INSTALACION DE AGUA POTABLE.
2. CUALQUIER CAMBIO DE PROYECTO DEBERA SER AVALADO POR PROYECTOS SOPNA Y/O COAPAMA.
3. LAS REVISIONES DEBERAN HACERSE CON LA MINUCIOSIDAD NECESARIA PARA COMPROBAR LA EXACTA CORRESPONDENCIA DE LOS TRABAJOS CON LO INDICADO EN EL PROYECTO; LAS ESPECIFICACIONES Y DEMÁS COMPLEMENTARIAS.
4. TODA LA INSTALACION DEBERÁ DE CUMPLIR CON LOS REQUISITOS Y LINEAMIENTOS QUE MARCA EL "MANUAL DE AGUA POTABLE, ALCANTARILLADO Y SANEAMIENTO", DE LA COMISIÓN NACIONAL DEL AGUA.
5. SE DEBE DE CUMPLIR CON LA HERMETICIDAD DE LA INSTALACIÓN DE ACUERDO A LA NORMA NT-001-CNA-2001 Y NOM-013-CONAGUA-2000.
6. LAS "TUBERÍAS DEBEN DE CUMPLIR CON LA NORMA NMX-E-143 Y LAS CONEXIONES CON LA NORMA NMX-E-211/2-1993.
7. LA PROFUNDIDAD MINIMA DE COLOCACION DE TUBERIA SERA DE 0.70 M DE NIVEL DE TERRENO O PISO TERMINADO A LOMO SUPERIOR DE TUBO.
8. TODOS LOS MATERIALES CON LOS QUE SE EJECUTEN LAS INSTALACIONES SERAN NUEVOS Y DE PRIMERA CALIDAD Y CUANDO EXISTA ALGUNA DUDA O DISCREPANCIA RESPECTO A DICHA CALIDAD, ESTA SERA RESUELTA POR EL SUPERVISOR. POR LO QUE SE REFIERE A LA CALIDAD DE LOS MATERIALES DEBERA SUJETARSE A LO ESTABLECIDO AL EFECTO EN LAS NORMAS OFICIALES MEXICANAS Y DE LA DIRECCION GENERAL DE NORMAS DE LA SECRETARIA DE COMERCIO Y FOMENTO.
9. LA TUBERIA NO SE DEBERA DOBLAR, PARA EVITAR REDUCCION DE SU SUCCION Y DE SU UNIFORMIDAD EN SU ESPESOR DEL MATERIAL.
10. LAS TUBERIAS DEBERAN DE CONSERVARSE LIMPIAS TANTO EN SU EXTERIOR COMO EN SU INTERIOR HASTA LA TERMINACION TOTAL Y ENTREGA DE LOS TRABAJOS.
11. LOS TRAMOS RECTOS DE TUBERIA ENTRE CONEXIONES, DEBERAN QUEDAR ALINEADOS SEAN VERTICALES U HORIZONTALES.
12. LOS CORTES EN LOS TUBOS SE EJECUTARAN EN ANGULO RECTO CON RESPECTO AL EJE LONGITUDINAL DEL MISMO.

La Dirección de Planeación y Proyectos solo autoriza el proyecto ejecutivo, no es responsable de la correcta ejecución de la obra. Este documento no tiene validez si no presenta las firmas de los responsables para su autorización, así como los sellos respectivos.

PRESIDENTE MUNICIPAL
M.P.P. Leonardo Montañez Castro
SECRETARIO DE OBRAS PUBLICAS DEL MUNICIPIO DE AGUASCALIENTES
Ing. Miguel Ángel Huizar Botello

REV	FECHA	OBSERVACIONES

Vo Bo DE LA DEPENDENCIA

RESP. DE PROY EXTERNO		LOGO EXTERNO
CED. PROFESIONAL		
PROYECTO	REVISO	AUTORIZO

Dirección de Planeación y Proyectos de Obra — Secretaría de Obras Públicas

PROYECTISTA	COORDINADOR
ING. DIEGO ROMO AGUILERA	ARQ. ALEJANDRO JAIME LEAL
JEFE DE DEP.	DIRECTOR
ARQ. J. JESÚS PALAFOX GONZÁLEZ	M. en ARQ. JOSÉ LUIS JIMÉNEZ GARCÍA

PROYECTO
CONSTRUCCIÓN DE CONCRETO HIDRAULICO CALLE SANTA MONICA (COL. LOS POCITOS)

UBICACIÓN
COLONIA LOS POCITOS
TRAMO ENTRE AV. EUGENIO GARZA SADA Y MARCOS CORONADO


CONTENIDO
RED HIDRAULICA

CLAVE	No PLANO
HID-01	15
FECHA	ESCALA
MAYO 2022	INDICADA
ACOTACIÓN	No. EXP.
METROS	E-000-22

Aguascalientes
LA CIUDAD DE TU VIDA

CONSTRUCCION DE GUARNICION RECTA Y/O CURVA TRAPEZOIDAL DE 15x20x40 CM DE SECCION CON CONCRETO SIMPLE MR=38KGF/CM2 , REVENIMIENTO DE 10 +- 2.5 CM, T.M.A. 3/4" (19MM), GRAVA TRITURADA, ACABADO PULIDO EN PARTE DE SUPERIOR Y DOBLADOR EN ARISTAS SUPERIORES. INCLUYE: COMPACTADO DE PLANTILLA, CIMBRADO, COLADO, ACABADO, DESCIMBRADO, ALINEADO, NIVELADO, DESCIMBRADO Y CURADO EN SU PARTE SUPERIOR CON MEMBRANA BASE AGUA A RAZON DE 1 LTO/M2.SEGUN FICHA TECNICA 204


PISO EN RAMPAS DE 10.00 cm DE ESPESOR DE CONCRETO SIMPLE MR=38 KGF/CM2, HECHO EN OBRA, TMA 1 1/2" (38MM), REVENIMIENTO DE 10+-2.5CM, GRAVA TRITURADA, ACABADO LAVADERO. INCLUYE: CIMBRADO, NIVELADO, VIBRADO, CURADO CON MEMBRANA BASE AGUA, ACARREOS DENTRO DE LA OBRA, ELEVACIONES, CUALQUIER ALTURA, LIMPIEZAS. SEGUN FICHA TECNICA 216

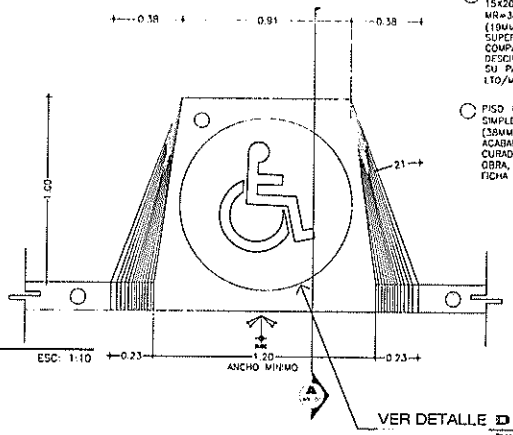


RAMPA TIPO II
VISTA EN PLANTA ESC: 1:10

CONSTRUCCION DE CENEFA EN RAMPAS DE 30 CM DE ANCHO Y 10 CM DE ESPESOR A BASE DE CONCRETO PREMEZCLADO F'c= 150 KG/CM2, T.M.A. 3/4", GRAVA TRITURADA REVENIMIENTO DE 10 +- 2 CM, ACABADO ESTAMPADO SEGUN DISEÑO(VER PLANOS DE RAMPA TIPO) COLOR ROJO DISOURO CLAVE C-007, DESMOLDANTE D-007, SELLADOR ACRILICO AL 25% SOLIDOS JUNTAS FRIAS ASERRADAS SECCION DE LOSAS COMO INDIQUE PROYECTO INCLUYE: SUMINISTRO Y HECHURA DE TAPETE DE POLIURETANO O LLANA METALICA DENTADA SEGUN DISEÑO DE ESTAMPADO, CIMBRADO, COLADO, DESCIMBRADO Y CURADO CON MEMBRANA QUIMICA APLICADA CON ASPERSOR, TRABAJO TERMINADO SEGUN FICHA TECNICA FT-200.


CONSTRUCCION DE CENEFA EN BANQUETAS (LINEA TACTIL) DE 30 CM DE ANCHO Y 10 CM DE ESPESOR A BASE DE CONCRETO PREMEZCLADO F'c= 150 KG/CM2, T.M.A. 3/4", GRAVA TRITURADA REVENIMIENTO DE 10 +- 2 CM, ACABADO ESTAMPADO SEGUN DISEÑO(VER PLANOS DE BANQUETA TIPO) COLOR ROJO DISOURO CLAVE C-007, DESMOLDANTE D-007, SELLADOR ACRILICO AL 25% SOLIDOS JUNTAS FRIAS ASERRADAS SECCION DE LOSAS COMO INDIQUE PROYECTO INCLUYE: SUMINISTRO Y HECHURA DE TAPETE DE POLIURETANO O LLANA METALICA DENTADA SEGUN DISEÑO DE ESTAMPADO, CIMBRADO, COLADO, DESCIMBRADO Y CURADO CON MEMBRANA QUIMICA APLICADA CON ASPERSOR, TRABAJO TERMINADO SEGUN FICHA TECNICA FT-200.

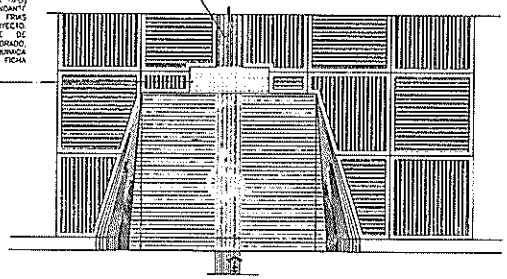

PISO EN RAMPAS DE 10.00 cm DE ESPESOR DE CONCRETO SIMPLE MR=38 KGF/CM2, HECHO EN OBRA, TMA 1 1/2" (38MM), REVENIMIENTO DE 10+-2.5CM, GRAVA TRITURADA, ACABADO LAVADERO. INCLUYE: CIMBRADO, NIVELADO, VIBRADO, CURADO CON MEMBRANA BASE AGUA, ACARREOS DENTRO DE LA OBRA, ELEVACIONES, CUALQUIER ALTURA, LIMPIEZAS. SEGUN FICHA TECNICA 216

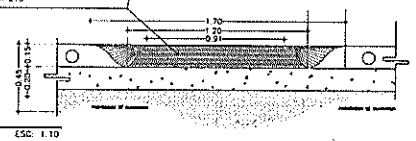

RAMPA TIPO II
VISTA FRONTAL ESC: 1:10

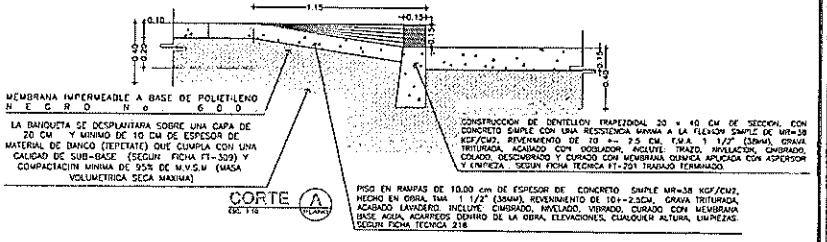

MEMBRANA IMPERMEABLE A BASE DE POLIETILENO NEGRO No 600


LA BANQUETA SE DESPLANTARA SOBRE UNA CAPA DE 20 CM Y MINIMO DE 10 CM DE ESPESOR DE MATERIAL DE BANCO (TEPETATE) QUE CUMPLA CON UNA CALIDAD DE SUB-BASE (SEGUN FICHA FT-329) Y COMPACTACION MINIMA DE 95% DE M.V.S.M (MASA VOLUMETRICA SECA MAXIMA)

CONSTRUCCION DE DENTELLON TRAPEZOIDAL 20 x 40 CM DE SECCION, CON CONCRETO SIMPLE CON UNA RESISTENCIA MINIMA A LA FLEXION SIMPLE DE MR=38 KGF/CM2, REVENIMIENTO DE 10 +- 2.5 CM, T.M.A. 1 1/2" (38MM), GRAVA TRITURADA, ACABADO CON DOBLADOR, INCLUYE: TRAZO, NIVELACION, CIMBRADO, COLADO, DESCIMBRADO Y CURADO CON MEMBRANA QUIMICA APLICADA CON ASPERSOR Y LIMPIEZA. SEGUN FICHA TECNICA FT-291 TRABAJO TERMINADO.

CORTE A (PLANO)
ESC 1:10

PISO EN RAMPAS DE 10.00 cm DE ESPESOR DE CONCRETO SIMPLE MR=38 KGF/CM2, HECHO EN OBRA, TMA 1 1/2" (38MM), REVENIMIENTO DE 10+-2.5CM, GRAVA TRITURADA, ACABADO LAVADERO. INCLUYE: CIMBRADO, NIVELADO, VIBRADO, CURADO CON MEMBRANA BASE AGUA, ACARREOS DENTRO DE LA OBRA, ELEVACIONES, CUALQUIER ALTURA, LIMPIEZAS. SEGUN FICHA TECNICA 216

LOCALIZACION:

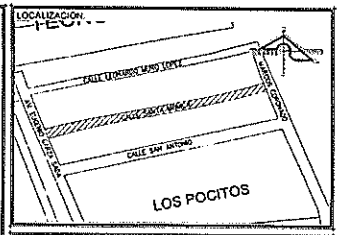

SIMBOLOGÍA

La Dirección de Planeación y Proyectos solo autoriza el proyecto ejecutivo, no es responsable de la correcta ejecución de la obra. Este documento no tiene validez si no presenta las firmas de los responsables para su autorización, así como los sellos respectivos.

PRESIDENTE MUNICIPAL
M.P.P. Leonardo Montañez Castro
SECRETARIO DE OBRAS PUBLICAS DEL MUNICIPIO DE AGUASCALIENTES
Ing. Miguel Ángel Huizar Botello

REV	FECHA	OBSERVACIONES

V°Bo. DE LA DEPENDENCIA

RESP. DE PROY. EXTERNO		LOGO EXTERNO
CED. PROFESIONAL		
PROYECTO	REVISÓ	AUTORIZÓ

Dirección de Planeación y Proyectos de Obra | Secretaría de Obras Públicas

PROYECTISTA	COORDINADOR
ING. DIEGO ROMO AGUILERA	ARQ. ALEJANDRO JAIME LEAL
JEFE DE DEP.	DIRECTOR
ARQ. J. JESÚS PALAFOX GONZÁLEZ	M. en ARQ. JOSÉ LUIS JIMÉNEZ GARCÍA


PROYECTO
CONSTRUCCIÓN DE CONCRETO HIDRAULICO CALLE SANTA MONICA (COL. LOS POCITOS)
UBICACIÓN
COLONIA LOS POCITOS
TRAMO ENTRE AV. EUGENIO GARZA SADA Y MARCOS CORONADO
CONTENIDO
RAMPAS PEATONALES

CLAVE	No. PLANO
DET 01	18
FECHA	ESCALA
MAYO 2022	INDICADA
ACOTACIÓN	No. EXP.
METROS	E-000-22

Aguascalientes
LA CIUDAD DE TU VIDA


BANQUETA DE 10 CM DE ESPESOR A BASE DE CONCRETO PREMEZCLADO F'c=25 kg/cm2, T.M.A. 3/4 " ACABADO RAYADO FINO CON BROCHA DE PELO, CON CONTRAJUNTA DE 1 ", SECCIÓN DE 1.50x1.50m. CON MALLA ELECTROSOLDADA 6-6/10-10.

PISO EN RAMPAS DE SECCIÓN 10 CM DE ESPESOR DE CONCRETO F'c= 250 kg/cm2, HECHO EN OBRA, T.M.A. 3/4 19 mm. ARMADO CON MALLA ELECTROSOLDADA 6x6/10-10.

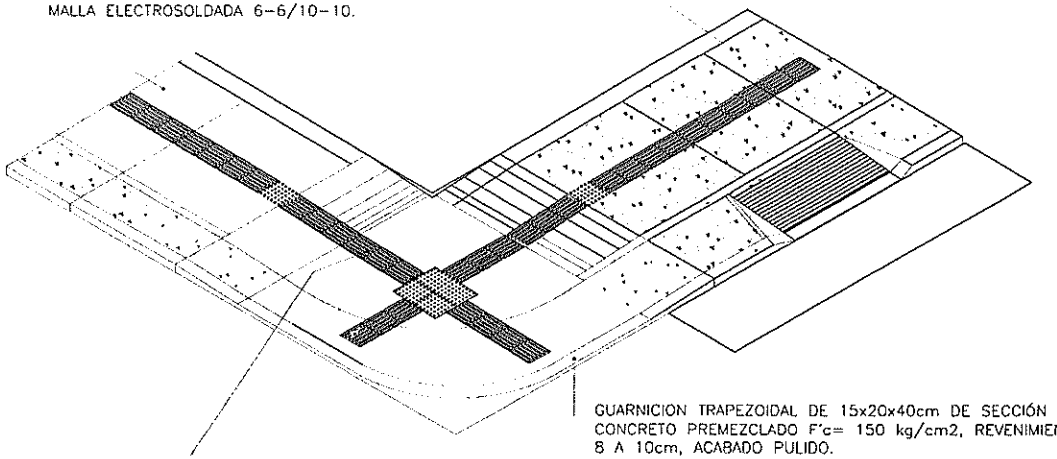

GUARNICION TRAPEZOIDAL DE 15x20x40cm DE SECCIÓN CON CONCRETO PREMEZCLADO F'c= 150 kg/cm2, REVENIMIENTO DE 8 A 10cm, ACABADO PULIDO.


BANDA TACTIL GUIA DE 10 CM DE ESPESOR A BASE DE CONCRETO PREMEZCLADO F'c= 250 kg/cm2. ACABADO SEGUN DETALLE.

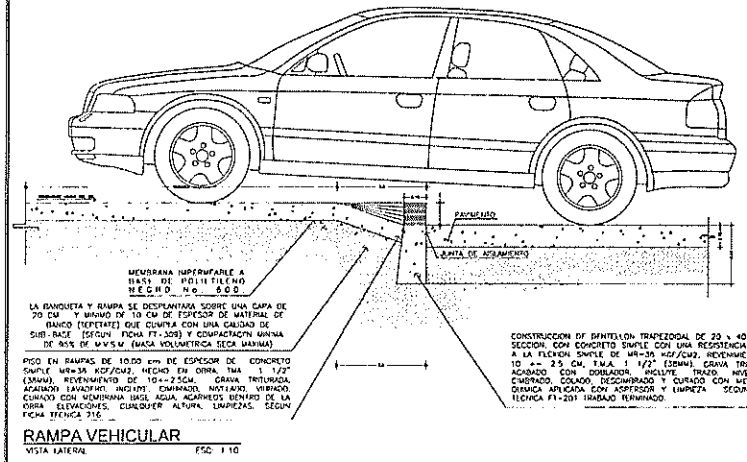


RAMPA VEHICULAR
VISTA LATERAL ESC: 1:10

PISO EN RAMPAS DE 10.00 cm DE ESPESOR DE CONCRETO SIMPLE MR=38 KGF/CM2, HECHO EN OBRA, TMA 1 1/2" (38MM), REVENIMIENTO DE 10+-2.5CM, GRAVA TRITURADA, ACABADO LAVADERO, INCLUYE: CIMBRADO, NIVELADO, VIBRADO, CURADO CON MEMBRANA BASE AGUA, ACARREOS DENTRO DE LA OBRA, ELEVACIONES, CUALQUIER ALTURA, LIMPIEZAS, SEGUN FICHA TECNICA 216.

RAMPA VEHICULAR
VISTA EN PLANTA ESC: 1:10

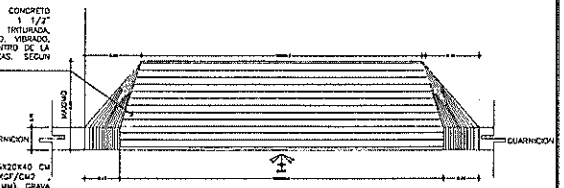


CONSTRUCCION DE GUARNICION TRAPEZOIDAL DE 15X20X40 CM DE SECCION CON CONCRETO SIMPLE MR=38KGF/CM2 REVENIMIENTO DE 10 +- 2.5 CM, T.M.A. 3/4" (19MM), GRAVA TRITURADA, ACABADO PULIDO EN PARTE DE SUPERIOR Y DOBLADOR EN ARISTAS SUPERIORES, INCLUYE: COMPACTADO DE PLANTILLA, CIMBRADO, COLADO, ACABADO, DESCIMBRADO, ALINEADO, NIVELADO, DESENCOFRADO Y CURADO EN SU PARTE SUPERIOR CON MEMBRANA BASE AGUA A RAZON DE 1 LTO/M2 SEGUN FICHA TECNICA 204.

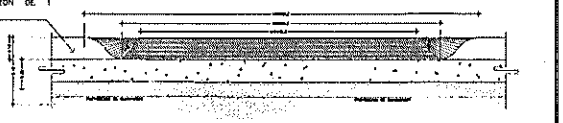

RAMPA VEHICULAR
VISTA FRONTAL ESC: 1:10

LOCALIZACIÓN:

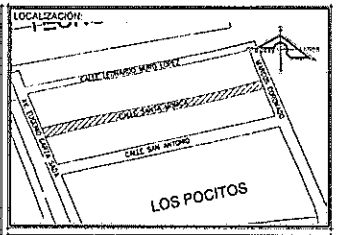

SIMBOLOGÍA

La Dirección de Planeación y Proyectos solo autoriza el proyecto ejecutivo, no es responsable de la correcta ejecución de la obra. Este documento no tiene validez si no presenta las firmas de los responsables para su autorización, así como los sellos respectivos.

PRESIDENTE MUNICIPAL
M.P.P. Leonardo Montañez Castro
SECRETARIO DE OBRAS PÚBLICAS DEL MUNICIPIO DE AGUASCALIENTES
Ing. Miguel Ángel Hulzar Botello

REV	FECHA	OBSERVACIONES

V°B° EL DE LA DEPENDENCIA

RESP. DE PROY. EXTERNO		LOGO EXTERNO
CED. PROFESIONAL		
PROYECTÓ	REVISÓ	AUTORIZÓ

Dirección de Planeación y Proyectos de Obra — Secretaría de Obras Públicas

PROYECTISTA	COORDINADOR
ING. DIEGO ROMO AGUILERA	ARQ. ALEJANDRO JAIME LEAL
JEFE DE DEP.	DIRECTOR
ARQ. J. JESÚS PALAFOX GONZÁLEZ	M. en ARQ. JOSÉ LUIS JIMÉNEZ GARCÍA

PROYECTO
CONSTRUCCIÓN DE CONCRETO HIDRAULICO CALLE SANTA MONICA (COL. LOS POCITOS)
UBICACIÓN
COLONIA LOS POCITOS
TRAMO ENTRE AV. EUGENIO GARZA SADA Y MARCOS CORONADO
CONTENIDO
RAMPA VEHICULAR (DETALLE CONSTRUCTIVO)

CLAVE	No. PLANO
DET 02	19
FECHA: MAYO 2022	ESCALA: INDICADA
ACOTACIÓN: METROS	No. EXP.: E-000-22

Aguascalientes
LA CIUDAD DE TU VIDA