Aguascalientes
LA CIUDAD DE TU VIDA

Dirección de Programación Presupuestal
Núm. Oficio AMPP/0440/22
Aguascalientes, Ags. 17 de Octubre del 2022
Asunto: Validación de Expediente Técnico

C.P. SERGIO ARTURO LOZANO GONZÁLEZ
SECRETARIO DE FINANZAS MUNICIPALES
P R E S E N T E

Con fundamento en los artículos 17 fracción XV, 60 fracción XVI y 76 fracción VI del Reglamento del Sistema Integral de Desarrollo Municipal y del Instituto Municipal de Planeación y Evaluación de Aguascalientes, hago referencia al oficio SOPMA/2254/2022 recibido por este Instituto el día 13 de Octubre del 2022 por parte de la Secretaría de Obras Públicas, mediante el cual remiten el expediente técnico original de la siguiente obra para su análisis, registro y priorización, conforme al Programa Anual de Obra Pública y Programas Sociales para el ejercicio presupuestal 2022:

DEPENDENCIA EJECUTORA:	SOPMA
NOMBRE DE LA OBRA O PROYECTO:	SOBRECARPETA ASFÁLTICA
UBICACIÓN:	CALLE PETRÓLEOS MEXICANOS, ENTRE GRAL. IGNACIO ZARAGOZA Y AQUILES SERDÁN, ZONA CENTRO, AGUASCALIENTES, AGS.
FONDO DE INVERSIÓN:	FONDO DE INFRAESTRUCTURA SOCIAL MUNICIPAL Y DE LAS DEMARCACIONES TERRITORIALES DEL DISTRITO FEDERAL
IMPORTE:	$2,978,592.33 (ET FINAL)
No. DE OBRA:	2022-FISMDF-0044-04-1101
MODALIDAD DE EJECUCIÓN:	CONTRATO
EJE:	MUNICIPIO SOBRESALIENTE
ESTRATEGIA:	OBRA PÚBLICA INTELIGENTE
POLITICA:	5.8.1.REHABILITACIÓN Y MANTENIMIENTO VIALIDADES, CAMINOS, CALLES, ÁREAS DE TERRACERÍA Y CAUCES (COM.

Al respecto, hago de su conocimiento que dicho expediente ha sido analizado en su integración técnica y documental, con base en el artículo 168 fracción I del Reglamento de la Ley de Obras Públicas y Servicios Relacionados para el Estado de Aguascalientes y sus Municipios.

Asimismo, le comento que este Instituto valida dicha obra acorde a lo establecido en los artículos 14, 22 párrafo segundo y 23 de la Ley de Obras Públicas y Servicios Relacionados para el Estado de Aguascalientes y sus Municipios, la cual se encuentra alineada al Plan de Desarrollo Municipal vigente, para dar cumplimiento a las metas establecidas en el mismo, y a los Lineamientos Generales para la Operación de este Fondo de Inversión, toda vez que la misma cuente con la autorización del CODEMUN. De igual manera, se hace de su conocimiento que deberá cumplir con lo establecido en los ordenamientos aplicables en lo que respecta al ejercicio, control e información de los recursos de este Fondo. Cabe hacer mención que los recursos solicitados para este proyecto de inversión, estarán sujetos a la disponibilidad presupuestal para el presente ejercicio fiscal que determine la Secretaría a su digno cargo. Sin otro particular por el momento, le envío un cordial saludo.

A T E N T A M E N T E

DR. RAMÓN RODRIGO RODRÍGUEZ CAMACHO
ENCARGADO DE DESPACHO DE LA DIRECCIÓN GENERAL DEL IMPLAN

CAAR / JDBC
C.c.p. I.C. Arq. Gloria Guadalupe Castillo González .- Secretaría de Obras Públicas. Para su conocimiento.
C.c.p. Archivo.

Instituto Municipal de Planeación y Evaluación de Aguascalientes
Antonio Acevedo Escobedo 103 A. Col. Centro
Aguascalientes, Ags. C.P. 20000
(449) 9101010 Ext. 3117
www.implanags.gob.mx

GOBIERNO MUNICIPAL DE AGUASCALIENTES

INSTITUTO MUNICIPAL DE PLANEACION

IMPLAN

ANÁLISIS INTEGRAL DE EXPEDIENTE TÉCNICO

No. DE OBRA (PAOP 2020):	2022-FISMDF-0044-04-1101	REGISTRO No.	215
OFICIO DE VALIDACIÓN:	AMPP/0440/22	FECHA RECIBIDO PARA REVISIÓN:	17 de Octubre del 2022
PROGRAMA:	URBANIZACION MUNICIPAL	LOCALIDAD O COLONIA:	ZONA CENTRO
SUB-PROGRAMA:	0411- Calles y Caminos	DELEGACIÓN:	Centro Oriente
DEPENDENCIA:	Secretaría de Obras Públicas	MOD. DE EJECUCIÓN:	CONTRATO
NOMBRE DE LA OBRA:	SOBRECARPETA ASFÁLTICA, CALLE PETRÓLEOS MEXICANOS, ENTRE GRAL. IGNACIO ZARAGOZA Y AQUILES SERDÁN		
FUENTE DE FINANCIAMIENTO:	FONDO DE INFRAESTRUCTURA SOCIAL MUNICIPAL Y DE LAS DEMARCACIONES TERRITORIALES DEL DISTRITO FEDERAL, FISMDF		
INVERSIÓN:	$2,978,592.33	CLASIFICACIÓN DE OBRA:	BIENES DE DOMINIO PUBLICA

TOTAL	FEDERAL	ESTATAL	MUNICIPAL	BENEFICIARIOS	OTROS	DIFERENCIA ENTRE MOD.
$2,978,592.33	$2,978,592.33	0.00	0.00	0.00	0.00	*$41,32*

TIPO DE EXPENDIENTE:	ET FINAL	AÑO: 2022	AÑO:	AÑO:		
AVANCES:	Financiero: 5 %		Físico: 5 %			
FECHA DE INICIO:	7 de Julio del 2022	FECHA DE TÉRMINO:	20 de Agosto del 2022	REGISTRO SIMA:	44	

CHEK LIST DE LOS ANEXOS DEL EXPEDIENTE TÉCNICO

CÉDULA DE REGISTRO DE OBRA	✓
DICTAMEN DE FACTIBILIDAD	✓
MEMORIA DESCRIPTIVA	✓
PRESUPUESTO BASE	✓
FACTIBILIDAD VERIFICADA EN CAMPO	✓
CROQUIS DE UBICACIÓN (MACRO)	✓
CROQUIS DE UBICACIÓN (MACRO)	✓
PROGRAMA DE OBRA Y MONTOS MENSUALES	✓
PLANOS O ESTUDIOS TÉCNICOS	✓
PADRÓN DE BENEFICIARIOS	N/A
ACTA DE ACEPTACIÓN DEL PROYECTO	N/A
DICTAMEN DE IMPACTO AMBIENTAL	N/A
CONVENIO DE CONCERTACIÓN	N/A
ACTA CONSTITUTIVA	N/A

METAS		BENEFICIARIOS		PERIODO DE EJECUCION		OBRA PROPUESTA		CLAVE SISCO
UNIDAD DE MEDIDA	CANT	TIPO DE BENEFICIARIOS	CANTIDAD	FECHA DE INICIO	FECHA DE TERMINO	CONCEPTO	JORNALES A GENERAR	
M2	4540	Personas	350	2022-07-07	2022-08-20	Sobrecarpeta Asfáltica	7744	2324

INCLUIDO EN PLAN DE DESARROLLO MUNICIPAL Y EL PROGRAMA ANUAL DE OBRA PÚBLICA

OBSERVACIONES:

SIN OBSERVACIONES

RECIBIO: ING. JOSÉ DAVID BURGUETE CLAUSTRO
Analista de Programación e Inversión de Obra Pública

17 de Octubre del 2022
Fecha de validación

17 de Octubre del 2022
Fecha de validación Expediente

PROCEDE Si ✓ No

H. AYUNTAMIENTO CONSTITUCIONAL DEL MUNICIPIO DE AGUASCALIENTES 2021-2024

AYUNTAMIENTO DE AGUASCALIENTES

CEDULA DE REGISTRO POR OBRA

Aguascalientes

050400-001E00E05-05-2-2-1-00-1-E-0510-0-17-0044-21-2502-6144

2022-FISMDF-0044-0411102-015	Obra **SOBRECARPETA ASFÁLTICA AV. PETRÓLEOS MEXICANOS**
Tipo DEFINITIVO 1 2022 Folio SISCO **2324**	Ubic. TRAMO: ENTRE CALLE IGNACIO ZARAGOZA Y CALLE AQUILES SERDÁN, CENTRO Zona , Deleg. Zona Centro

Ent. Ejecutora : **050400001E00E05**

Eje: **05**	MUNICIPIO SOBRESALIENTE
Finalidad: **2**	DESARROLLO SOCIAL
Función: **2**	VIVIENDA Y SERVICIOS A LA COMUNIDAD
Subfunción: **1**	URBANIZACIÓN
Tema: **00**	SIN TEMA
Cuenta del Gasto **1**	GASTO PROGRAMABLE
Clasif. Programatica: **E**	PRESTACIÓN DE SERVICIOS PÚBLICOS
Programa: **0510**	Movilidad Urbana
SubPrograma: **0**	SUBPROGRAMA GENÉRICO
Proyecto: **17**	
Tipo de Gasto: **21**	GASTO INVERSIÓN / OBRA PÚBLICA

I N V E R S I O N 2022

Municipal	2502	FONDO PARA LA INFRAESTRUCTURA SOCIAL MUNICIPAL Y DE LAS DEMARCACIONES TERRITORIALES DEL DISTRITO FEDERAL 2022	$2,978,592.33

Folio SIMA 44 Total $2,978,592.33

M E T A S

Unidad de Medida	Cantidad	Descripción
M2	4540	OBRA SOBRECARPETA ASFÁLTICA AV. PETRÓLEOS MEXICANOS

Inversión Ejercida Total al 31 de Diciembre de 2021 $0.00

Avance Fisico Acumulado al 31 de Diciembre de 2021

Avance Fisico Acumulado Programado al 31 de Diciembre de 2022 100 %

Fecha de Inicio 07 Jul 2022 Fecha de Terminación 20 Ago 2022

Jornales a Generar en 2022 7744

Modalidad de ejecución CONTRATO

Clasificación de la Obra Bienes de Dominio Público

Registro del Patrimonio: Obras del dominio público

OBRAS PÚBLICAS

Av. Aguascalientes Sur No. 2615
Fracc. Jardines de las Fuentes,
Aguascalientes, Ags. C.P. 20278

(449) 9 78 92 01, 06, 09

www.ags.gob.mx

GENERALES

Nombre del Proyecto : SOBRECARPETA ASFÁLTICA AV. PETRÓLEOS MEXICANOS

TRAMO: ENTRE CALLE IGNACIO ZARAGOZA Y CALLE AQUILES SERDÁN, CENTRO Zona , Deleg. Zona Centro

Programa : 04 URBANIZACION MUNICIPAL

Subprograma : 11 Calles y caminos (422.- Rehabilitación: 0411202- Concreto Asfáltico)

Clave del Municipio : AGUASCALIENTES

Localidad :

Barrio, Colonia o Ejido : CENTRO Zona

Tipo de Obra : NUEVA

DESCRIPCIÓN DEL PROYECTO:

SOBRECARPETA ASFÁLTICA AV. PETRÓLEOS MEXICANOS

PRELIMINARES Y DEMOLICIONES 207.00 M3
BACHEO PROFUNDO 8.05 Y 0.71 M3
SOBRECARPETA ASFÁLTICA 4,540.00 M2
OBRA COMPLEMENTARIA 1.00 OBRA
LIMPIEZAS 4,565.83 M2
GUARNICIONES Y/O DENTELLONES DE CONCRETO 51.5 ML
BANQUETA Y RAMPA 13.23 y 16.85 M2
EXTRAORDINARIOS 1.0 OBRA

Beneficiarios (No. y Tipo) :

350	PERSONAS

No. Folio SISCO 2324

Los abajo firmantes, hacen constar que el presente proyecto :

SOBRECARPETA ASFÁLTICA AV. PETRÓLEOS MEXICANOS

TRAMO: ENTRE CALLE IGNACIO ZARAGOZA Y CALLE AQUILES SERDÁN, CENTRO Zona , Deleg. Zona Centro

cumple con los Requisitos y Normas Técnicas establecidas por la Dependencia Normativa, por lo que es viable su ejecución. Comprometiéndose la misma a proporcionar la supervisión y asistencia técnica necesaria durante el proceso administrativo.

Por la Dependencia Ejecutora

Arq. Gloria Guadalupe Castillo González
Encargada de Despacho de la Secretaría de Obras Públicas

Lic. Jaime Gallo Camacho
Secretario de Desarrollo Urbano

LUGAR :AGUASCALIENTES, AGS.

Av. Aguascalientes Sur No. 2615
Fracc. Jardines de las Fuentes,
Aguascalientes, Ags. C.P. 20278

(449) 9 78 92 01, 06, 09

www.ags.gob.mx

No. Folio SISCO 2324

H. AYUNTAMIENTO CONSTITUCIONAL DEL MUNICIPIO DE AGUASCALIENTES 2021-2024

AYUNTAMIENTO DE AGUASCALIENTES

FACTIBILIDAD VERIFICADA EN CAMPO

Aguascalientes
LA CIUDAD DE TU VIDA

MUNICIPIO: AGUASCALIENTES

LOCALIZACION: TRAMO: ENTRE CALLE IGNACIO ZARAGOZA Y CALLE AQUILES SERDÁN, CENTRO Zona , Deleg. Zona Centro

PROGRAMA: URBANIZACION MUNICIPAL

SUBPROGRAMA: Calles y caminos (422.- Rehabilitación: 0411202- Concreto Asfáltico)

OBRA A REALIZAR: SOBRECARPETA ASFÁLTICA AV. PETRÓLEOS MEXICANOS

DEPENDENCIA EJECUTORA: SECRETARÍA DE OBRAS PUBLICAS DEL MUNICIPIO DE AGUASCALIENTES

FORMA DE EJECUCION: CONTRATO

TIPO DE OBRA PROPUESTA: NUEVA

CONDICIONES ACTUALES DE LA OBRA:

SOBRECARPETA ASFÁLTICA AV. PETRÓLEOS MEXICANOS

CARACTERISTICAS DE LA OBRA: Bueno

FACTIBILIDAD DE LA OBRA:

ESTA OBRA SE REQUIERE PARA EL BENEFICIO DE LA CIUDADANÍA

PROCEDE: SI [X] NO [ ]

REVISÓ: Jefa del Departamento de Expedientes Tecnicos y Costos

NOMBRE: Arq. Blanca Margarita Martinez Amador

FIRMA:

FECHA: 03 Oct 2022

SECRETARÍA DE OBRAS PÚBLICAS

Av. Aguascalientes Sur No. 2615
Fracc. Jardines de las Fuentes,
Aguascalientes, Ags. C.P. 20278


(449) 9 78 92 01, 06, 09

www.ags.gob.mx

No. Folio SISCO 2324

H. AYUNTAMIENTO DE AGUASCALIENTES
SECRETARÍA DE OBRAS PÚBLICAS
DIRECCIÓN DE SUPERVISIÓN DE OBRA
UBICACIÓN

OBRA:	FISMDF-0044-2022 - SOBRECARPETA ASFÁLTICA AV. PETRÓLEOS MEXICANOS					
NO. DE CONT	FISMDF-0044-2022		CONTRATISTA:	DINAMICA ALRO, S.A. DE C.V.		

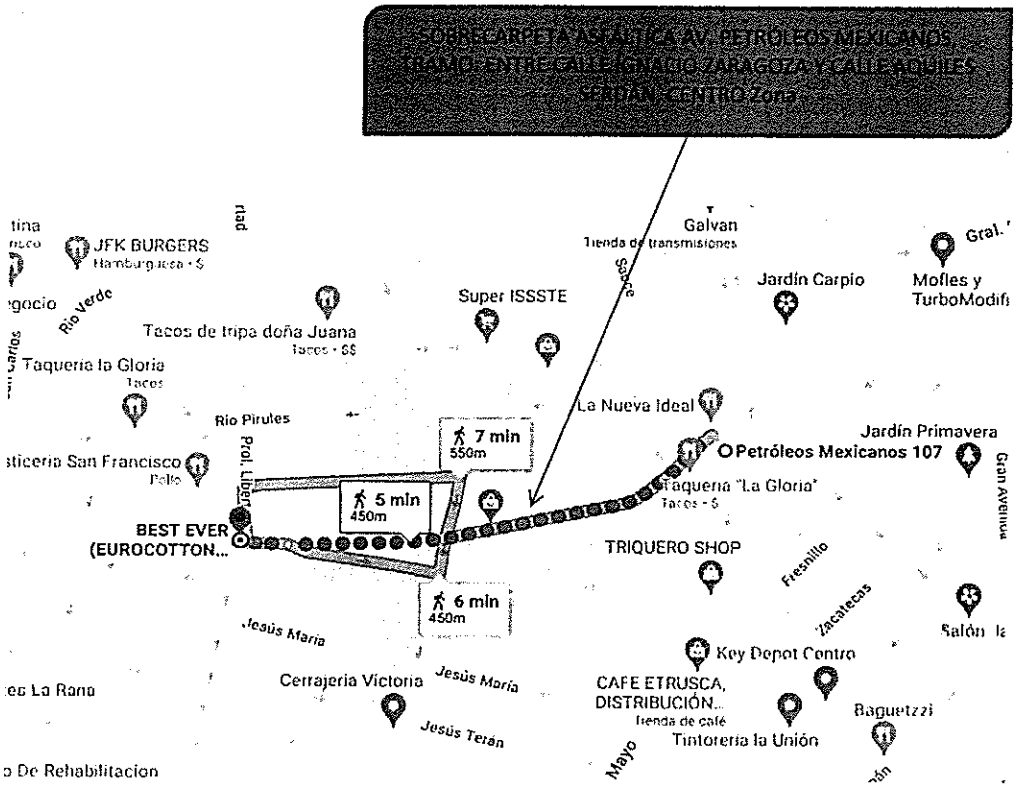


ING. RICARDO MACÍAS MERCADO
SUPERVISOR DE OBRA.

H. AYUNTAMIENTO DE AGUASCALIENTES
SECRETARÍA DE OBRAS PÚBLICAS
DIRECCIÓN DE SUPERVISIÓN DE OBRA

LOCALIZACION

OBRA:	FISMDF-0044-2022 - SOBRECARPETA ASFÁLTICA AV. PETRÓLEOS MEXICANOS					
NO. DE CONT	FISMDF-0044-2022		CONTRATISTA:	DINAMICA ALRO, S.A. DE C.V.		

SOBRECARPETA ASFÁLTICA AV. PETRÓLEOS MEXICANOS, TRAMO: ENTRE CALLE IGNACIO ZARAGOZA Y CALLE AQUILES SERDÁN, CENTRO Zona

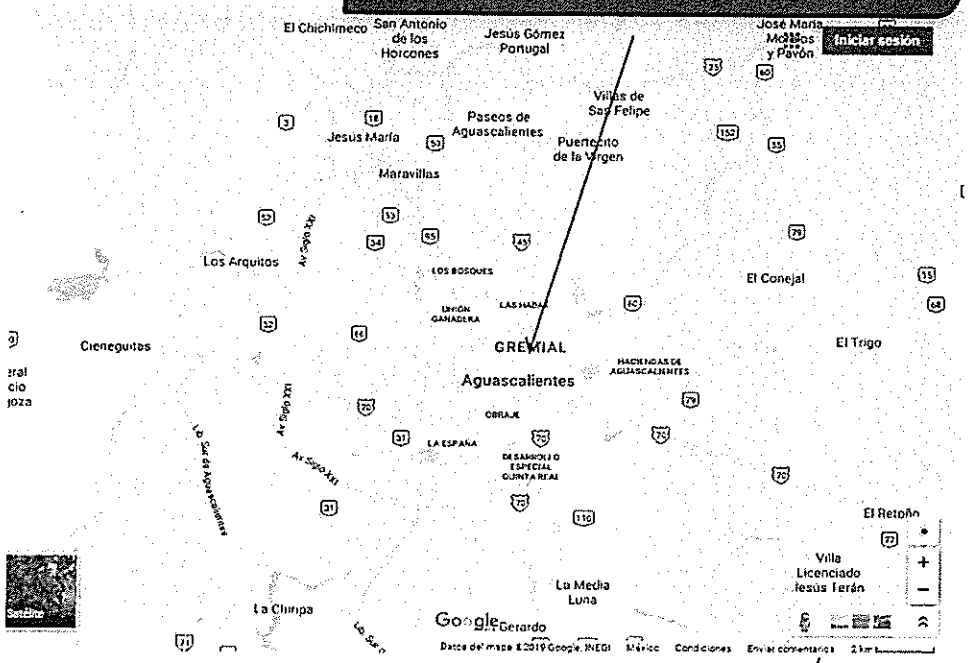

ING. RICARDO MACÍAS MERCADO
SUPERVISOR DE OBRA.

RO3-POS-SOS-7.5.1-04	
REVISION:	00
FECHA DE REVISION:	
RESPONSABLE:	SUPERVISOR DE OBRA
TIEMPO DE RET:	02 AÑOS

PROGRAMA DE OBRA DEFINITIVO

No. DE CONTRATO : FISMDF-0044-2022

PROGRAMA: 04-URBANIZACIÓN MUNICIPAL

No. OBRA Y NOMBRE DE LA OBRA: FISMDF-0044-2022 - SOBRECARPETA ASFÁLTICA AV. PETRÓLEOS MEXICANOS

INICIO VIGENTE: 07-julio-22

TERMINO REAL: 20-agosto-22

RECURSO: 2022

CONCEPTO				1	2	3	4	5	6	7	8	9	10	11	12	13	14	15	16	PONDERACIÓN %	
				2022																FINANCIERO	FÍSICO
				ENERO	FEBRERO	MARZO	ABRIL	MAYO	JUNIO	JULIO 07-jul	AGOSTO 20-ago	SEPTIEMBRE	OCTUBRE	NOVIEMBRE	DICIEMBRE					%	%
DESCRIPCION	INVERSION																				
FISMDF-0044-2022 - SOBRECARPETA ASFALTICA AV. PETROLEOS MEXICANOS																					
TRAMO: ENTRE CALLE IGNACIO ZARAGOZA Y CALLE AQUILES SERDAN, CENTRO 2mts																					
PRELIMINARES	$ 246,383.40	100								50	50									9.67	14.29
BACHEO PROFUNDO	$ 18,154.16	100								70	30									0.71	14.29
SOBRECARPETA ASFALTICA	$ 2,046,823.45	100								65	35									78.70	14.29
OBRA COMPLEMENTARIA	$ 189,213.98	100									80	20								7.37	14.29
LIMPIEZAS	$ 30,408.43	100										100								1.18	7.14
GUARNICIONES Y/O	$ 20,279.16	100								40	60									0.79	14.29
BANQUETA Y RAMPA	$ 17,915.38	100									50	50								0.70	14.29
EXTRAORDINARIO	-$ 3,225.94	100										100								-0.13	7.14
SUBTOTAL SIN IVA	$ 2,567,752.01	$ 14.00		0	0	0	0	0	0	2	4	2	2	2	0	0	0	0	0		
AVANCE SEMANAL %				0%	0%	0%	0%	0%	0%	1%	2%	1%	1%	1%	0%	0%	0%	0%	0%		
AVANCE SEMANAL ACUMULADO %				0%	0%	0%	0%	0%	0%	1%	3%	4%	5%	6%	6%	6%	6%	6%	6%	100.00	100.00
EJERCIDO SEMANAL $										132,303.35	182,320.87										
										1,799,365.66	49,853.43										
										414,770.04	27,182.49										
EJERCIDO MENSUAL $				$0.00	$0.00	$0.00	$0.00	$0.00	$0.00	$2,333,440.17	$234,311.84	$0.00	$0.00	$0.00	$0.00	$0.00	$0.00	$0.00	$0.00	$	2,567,752.01
EJERCIDO MENSUAL ACUMULADO $				0.00	0.00	0.00	0.00	0.00	0.00	2,333,440.17	2,567,752.01	2,567,752.01	2,567,752.01	2,567,752.01	2,567,752.01	2,567,752.01	2,567,752.01	2,567,752.01	2,567,752.01	$	410,840.32 IVA 6%
EJERCIDO SEMANAL %				0%	0%	0%	0%	0%	0%	5%	1%	0%	0%	0%	0%	0%	0%	0%	0%		
EJERCIDO MENSUAL %				0%	0%	0%	0%	0%	0%	91%	9%	0%	0%	0%	0%	0%	0%	0%	0%	GRAN TOTRAL EJERCIDO	
EJERCIDO MENSUAL ACUMULADO %				0%	0%	0%	0%	0%	0%	91%	100%	100%	100%	100%	100%	100%	100%	100%	100%	$	2,978,592.33

ING. RICARDO MACÍAS MERCADO
SUPERVISOR

PRESIDENCIA MUNICIPAL DE AGUASCALIENTES

FACTIBILIDAD VERIFICADA EN CAMPO

GENERALES

EJERCICIO: 2022 APROBACION No: 2022-FISMDF-0044-0411102-015
LOCALIDAD: TRAMO: ENTRE CALLE IGNACIO ZARAGOZA Y CALLE AQUILES SERDÁN, CENTRO Zona
MUNICIPIO: AGUASCALIENTES, AGS
TIPO DE INVERSION: FONDO PARA LA INFRAESTRUCTURA SOCIAL MUNICIPAL Y DE LAS DEMARCACIONES TERRITORIALES DEL DISTRITO FEDERAL

PROGRAMA: 04-URBANIZACIÓN MUNICIPAL

SUB-PROGRAMA: 11-CALLES Y CAMINOS, REHABILITACIÓN:0411202-CONCRETO ASFÁLTICO

OBRA A REALIZARSE:
FISMDF-0044-2022 - SOBRECARPETA ASFÁLTICA AV. PETRÓLEOS MEXICANOS

DEPENDENCIA EJECUTORA: SECRETARÍA DE OBRAS PÚBLICAS MUNICIPALES (S.O.P.M.A)
FORMACIÓN DE EJECUCION: CONTRATO NO. DE CONTRATO: FISMDF-0044-2022
NOMBRE CONTRATISTA: DINAMICA ALRO, S.A. DE C.V.
REPRESENTANTE: LUIS ÁNGEL BRUN TOLEDO
MONTO CONT. ORIGEN $2,978,633.65 ANTICIPO: $724,808.81 45 DIAS
1A AMPLIACION $: 0 1 AMPL DIAS 0
2A AMPLIACION $: 0 2 AMPL DIAS 0
FIRMA CONTRATO: 04/07/2022
INICIO CONT: dd/mm/aa 5 de julio de 2022 TERMINO CONT 18 de agosto de 2022
INICIO REAL: dd/mm/aa 7 de julio de 2022 TERMINO REAL: 20 de agosto de 2022

TIPO DE OBRA PROPUESTA

NUEVA CREACIÓN		CONSOLIDACIÓN	
COMPLEMENTARIA		AMPLIACIÓN	
REHABILITACIÓN	X	EQUIPAMIENTO	

CARACTERÍSTICAS DE LA OBRA:

SOBRECARPETA ASFÁLTICA AV. PETRÓLEOS MEXICANOS en el tramo entre Calle Ignacio Zaragoza y Calle Aquiles Serdán, se propone sea con un espesor de 5 cms., previamente tratado (fresado o demolición). Debido a que las bases de la vialidad se encuentras en buen estado (funcionables); se propone un bacheo profundo en las depresiones existentes en la vialidad, posteriormente se realizaran renivelaciones con asfalto, para colocar el riego de impregnación para el bacheo, el riego de liga con emulsión de rompimiento rapido y el tendido de carpeta asfáltica. Se renivelaran los brocales, tapas de registros y caimon existentes en la calzada.

BUEN ESTADO X REGULAR PESIMO ESTADO

FACTIBILIDAD DE LA OBRA: (CONDICIONES ACTUALES DE LA OBRA)

ESTA OBRA SE ENCUENTRA EN CONDICIONES PARA OPERARSE

PROCEDE: SI: X NO:
MARQUE SOLO UNA

ING. RICARDO MACÍAS MERCADO
SUPERVISOR

PRESIDENCIA MUNICIPAL DE AGUASCALIENTES

FACTIBILIDAD VERIFICADA EN CAMPO

GENERALES

LOCALIDAD: TRAMO: ENTRE CALLE IGNACIO ZARAGOZA Y CALLE AQUILES SERDÁN, CENTRO Zona
MUNICIPIO: AGUASCALIENTES, AGS
PROGRAMA: 04-URBANIZACIÓN MUNICIPAL
SUB-PROGRAMA: 11-CALLES Y CAMINOS, REHABILITACIÓN:0411202-CONCRETO ASFÁLTICO
OBRA A REALIZARSE: FISMDF-0044-2022 - SOBRECARPETA ASFÁLTICA AV. PETRÓLEOS MEXICANOS

DEPENDENCIA EJECUTORA: SECRETARÍA DE OBRAS PÚBLICAS MUNICIPALES (S.O.P.M.A)
FORMACIÓN DE EJECUCION: CONTRATO

TIPO DE OBRA PROPUESTA

NUEVA CREACIÓN		CONSOLIDACIÓN	
COMPLEMENTARIA		AMPLIACIÓN	
REHABILITACIÓN	X	EQUIPAMIENTO	

CARACTERÍSTICAS DE LA OBRA:

SOBRECARPETA ASFÁLTICA AV. PETRÓLEOS MEXICANOS en el tramo entre Calle Ignacio Zaragoza y Calle Aquiles Serdán, se propone sea con un espesor de 5 cms., previamente tratado (fresado o demolición). Debido a que las bases de la vialidad se encuentras en buen estado (funcionables); se propone un bacheo profundo en las depresiones existentes en la vialidad, posteriormente se realizaran renivelaciones con asfálto, para colocar el riego de impregnación para el bacheo, el riego de liga con emulsión de rompimiento rapido y el tendido de carpeta asfáltica. Se renivelaran los brocales, tapas de registros y caiman existentes en la calzada.

CONDICIONES ACTUALES DE LA OBRA:

BUEN ESTADO:	X	REGULAR:		PESIMO ESTADO:	

FACTIBILIDAD DE LA OBRA:

ESTA OBRA SE ENCUENTRA EN CONDICIONES PARA OPERARSE

PROCEDE	**SI:**	X	**NO:**	

ING. RICARDO MACÍAS MERCADO
SUPERVISOR

MUNICIPIO DE AGUASCALIENTES
SECRETARIA DE OBRA PUBLICAS MUNICIPALES
DIRECCION DE COSTOS Y LICITACION DE OBRA


CONTRATO: FISMDF-0044-2022

OBRA: SOBRECARPETA ASFÁLTICA AV. PETRÓLEOS MEXICANOS, TRAMO: ENTRE CALLE IGNACIO ZARAGOZA Y CALLE AQUILES SERDÁN, CENTRO Zona

MONTO MODIFICADO FINAL: $2,978,592.33

VOLUMEN	UNIDAD	COMPONENTE DE OBRA	MONTO	PU
4564.83	M2	LIMPIA, TRAZO, BARRIDO, CORTE CON DISCO, DEMOLICION, FRESADO, CARGA Y ACARREO DE CARPETA ASFALTICA	$ 248,383.40	$ 54.41
8.76	M3	BACHEO PORFUNDO, REPOSICION Y COMPACTACION DE BASE HIDRAULICA PARA CARPETA DE CONCRETO ASFALTICO	$ 18,154.16	$ 2,072.39
4540.00	M2	COLOCACION DE SOBRE CARPETA ASFALTICA EN CALIENTE DE GRANULOMETRIA DENSA, INCLUYE, RENIVELACIONES CON	$ 2,043,397.51	$ 450.09
9.00	PZAS	RENIVELACIONES DE TAPAS DE INFRAESTRUCTURA EXISTENTE Y TOPES DE CONCRETO ASFALTICO (POZOS,	$ 189,213.98	$ 21,023.78
4564.83	M2	LIMPIEZAS GENERAL DE OBRA A DETALLE Y DESASOLVE DE POZOS DE VISITA EN LINEAS DE ALCANTARILLADO	$ 30,408.43	$ 6.66
30.08	M2	CONSTRUCCION DE GUARNICION, BANQUETAS DE 10 CMS. DE ESPESOR, RAMPAS PARA DISCAPACITADOS Y RAMPAS	$ 38,194.53	$ 1,269.76

$ 2,567,752.01

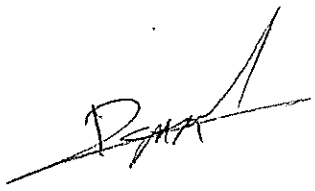

Obra: **SOBRECARPETA ASFÁLTICA AV. PETRÓLEOS MEXICANOS**

Ubicación: **TRAMO: ENTRE CALLE IGNACIO ZARAGOZA Y CALLE AQUILES SERDÁN, CENTRO Zona**

Contratista: **DINAMICA ALRO, S.A. DE C.V. (816)**

No.	Concepto	Unidad	Cantidad	Precio Unitario	Importe Total
GRUPO: **EXTRAORDINARIO**					
PARTIDA: **EXTRAORDINARIO**					
60	DEDUCTIVA POR CONCEPTO DE INDIRECTOS NO COMPROBADOS	LOTE	-3.22594	$1,000.00	-$3,225.94

Totales por Partida		**-$3,225.94**
Totales por Grupo		**-$3,225.94**
Totales Presup.		**$2,567,752.01**
Anticipo	+	**$724,808.81**
Amortizac. Ant.	-	**$724,808.81**
SubTotal. Ant.	=	**$2,567,752.01**
IVA	+	**$410,840.32**
Total	=	**$2,978,592.33**

PRESUPUESTO MODIFICADO

Obra: **SOBRECARPETA ASFÁLTICA AV. PETRÓLEOS MEXICANOS**

Ubicación: **TRAMO: ENTRE CALLE IGNACIO ZARAGOZA Y CALLE AQUILES SERDÁN, CENTRO Zona**

Contratista: **DINAMICA ALRO, S.A. DE C.V. (816)**

No.	Concepto	Unidad	Cantidad	Precio Unitario	Importe Total
	GRUPO: **PAVIMENTO ASFALTICO**				
	PARTIDA: **PRELIMINARES Y DEMOLICIONES**				
1	LIMPIA, TRAZO Y NIVELACION EN PAVIMENTOS, CALLES Y VIALIDADES CON EQUIPO TOPOGRAFICO, INCLUYE: EJES, BANCO DE NIVEL, RENIVELACIONES LAS VECES NECESARIAS, CORRECCION DE RASANTE A PUNTOS OBLIGADOS (AUTORIZADOS POR LA SUPERVISION), ESTACAS, VARILLAS, MANO DE OBRA CALIFICADA, HERRAMIENTA NECESARIA, EQUIPO DE PRECISION CALIBRADO, TRABAJO TERMINADO.P.U.O.T.	M2	4564.83	$6.42	$29,306.21
3	CORTE CON DISCO DIAMANTADO DE 14" EN PISOS DE CONCRETO ASFALTICO DE HASTA 8.00 cm. DE PROFUNDIDAD. INCLUYE: TRAZO, EQUIPO Y OPERACION, LIMPIEZAS.	ML	50.02	$43.01	$2,151.36
4	DEMOLICION PARCIAL DE PAVIMENTO HIDRAULICO Y/O ASFALTICO DE HASTA 15 CM. DE ESPESOR PROMEDIO EN PAVIMENTOS Y (BANQUETAS, LOSAS DIAMANTE Y CAJAS DE VALVULAS, TOPES) CON O SIN ARMADO DE ACERO, SIN RECUPERACION, MUROS, MOJONERAS, ANCLAJES, ETC, DE FORMA MANUAL Y MECANICA, INCLUYE ACARREO DE MATERIAL AL LUGAR DE ACOPIO, HERRAMIENTA NECESARIA Y TODO LO NECESARIO PARA SU CORRECTA EJECUCION, LIMPIEZA, TRABAJO TERMINADO	M3	5.61	$567.44	$3,183.34
5	FRESADO UNIFORME DE LA SUPERFICIE DE RODADURA EN PAVIMENTO DE CONCRETO ASFALTICO 3-7 CM (5 cm de espesor promedio) MEDIANTE FRESADORA EN FRIO COMPACTA, EQUIPADA CON BANDA TRANSPORTADORA PARA CARGA DIRECTA SOBRE CAMION DE VOLTEO, INCLUYE: TRAMO DE PRUEBA AL INICIO DEL FRESADO PARA AUTORIZACION DE SUPERVISION (SUPERFICIE FRESADA UNIFORME Y SIN PROTUBERANCIAS NI ONDEOS), ACARREOS LOCALES, CARGA Y ACARREO A KM SUBSECUENTES (11 A 15 KM APROX) DE MATERIAL PRODUCTO DEL FRESADO DE CARPETA ASFALTICA EL TRASLADO SERA A PARQUE DE MAQUINARIA DE LA SOPMA, PIEZAS DE DESGASTE, COMBUSTIBLES, CONSUMIBLES, MANO DE OBRA, CUALQUIER VOLUMEN Y AREA,EQUIPO NECESARIO, LIMPIEZA FINA Y GRUESA, TRABAJO TERMINADO.	M3	207	$938.64	$194,298.48
7	DEMOLICION CONTROLADA DE CONCRETO HIDRAULICO EN DENTELLONES Y GUARNICIONES DE 15 x 20 x 40 CM. DE FORMA MANUAL Y MECÁNICA, INCLUYE: CORTES CON DISCO, ACARREO DEL MATERIAL AL LUGAR DE ACOPIO PARA SU CARGA Y ACARREO FUERA DE LA OBRA.	ML	69.52	$256.24	$17,813.81
8	CARGA MECANICA Y ACARREO DE MATERIAL PRODUCTO DE EXCAVACION Y DEMOLICION EN CAMION DE VOLTEO AL 1er. KM, VOLUMEN MEDIDO COMPACTO.	M3	6.81	$37.10	$252.65
9	ACARREO DE MATERIAL PRODUCTO DE EXCAVACION Y/O DEMOLICION EN CAMION DE VOLTEO A KILOMETROS SUBSECUENTES, AL TIRADERO OFICIAL AUTORIZADO MAS CERCANO AUTORIZADO POR LA SUPERVISION, VOLUMEN MEDIDO COMPACTO.	M3-KM	168.2	$8.19	$1,377.56
				Totales por Partida	**$248,383.40**
	PARTIDA: **BACHEO PROFUNDO**				
10	BACHEO PROFUNDO AISLADO UTILIZANDO MATERIAL CALIDAD BASE HIDRAULICA PARA MAS DE UN MILLON DE EJES EQUIVALENTES DEL BANCO QUE ELIJA EL CONTRATISTA, INCISO N.CSV.CAR.1.02.004/03 DE LAS NORMAS DE CONSTRUCCION DE CARR. DE LA SCT, INCLUYE: PREPARACION, PERFILADO, MATERIALES, MANO DE OBRA, HERRAMIENTA MENOR Y EQUIPO NECESARIO QUE SE REQUIERA PARA LOGRAR LA COMPACTACION DE 100% PVSM, ACARREOS DENTRO Y FUERA DE LA OBRA, PREPARACION DE MATERIAL, HUMEDECIDO, NIVELADO, TRASLADO DE UN PUNTO A OTRO DENTRO DE LA OBRA, EN CUALQUIER VOLUMEN, MOVIMIENTO DE MAQUINARIA P.U.O.T	M3	8.05	$2,060.43	$16,586.46

Obra: **SOBRECARPETA ASFÁLTICA AV. PETRÓLEOS MEXICANOS**

Ubicación: **TRAMO: ENTRE CALLE IGNACIO ZARAGOZA Y CALLE AQUILES SERDÁN, CENTRO Zona**

Contratista: **DINAMICA ALRO, S.A. DE C.V. (816)**

No.	Concepto	Unidad	Cantidad	Precio Unitario	Importe Total
	GRUPO: **PAVIMENTO ASFALTICO**				
	PARTIDA: **BACHEO PROFUNDO**				
11	BACHEO PROFUNDO AISLADO UTILIZANDO MATERIAL CALIDAD BASE HIDRAULICA PARA MAS DE UN MILLON DE EJES EQUIVALENTES DEL BANCO QUE ELIJA EL CONTRATISTA, INCISO N.CSV.CAR-1.02.004/03 DE LAS NORMAS DE CONSTRUCCION DE CARR. DE LA SCT, BASE HIDRAULICA MEJORADA CON CEMENTO EN PROPORCION DE 40 KILOS DE CEMENTO POR CADA M3, INCLUYE: PREPARACION, PERFILADO, MATERIALES, MANO DE OBRA, HERRAMIENTA MENOR Y EQUIPO NECESARIO QUE SE REQUIERA PARA LOGRAR LA COMPACTACION DE 100 %, PVSM, ACARREOS DENTRO Y FUERA DE LA OBRA, PREPARACION DE MATERIAL, HUMEDECIDO, NIVELADO, TRASLADO DE UN PUNTO A OTRO DENTRO DE LA OBRA EN CUALQUIER VOLUMEN, MOVIMIENTO DE MAQUINARIA P.U.O.T	M3	0.71	$2,208.03	$1,567.70
			Totales por Partida		**$18,154.16**
	PARTIDA: **SOBRE CARPETA ASFALTICA**				
13	PREPARACIÓN DE LA SUPERFICIE DE CONTACTO EN LOS EXTREMOS DONDE LA PERFILADORA NO ALCANCE POR LÍMITES CON LA GUARNICIÓN, CON UN RASPADO SUPERFICIAL CON RETROEXCAVADORA, ELIMINANDO TECATAS QUE HAYAN QUEDADO PARA RENIVELADO, BARRIDOS ENTRE PASADA DE MOTOCONFORMADORA Y EN REMATES DE EMPATES A DETALLE A MANO, INCLUYE: RETIRO DE MATERIAL FUERA DE LA OBRA A TIRADERO OFICIAL INDICADO.	M2	53.12	$96.75	$5,139.36
14	RENIVELACIONES CON CONCRETO ASFALTICO MEZCLA EN PLANTA EN CALIENTE ASFALTO MODIFICADO CON POLIMERO TIPO I, CUMPLIENDO LAS NORMAS SCT REFERENTES DE CONSTRUCCCION Y CONSERVACION, GRANULOMETRIA DENSA 3/4" A FINOS, MEDIDO COMPACTO AL NOVENTA Y CINCO PORCIENTO (95%), INCLUYE CARGA Y ACARREO EN TRAMOS AISLADOS, MATERIALES, MANO DE OBRA, ACARREO DE MATERIALES, Y MAQUINARIA Y EQUIPO AL SIGUIENTE PUNTO EN CUALQUIER VOLUEN, PERFILADO, LIMPIEZA DE HUESO Y GRAVA SUELTA, TRABAJO TERMINADO P.U.O.T	M3	126.92	$5,342.25	$678,038.37
16	RIEGO DE IMPREGNACION CON EMULSION DE ROMPIMIENTO LENTO (ECL-60 %), INCLUYE BARRIDO DE LA SUPERFICIE, LIMPIEZA A DETALLE, SUMINISTRO, ALMACENAMIENTO, CALENTAMIENTO, Y APLICACION DE LA EMULSION CON EQUIPO ESPECIAL PARA ESA ACTIVIDAD, ESPREAS LIMPIAS Y ALINEADAS, EN CASO DE RECOMENDARLO EL LABORATORIO DE CALIDAD DEL CONTRATISTA SE DEBERÁ DAR UN RIEGO MATAPOLVO ANTES DE COLOCAR LA CAPA DE IMPREGNACION, A RAZON DE 1.5 LT DE EMULSION POR M2, O LO QUE INDIQUE EL LABORATORIO DE CALIDAD DEL CONTRATISTA, NO SE ACEPTAN LEVANTAMIENTO DEL RIEGO, TRABAJO TERMINADO, P.U.O.T.	M2	16.33	$34.66	$566.37
17	RIEGO DE LIGA CON EMULSION DE ROMPIMIENTO RAPIDO (ECR-65 %), INCLUYE, SUMINISTRO, ALMACENAMIENTO, CALENTAMIENTO, Y APLICACION DE LA EMULSION CON EQUIPO ESPECIAL PARA ESA ACTIVIDAD, ESPREAS O BACHADOR LIMPIAS Y ALINEADAS, CONTROL DE CALIDAD A CADA DOS REMESAS EN OBRA (INDEPENDIENTEMENTE DE LA CANTIDAD A UTILIZAR) EN LA PETROLIZADORA, A RAZON DE 0.8 LT DE EMULSION POR M2, O LO QUE INDIQUE EL LABORATORIO DE CALIDAD DEL CONTRATISTA, NO SE ACEPTAN "IMPREGNALIGA", TRABAJO TERMINADO, P.U.O.T.	M2	8687.6	$18.80	$163,326.88

Obra: **SOBRECARPETA ASFÁLTICA AV. PETRÓLEOS MEXICANOS**

Ubicación: **TRAMO: ENTRE CALLE IGNACIO ZARAGOZA Y CALLE AQUILES SERDÁN, CENTRO Zona**

Contratista: **DINAMICA ALRO, S.A. DE C.V. (816)**

No.	Concepto	Unidad	Cantidad	Precio Unitario	Importe Total
	GRUPO: **PAVIMENTO ASFALTICO**				
	PARTIDA: **SOBRE CARPETA ASFALTICA**				
18	SUMINISTRO Y COLOCACION DE CONCRETO ASFALTICO EN CALIENTE DE GRANULOMETRIA DENSA ELABORADA CON ASFALTO MODIFICADO TIPO I, AGREGADO 3/4" A FINOS, DE 5 CM DE ESPESOR, FORMADA Y COMPACTADO AL 95%, INCLUYE MATERIALES, QUE CUMPLAN LA NORMATIVA SCT-N-CMT-04-04, SCT-CMT-4-05-002, SCT-CMT-4-05-003, SCT-CMT-4-05-004, SCT-CTR-CAR-1-04-006-14 APLICADAS AL DIA DE HOY, DISEÑO MARSHALL (DEVERÁ SER AUTORIZADO POR EL LABORATORIO DE CALIDAD DE SOPMA AL MENOS 3 DIAS ANTES DE INICIO DE TENDIDO DE LA MEZCLA ASFALTICA), INCUYE: TRAMO DE PRUEBA AL INICIO PARA REVISION Y AUTORIZACION DEL ESPESOR POR PARTE DEL SUPERVISOR, EL CONTRATISTA DEBERÁ PREVEER EL SUMINISTRO Y TIEMPOS MUERTOS POR MOVIMIENTOS DEL TREN DE MAQUINAS DE TRABAJO EN TRAMOS AISLADOS. TRABAJO TERMINADO P.U.O.T. Y LIMPIEZAS DE GRANZON Y HUESO LATERAL.	M2	4540	$256.46	$1,164,328.40
19	COMPACTACION SOBRE MORTERO ASFALTICO TENDIDO EN APROCHES CON GUARNICIONES CON EQUIPO LIGERO (PLANCHITA), INCLUYE: MANO DE OBRA Y EQUIPO, TRABAJO TERMINADO.	M2	310.8	$113.34	$35,226.07
			Totales por Partida		**$2,046,623.45**
	PARTIDA: **OBRA COMPLEMENTARIA**				
20	RE NIVELACIÓN DE POZO DE VISITA HASTA 30 cm DE ALTURA. INCLUYE: RETIRO SIN RECUPERACIÓN DE BROCAL EXISTENTE, DEMOLICIONES, NIVELADO CON TABIQUE ROJO RECOCIDO 7X14X28, ASENTADO CON MORTERO CEMENTO-ARENA 1:3 DE 28 cm DE ESPESOR, APLANADO CON MORTERO CEMENTO-ARENA 1:3 , PLOMEADO, NIVELADO, DEMOLICIONES, CARGAS Y ACARREOS DENTRO DE LA OBRA, LIMPIEZAS Y TODO LO NECESARIO PARA SU CORRECTA EJECUCIÓN DEL CONCEPTO.	PZA	6	$4,641.61	$27,849.66
21	CONSTRUCCION DE LOSA DE DIAMANTE DE CONCRETO MR= 45 , T.M.A. DE 3/4" (19MM), GRAVA TRITURADA, REVENIMIENTO DE 8+-2.5CM CM, FRAGUADO RAPIDOA A 3 DIAS, DE 25 CM DE ESPESOR, EN POZO DE VISITA, Y 1.50 M POR LADO, INCLUYE: SUMINISTRO DE MATERIALES, ESPUMA DE POLIURETANO DE ALTA DENSIDAD EN TODO EL PERIMETRO EXTERIOR DE 1/2" ASI COMO DE LAS JUNTAS DIAGONALES PARA FORMAR 4 PARTES, BROCAL Y TAPA DE Fo. Fo. TIPO PESADO, (165 KG), CIMBRADO, COLADO, VIBRADO, DESCIMBRADO, CURADO CON MEMBRANA QUIMICA BASE AGUA, APLANADO FINO EN RECEPCION DE BROCAL, CORTES CON CORTADORA DE DISCO DE 5 CM ENTRE JUNTAS DIAGONALES FORMADO 8 PIEZAS Y SELLADO DE JUNTAS Y CORTES CON MATERIAL PREFORMADO Y SELLADOR AUTONIVELANTE, MANO DE OBRA, ACARREOS DE MATERIAL DENTRO Y FUERA DE LA OBRA, TRABAJO TERMINADO. P.U.O.T.	PZA	6	$10,009.60	$60,057.60
22	LIMPIEZA Y DESASOLVE DE POZOS DE VISITA Y LINEAS DE ALCANTARILLADO EXISTENTE CON CAMION TIPO VACTOR. INCLUYE: RESANE INTERIOR DEL POZO Y REMTE DE POZO CO TUBO CON SELLADOR, FESTER Y MORTERO 1:3, MANO DE OBRA, SUMINISTRO DE AGUA EN PIPA, HERRAMIENTAS Y EQUIPO PARA SU CORRECTA EJECUCION, LIMPIEZAS, RENTA DE CAMION VACTOR HASTA LA CORRECTA LIMPIEZA DE LAS LINEAS EXISTENTES DE POZO A POZO, ASI COMO EL TRASLADO DE LOS DESECHOS HASTA TIRADERO AUTORIZADO MEDIDO POZO A POZO.	LOTE	1	$13,278.23	$13,278.23

Obra: **SOBRECARPETA ASFÁLTICA AV. PETRÓLEOS MEXICANOS**

Ubicación: **TRAMO: ENTRE CALLE IGNACIO ZARAGOZA Y CALLE AQUILES SERDÁN, CENTRO Zona**

Contratista: **DINAMICA ALRO, S.A. DE C.V. (816)**

No.	Concepto	Unidad	Cantidad	Precio Unitario	Importe Total
	GRUPO: **PAVIMENTO ASFALTICO**				
	PARTIDA: **OBRA COMPLEMENTARIA**				
24	RENIVELACIÓN DE RASANTE (PARTE SUPERIOR) DE CAJA DE VÁLVULAS TIPO 3 DE HASTA 1.96 X 1. 75 MTS, NIVELADO HASTA UNA ALTURA MAXIMA DE 10 CM, Y MINIMA DE 5 CM. MEDIDAS INTERIORES INCLUYE: TRAZO, EXCAVACIÓN, NIVELACIÓN, PREPARACIONES , Y DEMOLICIONES, RETIRO SIN RECUPERACIÓN DE TAPA DE FOFO EXISTENTE, MURO DE TABIQUE ROJO RECOCIDO COMÚN 7X14X28 CM DE 14 CM DE ESPESOR, JUNTEADO CON MORTERO CEMENTO-ARENA 1:3 APLANADO INTERIOR CON MORTERO CEMENTO ARENA 1:3 DE 2.00 CM DE ESPESOR ACABADO PULIDO, LOSA DE CONCRETO F´C= 250 KG/CM2 T.M.A. 19 MM DE 15 CM DE ESPESOR ARMADA CON VRS No. 3 @15 cm EN AMBOS SENTIDOS, CONTRAMARCO SENCILLO DE CANAL FoFo DE 100 mm, CONTRAMARCO CON TAPA DE FOFO, TIPO PESADO DE 50X50 CM, DEMOLICIÓN Y RECONSTRUCCIÓN DE APROCHES, CARGA Y ACARREOS DENTRO DE LA OBRA, CIMBRADO, DESCIMBRADO, COLADO, VIBRADO, LIMPIEZA PREVIA, FINAL, Y TODO LO NECESARIO PARA LA CORRECTA EJECUCIÓN DEL CONCEPTO. PZA 2.00	PZA	2	$16,033.51	$32,067.02
26	RENIVELACION DE DE RASANTE (PARTE SUPERIOR) CAIMAN SECCION MAX DE HASTA 10.20 X 1.00 MTS Y MINIMA 10.00 X 0.90 MTS NIVELADO HASTA 0.10 m DE ALTURA. INCLUYE: DESMONTAJE, RETIRO DE REJILLA, CONSERVACIÓN DE LA MISMA PARA RECOLOCACIÓN POSTERIOR, DEMOLICIONES NECESARIAS, NIVELADO CON TABIQUE COMUN, ASENTADO EN 28CM CON MORTERO CEMENTO-ARENA 1:3 DE ESPESOR, APLANADO CON MORTERO CEMENTO-ARENA 1:3, ANCLAJES, Y TRASLAPES EN CASTILLOS SECCION 28 X 28 CM ARMADO CON 8 VRS DEL No. 3 ESTRIBOS DEL No. 2 @ 15 CM CONCRETO F´C 250 KG/CM2 T.M.A. 1 1/2", DALA DE REMATE SECCION 30X30CM ARMADO CON 7 VRS DEL No. 3 ESTRIBOS DEL No. 2@ 15CM CONCRETO F´C 250 KG/CM2 T.M.A. 1 1/2", CIMBRADO, DESCIMBRADO, COLADO Y VIBRADO, CURADO CON MEMPBRANA BASE AGUA, COLOCACION DE REJILLA, MARCO Y/O CONTRAMARCO , TRABAJOS DE TALLER PARA AJUSTES, PLOMEADO, NIVELADO, RECONSTRUCCIÓN DE APROCHES, DEMOLICIONES, CARGAS Y ACARREOS DENTRO DE LA OBRA, LIMPIEZAS, Y TODO LO NECESARIO PARA SU CORRECTA EJECUCIÓN DEL CONCEPTO.	PZA	1	$47,313.66	$47,313.66
27	LIMPIEZA Y DESASOLVE DE CAIMANES SECCIÓN MAXIMA DE HASTA 10.20 x 1.00 mts Y MINIMA 10.00 X 0.90 MTS, INCLUYE: MANO DE OBRA, SUMINISTRO DE AGUA EN PIPA, HERRAMIENTAS Y EQUIPO PARA SU CORRECTA EJECUCION, LIMPIEZAS MANUALES, CARGAS Y ACARREOS LOCALES ASI COMO RETIRO DE MATERIAL PRODUCTO DEL DESASOLVE A TIRADERO AUTORIZADO.	PZA	1	$8,64 / 81	$8,64 / 81
			Totales por Partida		**$189,213.98**
	PARTIDA: **LIMPIEZAS**				
28	LIMPIEZA GENERAL DE LA OBRA, INCLUYE: BARRIDO, CARGA, ACARREOS Y RETIRO DE ESCOMBROS FUERA DE LA OBRA, TRABAJO TERMINADO.	M2	4565.83	$6.66	$30,408.43
			Totales por Partida		**$30,408.43**

Obra: **SOBRECARPETA ASFÁLTICA AV. PETRÓLEOS MEXICANOS**

Ubicación: **TRAMO: ENTRE CALLE IGNACIO ZARAGOZA Y CALLE AQUILES SERDÁN, CENTRO Zona**

Contratista: **DINAMICA ALRO, S.A. DE C.V. (816)**

No.	Concepto	Unidad	Cantidad	Precio Unitario	Importe Total
	GRUPO: **PAVIMENTO ASFALTICO**				
	PARTIDA: **GUARNICIONES Y/O DENTELLONES DE CONCRETO**				
31	CONSTRUCCION DE GUARNICION Y/O DENTELLON, RECTA Y/O CURVA TRAPEZOIDAL 15-20X40 CM DE SECCION CON CONCRETO PREMEZCLADO MR=38 KGF/CM2, R.N.REVENIMIENTO DE 8 A 10 CM, T.M.A. 3/4" (19 MM), GRAVA TRITURADA, ACABADO PULIDO EN PARTE DE SUPERIOR Y DOBLADOR EN ARISTAS, INCLUYE: COMPACTADO DE PLANTILLA, CIMBRADO, COLADO, VIBRADO, ACABADO, DESCIMBRADO, ALINEADO, NIVELADO, Y CURADO EN SU PARTE SUPERIOR CON MEMBRANA BASE AGUA A RAZON DE 1 LTO/M2, SEGUN FICHA TECNICA 204	ML	51.5	$393.77	$20,279.15
			Totales por Partida		**$20,279.15**
	PARTIDA: **BANQUETA Y RAMPA**				
35	LIMPIA, TRAZO Y NIVELACION EN PAVIMENTOS, CALLES Y VIALIDADES CON EQUIPO TOPOGRAFICO, INCLUYE: EJES, BANCO DE NIVEL, RENIVELACIONES LAS VECES NECESARIAS, CORRECCION DE RASANTE A PUNTOS OBLIGADOS (AUTORIZADOS POR LA SUPERVISION), ESTACAS, VARILLAS, MANO DE OBRA CALIFICADA, HERRAMIENTA NECESARIA, EQUIPO DE PRECISION CALIBRADO, TRABAJO TERMINADO.P.U.O.T.	M2	24.23	$6.42	$155.56
39	COMPACTACION POR MEDIOS MECANICOS DE TERRENO NATURAL AL 90% DE SU PVSM EN UN ESPESOR DE 20 CM , INCLUYE: ESCARIFICADO, MANIOBRAS, HUMEDECIDO, SELECCION DE MATERIAL, ACARREOS DENTRO DE LA OBRA, MEDIDO COMPACTO, LIMPIEZAS Y TODO LO NECESARIO PARA SU CORRECTA APLICACION, TRABAJO TERMINADO.	M2	25.01	$154.02	$3,852.04
42	CONSTRUCCION DE BANQUETA DE 10 CM DE ESPESOR A BASE DE CONCRETO PREMEZCLADO F'C=150 KG/CM2, T.M.A. 3/4", R.N. GRAVA TRITURADA, REVENIMIENTI DE 10+-2 CM, ACABADO RAYADO FINO CON BROCHA DE PELO, JUNTAS FRIAS CON DOBLADOR DE 2" SECCION DE LOSAS COMO INDIQUE PROYECTO, INCLUYE: JUNTA A BASE DE ESPUMA DE POLIETILENO DE CELDAS CERRADAS DE 1/2" EN JUNTAS FRIAS LONGITUDINALES CON MUROS Y TRANSVERSALES DEL ELEMENTO, ASI COMO SU UNION CON ELEMENTOS VIEJOS O CAMBIO DE ELEMENTO, CIMBRADO, COLADO, DESCIMBRADO, CORTES CON CORTADORA DE DISCO, SELLADO DE CORTES CON SELLADOR AUTONIVELANTE Y TIRA DE RELLENO PREFORMADA NO ADHERENTE DE 1/8" (EN TODAS LAS JUNTAS DE CONTRACCCION Y CONSTRUCCION TRANSVERSALES), CURADO CON MEMBRANA QUIMICA APLICADA CON ASPERSOR, TRABAJO TERMINADO	M2	13.23	$406.46	$5,377.47
43	CONSTRUCCION DE RAMPA Y BANQUETA DE USO HABITACIONAL PARA TRAFICO VEHICULAR, DE 12 CM DE ESPESOR A BASE DE CONCRETO PREMEZCLADO MR=38 KGF/CM2, T.M.A. 1 1/2", R.R 7 DIAS. GRAVA TRITURADA, REVENIMIENTI DE 10+-2 CM, ACABADO RAYADO FINO CON BROCHA DE PELO, JUNTAS FRIAS CON DOBLADOR DE 2" SECCION DE LOSAS COMO INDIQUE PROYECTO, INCLUYE: JUNTA DE AISLAMIENTO Y DE EXPANSION A BASE DE ESPUMA DE POLIETILENO DE CELDAS CERRADAS DE 1/2" EN JUNTAS FRIAS LONGITUDINALES CON MUROS Y TRANSVERSALES DEL ELEMENTO, ASI COMO SU UNION CON ELEMENTOS VIEJOS O CAMBIO DE ELEMENTO, CIMBRADO, COLADO, DESCIMBRADO, CORTES CON CORTADORA DE DISCO, SELLADO DE CORTES CON SELLADOR AUTONIVELANTE Y TIRA DE RELLENO PREFORMADA NO ADHERENTE DE 1/8" (EN TODAS LAS JUNTAS DE CONTRACCCION Y CONSTRUCCION TRANSVERSALES), CURADO CON MEMBRANA QUIMICA APLICADA CON ASPERSOR, TRABAJO TERMINADO FICHA TECNICA 216	M2	16.85	$506.25	$8,530.31
			Totales por Partida		**$17,915.38**
			Totales por Grupo		**$2,570,977.95**

PRESUPUESTO MODIFICADO

Obra: **SOBRECARPETA ASFÁLTICA AV. PETRÓLEOS MEXICANOS**

Ubicación: **TRAMO: ENTRE CALLE IGNACIO ZARAGOZA Y CALLE AQUILES SERDÁN, CENTRO Zona**

Contratista: **DINAMICA ALRO, S.A. DE C.V. (816)**

Grupo	Partida	Importe
PAVIMENTO ASFALTICO		
	PRELIMINARES Y DEMOLICIONES	$248,383.40
	BACHEO PROFUNDO	$18,154.16
	SOBRE CARPETA ASFALTICA	$2,046,623.45
	OBRA COMPLEMENTARIA	$189,213.98
	LIMPIEZAS	$30,408.43
	GUARNICIONES Y/O DENTELLONES DE CONCRETO	$20,279.15
	BANQUETA Y RAMPA	$17,915.38
	Subtotal por Grupo	**$2,570,977.95**
EXTRAORDINARIO		
	EXTRAORDINARIO	-$3,225.94
	Subtotal por Grupo	**-$3,225.94**

Totales Presup.		**$2,567,752.01**
Anticipo	+	**$724,808.81**
Amortizac. Ant.	-	**$724,808.81**
SubTotal. Ant.	=	**$2,567,752.01**
IVA	+	**$410,840.32**
Total	=	**$2,978,592.33**

H. AYUNTAMIENTO DE AGUASCALIENTES
SECRETARÍA DE OBRAS PÚBLICAS
DIRECCIÓN DE SUPERVISIÓN DE OBRA


Aguascalientes
LA CIUDAD DE TU VIDA


MEMORIA FOTOGRAFICA


OBRA:	FISMDF-0044-2022 - SOBRECARPETA ASFÁLTICA AV. PETRÓLEOS MEXICANOS					
NO. DE CONTRATO:	FISMDF-0044-2022		CONTRATISTA:	DINAMICA ALRO, S.A. DE C.V.		

INICIO.



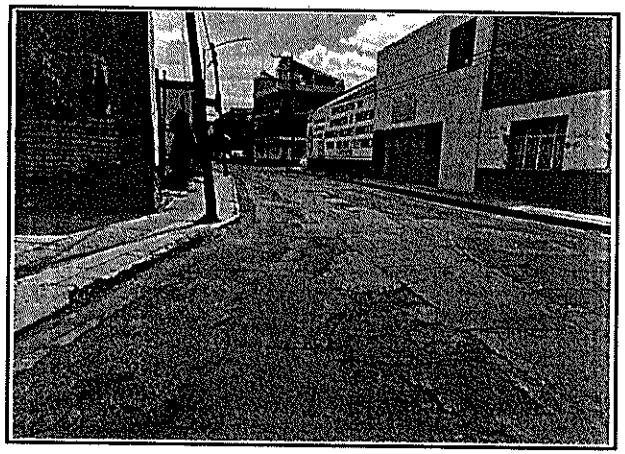

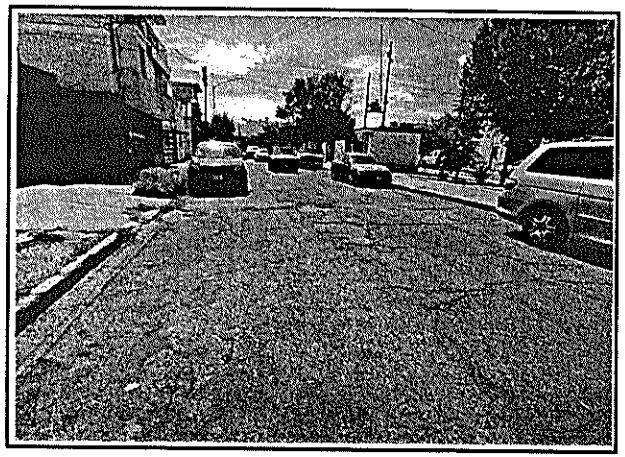

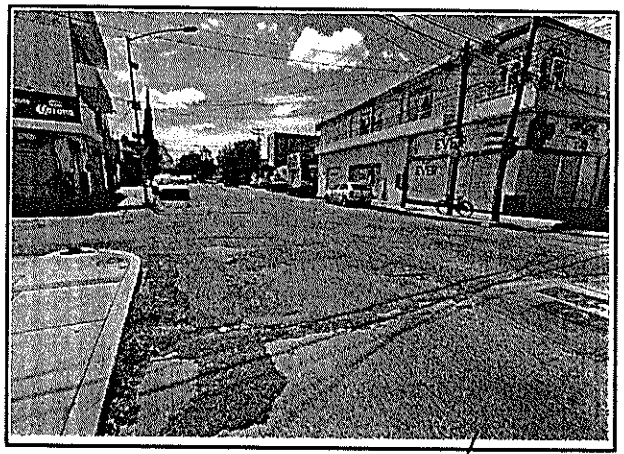

ING. RICARDO MACÍAS MERCADO
SUPERVISOR DE OBRA.


SECRETARÍA DE OBRAS PÚBLICAS
DIRECCIÓN DE SUPERVISIÓN DE OBRA


Aguascalientes
LA CIUDAD DE TU VIDA


MEMORIA FOTOGRAFICA


OBRA.	FISMDF-0044-2022 - SOBRECARPETA ASFÁLTICA AV. PETRÓLEOS MEXICANOS					
NO. DE CONTRATO:	FISMDF-0044-2022		CONTRATISTA:	DINAMICA ALRO, S.A. DE C.V.		

PROCESO

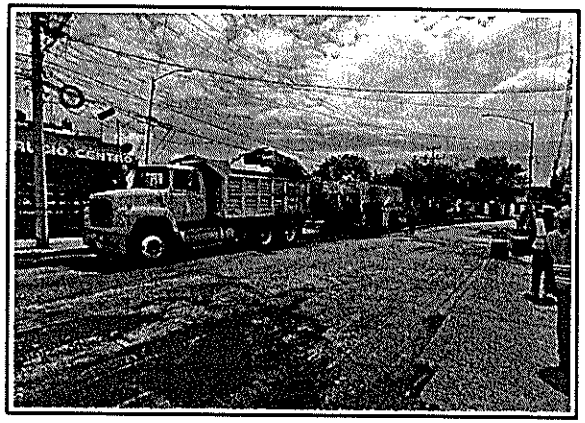

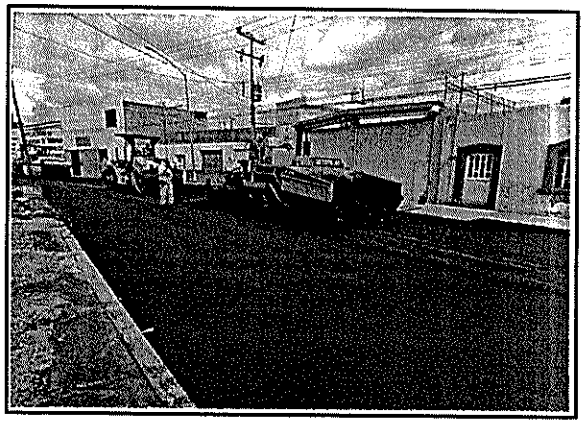

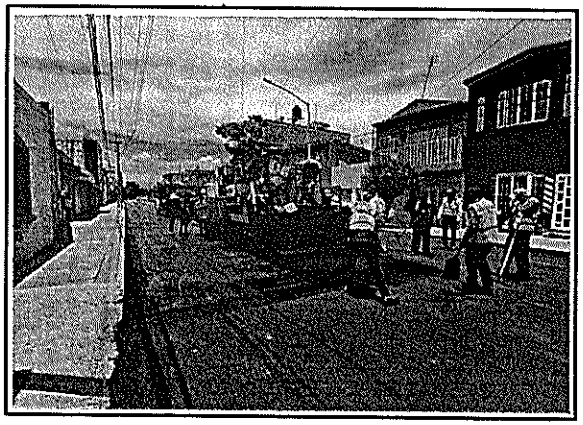

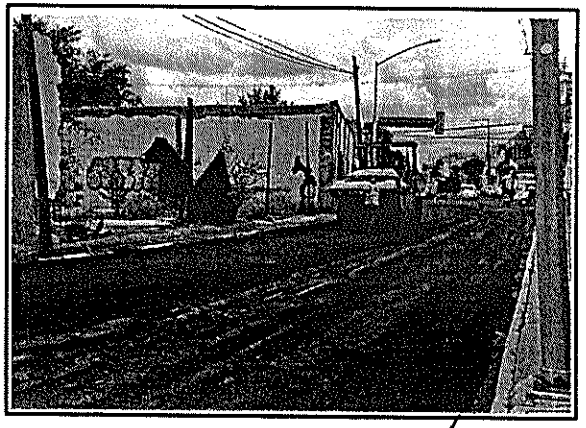

ING. RICARDO MACÍAS MERCADO
SUPERVISOR DE OBRA.


H. AYUNTAMIENTO DE AGUASCALIENTES
SECRETARÍA DE OBRAS PÚBLICAS
DIRECCIÓN DE SUPERVISIÓN DE OBRA


Aguascalientes
LA CIUDAD DE TU VIDA


MEMORIA FOTOGRAFICA


OBRA:	FISMDF-0044-2022 - SOBRECARPETA ASFÁLTICA AV. PETRÓLEOS MEXICANOS					
NO. DE CONTRATO:	FISMDF-0044-2022		CONTRATISTA:	DINAMICA ALRO, S.A. DE C.V.		

TERMINO

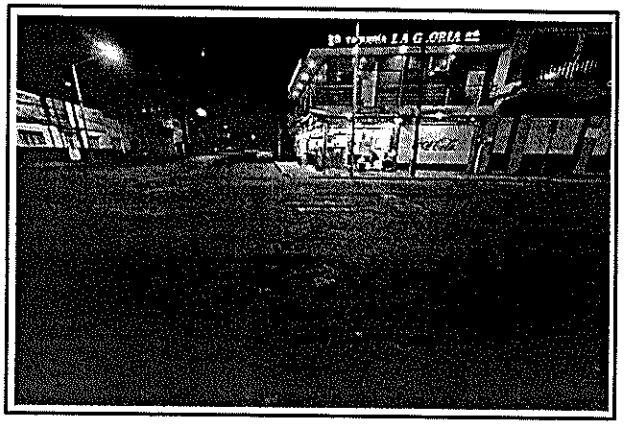

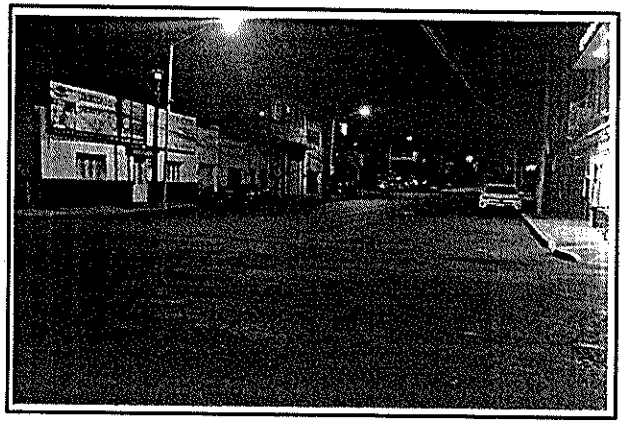


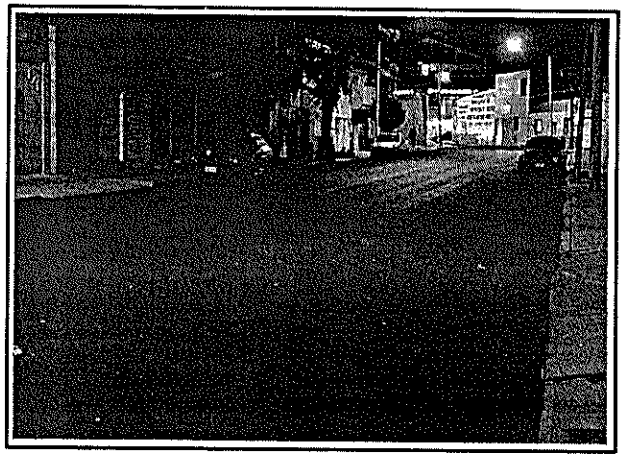

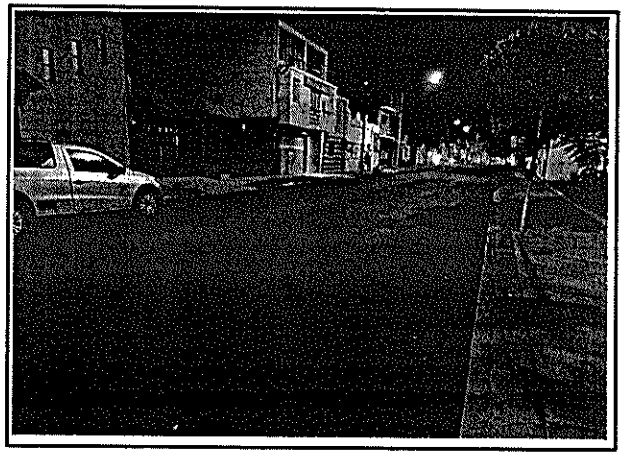

ING. RICARDO MACÍAS MERCADO
SUPERVISOR DE OBRA.

UBICACION

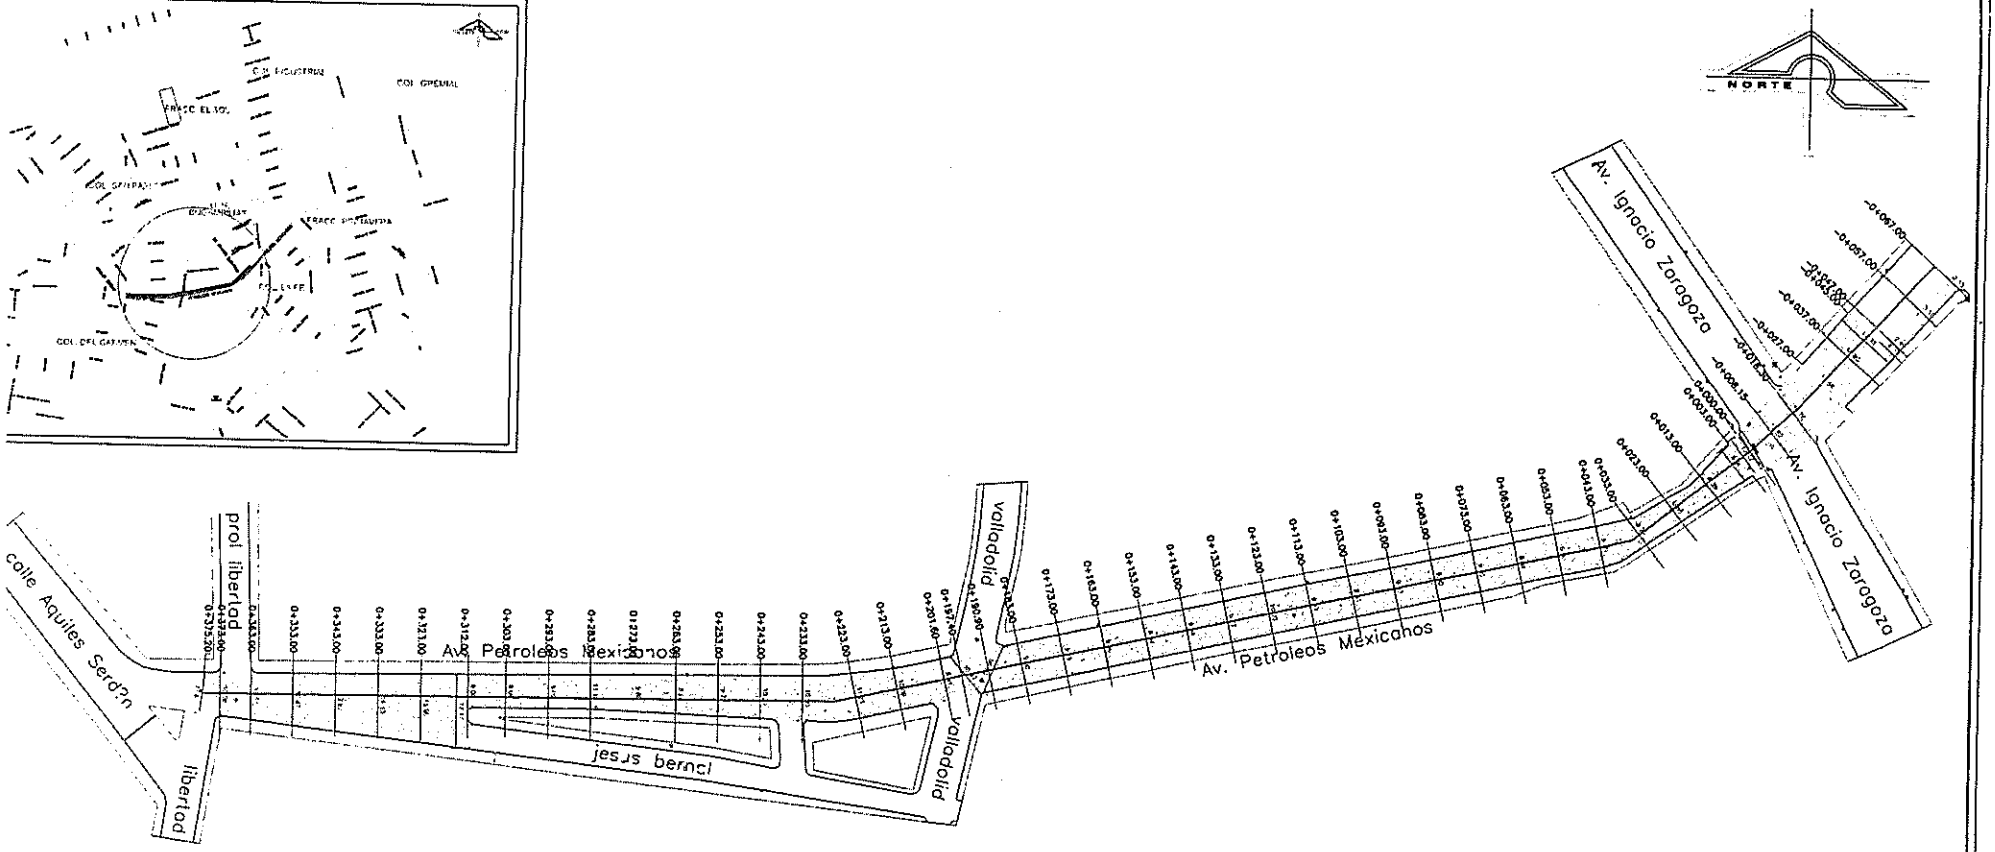

SIMBOLOGÍA

	EJE DE PROYECTO		CAIMAN
	BANQUETAS		CARPETA NUEVA
	PARAMENTOS		
0+053.60	CADENAMIENTO		POZO DE VISITA
E15	EJE DE PROYECTO		CAJA DE VALVULAS

FIRMAS

CONTRATISTA

DINAMICA ALRO S.A. DE C.V.
ING ANGEL LUIS BRUN TOLEDO
REPRESENTANTE LEGAL

SECRETARIA DE OBRAS PUBLICAS
DEL MUNICIPIO DE AGUASCALIENTES

SOPMA
ING RICARDO MACIAS MERCADO
SUPERVISOR DE OBRA

ESC: 1:100

PRESIDENTE MUNICIPAL
M.P.P. Leonardo Montañez Castro
SECRETARIA DE OBRAS PUBLICAS DEL MUNICIPIO DE AGUASCALIENTES
Arq. Gloria Guadalupe Castillo González

CONTRATO:
FISMDF-0044-2022
SUPERVISOR:
ING. RICARDO MACIAS MERCADO
RESIDENTE:
ING. DULCE SARAY MENDOZA MORENO

Aguascalientes
LA CIUDAD DE TU VIDA

CONTRATISTA:
DINAMICA ALRO S.A. DE C.V.
RFC:
DAL190219SWA
DIRECCION;
AV. DE LOS MAESTROS #2624
COL. VERSALLES 2DA SECCIÓN

DALRO

CLAVE:
ARQ-01

OBRA:
SOBRECARPETA ASFALTICA AV. PETROLEOS MEXICANOS.
UBICACIÓN:
TRAMO ENTRE CALLE IGNACIO ZARAGOZA Y CALLE AQUILES SERDAN CENTRO Zona
CONTENIDO:
PLANO DEFINITIVO